


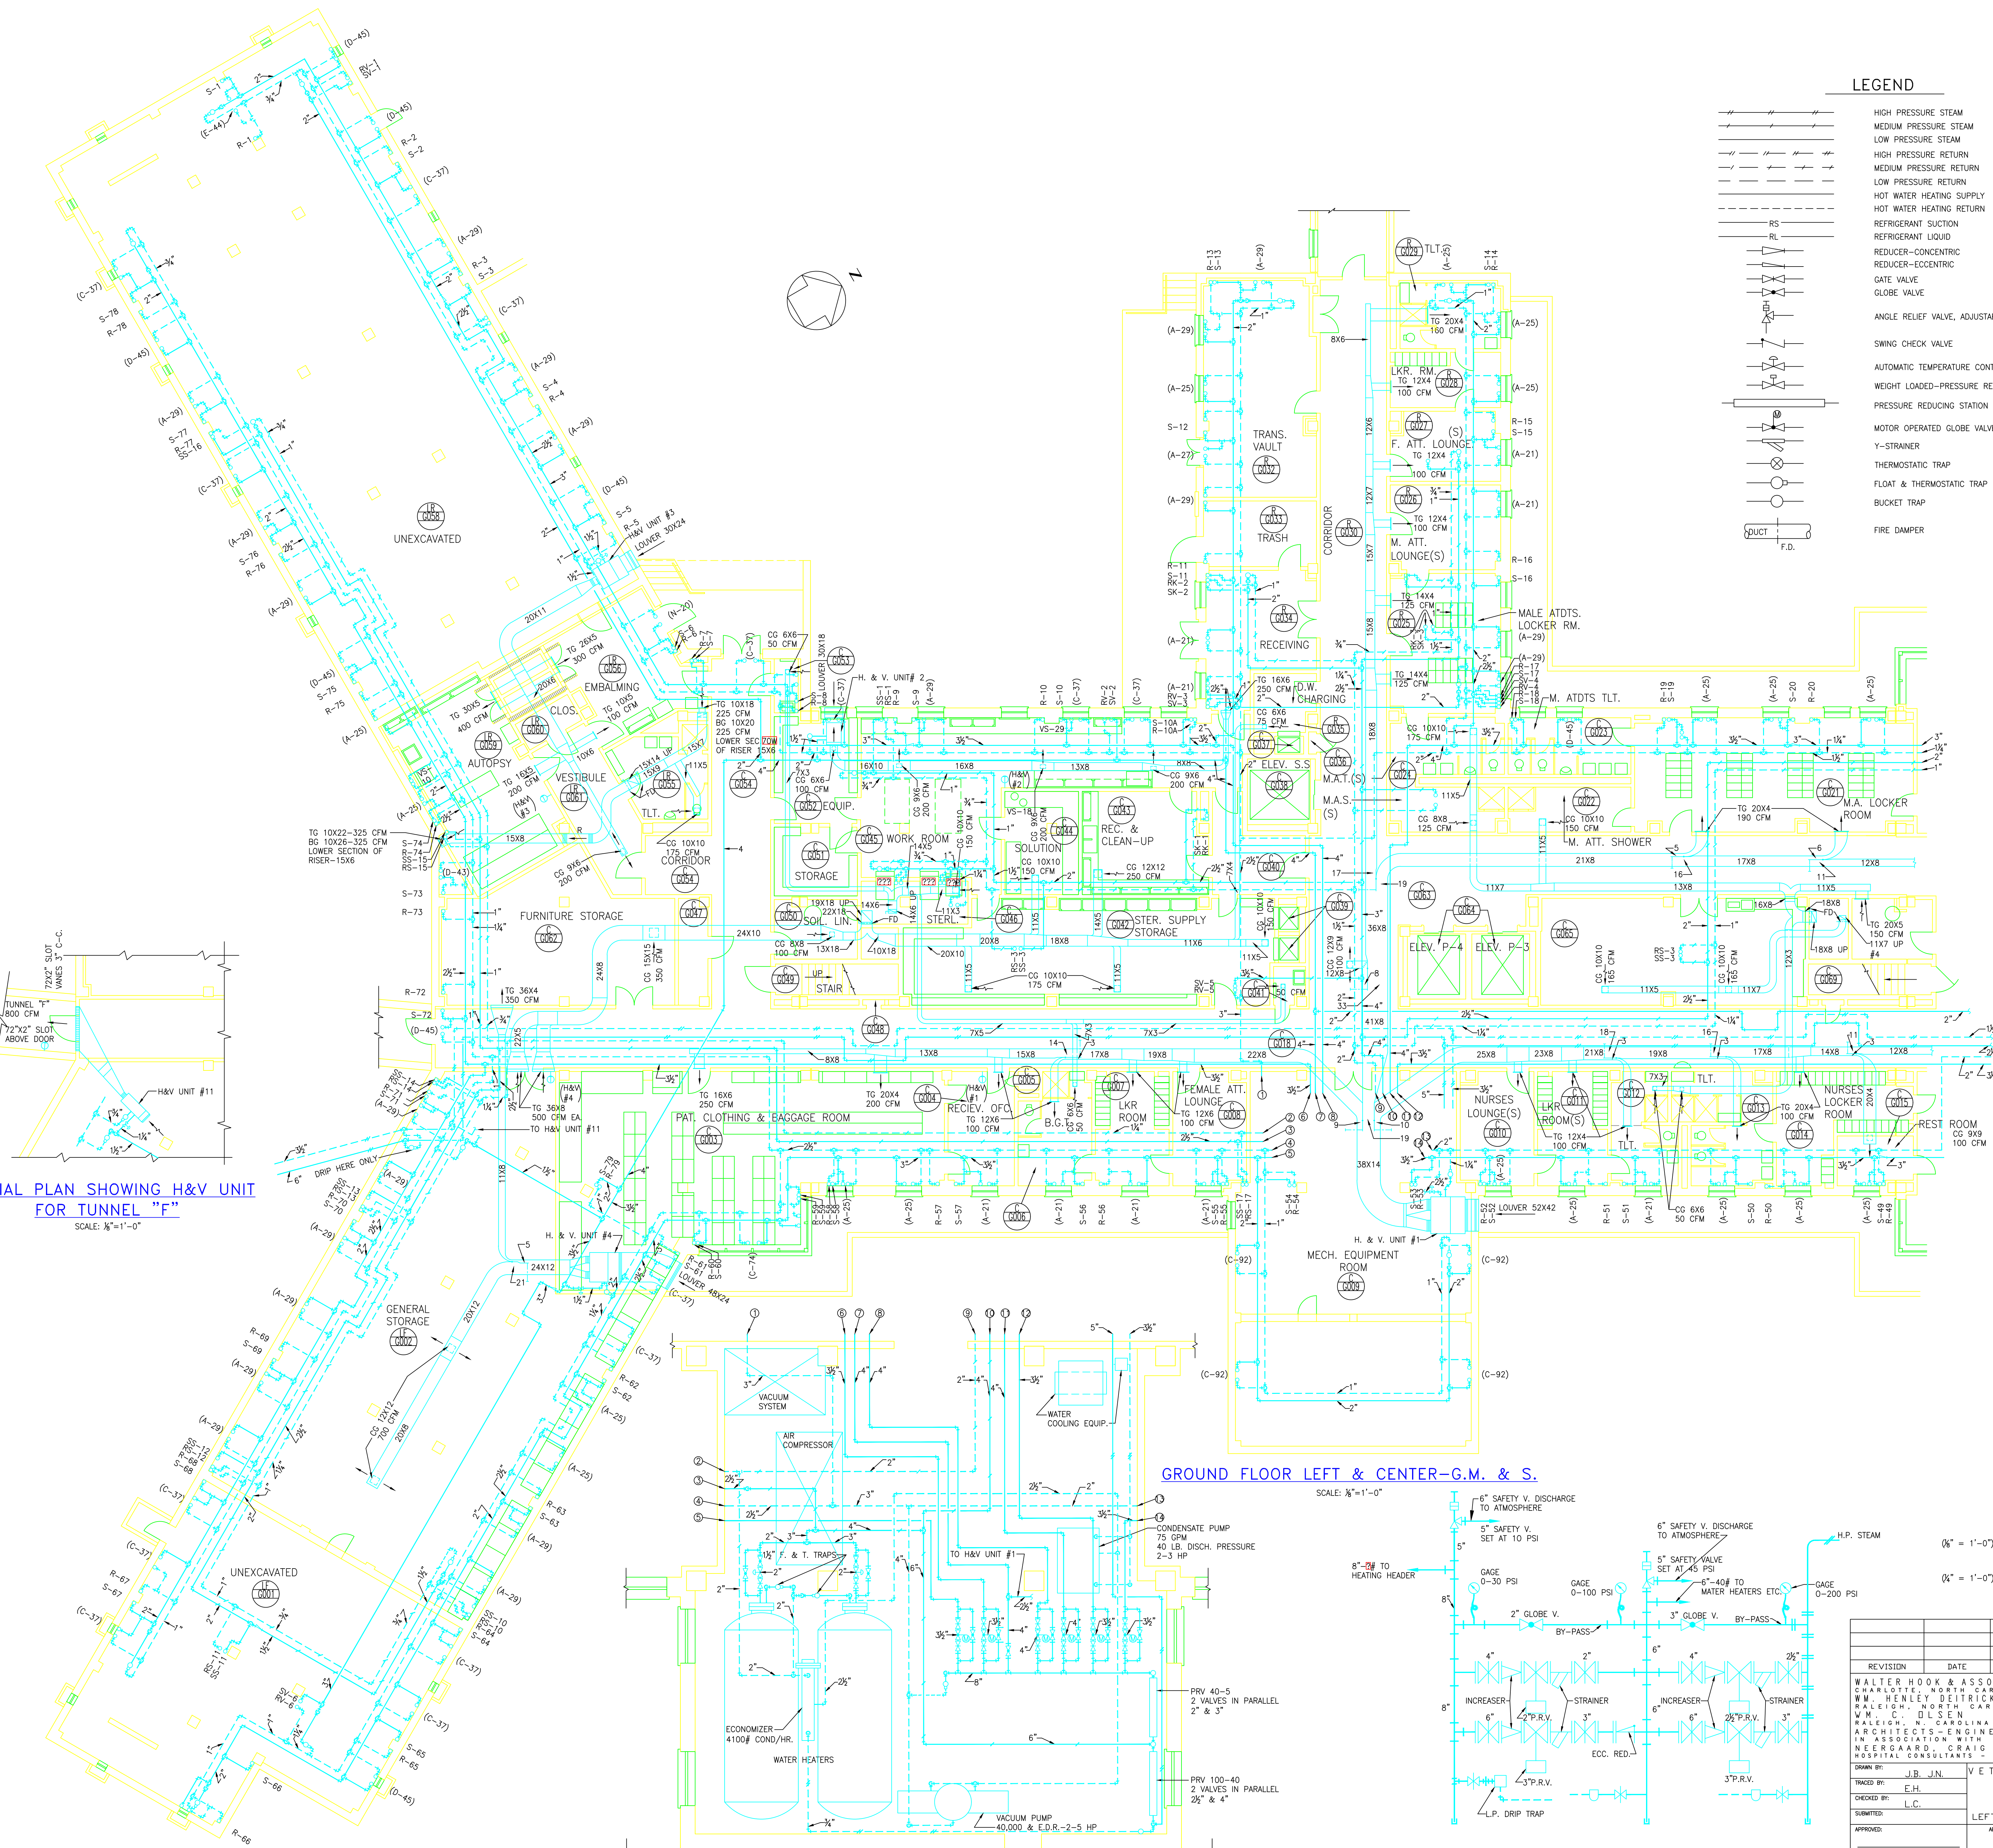

PARTIAL PLAN SHOWING H&V UNIT FOR TUNNEL "F"

SCALE: 1/8"=1'-0"

PLAN OF MECHANICAL EQUIPMENT ROOM

SCALE: 1/4"=1'-0"

DIAGRAM OF PRESSURE REDUCING STATION

NOT TO SCALE