


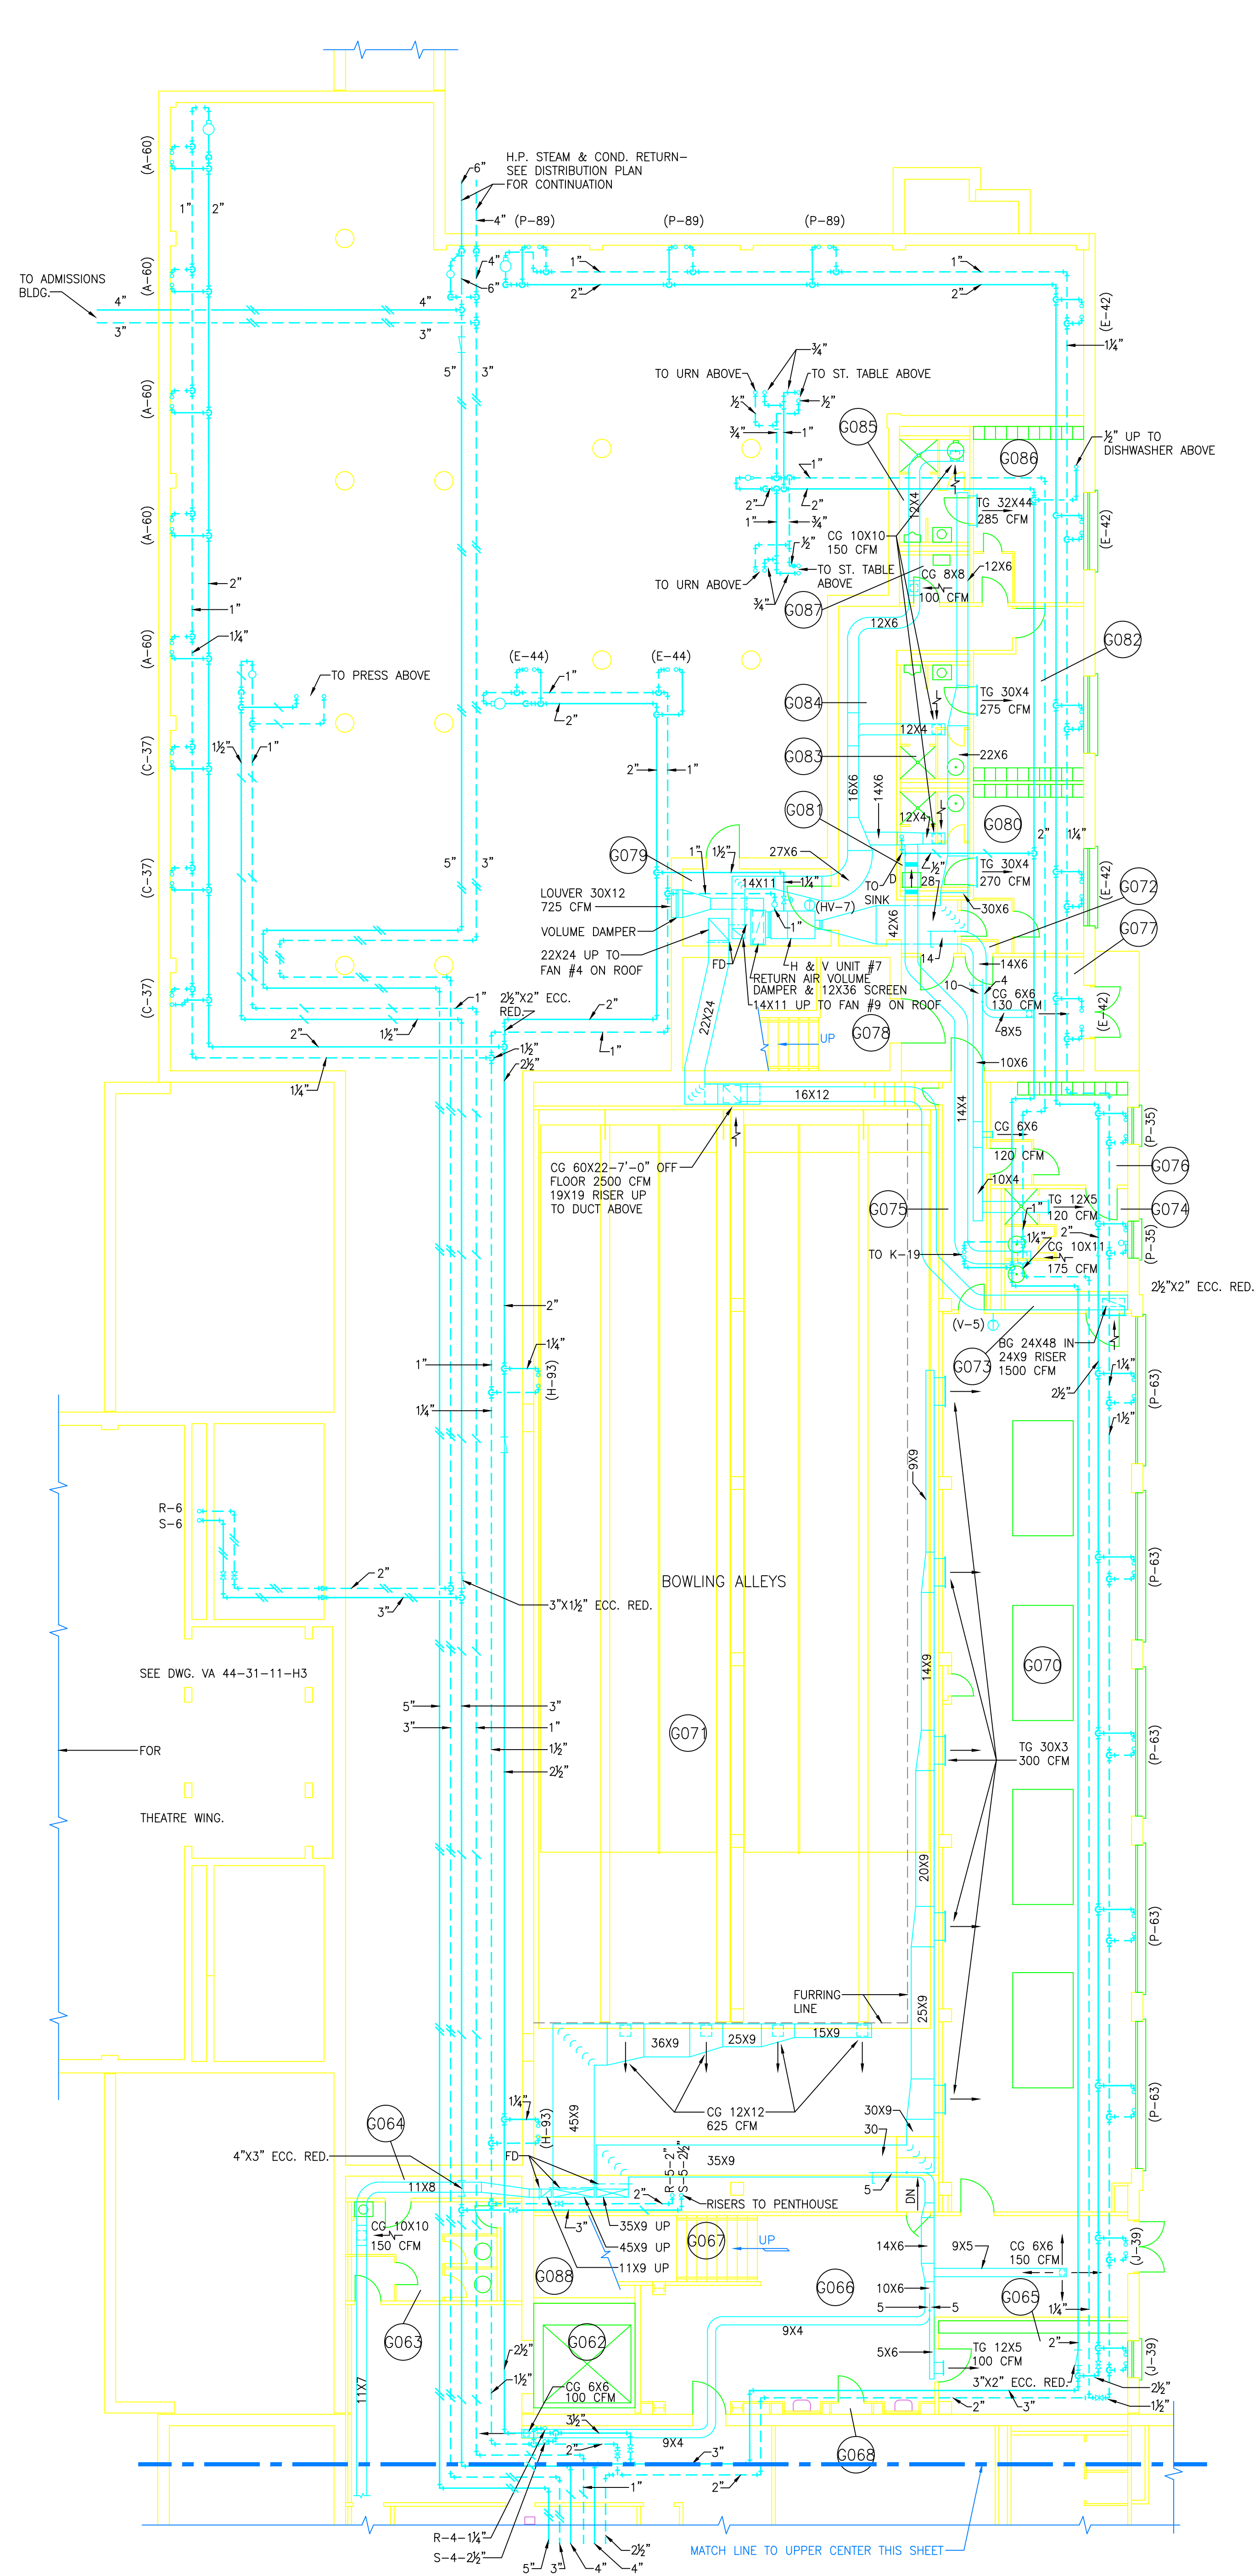


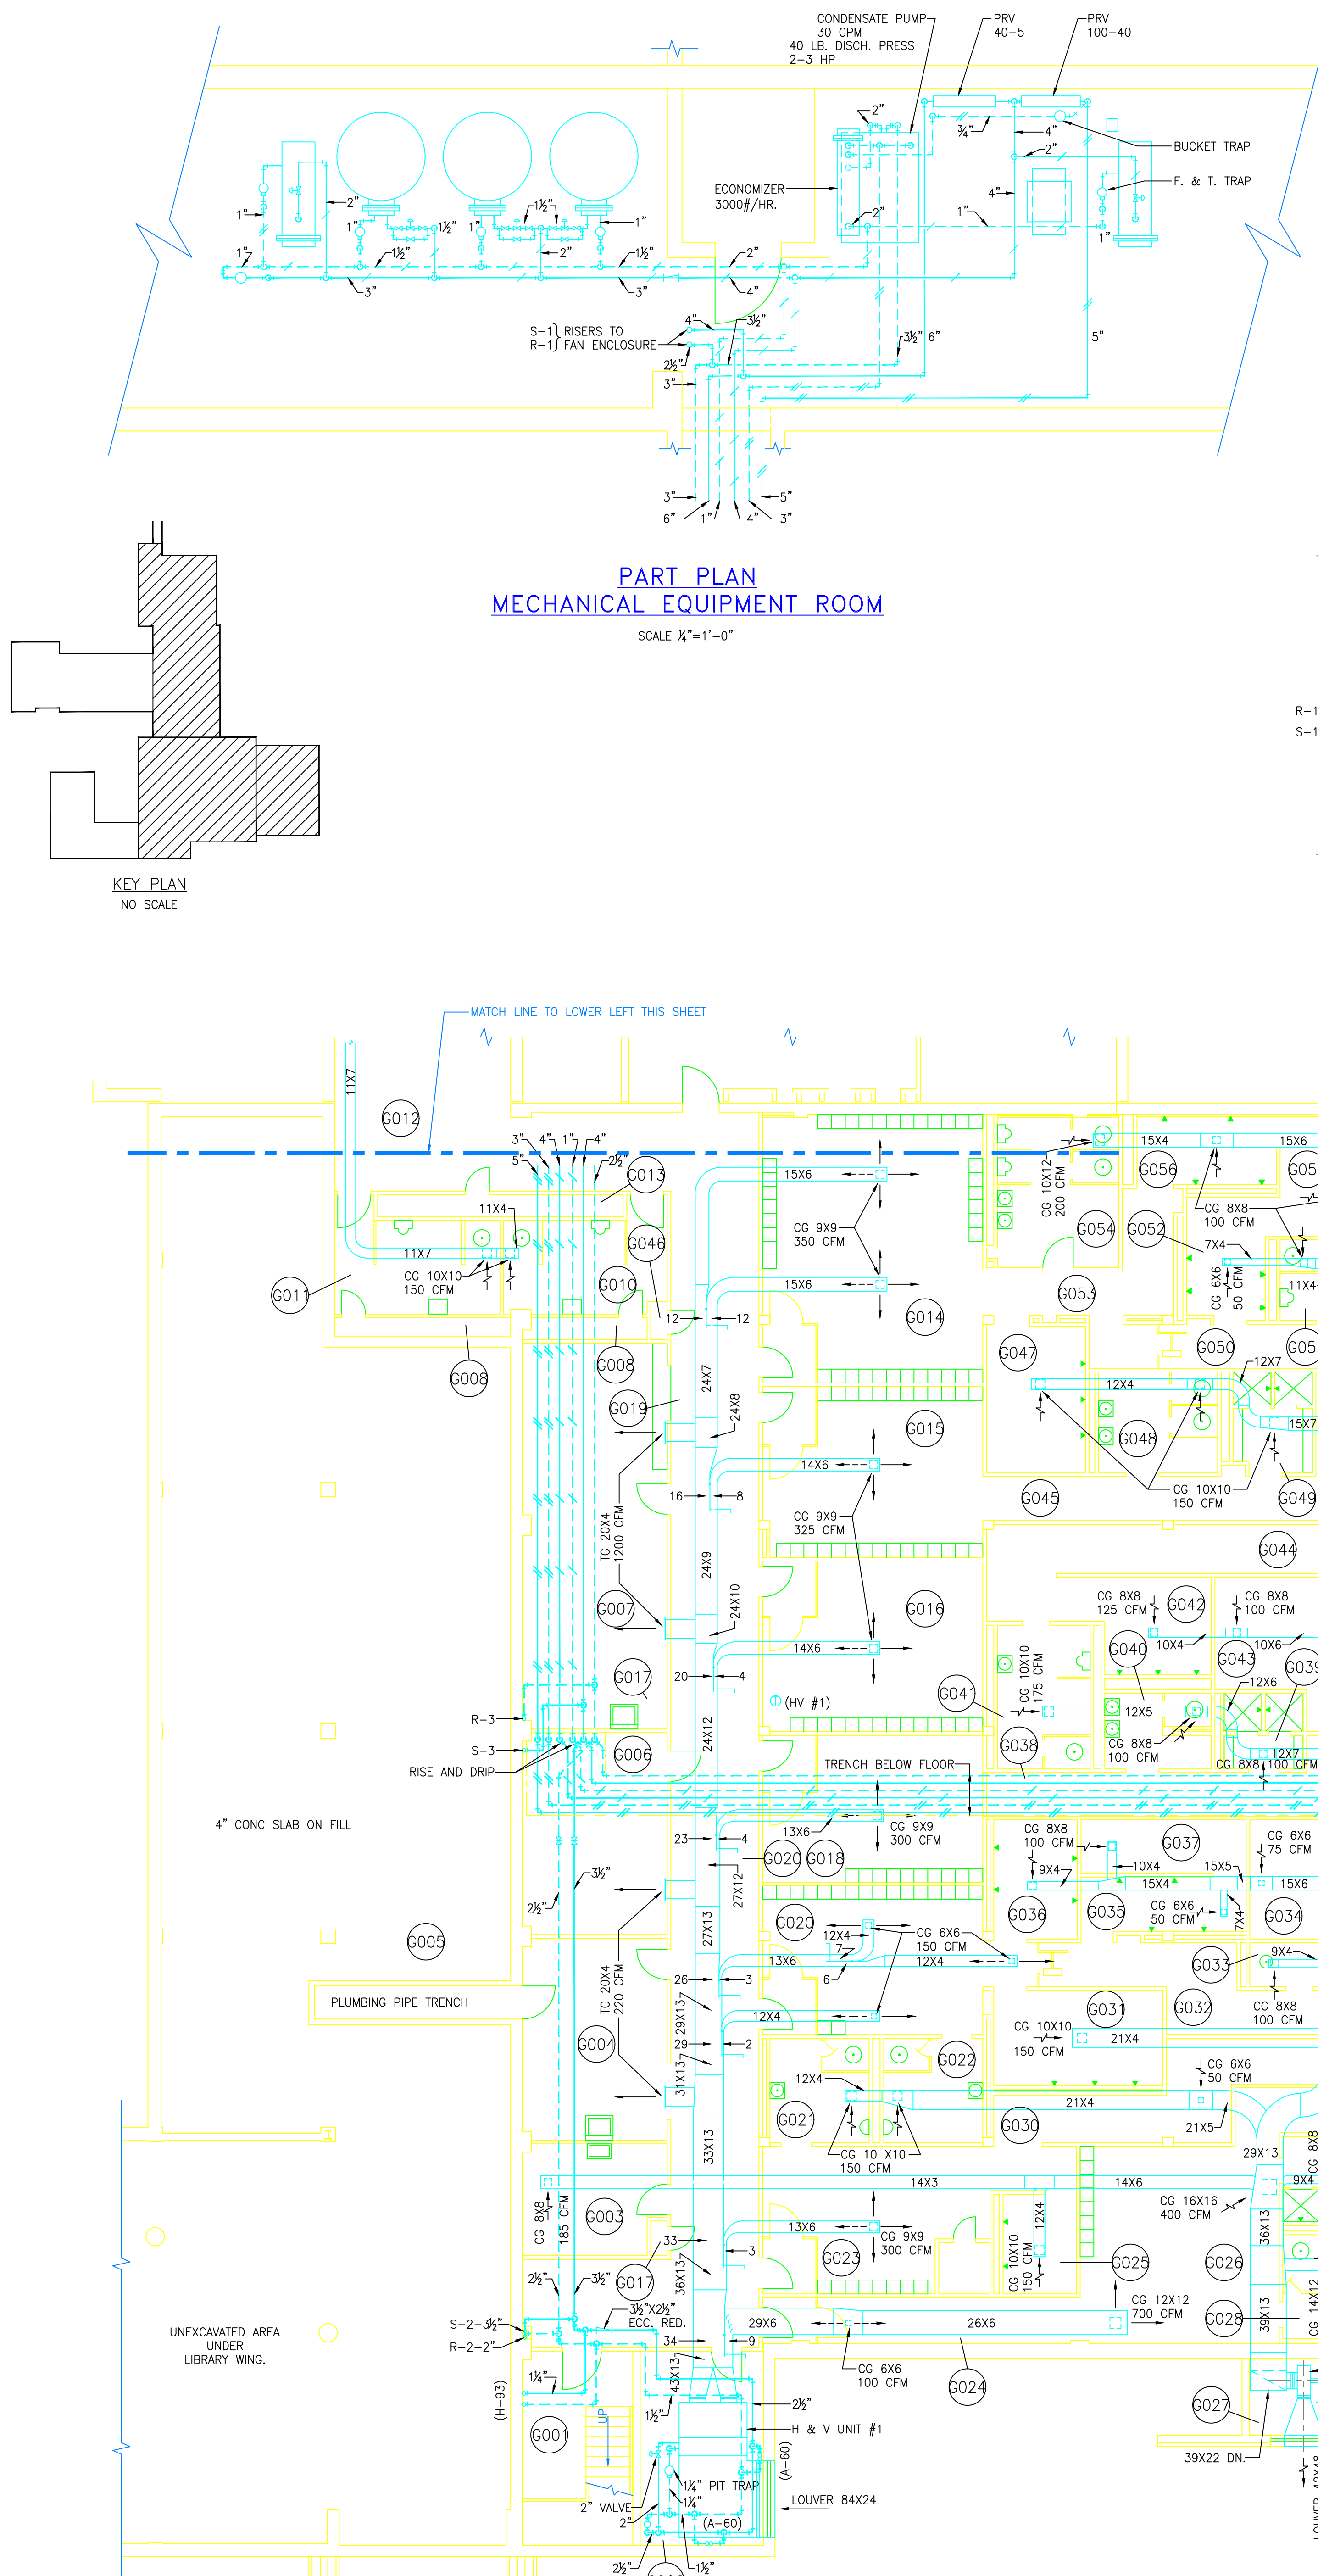

GROUND FLOOR PLAN-SOUTH PORTION
SCALE 1/8"=1'-0"

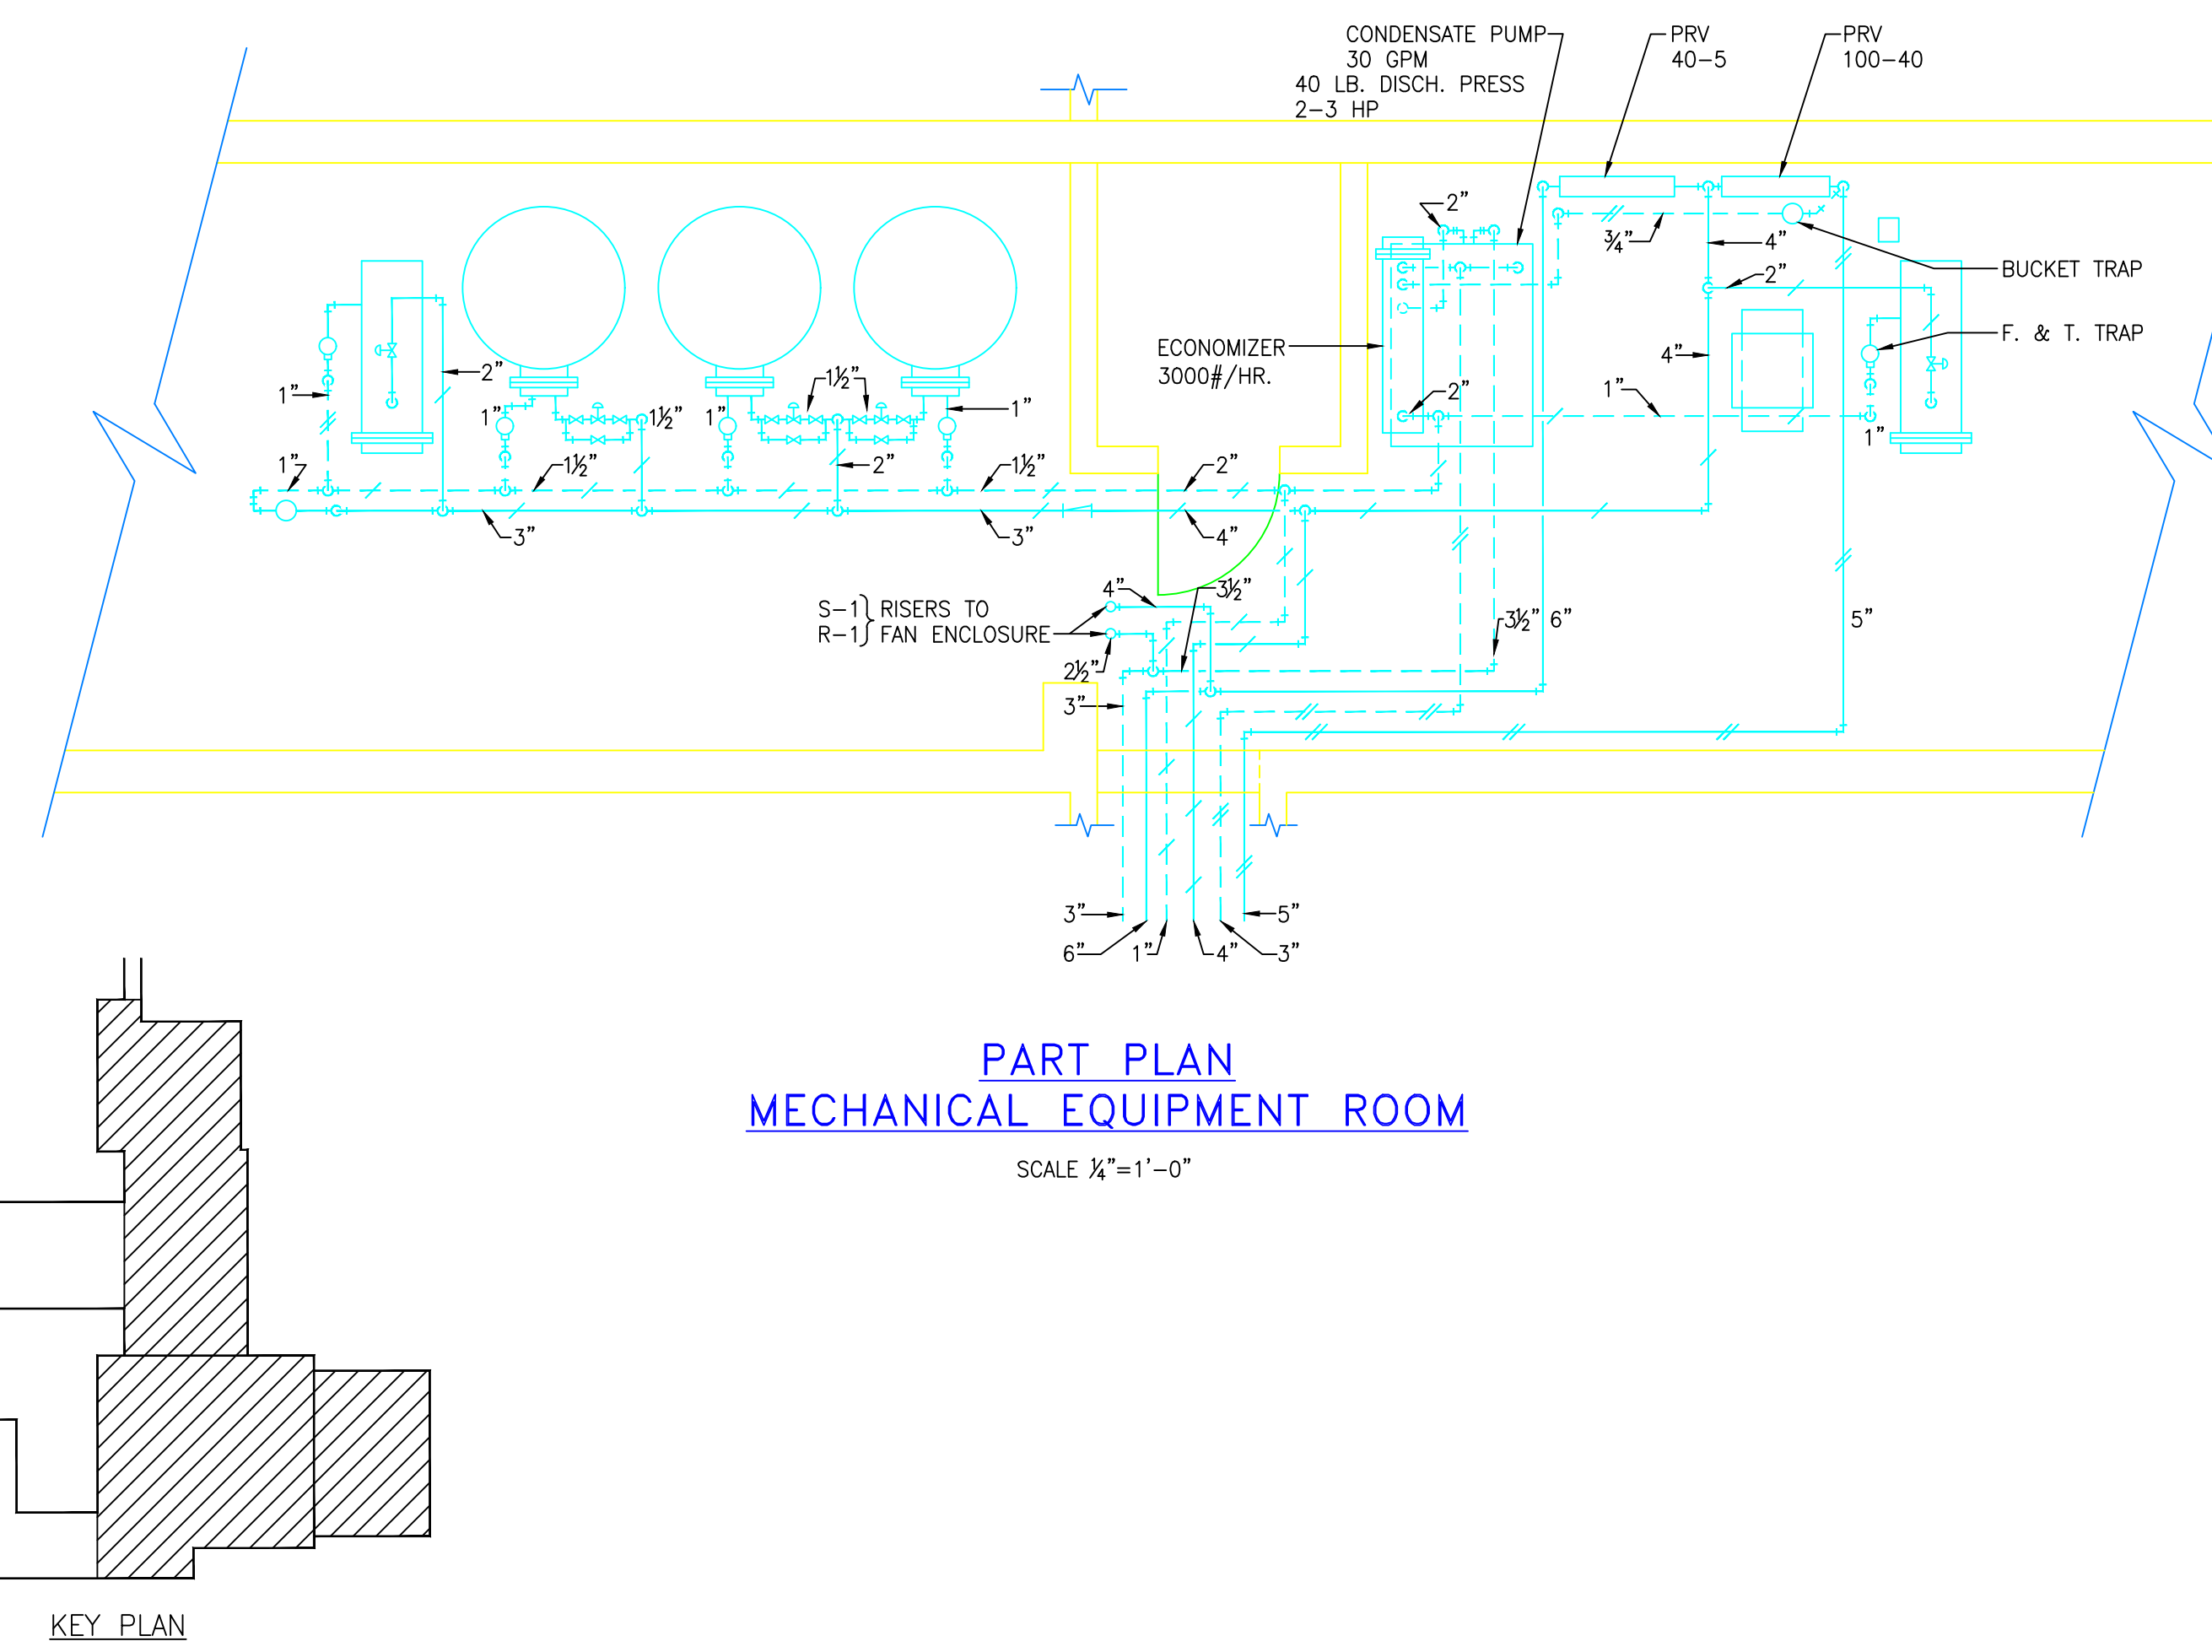

GROUND FLOOR PLAN-NORTH PORTION
SCALE 1/8"=1'-0"

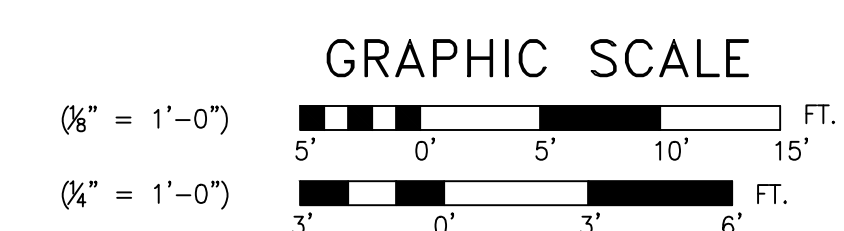

PART PLAN
MECHANICAL EQUIPMENT ROOM
SCALE 1/4"=1'-0"


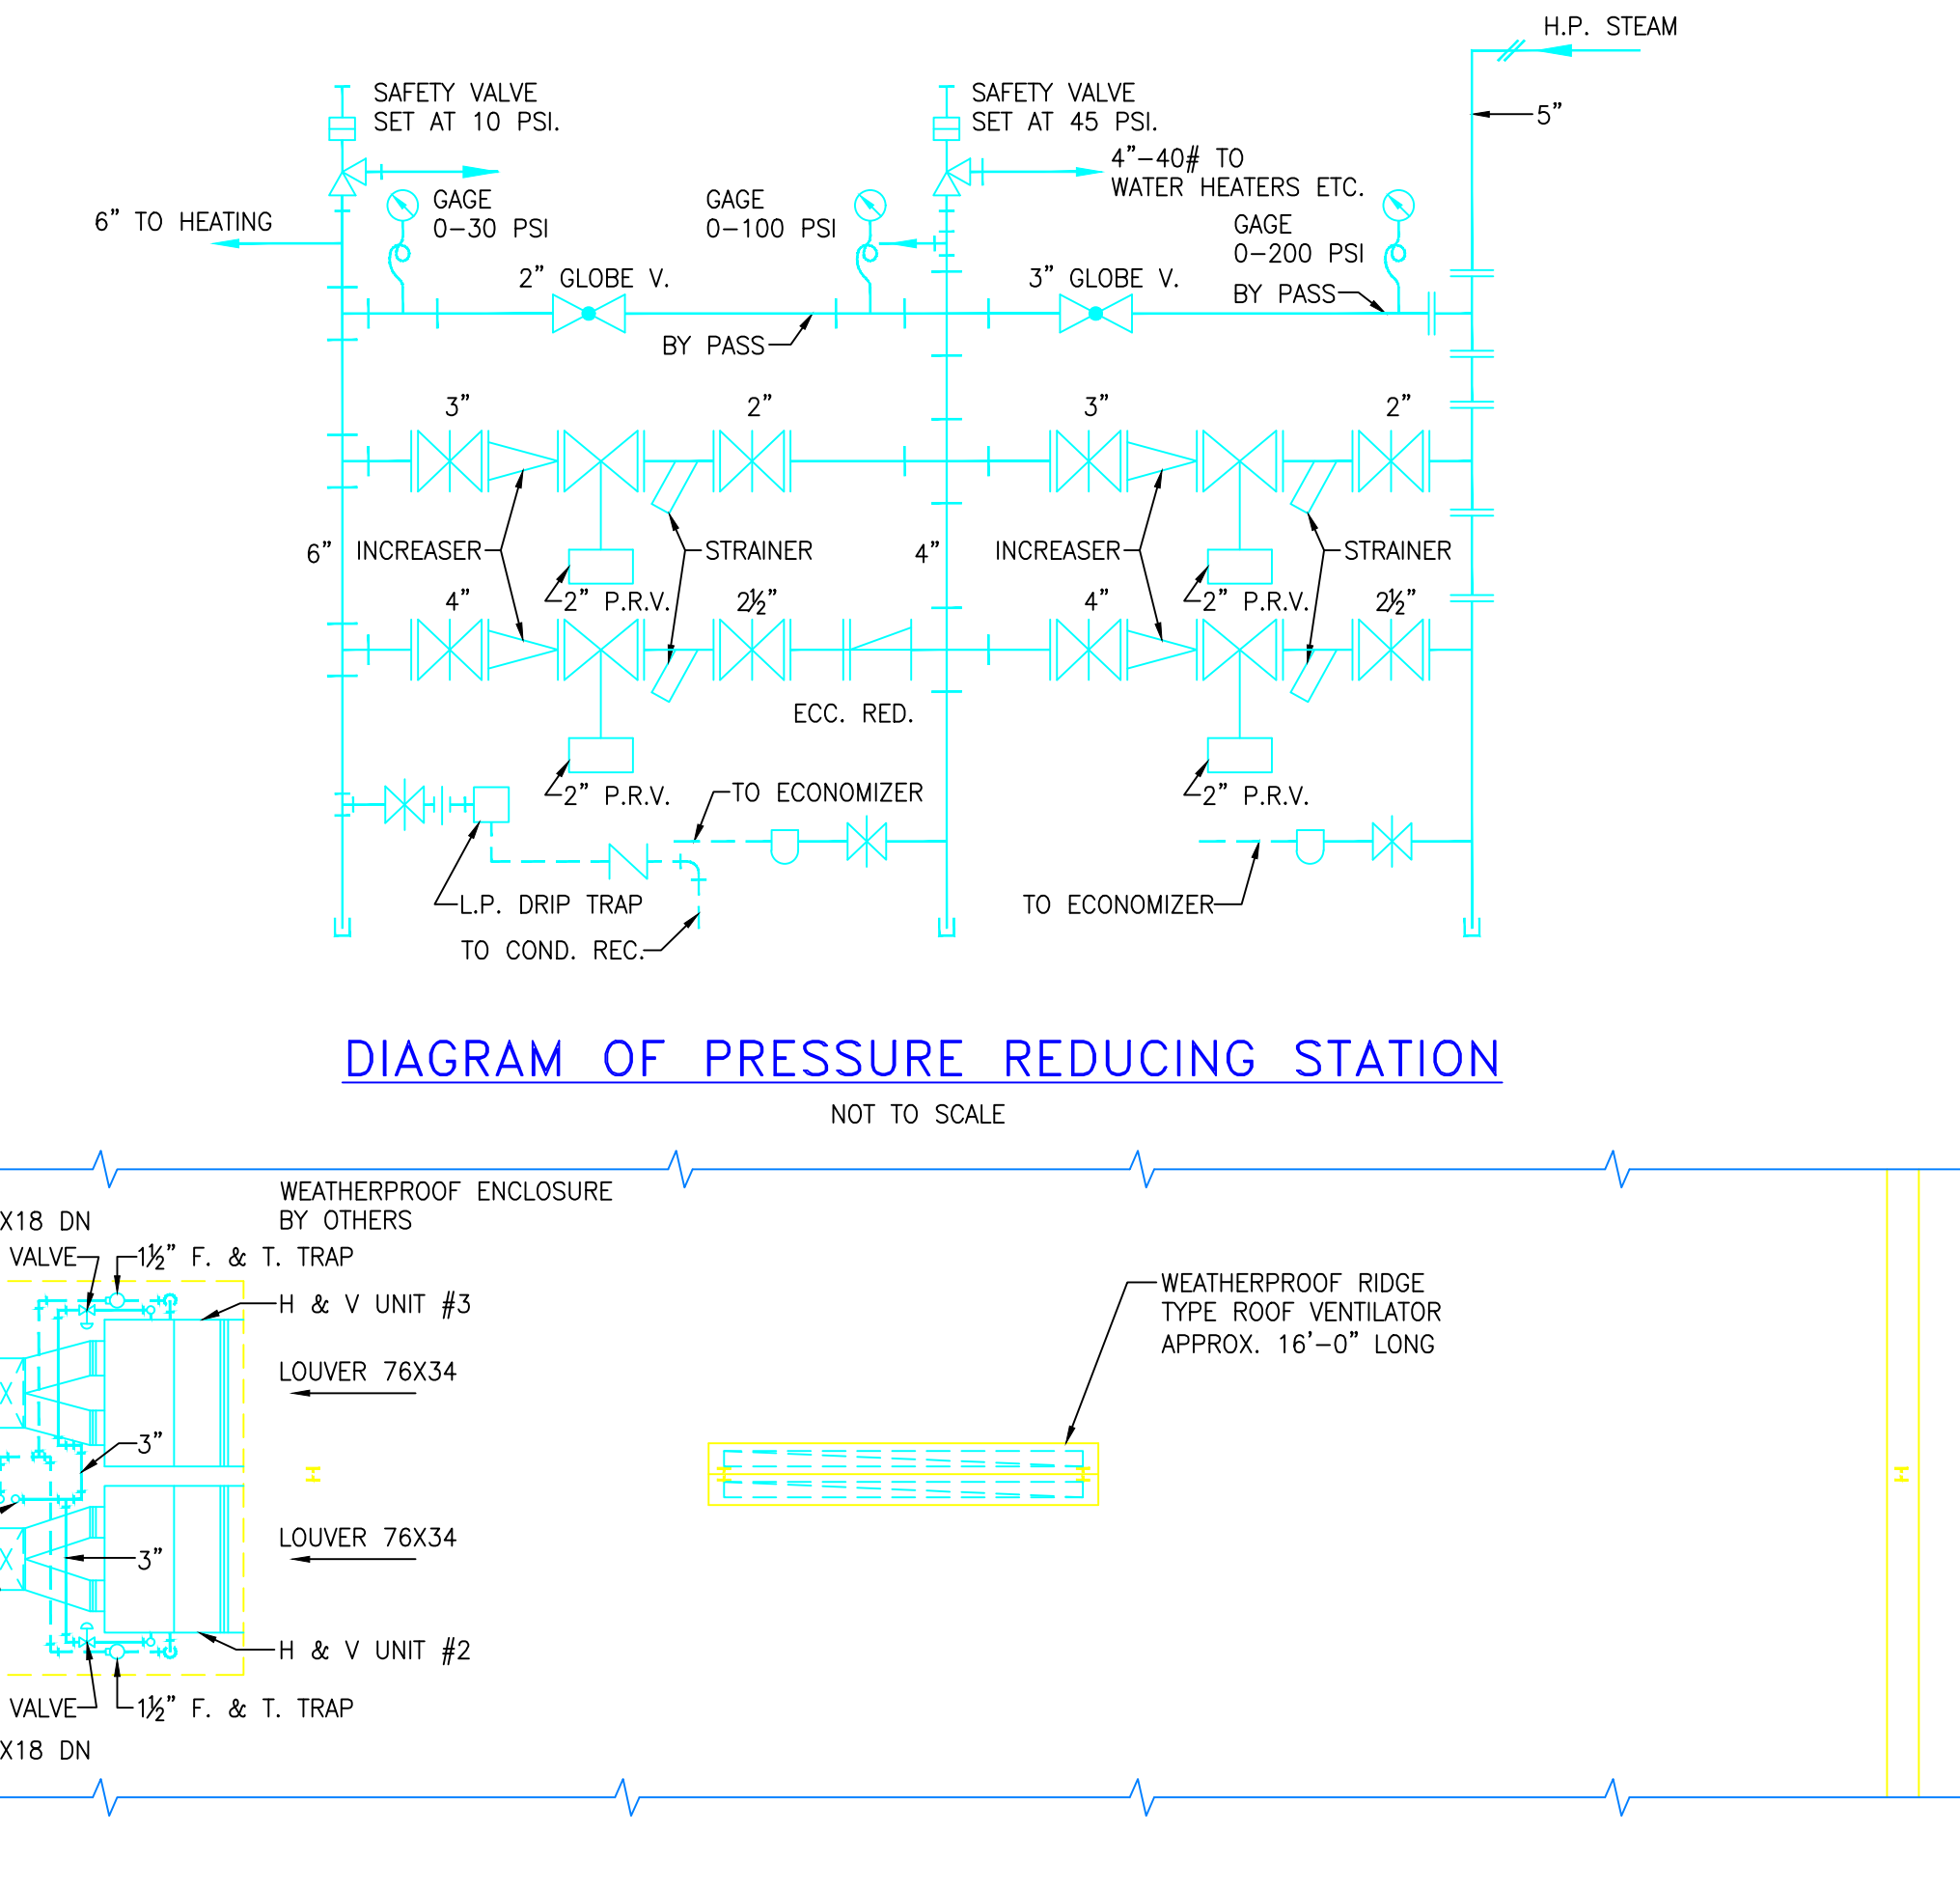


DIAGRAM OF PRESSURE REDUCING STATION
NOT TO SCALE

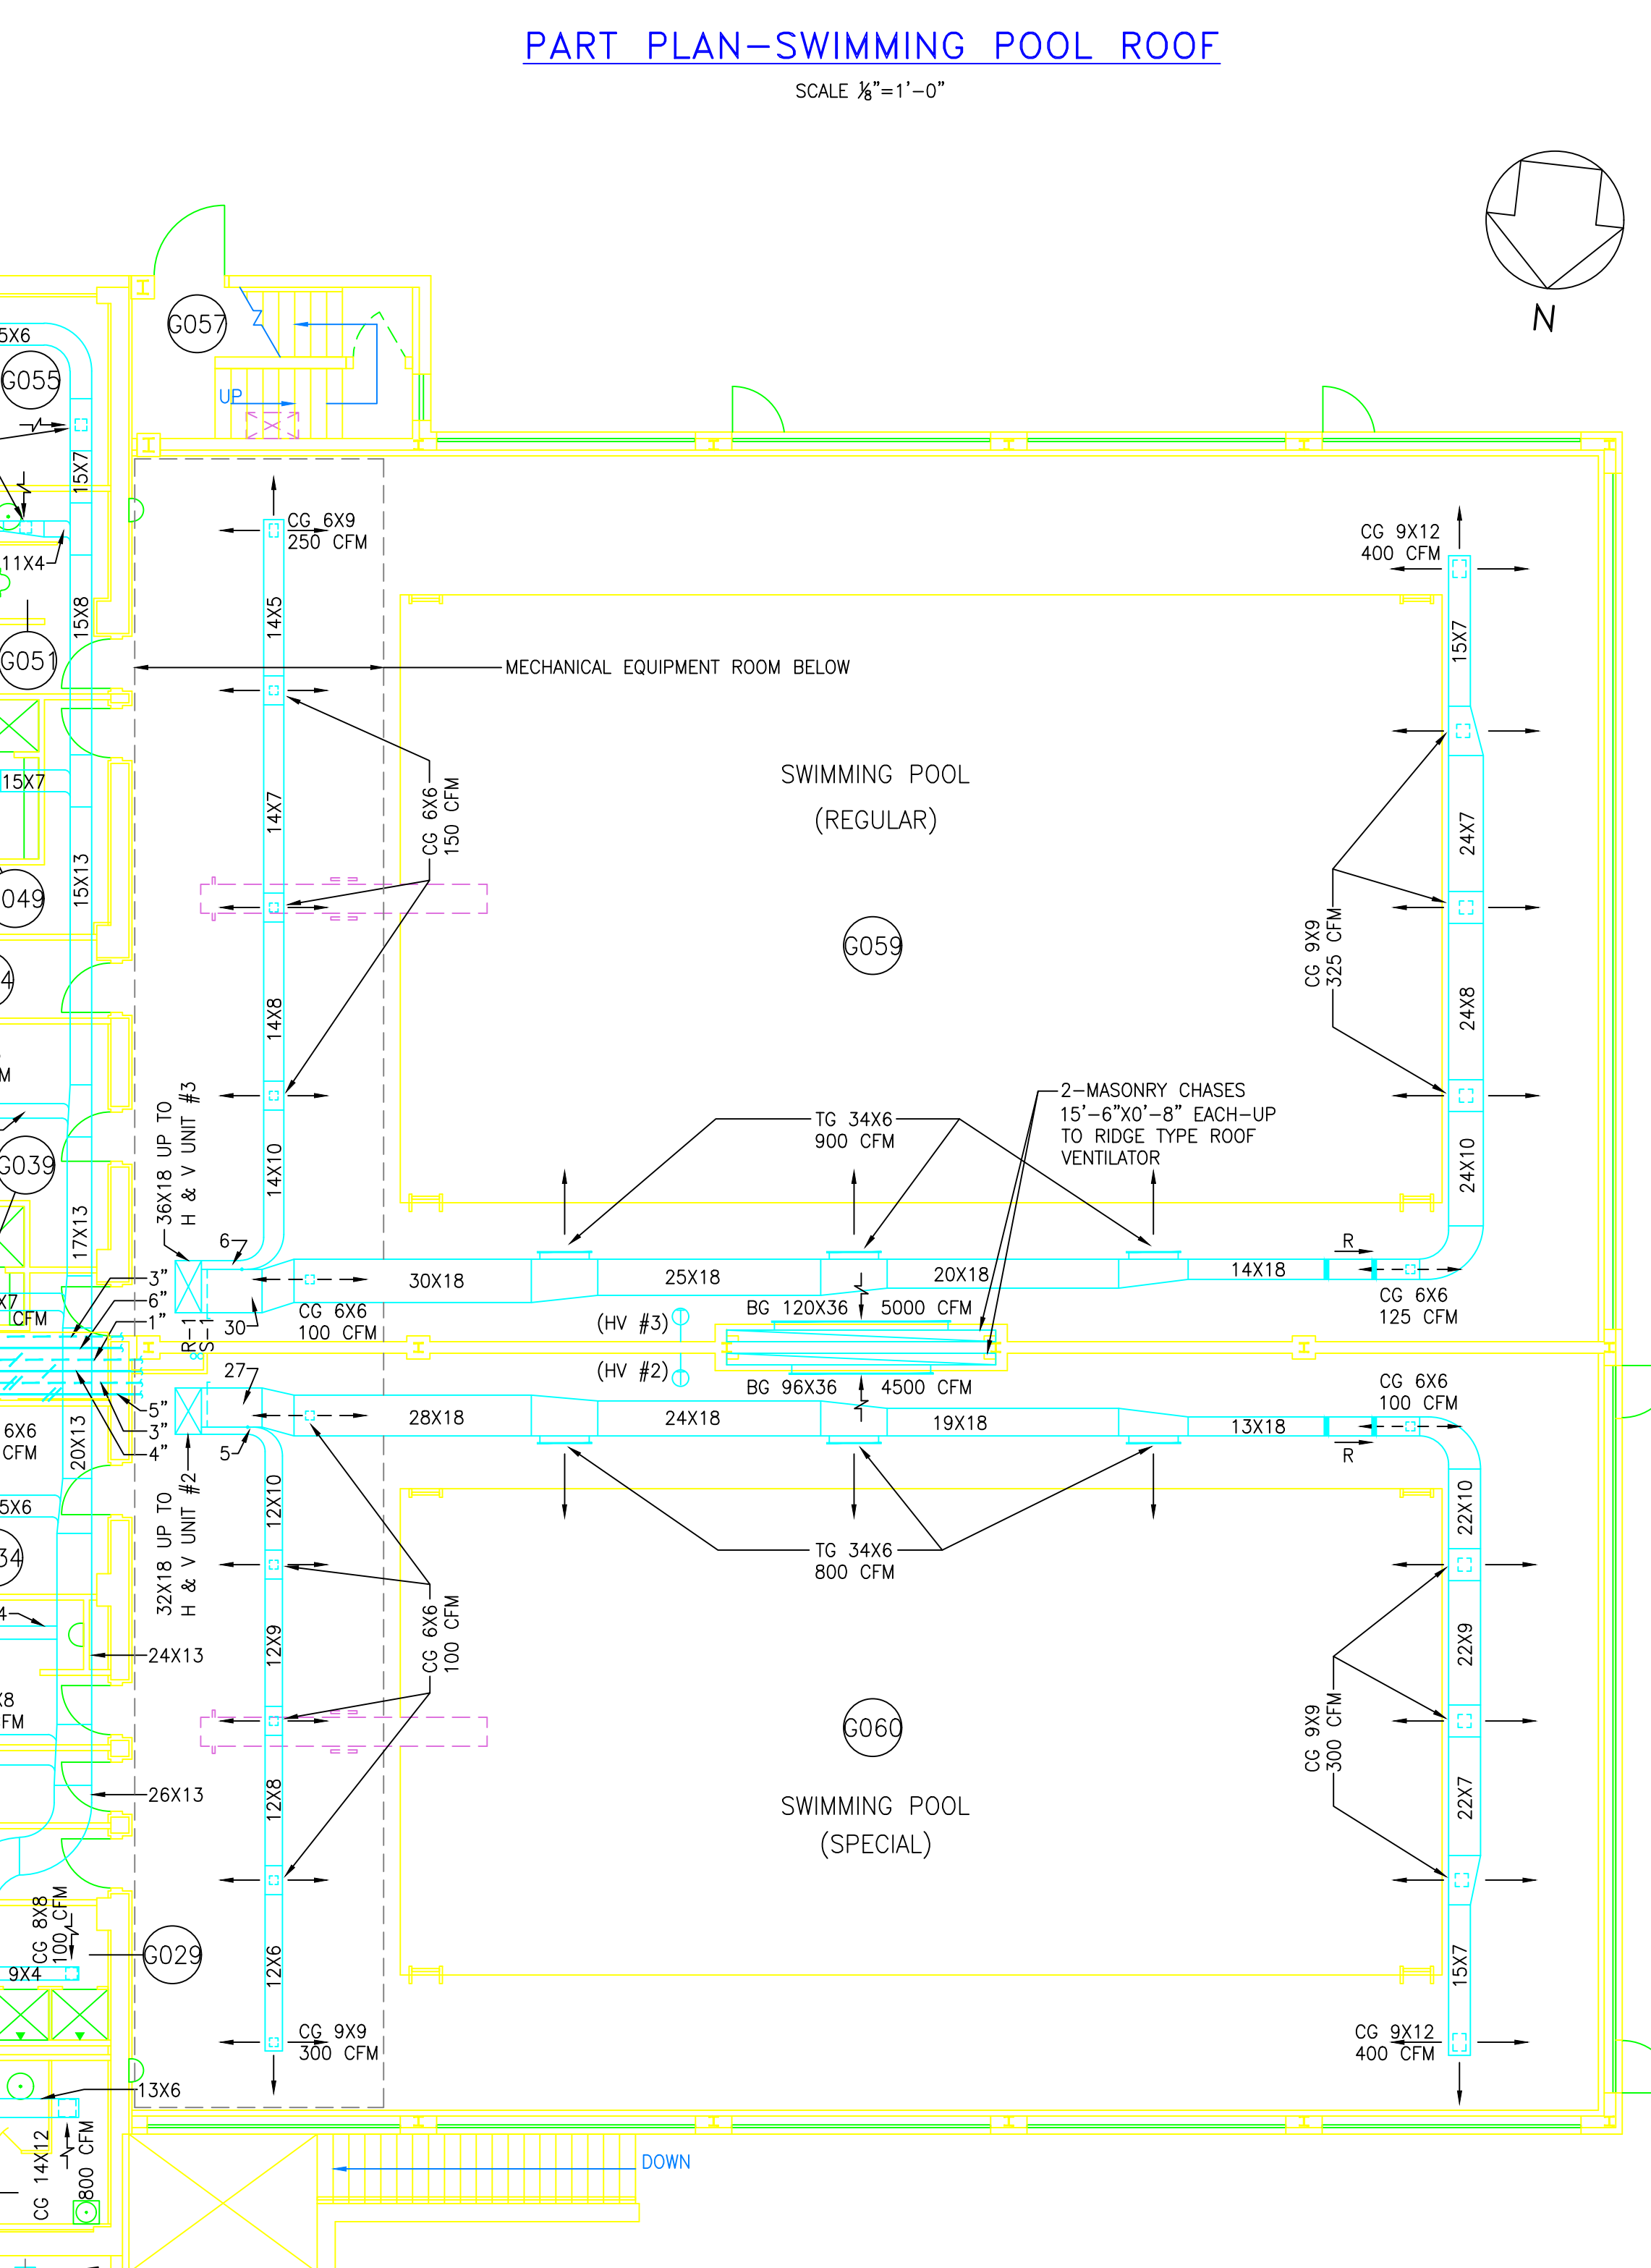

PART PLAN-SWIMMING POOL ROOF
SCALE 1/8"=1'-0"

REVISION	DATE	DESCRIPTION	BY
1			
2			
