

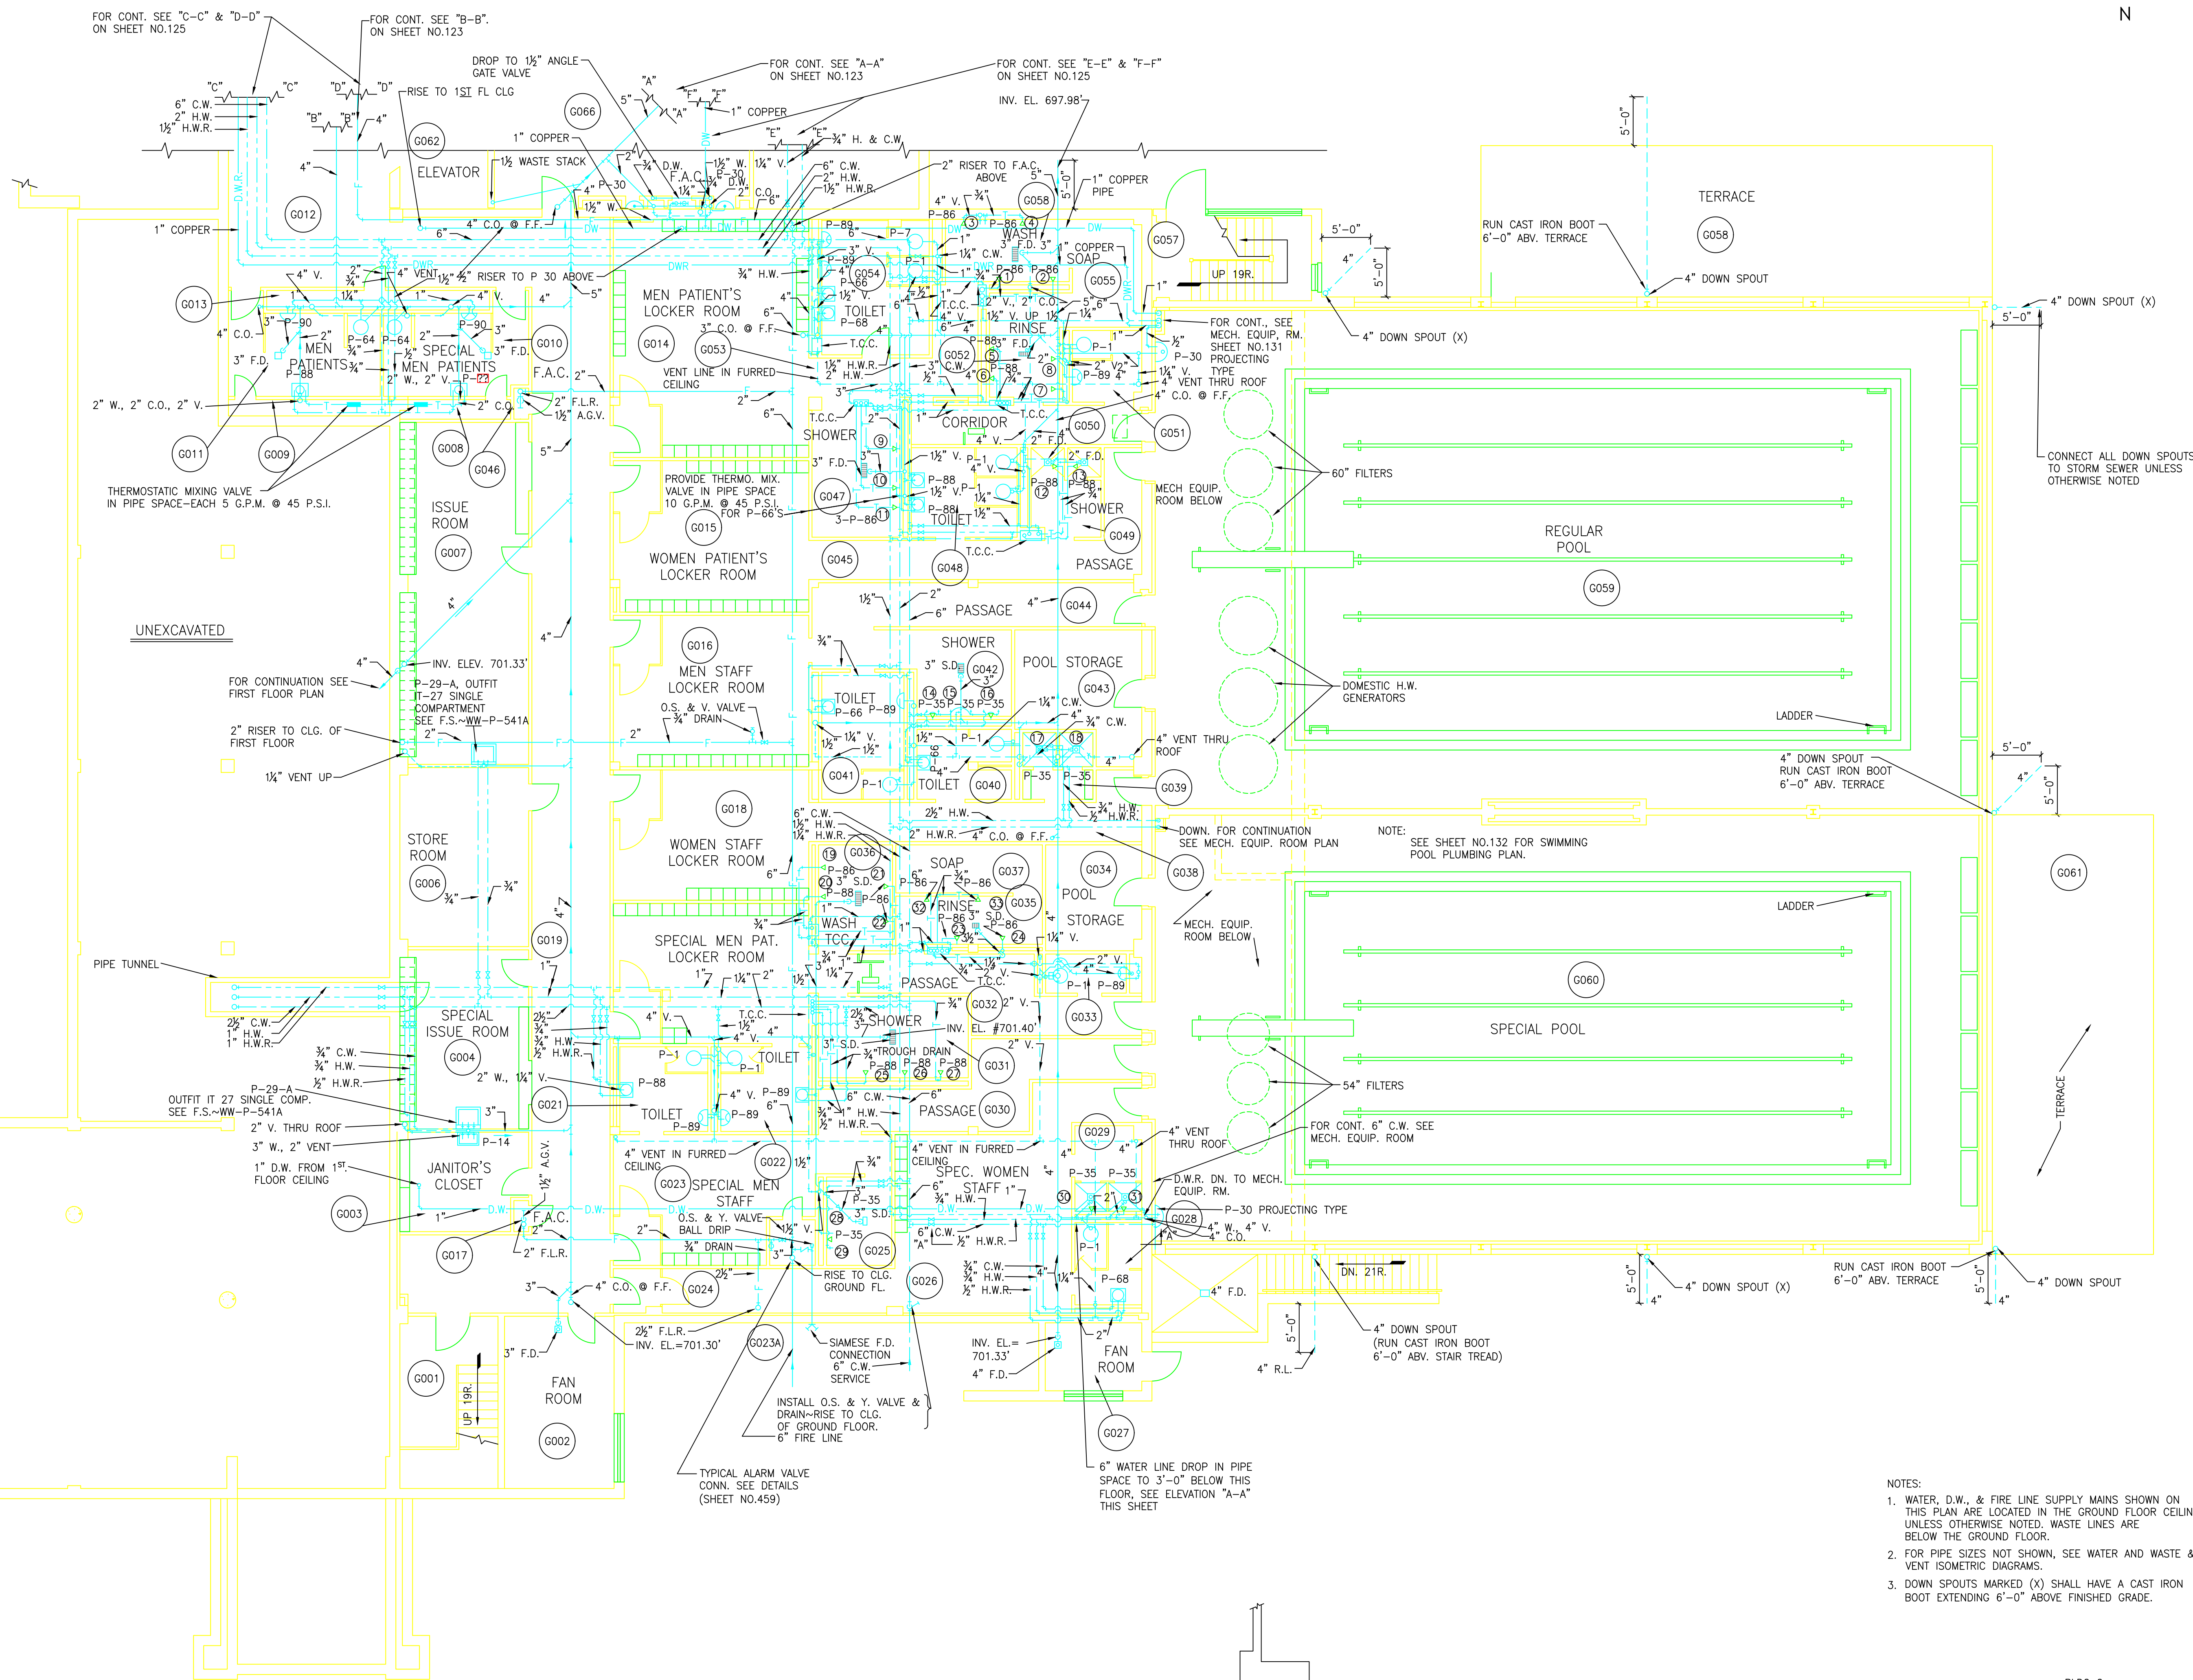
 
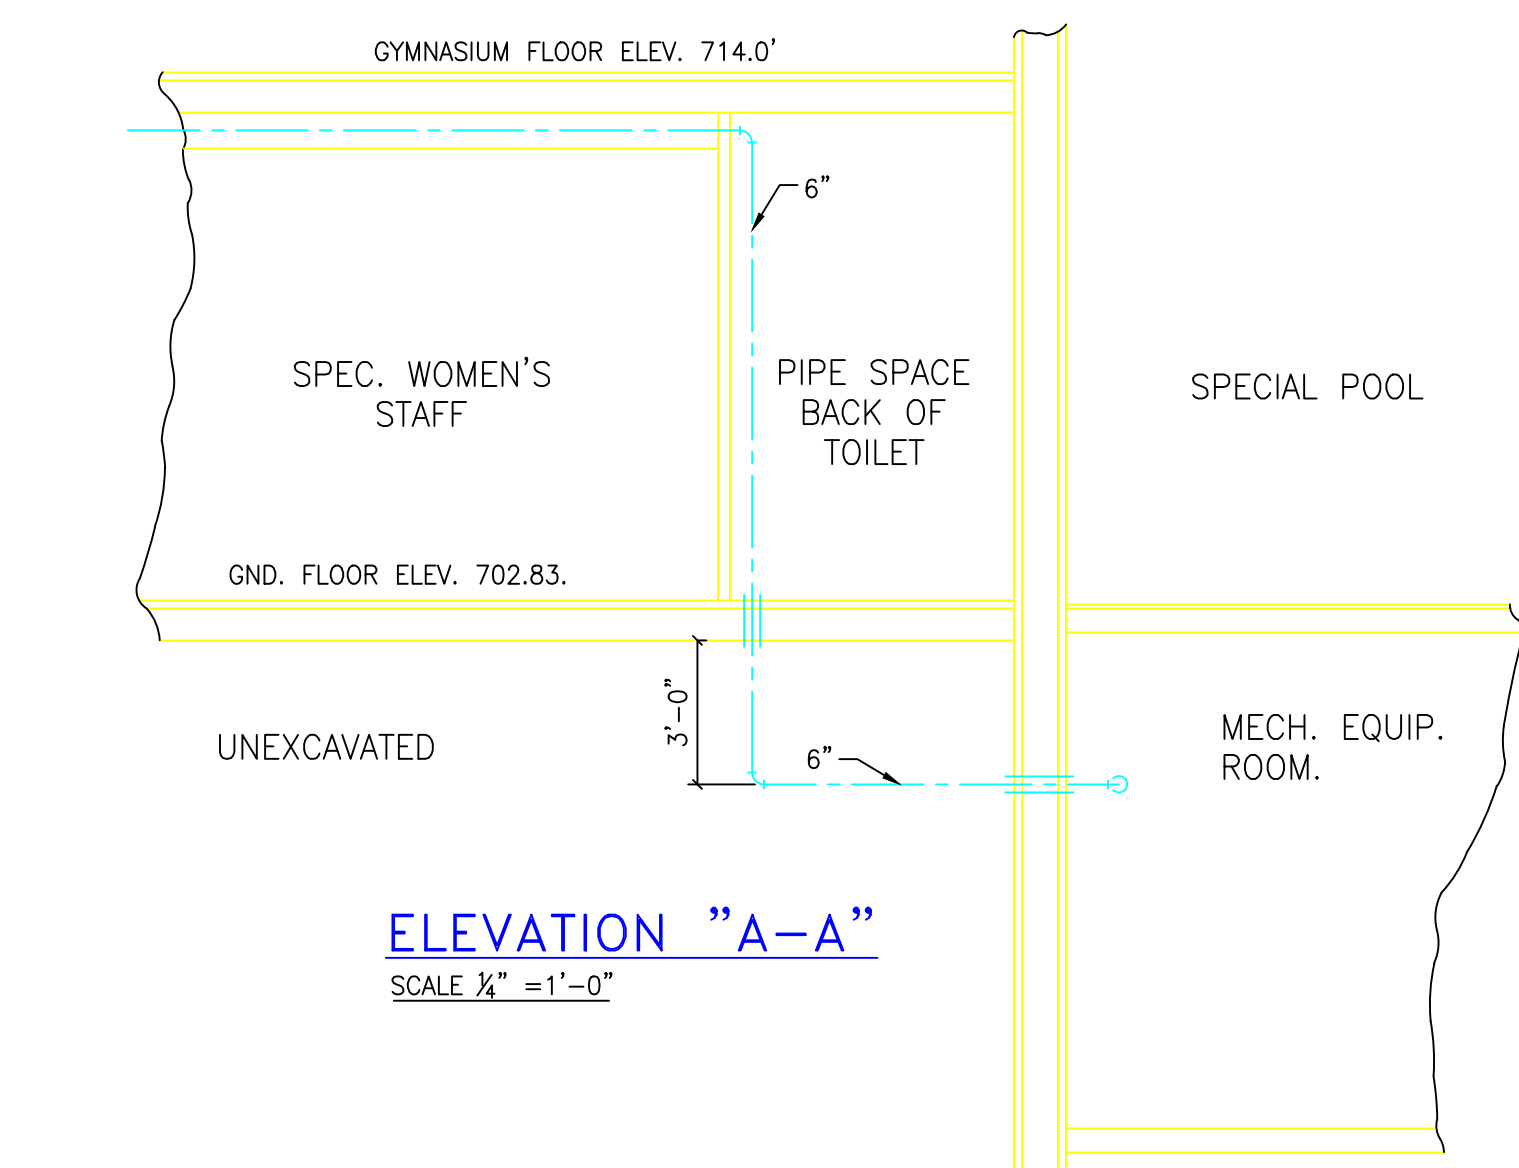


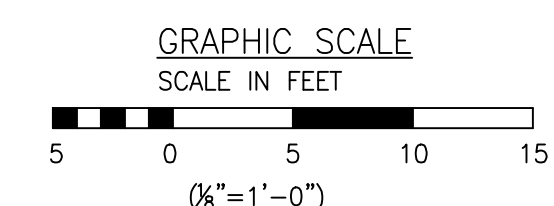

GROUND FLOOR PLAN
LIBRARY, GYMNASIUM & SWIMMING POOL WING

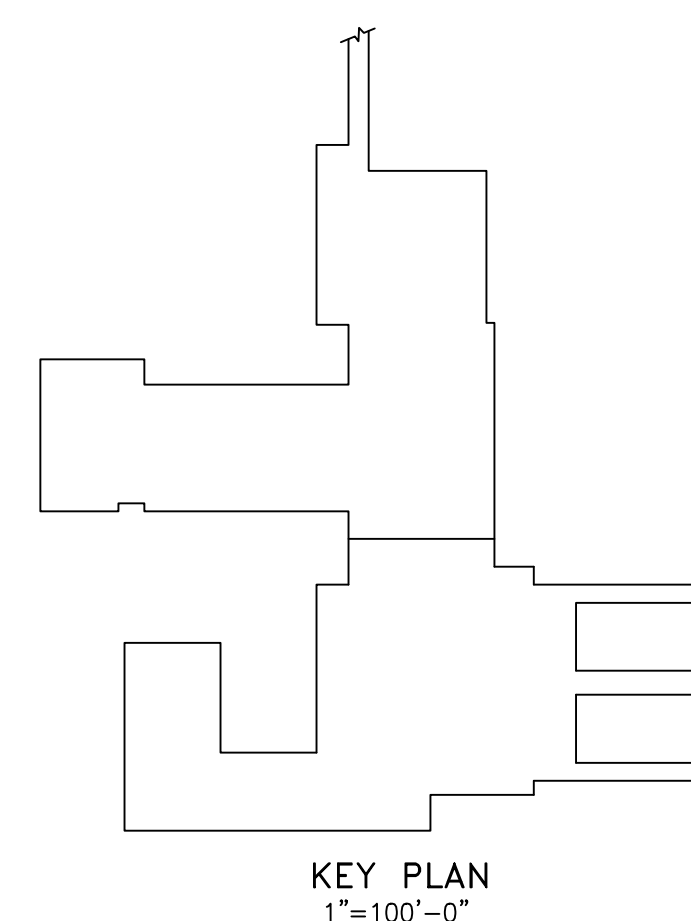

- NOTES:
1. WATER, D.W., & FIRE LINE SUPPLY MAINS SHOWN ON THIS PLAN ARE LOCATED IN THE GROUND FLOOR CEILING UNLESS OTHERWISE NOTED. WASTE LINES ARE BELOW THE GROUND FLOOR.
 2. FOR PIPE SIZES NOT SHOWN, SEE WATER AND WASTE & VENT ISOMETRIC DIAGRAMS.
 3. DOWN SPOUTS MARKED (X) SHALL HAVE A CAST IRON BOOT EXTENDING 6'-0" ABOVE FINISHED GRADE.

BLOC 6	
REVISION	DATE
WALTER HOOK & ASSOCIATES, INC. CHARLOTTE, NORTH CAROLINA WM. HENLEY DEITRICK, INC. RALEIGH, NORTH CAROLINA WM. C. OLSEN RALEIGH, NORTH CAROLINA ARCHITECTS, ENGINEERS IN ASSOCIATION WITH NEERGAARD, CRAIG & McCAGG HOSPITAL CONSULTANTS-NEW YORK, N.Y.	
CORPS OF ENGINEERS U.S. ARMY CHARLESTON DISTRICT CHARLESTON, S.C.	
VETERANS ADMINISTRATION HOSPITAL SALISBURY, NORTH CAROLINA 960 BED NP HOSPITAL RECREATION BUILDING GROUND FLOOR PLUMBING PLAN (LIBRARY WING)	
TRACED BY: TCB	DATE: DEC. 9, 1949
CHECKED BY: ORB	CIV. ENG.-38-081-50
SUBMITTED: COL	SCALE: AS NOTED
APPROVED:	SPEC. NO.
CHIEF ENGINEER	LT. COL. C. E. DISTRICT ENGINEER
V.A. PROJECT NO.2448	DRAWING NUMBER VA44-31-11-P1
	NUMBER OF SHEETS 122