



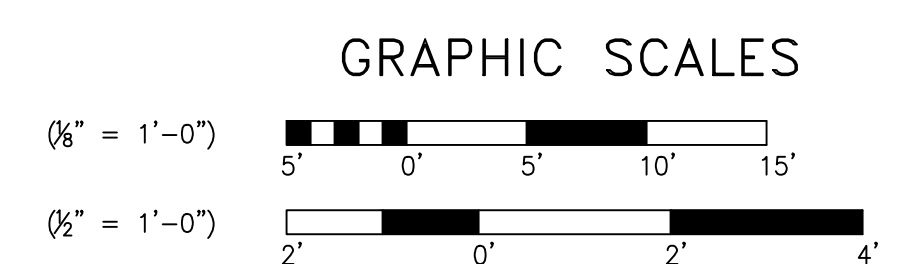

CONVECTOR SCHEDULE

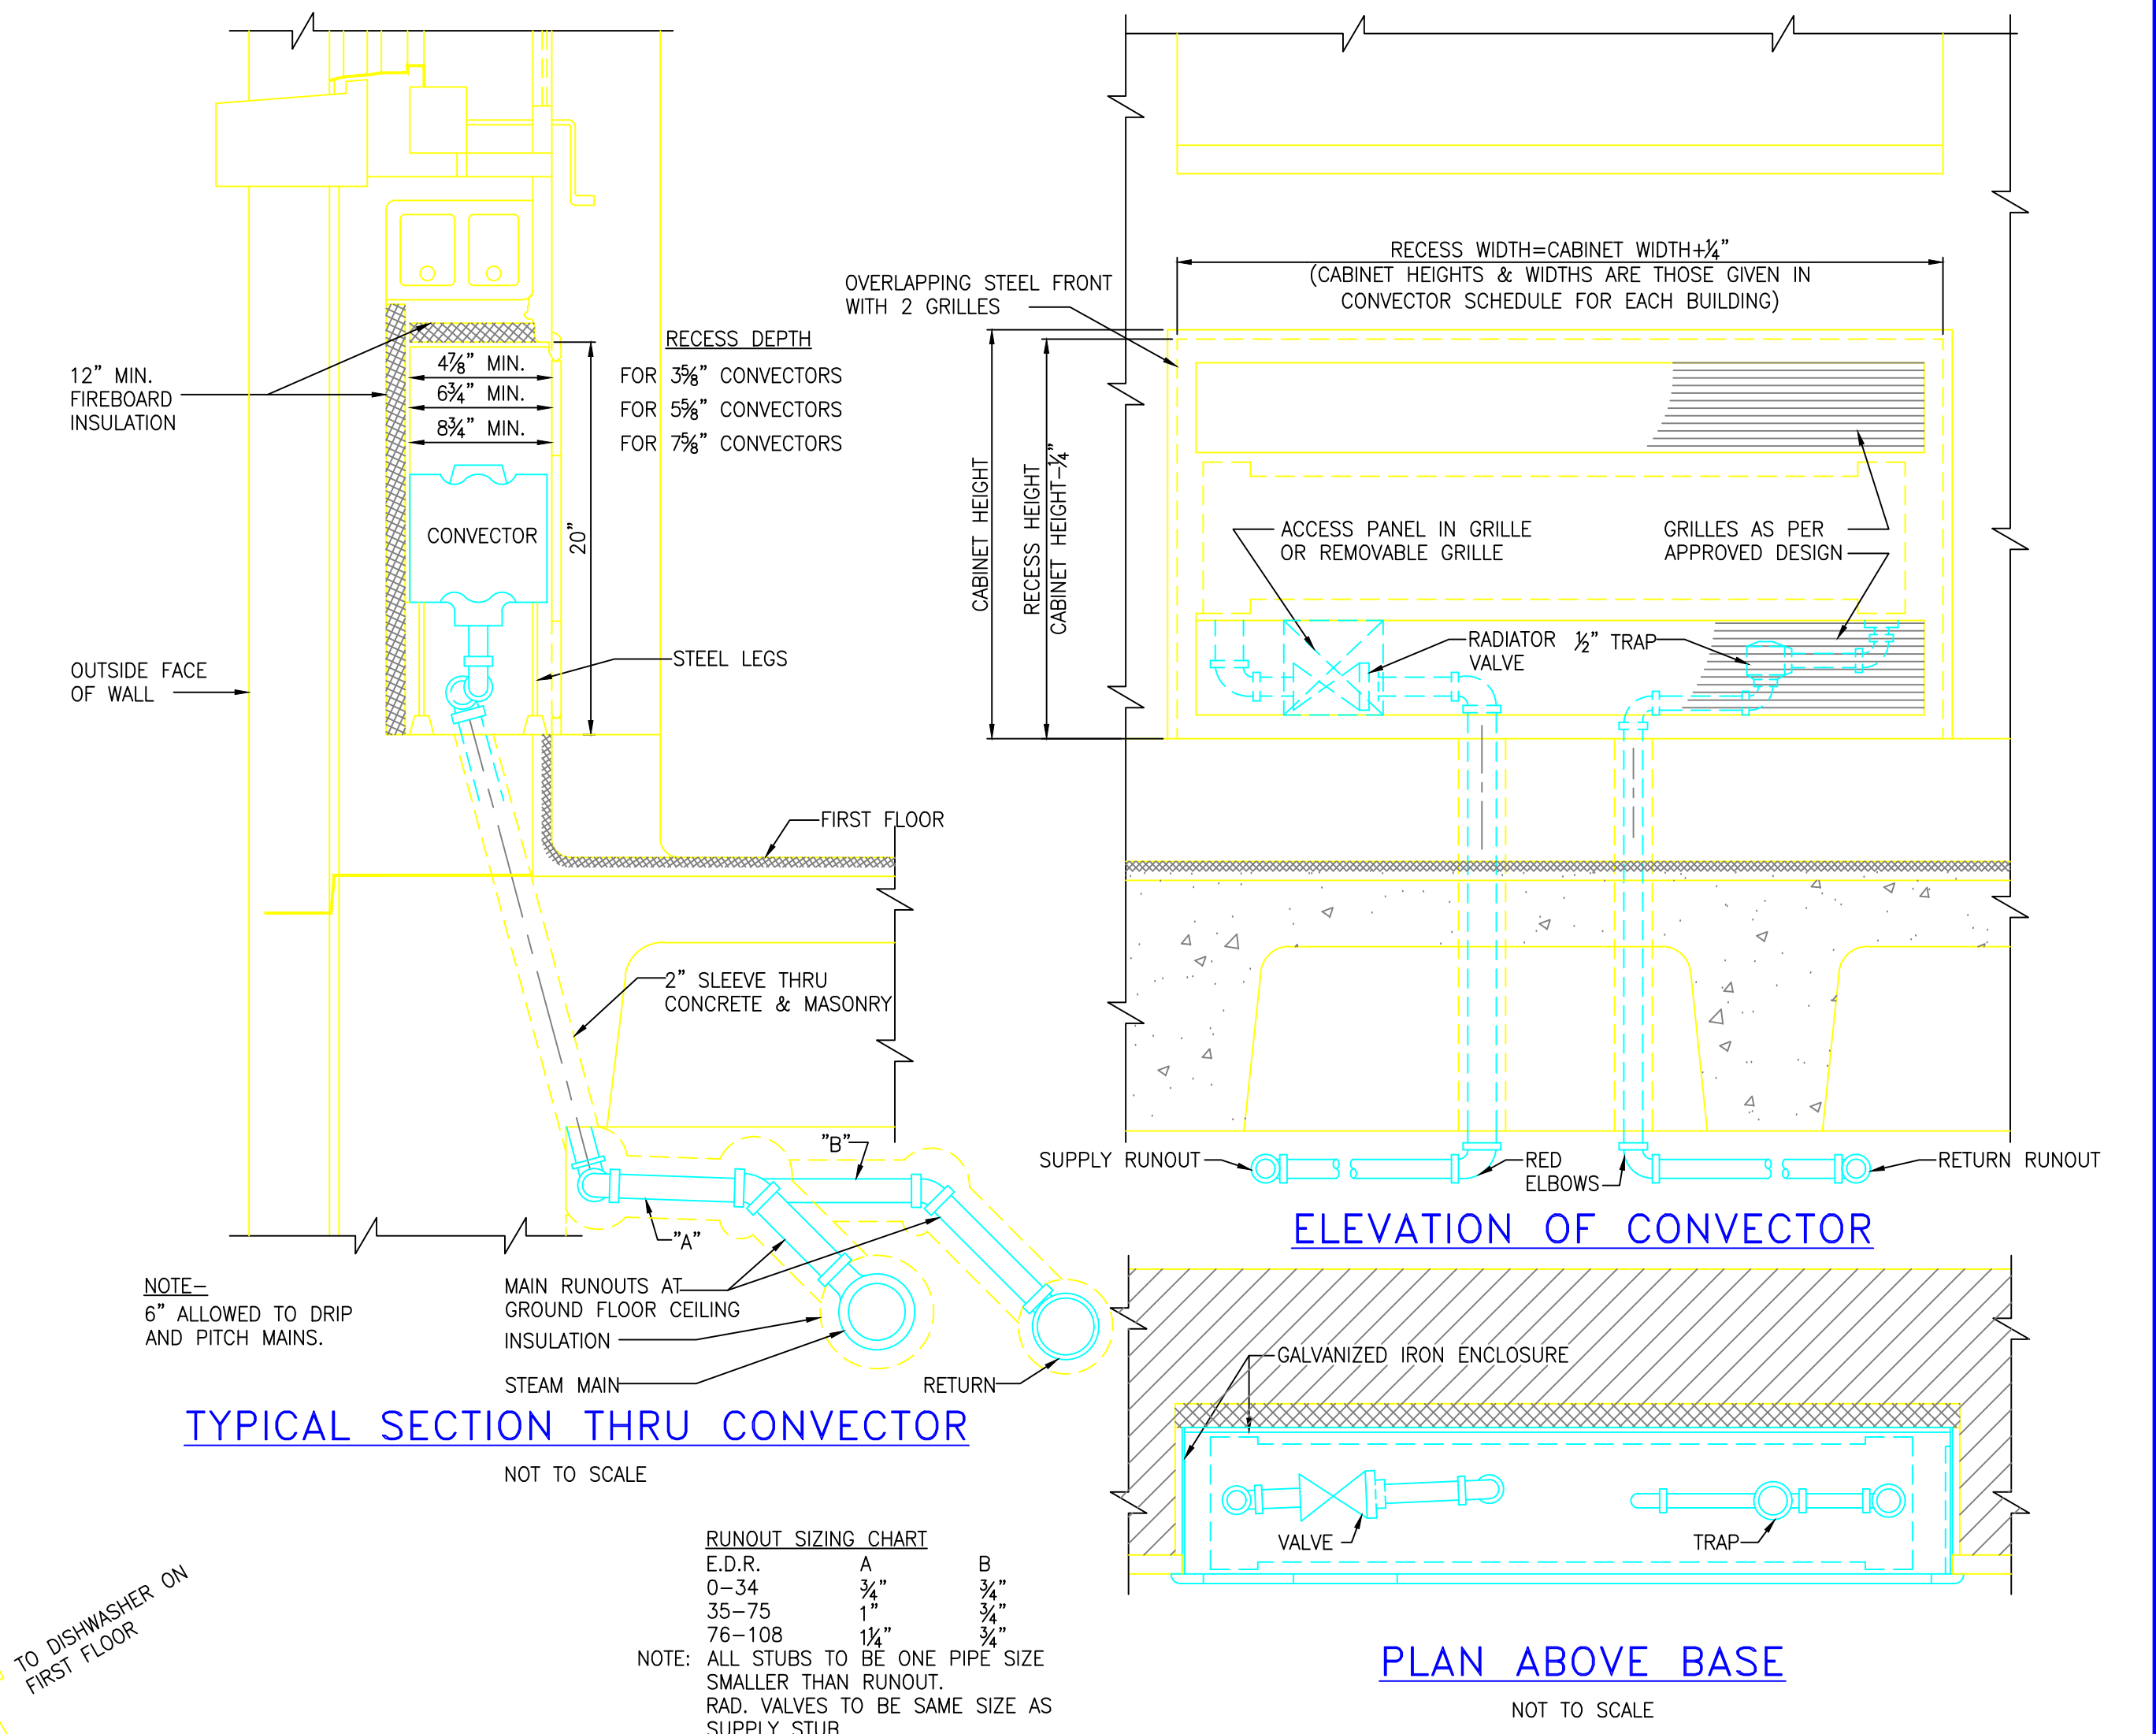

REVISION	DATE	DESCRIPTION	BY
WALTER HOOK & ASSOCIATES, INC. CHARLOTTE, NORTH CAROLINA W.W. HENLEY, DETRICK, INC. RALEIGH, NORTH CAROLINA W.M. C. DOLSEN RALEIGH, N. CAROLINA ARCHITECTS - ENGINEERS IN ASSOCIATION WITH NEERDAARD, CRAIG & MCCAGG HOSPITAL CONSULTANTS - NEW YORK, N.Y.			
DRAWN BY: <u>L.C.</u> TRACED BY: <u>J.S.</u> CHECKED BY: <u>J.S.</u> SUBMITTED: <u>JUN.</u>		VETERANS ADMINISTRATION HOSPITAL SALISBURY, NORTH CAROLINA 960 BED, NON HOSPITAL G. M. & S. BLDG RIGHT WING - GROUND & FIRST FLOOR HEATING & VENTILATING PLANS	
APPROVED:	APPROVED:	DATE:	
		DEC. 9, 1949	
CHIEF ENGINEER	L.T. COL. C. E. DISTRICT ENGINEER	CIV. ENG.-38-08T-50	
SCALE		SPEC. NO.	NUMBER OF SHEETS IN SET
DRAWING NUMBER V444-32-05-H2			773/177