



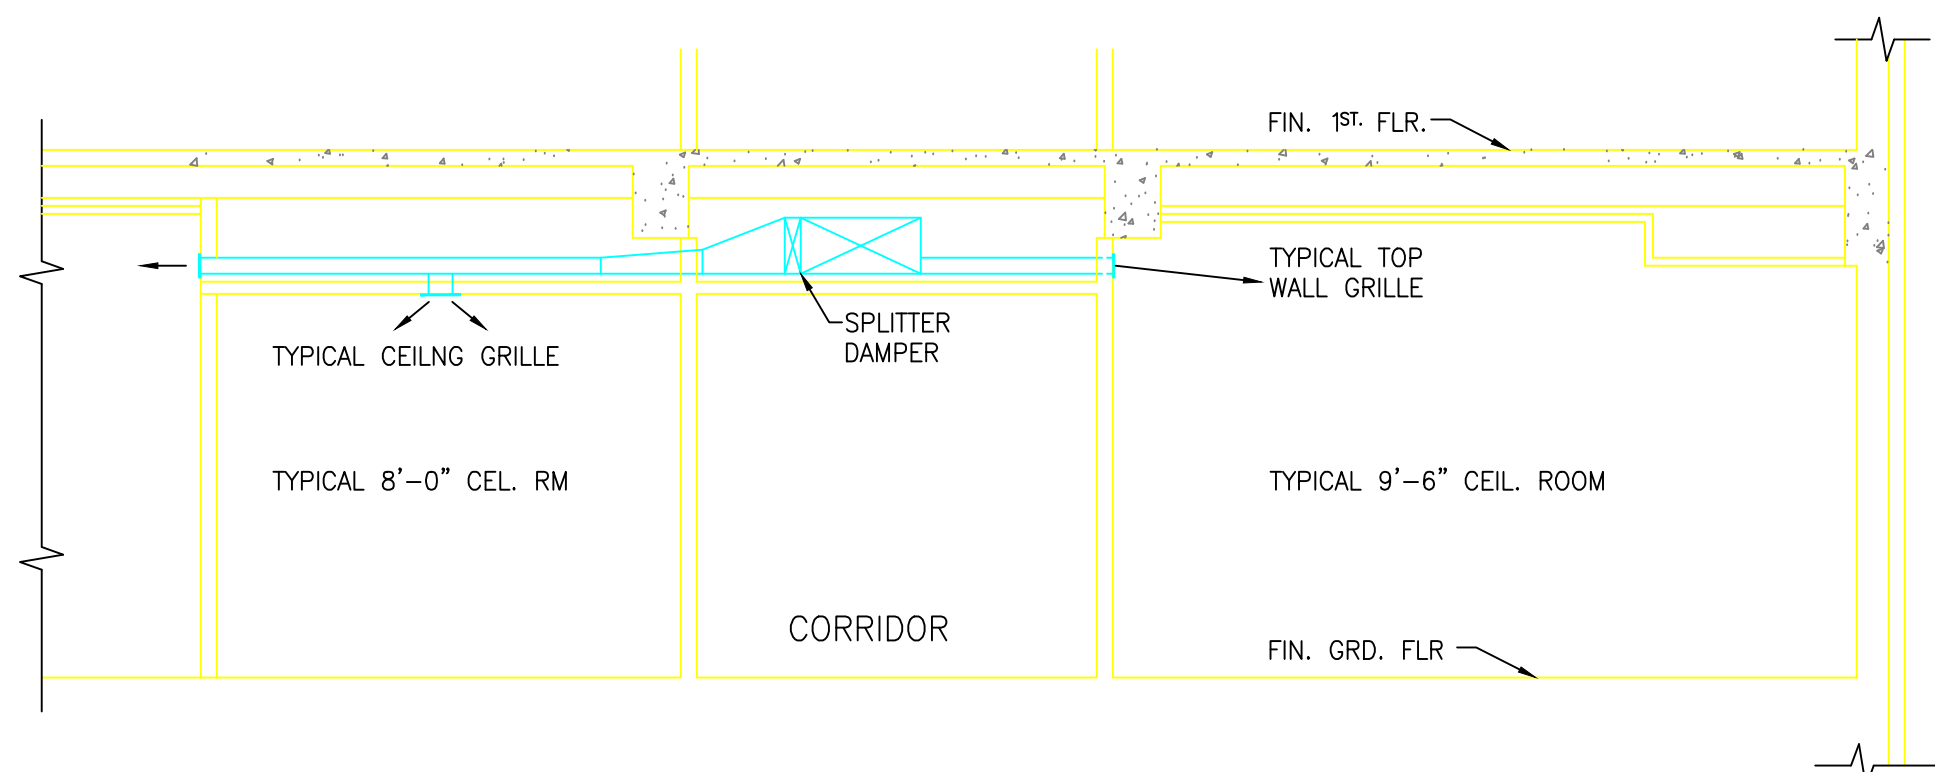


TYPICAL SECTION—GROUND FLOOR CORRIDOR

SCALE: 1/4"=1'-0"

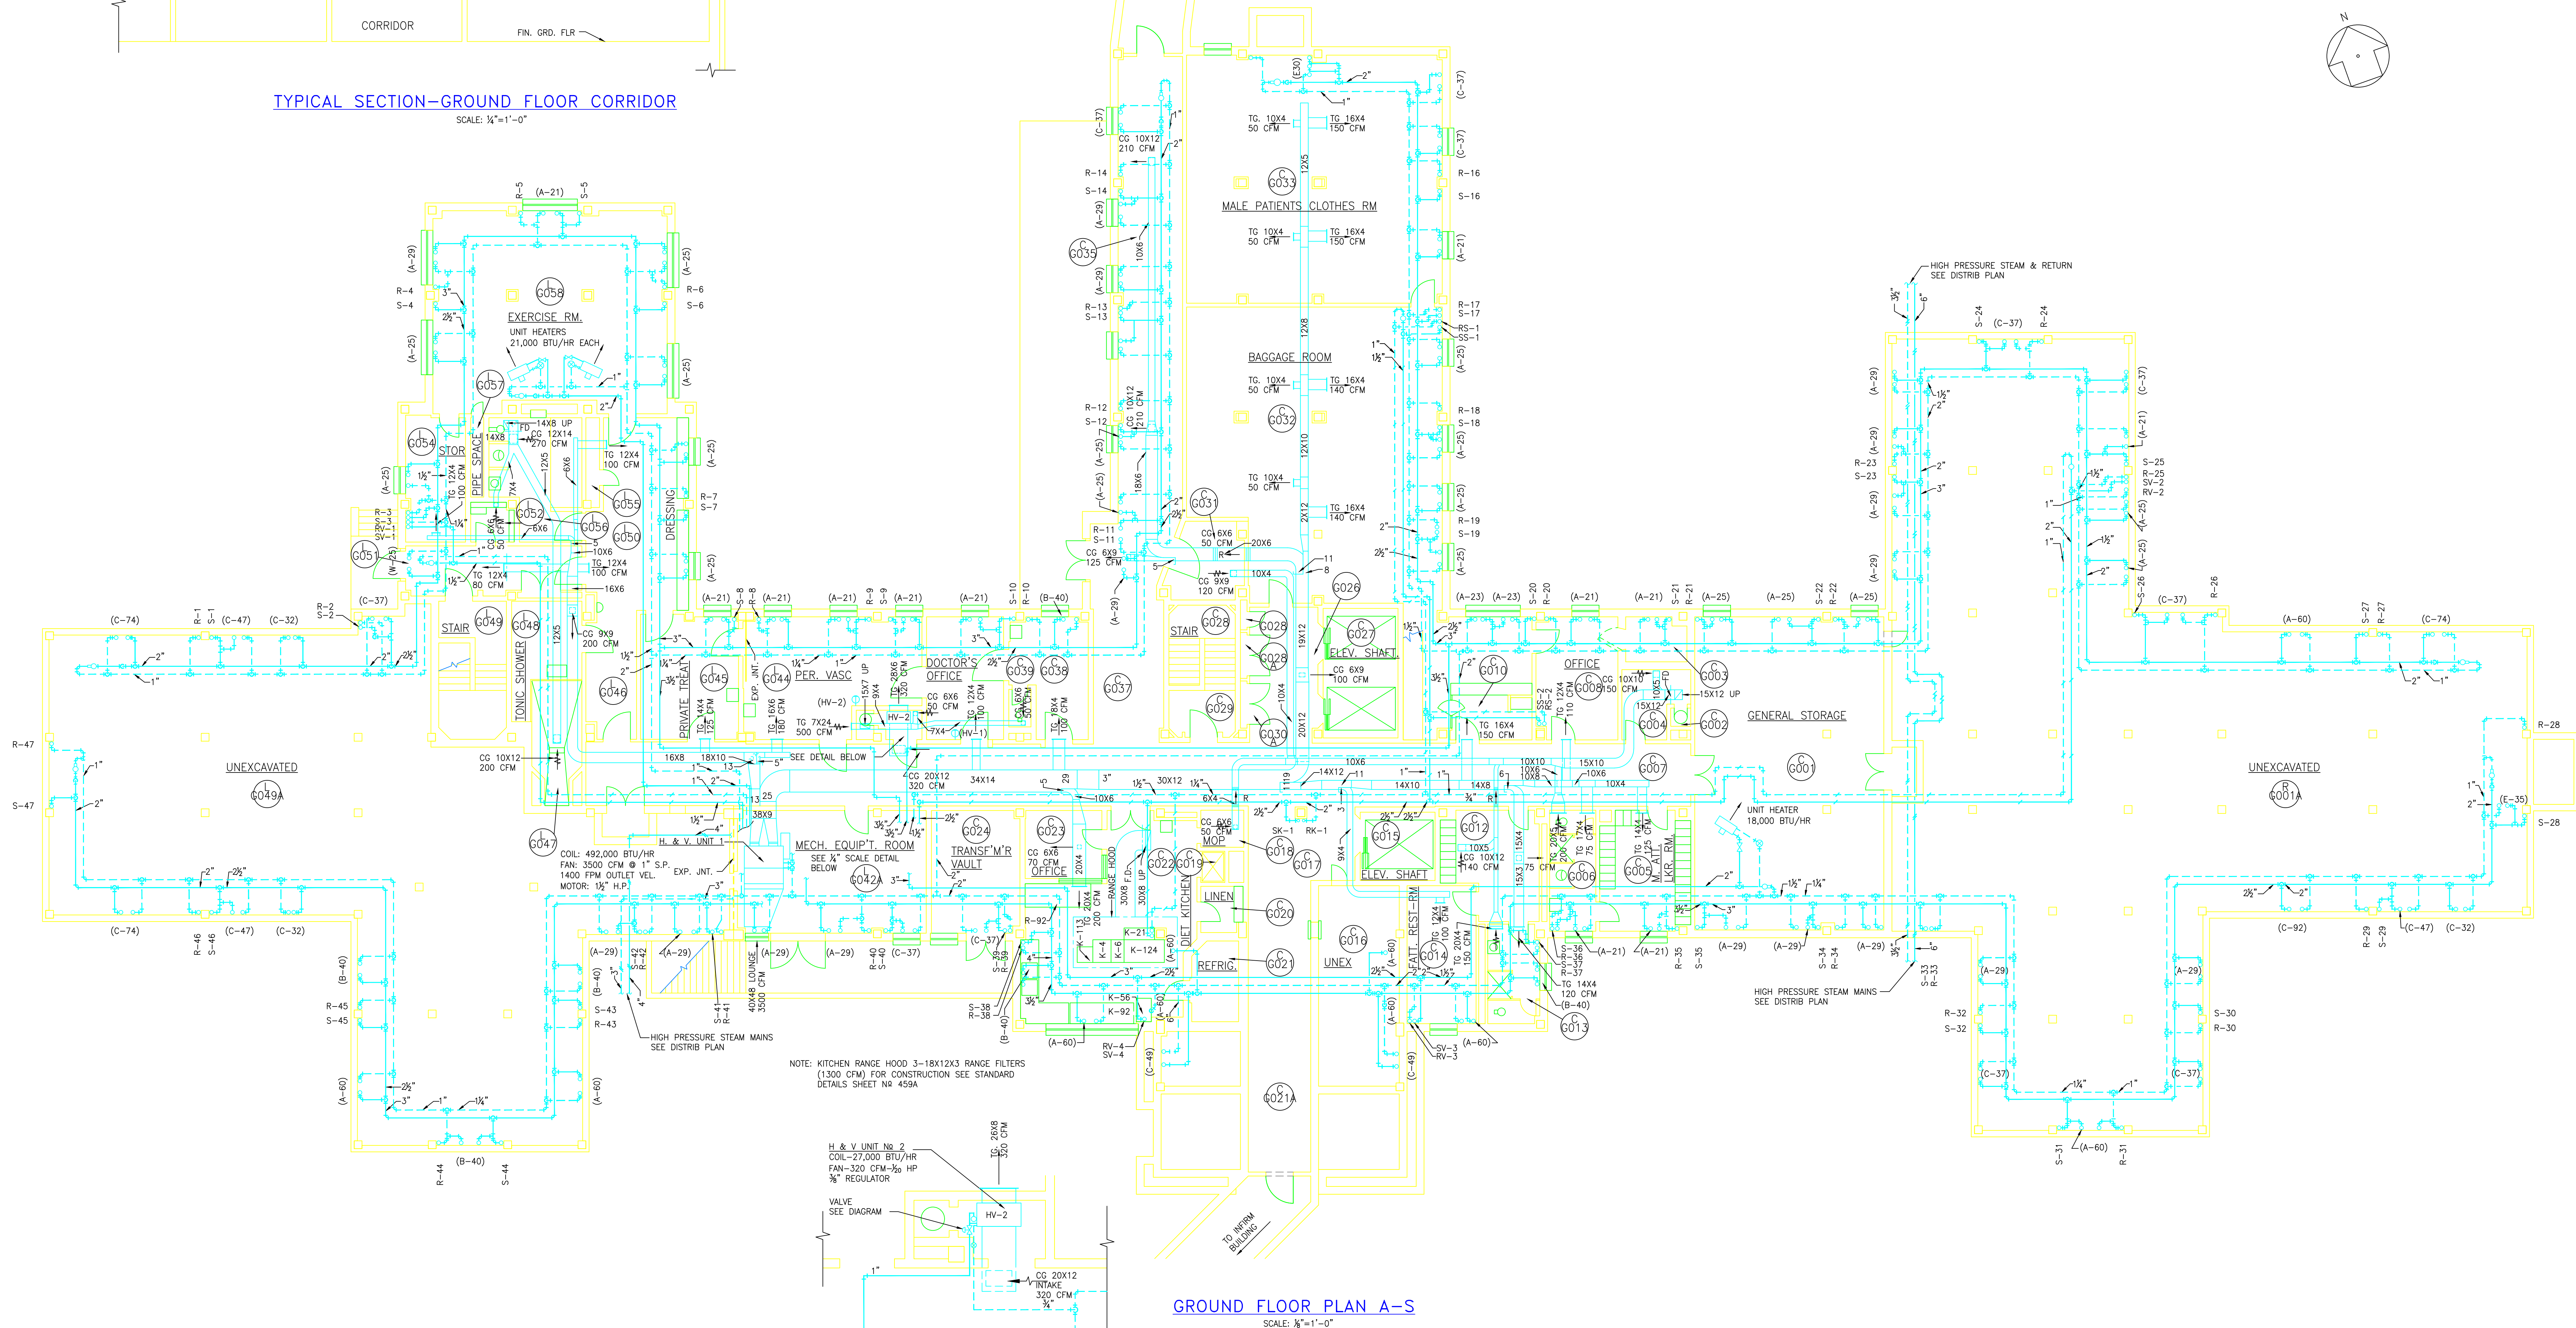

GROUND FLOOR PLAN A-S

SCALE: 1/8"=1'-0"


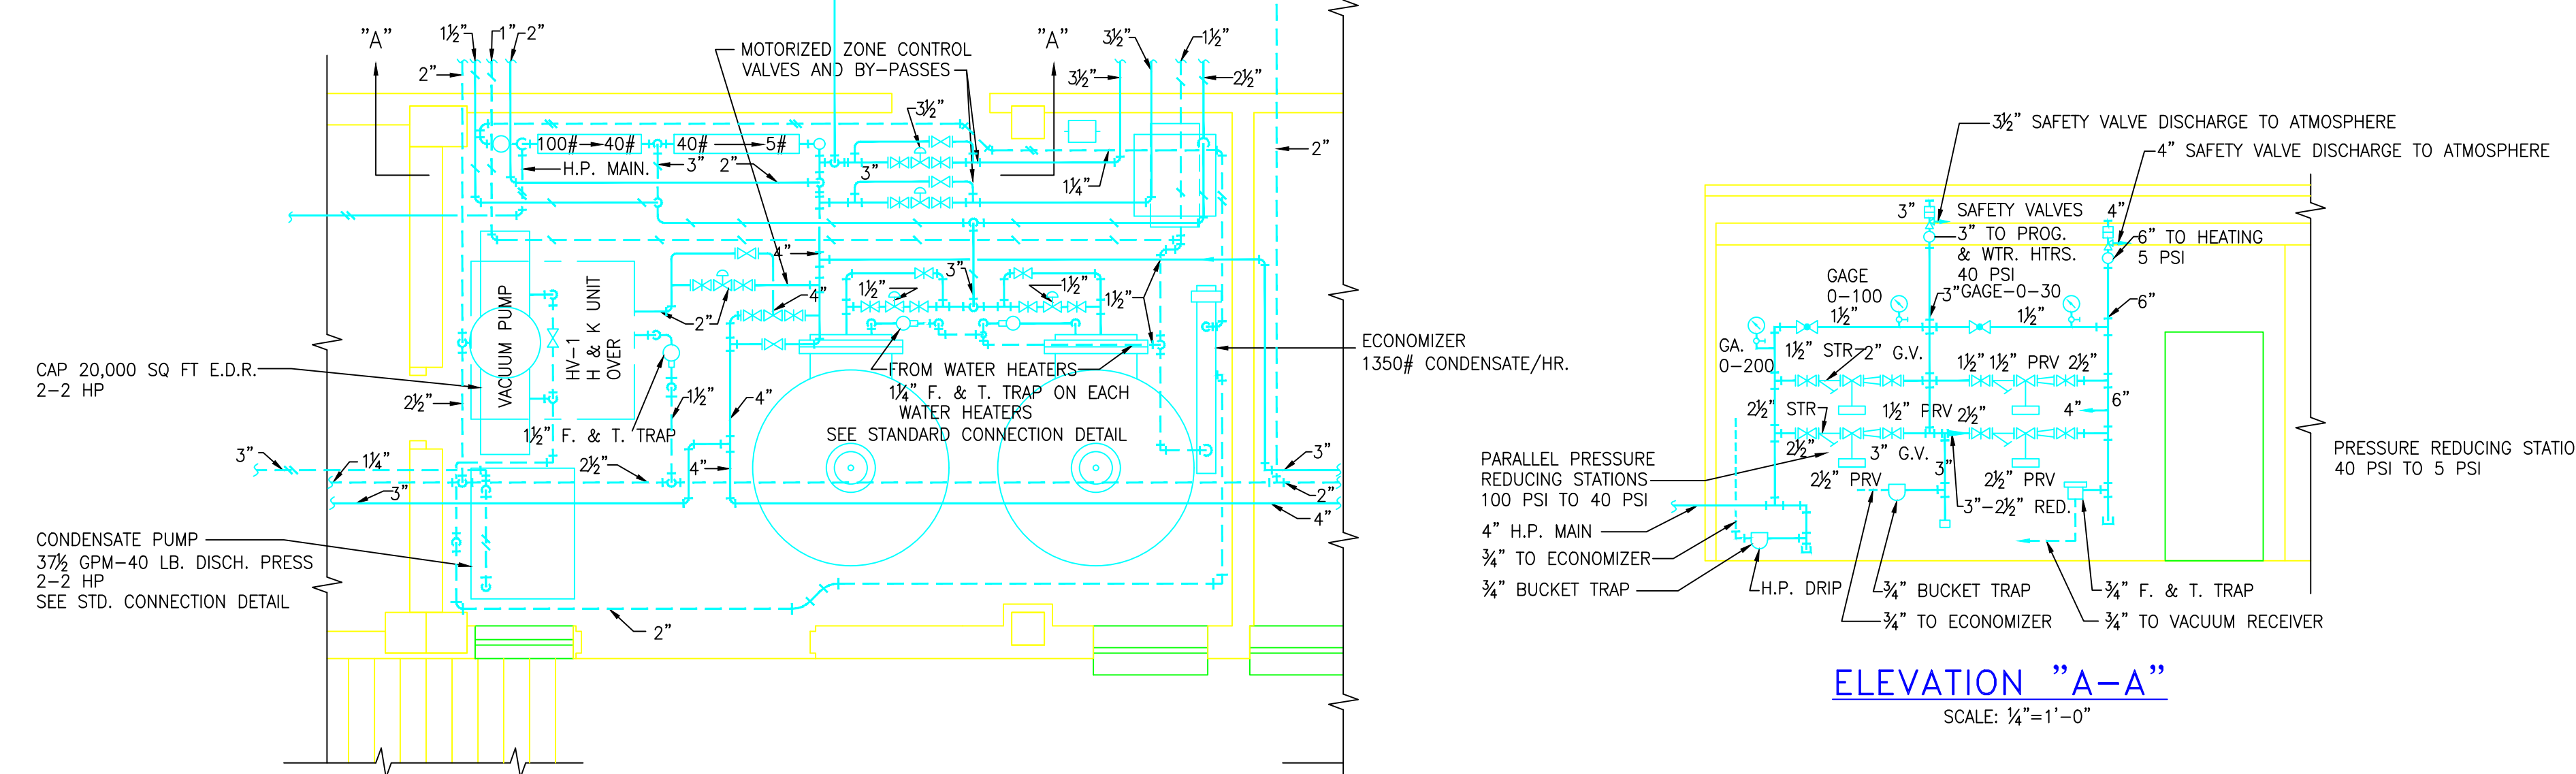


PLAN OF MECHANICAL EQUIPMENT ROOM

SCALE: 1/4"=1'-0"

ELEVATION "A-A"

SCALE: 1/4"=1'-0"

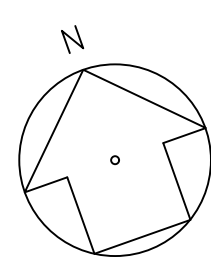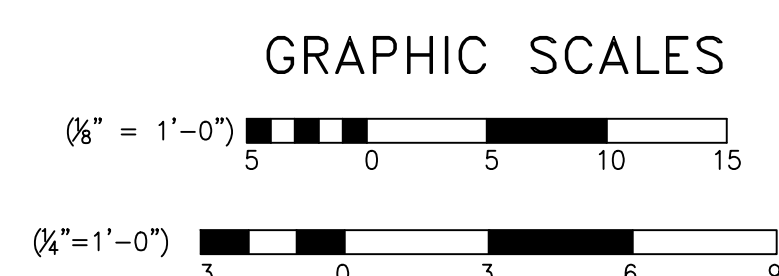

BLDG-4

REVISION		DATE	DESCRIPTION	BY
WALTER HOOK & ASSOCIATES, INC.				
CHARLOTTE, NORTH CAROLINA				
W.M. HENLEY DEITRICK, INC.				
RALEIGH, NORTH CAROLINA			CORPS OF ENGINEERS	
W.M. C. OLSEN			U. S. ARMY	
RALEIGH, N. CAROLINA			CHARLESTON DISTRICT	
ARCHITECTS-ENGINEERS			CHARLESTON, S.C.	
IN ASSOCIATION WITH				
NEERGAARD, CRAIG & MCCAGG				
HOSPITAL CONSULTANTS - NEW YORK, N.Y.				
DRAWN BY:	J.N.	VETERANS ADMINISTRATION HOSPITAL		
TRACED BY:	R.R.C.	SALISBURY NORTH CAROLINA		
CHECKED BY:	L.C.	960 BED NP HOSPITAL		
SUBMITTED:		ADMISSION BLDG (S)		
APPROVED:		GROUND FLOOR HEATING & VENTILATING PLAN		
		DATE:	DEC. 9, 1949	
CHIEF ENGINEER	L.T. COL. C. E. DISTRICT ENGINEER	CIV. ENG.-38-081-50	SPEC. NO.	
SCALE		DRAWING NUMBER		
V.A. PROJECT NO. 2448		VA44-32-15-H1		NUMBER OF SHEETS IN SET 303/471