


3/23/2026 11:06:42 AM AE121
C:\Users\cearl\Documents\227103.25_BLDG80_ARCHITECTURAL-V23_cearl\HCLDR.rvt

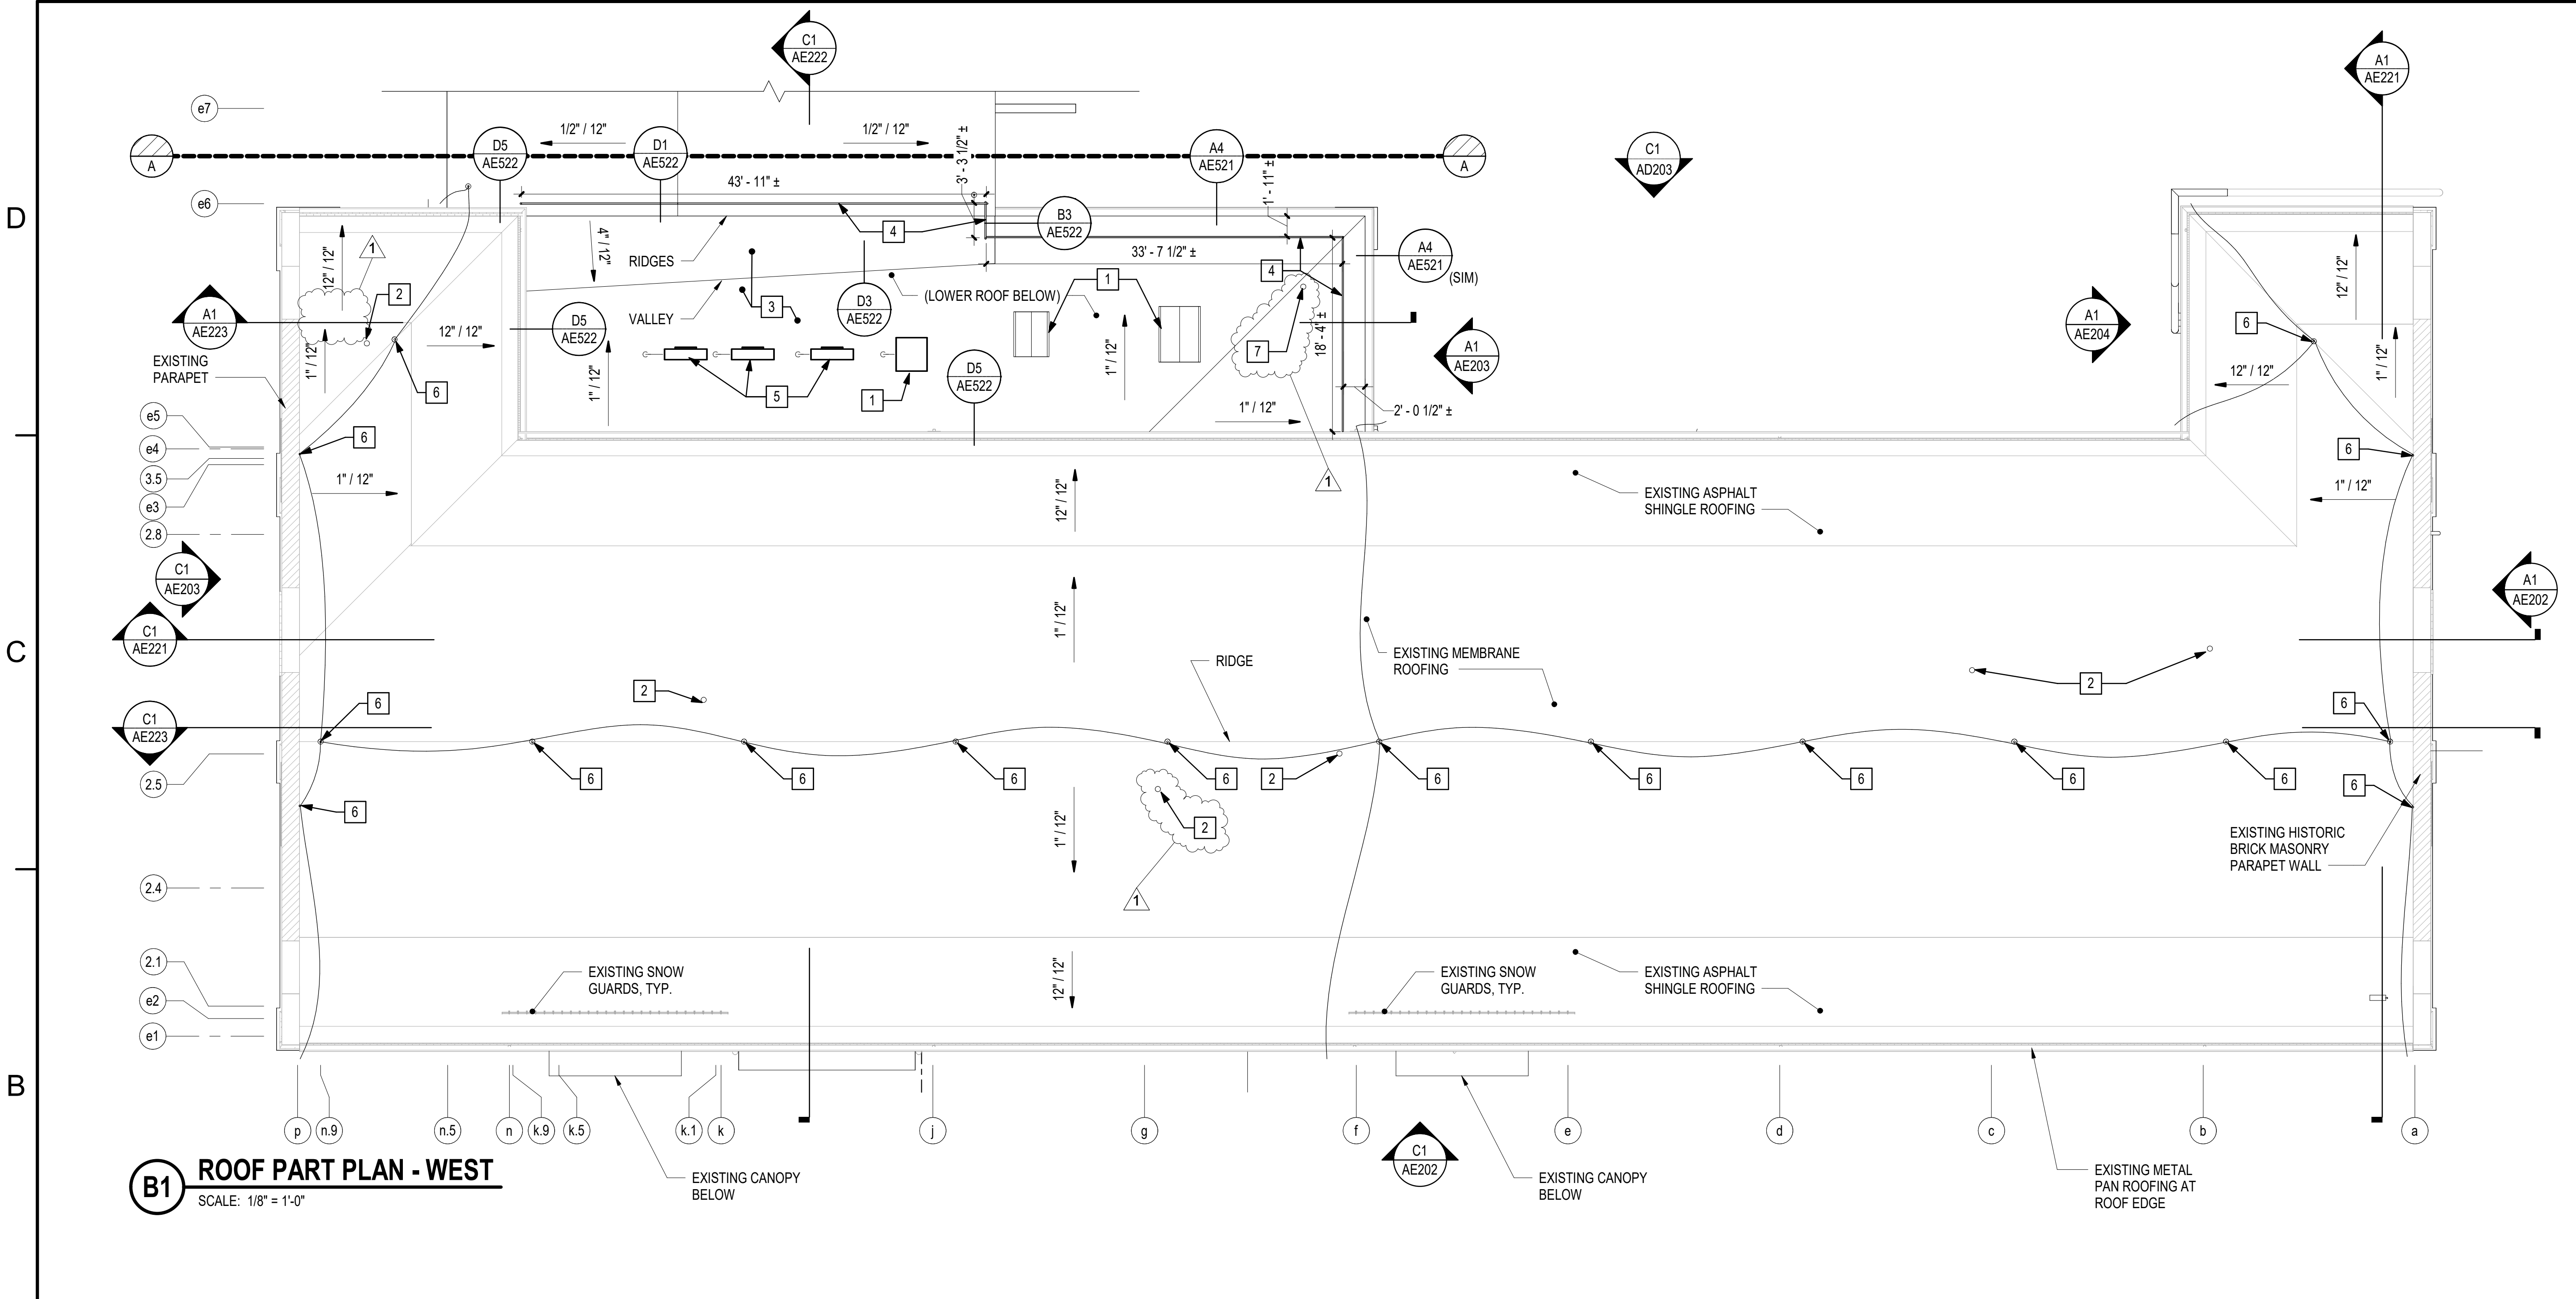

B1 ROOF PART PLAN - WEST
SCALE: 1/8" = 1'-0"


GENERAL NOTES

1. SEE SHEET G-004A FOR GENERAL CONSTRUCTION NOTES.

KEYNOTES

- 1 MECHANICAL EQUIPMENT CURB, SEE MECHANICAL SHEETS AND DETAIL A1/AE521.
- 2 VENT THROUGH ROOF, SEE DETAIL D1/AE521.
- 3 MEMBRANE ROOF SYSTEM, SEE DETAIL B4/AE521
- 4 REINSTALL BALLASTED FALL PROTECTION RAILING SYSTEM COORDINATE CONFIGURATION WITH CONTRACTING OFFICER.
- 5 MECHANICAL EQUIPMENT, SEE MECHANICAL SHEETS AND DETAILS A2/AE521 (PITCH POCKET) AND B1/AE522 (SLEEPER).
- 6 LIGHTNING PROTECTION TERMINAL AND CONDUCTOR, SEE DETAILS A1/AE522 AND B5/AE522 AND ELECTRICAL SHEETS.
- 7 VENT THROUGH ROOF, SEE DETAIL B1/AE521.

KEY PLAN

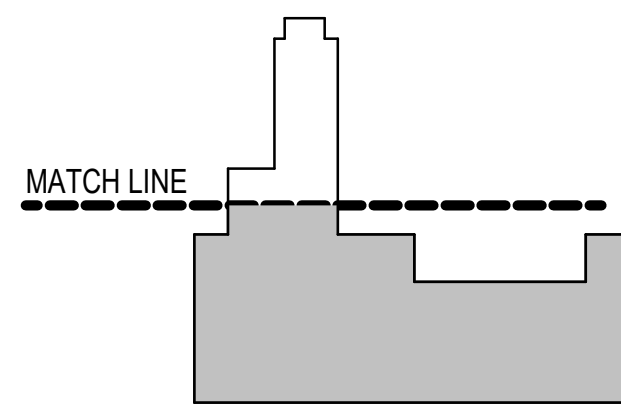

GRAPHIC SCALE(S)



APPROVED		DATE	APR
FOR COMMANDER NAVFAC		DATE	APR
ACTIVITY		DATE	APR
SATISFACTORY TO DATE		DATE	APR
DESIGNER JMR		DATE	APR
DRAWN BY MJD		DATE	APR
CHECKED BY RSH		DATE	APR
DESIGN MANAGER T. CARLETON		DATE	APR
PROJECT MANAGER L. LYONS		DATE	APR
HEADPRAISE		DATE	APR
FIRE PROTECTION S. RUCINSKI		DATE	APR
NAVAL FACILITIES ENGINEERING SYSTEMS COMMAND - MID-ATLANTIC		DATE	APR
PORTSMOUTH NAVAL SHIPYARD - KITTEERY, ME		DATE	APR
B60 REPAIRS		DATE	APR
ROOF PART PLAN - WEST		DATE	APR
PROJECT NO. 1740579		DATE	APR
NAV-FAC DRAWINGS NO.		DATE	APR
SHEET 101 OF 282		DATE	APR
AE121		DATE	APR
DRAWING REVISION: 14 SEP 2023		DATE	APR