


3/16/2026 9:53:27 AM AE104
C:\Users\mdonovan\Documents\22103_25_BLDG90_ARCHITECTURAL-V23_mdonovan8VPXR.rvt

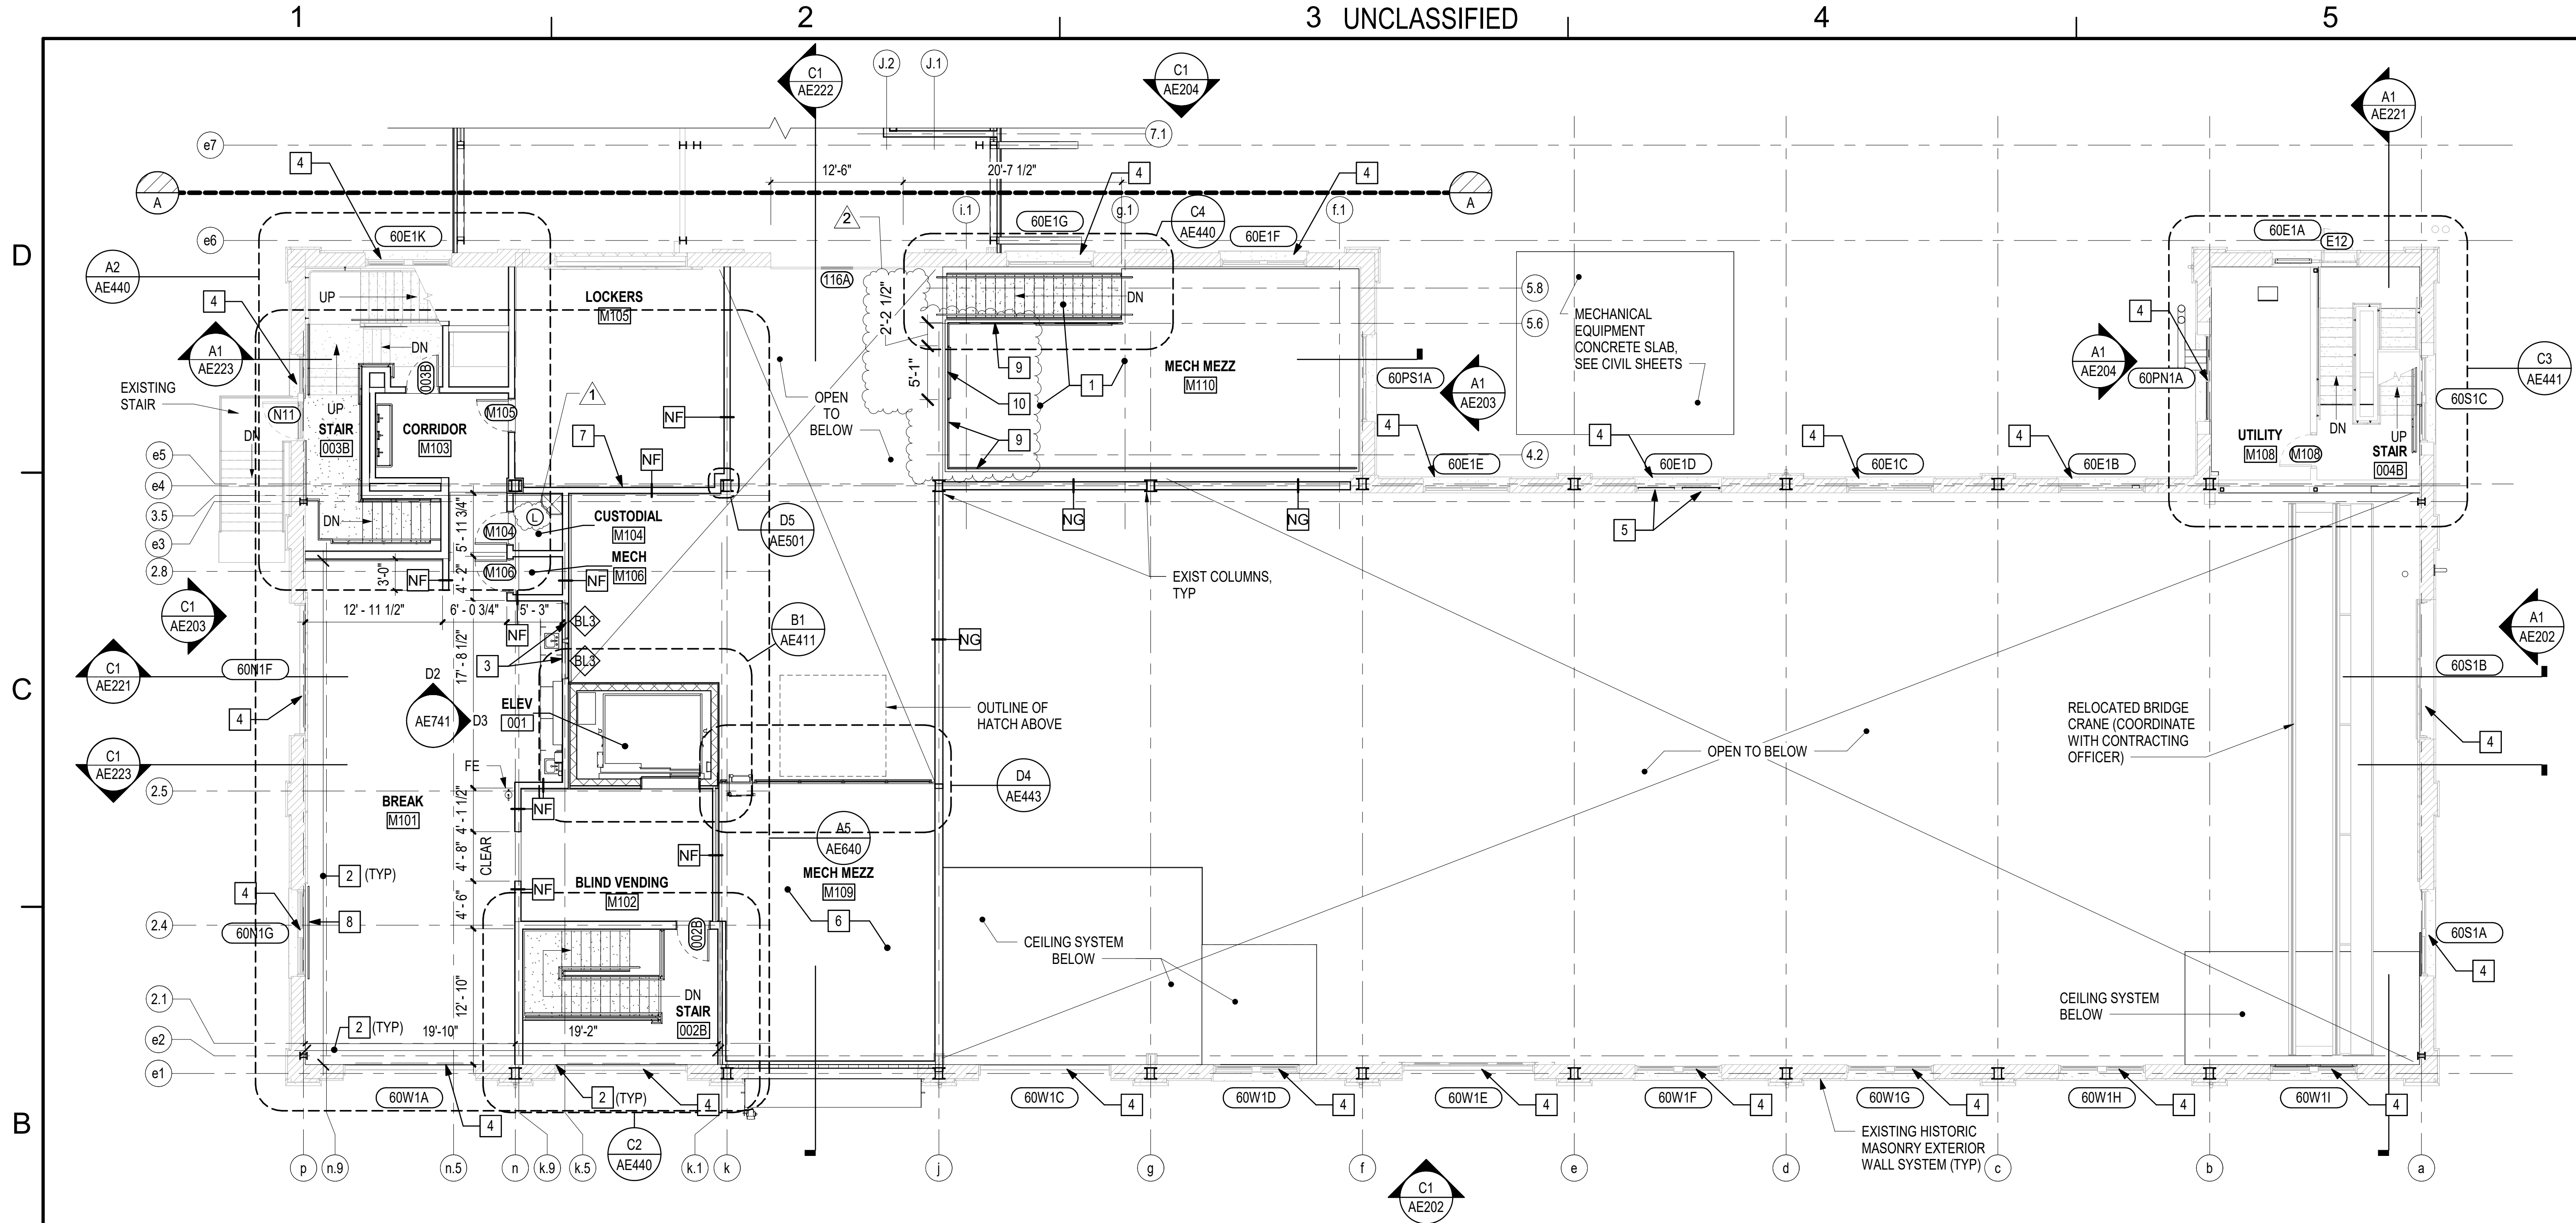

B1 FIRST FLOOR MEZZANINE PART PLAN - WEST
SCALE: 1/8" = 1'-0"


GENERAL NOTES

- SEE SHEET AE101 FOR GENERAL NOTES.
- B59 WILL BE OCCUPIED DURING CONTRACTING. COORDINATE WORK PLAN AND ACCESS WITH CONSTRUCTION OFFICER.
- IN ADDITION TO THE AREAS INDICATED, PROVIDE 200 SF OF PATCH AND REPAIR WOOD FLOOR WORK FOR WORK NOT OTHERWISE INDICATED IN THE DRAWINGS. LOCATIONS TO BE COORDINATED WITH THE CONTRACTING OFFICER, PLANS, SPECIFICATIONS, AND REPORTS. THE QUANTITIES INDICATED IN PLANS AND SPECIFICATIONS AND NOTED ABOVE ARE TO BE INCLUDED IN THE LUMP SUM BASE BID LINE ITEM.


KEYNOTES (THIS SHEET ONLY)

- MEZZANINE PLATFORM AND STAIRS, SEE STRUCTURAL SHEETS.
- PERIMETER EXPANSION JOINT, SEE DETAILS C1 AND C3 ON SHEET AE530.
- INSTALL SALVAGED HISTORIC BORROWED LIGHTS.
- REPAIR HISTORIC WOOD WINDOW/DOOR, SEE RESTORATION SCHEDULE ON SHEET AE622.
- MECHANICAL DUCT WINDOW PENETRATION, SEE DETAIL C3/AE621 AND COORDINATE WITH MECHANICAL SHEETS.
- 3/4" PLYWOOD FLOORING OVER METAL DECKING.
- PROVIDE BLOCKING IN STUD WALL FOR MECHANICAL EQUIPMENT AND SUPPORT BRACKETS, COORDINATE LOCATIONS WITH MECHANICAL SHEETS.
- GUARDRAIL SYSTEM, SEE DETAIL A4/AE626.
- GUARDRAIL SYSTEM, SEE DETAIL D1/AE445.
- PROVIDE REMOVABLE SECTION OF GUARDRAIL.

KEY PLAN

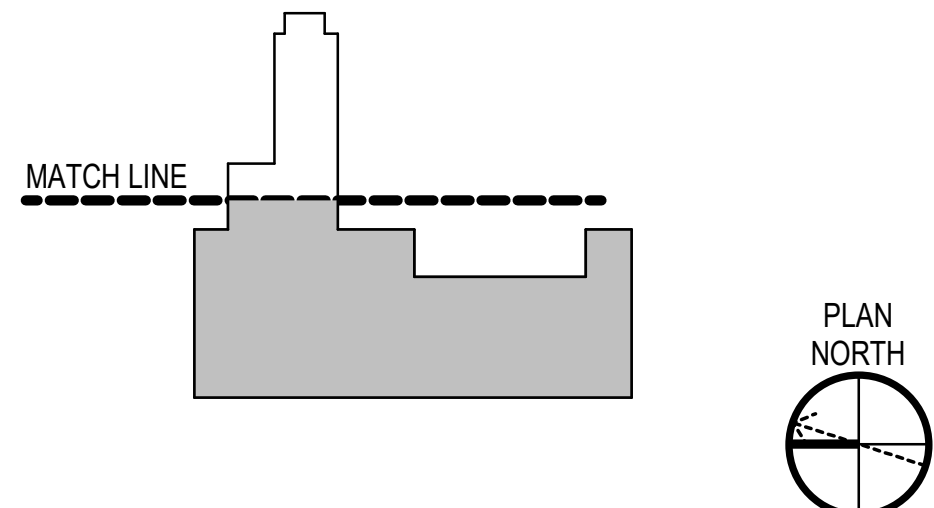

GRAPHIC SCALE(S)

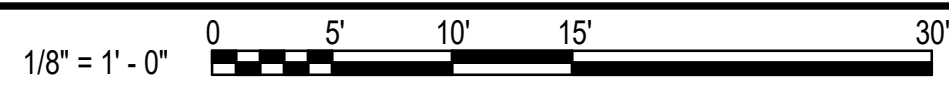

APPROVED	FOR COMMANDER NAVFAC	ACTIVITY
SATISFACTORY TO DATE	DESIGNER JMR	DRAWN BY MJD
CHECKED BY RSH	DESIGN MANAGER T. CARLETON	PROJECT MANAGER L. LYONS
READ/NAME	PREP/PROTECTION	S. RUCINSKI
NAVAL FACILITIES ENGINEERING SYSTEMS COMMAND - MID-ATLANTIC		
PORTSMOUTH NAVAL SHIPYARD - KITTEERY, ME		
B60 REPAIRS		
FIRST FLOOR MEZZANINE PART PLAN - WEST		
PROJECT NO. 1740579		
NAVFAC DRAWINGS NO.		
SHEET 95 OF 282		
AE104		
DRAWN/REVISION: 14 SEP 2023		