


3/10/2026 5:11:41 PM SF502
C:\Users\mdonovan\Documents\22103.25_BLDG60_STRUCTURAL-V23_mdonovan\FXR.rvt

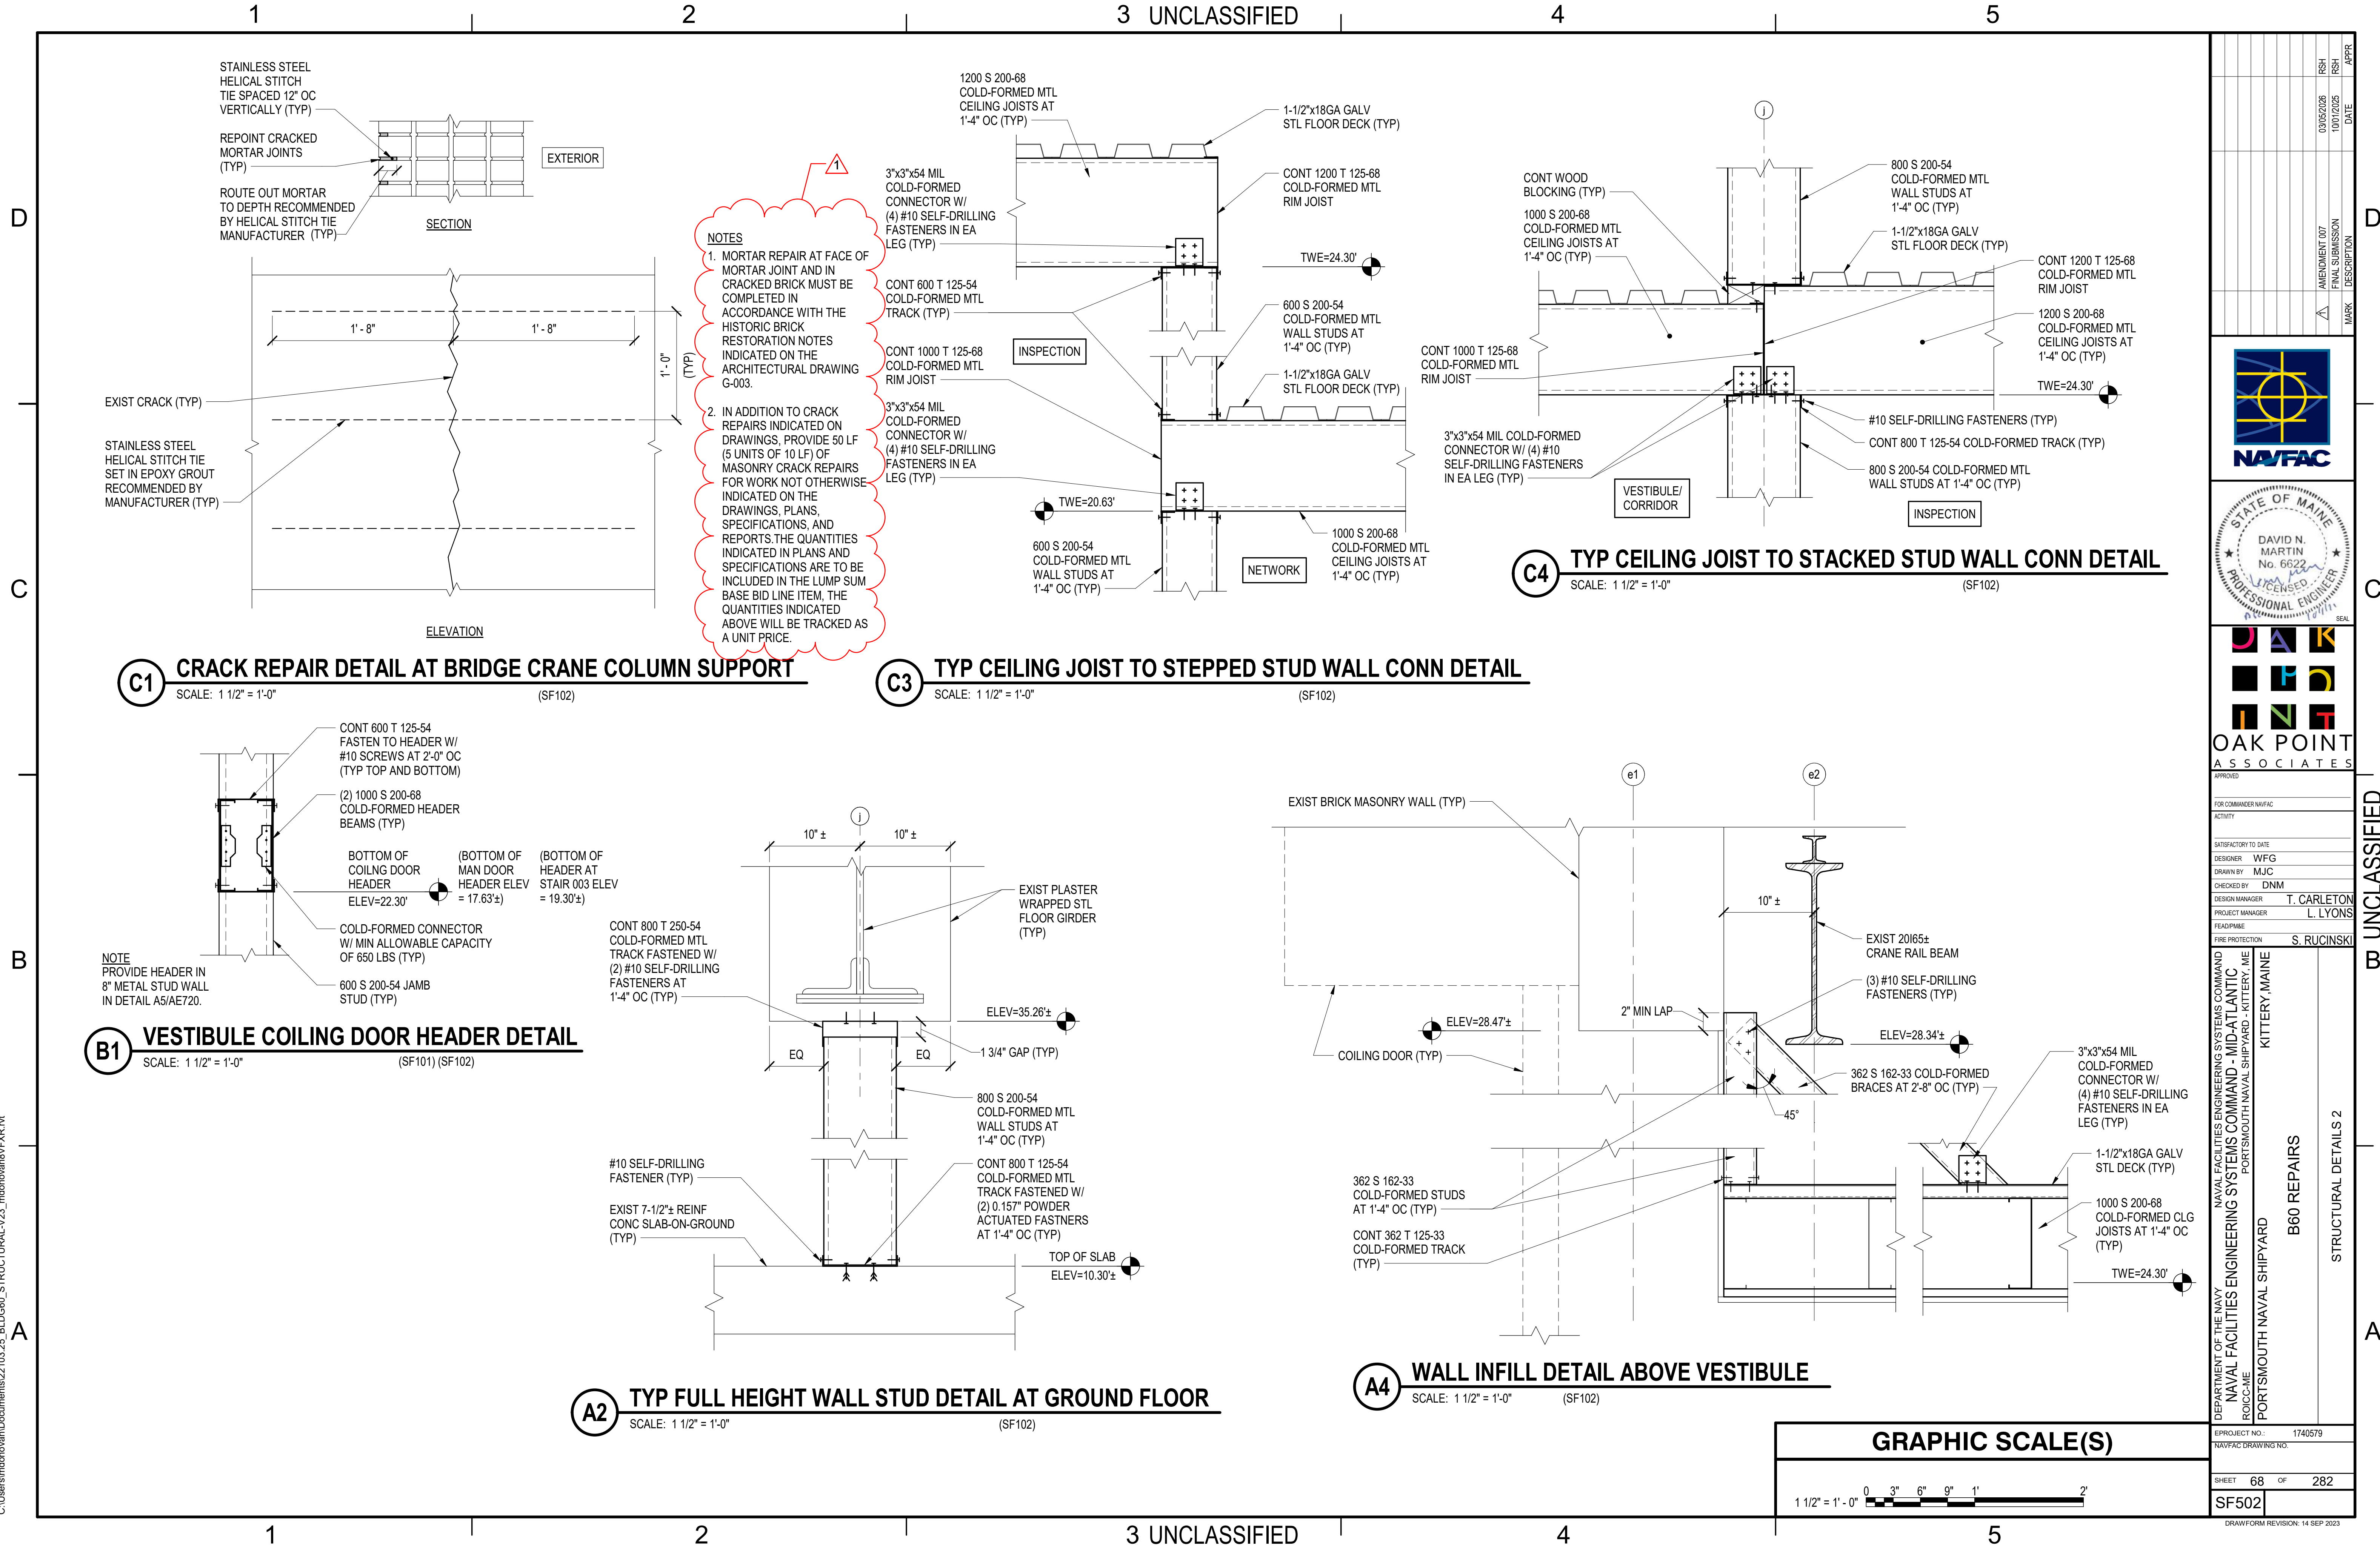

APPROVED	DATE	03/02/26	DATE	10/02/25
FOR COMMANDER NAVFAC	ACTIVITY	NAVAL FACILITIES ENGINEERING SYSTEMS COMMAND - MID-ATLANTIC		PORTSMOUTH NAVAL SHIPYARD - KITTERY, ME
SATISFACTORY TO DATE	DESIGNER	WFG		
DRAWN BY	MJC			
CHECKED BY	DNM			
DESIGN MANAGER	T. CARLETON			
PROJECT MANAGER	L. LYONS			
HEADLINE				
FIRE PROTECTION	S. RUCINSKI			
NAVAL FACILITIES ENGINEERING SYSTEMS COMMAND - MID-ATLANTIC				
PORTSMOUTH NAVAL SHIPYARD				
KITTERY, MAINE				
B60 REPAIRS				
STRUCTURAL DETAILS 2				
PROJECT NO. 1740579				
NAVFAC DRAWING NO.				
SHEET 68 OF 282				
SF502				
DRAWING REVISION: 14 SEP 2023				

NAVFAC

STATE OF MAINE

DAVID N. MARTIN

No. 6622

PROFESSIONAL ENGINEER

OAK POINT ASSOCIATES

UNCLASSIFIED