

3/20/2026 11:39:56 AM AE444
C:\Users\mdonovan\Documents\22103.25_BLDG00_ARCHITECTURAL-V23_mdonovan\VPXR.rvt

1

2

3 UNCLASSIFIED

4


5

D


C

B


A

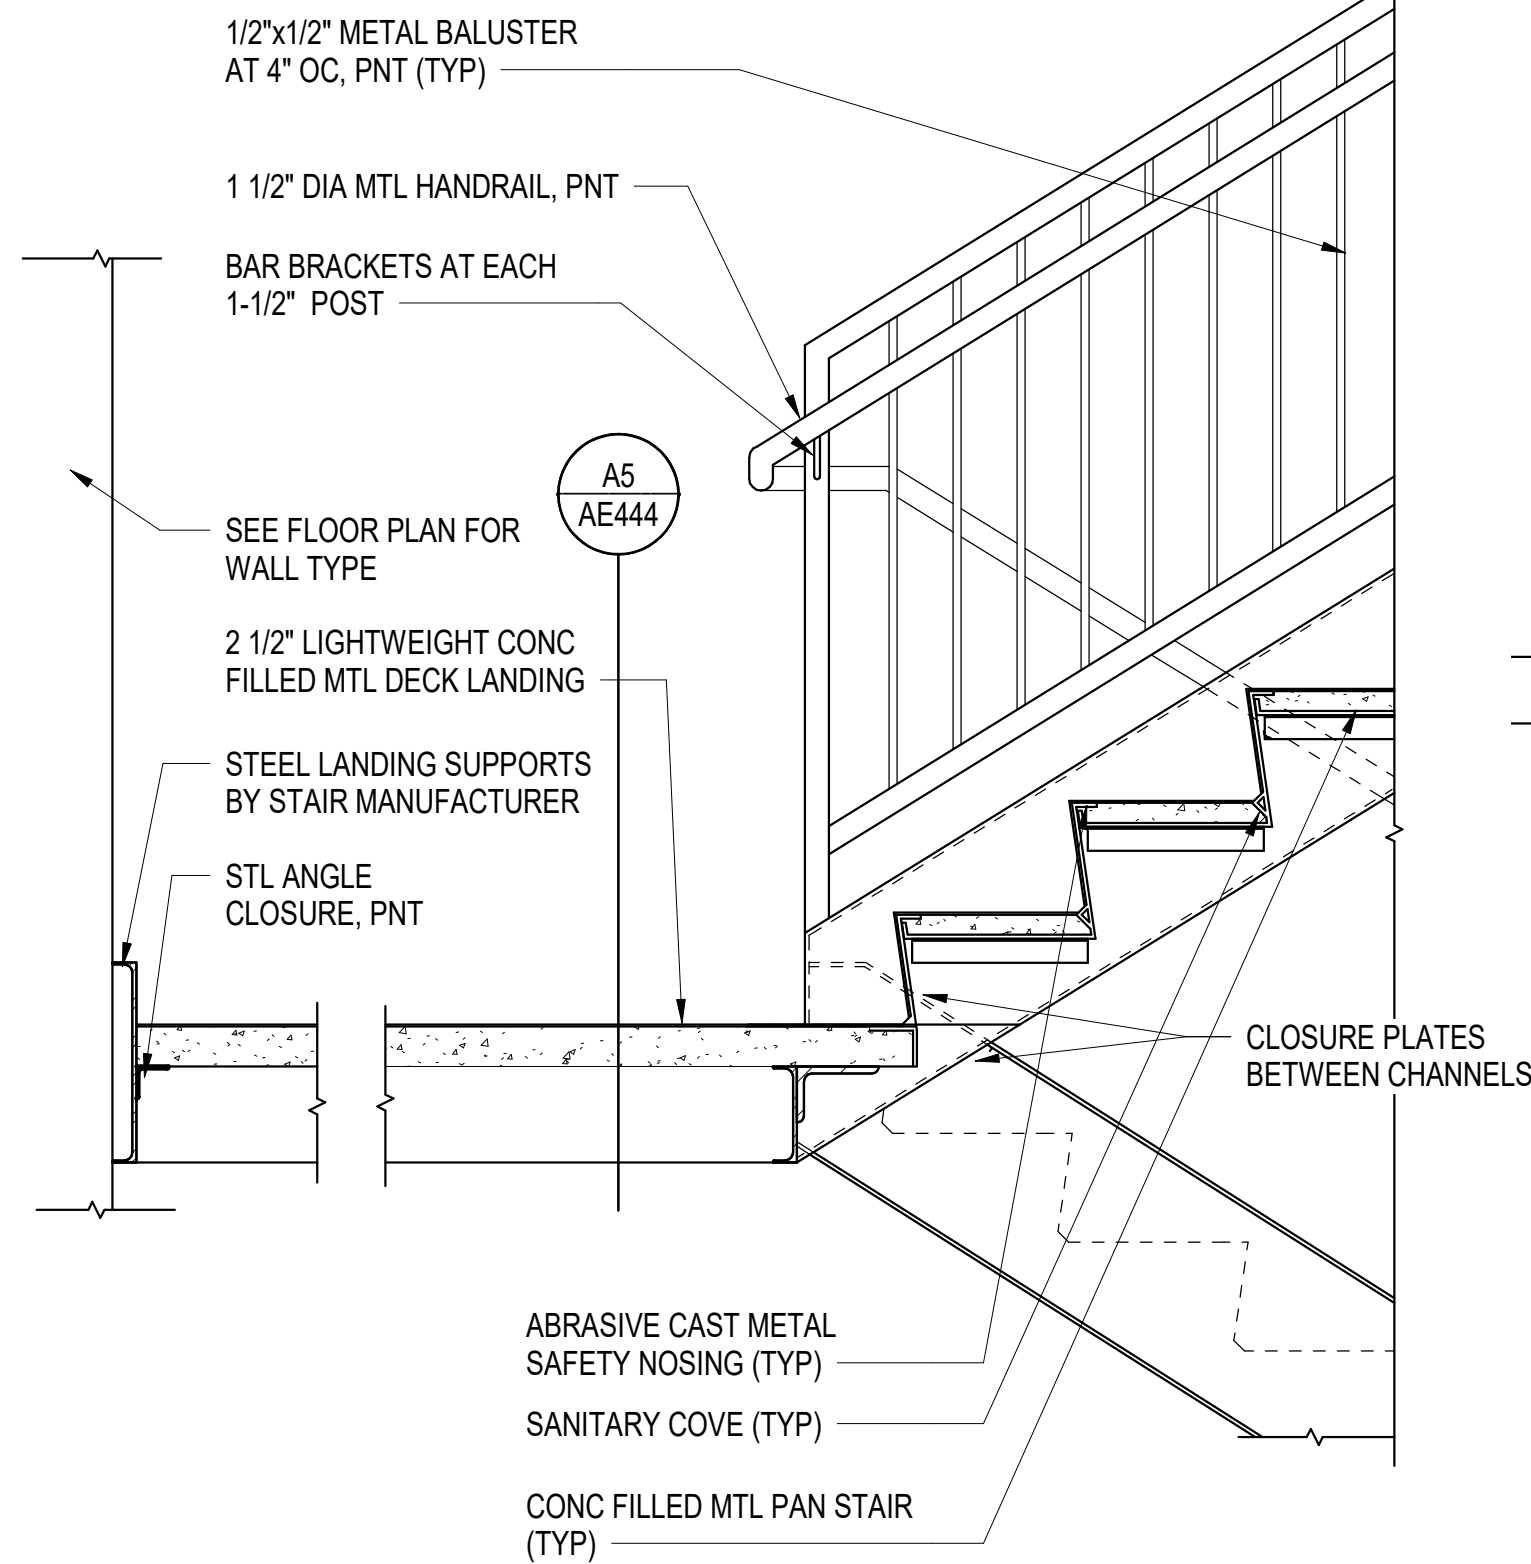


C2 STAIR LANDING DETAIL (TYP)
SCALE: 1" = 1'-0" (AE442)

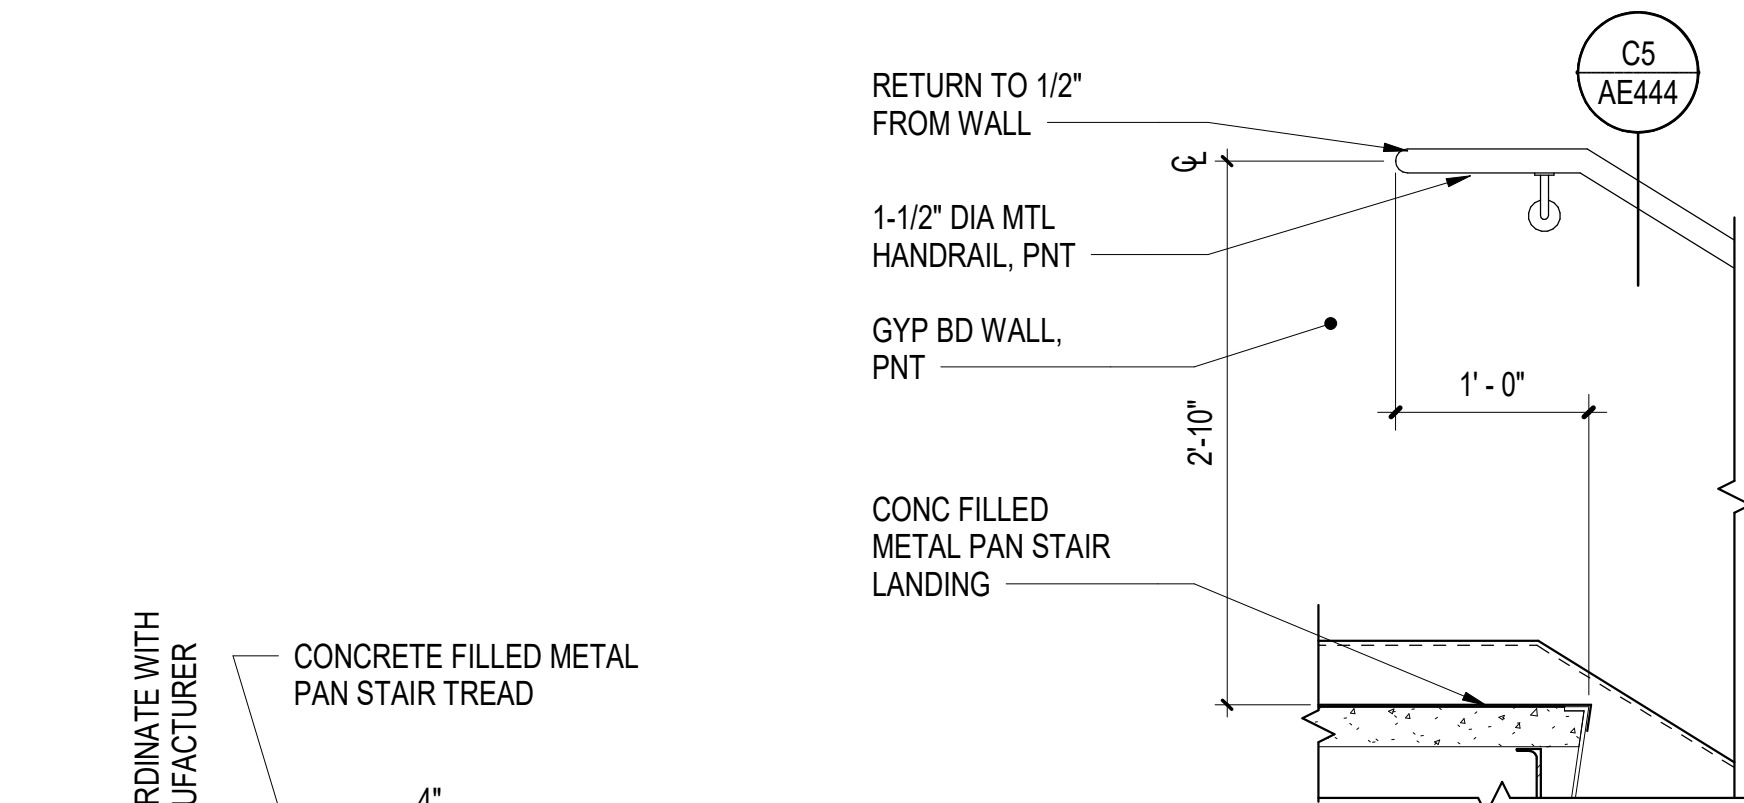


A2 STAIR HANDRAIL DETAIL (TYP)
SCALE: 1" = 1'-0" (AE442)

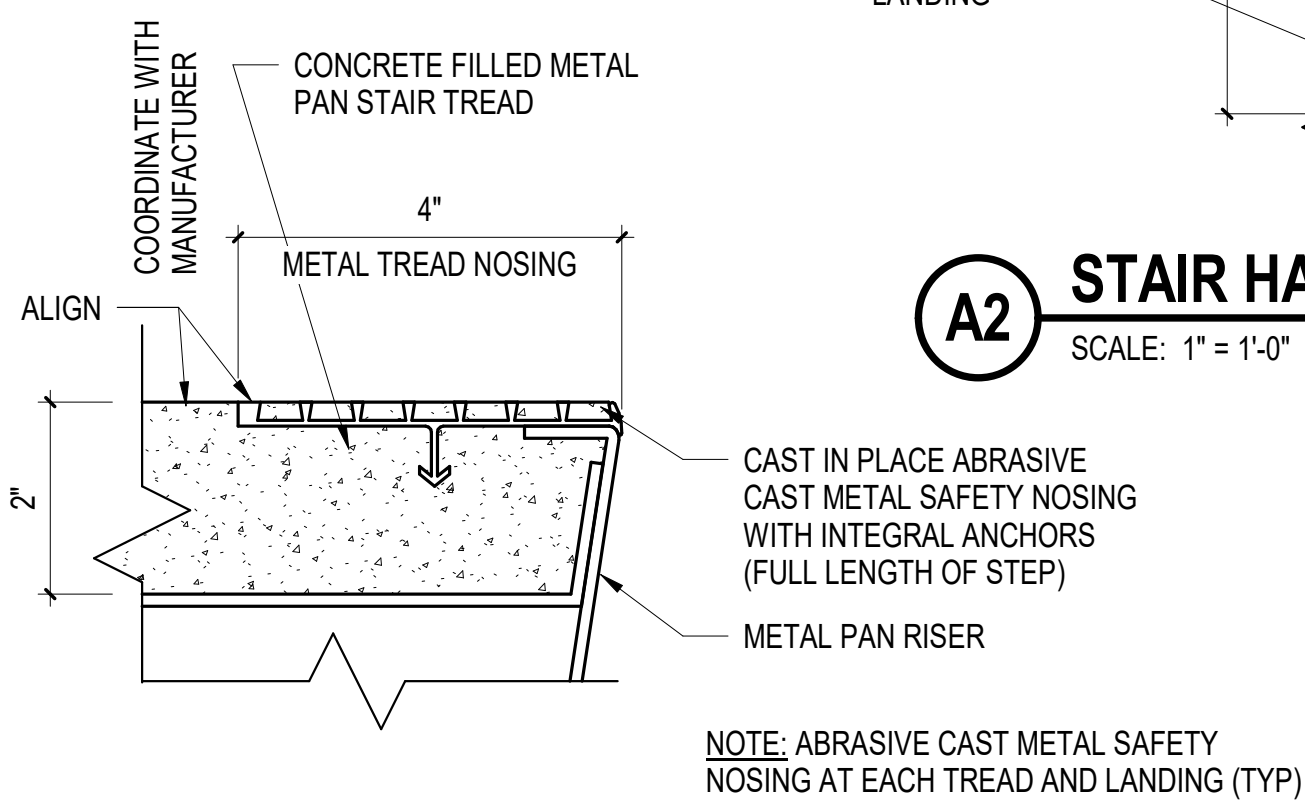


A1 TYP TREAD DETAIL
SCALE: 6" = 1'-0" (AE444)

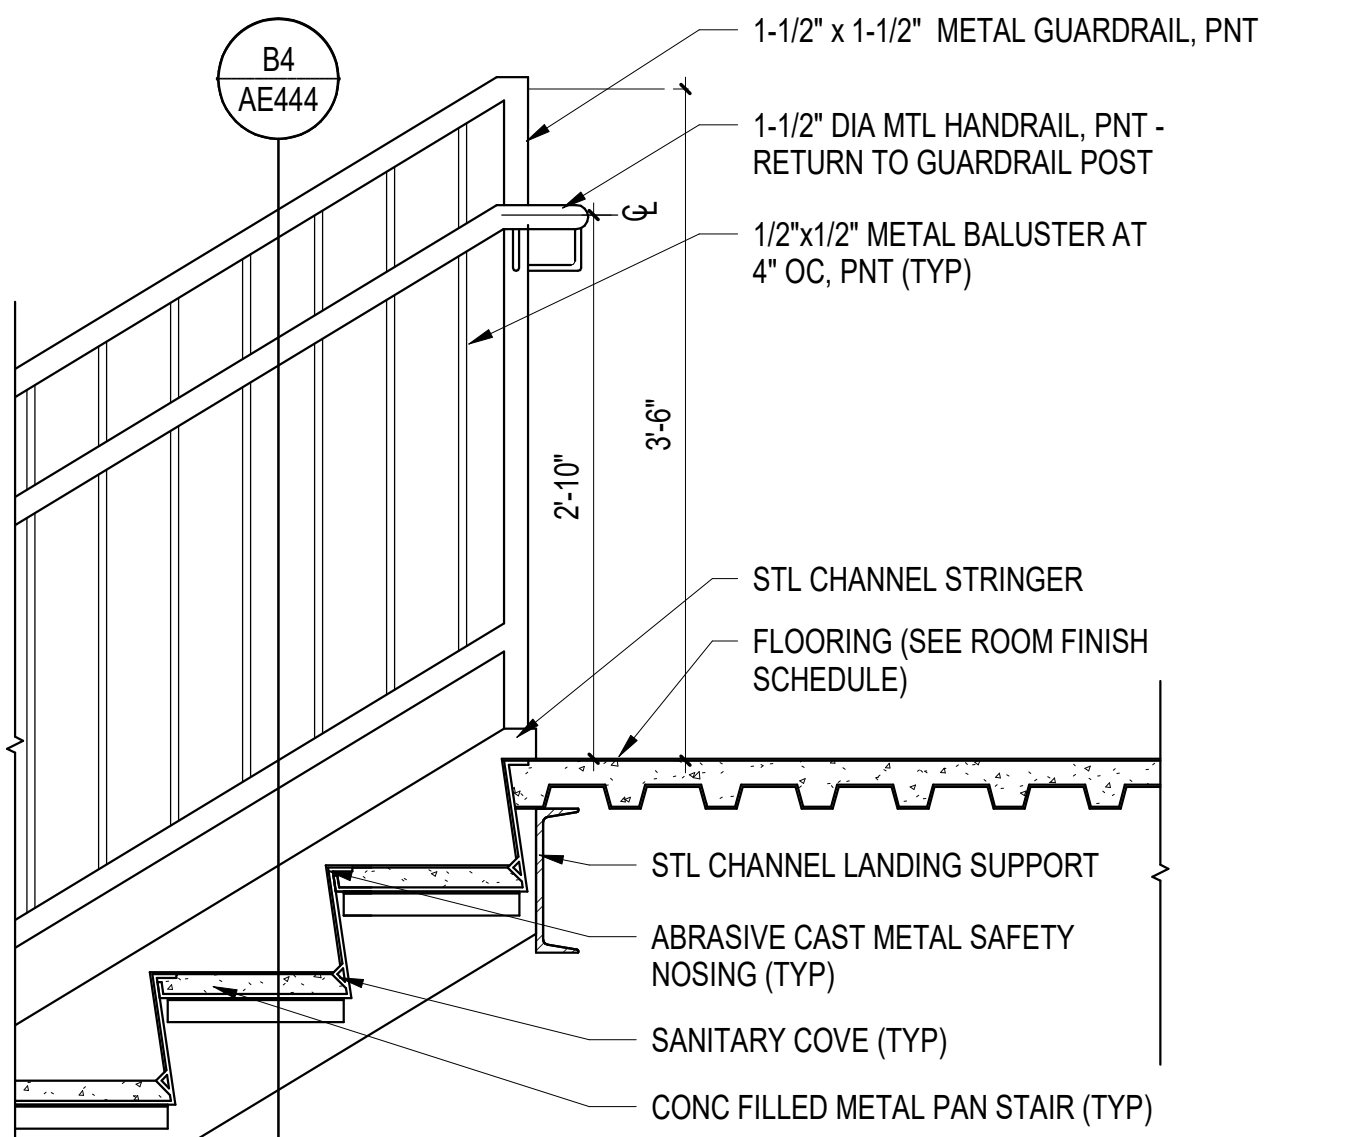


D3 STAIR TOP FLOOR LEVEL LANDING DETAIL (TYP)
SCALE: 1" = 1'-0" (AE442)

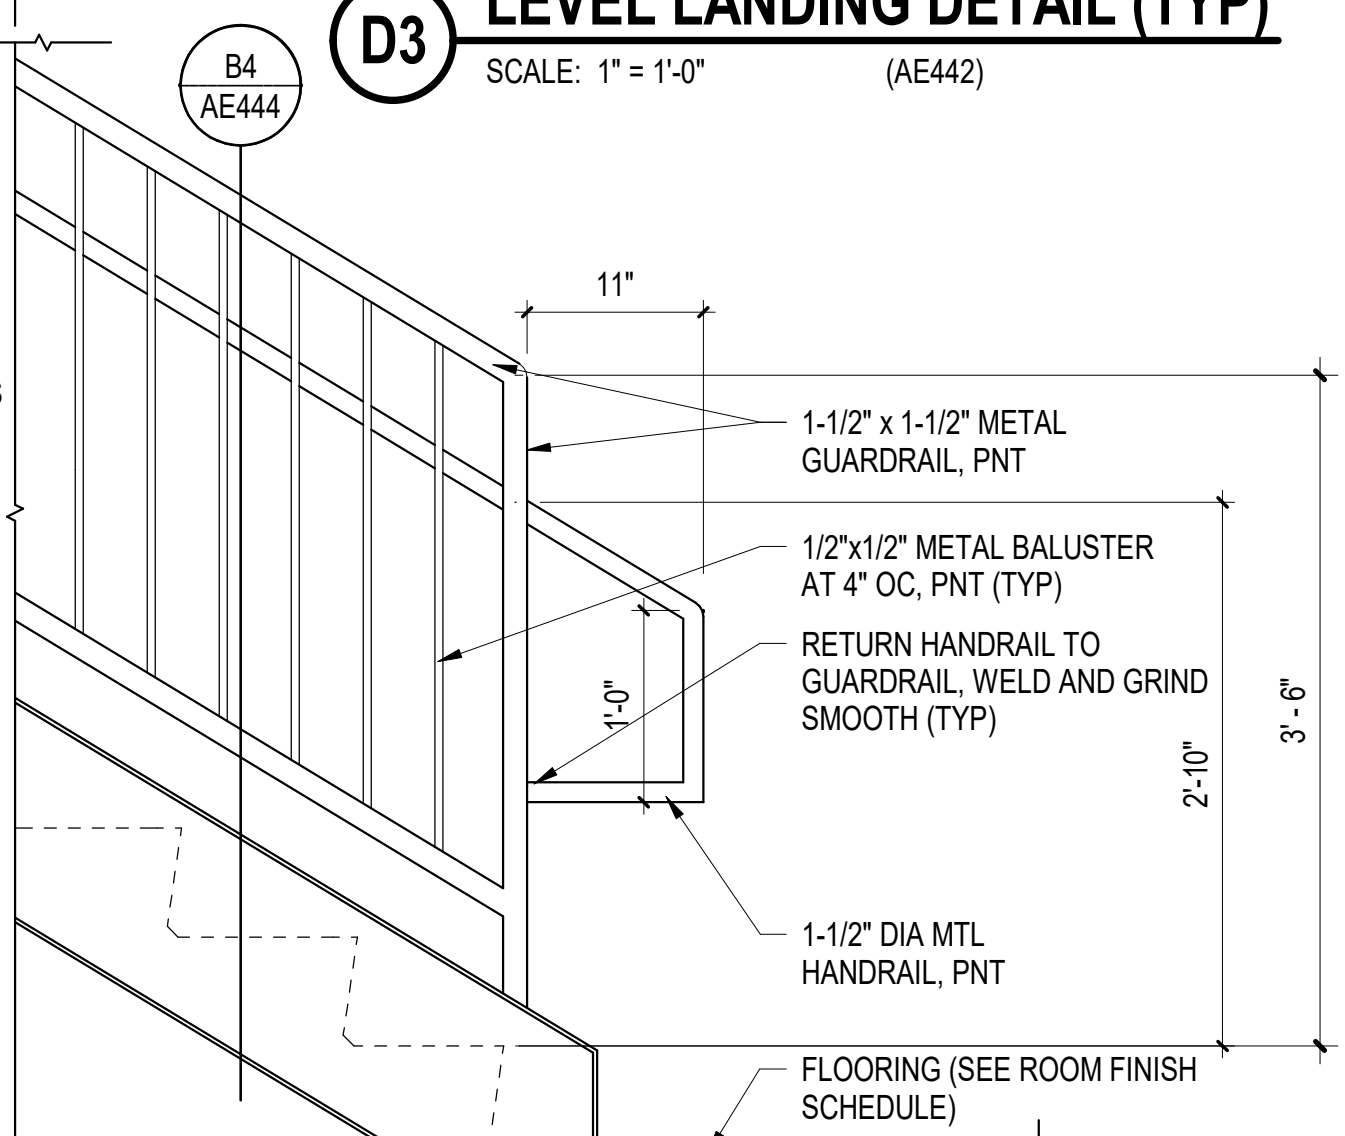


B3 STAIR BOTTOM LANDING (TYP)
SCALE: 1" = 1'-0" (AE442)

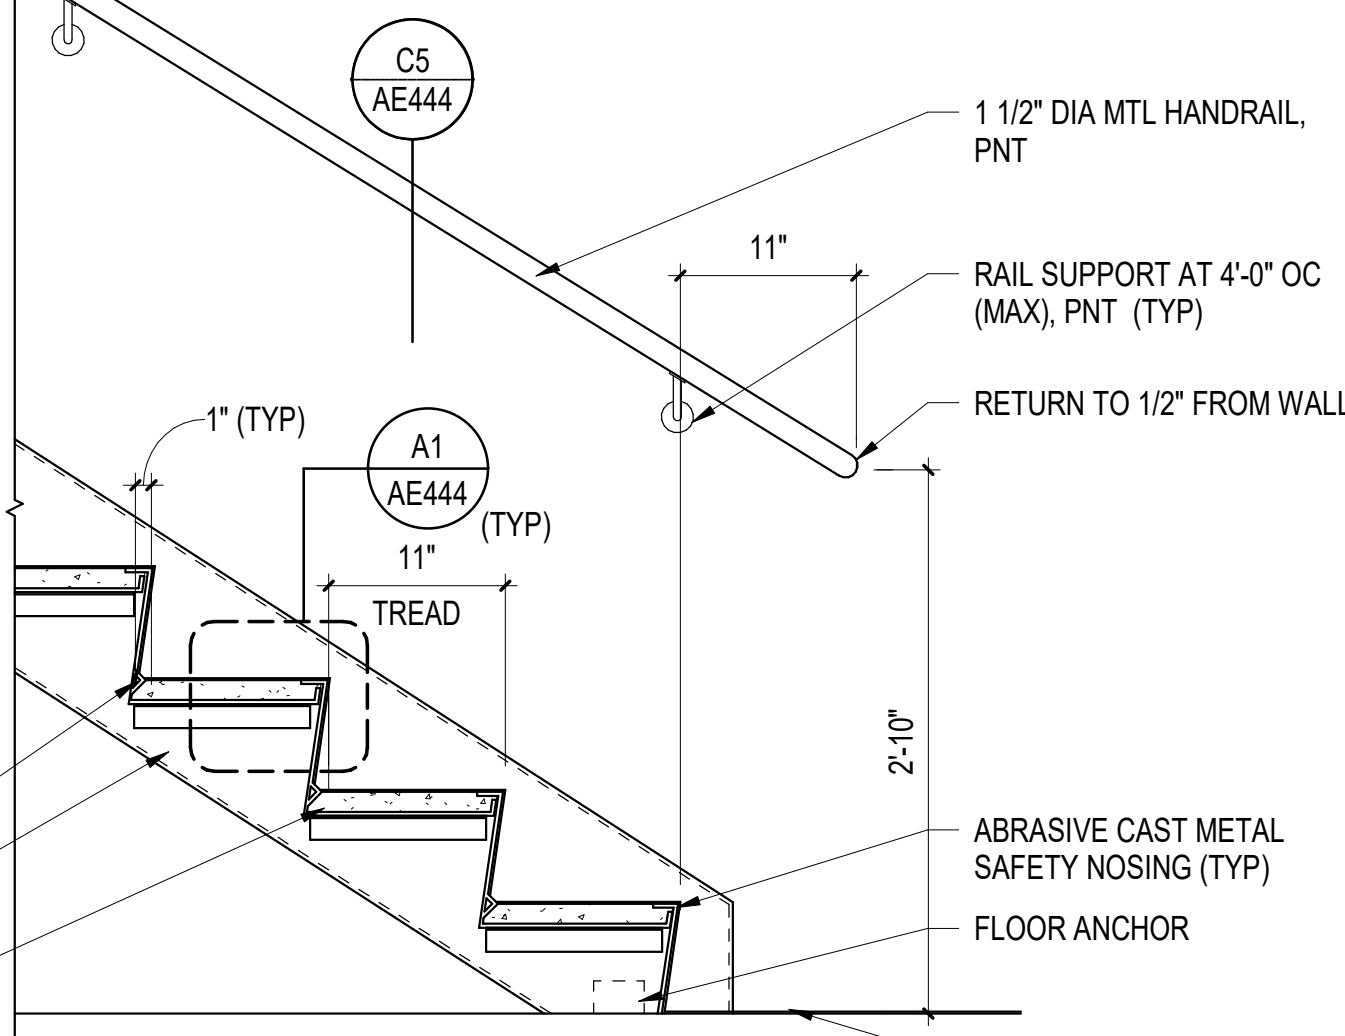


A3 STAIR RUN DETAIL (TYP)
SCALE: 1" = 1'-0" (AE442)

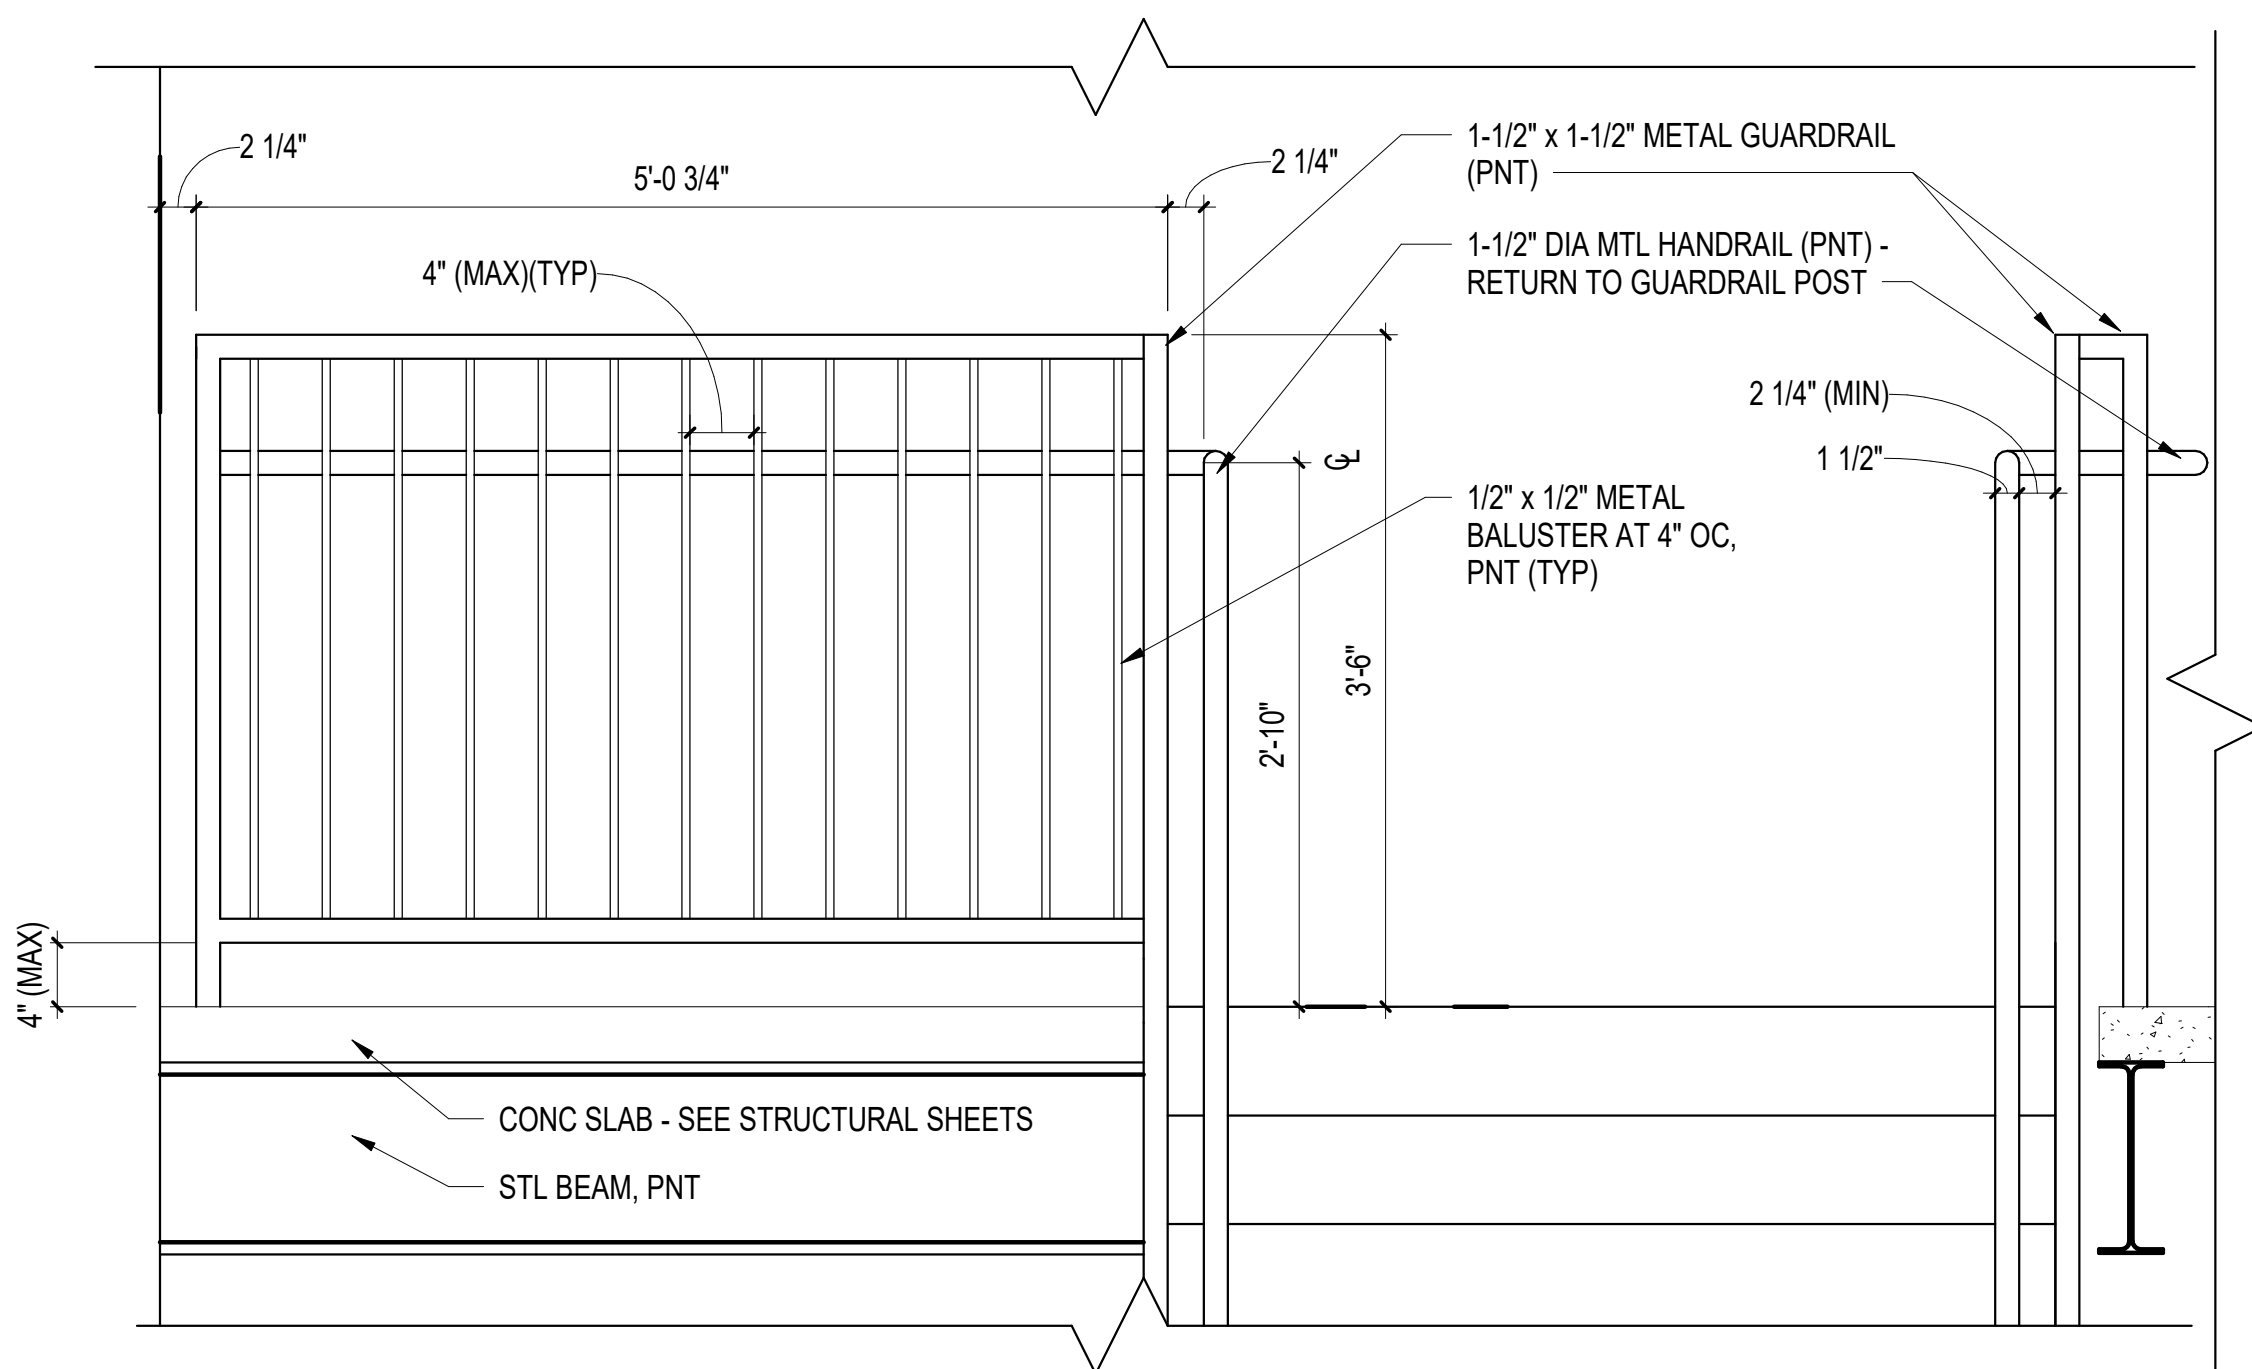


C4 STAIR TOP LANDING DETAIL (TYP)
SCALE: 1" = 1'-0" (AE440)

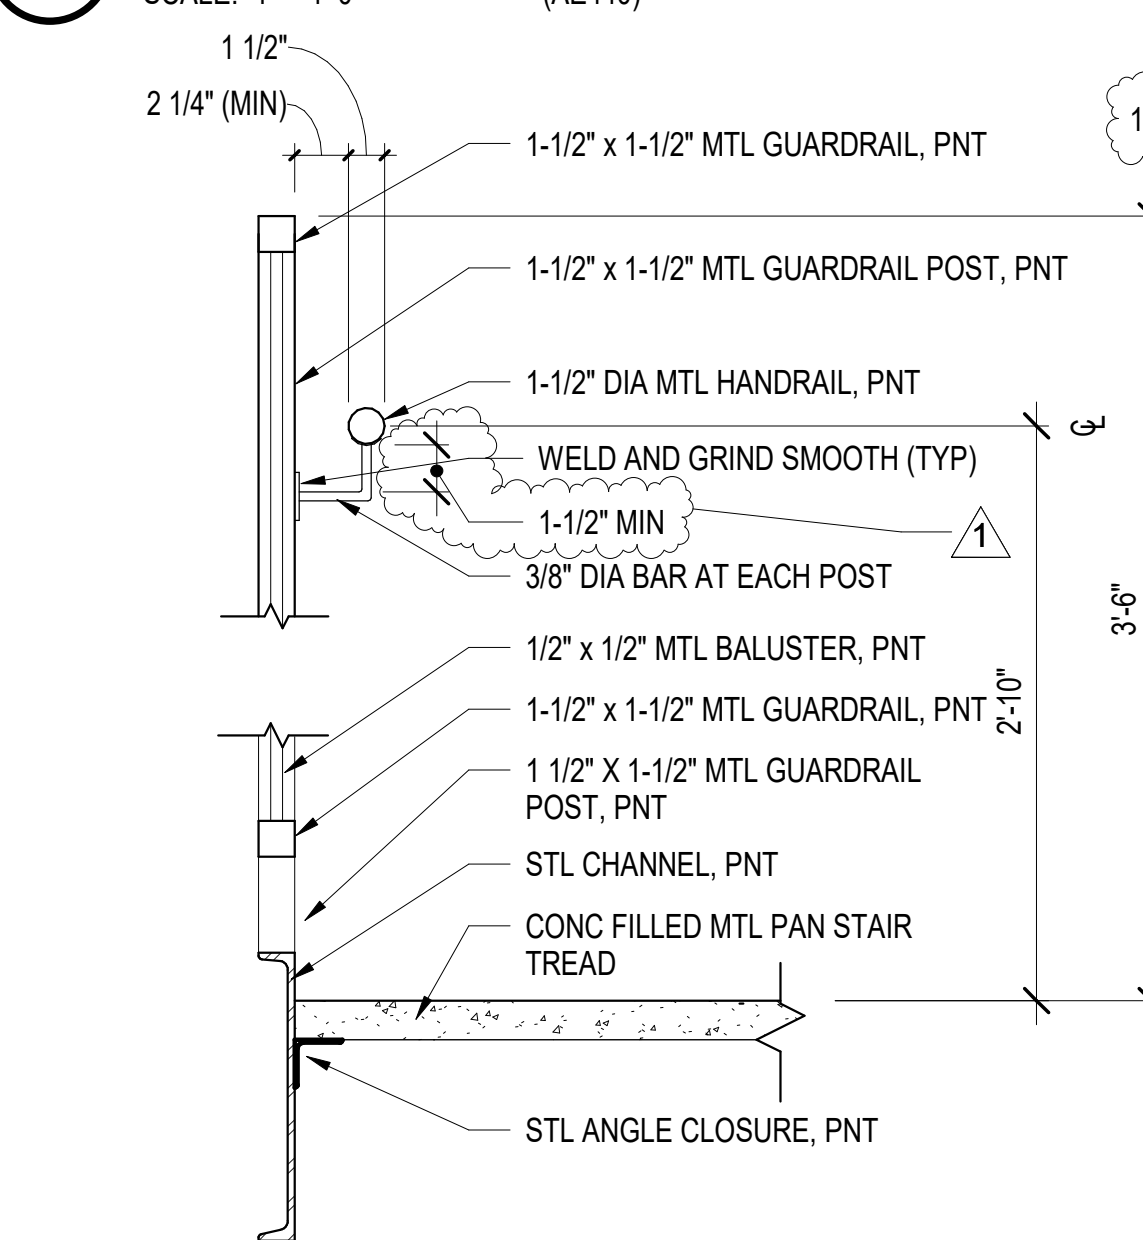


B4 STAIR LANDING FLOOR LEVEL EDGE DETAIL (TYP)
SCALE: 1 1/2" = 1'-0" (AE444)

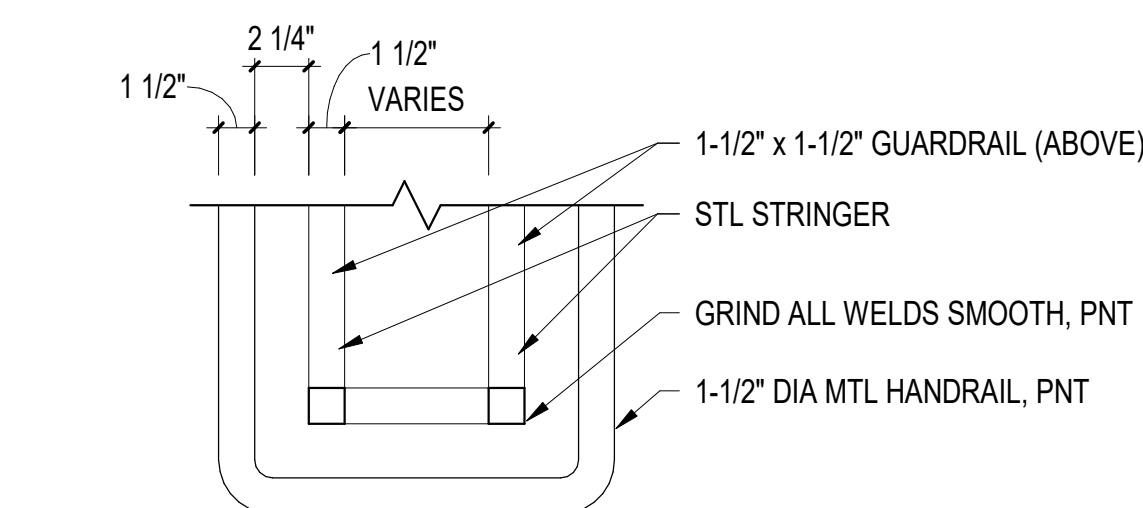


A4 STAIR DETAIL (TYP)
SCALE: 1 1/2" = 1'-0" (AE444)

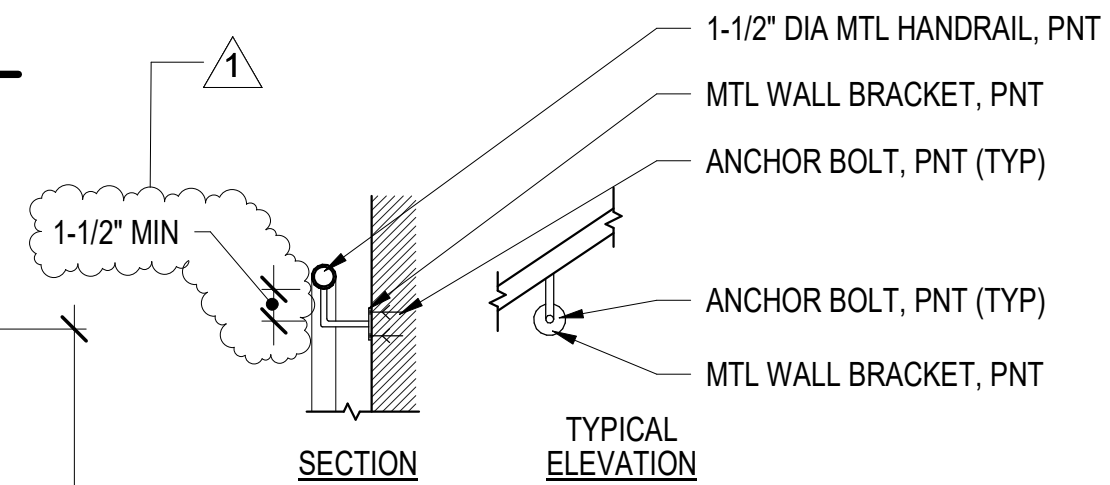

C5 STAIR RAILING DETAIL (TYP)
SCALE: 1" = 1'-0" (AE444)

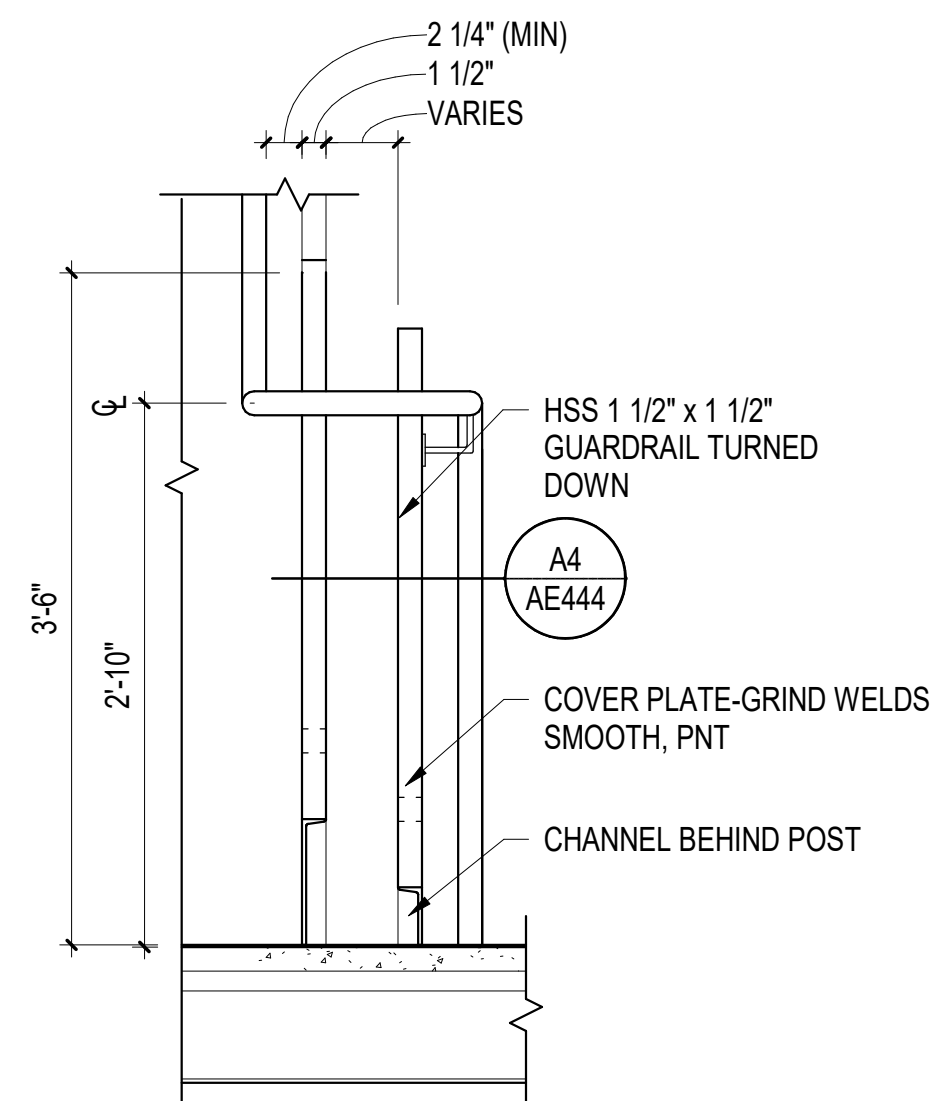

A5 STAIR RAILING ELEVATION (TYP)
SCALE: 1" = 1'-0" (AE444)

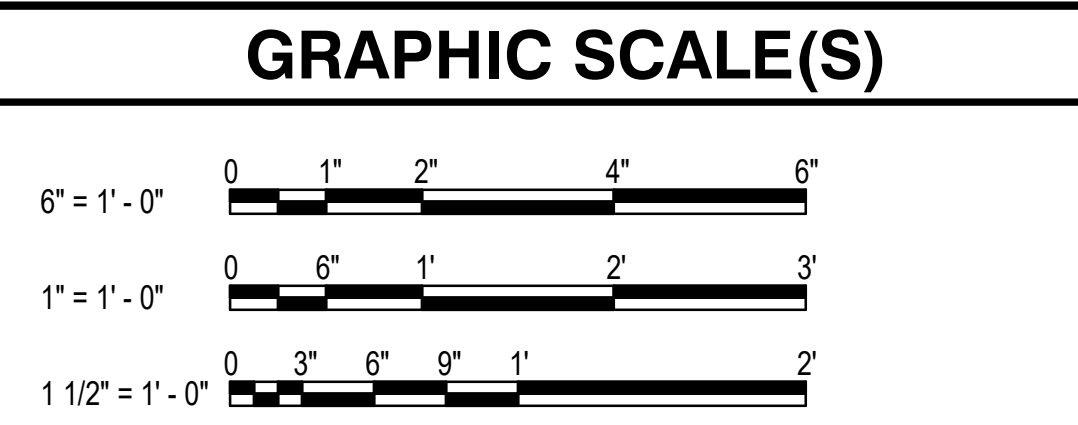

APR	DATE	10/07/2025	RSH	03/20/2026	RSH
AMENDMENT 010	FINAL SUBMISSION	MARK	DESCRIPTION	DATE	APR
FOR COMMANDER NAVFAC					
ACTIVITY					
SATISFACTORY TO DATE					
DESIGNER JMR					
DRAWN BY CJE					
CHECKED BY RSH					
DESIGN MANAGER T. CARLETON					
PROJECT MANAGER L. LYONS					
HEADLINE					
FIRE PROTECTION S. RUCINSKI					
NAVAL FACILITIES ENGINEERING SYSTEMS COMMAND - MID-ATLANTIC					
PORTSMOUTH NAVAL SHIPYARD - KITTERY, ME					
B60 REPAIRS					
STAIR DETAILS					
PROJECT NO. 1740579					
NAVFAC DRAWING NO.					
SHEET 123 OF 282					
AE444					
DRAWING REVISION: 14 SEP 2023					

1

2

3 UNCLASSIFIED

4

5

D

C

B UNCLASSIFIED

A