



D4 **TYP FOAM EXPANSION JOINT SYSTEM**
SCALE: NOT TO SCALE

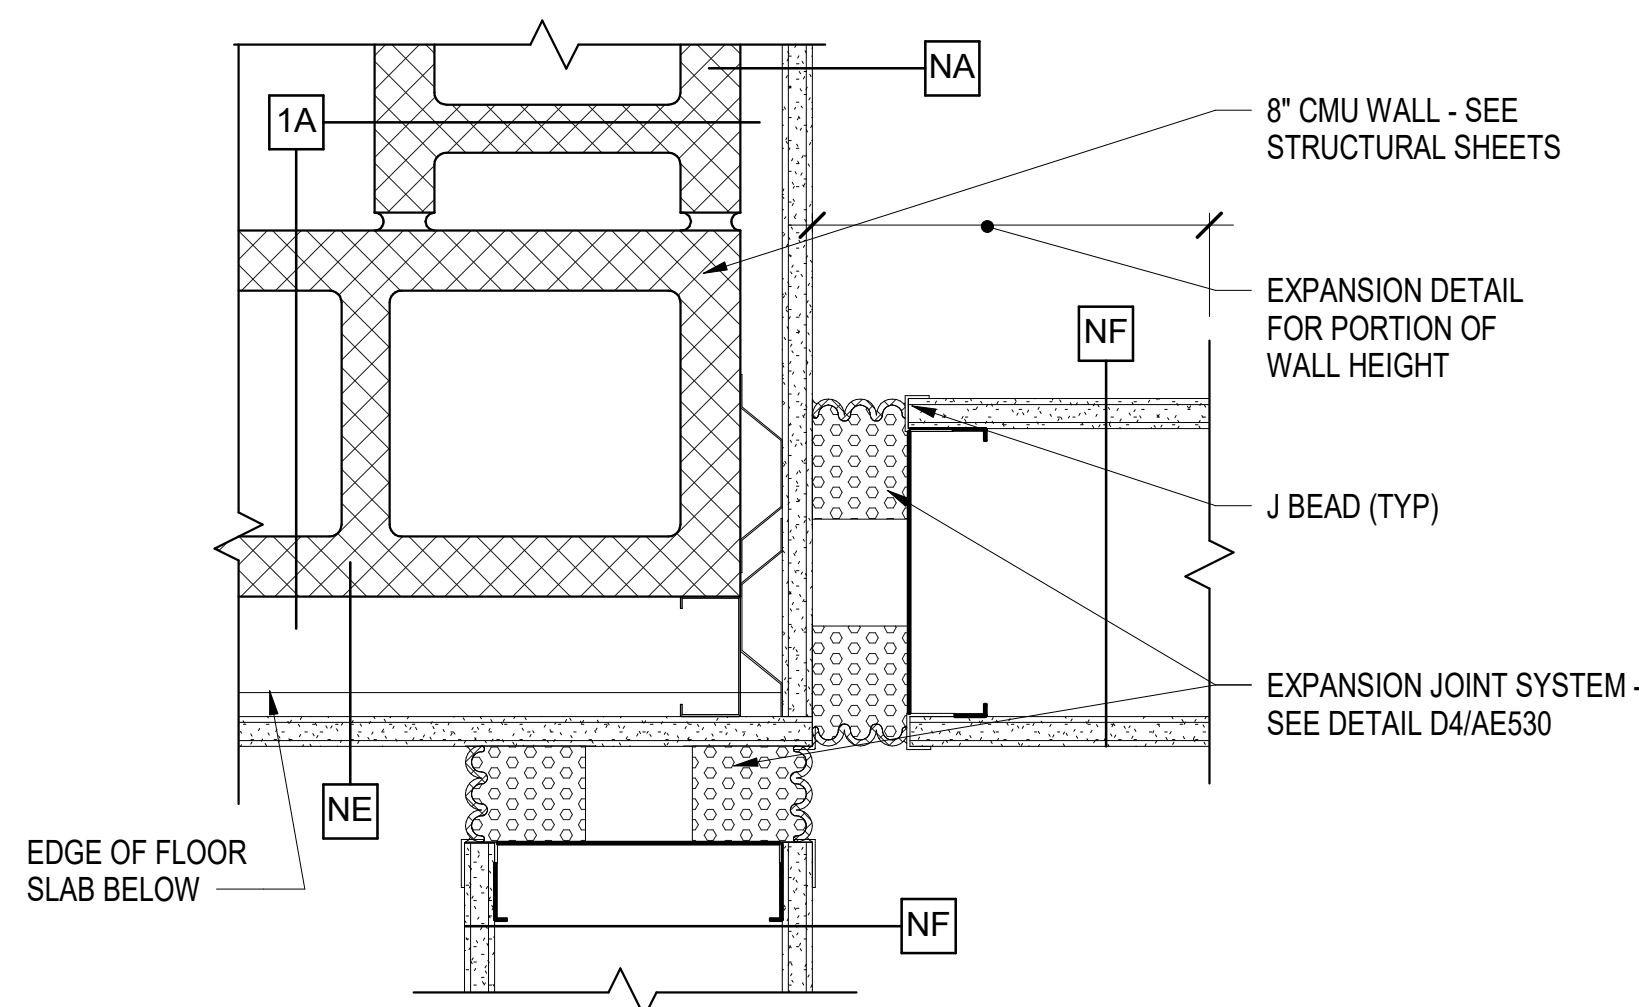

B4 **ELEVATOR/FLOOR EXPANSION JOINT PLAN DETAIL 1**
SCALE: 3" = 1'-0" (AE411)

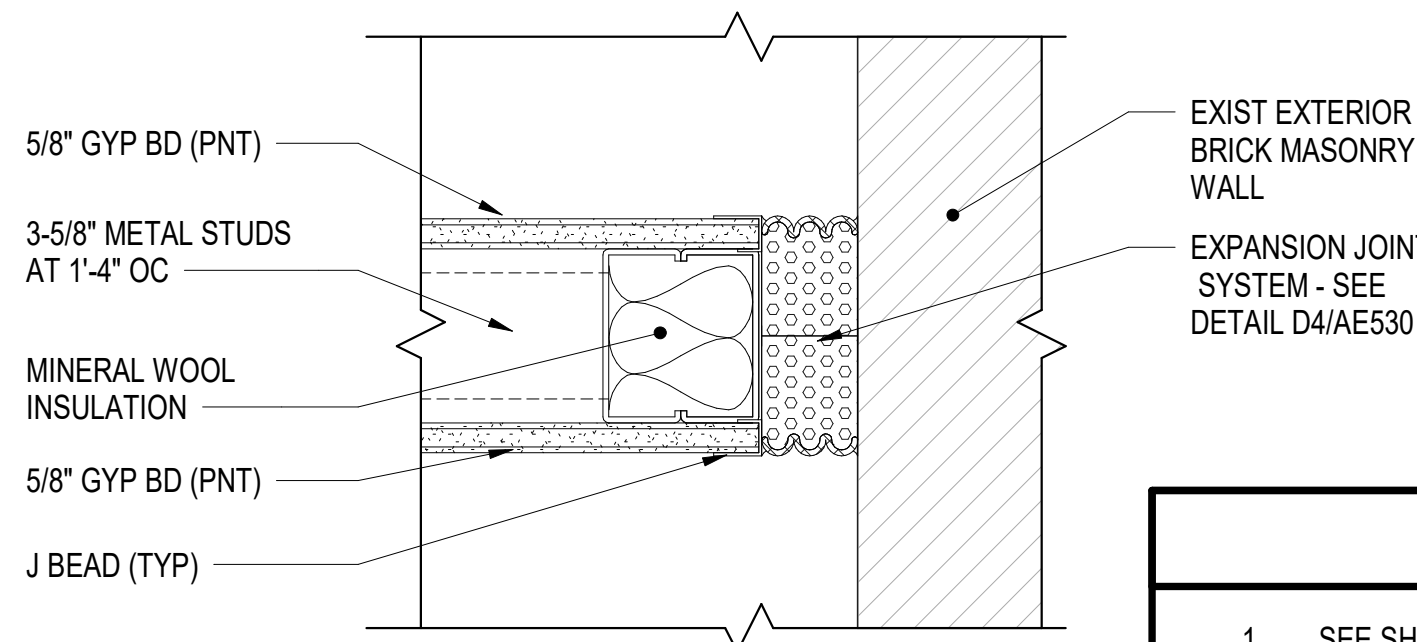

A4 WALL EXPANSION JOINT PLAN DETAIL
SCALE: 3" = 1'-0"

1. SEE SHEET AE001 FOR WALL TYPES.
2. SEE SHEET AE601 FOR DOOR SCHEDULE.
3. SEE SHEET AE602 FOR DOOR REPAIR AND RESTORATION SCHEDULE.

3" = 1' - 0"



A horizontal graphic scale bar with alternating black and white segments. It is marked with '0' at the left end, '3"' at the first segment boundary, and '6"' at the second segment boundary.

DRAWFORM REVISION: 14 SEP 2023