



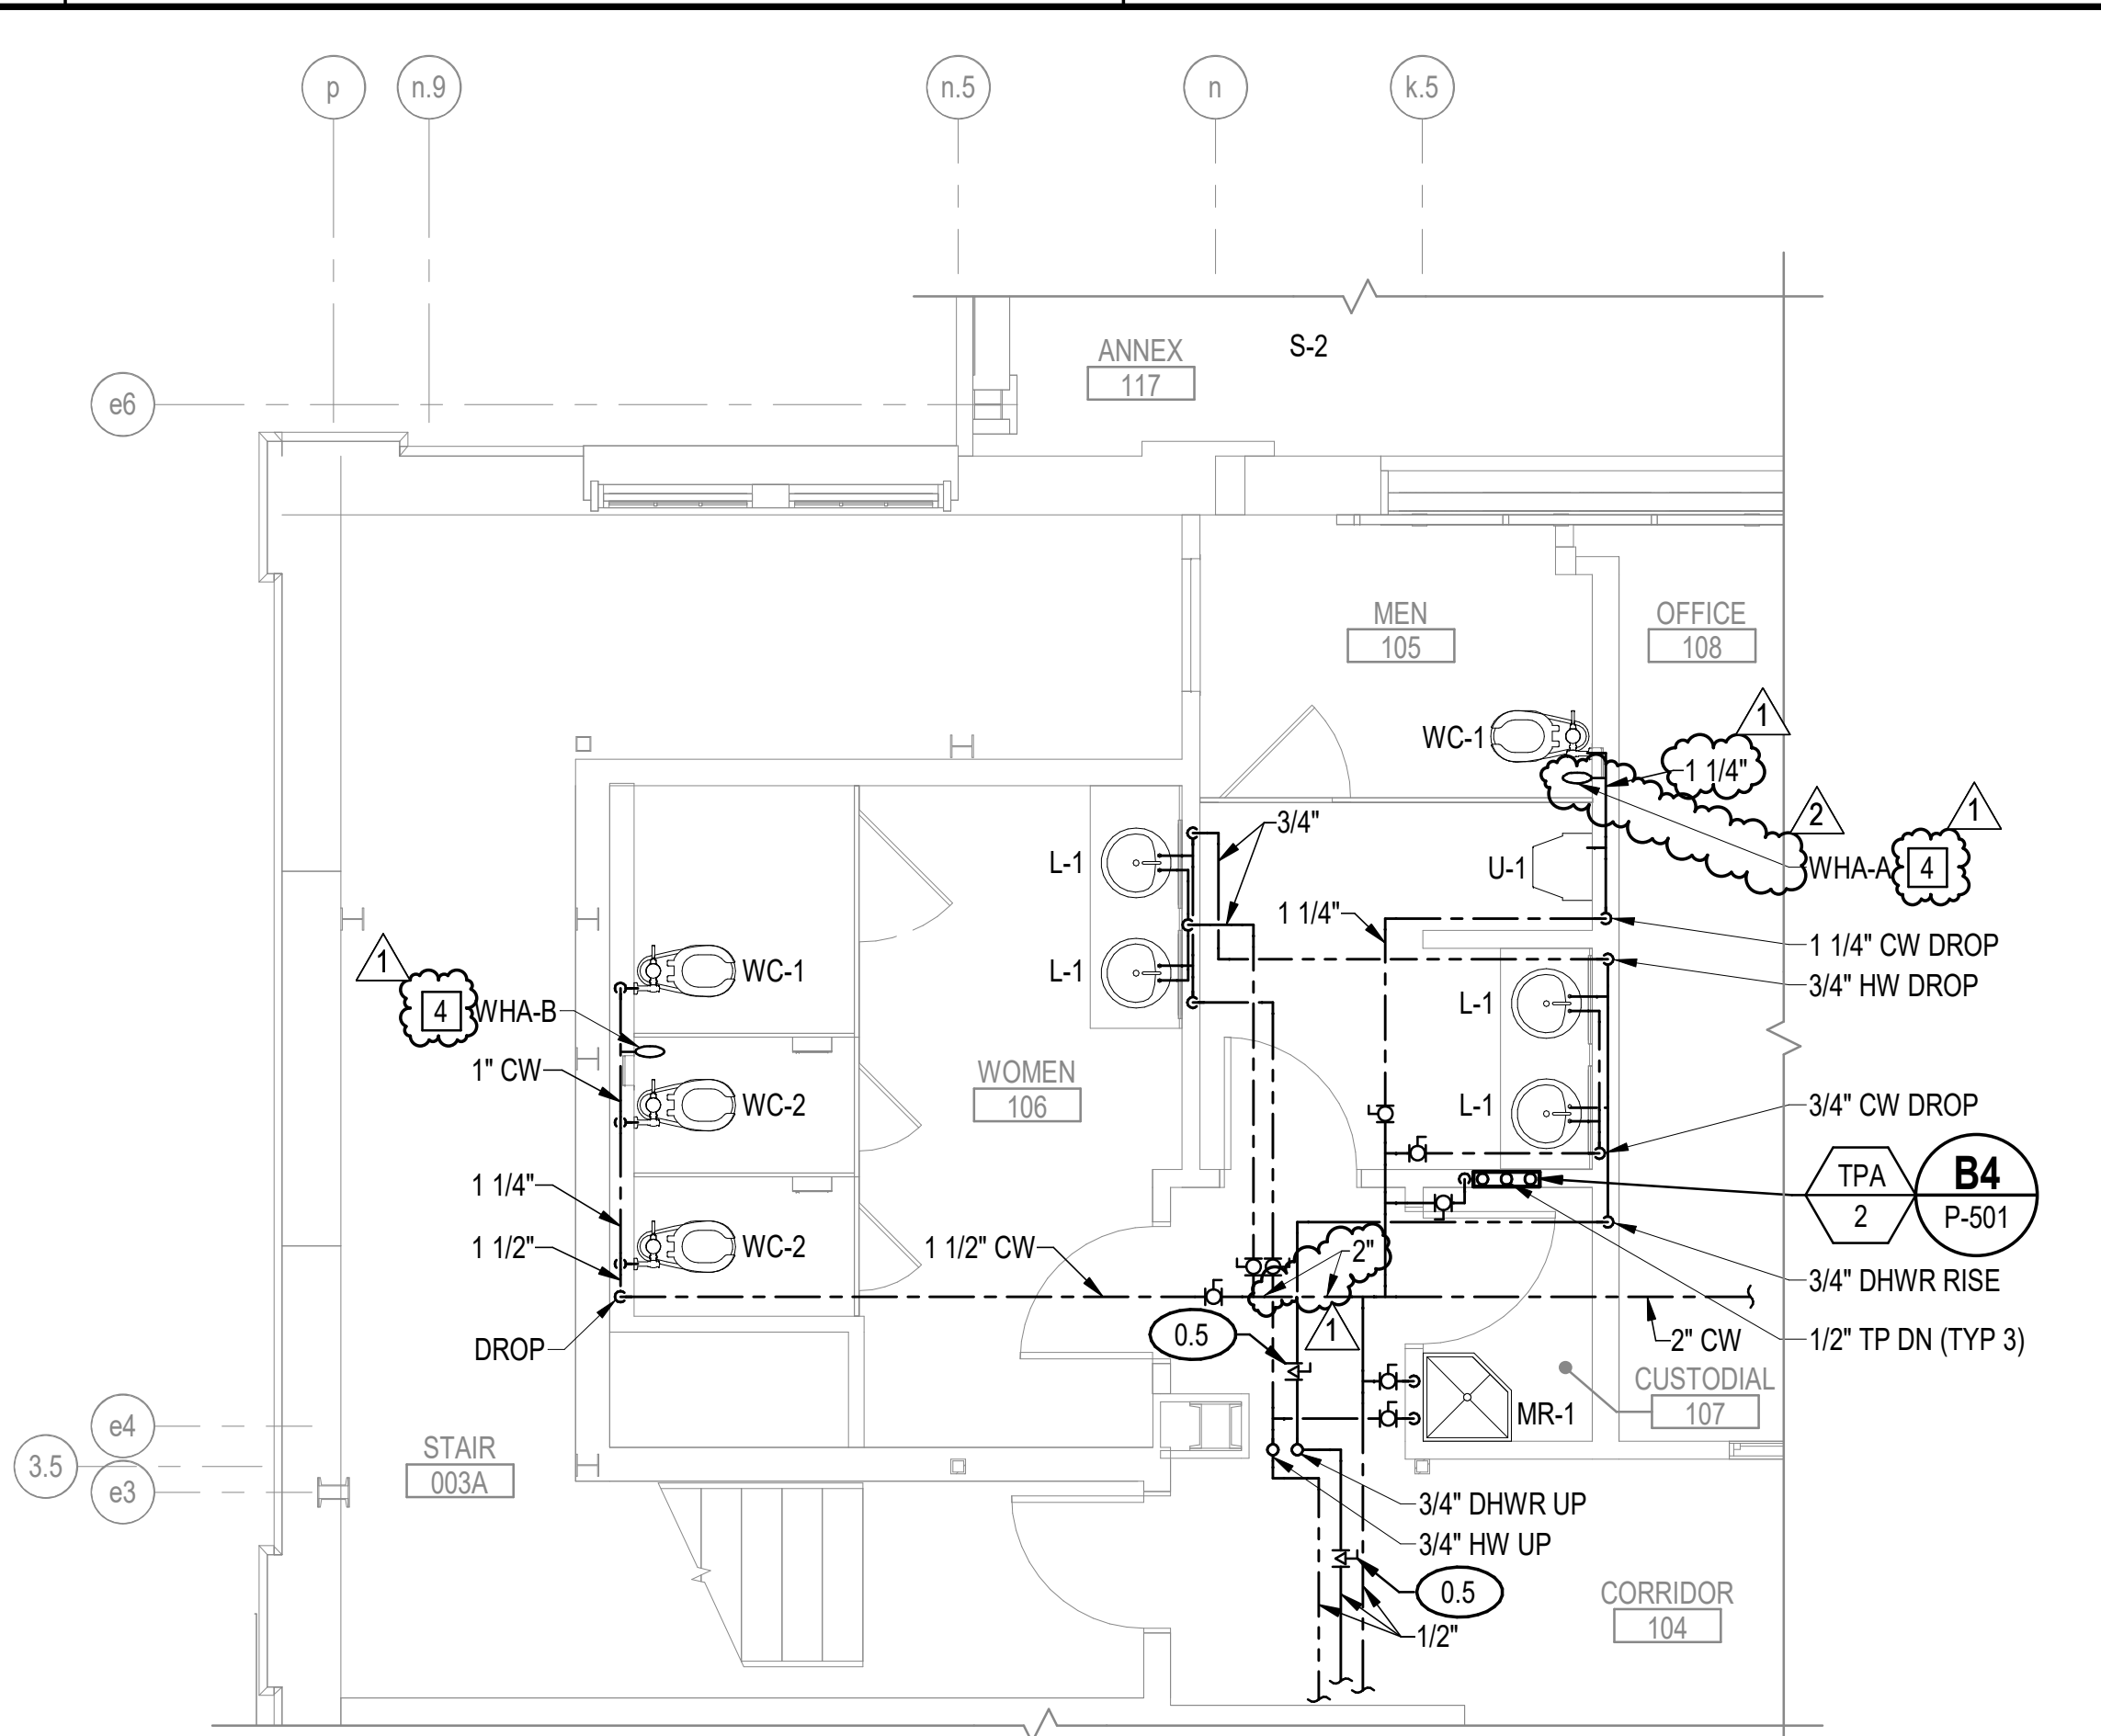

C3 **ENLARGED FIRST FLOOR DOMESTIC WATER SUPPLY PART PLAN**
SCALE: 1/4" = 1'-0" (P-104)

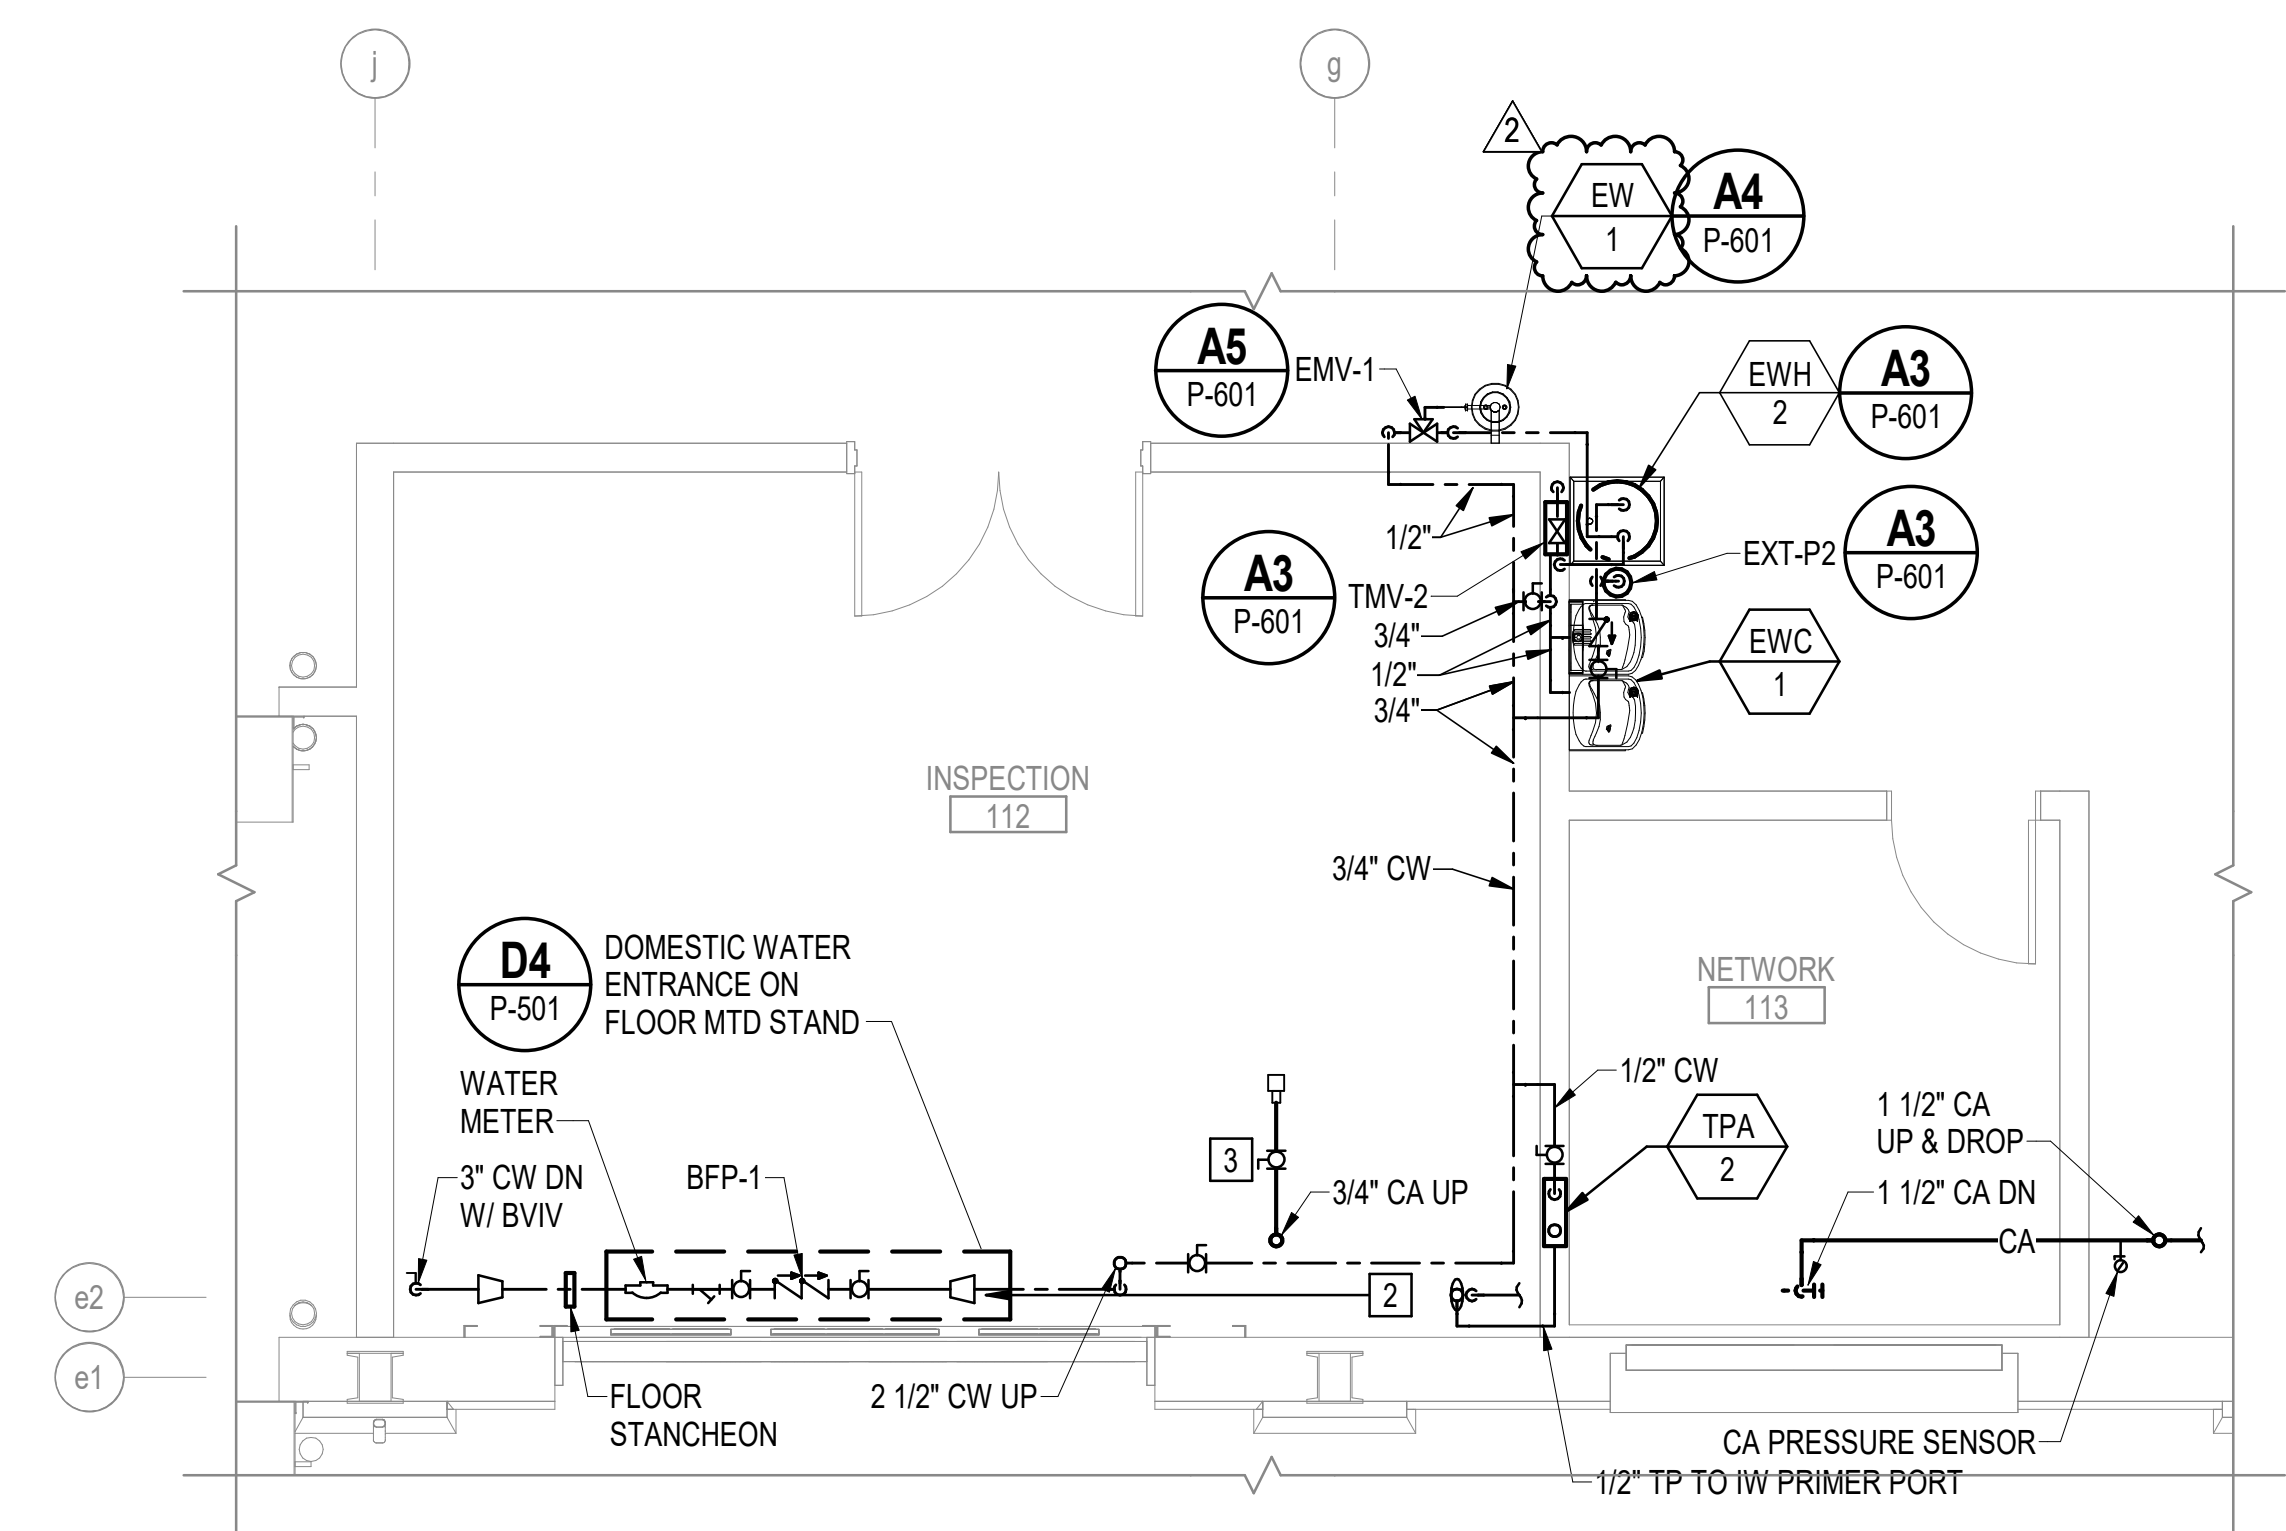



A3 ENLARGED FIRST FLOOR DOMESTIC WATER SUPPLY PART PLAN
SCALE: 1/4" = 1'-0" (P-104)

1. SEE P-001 FOR PLUMBING LEGENDS, ABBREVIATIONS AND GENERAL NOTES.
2. COORDINATE THE INSTALLATION OF PIPING AND EQUIPMENT TO MAINTAIN MANDATORY CLEARANCE ZONES AROUND CRANE RAILS AND BRIDGE CRANE OPERATIONAL TRAVEL PATH.

- 1 PIPE 3/4" DRAIN DOWN TO SINK S-2. SECURE TO WALL.
- 2 3" INDIRECT WASTE DRAIN TRAP WITH FUNNEL OPENING FITTING. PIPE DRAIN FROM BFP-1 AND CONDENSATE DRAINS FROM SCU-1 AND TU-2 TO AIR GAP FITTING PROVIDE TRAP WITH PRIMER PORT.
- 3 PROVIDE 1/2" CA WITH ISOLATION BALL VALVE AND QUICK CONNECT FEMALE HOSE CONNECTION FITTING 80" AFF. COORDINATE QUICK CONNECT FITTING SELECTION WITH CONTRACTING OFFICER
- 4 PROVIDE 8"x8" WALL MOUNTED WATER HAMMER ARRESTOR SERVICE ACCESS DOOR.

1/4" = 1' - 0"

CHECK GRAPHIC SCALE BEFORE USING

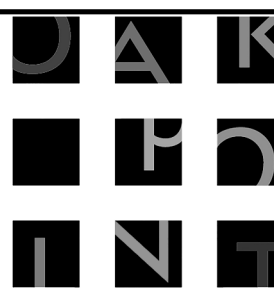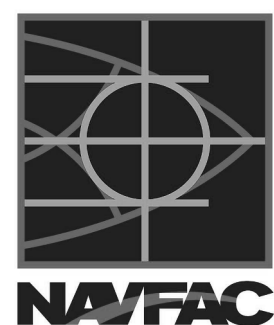[illegible]

OAK POINT
ASSOCIATES

APPROVED	
FOR COMMANDER NAVFAC	
ACTIVITY	
SATISFACTORY TO DATE	
DESIGNER	RNC
DRAWN BY	SRW
CHECKED BY	MSA
DESIGN MANAGER	T. CARLETON
PROJECT MANAGER	L. LYONS
FEAD/PMSE	
FIRE PROTECTION	
S. RUCINSKI	

PORTSMOUTH NAVAL SHIPYARD
B60 REPAIRS
ENLARGED PLUMBING PART PLANS 1

EPROJECT NO.:		1740579	
NAVFAC DRAWING NO.			
SHEET 178		OF 282	
P-401			