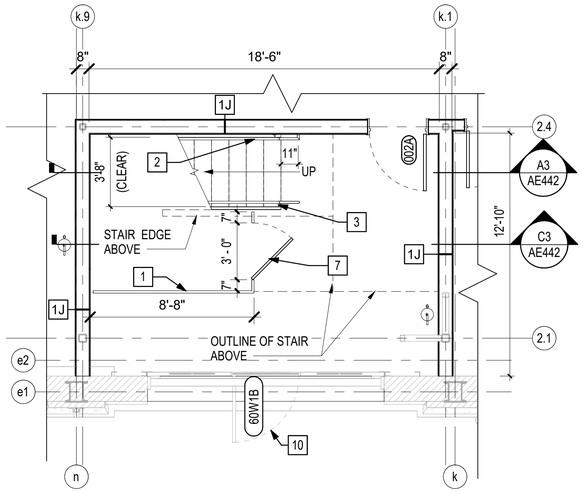

C1 STAIR 002 FIRST FLOOR PLAN

SCALE: 1/4" = 1'-0" (AE102)

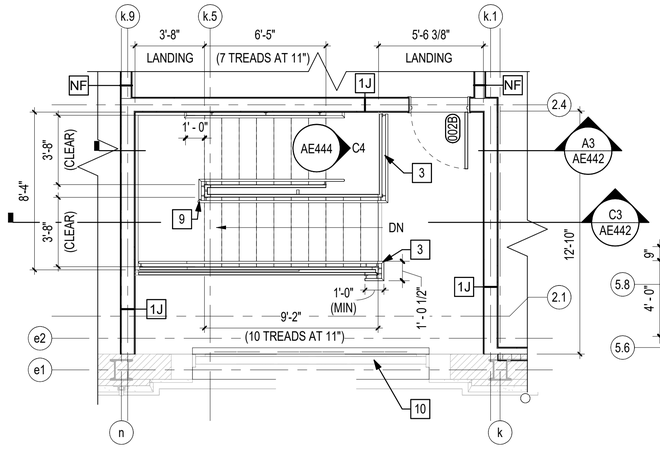

C2 STAIR 002 FIRST FLOOR MEZZANINE PLAN

SCALE: 1/4" = 1'-0" (AE104)

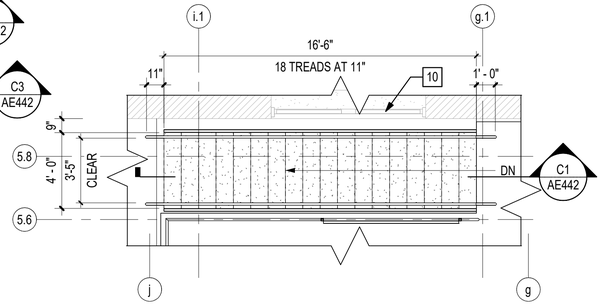

C4 STAIR M110 MEZZANINE FLOOR PLAN

SCALE: 1/4" = 1'-0" (AE104)

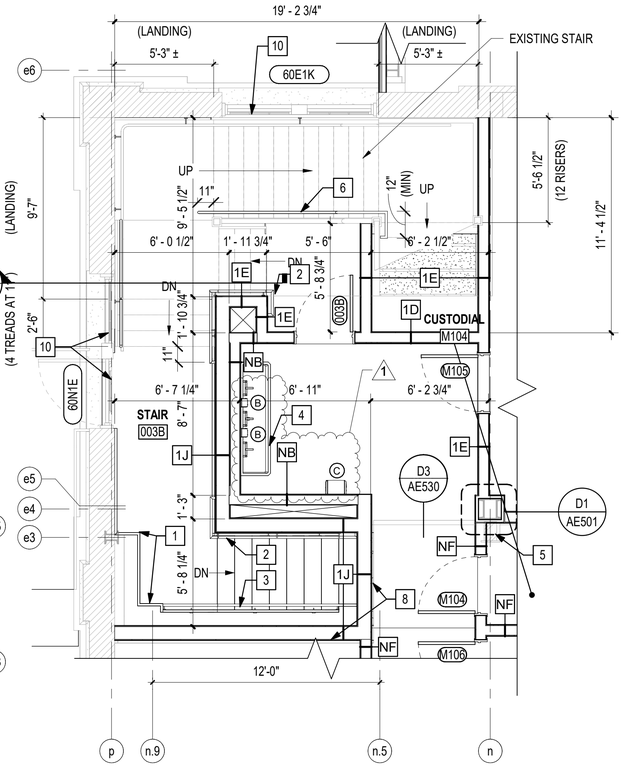

A1 STAIR 003 FIRST FLOOR PLAN

SCALE: 1/4" = 1'-0" (AE102)

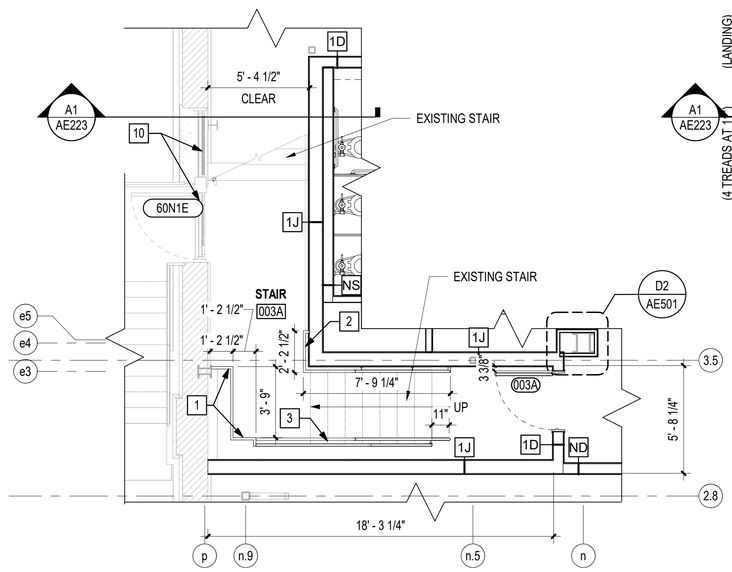

A2 STAIR 003 FIRST FLOOR MEZZANINE PLAN

SCALE: 1/4" = 1'-0" (AE104)

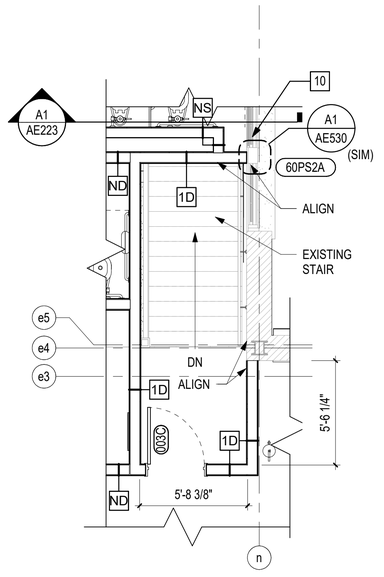

A4 STAIR 003 SECOND FLOOR PLAN

SCALE: 1/4" = 1'-0" (AE105)

GENERAL NOTES

1. SEE SHEET AE001 FOR WALL TYPES.
2. SEE SHEET AE601 FOR DOOR SCHEDULE.
3. SEE SHEET AE622 FOR DOOR RESTORATION SCHEDULES.
4. SEE SHEET AE640 FOR ROOM FINISH SCHEDULE.

KEYNOTES (THIS SHEET ONLY)

1. GUARDRAIL SYSTEM, SEE SIMILAR DETAIL C4/AE444.
2. HANDRAIL, SEE DETAILS A2/AE444 AND A3/AE444.
3. GUARDRAIL AND HANDRAIL, SEE DETAIL B3/AE444.
4. PLUMBING FIXTURE, SEE PLUMBING SHEETS.
5. EXISTING CRANE RAIL BRACKET.
6. IMPROVE GUARDRAIL AND PROVIDE HANDRAIL, SEE DETAIL A4/AE445
7. SELF-CLOSING SAFETY GATE, SEE DETAIL D3/AE445.
8. CONT ALUM ISOLATION JOINT COVER WITH SPRING CLIP.
9. HANDRAIL, SEE DETAIL A4/AE444.
10. REPAIR WOOD WINDOW/DOOR. SEE RESTORATION SCHEDULES.

KEY PLAN

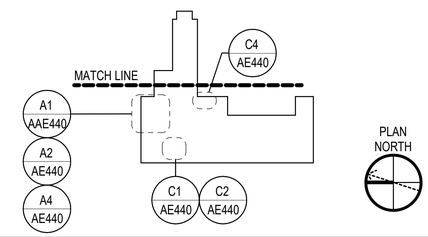

GRAPHIC SCALE(S)

1/4" = 1' - 0"

0 1' 5' 10' 15'

MARK	DESCRIPTION	DATE	APPR
1	AMENDMENT 010	03/20/2026	RSH
	FINAL SUBMISSION	10/01/2025	RSH

NAVFAC

SEAL

OAK POINT ASSOCIATES

APPROVED

FOR COMMANDER NAVFAC

ACTIVITY

SATISFACTORY TO DATE

DESIGNER JMR

DRAWN BY MJD

CHECKED BY RSH

DESIGN MANAGER T. CARLETON

PROJECT MANAGER L. LYONS

FEAD/PM&E

FIRE PROTECTION S. RUCINSKI

DEPARTMENT OF THE NAVY
NAVAL FACILITIES ENGINEERING SYSTEMS COMMAND
ROICC-ME
NAVAL FACILITIES ENGINEERING SYSTEMS COMMAND - MID-ATLANTIC
PORTSMOUTH NAVAL SHIPYARD - KITTERY, ME
PORTSMOUTH NAVAL SHIPYARD
KITTERY, ME
B60 REPAIRS
ENLARGED STAIR PLANS 1

EPROJECT NO.: 1740579

NAVFAC DRAWING NO.

SHEET 119 OF 282

AE440

DRAWFORM REVISION: 14 SEP 2023

3/23/2026 1:17:37 PM AE440
C:\Users\mdonovan\Documents\22103.25_BLDG60_ARCHITECTURAL-V23_mdonovan8VFXR.rvt

UNCLASSIFIED