


3/20/2026 1:29:35 PM P-701
C:\Users\richards\Documents\22103.25_BLDG60_MECHANICAL-V23_swhic882ZD.rvt

D

C

B

A

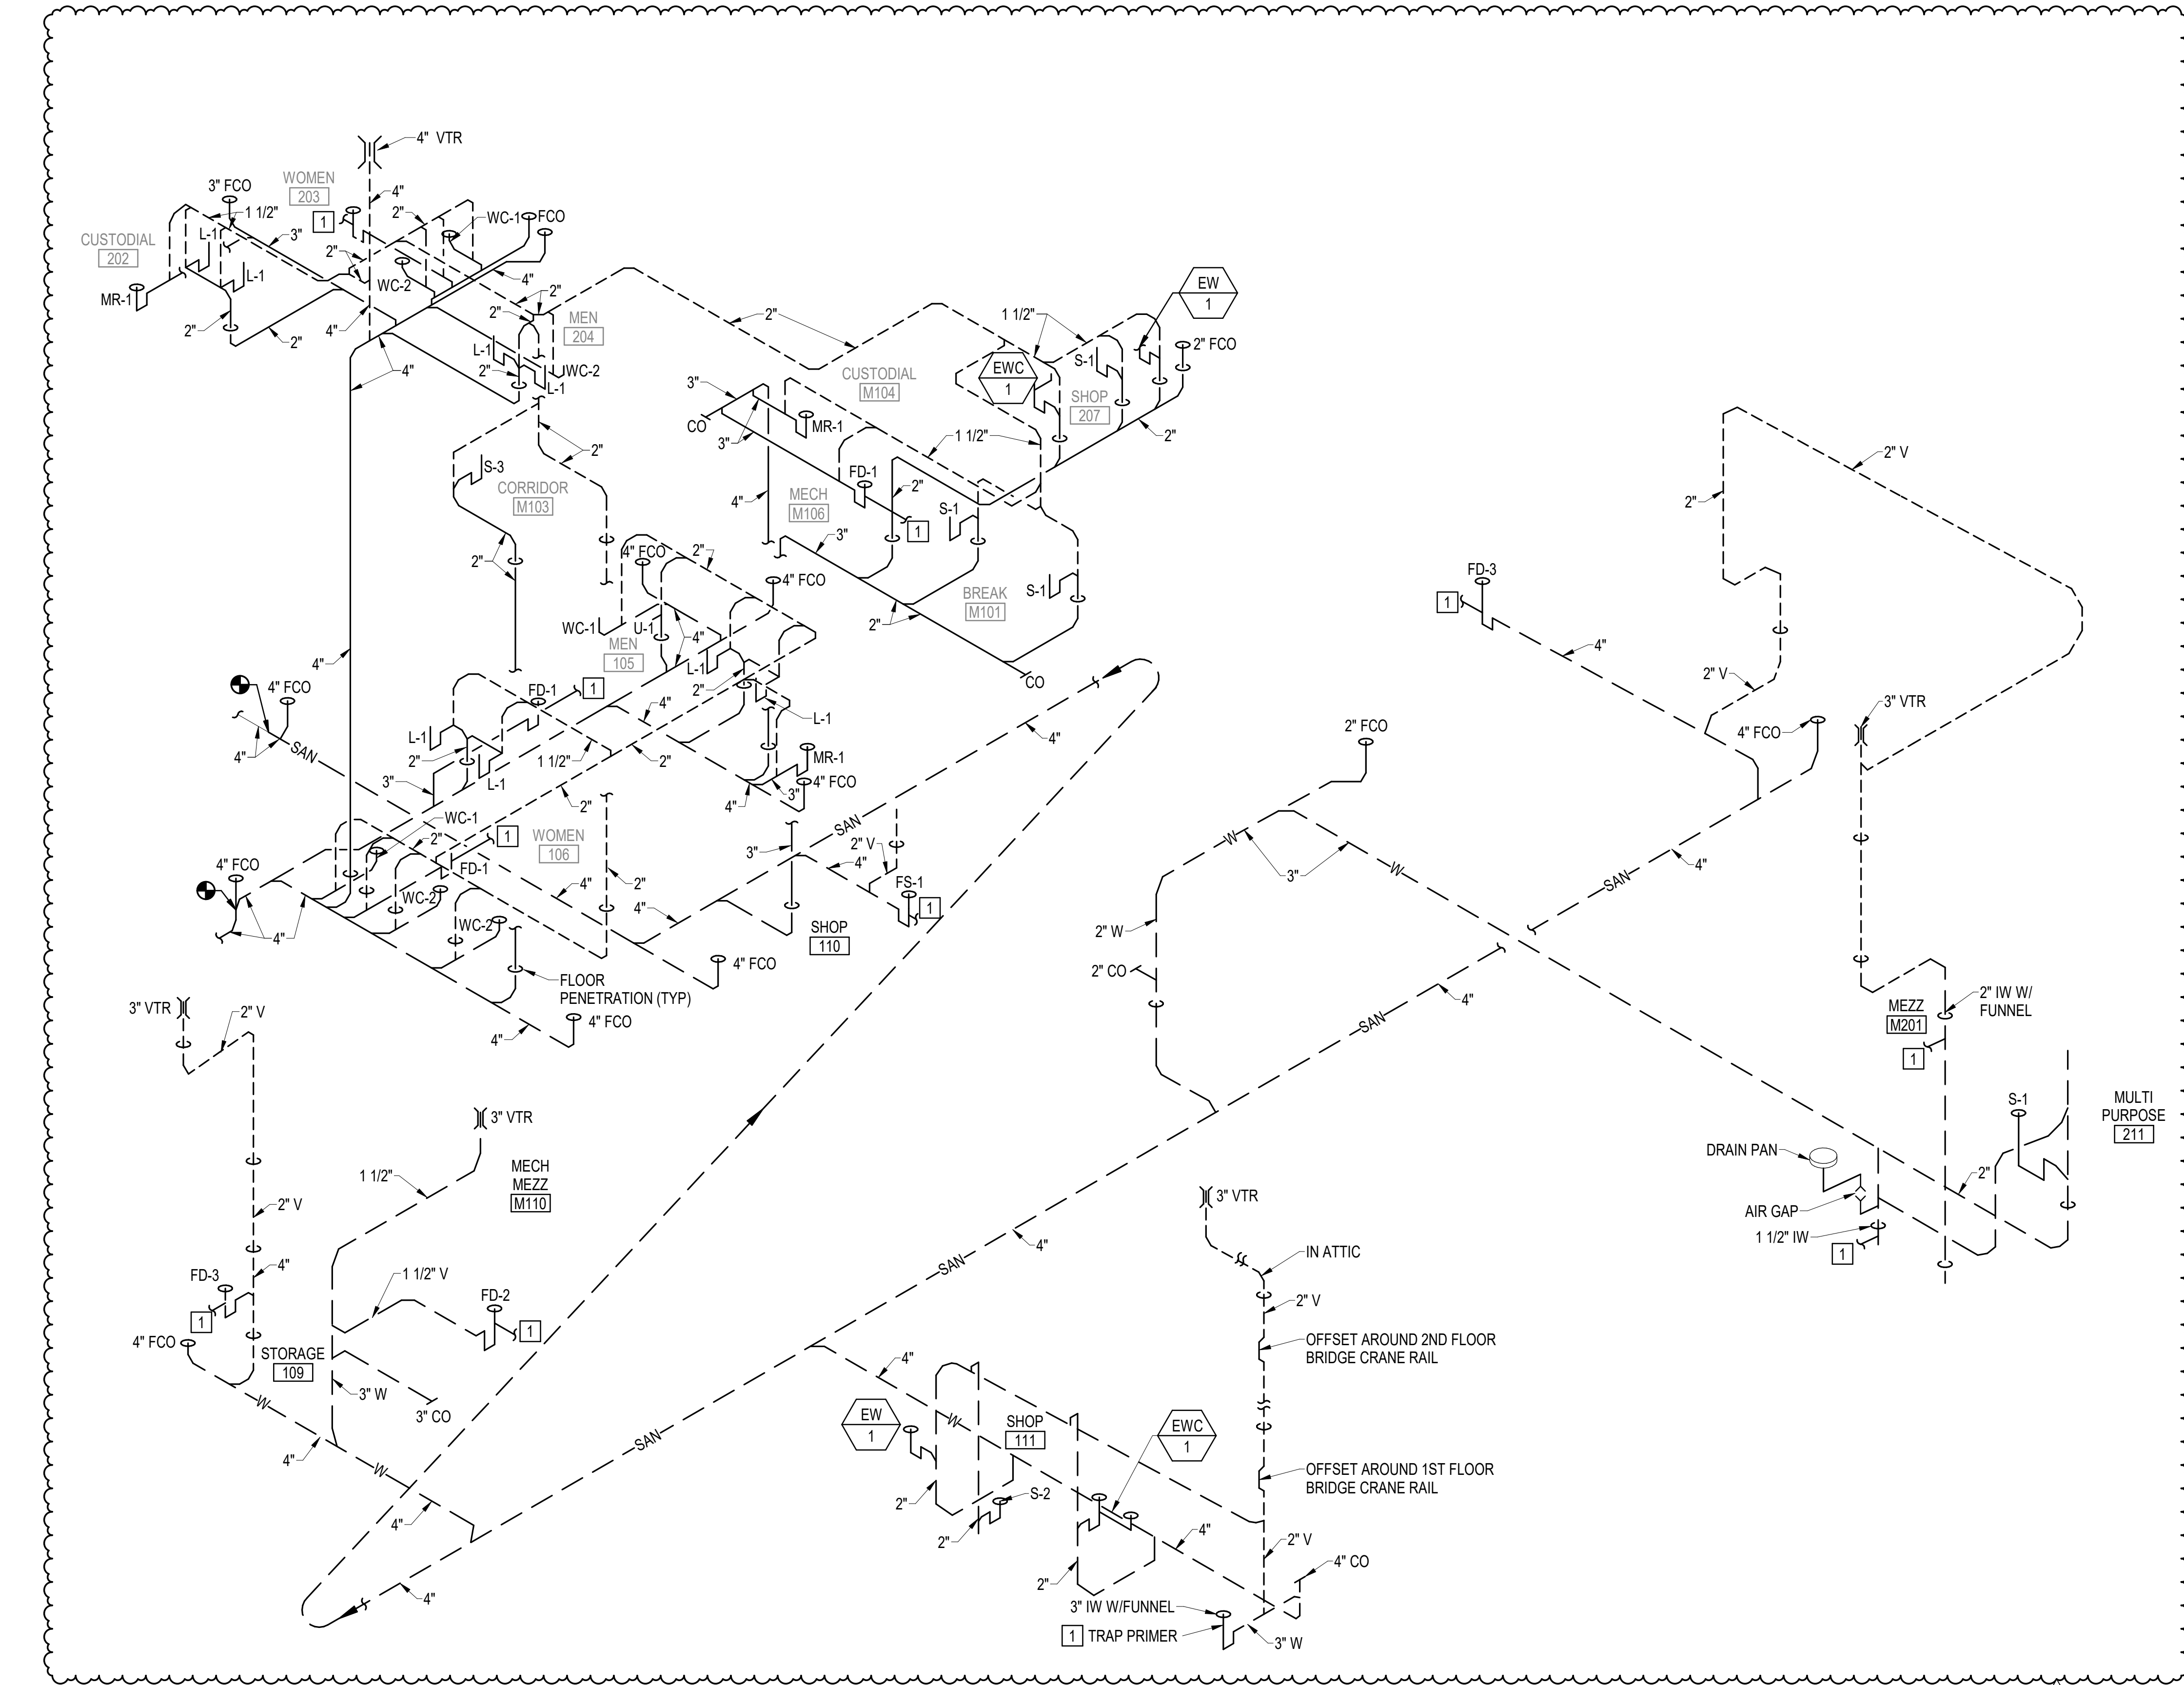

C1 **SANITARY AND VENT PLUMBING RISER DIAGRAM**
SCALE: NOT TO SCALE

GENERAL NOTES

- SEE P-001 FOR PLUMBING LEGENDS, ABBREVIATIONS AND GENERAL NOTES.

KEYNOTES (THIS SHEET ONLY)

- 1/2" TRAP PRIMER CONNECTION. SEE PLANS FOR PIPE ROUTING TO TRAP PRIMER ASSEMBLY.

DATE	DESCRIPTION	MARK	REVISION
03/20/2026	FINAL SUBMISSION	Δ	AMENDMENT 010



APPROVED
FOR COMMANDER NAVFAC
ACTIVITY
SATISFACTORY TO DATE
DESIGNER RNC
DRAWN BY SRW
CHECKED BY MSA
DESIGN MANAGER T. CARLETON
PROJECT MANAGER L. LYONS
HEADLINE
FIRE PROTECTION S. RUCINSKI

DEPARTMENT OF THE NAVY	NAVAL FACILITIES ENGINEERING SYSTEMS COMMAND
NAVAL FACILITIES ENGINEERING SYSTEMS COMMAND - MID-ATLANTIC	PORTSMOUTH NAVAL SHIPYARD - KITTEERY, ME
ROCCC-ME	B60 REPAIRS
PORTSMOUTH NAVAL SHIPYARD	PLUMBING RISER DIAGRAM

PROJECT NO.	1740579
NAVFAC DRAWINGS NO.	

SHEET	183	OF	282
-------	-----	----	-----

P-701

DRAWING REVISION: 14 SEP 2023

B UNCLASSIFIED

A

3 UNCLASSIFIED

5

4

2

1