



3/20/2026 1:29:31 PM P-402
C:\Users\richards\Documents\22103.25_BLDG60_MECHANICAL-V23_whitec82ZD.rvt

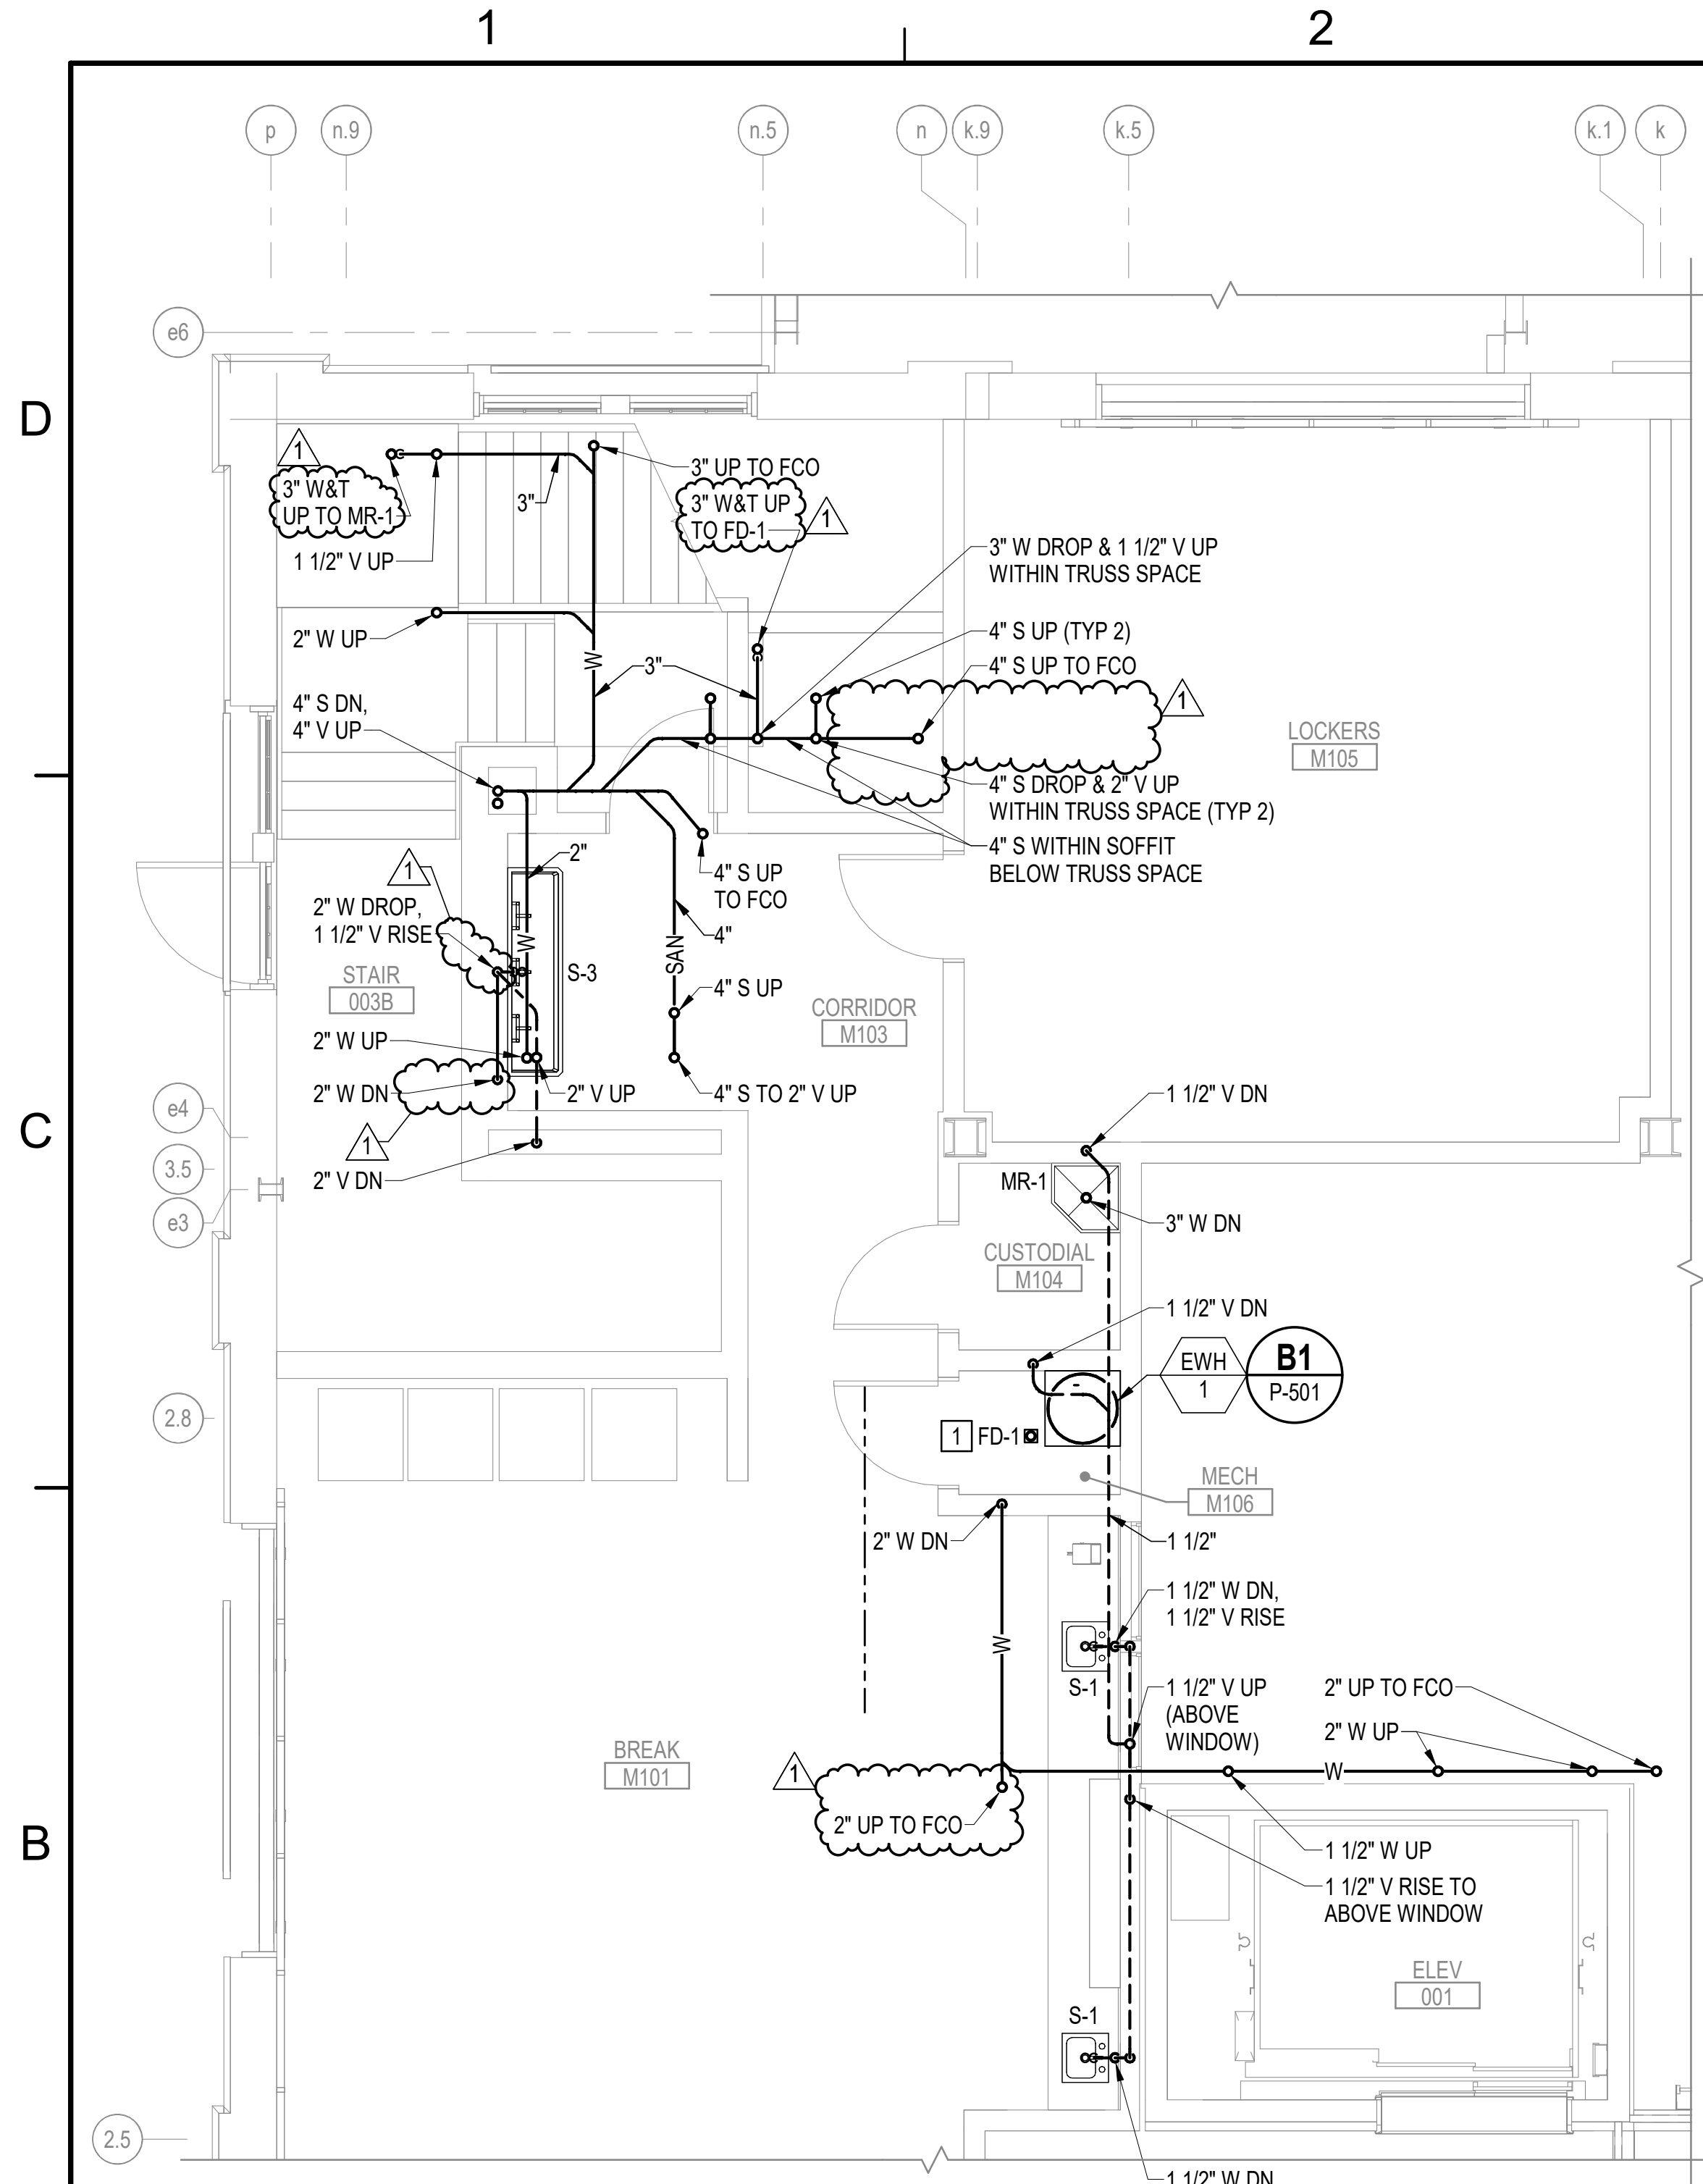

A1 ENLARGED FIRST FLOOR MEZZANINE SANITARY WASTE AND VENT PART PLAN
SCALE: 1/4" = 1'-0" (P-106)

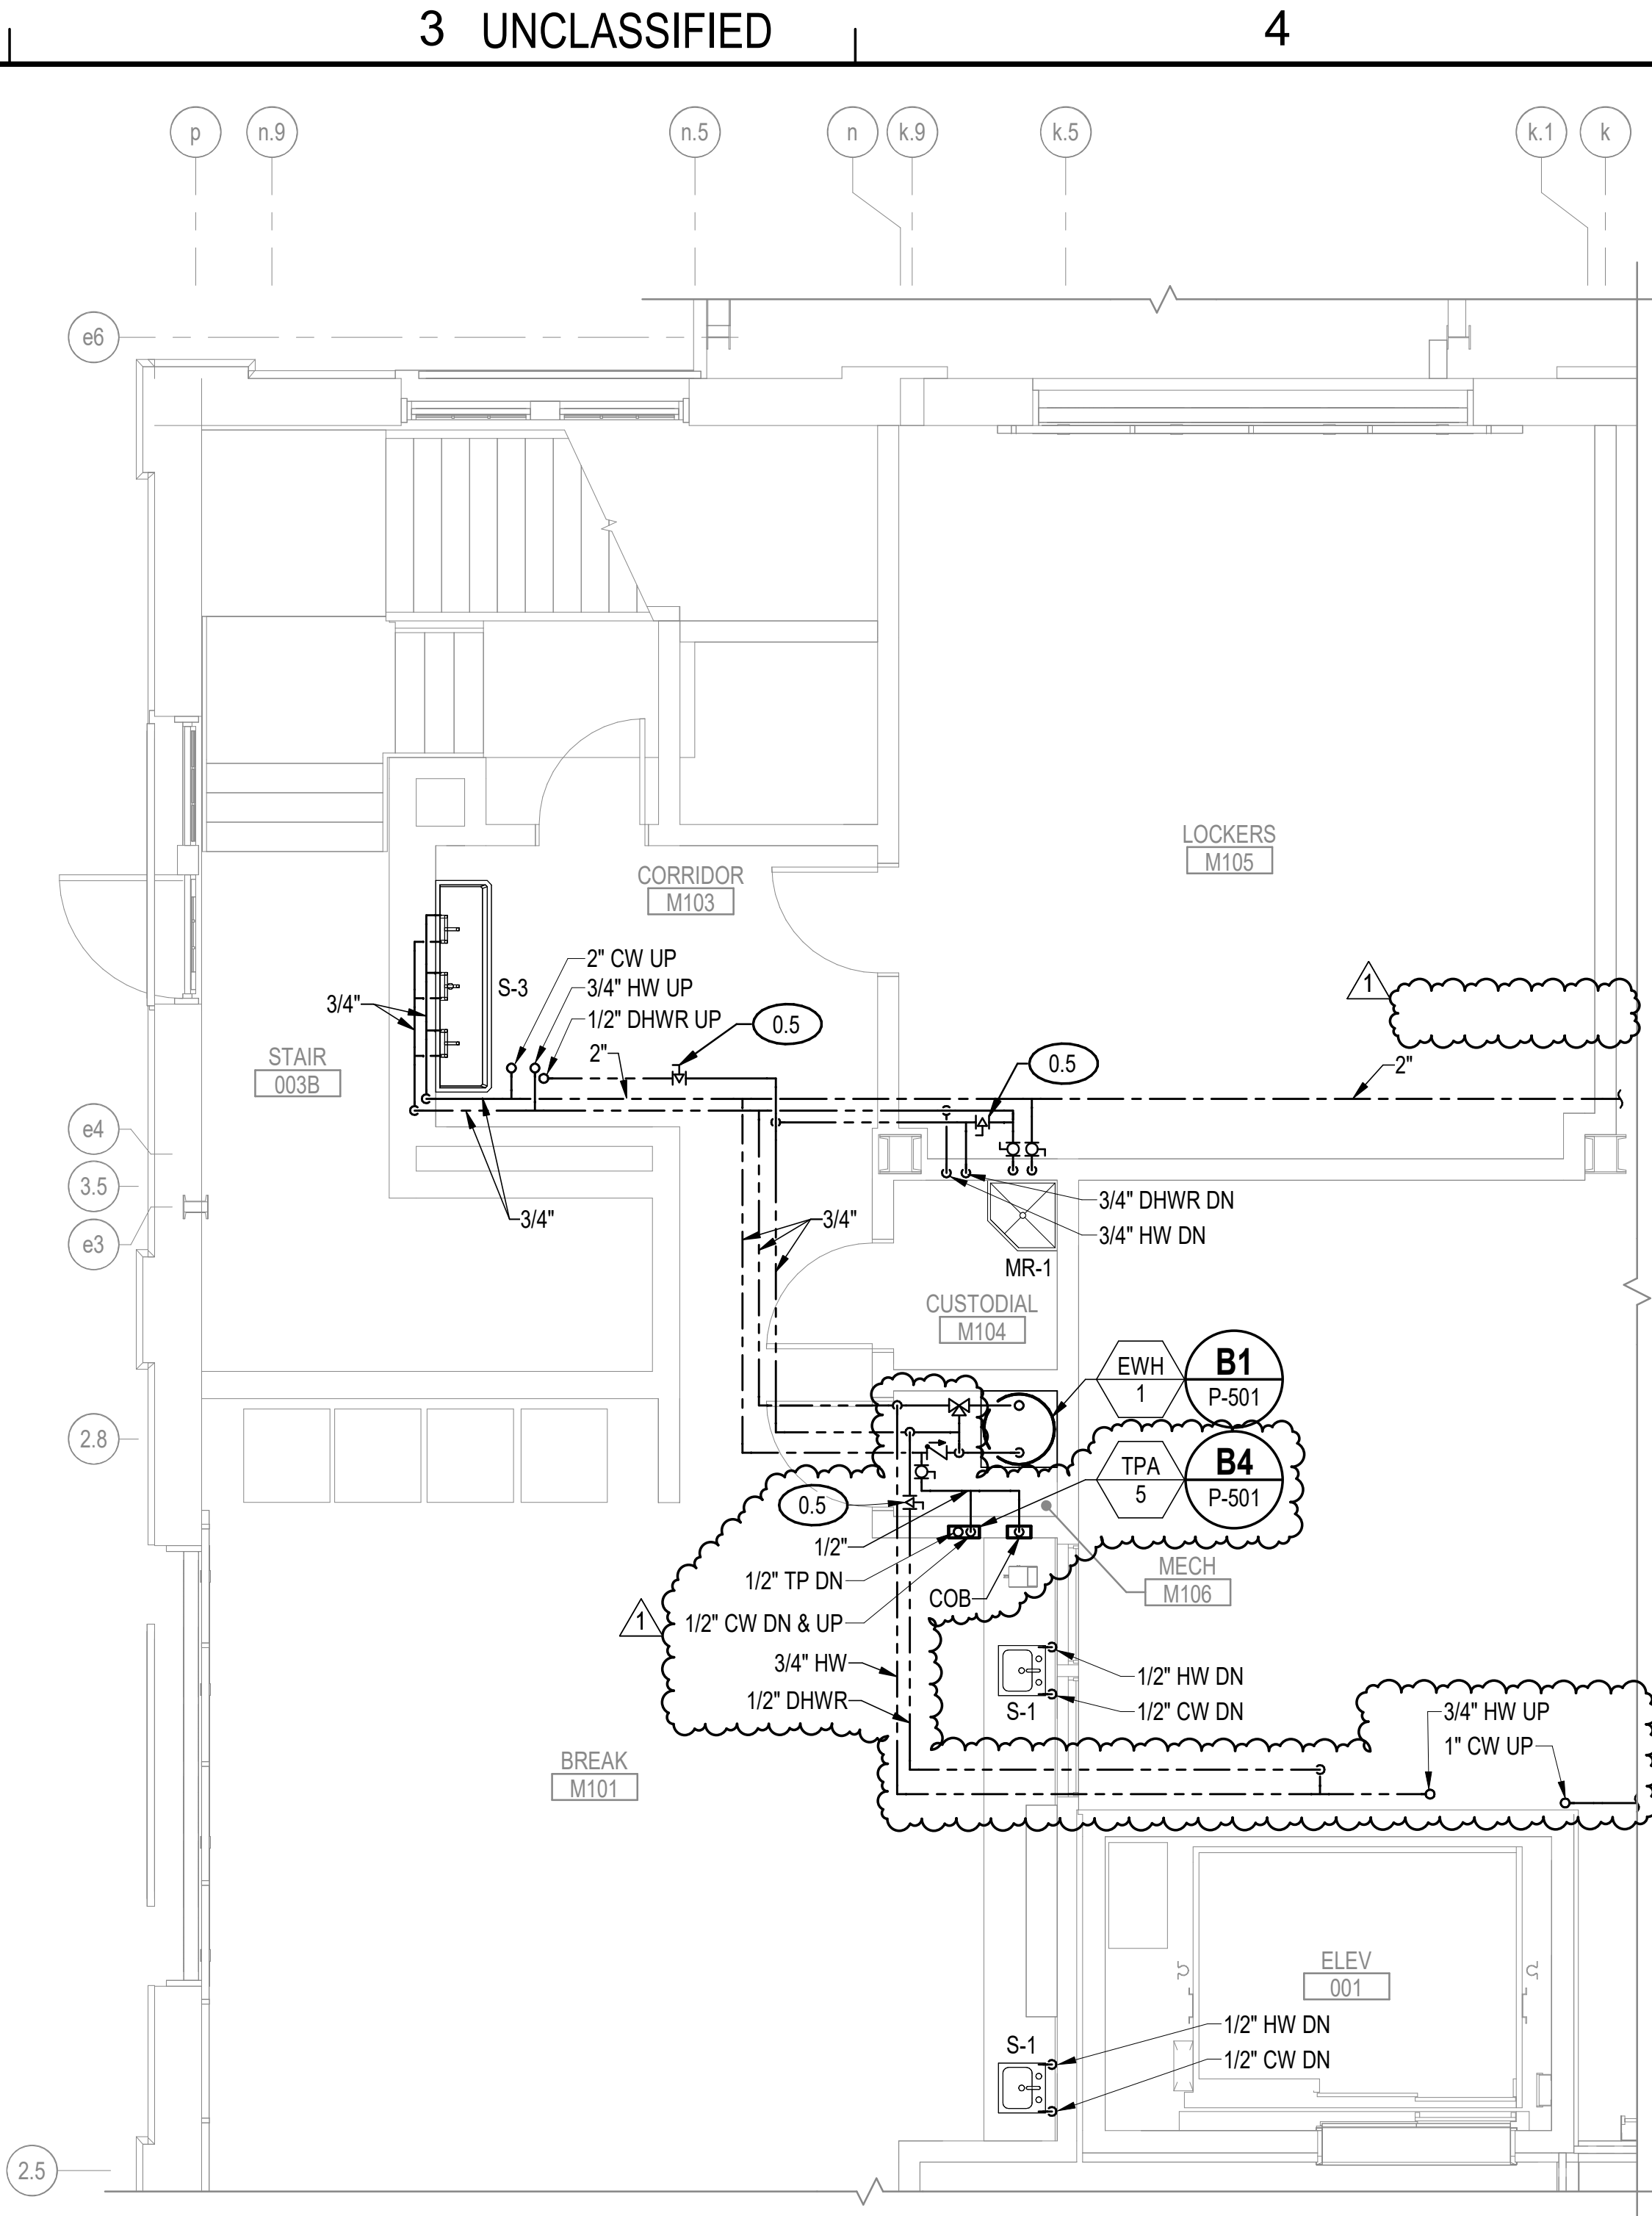

A3 ENLARGED FIRST FLOOR MEZZANINE DOMESTIC WATER SUPPLY PART PLAN
SCALE: 1/4" = 1'-0" (P-106)



GENERAL NOTES

- SEE P-001 FOR PLUMBING LEGENDS, ABBREVIATIONS AND GENERAL NOTES.
- COORDINATE THE INSTALLATION OF PIPING AND EQUIPMENT TO MAINTAIN MANDATORY CLEARANCE ZONES AROUND CRANE RAILS AND BRIDGE CRANE OPERATIONAL TRAVEL PATH.

KEYNOTES (THIS SHEET ONLY)

- 1 RUN THE WATER HEATER AUXILIARY DRAIN PAN PIPING TO FD-1.

APPROVED	
FOR COMMANDER NAVFAC	
ACTIVITY	
SATISFACTORY TO DATE	
DESIGNER	RNC
DRAWN BY	SRW
CHECKED BY	MSA
DESIGN MANAGER	T. CARLETON
PROJECT MANAGER	L. LYONS
HEADLINE	
FIRE PROTECTION	S. RUCINSKI
NAVAL FACILITIES ENGINEERING SYSTEMS COMMAND - MID-ATLANTIC	
PORTSMOUTH NAVAL SHIPYARD - KITTERY, ME	
B60 REPAIRS	
ENLARGED PLUMBING PART PLANS 2	

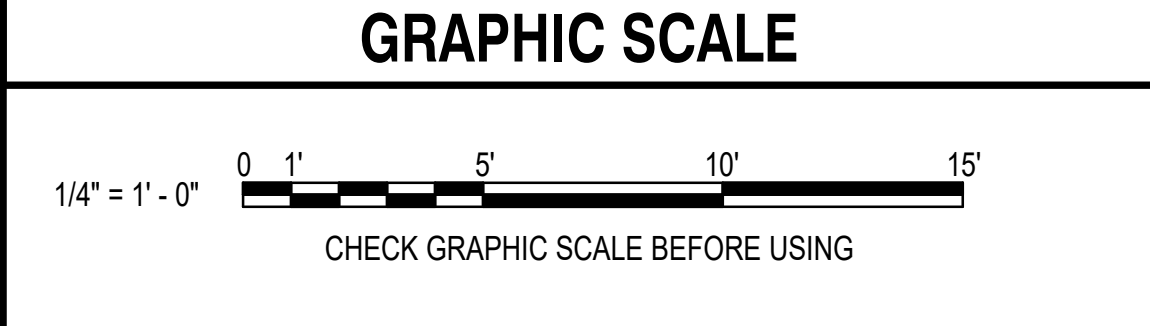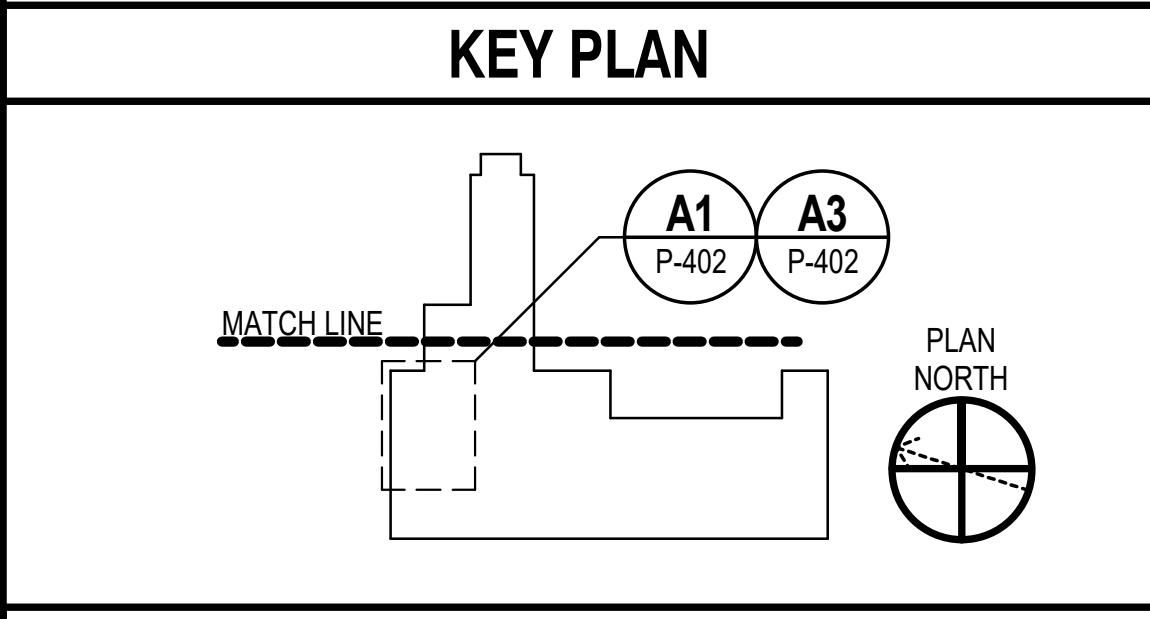

RSR	03/20/2026	RSR	10/07/2025	RSR	APR
AMENDMENT 010	FINAL SUBMISSION	MARK	DESCRIPTION	DATE	
UNCLASSIFIED					
B60 REPAIRS					
ENLARGED PLUMBING PART PLANS 2					
PROJECT NO. 1740579					
NAVIFAC DRAWINGS NO.					
SHEET 179 OF 282					
P-402					
DRAWING REVISION: 14 SEP 2023					