


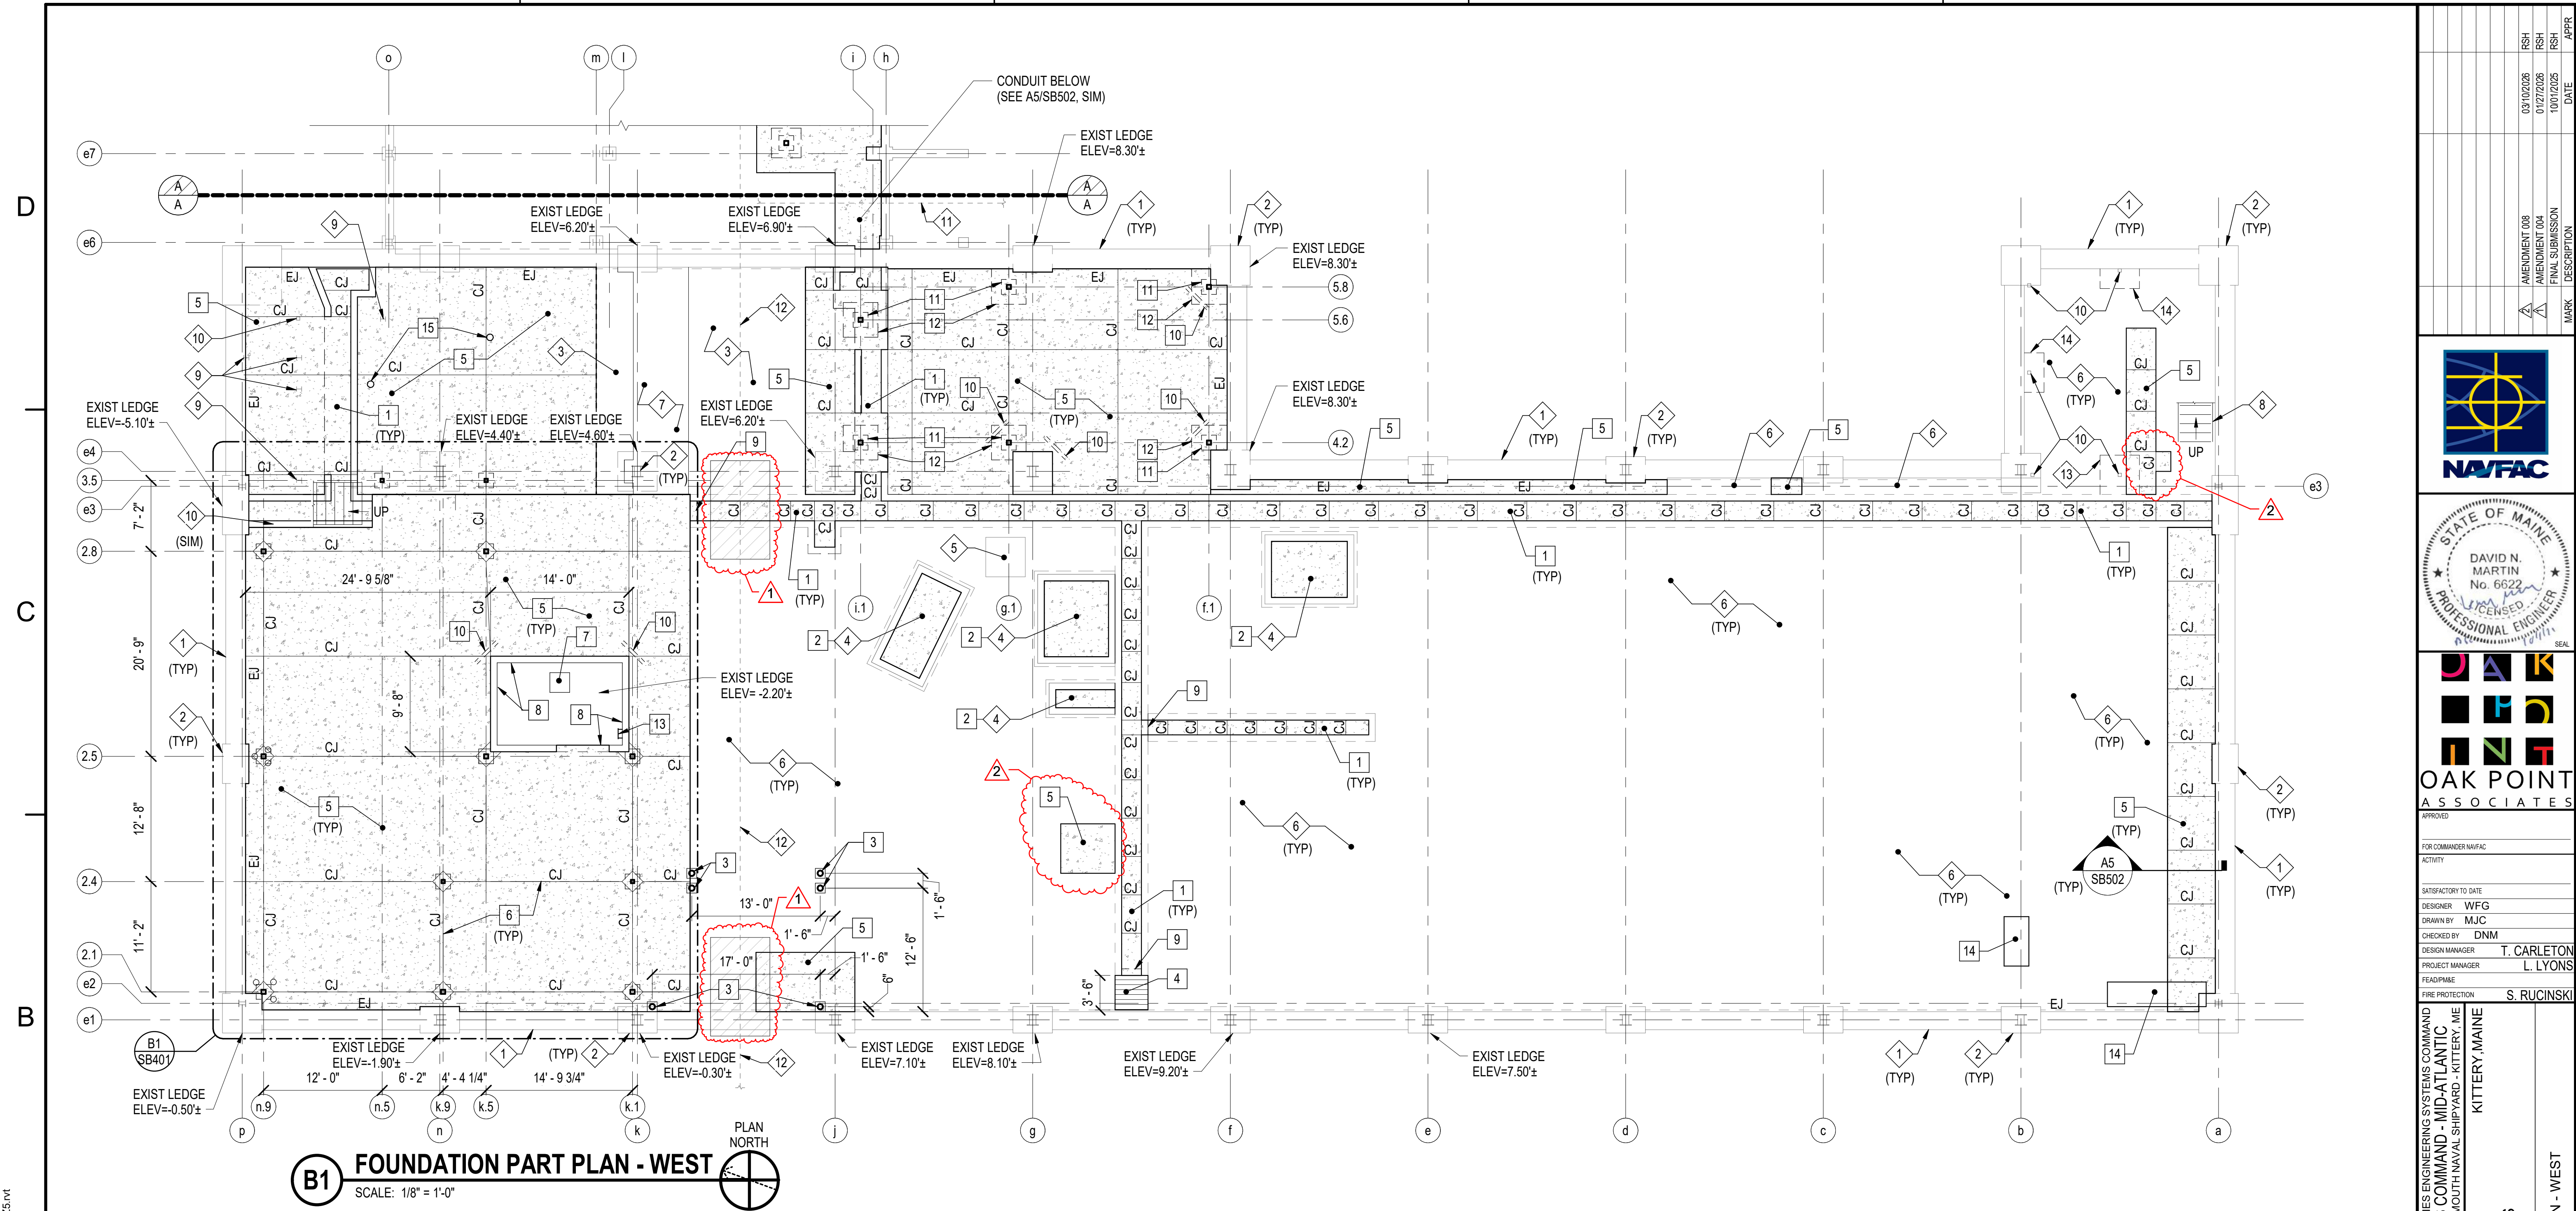


B1 FOUNDATION PART PLAN - WEST
SCALE: 1/8" = 1'-0"

GENERAL NOTES

1. TOP OF EXISTING AND NEW SLAB-ON-GROUND ELEVATION = 10.30±.
2. REFER TO SHEET SB401 FOR PILE AND PILE CAP LAYOUT.
3. EXISTING LEDGE ELEVATIONS ARE APPROXIMATE AND ARE BASED ON EXISTING REFERENCE DRAWING 60-02-2.

LEGEND

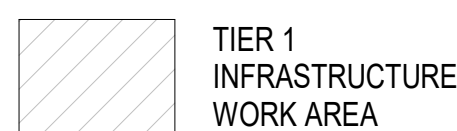

TIER 1
INFRASTRUCTURE
WORK AREA

EXISTING KEYNOTES (THIS SHEET ONLY)


- 1 EXISTING REINFORCED CONCRETE FOUNDATION WALL.
- 2 EXISTING REINFORCED CONCRETE PIER.
- 3 EXISTING 6"± THICK REINFORCED CONCRETE SLAB-ON-GROUND WITH 1-1/2"± CONCRETE TOPPING SLAB.
- 4 EXISTING CONCRETE PIT SUPPORTING EXISTING EQUIPMENT. DEPTH OF PIT INDICATED ON SHEET SD102.
- 5 EXISTING REINFORCED CONCRETE JIB CRANE FOUNDATION.
- 6 EXISTING 7-1/2"± THICK REINFORCED CONCRETE SLAB-ON-GROUND.
- 7 EXISTING 6"± THICK REINFORCED CONCRETE SLAB-ON-GROUND AND 1-1/2"± THICK WOOD PLANK FLOOR BOARDS.

- 8 EXISTING STEEL CHANNEL STAIR STRINGERS AND CONCRETE FILLED METAL PAN STAIR TREADS.
- 9 EXISTING W6± STEEL COLUMN SUPPORTING EXISTING STAIRS OR MEZZANINE.
- 10 EXISTING HSS STEEL COLUMN SUPPORTING EXISTING STAIRS OR MEZZANINE.
- 11 EXISTING STORM DRAIN LINE BELOW SLAB. (TIER 1 INFRASTRUCTURE 3-Feet EITHER SIDE OF WATER LINE). SEE CIVIL DRAWINGS.
- 12 EXISTING WATER LINE BELOW SLAB. SEE CIVIL DRAWINGS.
- 13 EXISTING 4'-0"x4'-0"x1'-0"± REINFORCED CONCRETE FOOTING.
- 14 EXISTING 2'-0"x4'-0"x1'-0"± REINFORCED CONCRETE FOOTING.


KEYNOTES (THIS SHEET ONLY)

- 1 INFILL EXISTING TRENCH WITH CONCRETE. SEE DETAIL C3/SB501.
- 2 INFILL EXISTING EQUIPMENT PIT WITH CONCRETE. SEE DETAIL B4/SB502.
- 3 INTERIOR BOLLARD. SEE DETAIL B5/SB502.
- 4 2-1/2" x 3/16" BANDAED EDGE GALVANIZED STEEL GRATING. SEE DETAIL C4/SB503.
- 5 7-1/2" THICK REINFORCED CONCRETE SLAB-ON-GROUND. SEE DETAIL A4/SB501.
- 6 SAWCUT CONTROL JOINT. SEE DETAIL A4/SB501.
- 7 2'-0"x2'-0"x2'-0" ELEVATOR SUMP PIT. SEE DETAIL C2/SB502.
- 8 8" REINFORCED CONCRETE FOUNDATION WALL. SEE DETAIL C1/SB502.
- 9 REINFORCED CONCRETE BULKHEAD. SEE DETAIL C4/SB501.
- 10 (2) DIAGONAL #5S, 3'-0" LONG, SPACED 4" ON-CENTER AND LOCATED 4" FROM CORNER.
- 11 1'-6"x1'-6" REINFORCED CONCRETE PIER. TOP OF PIER ELEVATION = 9.63'. SEE DETAIL C4/SB502 (SIMILAR).
- 12 REINFORCED CONCRETE FOOTING. BOTTOM OF FOOTING ELEVATION = 7.00'.
- 13 ELEVATOR PIT LADDER. SEE DETAIL A1/SB501.
- 14 HOUSEKEEPING PAD. SEE DETAIL B4/SB501. COORDINATE EXACT SIZE WITH ELECTRICAL DRAWINGS.
- 15 FLOOR DRAIN.

KEY PLAN

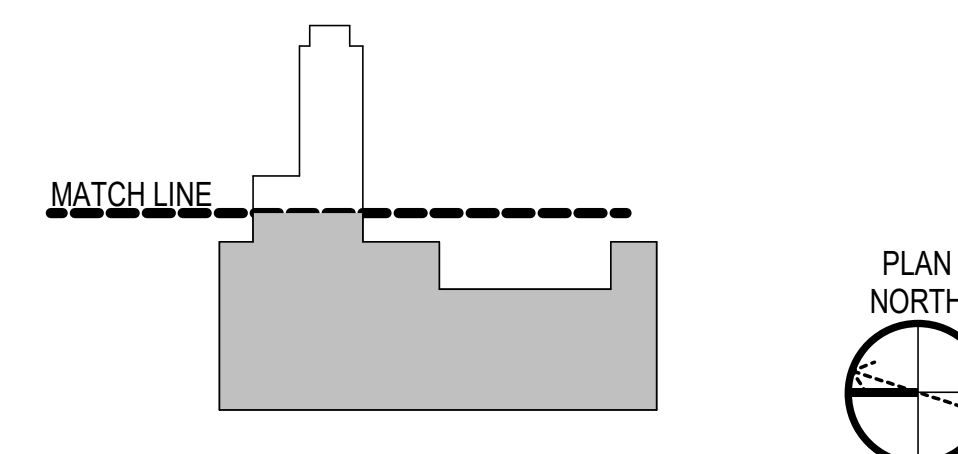

GRAPHIC SCALE(S)

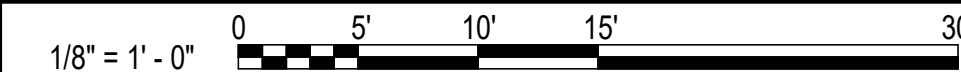

APPROVED	DATE	APPROVED	DATE
DAVID N. MARTIN	03/02/2026	DAVID N. MARTIN	03/02/2026
PROFESSIONAL ENGINEER	01/27/2026	PROFESSIONAL ENGINEER	01/27/2026
NO. 6622	10/07/2025	NO. 6622	10/07/2025
AMENDMENT 008	AMENDMENT 004	AMENDMENT 008	AMENDMENT 004
FINAL SUBMISSION	FINAL SUBMISSION	FINAL SUBMISSION	FINAL SUBMISSION
MARK	DESCRIPTION	MARK	DESCRIPTION
NAVFAC		NAVFAC	
STATE OF MAINE		STATE OF MAINE	
DAVID N. MARTIN		DAVID N. MARTIN	
No. 6622		No. 6622	
PROFESSIONAL ENGINEER		PROFESSIONAL ENGINEER	
SEAL		SEAL	
OAK POINT ASSOCIATES		OAK POINT ASSOCIATES	
FOR COMMANDER NAVFAC		FOR COMMANDER NAVFAC	
ACTIVITY		ACTIVITY	
SATISFACTORY TO DATE		SATISFACTORY TO DATE	
DESIGNER WFG		DESIGNER WFG	
DRAWN BY MJC		DRAWN BY MJC	
CHECKED BY DNM		CHECKED BY DNM	
DESIGN MANAGER T. CARLETON		DESIGN MANAGER T. CARLETON	
PROJECT MANAGER L. LYONS		PROJECT MANAGER L. LYONS	
FEEDBACK		FEEDBACK	
FIRE PROTECTION S. RUCINSKI		FIRE PROTECTION S. RUCINSKI	
NAVAL FACILITIES ENGINEERING SYSTEMS COMMAND		NAVAL FACILITIES ENGINEERING SYSTEMS COMMAND	
NAVAL FACILITIES ENGINEERING SYSTEMS COMMAND - MID-ATLANTIC		NAVAL FACILITIES ENGINEERING SYSTEMS COMMAND - MID-ATLANTIC	
PORTSMOUTH NAVAL SHIPYARD - KITTY HAWK		PORTSMOUTH NAVAL SHIPYARD - KITTY HAWK	
PORTSMOUTH NAVAL SHIPYARD		PORTSMOUTH NAVAL SHIPYARD	
B60 REPAIRS		B60 REPAIRS	
FOUNDATION PART PLAN - WEST		FOUNDATION PART PLAN - WEST	
PROJECT NO. 1740579		PROJECT NO. 1740579	
NAVJAG DRAWING NO.		NAVJAG DRAWING NO.	
SHEET 56 OF 282		SHEET 56 OF 282	
SB102		SB102	
DATE		DATE	
14 SEP 2023		14 SEP 2023	