

3/10/2026 5:00:21 PM SF506
C:\Users\mndonovan\Documents\22103.25_BLDG60_STRUCTURAL-V23_mndonovan\FXR.rvt

1

2

3 UNCLASSIFIED

4


5

D


C

B


A

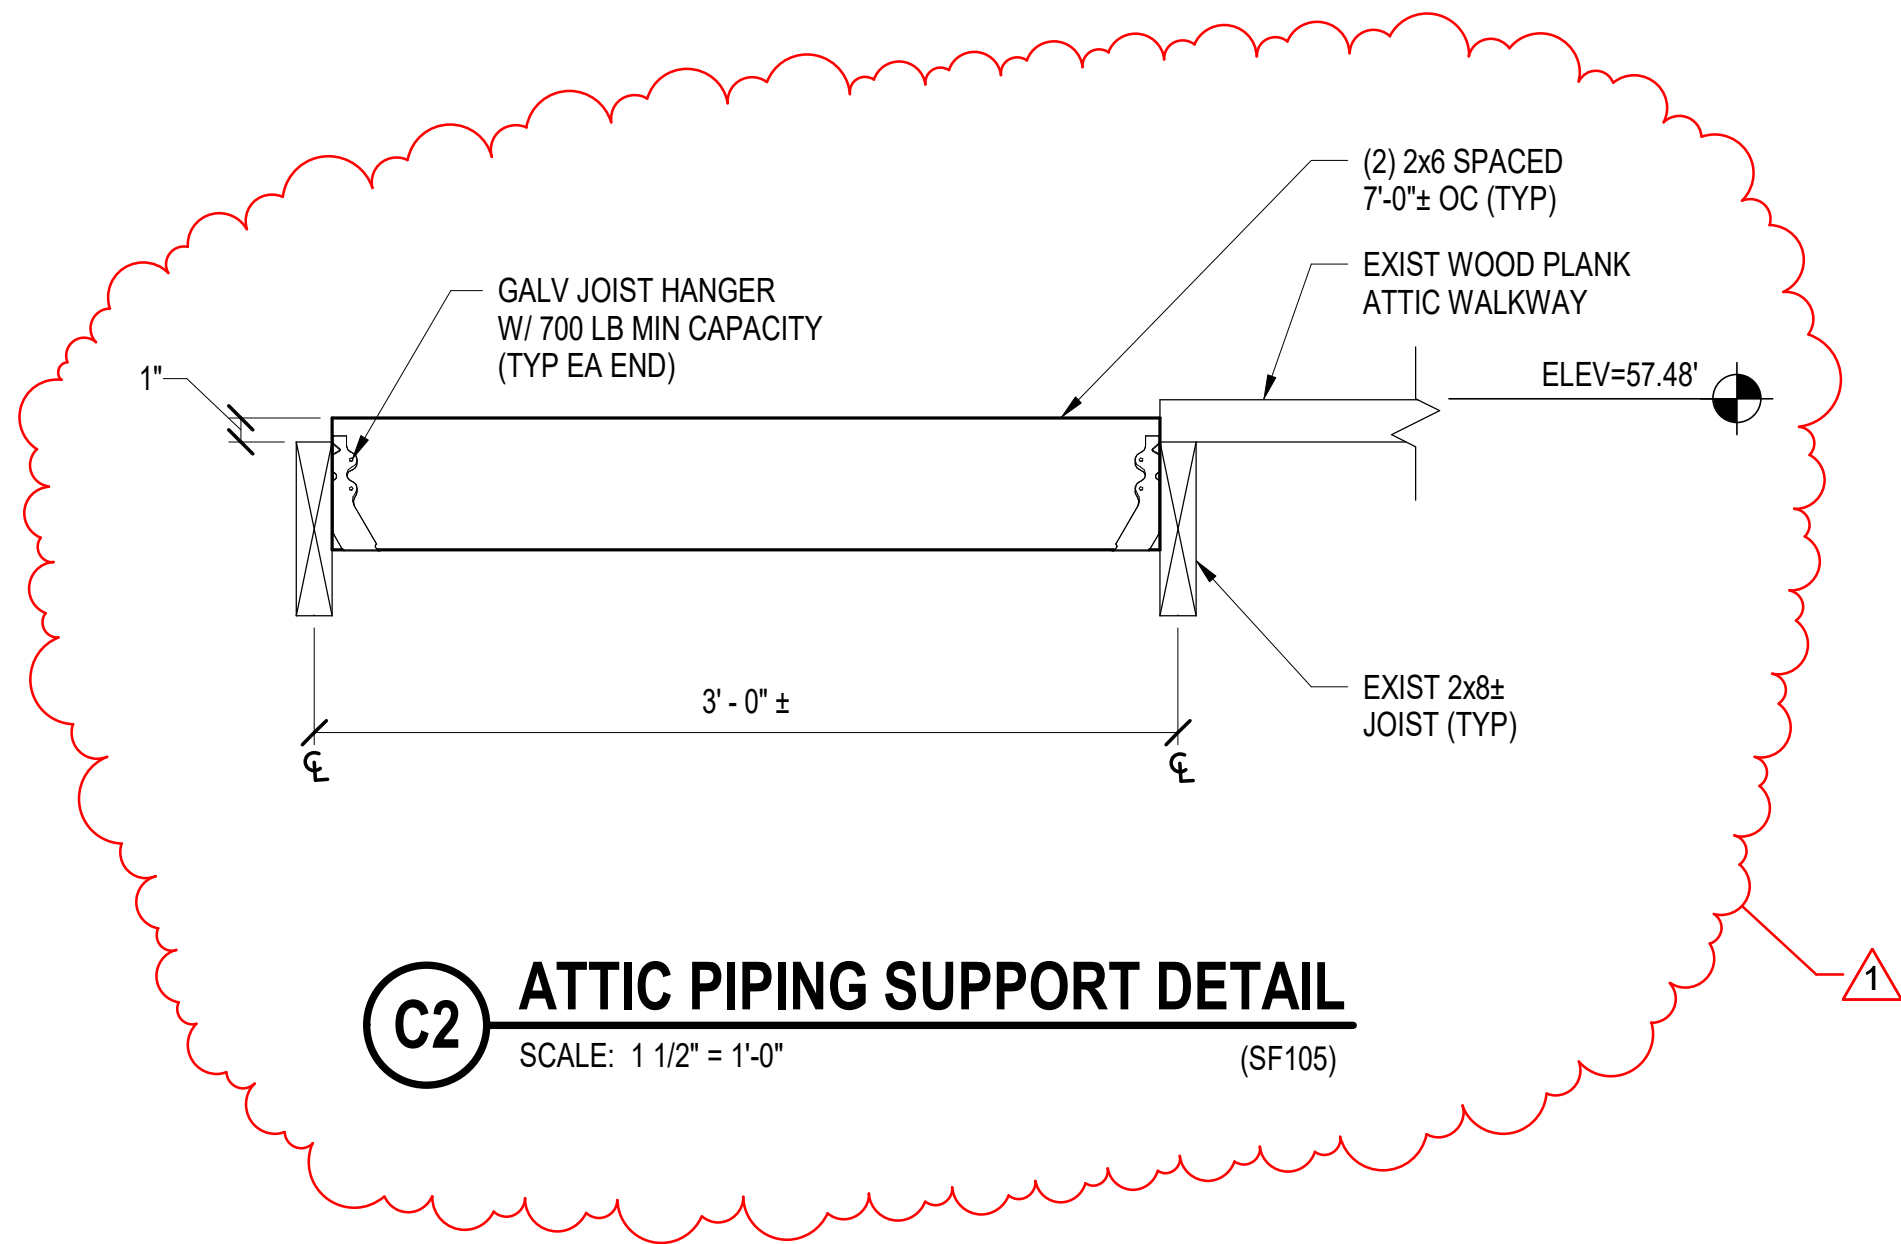


C2 ATTIC PIPING SUPPORT DETAIL
SCALE: 1 1/2" = 1'-0" (SF105)

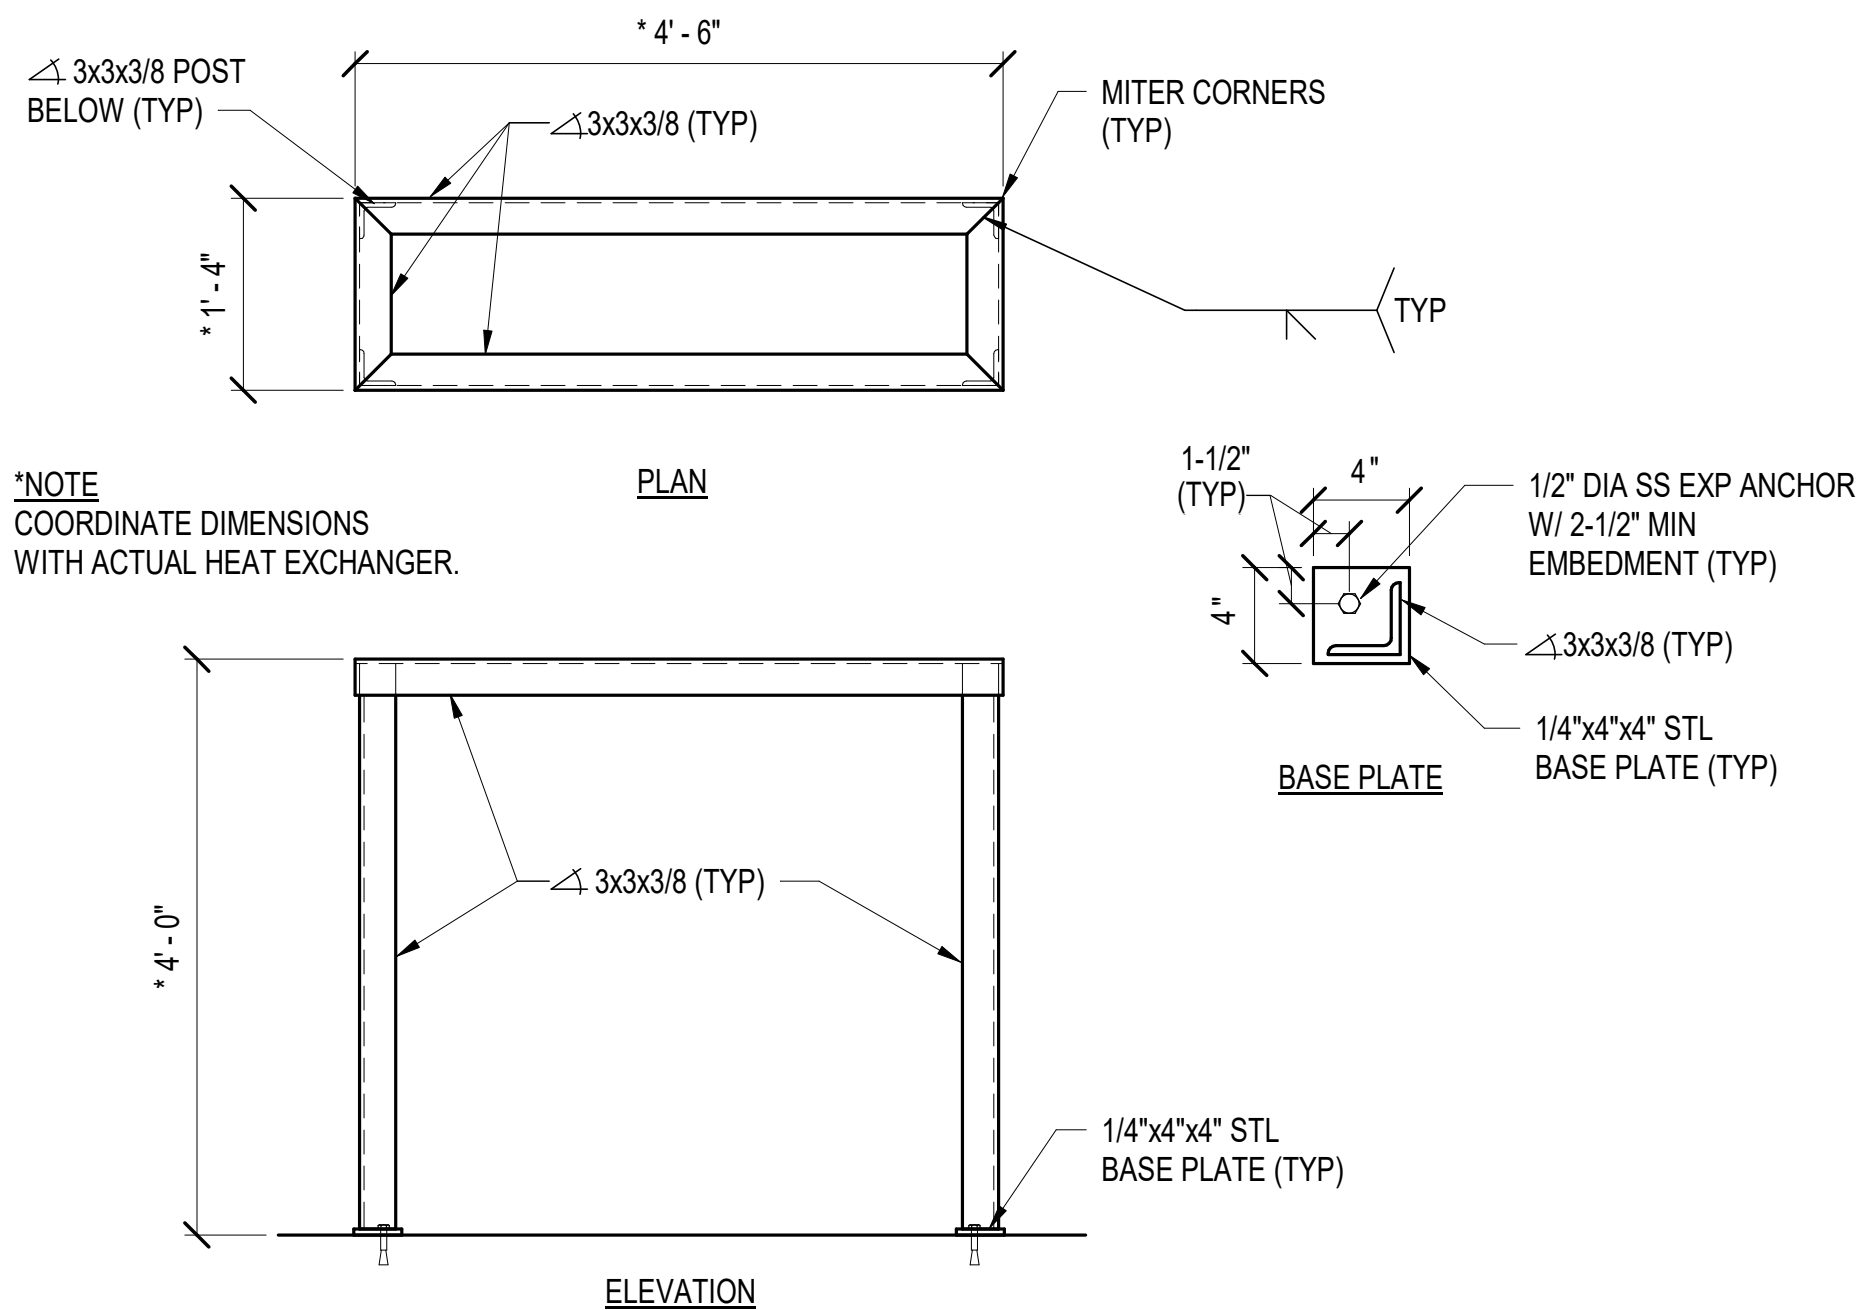

A2 HEAT EXCHANGER SUPPORT FRAME DETAIL
SCALE: 3/4" = 1'-0" (M-504)

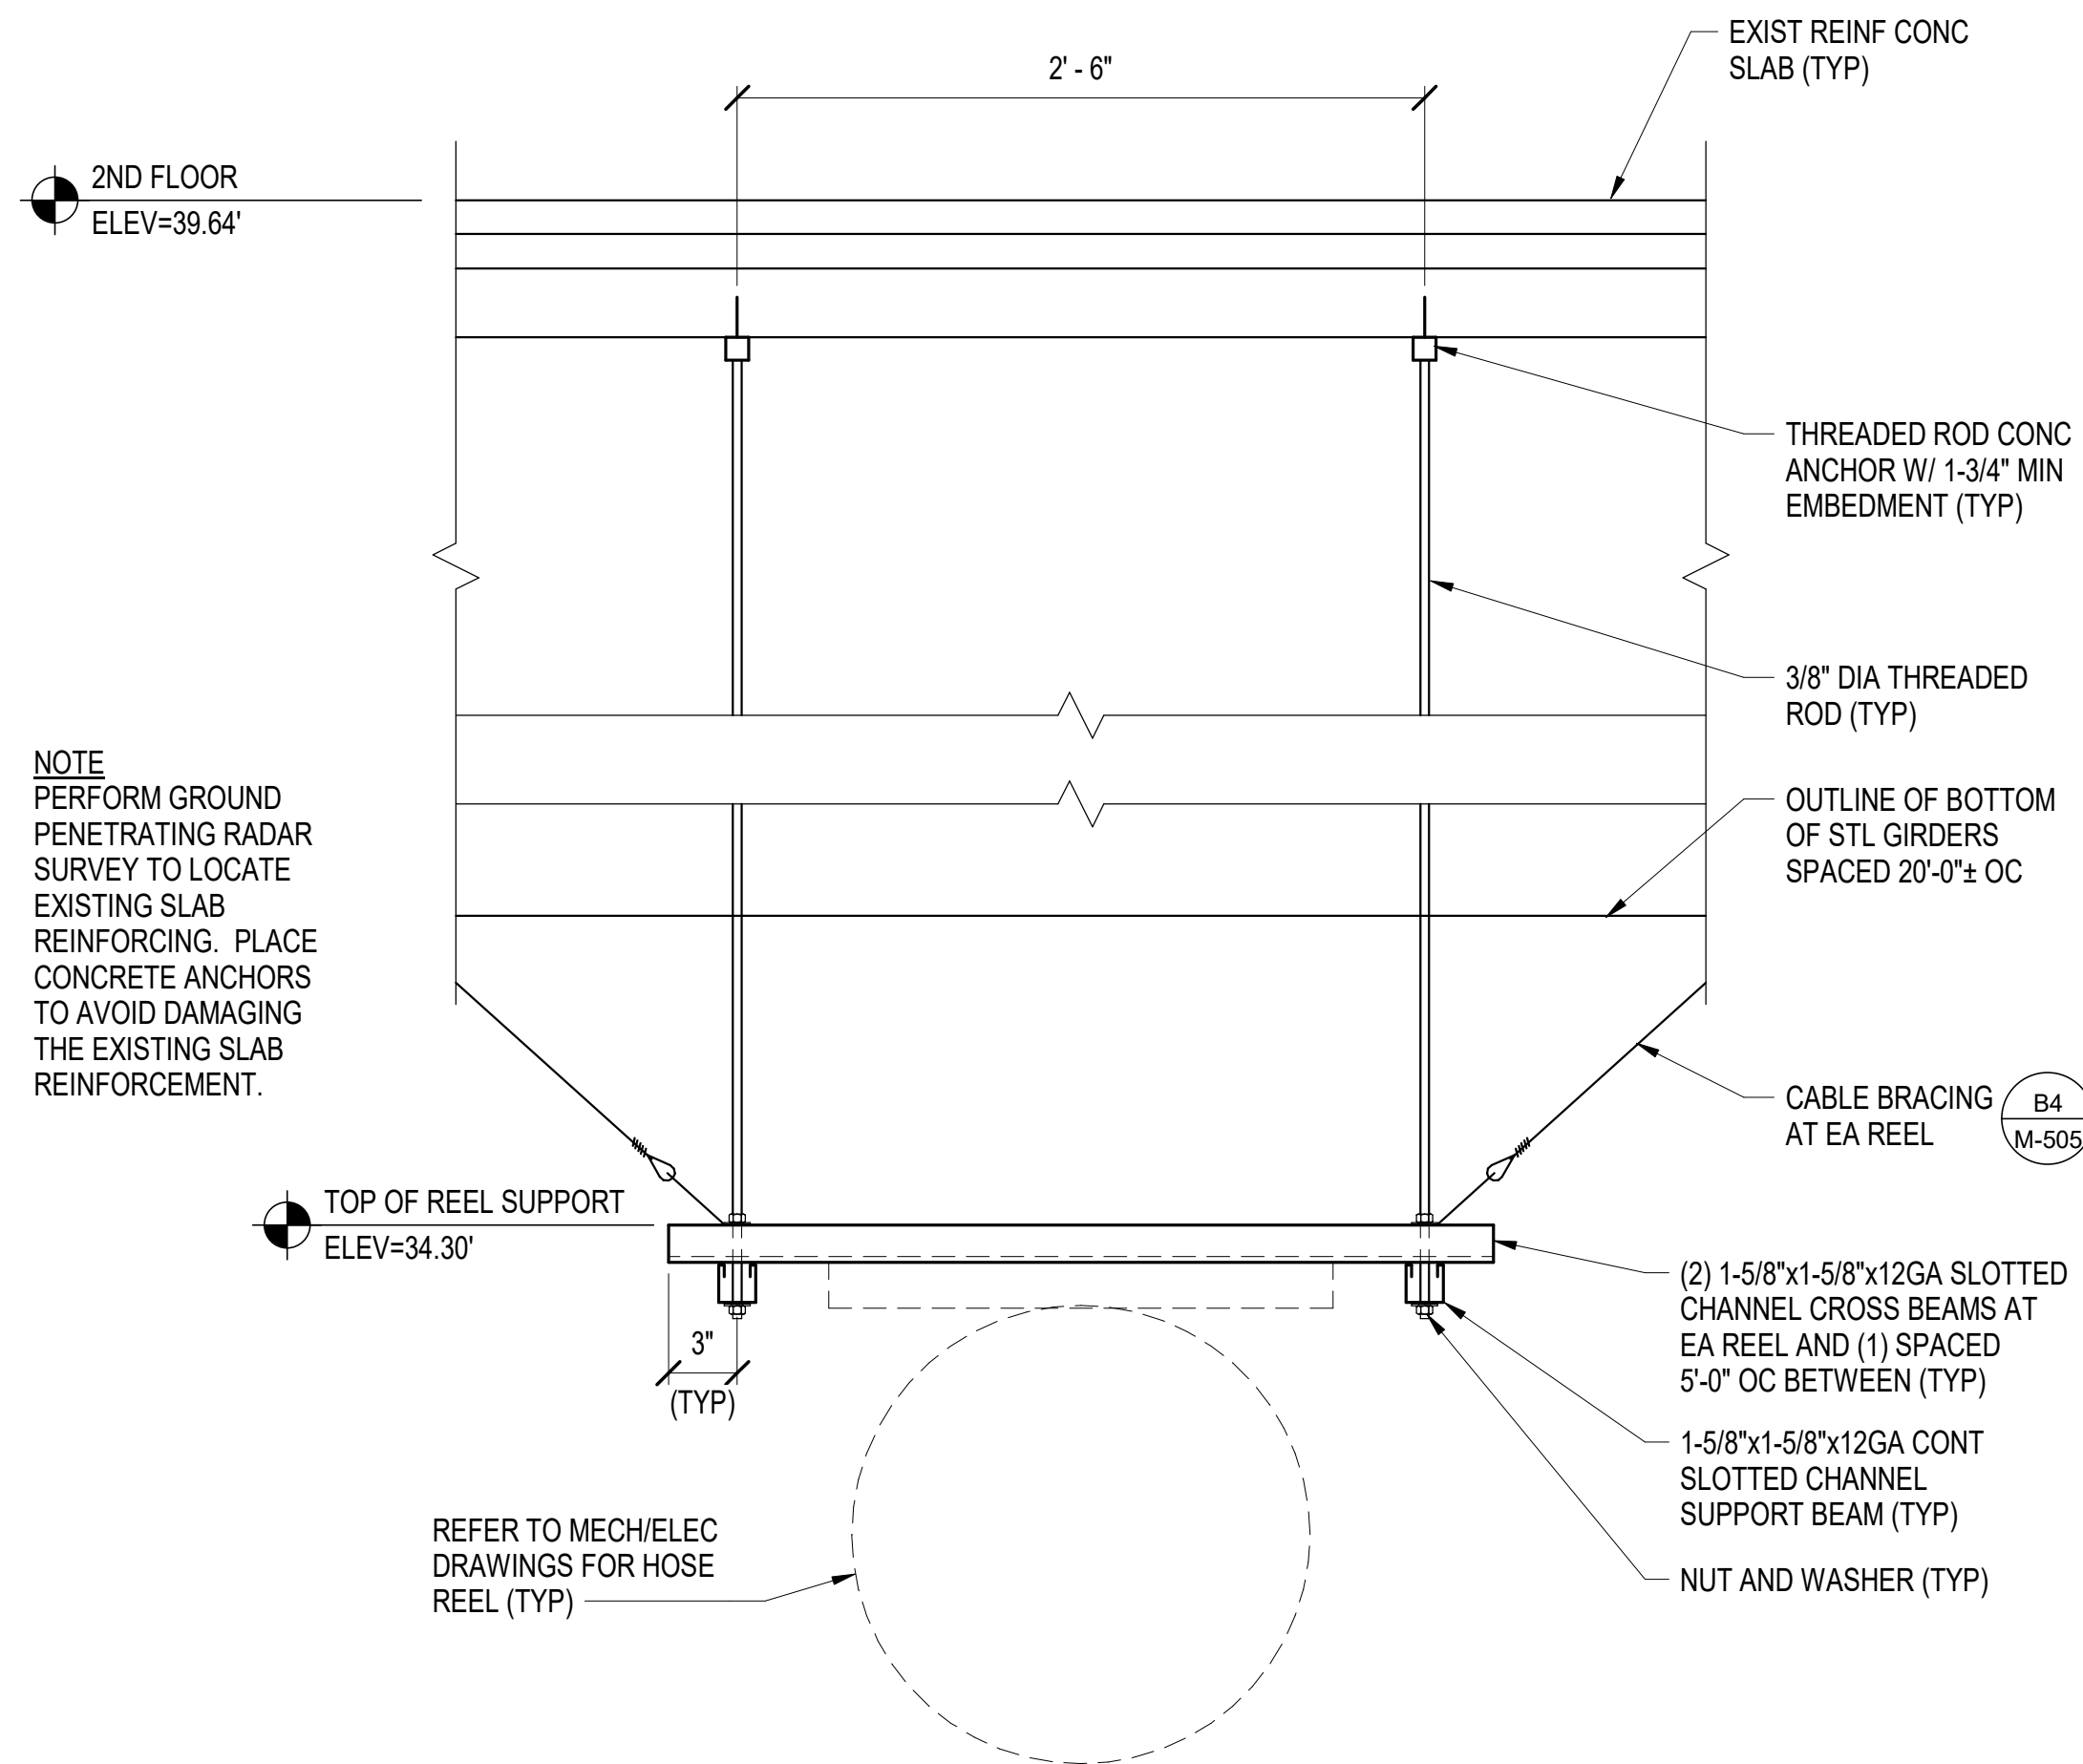


C4 COMPRESSED AIR/ELECTRICAL HOSE REEL SUPPORT DETAIL
SCALE: 1 1/2" = 1'-0" (EP104) (SF103)

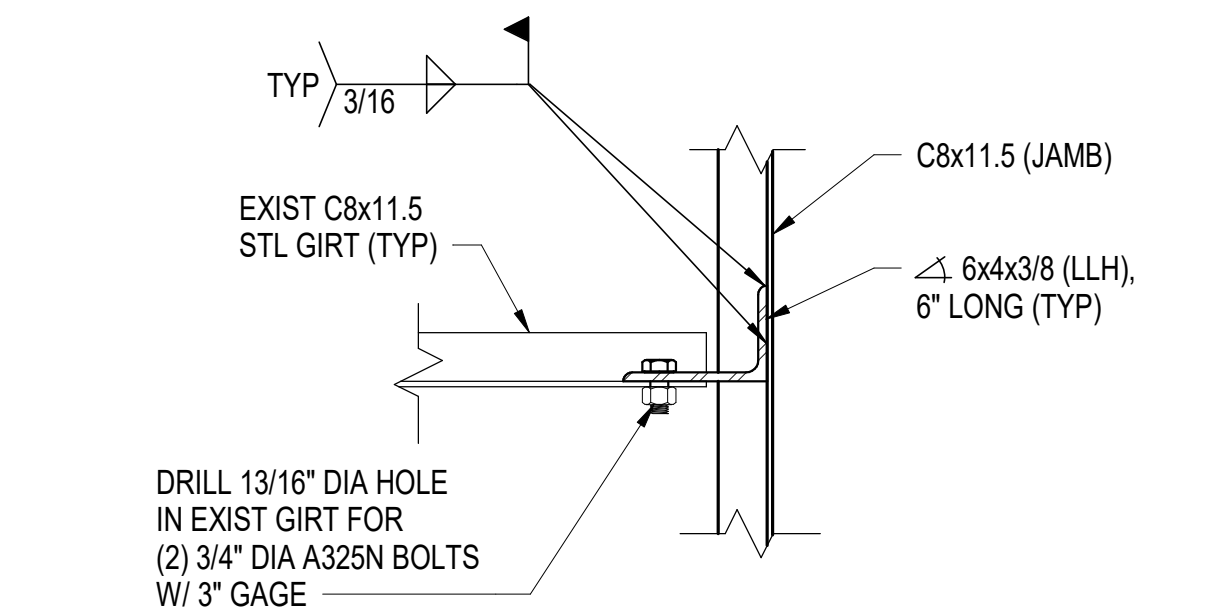


A4 TYP EXIST GIRT TO C8x11.5 DOOR JAMB
SCALE: 1 1/2" = 1'-0" (SF503)

GRAPHIC SCALE(S)

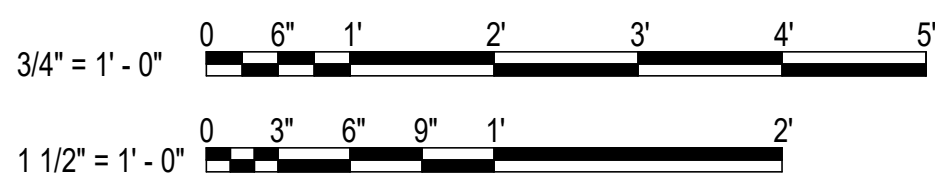

MARK	DESCRIPTION	DATE	APPR
1	AMENDMENT 008 FINAL SUBMISSION	03/10/2026 10/07/2025	RSB RSB

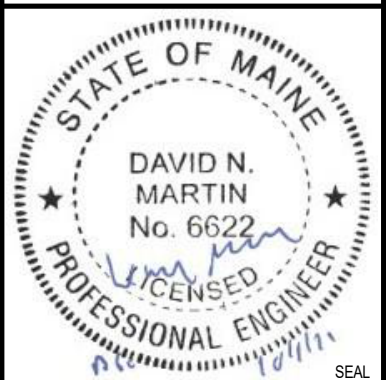

OAK POINT ASSOCIATES

APPROVED
FOR COMMANDER NAVFAC
ACTIVITY
SATISFACTORY TO DATE
DESIGNER WFG
DRAWN BY MJC
CHECKED BY DNM
DESIGN MANAGER T. CARLETON
PROJECT MANAGER L. LYONS
HEADLINE
FIRE PROTECTION S. RUCINSKI

DEPARTMENT OF THE NAVY	NAVAL FACILITIES ENGINEERING SYSTEMS COMMAND	NAVAL FACILITIES ENGINEERING SYSTEMS COMMAND - MID-ATLANTIC	PORTSMOUTH NAVAL SHIPYARD - KITTY, MAINE
ROCC-ME	PORTSMOUTH NAVAL SHIPYARD	B60 REPAIRS	STRUCTURAL DETAILS 6

PROJECT NO.	1740579
NAVFAC DRAWING NO.	
SHEET	72 OF 282
SF506	

DRAWING REVISION: 14 SEP 2023

1

2

3 UNCLASSIFIED

4

5

B UNCLASSIFIED

A