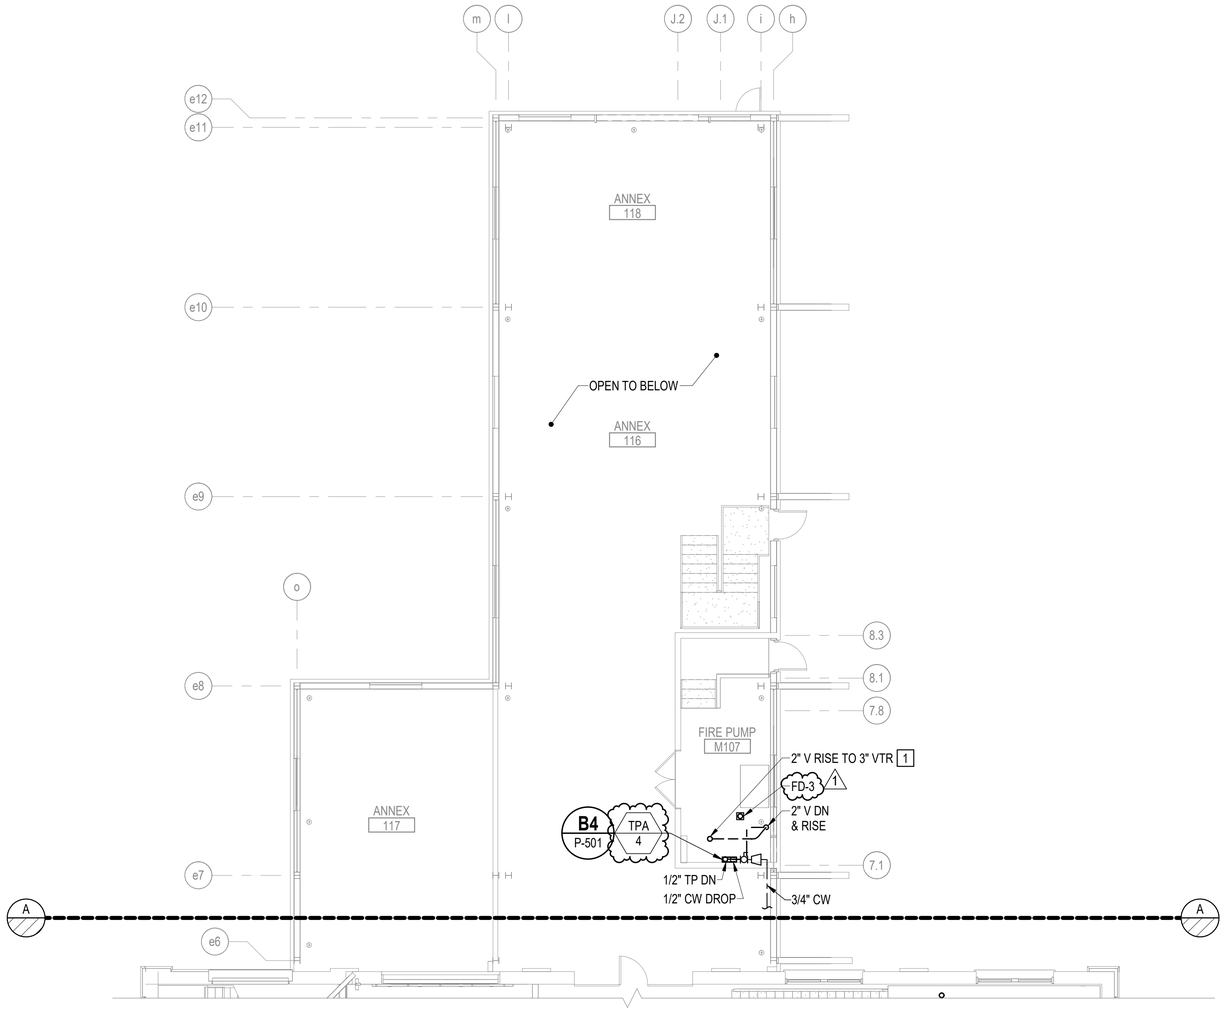


A1 FIRST FLOOR MEZZANINE PLUMBING PLAN - EAST

SCALE: 1/8" = 1'-0"


GENERAL NOTES

1. SEE P-001 FOR PLUMBING LEGENDS, ABBREVIATIONS AND GENERAL NOTES.
2. COORDINATE THE INSTALLATION OF PIPING AND EQUIPMENT TO MAINTAIN MANDATORY CLEARANCE ZONES AROUND CRANE RAILS AND BRIDGE CRANE OPERATIONAL TRAVEL PATH.

KEYNOTES (THIS SHEET ONLY)

1 PROVIDE 2" V UP WITH 3" VTR. VTR MUST BE A MINIMUM OF 10'-0" FROM EDGE OF THE WALL.

KEY PLAN

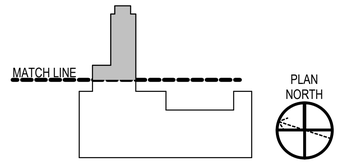

GRAPHIC SCALE

1/8" = 1' - 0" 0 5' 10' 15' 30'

CHECK GRAPHIC SCALE BEFORE USING

MARK	DESCRIPTION	DATE	APPR
1	AMENDMENT 010	03/20/2026	RSH
	FINAL SUBMISSION	10/01/2025	RSH

SEAL

OAK POINT ASSOCIATES

APPROVED	
FOR COMMANDER NAVFAC	
ACTIVITY	
SATISFACTORY TO DATE	
DESIGNER	RNC
DRAWN BY	SRW
CHECKED BY	MSA
DESIGN MANAGER	T. CARLETON
PROJECT MANAGER	L. LYONS
FEAD/PM&E	
FIRE PROTECTION	S. RUCINSKI

DEPARTMENT OF THE NAVY
NAVAL FACILITIES ENGINEERING SYSTEMS COMMAND
ROICC-ME
PORTSMOUTH NAVAL SHIPYARD
NAVAL FACILITIES ENGINEERING SYSTEMS COMMAND - MID-ATLANTIC
PORTSMOUTH NAVAL SHIPYARD - KITTERY, ME
KITTERY, ME
B60 REPAIRS
FIRST FLOOR MEZZANINE PLUMBING PLAN - EAST

EPROJECT NO.: 1740579
NAVFAC DRAWING NO.
SHEET 173 OF 282
P-105

DRAWFORM REVISION: 14 SEP 2023

3/20/2026 1:29:21 PM P-105
C:\Users\sschards\Documents\22103.25_BLDG60_MECHANICAL-V23_swhiteG822D.rvt