


3/20/2026 1:29:25 PM P-108
C:\Users\richards\Documents\22103.25_BLDG60_MECHANICAL-V23_swhitec82ZD.rvt

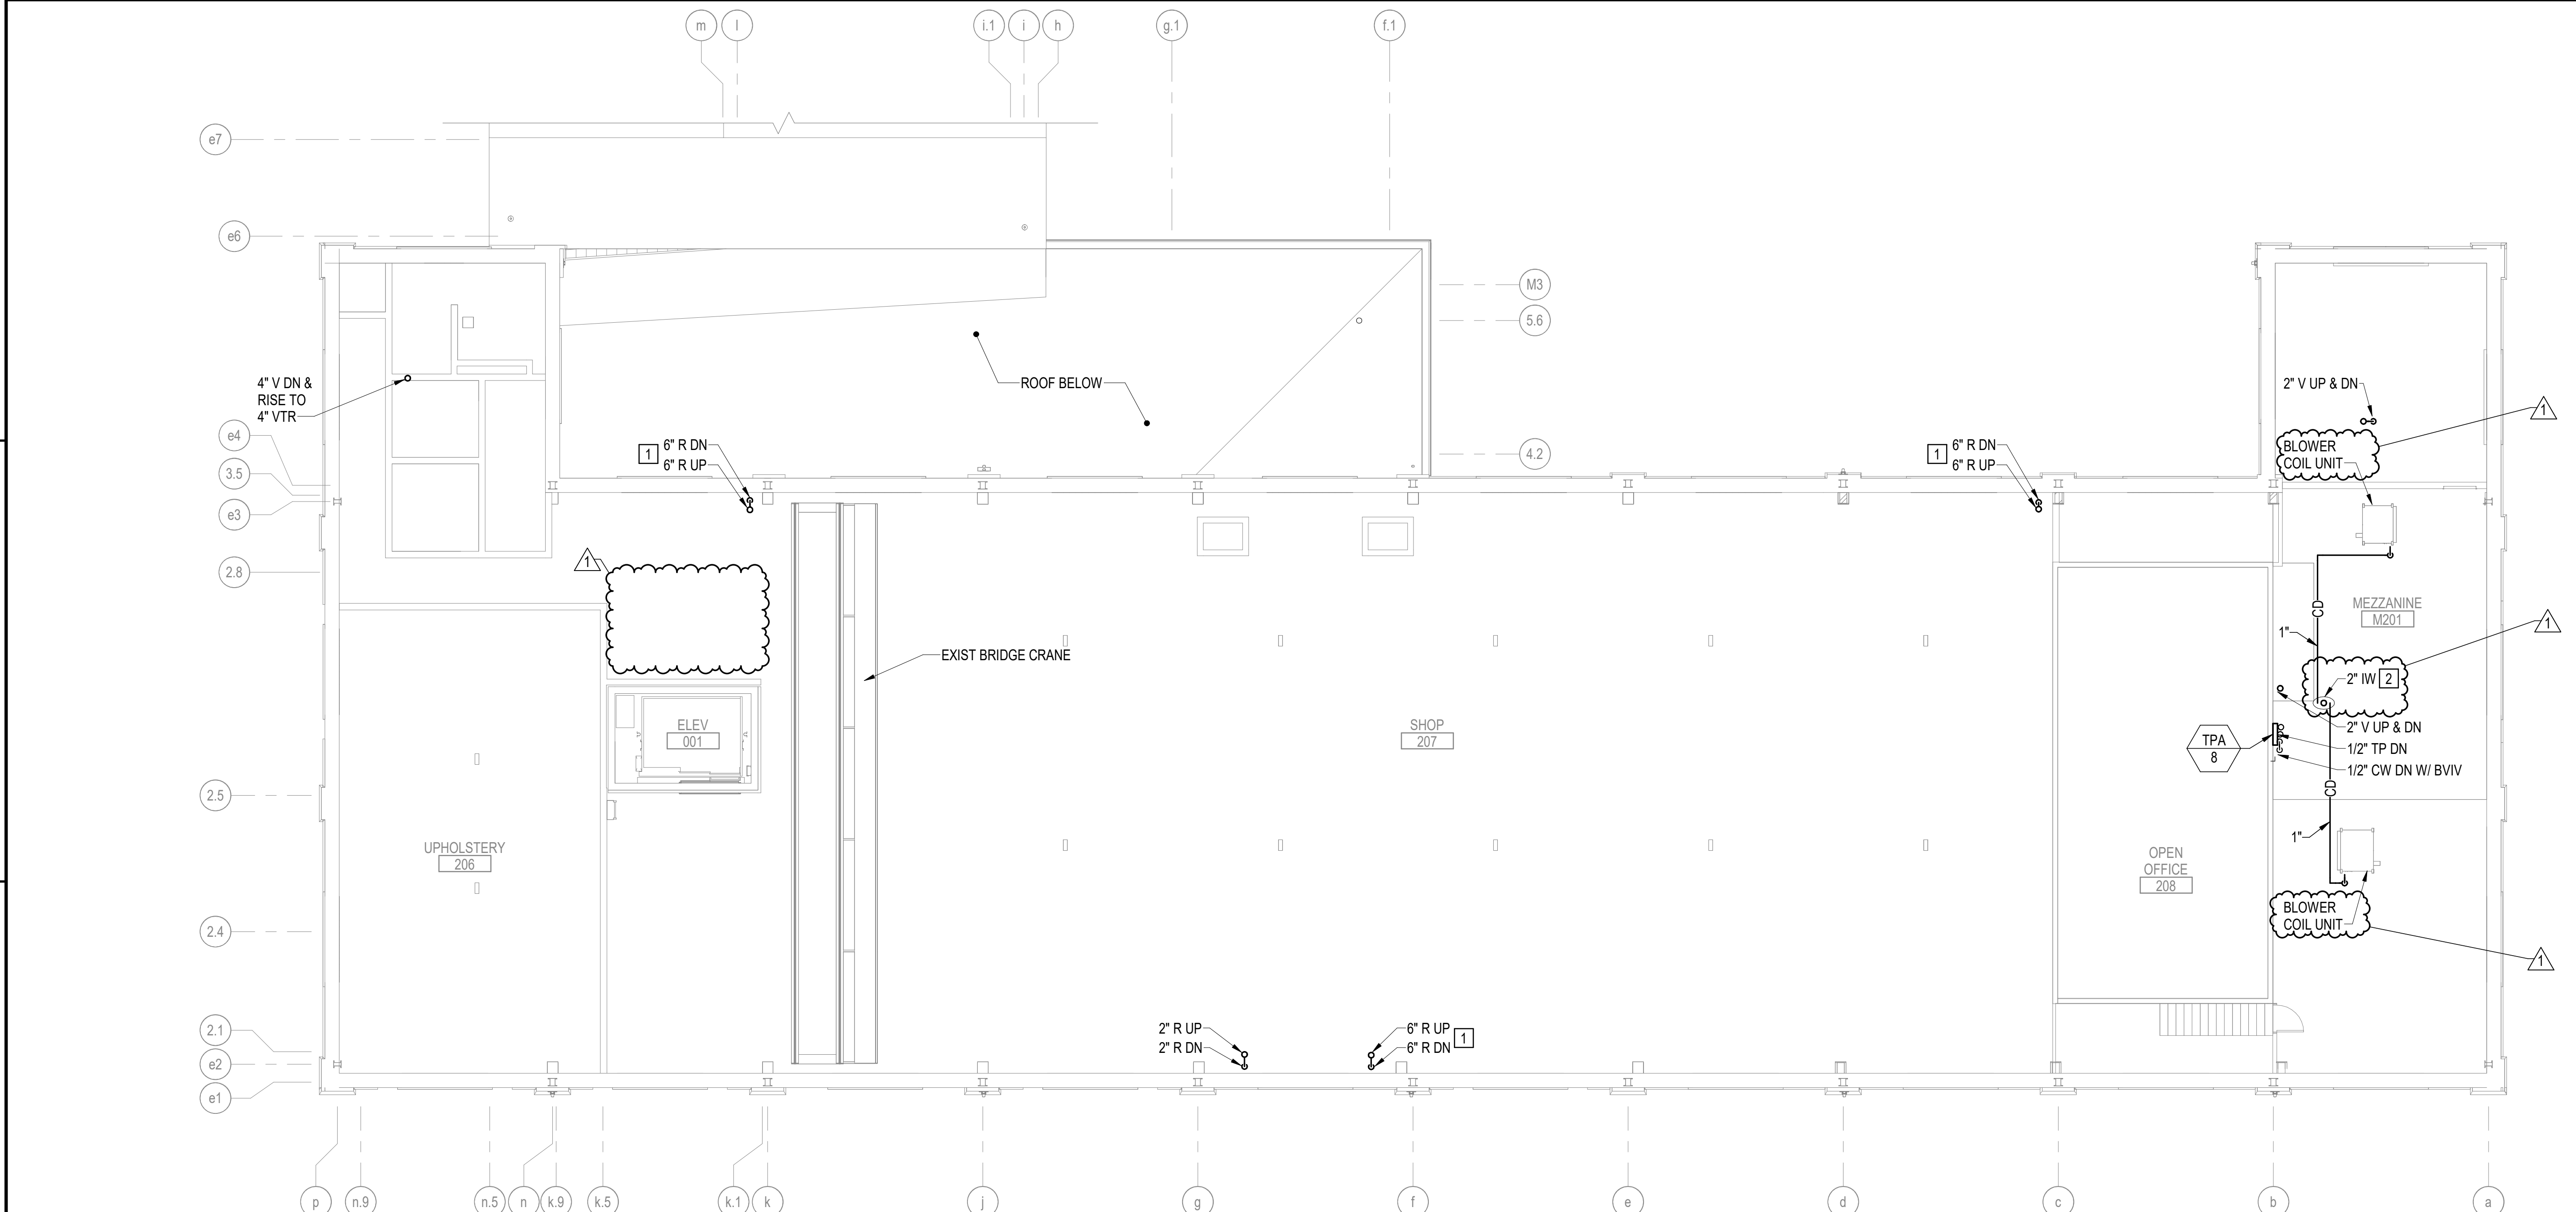

B1 SECOND FLOOR MEZZANINE PLUMBING PLAN - WEST
SCALE: 1/8" = 1'-0"


GENERAL NOTES

- SEE P-001 FOR PLUMBING LEGENDS, ABBREVIATIONS AND GENERAL NOTES.
- COORDINATE THE INSTALLATION OF PIPING AND EQUIPMENT TO MAINTAIN MANDATORY CLEARANCE ZONES AROUND CRANE RAILS AND BRIDGE CRANE OPERATIONAL TRAVEL PATH.


KEYNOTES (THIS SHEET ONLY)

- PROVIDE PIPING RISER OFFSET USING 45 DEGREE ANGLES TO AVOID CONFLICT WITH HEATING WATER PIPING AND CRANE RAIL. SEE SHEET MP106 FOR HYDRONIC HEATING PIPING ARRANGEMENT.
- PIPE 1" CONDENSATE DRAINS FROM BCU-2 AND BCU-3 TO OPEN FUNNEL FITTING ON 2" IW, POSITIONED JUST ABOVE THE EXISTING WOOD PLANKED FLOOR.

KEY PLAN

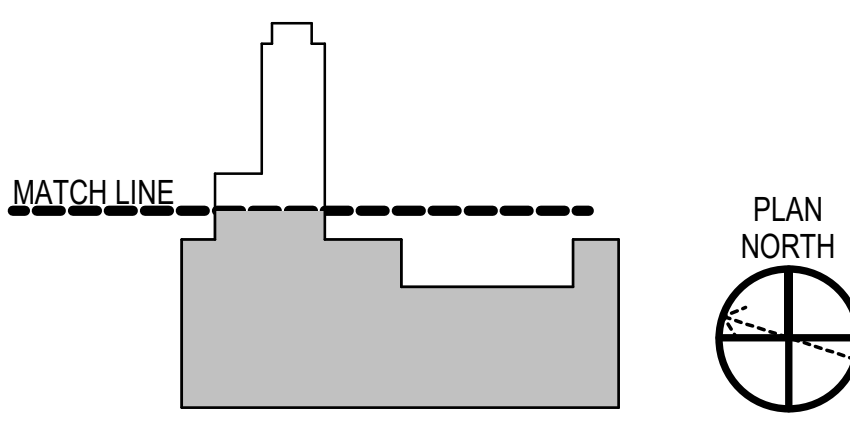

GRAPHIC SCALE

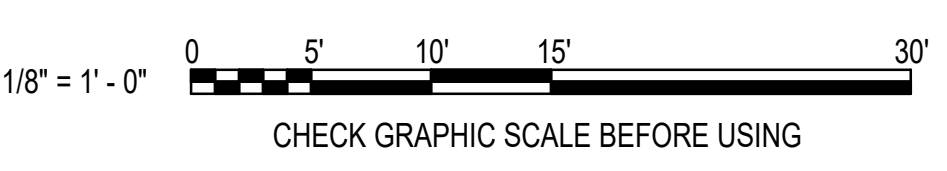

APPROVED		FOR COMMANDER NAVFAC		ACTIVITY		SATISFACTORY TO DATE		DESIGNER RNC		DRAWN BY SRW		CHECKED BY MSA		DESIGN MANAGER T. CARLETON		PROJECT MANAGER L. LYONS		HEADLINE		FIRE PROTECTION S. RUCINSKI		DEPARTMENT OF THE NAVY		NAVAL FACILITIES ENGINEERING SYSTEMS COMMAND		NAVAL FACILITIES ENGINEERING SYSTEMS COMMAND - MID-ATLANTIC		PORTSMOUTH NAVAL SHIPYARD - KITTERY, ME		B60 REPAIRS		SECOND FLOOR MEZZANINE PLUMBING PLAN		P-108		SHEET 176 OF 282		DRAWING REVISION: 14 SEP 2023					
NAVFAC		RICHARD CRESWELL No. 13178 PROFESSIONAL ENGINEER		OAK POINT ASSOCIATES		FOR COMMANDER NAVFAC		ACTIVITY		SATISFACTORY TO DATE		DESIGNER RNC		DRAWN BY SRW		CHECKED BY MSA		DESIGN MANAGER T. CARLETON		PROJECT MANAGER L. LYONS		HEADLINE		FIRE PROTECTION S. RUCINSKI		DEPARTMENT OF THE NAVY		NAVAL FACILITIES ENGINEERING SYSTEMS COMMAND		NAVAL FACILITIES ENGINEERING SYSTEMS COMMAND - MID-ATLANTIC		PORTSMOUTH NAVAL SHIPYARD - KITTERY, ME		B60 REPAIRS		SECOND FLOOR MEZZANINE PLUMBING PLAN		P-108		SHEET 176 OF 282		DRAWING REVISION: 14 SEP 2023	
NAVFAC		RICHARD CRESWELL No. 13178 PROFESSIONAL ENGINEER		OAK POINT ASSOCIATES		FOR COMMANDER NAVFAC		ACTIVITY		SATISFACTORY TO DATE		DESIGNER RNC		DRAWN BY SRW		CHECKED BY MSA		DESIGN MANAGER T. CARLETON		PROJECT MANAGER L. LYONS		HEADLINE		FIRE PROTECTION S. RUCINSKI		DEPARTMENT OF THE NAVY		NAVAL FACILITIES ENGINEERING SYSTEMS COMMAND		NAVAL FACILITIES ENGINEERING SYSTEMS COMMAND - MID-ATLANTIC		PORTSMOUTH NAVAL SHIPYARD - KITTERY, ME		B60 REPAIRS		SECOND FLOOR MEZZANINE PLUMBING PLAN		P-108		SHEET 176 OF 282		DRAWING REVISION: 14 SEP 2023	