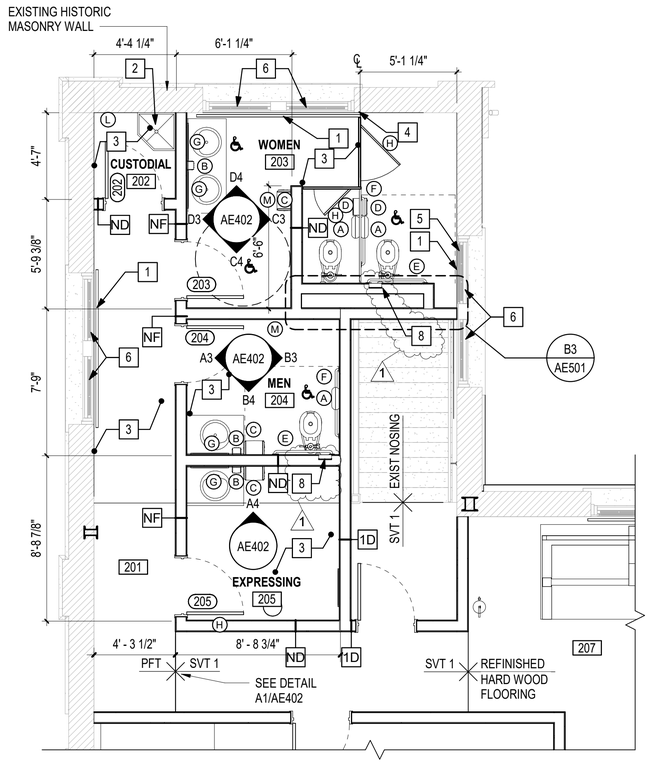

C1 ENLARGED SECOND FLOOR TOILET ROOM PLAN

SCALE: 1/4" = 1'-0" (AE105)

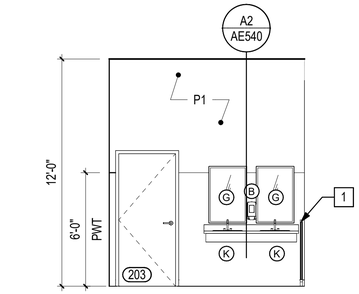

D3 WOMEN 203 NORTH INTERIOR ELEVATION

SCALE: 1/4" = 1'-0" (AE402)

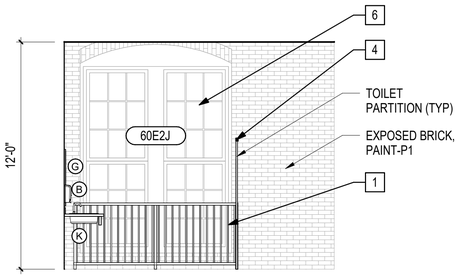

D4 WOMEN 203 EAST INTERIOR ELEVATION

SCALE: 1/4" = 1'-0" (AE402)

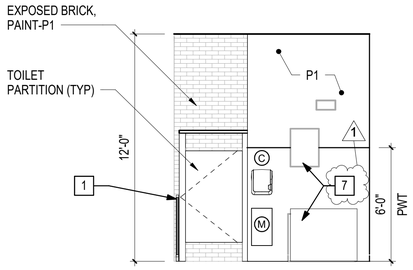

C3 WOMEN 203 SOUTH INTERIOR ELEVATION

SCALE: 1/4" = 1'-0" (AE402)

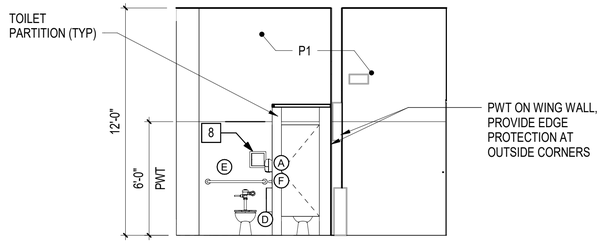

C4 WOMEN 203 WEST INTERIOR ELEVATION

SCALE: 1/4" = 1'-0" (AE402)

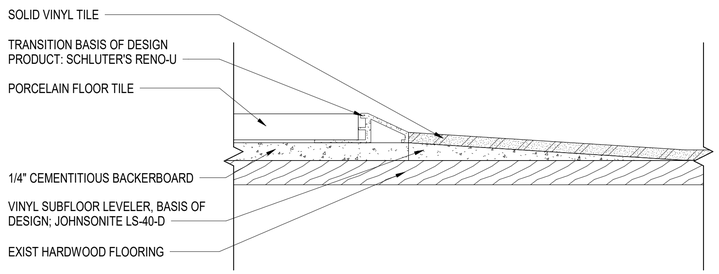

A1 FLOORING TRANSITION SOLID VINYL TO PORCELAIN TILE

SCALE: 1 1/2" = 1'-0"

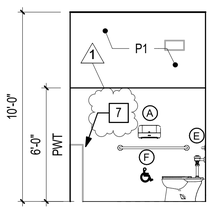

A3 MEN 204 NORTH INTERIOR ELEVATION

SCALE: 1/4" = 1'-0" (AE402)

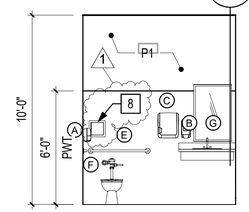

A4 EXPRESSING ROOM 205 ELEVATION

SCALE: 1/4" = 1'-0" (AE402)

B3 MEN 204 SOUTH INTERIOR ELEVATION

SCALE: 1/4" = 1'-0" (AE402)

B4 MEN 204 WEST INTERIOR ELEVATION

SCALE: 1/4" = 1'-0" (AE402)

GENERAL NOTES

1. SEE AE002 FOR WALL TYPES.
2. SEE SHEET AE401 FOR TOILET ACCESSORY SCHEDULE AND AE002 FOR STANDARD MOUNTING HEIGHTS.
3. SEE SHEET AE601 FOR DOOR SCHEDULE.
4. SEE SHEET AE641 FOR ROOM FINISH SCHEDULE.
5. PROVIDE SOLID BLOCKING BEHIND SURFACE APPLIED TOILET ACCESSORIES WHEN MOUNTED ON STUD WALLS.

KEYNOTES

1. WINDOW GUARDRAIL SYSTEM SIMILAR , SEE DETAIL A4/AE626.
2. MOP SINK, SEE PLUMBING SHEETS.
3. PROVIDE 1/4" CEMENTITIOUS BACKER BOARD UNDER PORCELAIN FLOOR TILE.
4. COORDINATE TOILET PARTITION MOUNTING HARDWARE WITH HISTORIC MASONRY. FASTEN INTO MORTAR JOINTS.
5. REPAIR AND REINSTALL SALVAGED INTERIOR ALUMINUM STORM WINDOW.
6. REPAIR WOOD WINDOW/DOOR, SEE RESTORATION SCHEDULE ON SHEET AE622.
7. MECHANICAL EQUIPMENT, SEE MECHANICAL SHEETS
8. ACCESS PANEL 8" x 8", COORDINATE WITH PLUMBING SHEETS.

KEY PLAN

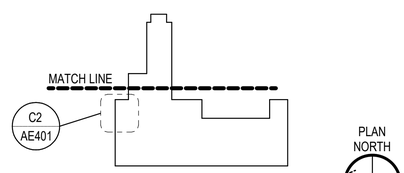

GRAPHIC SCALE(S)

1/4" = 1' - 0" 0 1' 5' 10' 15'

MARK	DESCRIPTION	DATE	APPR
1	AMENDMENT 010	03/20/2026	RSH
	FINAL SUBMISSION	10/01/2025	RSH

NAVFAC

SEAL

OAK POINT ASSOCIATES

APPROVED	
FOR COMMANDER NAVFAC	
ACTIVITY	
SATISFACTORY TO DATE	
DESIGNER	JMR
DRAWN BY	MJD
CHECKED BY	RSH
DESIGN MANAGER	T. CARLETON
PROJECT MANAGER	L. LYONS
FEAD/PM&E	
FIRE PROTECTION	S. RUCINSKI

DEPARTMENT OF THE NAVY
NAVAL FACILITIES ENGINEERING SYSTEMS COMMAND
ROICC-ME
PORTSMOUTH NAVAL SHIPYARD

NAVAL FACILITIES ENGINEERING SYSTEMS COMMAND - MID-ATLANTIC
PORTSMOUTH NAVAL SHIPYARD - KITTERY, ME

KITTERY, ME

B60 REPAIRS

ENLARGED SECOND FLOOR TOILET ROOM PLANS AND ELEVATIONS

EPROJECT NO.: 1740579

NAVFAC DRAWING NO.

SHEET 115 OF 282

AE402

DRAWFORM REVISION: 14 SEP 2023

3/20/2026 11:40:13 AM AE402
C:\Users\mdonovan\Documents\22103.25_BLDG60_ARCHITECTURAL-V23_mdonovan8VFXR.rvt