




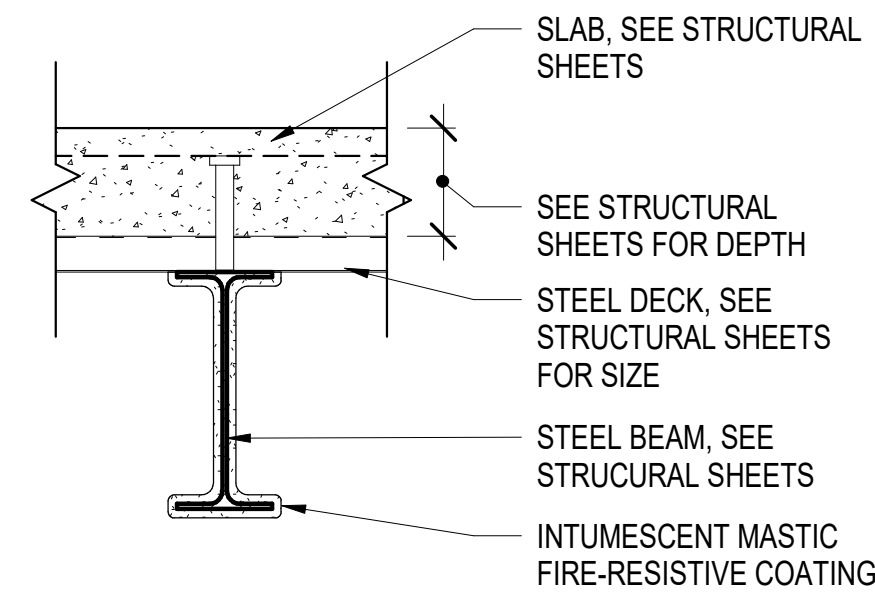


**D1 1 HOUR RATED FLOOR ASSEMBLY UL D925**  
SCALE: 1 1/2" = 1'-0"

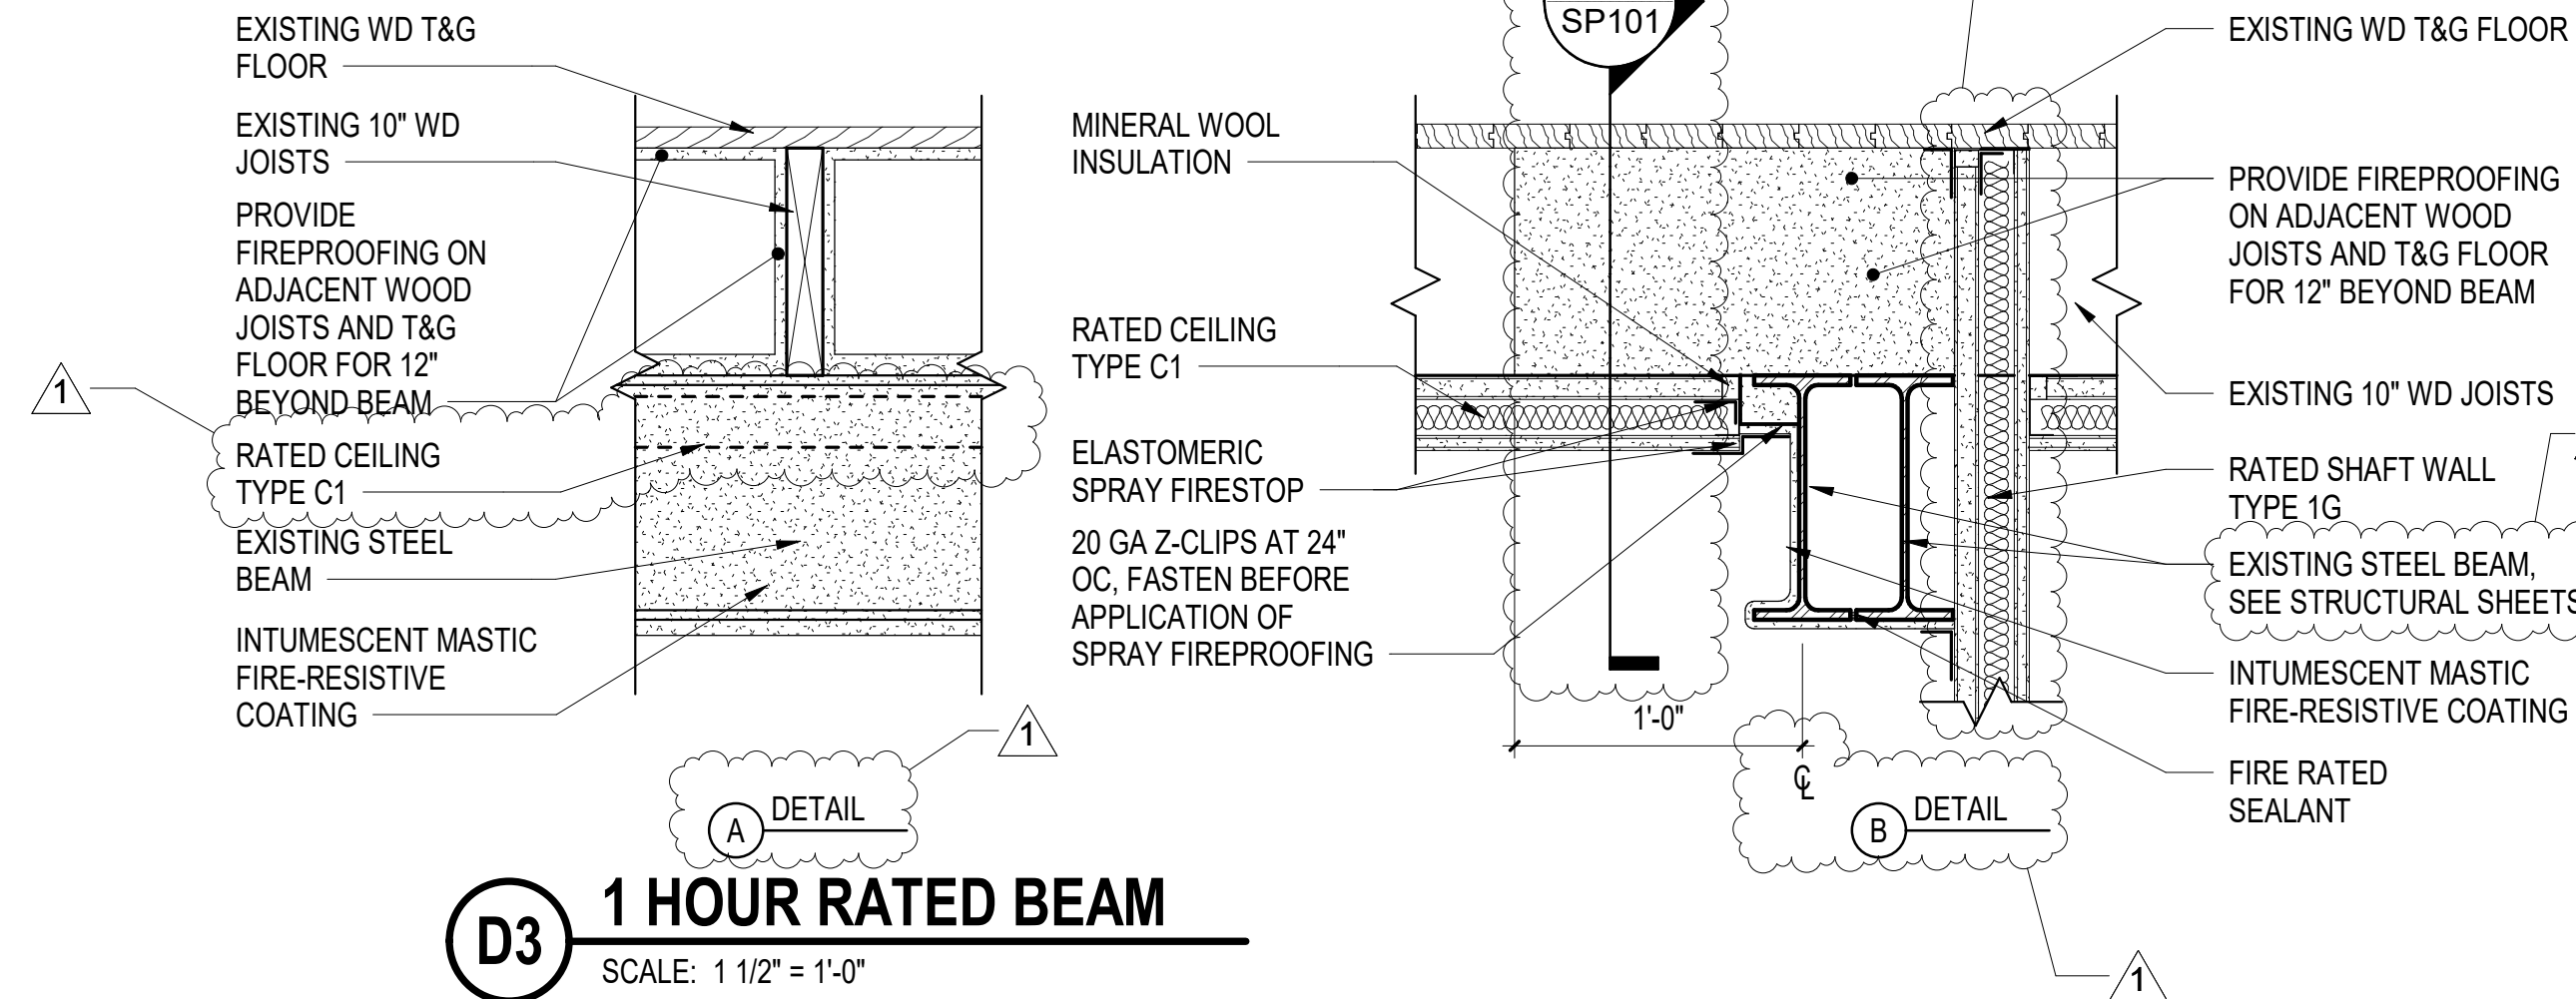


**D3** **1 HOUR RATED BEAM**  
SCALE: 1 1/2" = 1'-0"

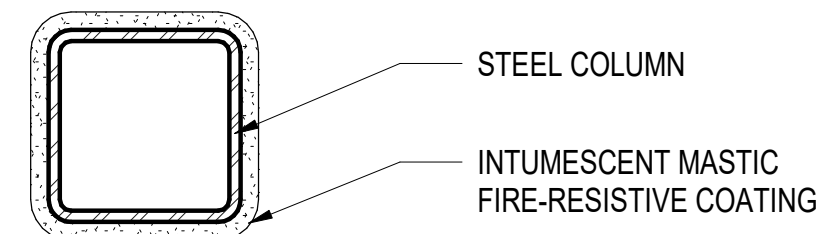

**C3 1 HOUR RATED HSS COLUMNS UL X771**  
SCALE: 3" = 1'-0"

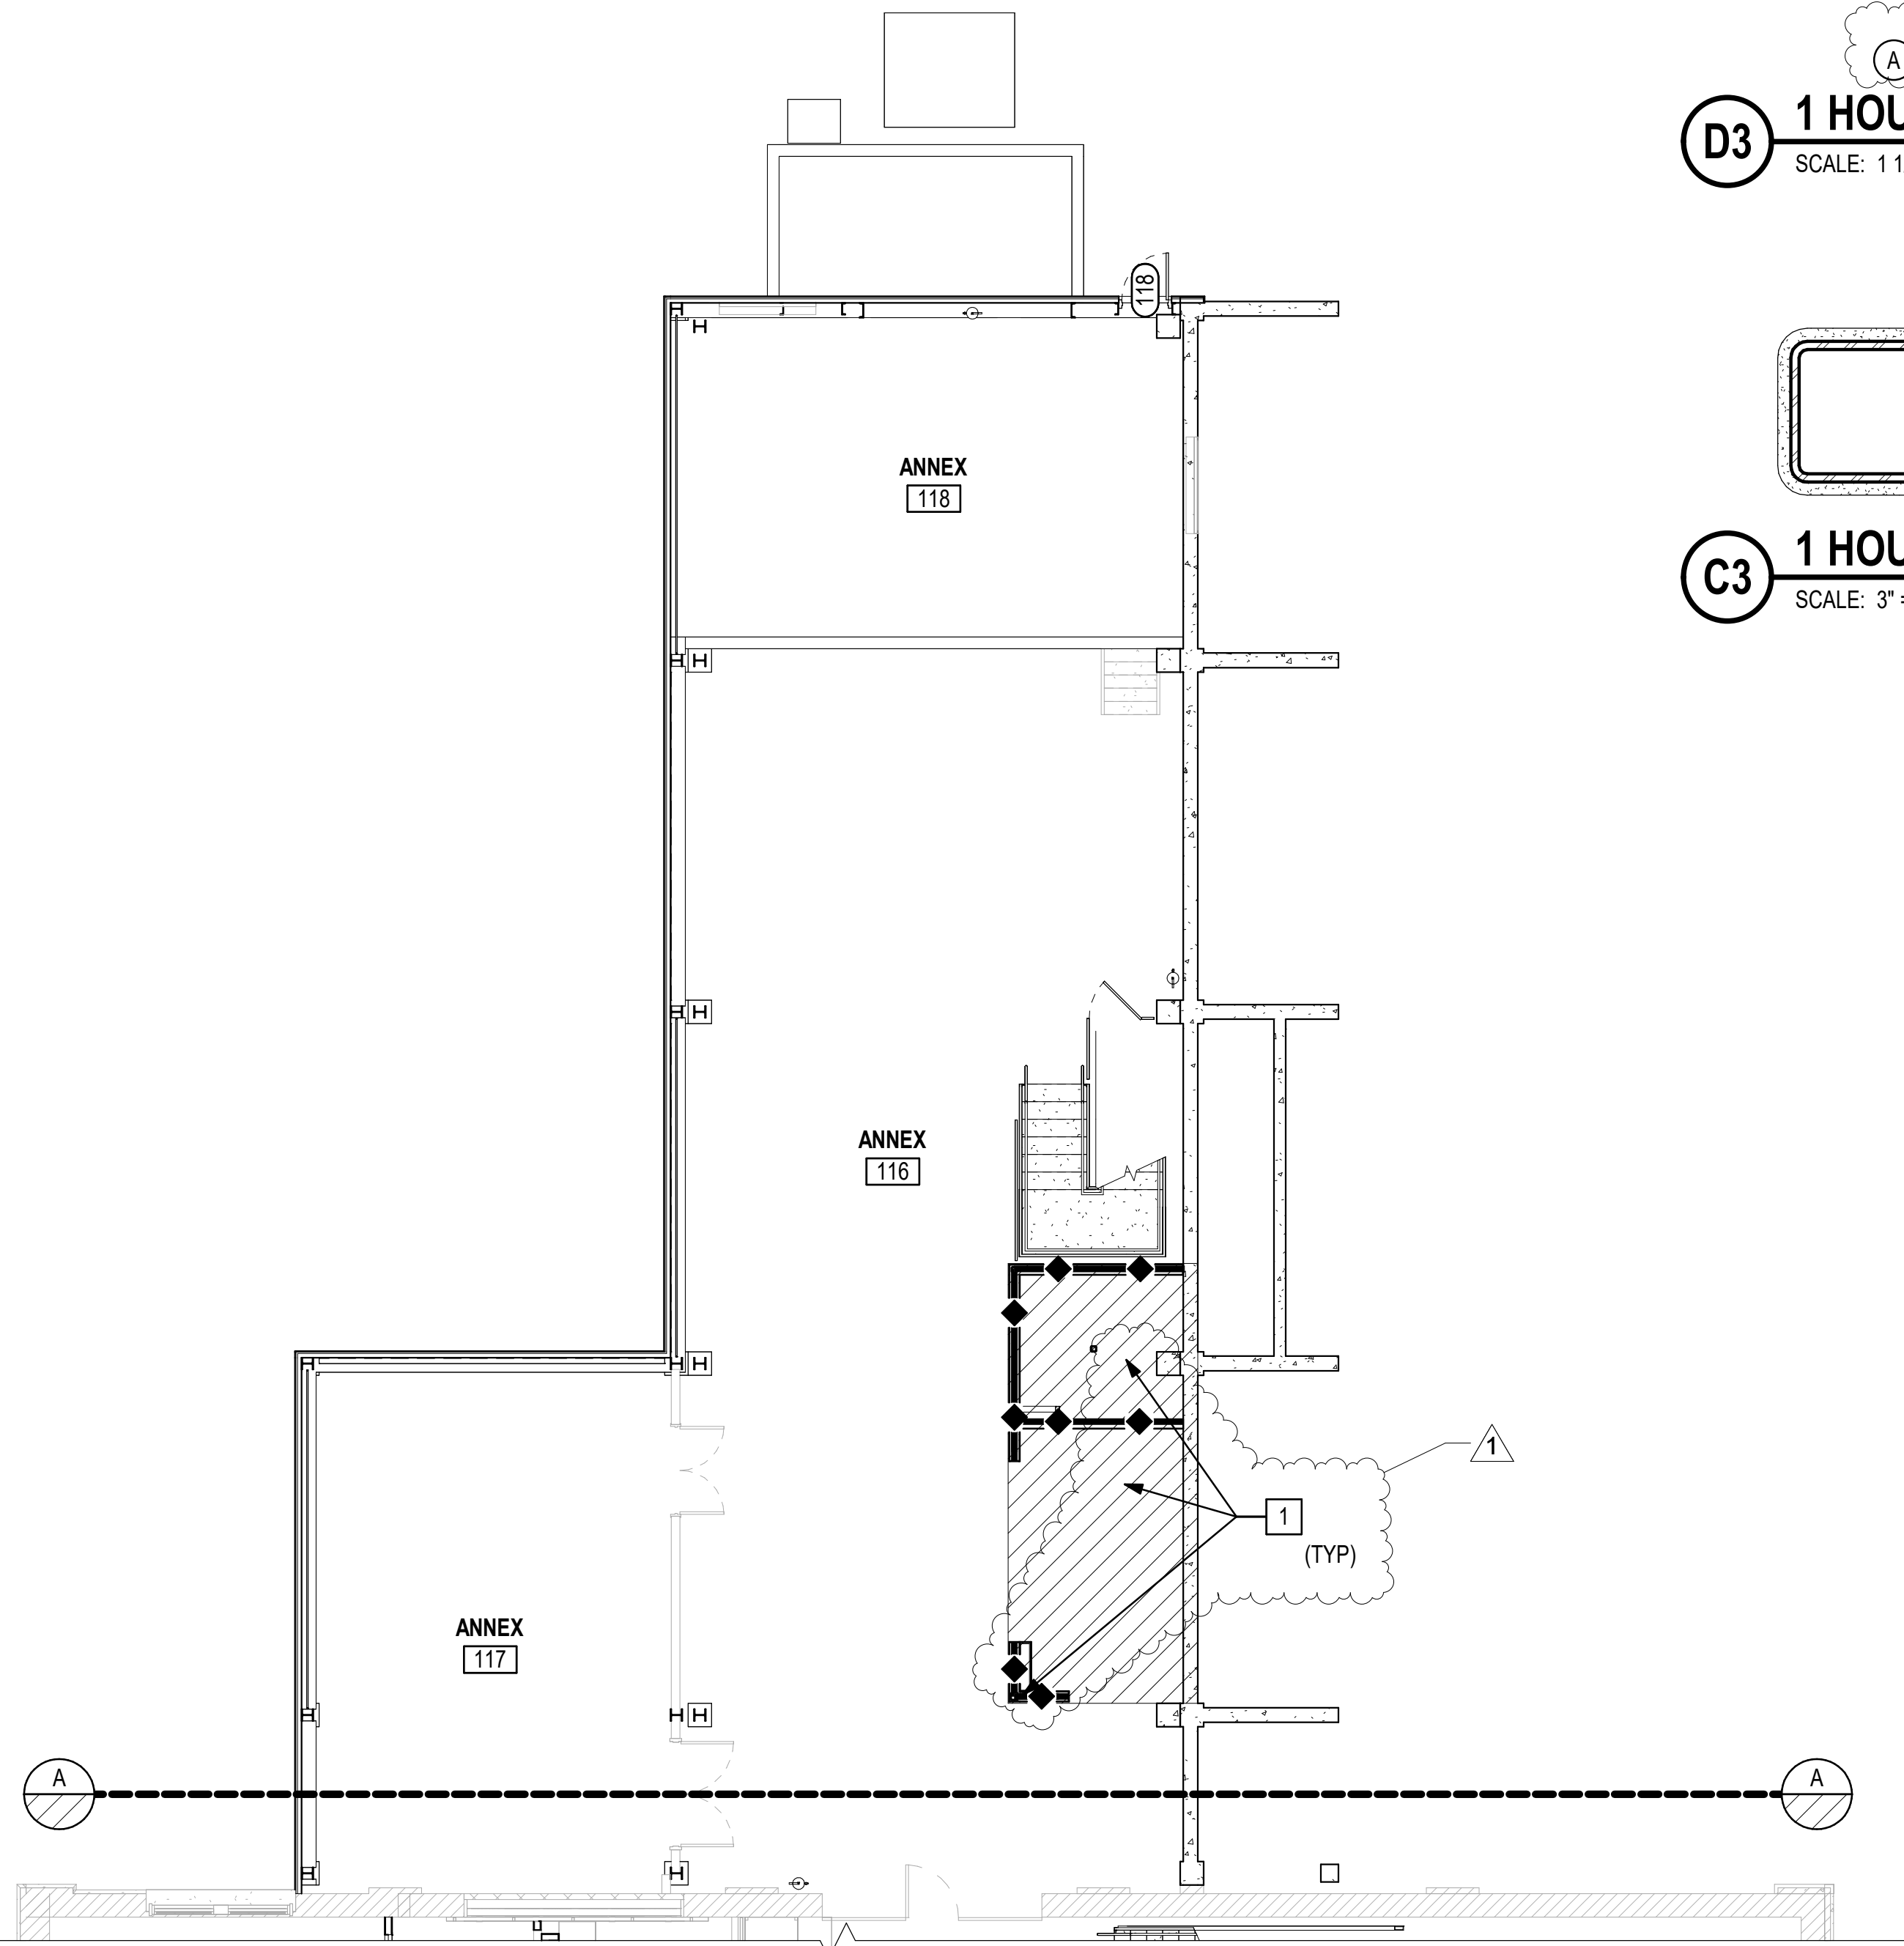

**A1 FIRE PUMP FIREPROOFING PLAN**  
SCALE: 1/8" = 1'-0"

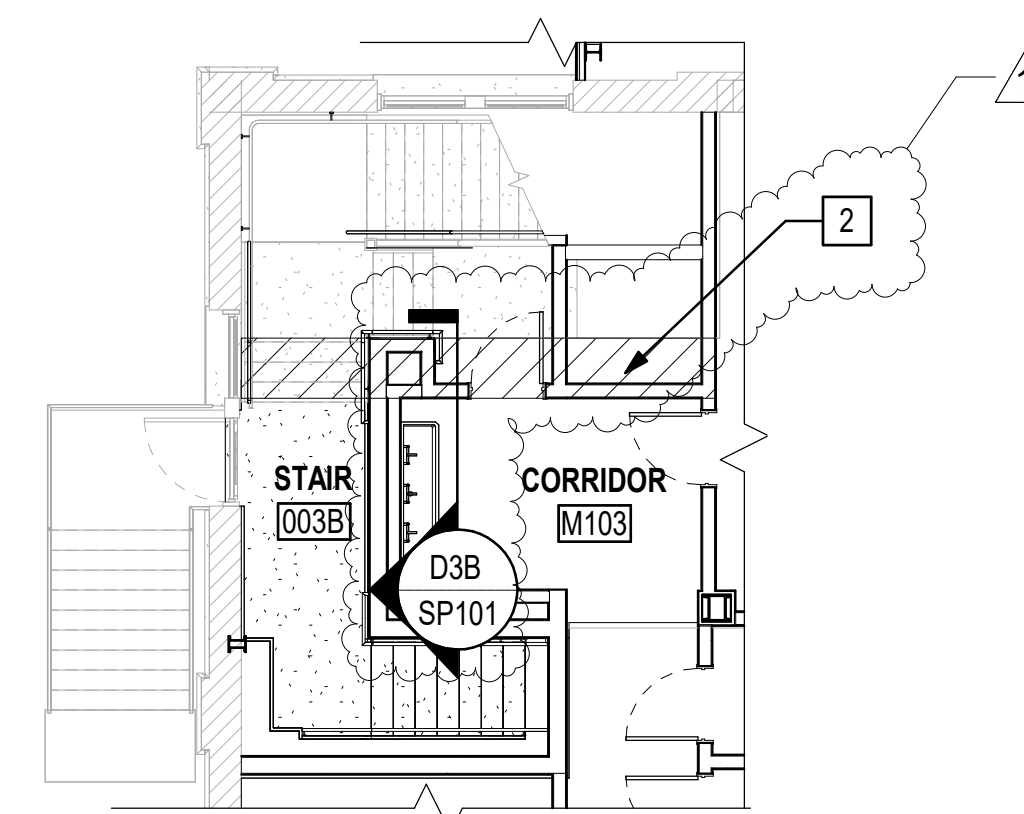

**A3** **NORTHEAST STAIR FIREPROOFING PLAN**  
SCALE: 1/8" = 1'-0" (90.1 Appendix G 105)

## GENERAL NOTES

1. PROVIDE FIREPROOFING TO MAINTAIN INTERNATIONAL BUILDING CODE (IBC), TYPE IIIB CONSTRUCTION.
2. STRUCTURAL COMPONENTS ARE AS DEFINED BY THE 2021 IBC.
3. MEMBERS ARE CONSIDERED UNRESTRAINED FOR PURPOSES OF DETERMINING FIRE RESISTANT MATERIAL THICKNESS. THICKNESS OF FIREPROOFING WILL BE BASED ON MANUFACTURER'S RECOMMENDATIONS TO ACHIEVE THE REQUIRE RATING.
4. SEE SHEET AE001 FOR WALL AND CEILING TYPES.
5. SEE SHEET AE002 FOR FIRESTOPPING OF JOINTS AND PENETRATIONS.
6. PIPES, WIRES, CONDUITS, DUCTS, OR OTHER UTILITIES MUST NO BE EMBEDDED IN THE REQUIRED FIREPROOFING DEPTH.
7. FRAMING SHOWN ON THE SP SHEETS IS FOR REFERENCE ONLY AND TO ESTABLISH GENERAL FIRE RESISTANCE RATING INTENT. REFER TO THE STRUCTURAL FRAMING PLANS FOR THE FRAMING LAYOUT AND FOR MEMBER SIZING.
8. WHEN A RATING IS INDICATED FOR A STRUCTURAL MEMBER, THIS RATING MUST EXTEND FOR THE FULL LENGTH/HEIGHT OF THE MEMBER AND MUST INCLUDE PROTECTION OF ITS CONNECTIONS TO OTHER STRUCTURAL MEMBERS.
9. WHEN A RATING IS INDICATED FOR A STRUCTURAL MEMBER, NON-RATED MEMBERS CONNECTING TO THE RATED MEMBERS MUST BE PROTECTED AS REQUIRED FOR THE RATED MEMBER FOR 12 INCHES BEYOND THE RATED MEMBER UNLESS NOTED OTHERWISE.
10. REFER TO UL LISTINGS FOR THE FULL DESIGN CRITERIA.
11. DO NOT CONCEAL FIREPROOFING PRIOR TO INSPECTION AND ACCEPTANCE BY CONTRACTING OFFICER.


## KEYNOTES

- 1 FIREPROOFING AT BEAMS, BRACING, AND COLUMNS SUPPORTING DECK ABOVE. SEE FRAMING PLANS FOR LAYOUT AND REFER TO DETAILS C3 AND D1/SP101.
- 2 FIREPROOFING AT BEAMS AT UNDERSIDE OF SECOND FLOOR DECK. REFER TO DETAIL D3/SP101.

## LEGEND


- |                                                                                       |   |
|---------------------------------------------------------------------------------------|---|
|  | 1 HOUR INTUMESCENT MASTIC FIRE-RESISTIVE COATING ON COLUMNS AND REMAINING STRUCTURAL MEMBERS SUPPORTING THE FLOOR DECK ABOVE (SUCH AS BEAMS). |
|  | 1-HOUR FIRE RESISTANCE RATED WALL (SEE LIFE SAFETY SHEETS)                                                                                    |

## KEY PLAN

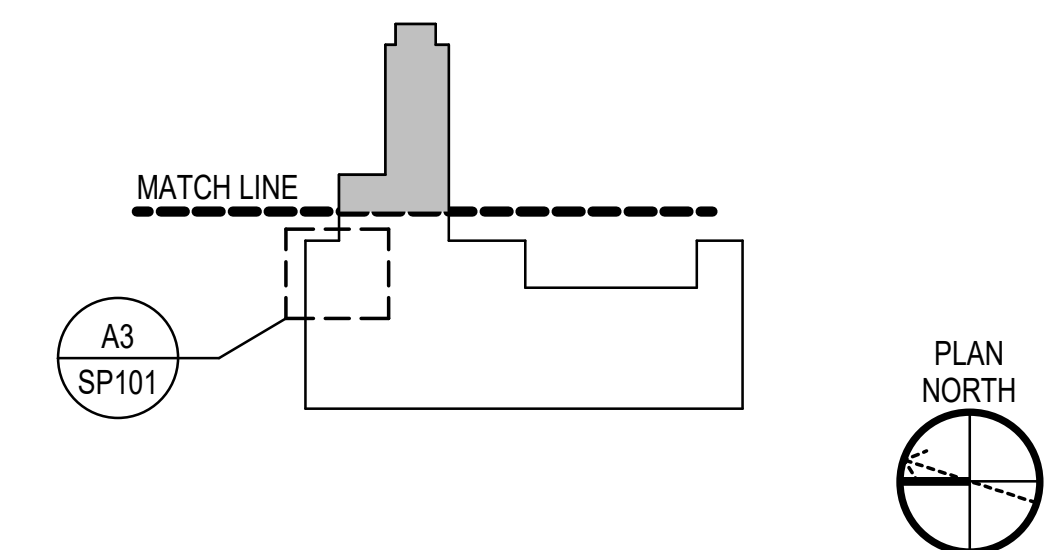

**GRAPHIC SCALE(S)**

- 
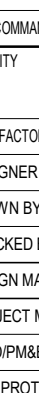
|   |  |                                                            |
|---|--|------------------------------------------------------------|
|   |  | RSH<br>03/21/2026<br>RSH<br>10/12/2025<br>DATE<br>APPR<br> |
|   |  | AMENDMENT 010<br>FINAL SUBMISSION<br>DESCRIPTION<br>       |
|   |  | MARK<br>                                                   |
| SEAL<br>   |  |                                                            |
| OAK POINT ASSOCIATES<br>   |  |                                                            |
| FOR COMMANDER NAVFAC<br>   |  |                                                            |
| ACTIVITY<br>   |  |                                                            |
| SATISFACTORY TO DATE<br>   |  |                                                            |
| DESIGNER JMR<br>   |  |                                                            |
| DRAWN BY CJE<br>   |  |                                                            |
| CHECKED BY RSH<br>   |  |                                                            |
| DESIGN MANAGER T. CARLETON<br>   |  |                                                            |
| PROJECT MANAGER L. LYONS<br>   |  |                                                            |
| FEEDBACK<br>   |  |                                                            |
| FIRE PROTECTION S. RUCINSKI<br>   |  |                                                            |
| DEPARTMENT OF THE NAVY<br>NAVAL FACILITIES ENGINEERING SYSTEMS COMMAND<br>NAVAL FACILITIES ENGINEERING SYSTEMS COMMAND - MID-ATLANTIC<br>ROICC-ME<br>PORTSMOUTH NAVAL SHIPYARD - KITTERY, ME<br>KITTERY, ME<br> |  |                                                            |
| PORTSMOUTH NAVAL SHIPYARD<br>   |  |                                                            |
| B60 REPAIRS<br>   |  |                                                            |
| STRUCTURAL PROTECTION PART PLAN AND DETAILS<br>   |  |                                                            |
| EPROJECT NO.: 1740579<br>   |  |                                                            |
| NAVFAC DRAWING NO.<br>   |  |                                                            |
| SHEET 74 OF 282<br>   |  |                                                            |
| SP101<br>   |  |                                                            |