

3/16/2026 8:55:26 AM AE411
C:\Users\indonovan\Documents\22103.25_BLDG00_ARCHITECTURAL-V23_mdonovan\VPXR.rvt

3 UNCLASSIFIED

4

5


GENERAL NOTES

1. SEE SHEET AE001 FOR ALL WALL/CEILING TYPES.
2. SEE SHEET AE601 FOR DOOR SCHEDULE.
3. SEE SHEET AE640 FOR ROOM FINISH SCHEDULE.

KEYNOTES

- 1 ELEVATOR PIT LADDER WITH NON-SLIP RUNGS. SEE STRUCTURAL SHEETS.
- 2 PAINT ELEVATOR PIT WALLS.
- 3 UFC REQUIRED CLEAR ENTRAPMENT AREA. (1'-8" X 3'-0" MIN)
- 4 HOIST BEAM, SEE STRUCTURAL SHEETS.
- 5 STEEL COLUMN, SEE STRUCTURAL SHEETS.
- 6 MINIMUM CLEAR WIDTH AND HEIGHT DOOR OPENING. COORDINATE ROUGH OPENING WITH ELEVATOR MANUFACTURER.
- 7 EXTEND METAL STUD WALL TO UNDERSIDE OF BEADBOARD CEILING.
- 8 9'-0" (WIDE) X 6'-5" (DEEP) CLEAR INSIDE PASSENGER ELEVATOR CAB.
- 9 1-HR RATED CEILING SYSTEM C-1. PAINT.
- 10 PLUMBING FIXTURE, SEE PLUMBING SHEETS. PROVIDE BLOCKING IN STUD WALL AT WALL MOUNTED FIXTURE LOCATIONS.
- 11 METAL LADDER, SEE DETAIL A2/AE443.
- 12 LIGHT FIXTURE (TYP). SEE ELECTRICAL DRAWINGS.
- 13 REINSTALL SALVAGE WOOD STRIP FLOORING AT STL DECK FLOOR SYSTEM, SEE STRUCT SHEETS.

GRAPHIC SCALE(S)

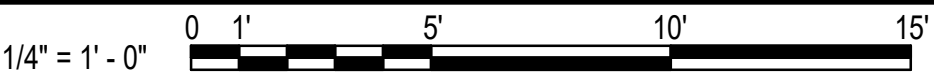

FOR COMMANDER NAVFAC
ACTIVITY
SATISFACTORY TO DATE
DESIGNER JMR
DRAWN BY MJD
CHECKED BY RSH
DESIGN MANAGER T. CARLETON
PROJECT MANAGER L. LYONS
HEADLINE
FIRE PROTECTION S. RUCINSKI


DEPARTMENT OF THE NAVY
NAVAL FACILITIES ENGINEERING SYSTEMS COMMAND
NAVAL FACILITIES ENGINEERING SYSTEMS COMMAND - MID-ATLANTIC
ROCC-ME
PORTSMOUTH NAVAL SHIPYARD
PORTSMOUTH NAVAL SHIPYARD - KITTEERY, ME
B60 REPAIRS
ENLARGED ELEVATOR PLANS AND SECTIONS

PROJECT NO.: 1740579
NAVFAC DRAWINGS NO.


SHEET 116 OF 282

AE411


DRAWING REVISION: 14 SEP 2023

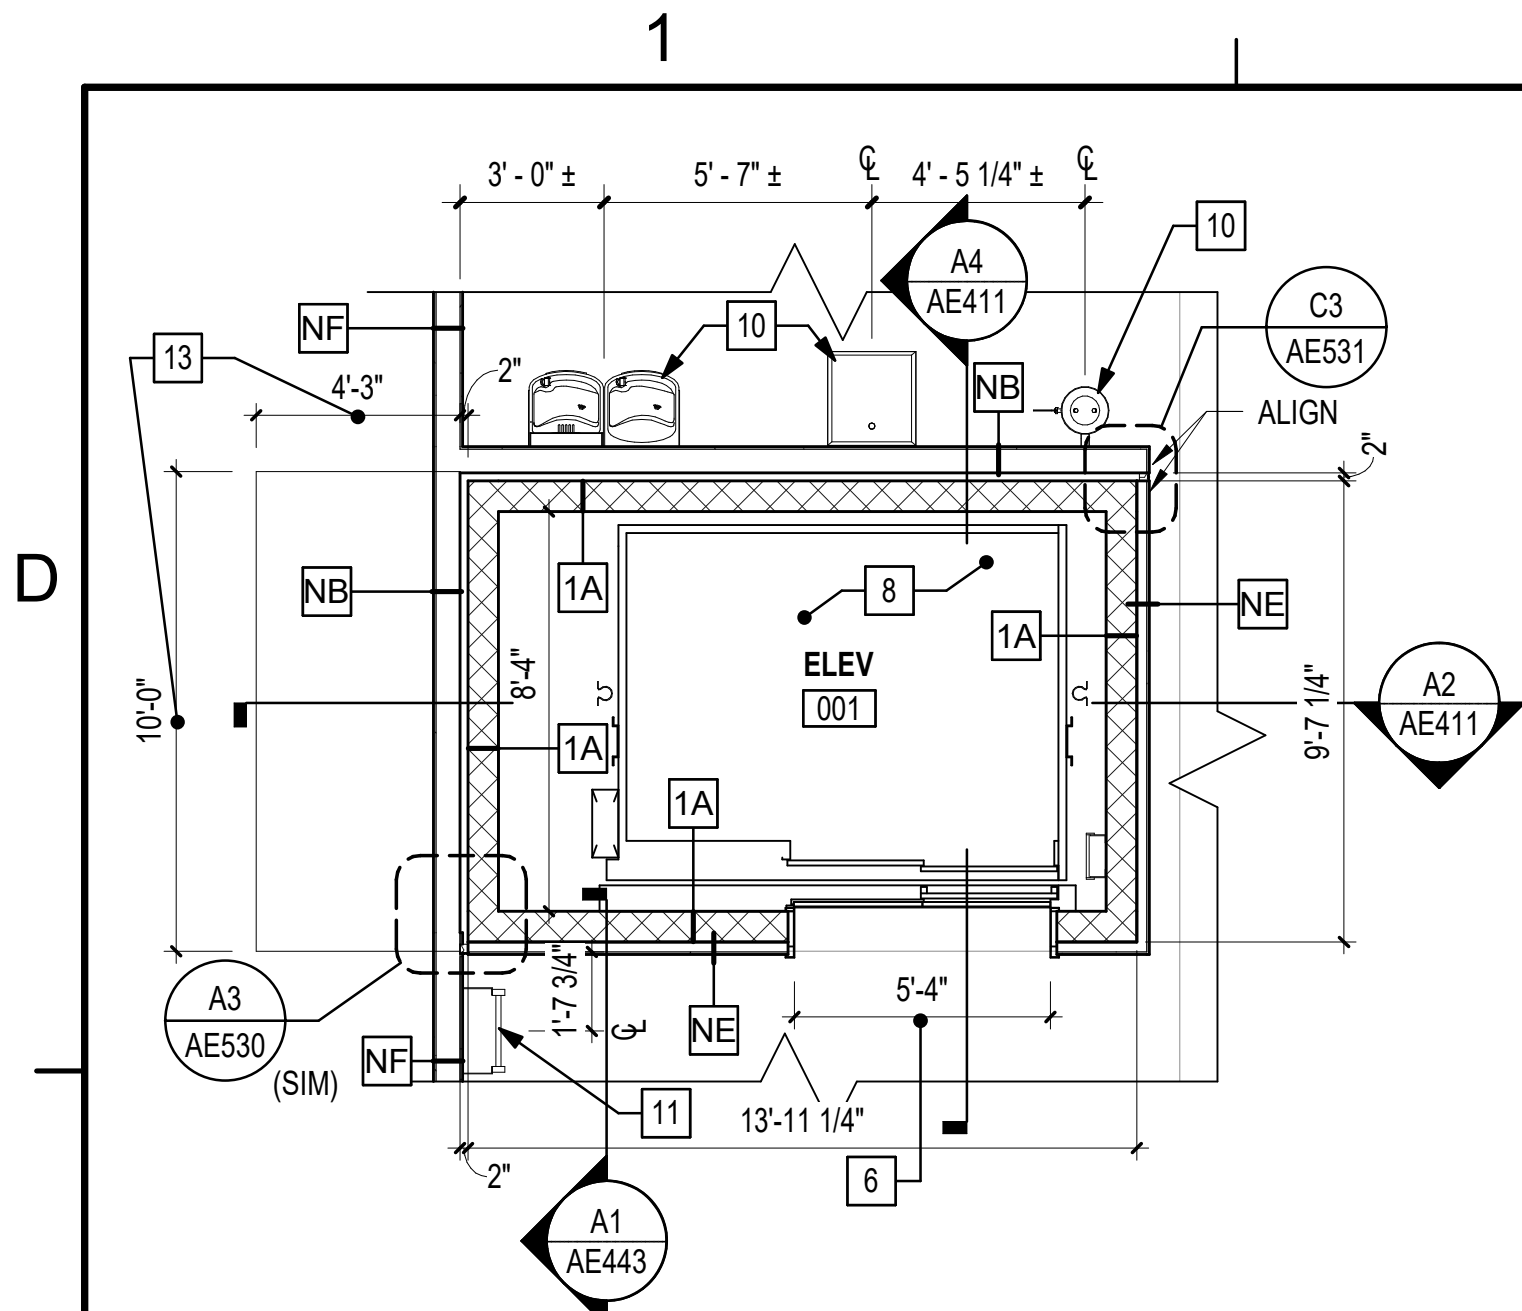


C1 ELEV 001 SECOND FLOOR PLAN
SCALE: 1/4" = 1'-0" (AE105)

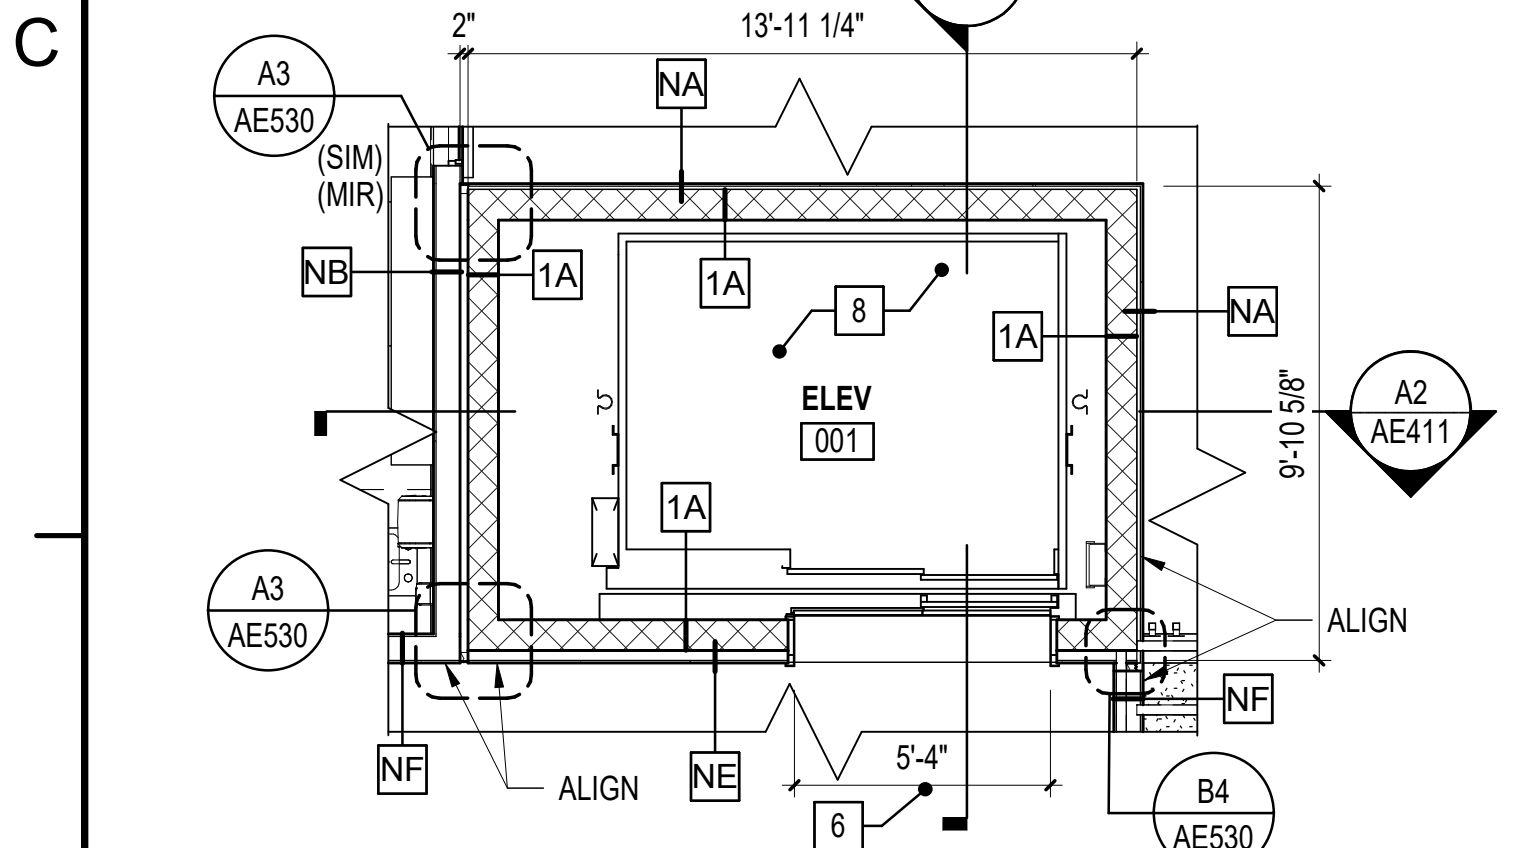


B1 ELEV 001 FIRST FLOOR MEZZANINE PLAN
SCALE: 1/4" = 1'-0" (AE104)

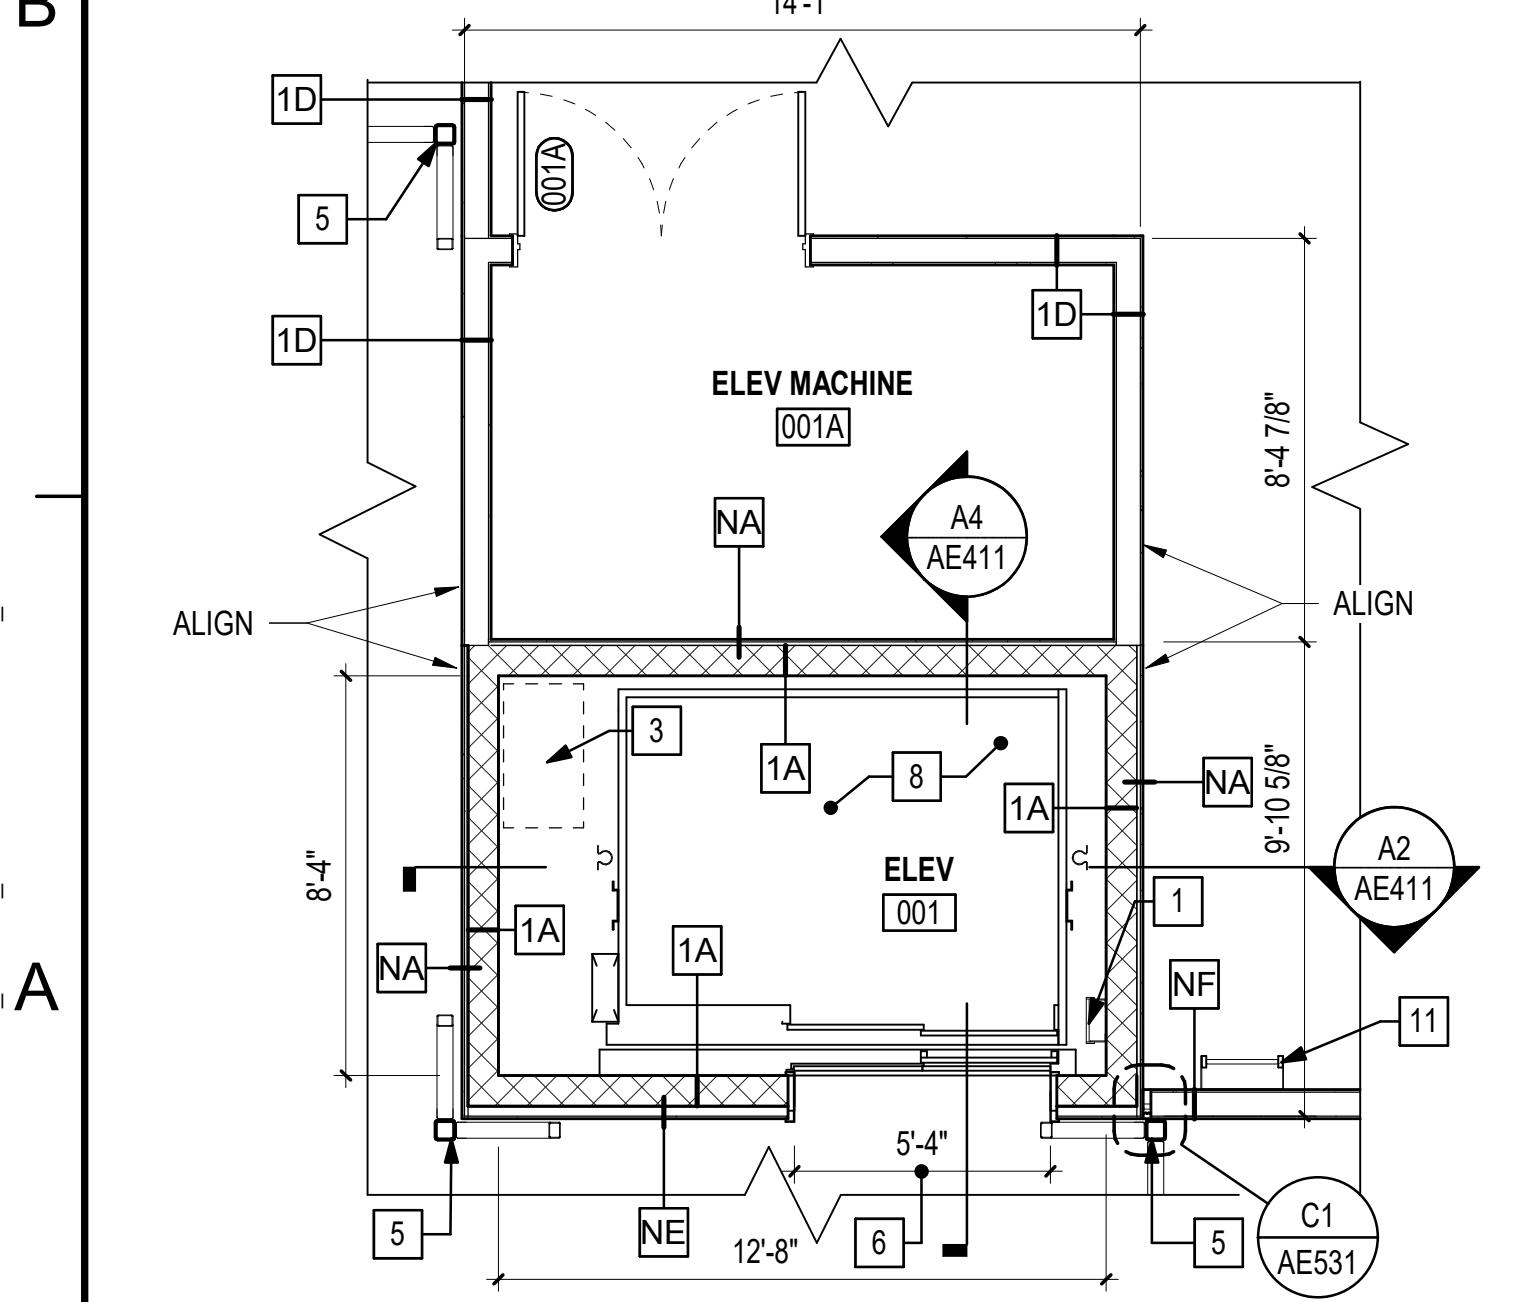

A1 ELEV 001 FIRST FLOOR PLAN
SCALE: 1/4" = 1'-0" (AE102)

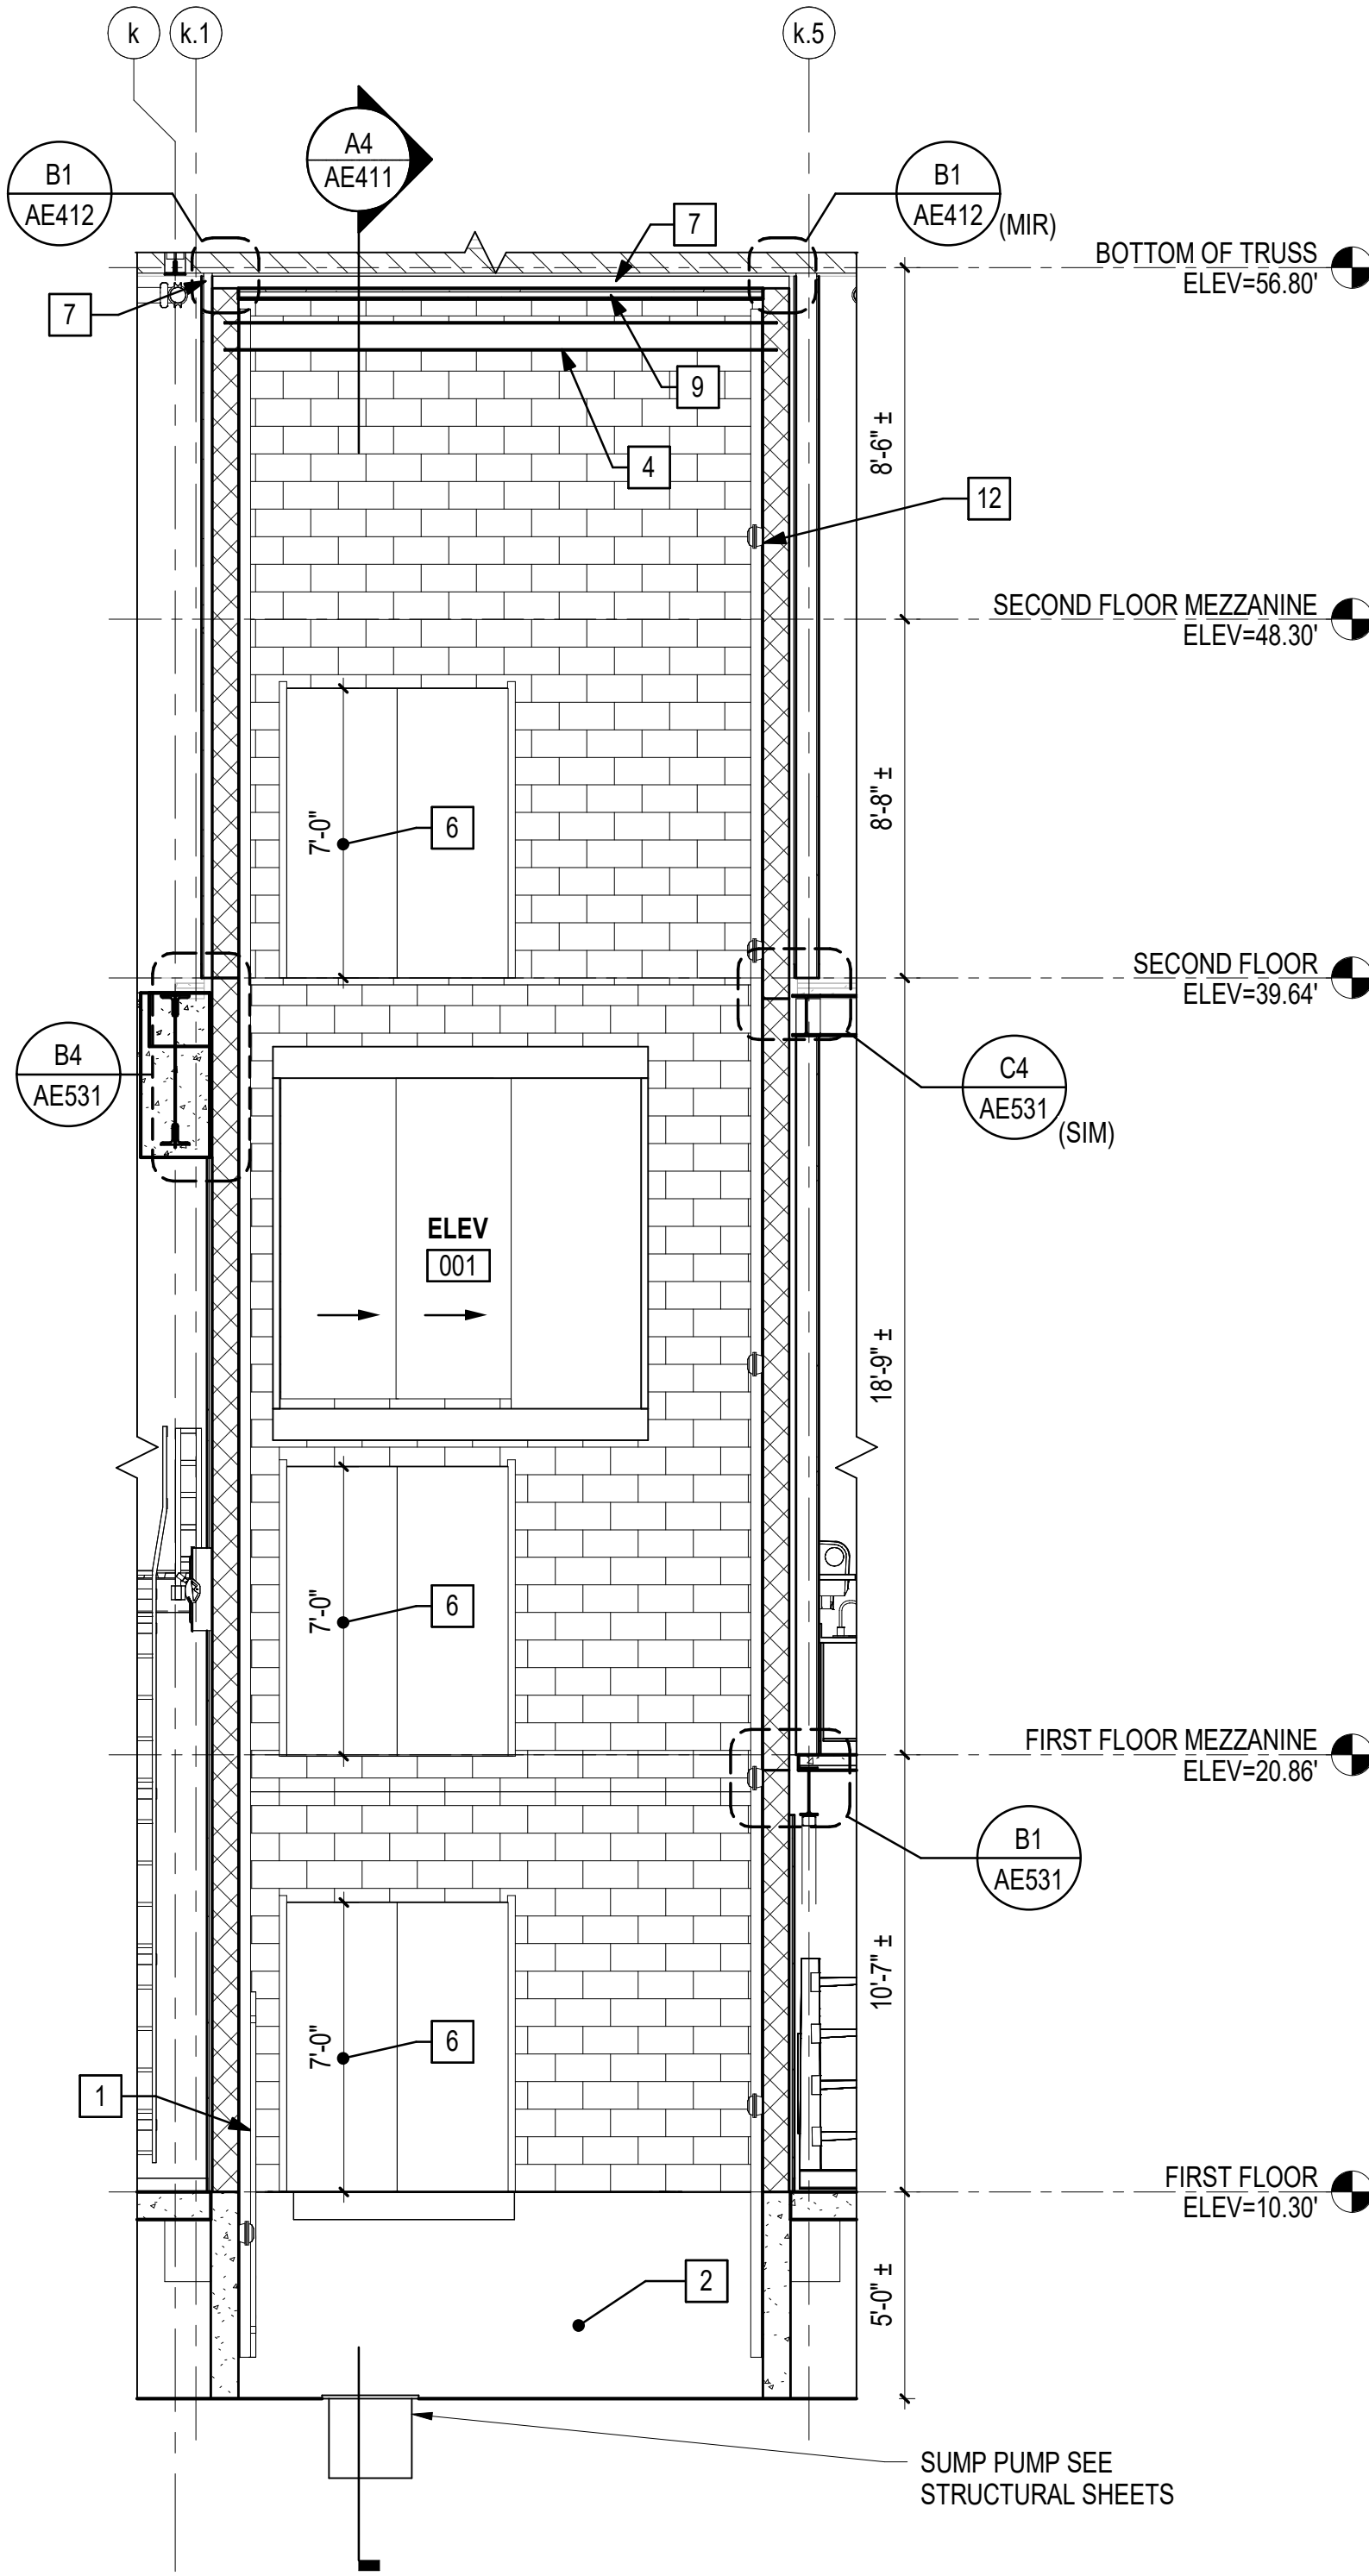

A2 ELEVATOR SECTION 1
SCALE: 1/4" = 1'-0" (AE411)

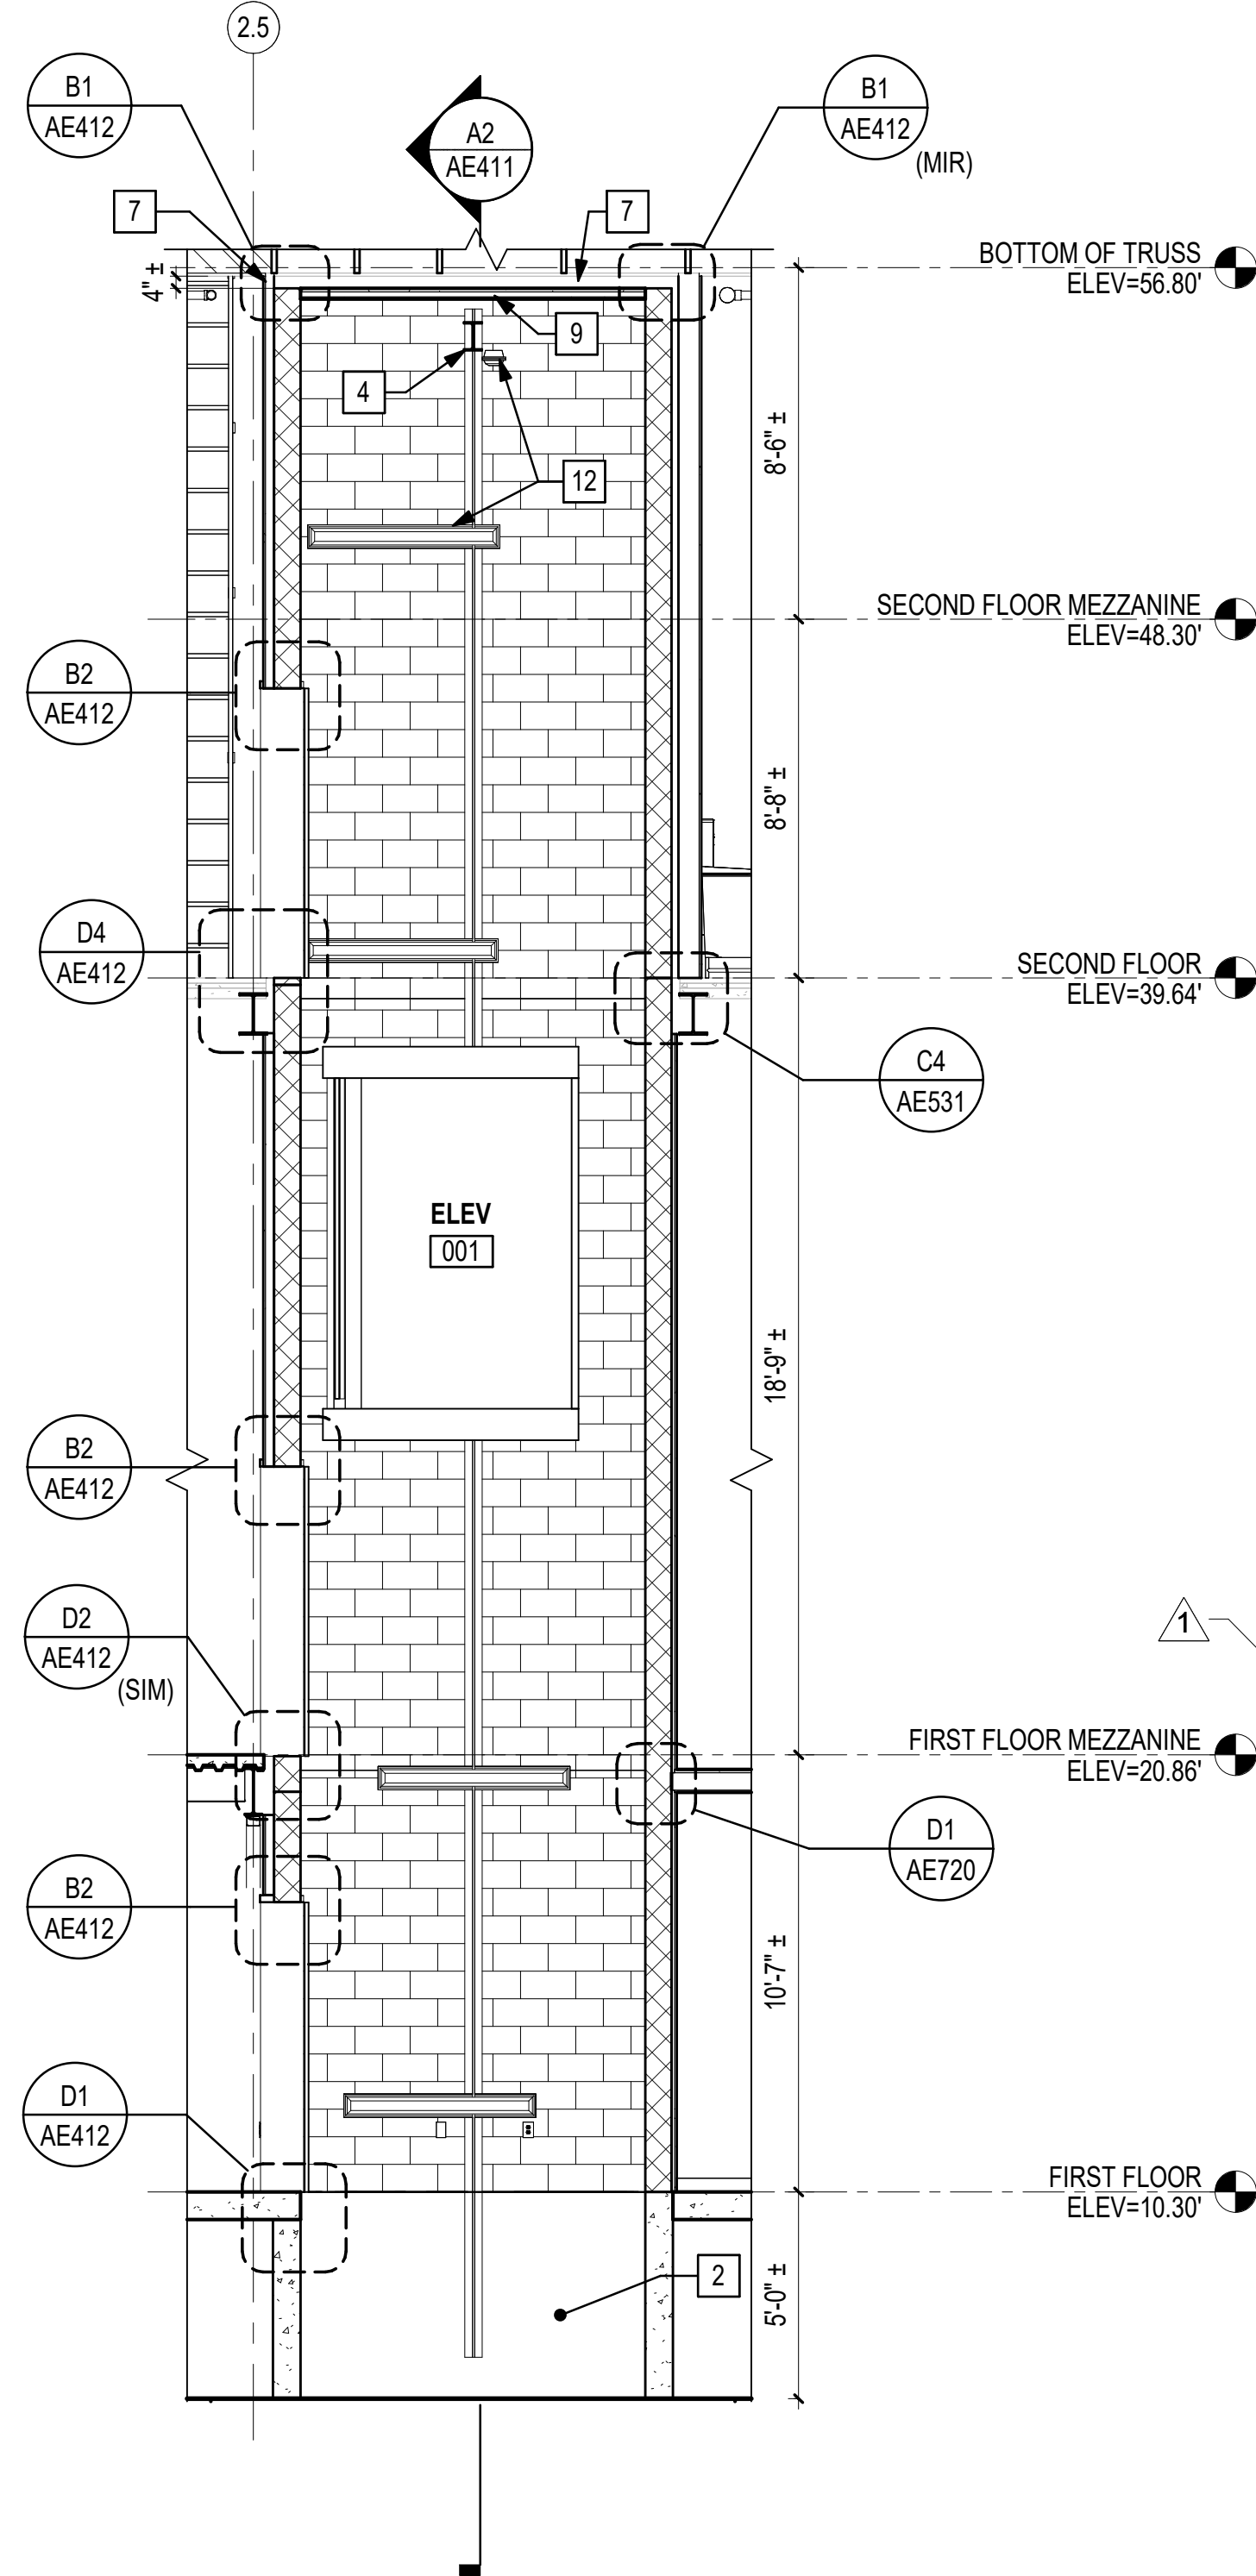

A4 ELEVATOR SECTION 2
SCALE: 1/4" = 1'-0" (AE411)