
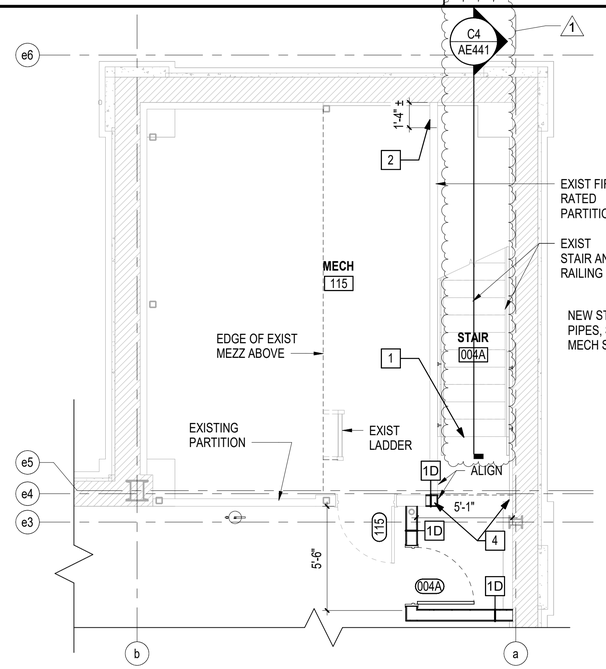



C1 STAIR 004 FIRST FLOOR PLAN

SCALE: 1/4" = 1'-0" (AE102)

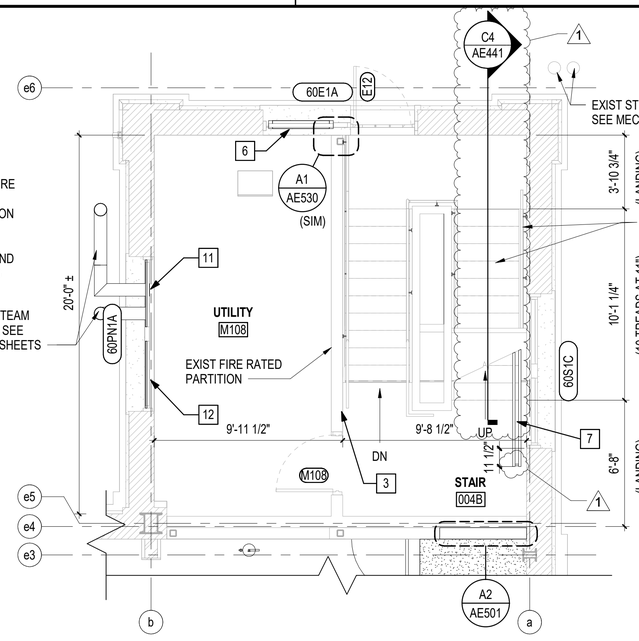


C3 STAIR 004 INTERMEDIATE LANDING PLAN

SCALE: 1/4" = 1'-0" (AE104)

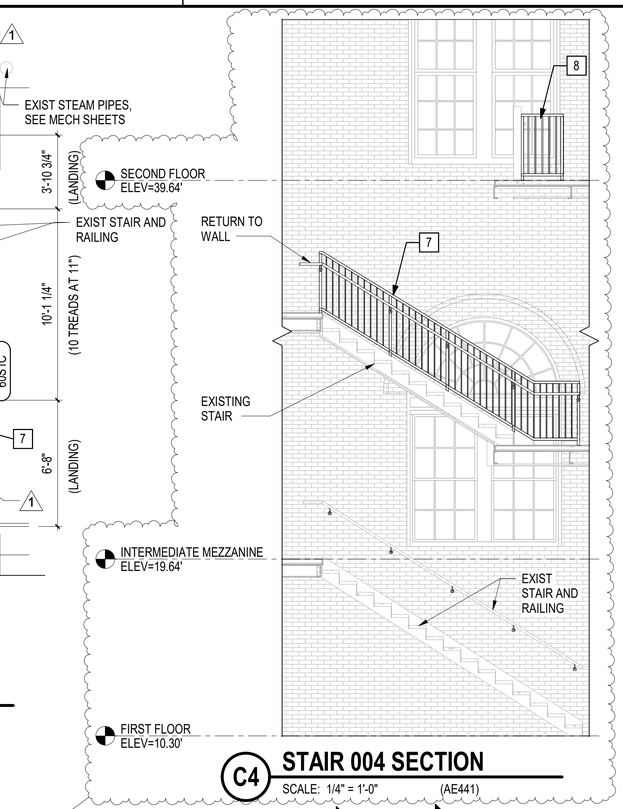


C4 STAIR 004 SECTION

SCALE: 1/4" = 1'-0" (AE441)

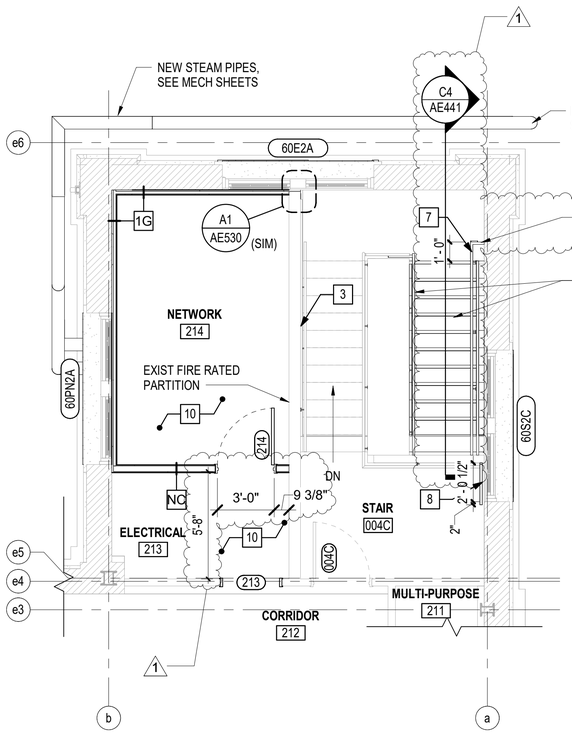


A1 STAIR 004 SECOND FLOOR PLAN - WEST

SCALE: 1/4" = 1'-0" (AE105)

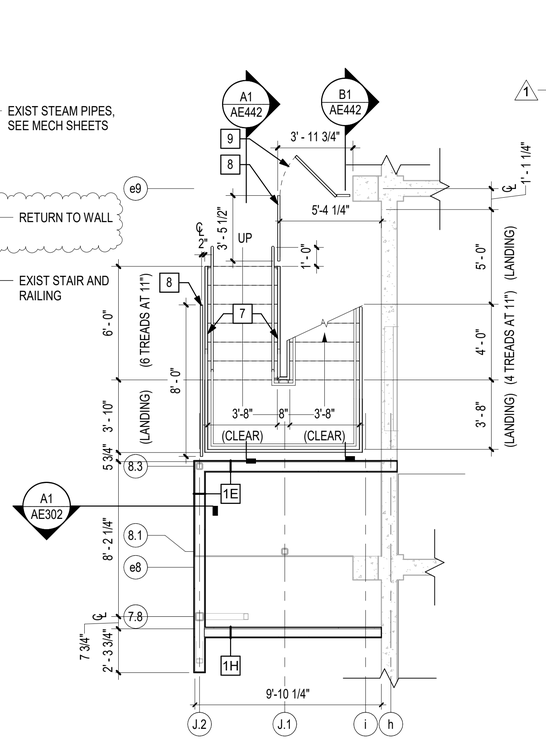

A3 STAIR 005 LANDING FLOOR PLAN

SCALE: 1/4" = 1'-0" (AE101)

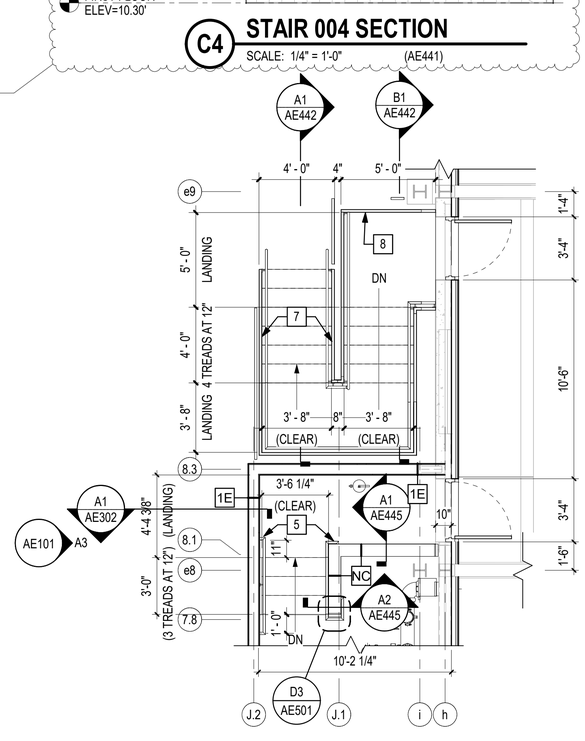

A4 STAIR 005 MEZZANINE FLOOR PLAN

SCALE: 1/4" = 1'-0" (AE103)


GENERAL NOTES

1. SEE SHEET AE001 FOR WALL TYPES.
2. SEE SHEET AE601 FOR DOOR SCHEDULE.
3. SEE SHEET AE622 FOR DOOR RESTORATION SCHEDULES.
4. SEE SHEET AE640 FOR ROOM FINISH SCHEDULE.

LEGEND

1. REPAIR DAMAGED SECTION OF STAIR. (REPLACE RISER AND PATCH STRINGER).
2. PATCH SECTION OF WALL WITH WALL TYPE 1D SIMILAR.
3. PROVIDE FIRESTOPPING AT EXISTING WALL PENETRATIONS (VIF), SEE C4/AE002 DETAILS.
4. SUPPORT FOR FIRE RATED WALL ABOVE, SEE DETAIL A2/AE501.
5. HANDRAIL, SEE DETAIL A2/AE444 AND A3/AE444.
6. LOUVER, SEE MECHANICAL SHEETS AND DETAIL A3/AE621
7. GUARDRAIL AND HANDRAIL, SEE DETAIL B3/AE444.
8. GUARDRAIL SYSTEM, SEE SIMILAR DETAIL C4/AE444.
9. SELF CLOSING SAFETY GATE, SEE DETAIL D3/AE445.
10. PATCH AND REPAIR WOOD FLOOR WHERE PLYWOOD WAS REMOVED, REFINISH WOOD FLOOR.
11. MECHANICAL EQUIPMENT WINDOW PENETRATION, SEE SIMILAR DETAIL C3/AE621 AND COORDINATE WITH MECHANICAL SHEETS.
12. MECHANICAL PIPE WINDOW PENETRATION, SEE DETAIL C1/AE621 AND COORDINATE WITH MECHANICAL AND PLUMBING SHEETS.

KEY PLAN

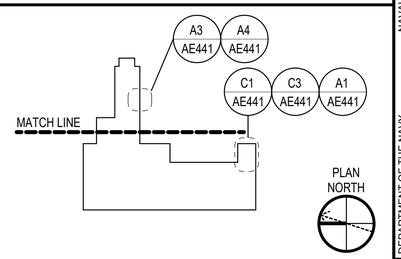

GRAPHIC SCALE(S)

1/8" = 1' - 0"

0 5' 10' 15' 30'

MARK	DESCRIPTION	DATE	APPR
1	AMENDMENT 010	03/20/2026	RSH
	FINAL SUBMISSION	10/01/2025	RSH

SEAL

OAK POINT ASSOCIATES

APPROVED
FOR COMMANDER NAVFAC
ACTIVITY
SATISFACTORY TO DATE
DESIGNER JMR
DRAWN BY MJD
CHECKED BY RSH
DESIGN MANAGER T. CARLETON
PROJECT MANAGER L. LYONS
FEAD/PM&E
FIRE PROTECTION S. RUCINSKI

NAVAL FACILITIES ENGINEERING SYSTEMS COMMAND - MID-ATLANTIC
PORTSMOUTH NAVAL SHIPYARD - KITTERY, ME

KITTERY, ME
B60 REPAIRS
ENLARGED STAIR PLANS 2

DEPARTMENT OF THE NAVY
NAVAL FACILITIES ENGINEERING SYSTEMS COMMAND
ROICC-ME
PORTSMOUTH NAVAL SHIPYARD

EPROJECT NO.: 1740579
NAVFAC DRAWING NO.

SHEET 120 OF 282

AE441

DRAWFORM REVISION: 14 SEP 2023

3/20/2026 11:39:55 AM AE441
C:\Users\mdonovan\Documents\22103.25_BLDG60_ARCHITECTURAL-V23_mdonovan8VFXR.rvt