


DOOR SCHEDULE																
DOOR NO.	TYPE	DOOR			FRAME			DETAILS			FIRE RATE	HDWR SET	NOTES			
		SIZE			MAT	FINISH	GLAZING	TYPE	MAT	FINISH				HEAD	JAMB	SILL
W	H	THK														
FIRST FLOOR																
001A	FD	6'-0"	7'-0"	1 3/4"	HM	PNT	N	1	HM	PNT	C1A/AE602	C1B/AE602	C1C/AE602	60 MIN	8	F
002A	NL	3'-0"	7'-0"	1 3/4"	HM	PNT	Y	1	HM	PNT	C1A/AE602	C1B/AE602	C1C/AE602	60 MIN	5	B, C, F
003A	NL	3'-0"	7'-0"	1 3/4"	HM	PNT	Y	1	HM	PNT	C1A/AE602	C1B/AE602	C1C/AE602	60 MIN	5	B, C, F
004A	NL	3'-0"	7'-0"	1 3/4"	HM	PNT	Y	1	HM	PNT	C1A/AE602	C1B/AE602	C1C/AE602	60 MIN	5	B, C, F
101A	OH	16'-0"	18'-2"	1 1/2"	STL	STD	N	-	STL	STD	B4A/AE602	B4B/AE602	-			
101B	OH	12'-0"	10'-0"	1 1/2"	STL	STD	N	-	STL	STD	B3A/AE602	B3B/AE602	-			
101C	NL	3'-0"	7'-0"	1 3/4"	HM	PNT	Y	1	HM	PNT	C1A/AE602	C1B/AE602	C1C/AE602		6	C
102	GD	8'-0"	8'-0"	1 3/4"	HM	PNT	Y	1	HM	PNT	C1A/AE602	C1B/AE602	C1C/AE602		15	C
105	F	3'-0"	7'-0"	1 3/4"	HM	PNT	N	1	HM	PNT	C1A/AE602	C1B/AE602	C1C/AE602		6	
106	F	3'-0"	7'-0"	1 3/4"	HM	PNT	N	1	HM	PNT	C1A/AE602	C1B/AE602	C1C/AE602	60 MIN	6	F
107	F	3'-0"	7'-0"	1 3/4"	HM	PNT	N	1	HM	PNT	C1A/AE602	C1B/AE602	C1C/AE602		7	
108A	EXIST	3'-6"	6'-8"	1 3/4"	WD	PNT	EXIST	WD	PNT	-	-	-	-		16	M
108B	EXIST	6'-10"	8'-0"	1 3/4"	WD	PNT	N	EXIST	WD	PNT	-	-	-			A
112	GD	6'-0"	8'-0"	1 3/4"	HM	PNT	Y	1	HM	PNT	C1A/AE602	C1B/AE602	C1C/AE602		14	C
113	F	3'-0"	7'-0"	1 3/4"	HM	PNT	N	1	HM	PNT	C1A/AE602	C1B/AE602	C1C/AE602		7	
114A	F	4'-0"	7'-0"	1 3/4"	HM	PNT	N	1	HM	PNT	C1A/AE602	C1B/AE602	C1C/AE602		7A	
114B	F	3'-0"	7'-0"	1 3/4"	HM	PNT	N	1	HM	PNT	C1A/AE602	C1B/AE602	C1C/AE602		7A	
115	EXIST	3'-0"	7'-0"	1 3/4"	HM	PNT	N	EXIST	HM	PNT	-	-	-		7	M
116A	EXIST	12'-6"	16'-0"	1 3/4"	STL	-	N	EXIST	-	-	-	-	-			I
117A	EXIST	6'-0"	8'-0"	1 3/4"	HM	-	Y	EXIST	MTL	-	-	-	-			A
117B	EXIST	5'-0"	5'-0"	1 3/4"	WD	-	N	EXIST	WD	-	-	-	-			A
118	F	2'-8"	7'-0"	1 3/4"	HM	PNT	N	1	HM	PNT	A1A/AE602	A1B/AE602	A1C/AE602		1	G
N11	EXIST	3'-0"	7'-0"	1 3/4"	WD	PNT	EXIST	EXIST	HM	PNT	-	-	-		4	M
W13	EXIST	3'-6"	7'-2"	2"	WD	PNT	EXIST	EXIST	HM	PNT	-	-	-			A, J
W14	EXIST	3'-6"	7'-2"	2"	WD	PNT	EXIST	EXIST	HM	PNT	-	-	-		4	M
FIRST FLOOR MEZZANINE																
002B	NL	3'-0"	7'-0"	1 3/4"	HM	PNT	Y	1	HM	PNT	C1A/AE602	C1B/AE602	C1C/AE602	60 MIN	5	B, C, F
003B	NL	3'-0"	7'-0"	1 3/4"	HM	PNT	Y	1	HM	PNT	C1A/AE602	C1B/AE602	C1C/AE602	60 MIN	5	B, C, F
E12	EXIST	3'-0"	7'-0"	1 3/4"	WD	PNT	EXIST	EXIST	HM	PNT	-	-	-		4	A
M104	P1	3'-0"	7'-0"	1 3/4"	WD	PNT	N	1	HM	PNT	C1A/AE602	C1B/AE602	C1C/AE602		7	
M105	FL	3'-0"	7'-0"	1 3/4"	HM	PNT	N	1	HM	PNT	C1A/AE602	C1B/AE602	C1C/AE602		6	H
M106	P1	3'-0"	7'-0"	1 3/4"	WD	PNT	N	1	HM	PNT	C1A/AE602	C1B/AE602	C1C/AE602		7	
M107A	FD	6'-0"	7'-0"	1 3/4"	HM	PNT	N	1	HM	PNT	C1A/AE602	C1B/AE602	C1C/AE602	60 MIN	8	F
M107B	F	3'-0"	7'-0"	1 3/4"	HM	PNT	N	1	HM	PNT	A1A/AE602	A1B/AE602	A1C/AE602		2	
M108	EXIST	3'-0"	7'-0"	1 3/4"	HM	PNT	EXIST	EXIST	HM	PNT	-	-	-	60 MIN	17	M, F
M116	F	3'-0"	7'-0"	1 3/4"	HM	PNT	N	1	HM	PNT	A1A/AE602	A1B/AE602	A1C/AE602		3	D
SECOND FLOOR																
003C	NL	3'-0"	7'-0"	1 3/4"	HM	PNT	Y	1	HM	PNT	C1A/AE602	C1B/AE602	C1C/AE602	60 MIN	5	B, C, F
004C	EXIST	3'-0"	7'-0"	1 3/4"	HM	PNT	EXIST	EXIST	HM	PNT	C1A/AE602	C1B/AE602	C1C/AE602	60 MIN	5	M, F
202	FL	3'-0"	7'-0"	1 3/4"	HM	PNT	N	1	HM	PNT	C1A/AE602	C1B/AE602	C1C/AE602		7	H
203	P1	3'-0"	7'-0"	1 3/4"	WD	PNT	N	1	HM	PNT	C1A/AE602	C1B/AE602	C1C/AE602		6	
204	P1	3'-0"	7'-0"	1 3/4"	WD	PNT	N	1	HM	PNT	C1A/AE602	C1B/AE602	C1C/AE602		10	
205	P1	3'-0"	7'-0"	1 3/4"	WD	PNT	N	1	HM	PNT	C1A/AE602	C1B/AE602	C1C/AE602		10	
206A	NL	3'-0"	7'-0"	1 3/4"	HM	PNT	Y	1	HM	PNT	C1A/AE602	C1B/AE602	C1C/AE602		9	C
206B	GD	6'-0"	8'-0"	1 3/4"	HM	PNT	Y	1	HM	PNT	C1A/AE602	C1B/AE602	C1C/AE602		14	C
208A	FD	5'-8"	7'-0"	1 3/4"	HM	PNT	N	1	MTL	PNT	C1A/AE602	C1B/AE602	C1C/AE602	60 MIN	13	D
208B	EXIST	2'-5"	6'-7"	1 3/4"	WD	PNT	N	EXIST	WD	PNT	-	-	-		12	M
209A	P1	3'-0"	7'-0"	1 3/4"	WD	PNT	N	1	HM	PNT	C1A/AE602	C1B/AE602	C1C/AE602		12	G
209B	P1	3'-0"	7'-0"	1 3/4"	WD	PNT	N	1	HM	PNT	C1A/AE602	C1B/AE602	C1C/AE602		11	D, G
210	P1	3'-0"	7'-0"	1 3/4"	WD	PNY	N	1	HM	PNT	C1A/AE602	C1B/AE602	C1C/AE602		9	C
211	P1	3'-0"	7'-0"	1 3/4"	WD	PNY	N	1	HM	PNT	C1A/AE602	C1B/AE602	C1C/AE602		6	C, G
212	-	-	-	-	-	-	-	3	HM	PNT	C1A/AE602	C1B/AE602	C1C/AE602			L
213	-	-	-	-	-	-	-	EXIST	HM	PNT	-	-	-			K
214	F	3'-0"	7'-0"	1 3/4"	HM	PNT	N	1	HM	PNT	C1A/AE602	C1B/AE602	C1C/AE602		7	
SECOND FLOOR MEZZANINE																
M201	EXIST	2'-6"	7'-2"	1 3/4"	WD	-	N	EXIST	WD	-	-	-	-			N

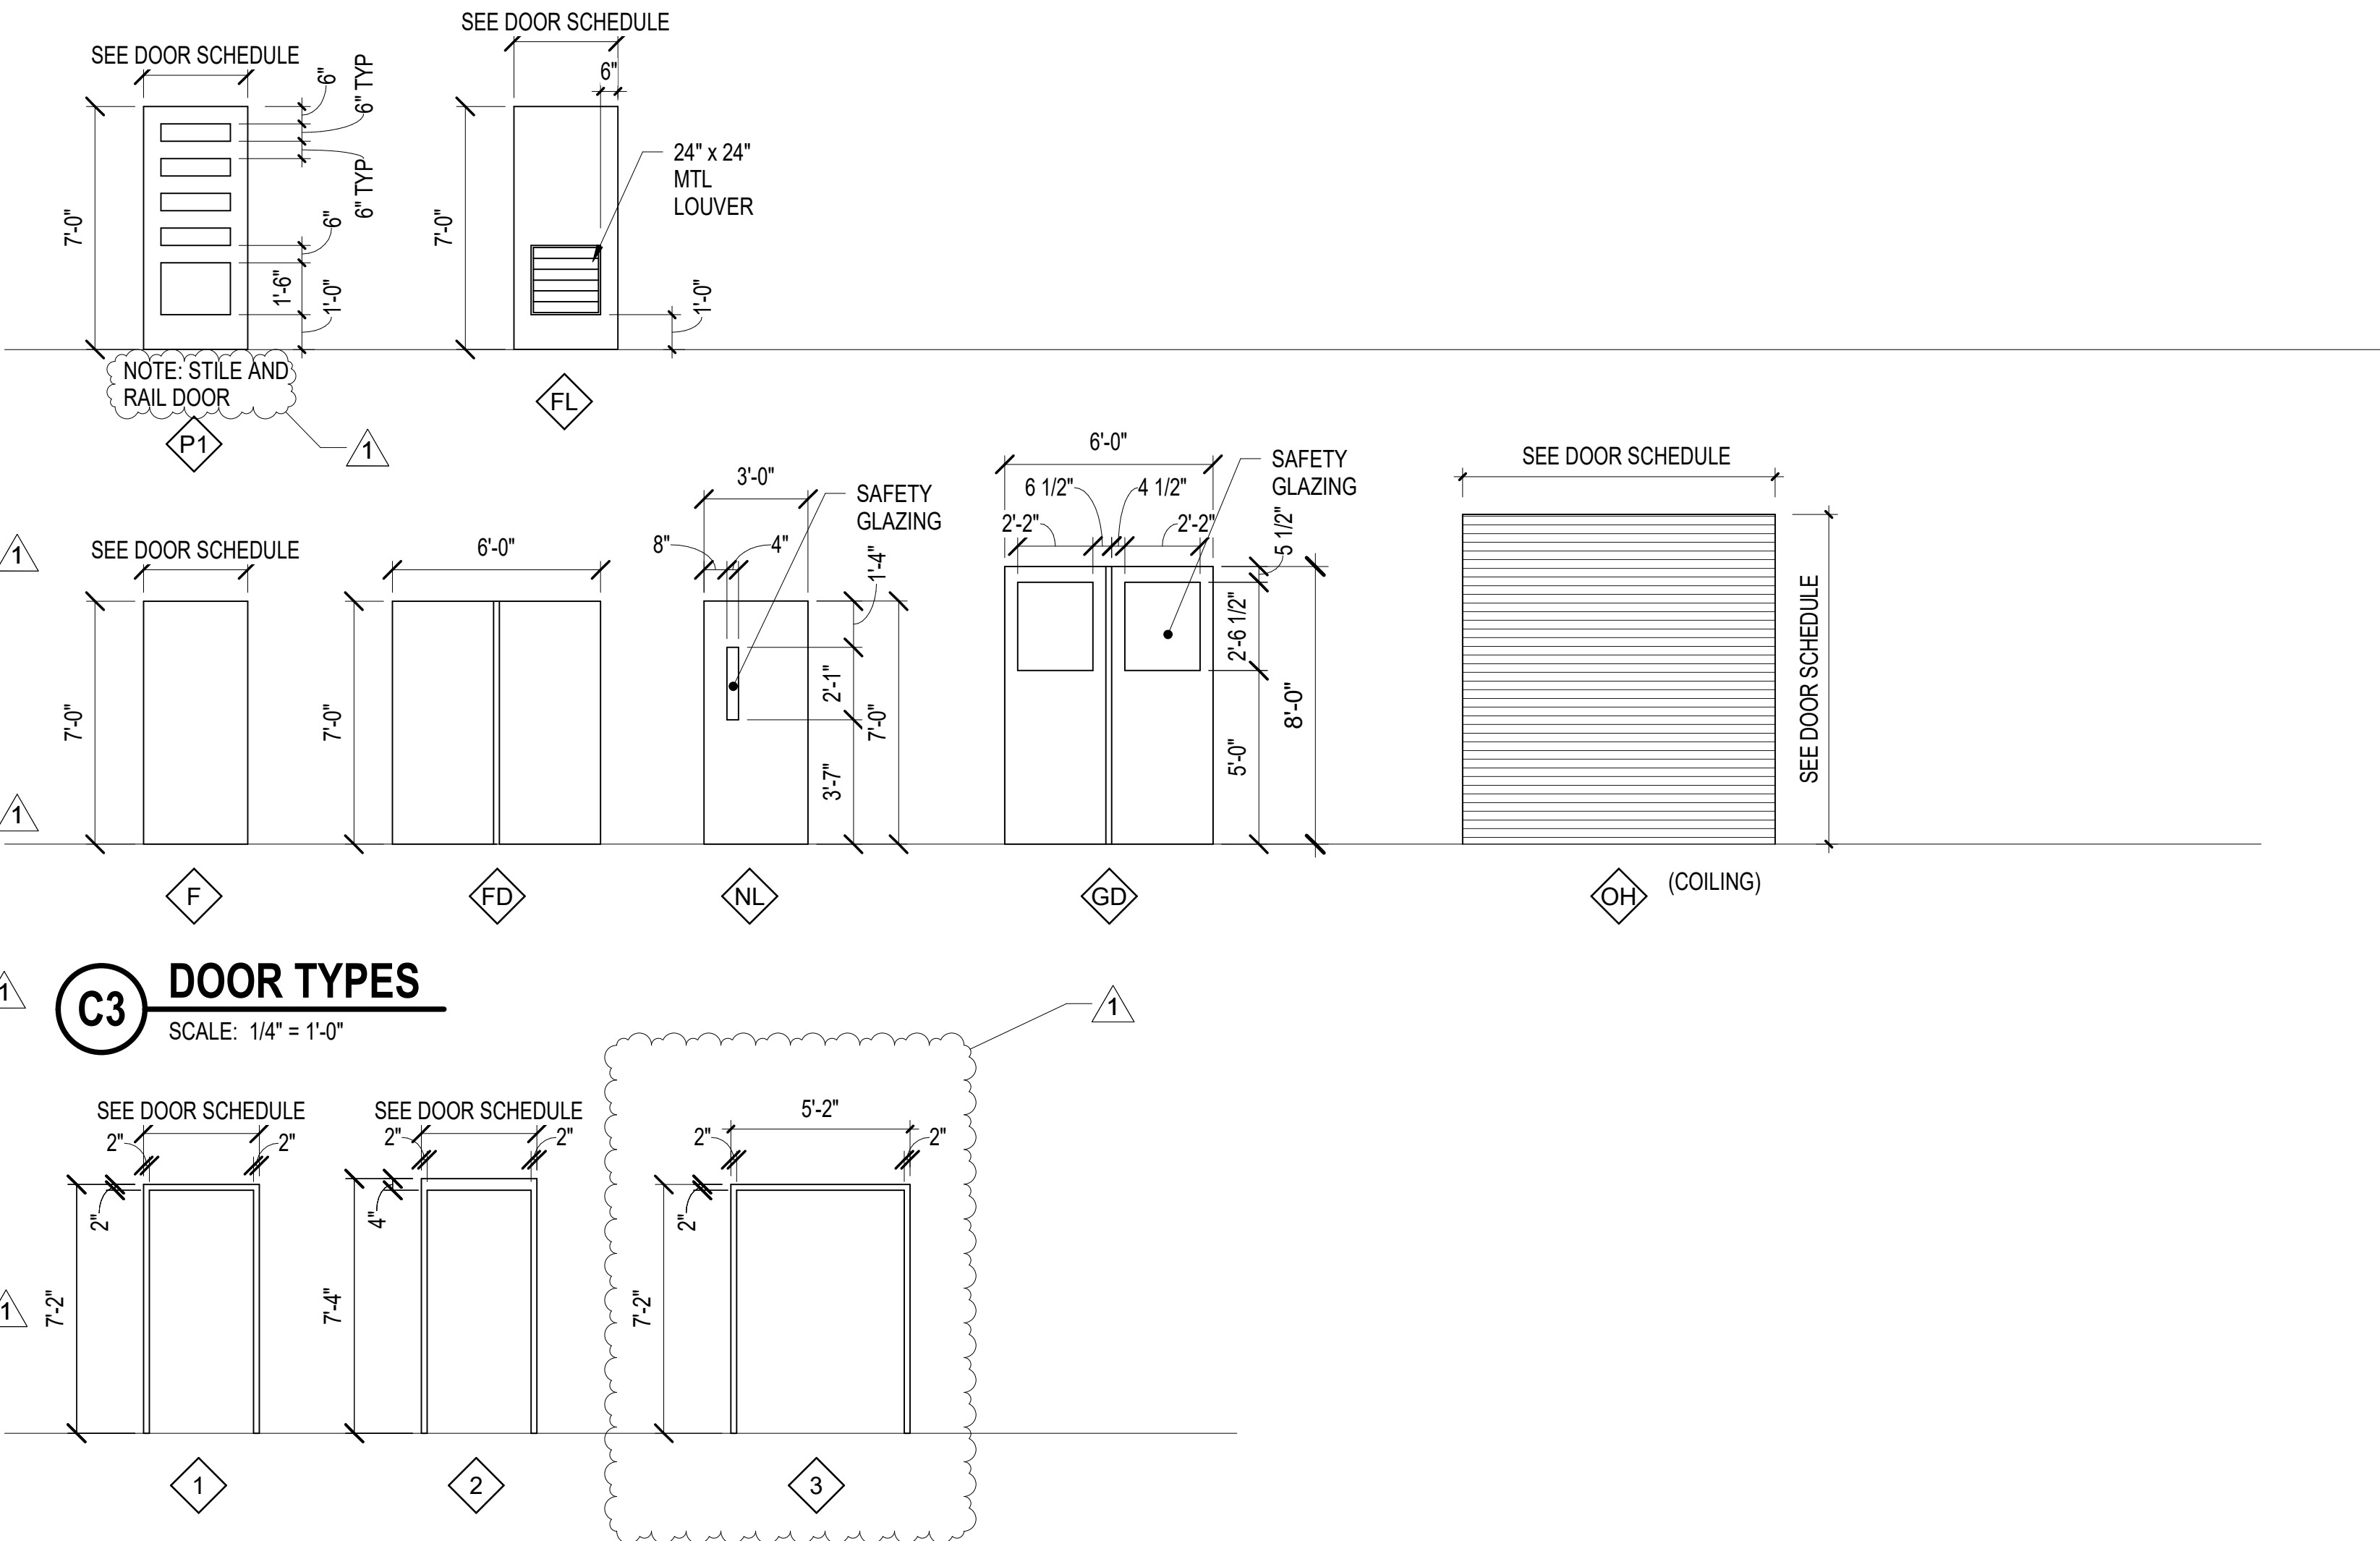

C3 DOOR TYPES
SCALE: 1/4" = 1'-0"

B3 FRAME TYPES
SCALE: 1/4" = 1'-0"

DOOR SCHEDULE NOTES	
A	REMOVE EXISTING DOOR, REFINISH DOOR AND HARDWARE, REINSTALL
B	FIRE PROTECTION RATED GLAZING
C	1/4" THICK TEMPERED GLAZING
D	BADGE READER, COORDINATE WITH ELECTRICAL SHEETS
E	INSULATED LAMINATED GLAZING
F	INSTALL FIRE DOORS IN ACCORDANCE WITH NFPA 80 AND SMOKE DOORS IN ACCORDANCE WITH NFPA 105. DO NOT PAINT OVER LABELS.
G	DOOR/FRAME INSTALLED IN EXISTING OPENING. VERIFY DIMENSIONS IN FIELD.
H	DOOR LOUVER, COORDINATE WITH MECHANICAL SHEETS.
I	PAINT MAN DOOR. EXPOSED GALVANIZED FINISH AT SLIDING DOOR TO REMAIN.
J	EXISTING DOOR. FASTEN DOOR IN CLOSED POSITION. SEE DETAIL D4/AE302.
K	EXISTING DOOR FRAME. PAINT.
L	DOOR FRAME ONLY. DOOR DETAILS SIMILAR.
M	REMOVE EXISTING DOOR, REFINISH DOOR AND HARDWARE, REINSTALL. PROVIDE NEW HARDWARE AS INDICATED IN HARDWARE SET.
N	EXISTING DOOR TO REMAIN.

DOOR SCHEDULE GENERAL NOTES	
1.	PROVIDE DOORS WITH CONSTRUCTION CORES.
2.	SEE LIFE SAFETY SHEETS FOR FIRE/SMOKE PARTITION LOCATIONS.
3.	SEE SHEET AE622 FOR HISTORIC WOOD DOOR REPAIRS.

SCHEDULE KEY					
ALUM	ALUMINUM	MIN	MINUTE	STD	MANUFACTURERS STANDARD
EXIST	EXISTING	MTL	METAL	STL	STEEL
HDWR	HARDWARE	NAT	NATURAL/STAINED FINISH	QTY	QUANTITY
HM	HOLLOW METAL	PNT	PAINT	WD	WOOD
MAT	MATERIAL	SS	STAINLESS STEEL		

GENERAL NOTES	GRAPHIC SCALE(S)
1. SEE SHEET AE622 FOR HISTORICAL DOOR REPAIR AND RESTORATION INFORMATION.	01'5'10'15' 1/4" = 1' - 0"

APPROVED

FOR COMMANDER NAVFAC

ACTIVITY

SATISFACTORY TO DATE

DESIGNER JMR

DRAWN BY MJD

CHECKED BY RSH

DESIGN MANAGER T. CARLETON

PROJECT MANAGER L. LYONS

READ/NAME

FIRE PROTECTION S. RUCINSKI

NAVAL FACILITIES ENGINEERING SYSTEMS COMMAND

NAVAL FACILITIES ENGINEERING SYSTEMS COMMAND - MID-ATLANTIC

PORTSMOUTH NAVAL SHIPYARD - KITTEERY, ME

B60 REPAIRS

DOOR SCHEDULE AND DETAILS

PROJECT NO. 1740579

NAVFAC DRAWINGS NO.

SHEET 132 OF 282

AE601

DATE 03/20/2026

RSH

DATE 10/07/2025

MARK DESCRIPTION

AMENDMENT 010

DATE

APR

SEAL

NAVFAC

OAK POINT ASSOCIATES