

D

C

B


A

D

C

B

A

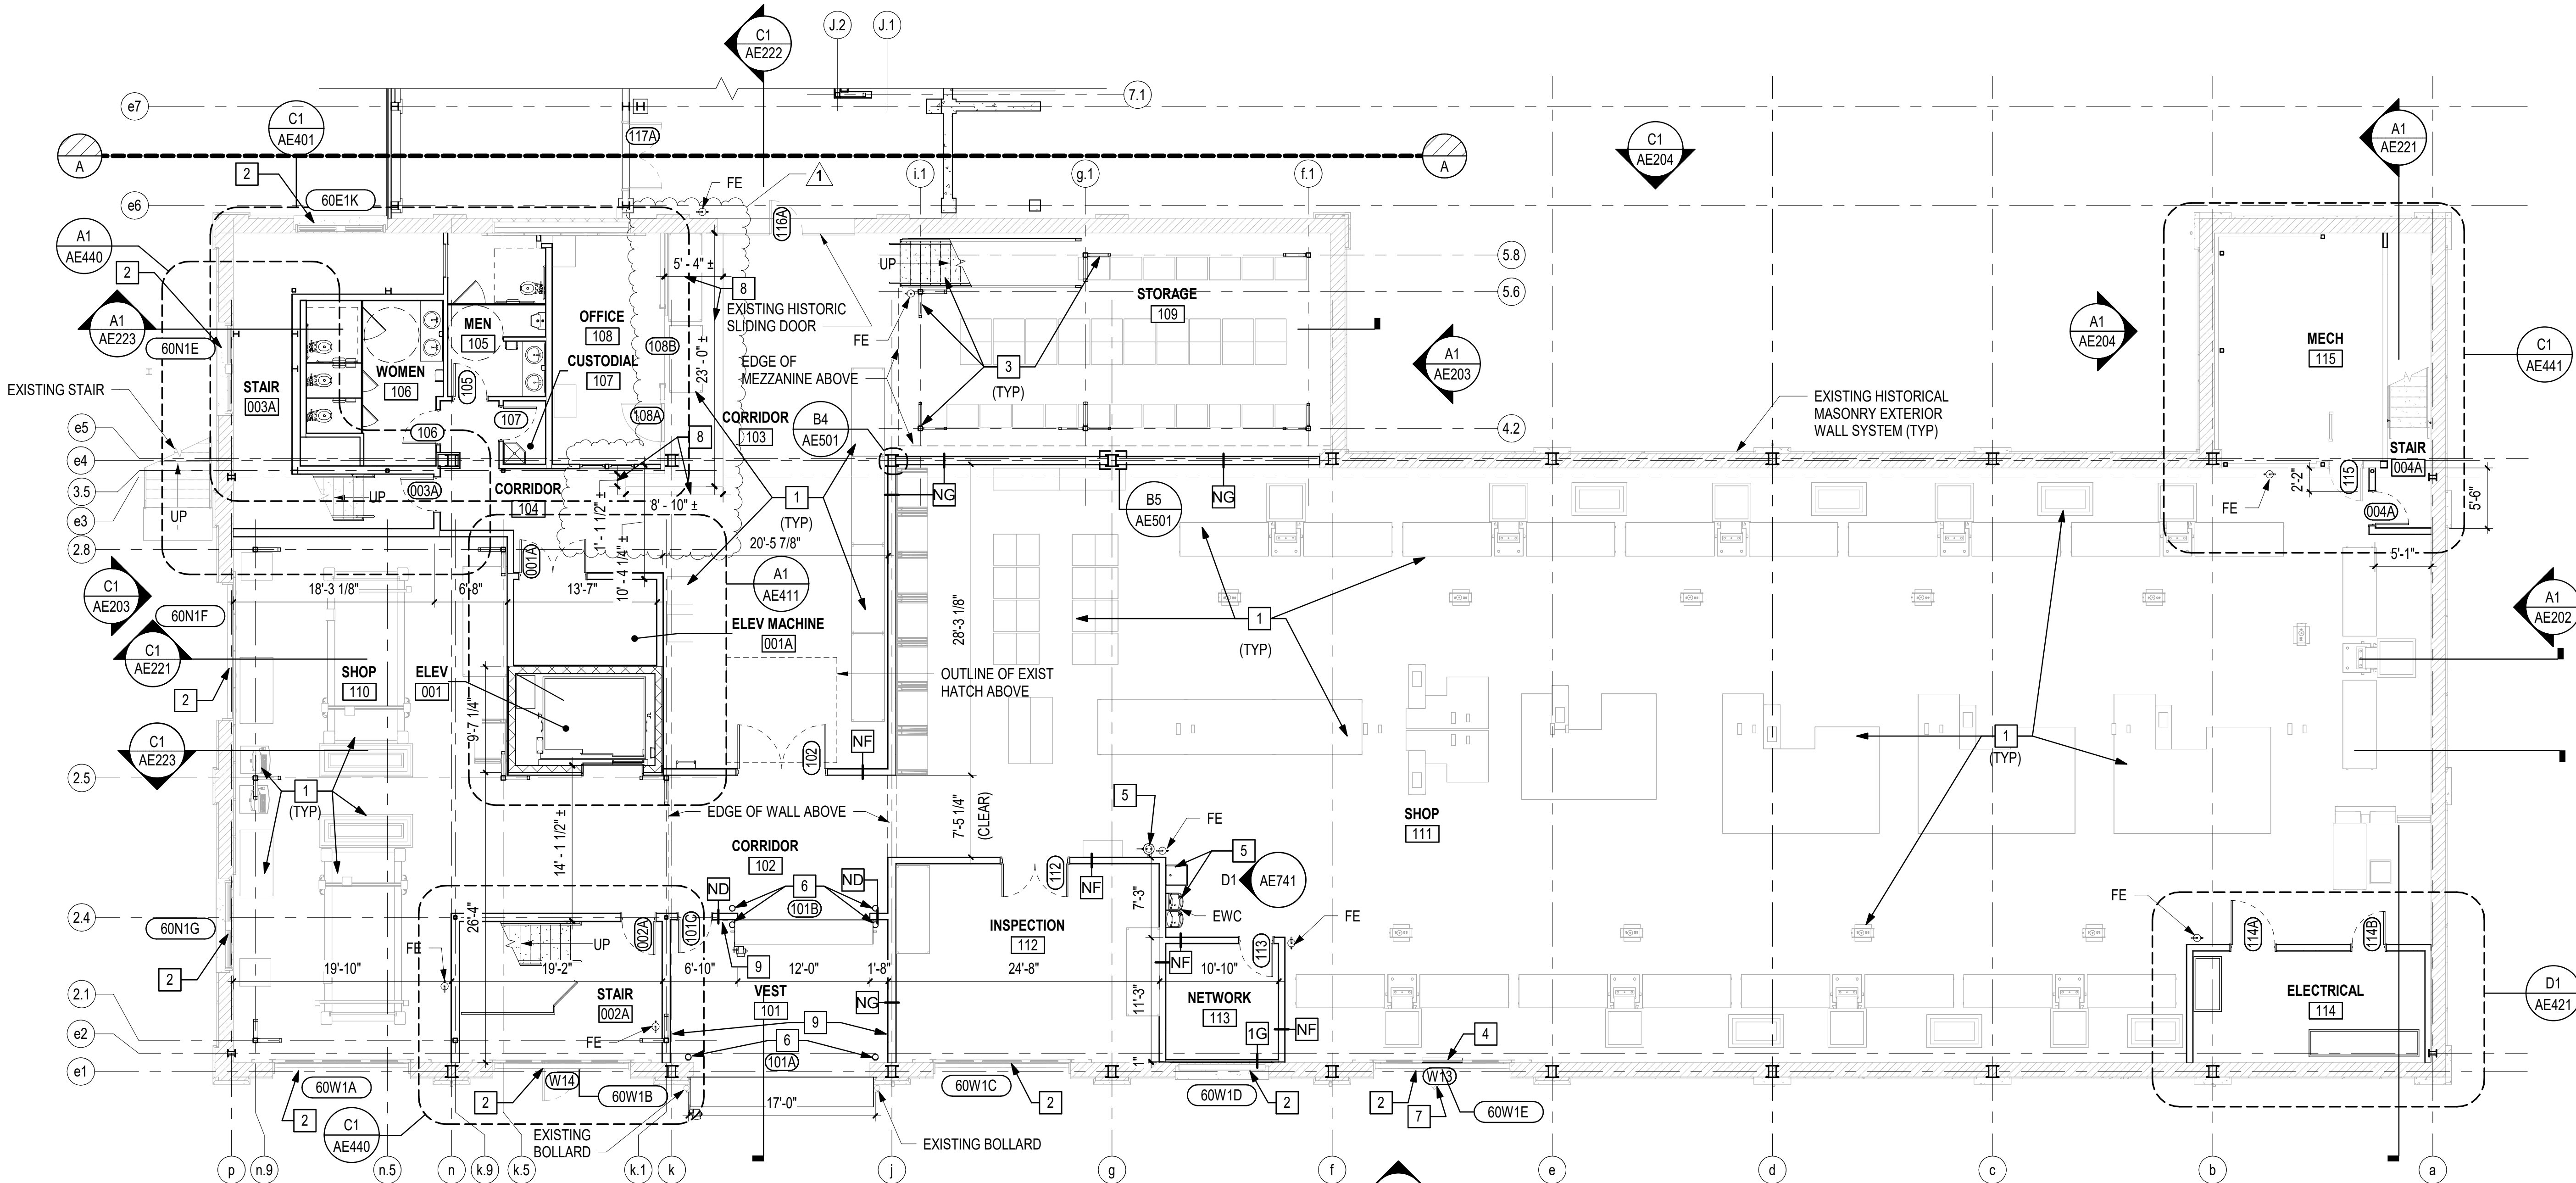

B1 FIRST FLOOR PART PLAN - WEST
SCALE: 1/8" = 1'-0"


GENERAL NOTES

1. SEE SHEET AE101 FOR GENERAL NOTES.
2. B59 WILL BE OCCUPIED DURING CONTRACTING. COORDINATE WORK PLAN AND ACCESS WITH CONSTRUCTION OFFICER.
3. IN ADDITION TO THE AREAS INDICATED, PROVIDE 200 SF OF PATCH AND REPAIR WOOD FLOOR WORK FOR WORK NOT OTHERWISE INDICATED IN THE DRAWINGS. LOCATIONS TO BE COORDINATED WITH THE CONTRACTING OFFICER.

KEYNOTES

- 1 INDUSTRIAL EQUIPMENT, SEE Q-SHEETS.
- 2 REPAIR HISTORIC WOOD WINDOW/DOOR, SEE RESTORATION SCHEDULE ON SHEET AE622.
- 3 METAL FRAMED MEZZANINE AND STAIR STRUCTURE, SEE STRUCTURAL SHEETS.
- 4 PATCH SLAB AND SEAL DOOR THRESHOLD SEE DETAIL D4/AE302.
- 5 PLUMBING FIXTURE, SEE PLUMBING SHEETS. PROVIDE BLOCKING IN STUD WALL AT WALL MOUNTED FIXTURE LOCATIONS.
- 6 BOLLARD, SEE STRUCTURAL SHEETS.
- 7 EXISTING WOOD DOOR. FIX IN CLOSED AND LOCKED POSITION AND SEAL PERIMETER OF EACH LEAF.
- 8 REFINISH APPROXIMATELY 125 SF WOOD PLANK FLOORING [OPTION 8].
- 9 WATER RESISTANT GYP BOARD (PNT).

KEY PLAN

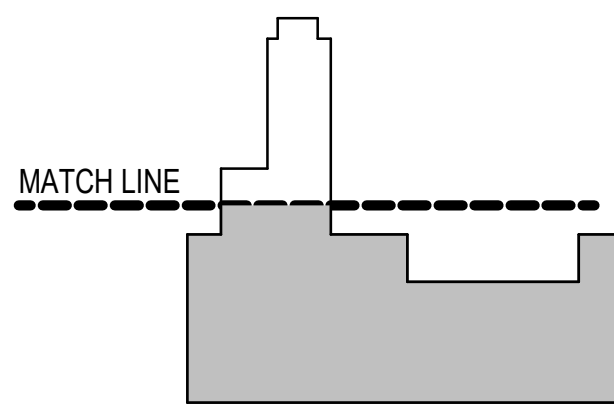

GRAPHIC SCALE(S)



APR	DATE	RSH	03/10/2026	AMENDMENT 008	FINAL SUBMISSION	MARK	DESCRIPTION
FOR COMMANDER NAVFAC							
ACTIVITY							
SATISFACTORY TO DATE							
DESIGNER JMR							
DRAWN BY MJD							
CHECKED BY RSH							
DESIGN MANAGER T. CARLETON							
PROJECT MANAGER L. LYONS							
HEADLINE							
FIRE PROTECTION S. RUCINSKI							
NAVAL FACILITIES ENGINEERING SYSTEMS COMMAND - MID-ATLANTIC							
PORTSMOUTH NAVAL SHIPYARD - KITTEERY, ME							
B60 REPAIRS							
FIRST FLOOR PART PLAN - WEST							
PROJECT NO. 1740579							
NAVFAC DRAWING NO.							
SHEET 93 OF 282							
AE102							
DRAWING REVISION: 14 SEP 2023							