

PLUMBING FIXTURE ROUGH-IN SCHEDULE

UNIT NO	DESCRIPTION	WASTE	VENT	HW	CW	REMARKS	BASIS OF DESIGN
WC-1	WATER CLOSET	4"	2"	-	1"	FLOOR MOUNTED, FLOOR OUTLET, MANUAL FLUSH VALVE, ADA HEIGHT	AMERICAN STANDARD MADERA 2854.016
WC-2	WATER CLOSET	4"	2"	-	1"	FLOOR MOUNTED, FLOOR OUTLET, MANUAL FLUSH VALVE	AMERICAN STANDARD MADERA 2858.016
U-1	URINAL	2"	1 1/2"	-	3/4"	WALL HUNG, MANUAL FLUSH VALVE, ADA HEIGHT	AMERICAN STANDARD WASHBROOK 6590.501
L-1	LAVATORY, COUNTER	1 1/2"	1 1/2"	1/2"	1/2"	OVAL, STAINLESS STEEL, COUNTERTOP, UNDERMOUNT, MANUAL FAUCET, ADA HEIGHT	ELKAY ASANA ELUH1511
L-2	LAVATORY, WALL HUNG	1 1/2"	1 1/2"	1/2"	1/2"	WALL HUNG, CONCEALED CARRIER, MANUAL FAUCET, ADA HEIGHT	SLOAN SS-3003
S-1	SINK, KITCHENETTE	2"	1 1/2"	1/2"	1/2"	SINGLE-BASIN, STAINLESS STEEL, COUNTERTOP, UNDERMOUNT, ADA HEIGHT	ELKAY ELUHAD 191655
S-3	3-STATION WASH SINK	2"	1 1/2"	3 @ 1/2"	3 @ 1/2"	WALL MOUNTED, STAINLESS STEEL, THREE MANUAL FAUCETS, ADA HEIGHT	ELKAY EWMA6020C
S-2	UTILITY SINK	2"	1 1/2"	1/2"	1/2"	PLASTIC DEEP BASIN W/ STEEL LEGS, MANUAL FAUCET	SWAN MODEL MF-F
MR-1	MOP RECEPTOR	3"	1 1/2"	1/2"	1/2"	FLOOR MOUNTED, 24x24 NEO-ANGLE DROP FRONT TERAZZO, MANUAL WALL FAUCET	FLORESTONE MODEL 96
EW-1	EMERGENCY EYEWASH			1/2"		WALL MOUNTED W/ COVER (*TEMPERED WATER), WITH EMERGENCY ALARM SYSTEM	HAWS MODEL 7360 BTWC, HAWS 9001.5
EW-1	ELECTRIC WATER COOLER	1 1/2"	1 1/2"	-	1/2"	WALL MOUNTED, BI-LEVEL, WITH BOTTLE FILLER, FIXTURE CARRIER, NO FILTER	ELKAY EZSTLG8WSSK
HB	HOSE BIBB	-	-	-	3/4"	SURFACE MOUNTED, CHROME FINISH, WHEEL HANDLE	
COB	COFFE MAKER OUTLET BOX	-	-	-	1/2"	RECESSED, WITH INTEGRAL BALL VALVE	
FD-1	FLOOR DRAIN	2"	1 1/2"	-	1/2" TP	SEE DRAIN SCHEDULE	
FD-2	FLOOR DRAIN	3"	1 1/2"	-	1/2" TP	SEE DRAIN SCHEDULE	
FD-3	FLOOR DRAIN	4"	2"	-	1/2" TP	SEE DRAIN SCHEDULE	
FS-1	FLOOR SINK	4"	2"	-	1/2" TP	SEE DRAIN SCHEDULE	

- NOTES:
- FOR FIXTURE, FAUCET, AND/OR FAUCET MOUNTING HEIGHTS, SEE AE002.
 - PROVIDE WITH ASSE 1070 TEMPERATURE LIMITING DEVICE, EITHER INTEGRAL WITH FAUCET OR SUPPLIED ON HOT WATER LINE TO FAUCET.

PUMP SCHEDULE

UNIT NO	SERVES	LOCATION	TYPE	GPM	TOTAL HEAD	MOTOR DATA			SUCTION/ DISCHARGE (IN)	BASIS OF DESIGN	NOTES
						HP	RPM	VOLTS/PHASE			
RP-1	DHW RECIRC	MECH. M106	IN-LINE	3.0	25	1/8	3250	115/1	1/1	TACO GENIE 008	1
SP-1	ELEV PIT	ELEV SHAFT	SUMP	50.0	10	4/10	-	115/1	11.5	ZOELLER N152 OIL GUARD SYSTEM	2

- NOTES:
- PROVIDE STAINLESS STEEL PUMP FOR POTABLE WATER.
 - PROVIDE PACKAGED PUMP SYSTEM WITH OIL SWITCH, FLOAT SWITCH, AND NEMA 4x ALARM AND CONTROL PANEL WITH H-O-A SWITCH, AUDIO AND VISUAL ALARM DEVICES, AND DRY ALARM CONTACT FOR DDC SYSTEM INTERFACE.

BACKFLOW PREVENTER SCHEDULE

UNIT NO	LOCATION	SYSTEM SERVED	TYPE	SIZE	DESIGN FLOW (GPM)	MAX WPD @ DESIGN (PSI)	MAX RELIEF FLOW RATE @ 55 PSI (GPM)	BASIS OF DESIGN	NOTES
BFP-1	INSPECTION 112	BUILDING WATER SERVICE	RPZ	2"	88	14	150	WATTS LP 009 QTS	1
BFP-2	MECH 115	HEATING WATER MAKE-UP	RPZ	1"	15	12	50	WATTS LP 009 QTS	1

- NOTES:
- PROVIDE WITH BALL TYPE ISOLATION VALVES AND AIR GAP FITTING FOR DRAIN.

ELECTRIC WATER HEATER SCHEDULE

UNIT NO	LOCATION	STORAGE GALLONS	CW INLET TEMP °F	HW OUTLET TEMP °F	MIN GPH RECOVERY @95°ΔT	WATTAGE PER ELEMENT	NUMBER OF ELEMENTS	TOTAL INPUT KW	VOLTS / PHASE	BASIS OF DESIGN	NOTES
EW-1	CUSTODIAL M106	119	45	140	95	6000	2	12.0	460 / 3	LOCHINVAR CHPA120PD	
EW-2	SHOP 111	20	45	140	95	2000	1	2.0	120 / 1	RHEEM XE20	
EW-3	OPEN OFF 2ND FLOOR	2.5	45	120		1440	1	1.44	120 / 1	RHEEM XE02	

- NOTES:
-

MIXING VALVE SCHEDULE

UNIT NO	LOCATION	SERVES	INLET	OUTLET	SUPPLY TEMP °F	DESIGN GPM	MIN GPM	PRESSURE DROP (PSIG)	BASIS OF DESIGN	NOTES
TMV-1	MECH M106	DOMESTIC HOT WATER	3/4"	1"	120°	20	1.0	15.0	LEONARD XL32A-LF	1, 2
TMV-2	SHOP 111	DOMESTIC HOT WATER	1/2"	1/2"	120°	3	0.3	5.0	LEONARD 170-LF-STSTL EXP	3
EMV-1	SHOP 111	EYEWASH-SHIP 111	1/2"	1/2"	78°	3		5.0	GUARDIAN G6020	
EMV-2	SHOP 207	EYEWASH-SHOP 207	1/2"	1/2"	78°	3		5.0	GUARDIAN G6020	

- NOTES:
- PROVIDE VALVE IN MANUFACTURER'S LOCKABLE, PAINTABLE STEEL CABINET.
 - PROVIDE HIGH-LOW DUAL MIXING VALVE ASSEMBLY WITH INTEGRAL MANUFACTURER'S OUTLET THERMOMETER.
 - PROVIDE VALVE IN MANUFACTURER'S RECESSED LOCKABLE, PAINTABLE STEEL CABINET.
 - PROVIDE VALVE IN MANUFACTURER'S SURFACE MOUNTED, LOCKABLE, PAINTABLE STEEL CABINET.

EXPANSION TANK SCHEDULE

UNIT NO	LOCATION	SERVES	MIN TANK VOLUME (GAL)	ACCEPTANCE VOLUME	DIMENSIONS (IN)	BASIS OF DESIGN	NOTES
EXT-P1	MECH M106	DOMESTIC WATER	6.4	3.2	12ø x 18	AMTROL ST-12C-DD	1
EXT-P2	SHOP 111	DOMESTIC WATER	1.4	0.35	8ø x 13	AMTROL ST-5	

- NOTES:
- PROVIDE DIAPHRAGM TANK LISTED FOR USE WITH POTABLE WATER.

AUTOMATIC TRAP PRIMER ASSEMBLY SCHEDULE

UNIT NO	LOCATION	MOUNTING	NO OF MANIFOLD OPENINGS	NO OF DESIGN CONNECTIONS	CONN SIZE	VOLTS / PHASE	BASIS OF DESIGN	NOTES
TPA-1	CUSTODIAL 107	RECESSED	4	3	1/2"	120 / 1	PRECISION PLUMBING PRODUCTS PT-4	1, 2
TPA-2	INSPECTION 112	RECESSED	4	1	1/2"	120 / 1	PRECISION PLUMBING PRODUCTS PT-4	1, 2
TPA-3	MECH 115	RECESSED	4	1	1/2"	120 / 1	PRECISION PLUMBING PRODUCTS PT-4	1, 2
TPA-4	FIRE PUMP M107	RECESSED	4	1	1/2"	120 / 1	PRECISION PLUMBING PRODUCTS PT-4	1, 2
TPA-5	MECH M106	RECESSED	4	1	1/2"	120 / 1	PRECISION PLUMBING PRODUCTS PT-4	1, 2
TPA-6	MECH MEZZ M107	RECESSED	4	1	1/2"	120 / 1	PRECISION PLUMBING PRODUCTS PT-4	1, 2
TPA-7	WOMEN 203	RECESSED	4	1	1/2"	120 / 1	PRECISION PLUMBING PRODUCTS PT-4	1, 2
TPA-8	MEZZANINE M201	RECESSED	4	1	1/2"	120 / 1	PRECISION PLUMBING PRODUCTS PT-4	1, 2

- NOTES:
- CAP UNUSED OUTLETS.
 - PROVIDE WITH MANUFACTURER'S LOCKABLE, PAINTABLE STEEL PANEL ACCESS DOOR.

DRAIN SCHEDULE

UNIT NO	TYPE	DESCRIPTION	PIPE SIZE	STRAINER DIMENSIONS	BASIS OF DESIGN	NOTES
FD-1	FLOOR DRAIN	SQUARE DRAIN FOR FINISHED SPACES	2"	6" x 6"	ZURN EZ-PV2-S6	1, 3
FD-2	FLOOR DRAIN	ROUND DRAIN FOR UNFINISHED SPACES W/ FUNNEL	3"	7ø	ZURN Z415E	1, 2
FD-3	FLOOR DRAIN	ROUND DRAIN FOR UNFINISHED SPACES W/ FUNNEL	4"	7ø	ZURN Z415E	1, 2
FS-1	FLOOR SINK	1/2" GRATE, 6" DEEP	4"	6" x 6"	ZURN	1, 2


- NOTES:
- PROVIDE TRAP PRIMER CONNECTION TO FLOOR DRAIN OR FLOOR SINK.
 - PROVIDE WITH SEDIMENT BUCKET.
 - PROVIDE WITH CHROME PLATED FINISH.

RADON FAN SCHEDULE (OPTION 3)

UNIT NO	SERVES	CFM	ESP IN WC	DRIVE TYPE	FAN TYPE	FAN RPM	WATTS	VOLTS / PHASE	BASIS OF DESIGN	NOTES	ACCESSORIES
RF-1	RADON MITIGATION	200	2	DIRECT	IN-LINE	4099	175	120 / 1	FANTECH 4EC-4	1, 2	A, B, C

- NOTES:
- PROVIDE UNDER OPTION 3 ONLY
 - TYPICAL FOR 3 FANS
 - FOR DDC SYSTEM FAN MONITORING AND ALARM CONTROL POINTS, SEE C2/M-705.

- ACCESSORIES:
- MFR INTEGRAL FAN SPEED CONTROLLER.
 - MFR ANTI-VIBRATION COUPLERS FOR 4" PVC PIPE.
 - WALL MOUNTING BRACKET FOR VERTICAL INSTALLATION.

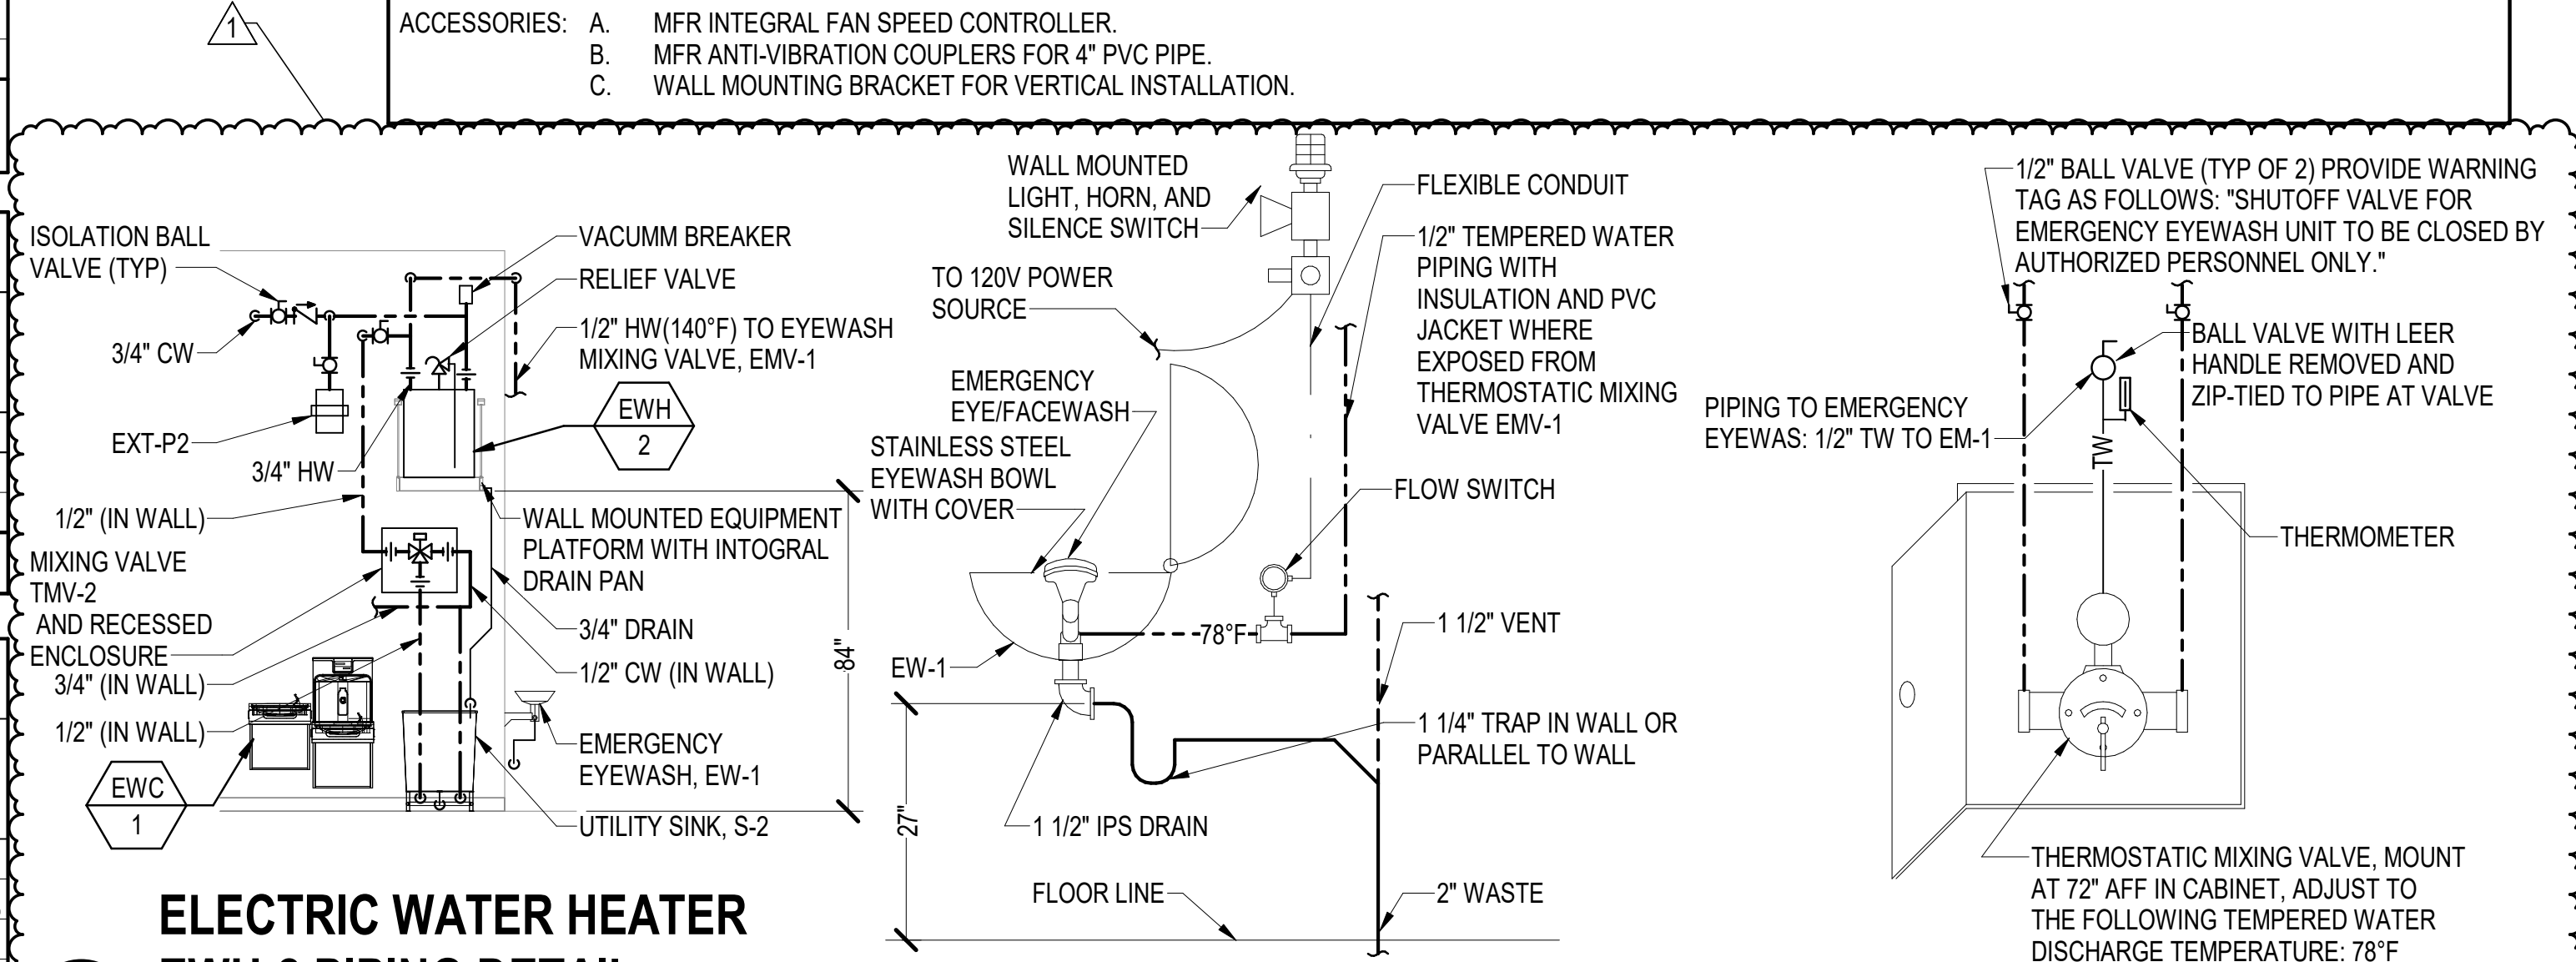

ELECTRIC WATER HEATER

EWH-2 PIPING DETAIL

SCALE: NOT TO SCALE

EMERGENCY EYEWASH DETAIL

SCALE: NTS

TYPICAL EMERGENCY TEMPERED

WATER MIXING VALVE(EMV-) DETAIL

SCALE: NTS