



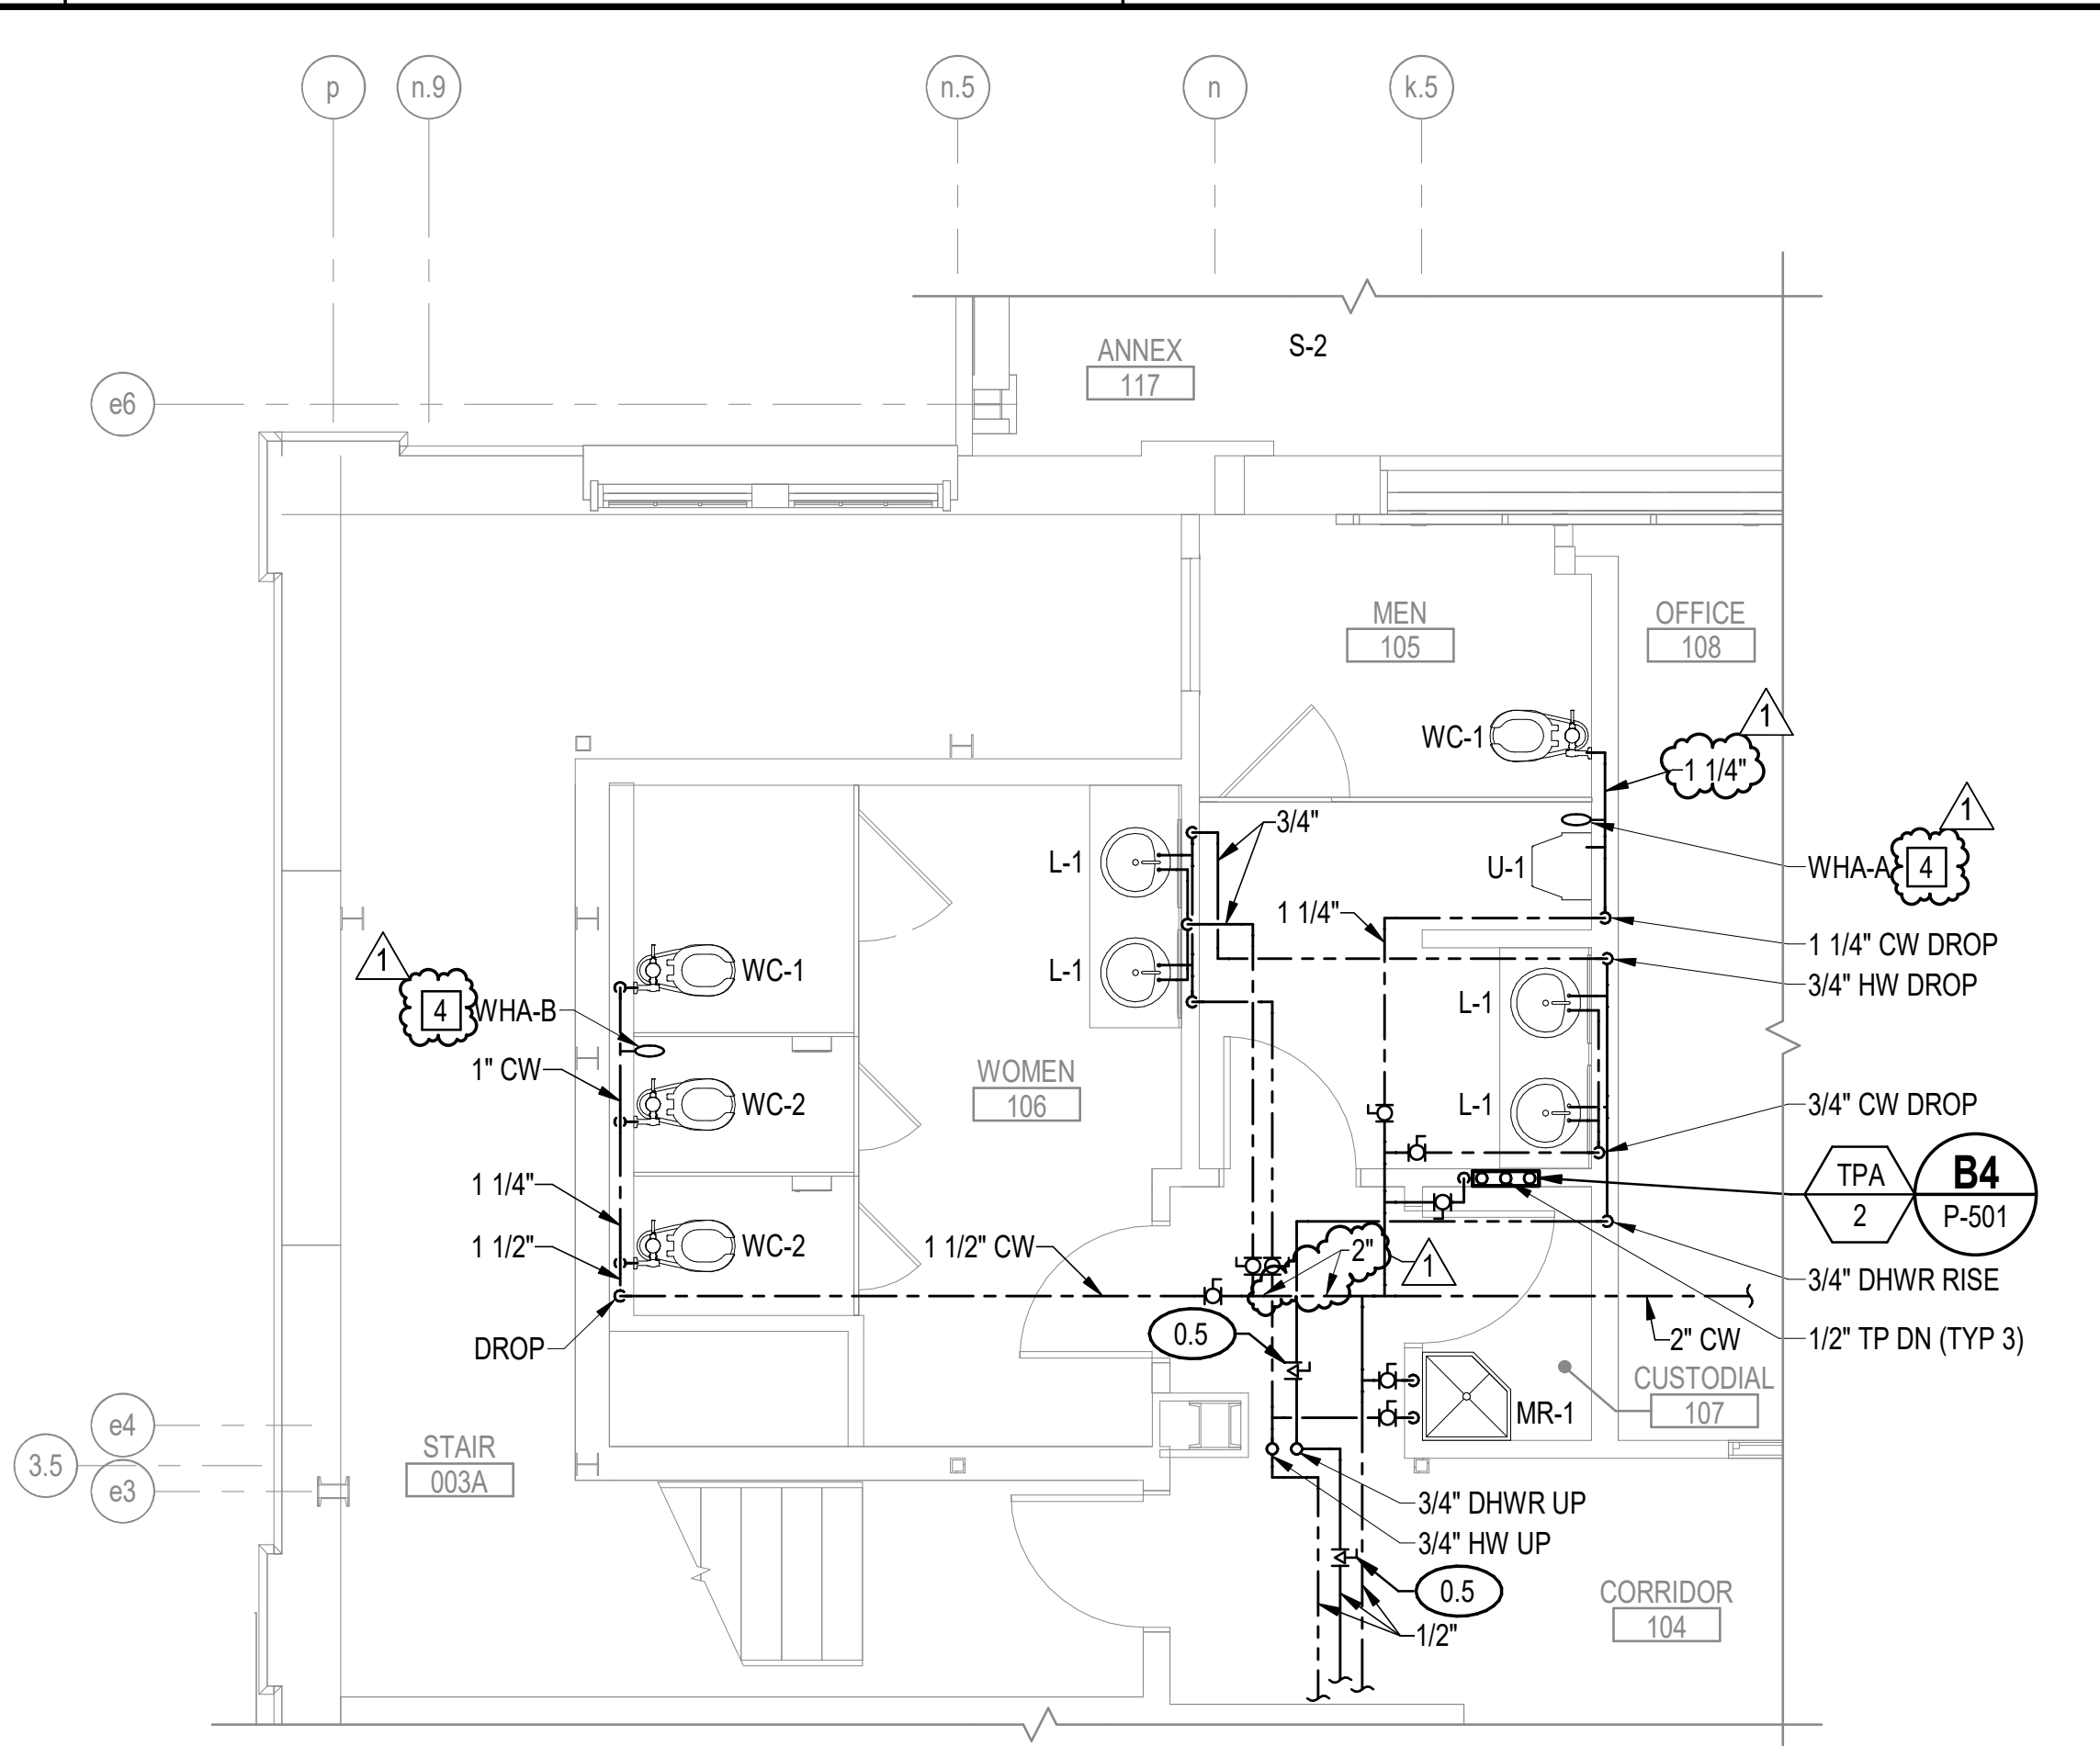

C3 ENLARGED FIRST FLOOR DOMESTIC WATER SUPPLY PART PLAN
SCALE: 1/4" = 1'-0" (P-104)

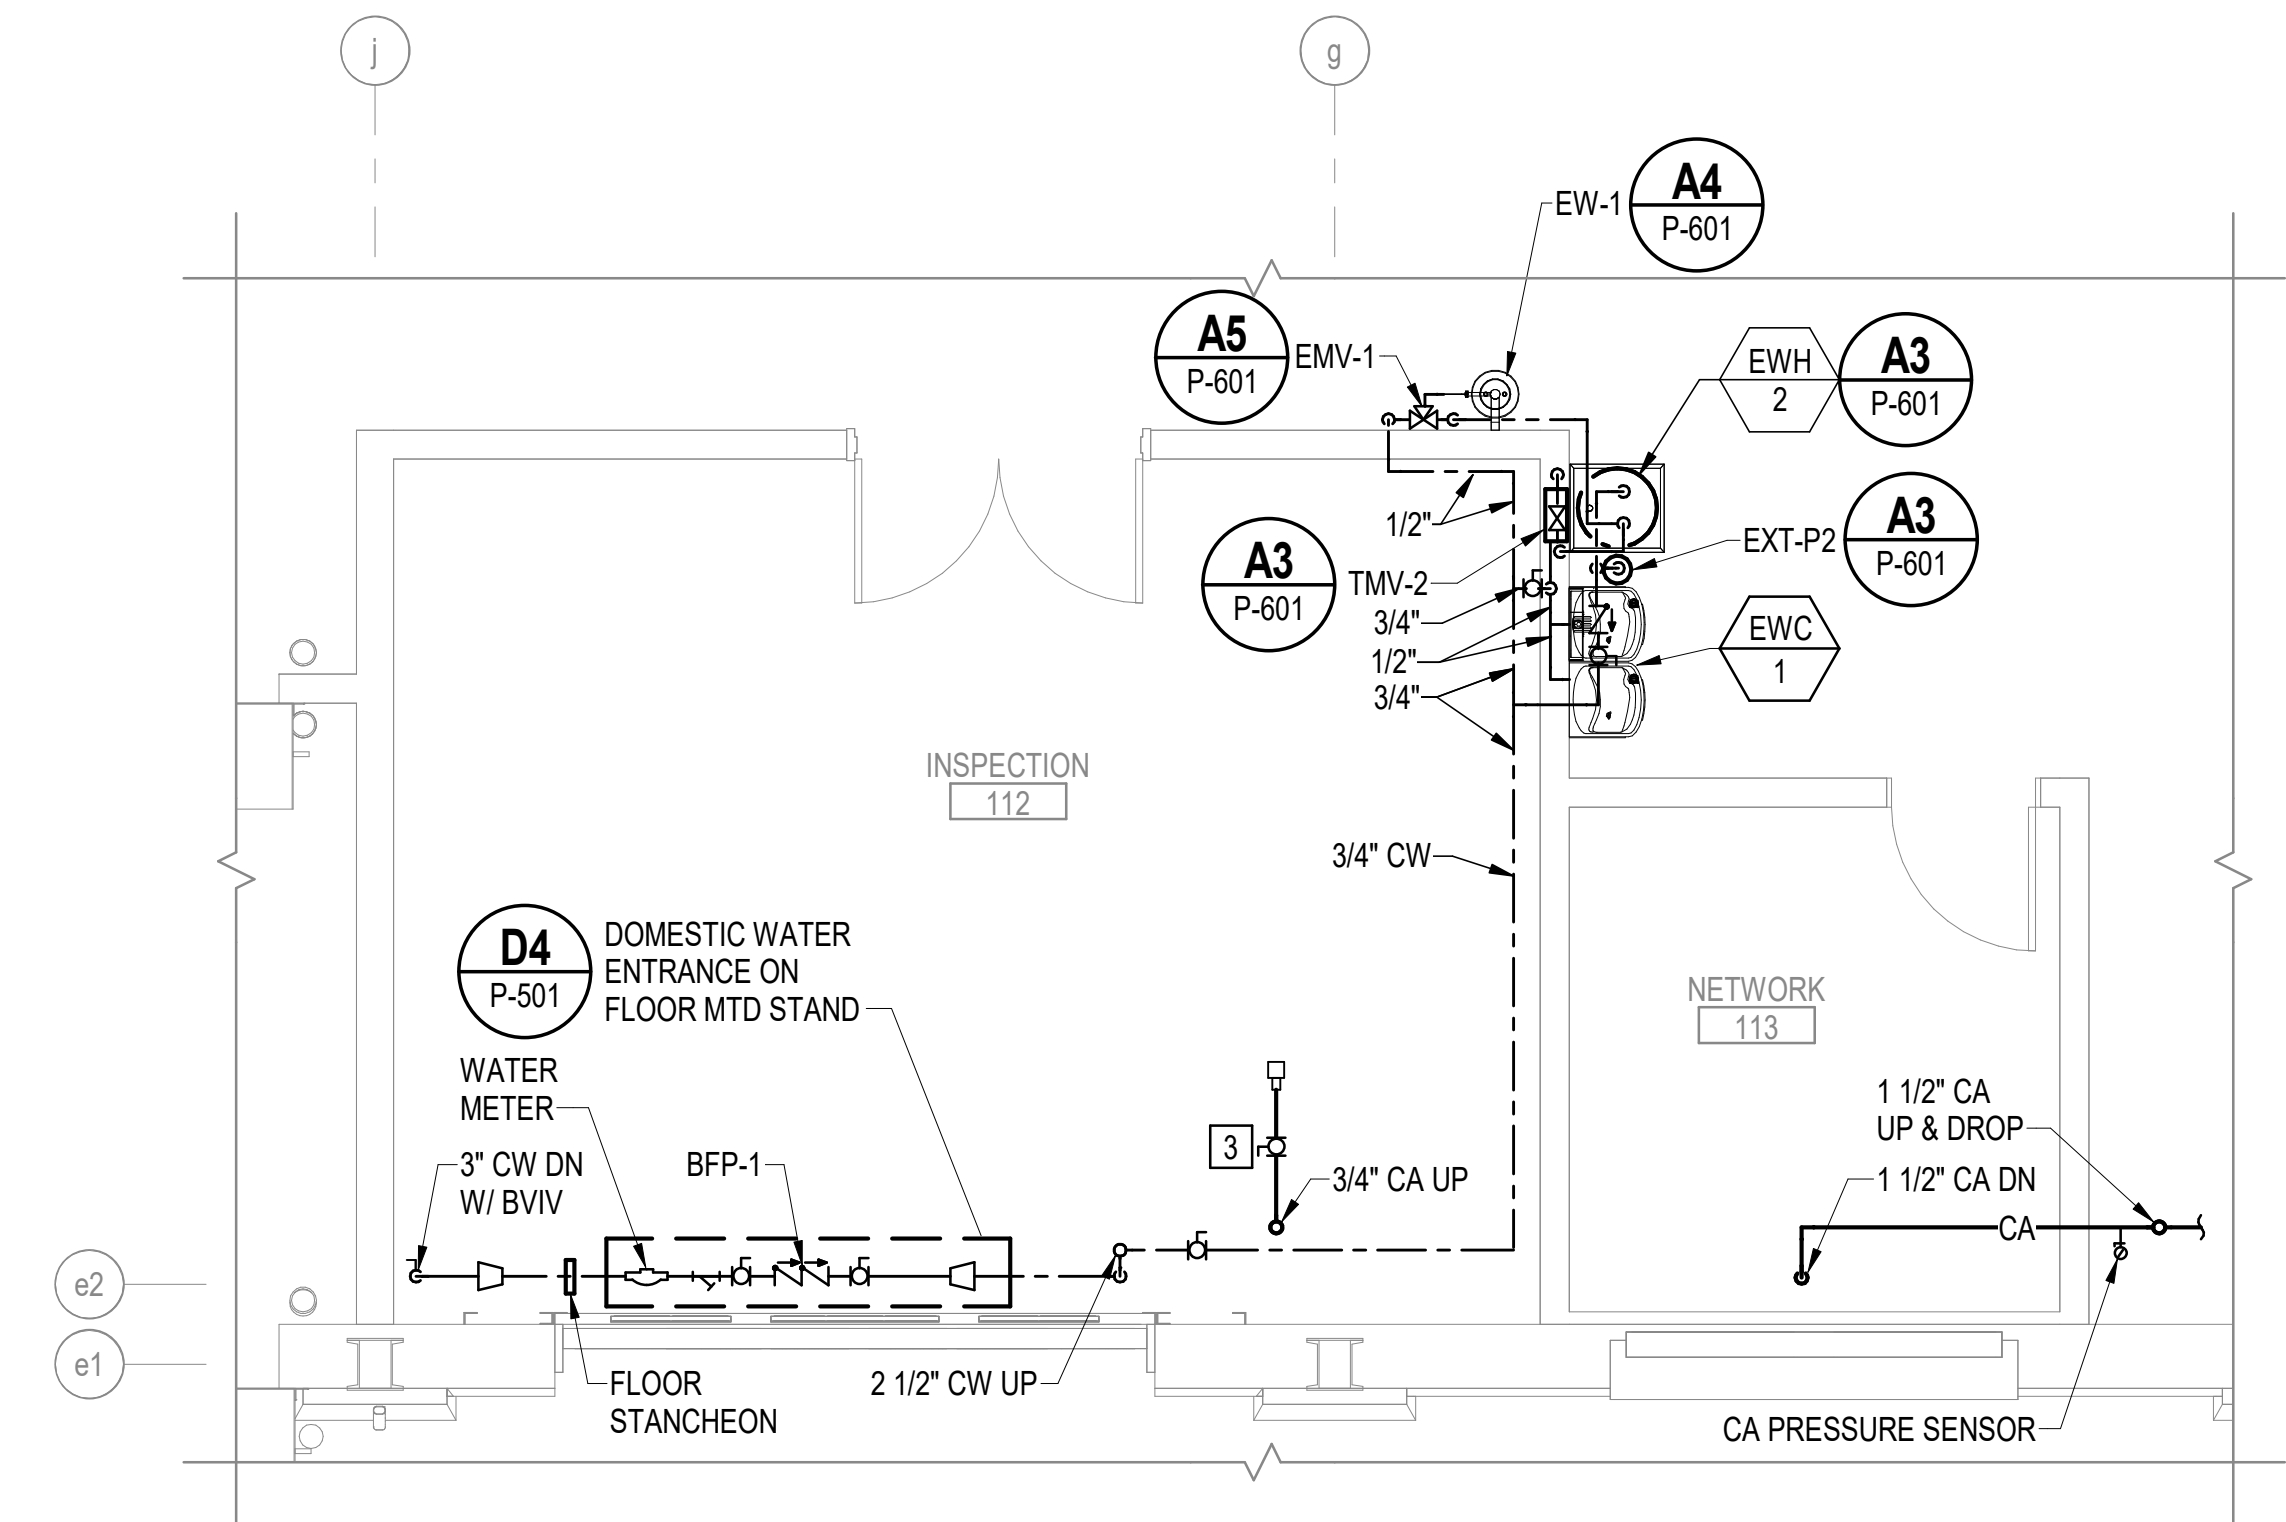


A3 ENLARGED FIRST FLOOR DOMESTIC WATER SUPPLY PART PLAN
SCALE: 1/4" = 1'-0" (P-104)

KEYNOTES (THIS SHEET ONLY)

- 1 PIPE 3/4" DRAIN DOWN TO SINK S-2. SECURE TO WALL.
- 2 2" INDIRECT WASTE DRAIN TRAP WITH AIR GAP FITTING. PIPE DRAIN FROM BFP-1 AND CONDENSATE DRAINS FROM BCU-1 AND IU-2 TO AIR GAP FITTING.
- 3 PROVIDE 1/2" CA WITH ISOLATION BALL VALVE AND QUICK CONNECT FEMALE HOSE CONNECTION FITTING 80" AFF. COORDINATE QUICK CONNECT FITTING SELECTION WITH CONTRACTING OFFICER.
- 4 PROVIDE 8"x8" WALL MOUNTED WATER HAMMER ARRESTOR SERVICE ACCESS DOOR.

C1

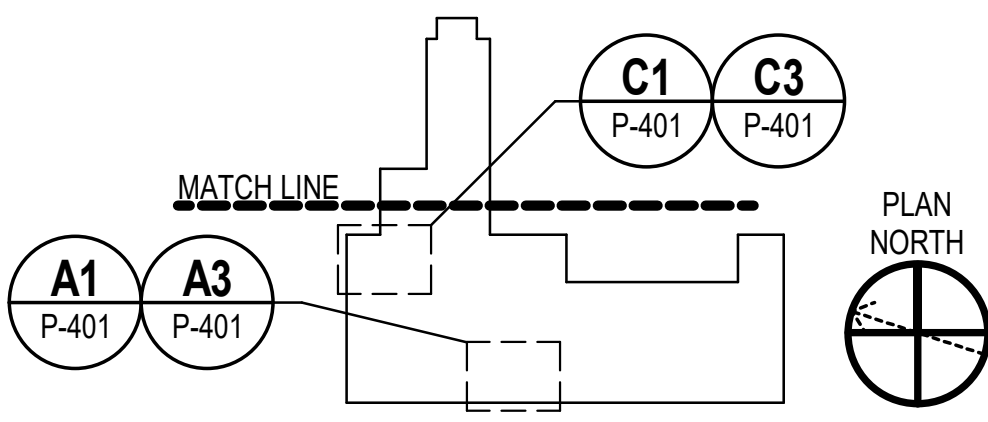

0 1' 5' 10' 15'

$1/4" = 1' - 0"$

CHECK GRAPHIC SCALE BEFORE USING

[illegible]