


3/20/2026 1:29:33 PM P-403
C:\Users\richards\Documents\22103.25_BLDG60_MECHANICAL-V23_swhic82ZD.rvt

D


C

B

A

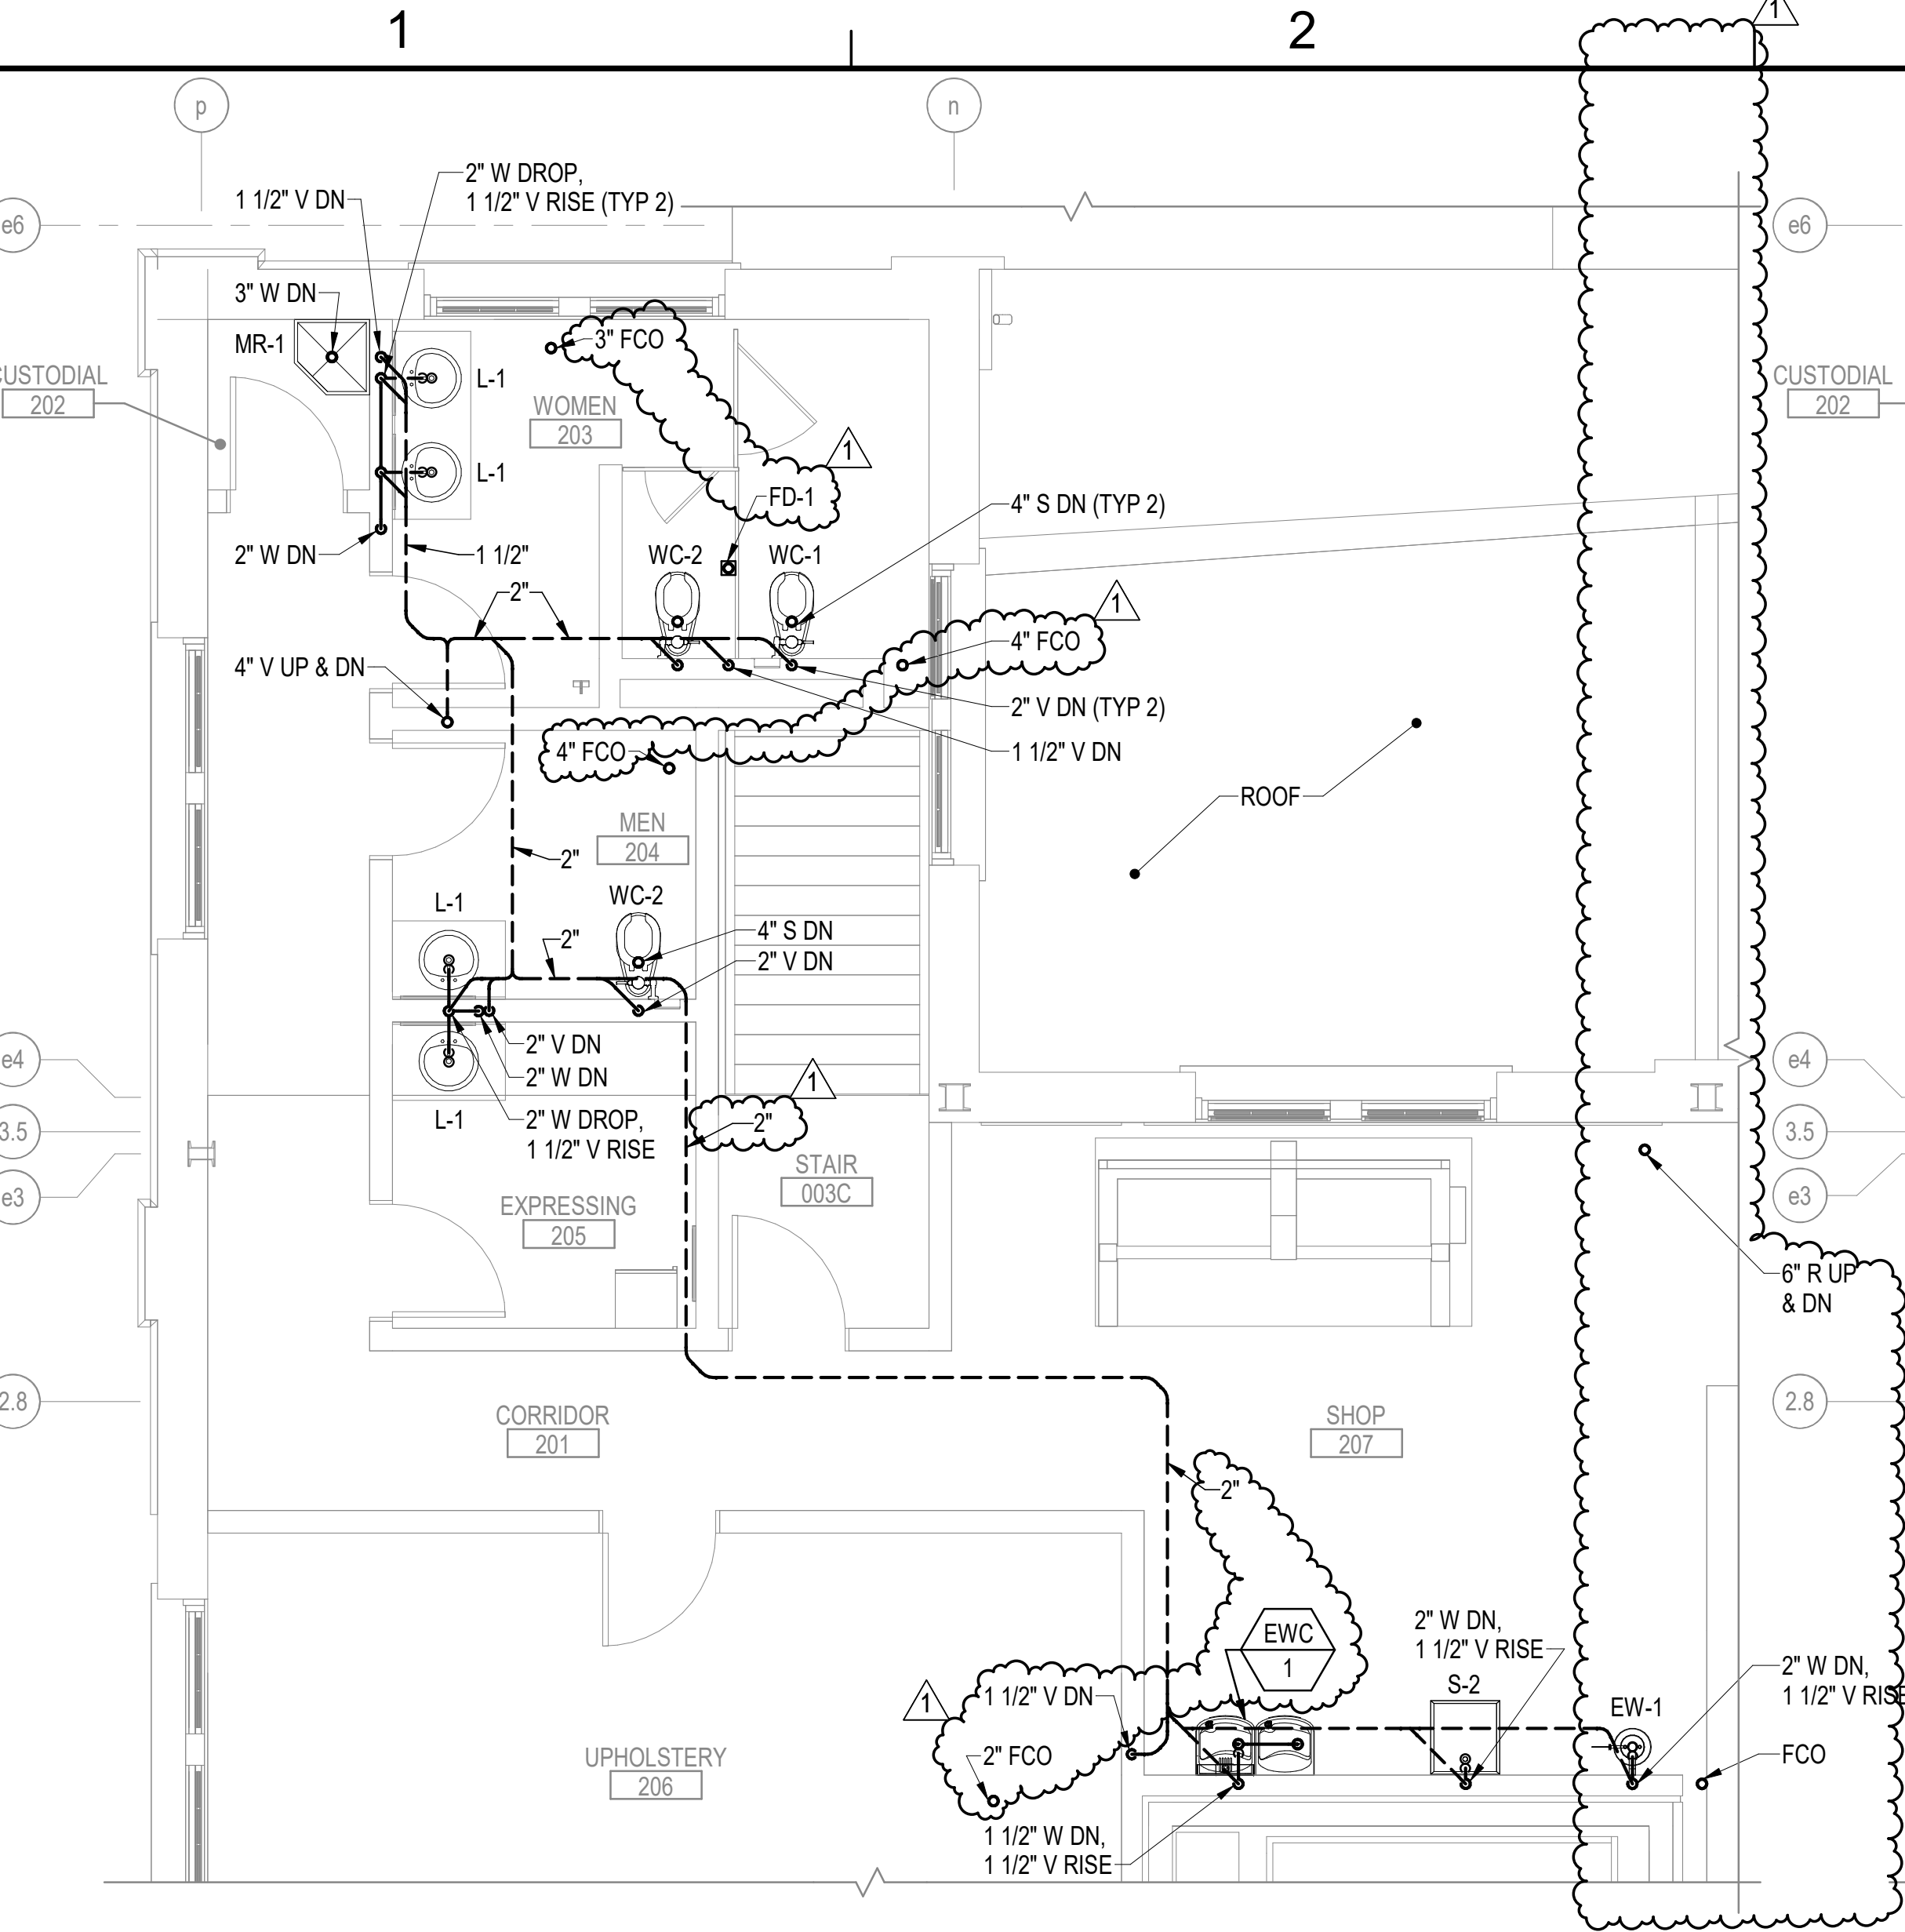

B1 ENLARGED SECOND FLOOR SANITARY WASTE AND VENT PART PLAN
SCALE: 1/4" = 1'-0" (P-107)

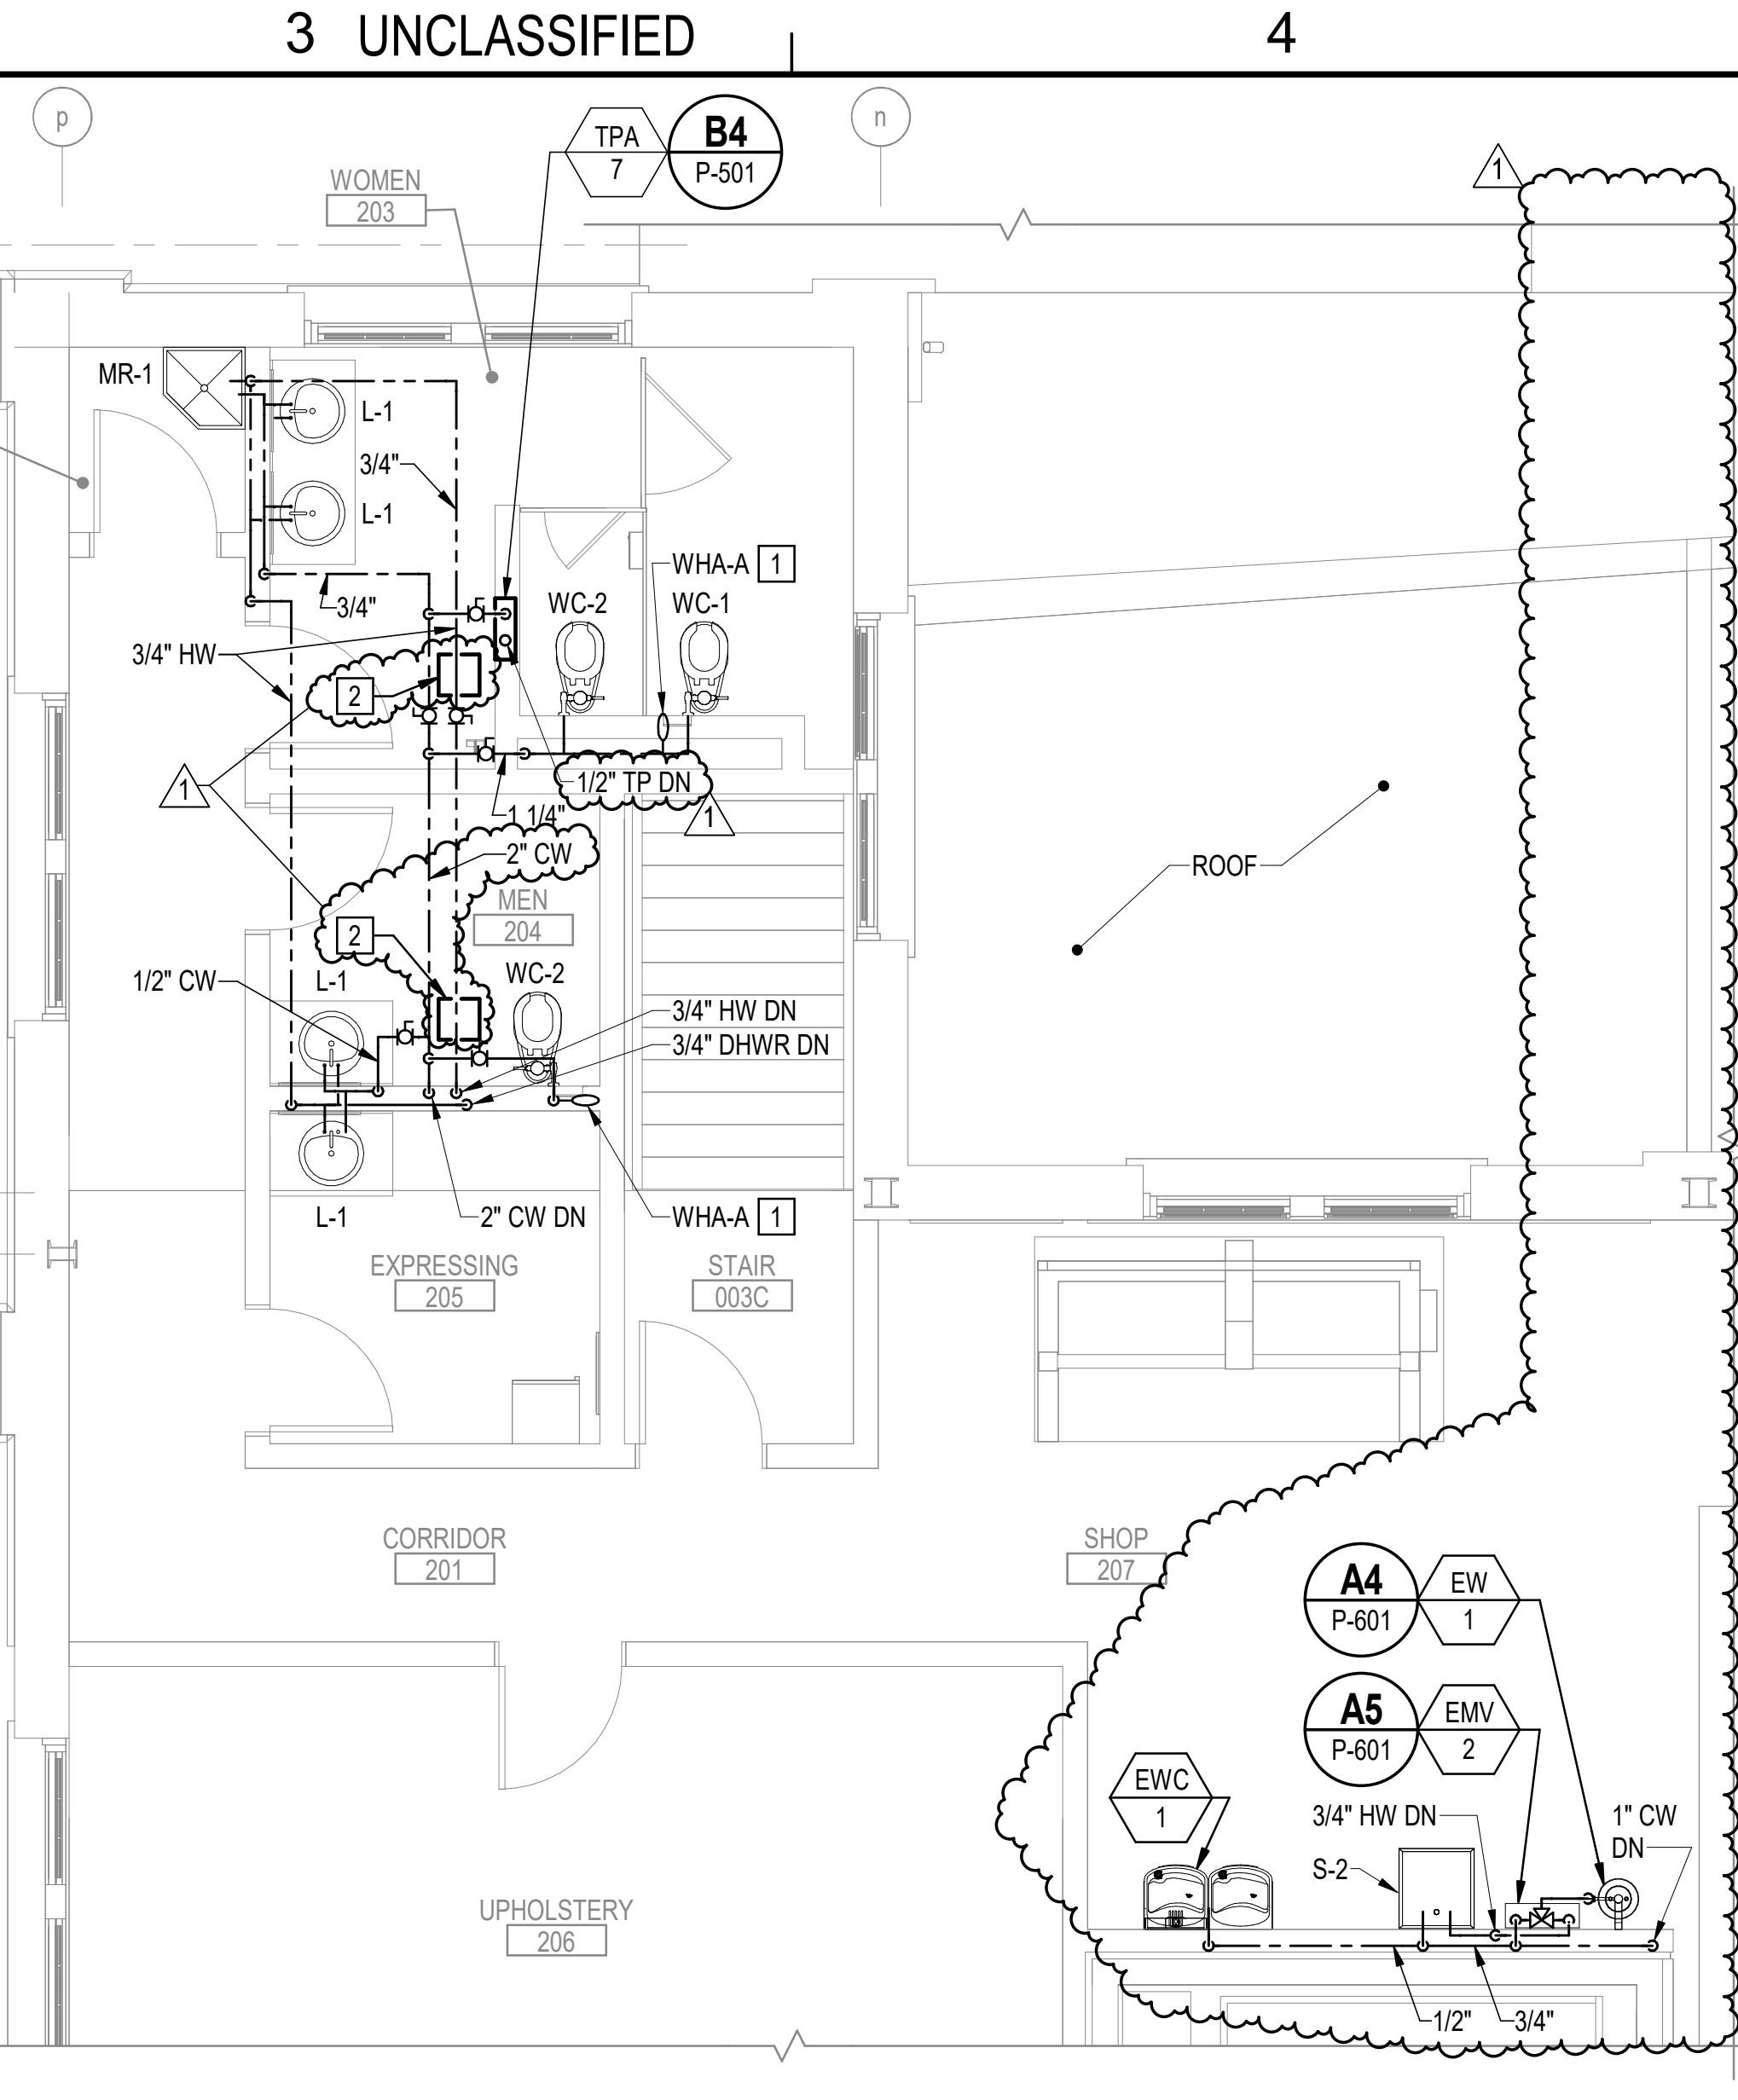

B3 ENLARGED SECOND FLOOR DOMESTIC WATER SUPPLY PART PLAN
SCALE: 1/4" = 1'-0" (P-107)

3 UNCLASSIFIED

3 UNCLASSIFIED


GENERAL NOTES

- SEE P-001 FOR PLUMBING LEGENDS, ABBREVIATIONS AND GENERAL NOTES.
- COORDINATE THE INSTALLATION OF PIPING AND EQUIPMENT TO MAINTAIN MANDATORY CLEARANCE ZONES AROUND CRANE RAILS AND BRIDGE CRANE OPERATIONAL TRAVEL PATH.


KEYNOTES (THIS SHEET ONLY)

- PROVIDE 8"x8" WALL MOUNTED WATER HAMMER ARRESTOR SERVICE ACCESS DOOR.
- PROVIDE 12"x12" ACCESS PANEL. COORDINATE PLACEMENT OF PANEL AND ISOLATION VALVES TO ENSURE SERVICE ACCESS.


KEY PLAN

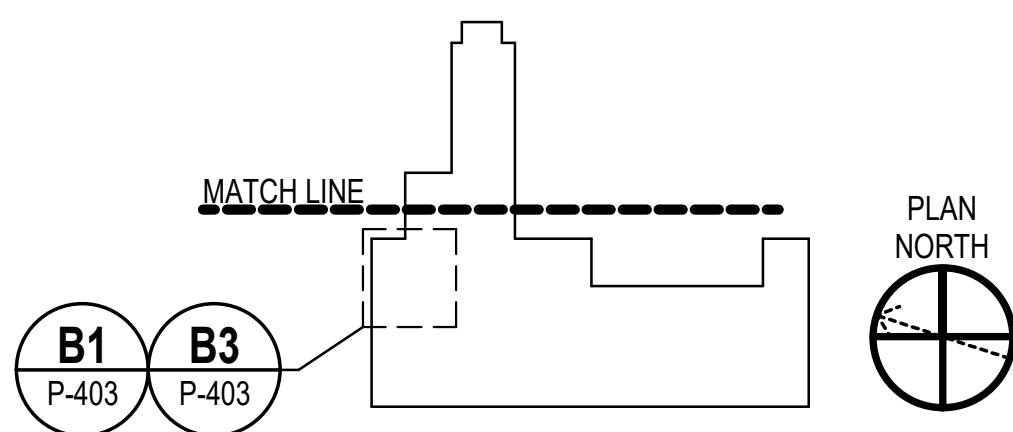

GRAPHIC SCALE

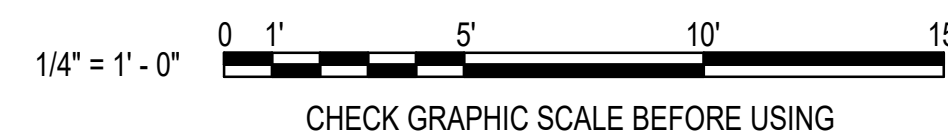

--	--	

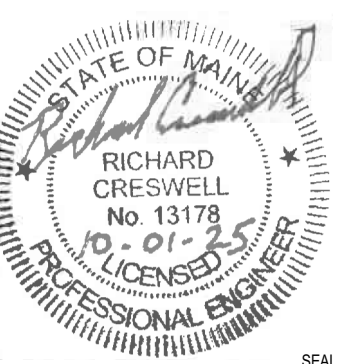

FOR COMMANDER NAVFAC
ACTIVITY
SATISFACTORY TO DATE
DESIGNER RNC
DRAWN BY SRW
CHECKED BY MSA
DESIGN MANAGER T. CARLETON
PROJECT MANAGER L. LYONS
HEADLINE
FIRE PROTECTION S. RUCINSKI

DEPARTMENT OF THE NAVY NAVAL FACILITIES ENGINEERING SYSTEMS COMMAND - MID-ATLANTIC PORTSMOUTH NAVAL SHIPYARD - KITTERY, ME	B60 REPAIRS ENLARGED PLUMBING PART PLANS 3
--	---

PROJECT NO. 1740579
NAVFAC DRAWINGS NO.
SHEET 180 OF 282
P-403

DRAWING REVISION: 14 SEP 2023

3 UNCLASSIFIED

A