


FILE NAME: P:\Projects\2024\21287-24020 NAVFAC Midant LP-38 Berm Recert\500-CAD\510-Arch\WD\A-DWG\1766588-G-001.dwg LAYOUT NAME: G-001 PLOTTED: Wednesday, February 11, 2026 - 9:07am USER: cmore


LP-38 BERM RECERTIFICATION REPAIR

NORFOLK NAVAL STATION
NORFOLK, VIRGINIA

OCTOBER 17, 2025

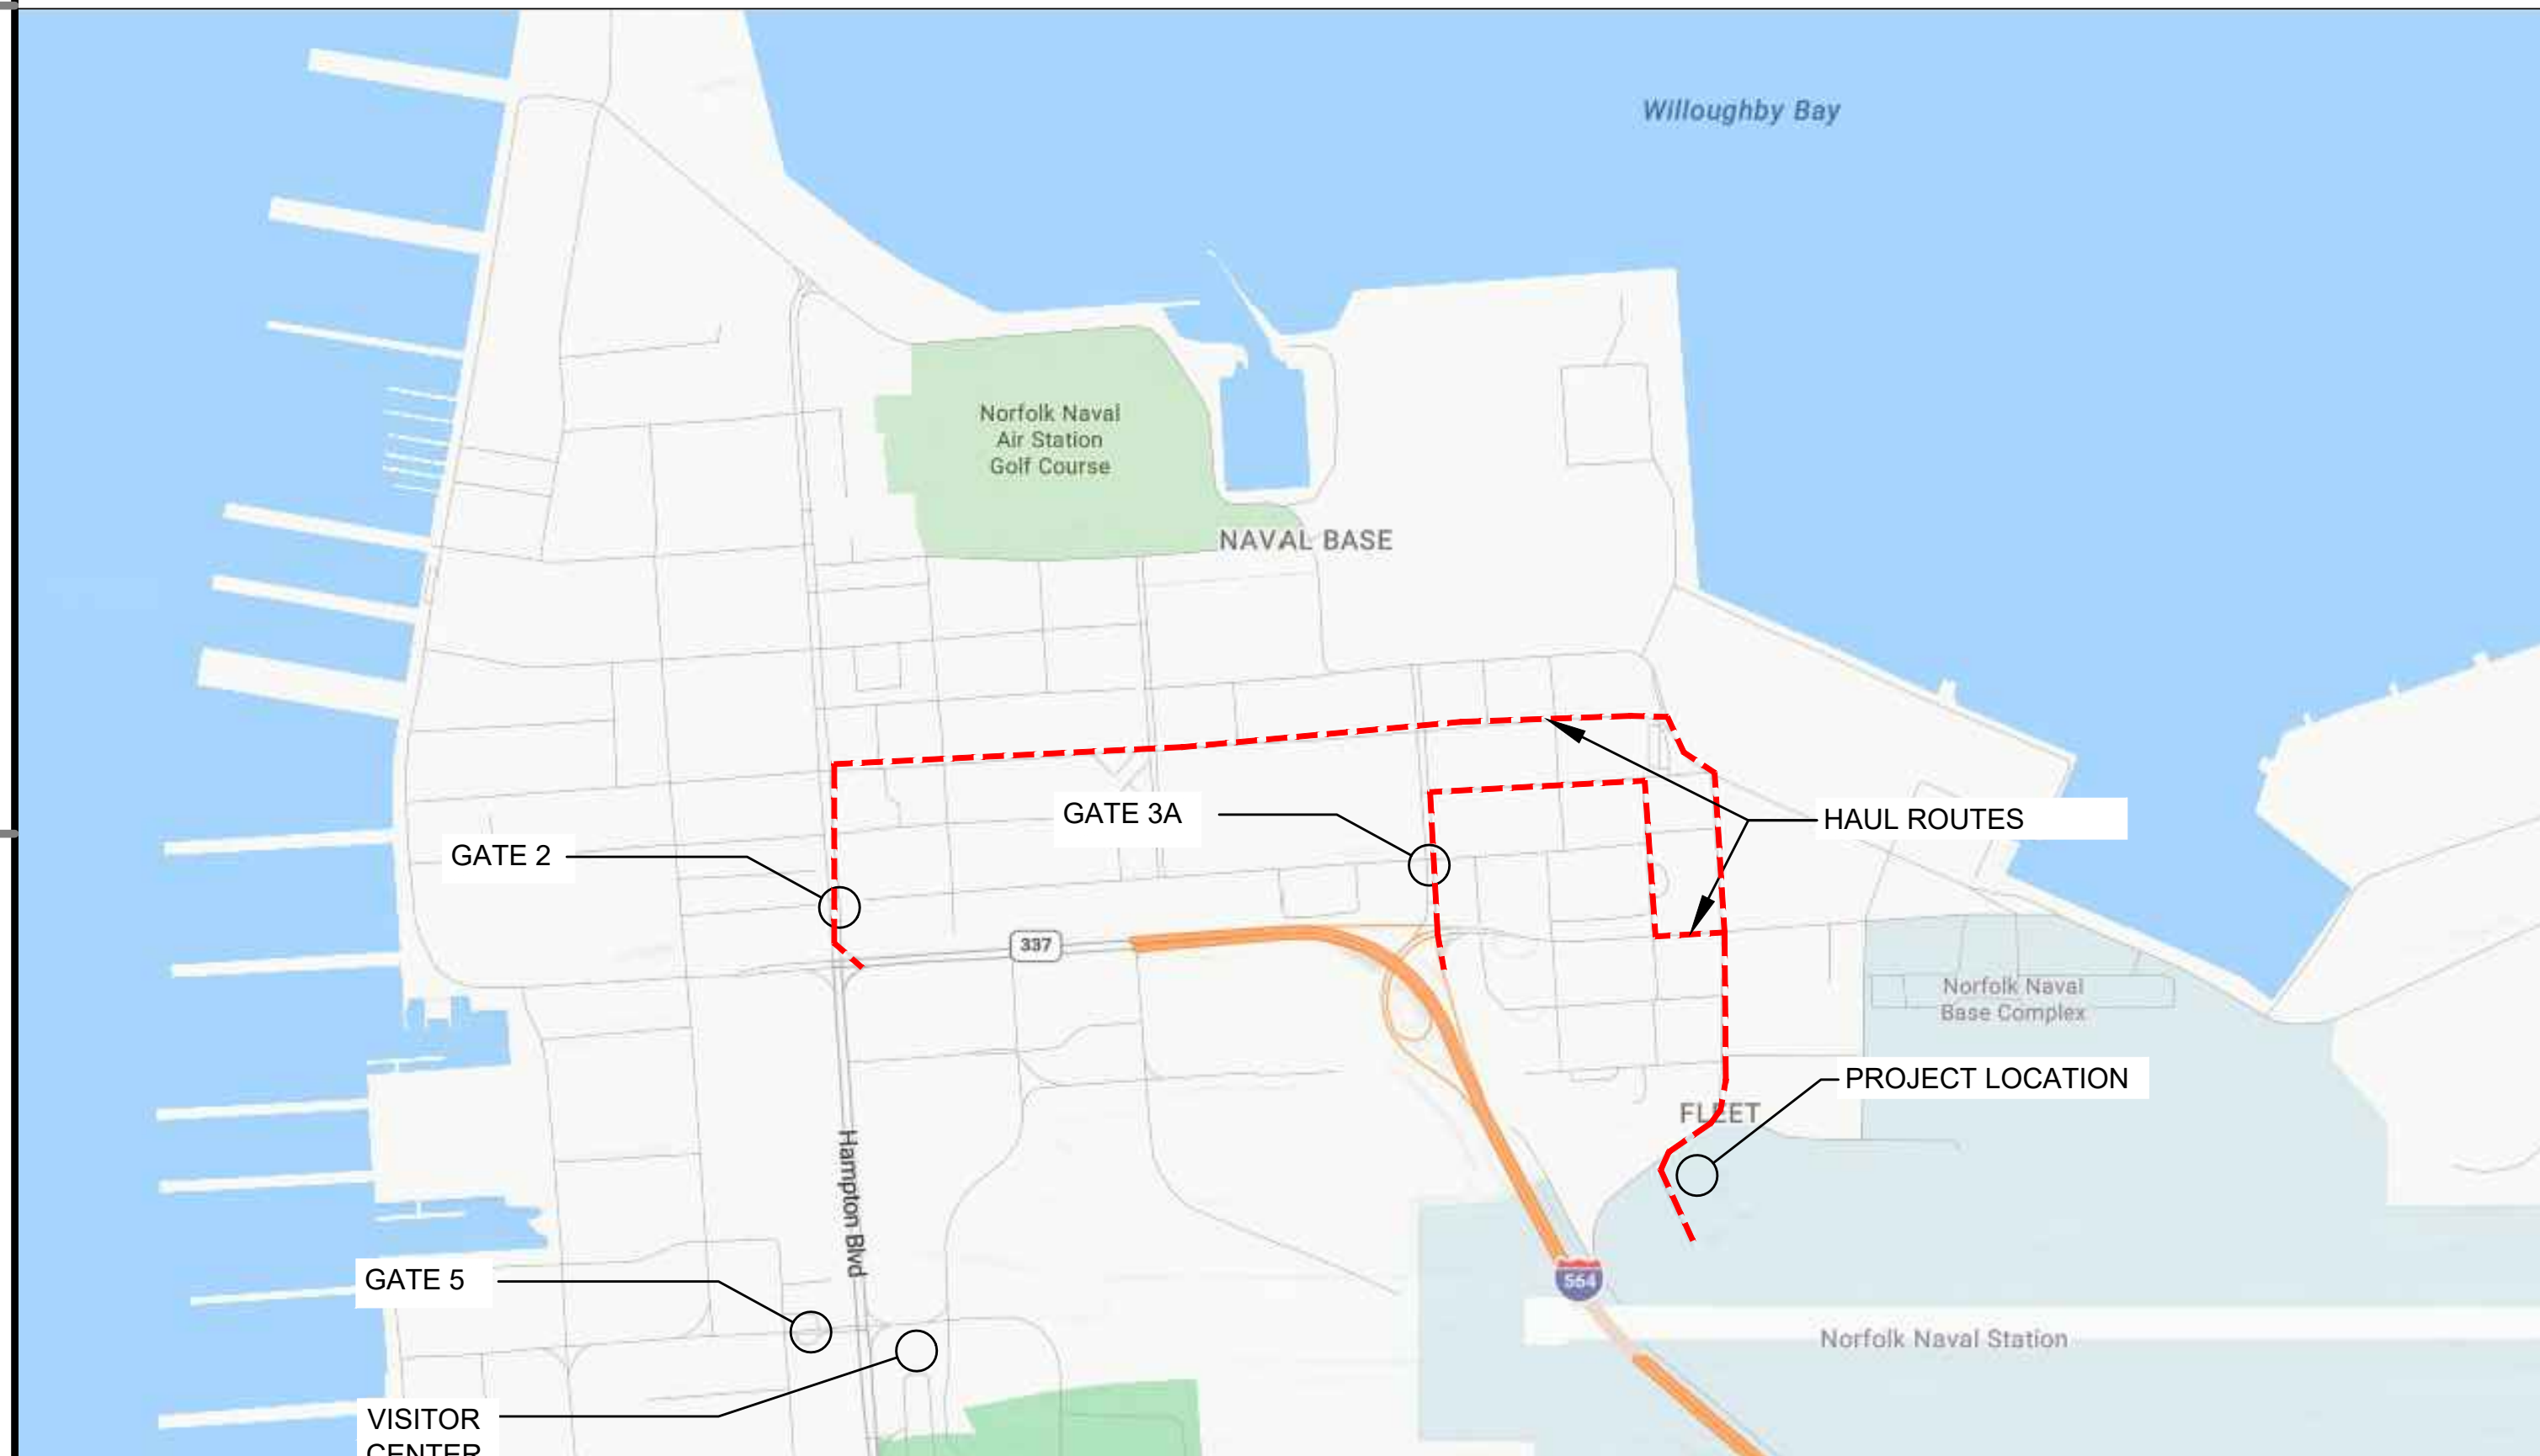


A1 VICINITY MAP
SCALE: NTS

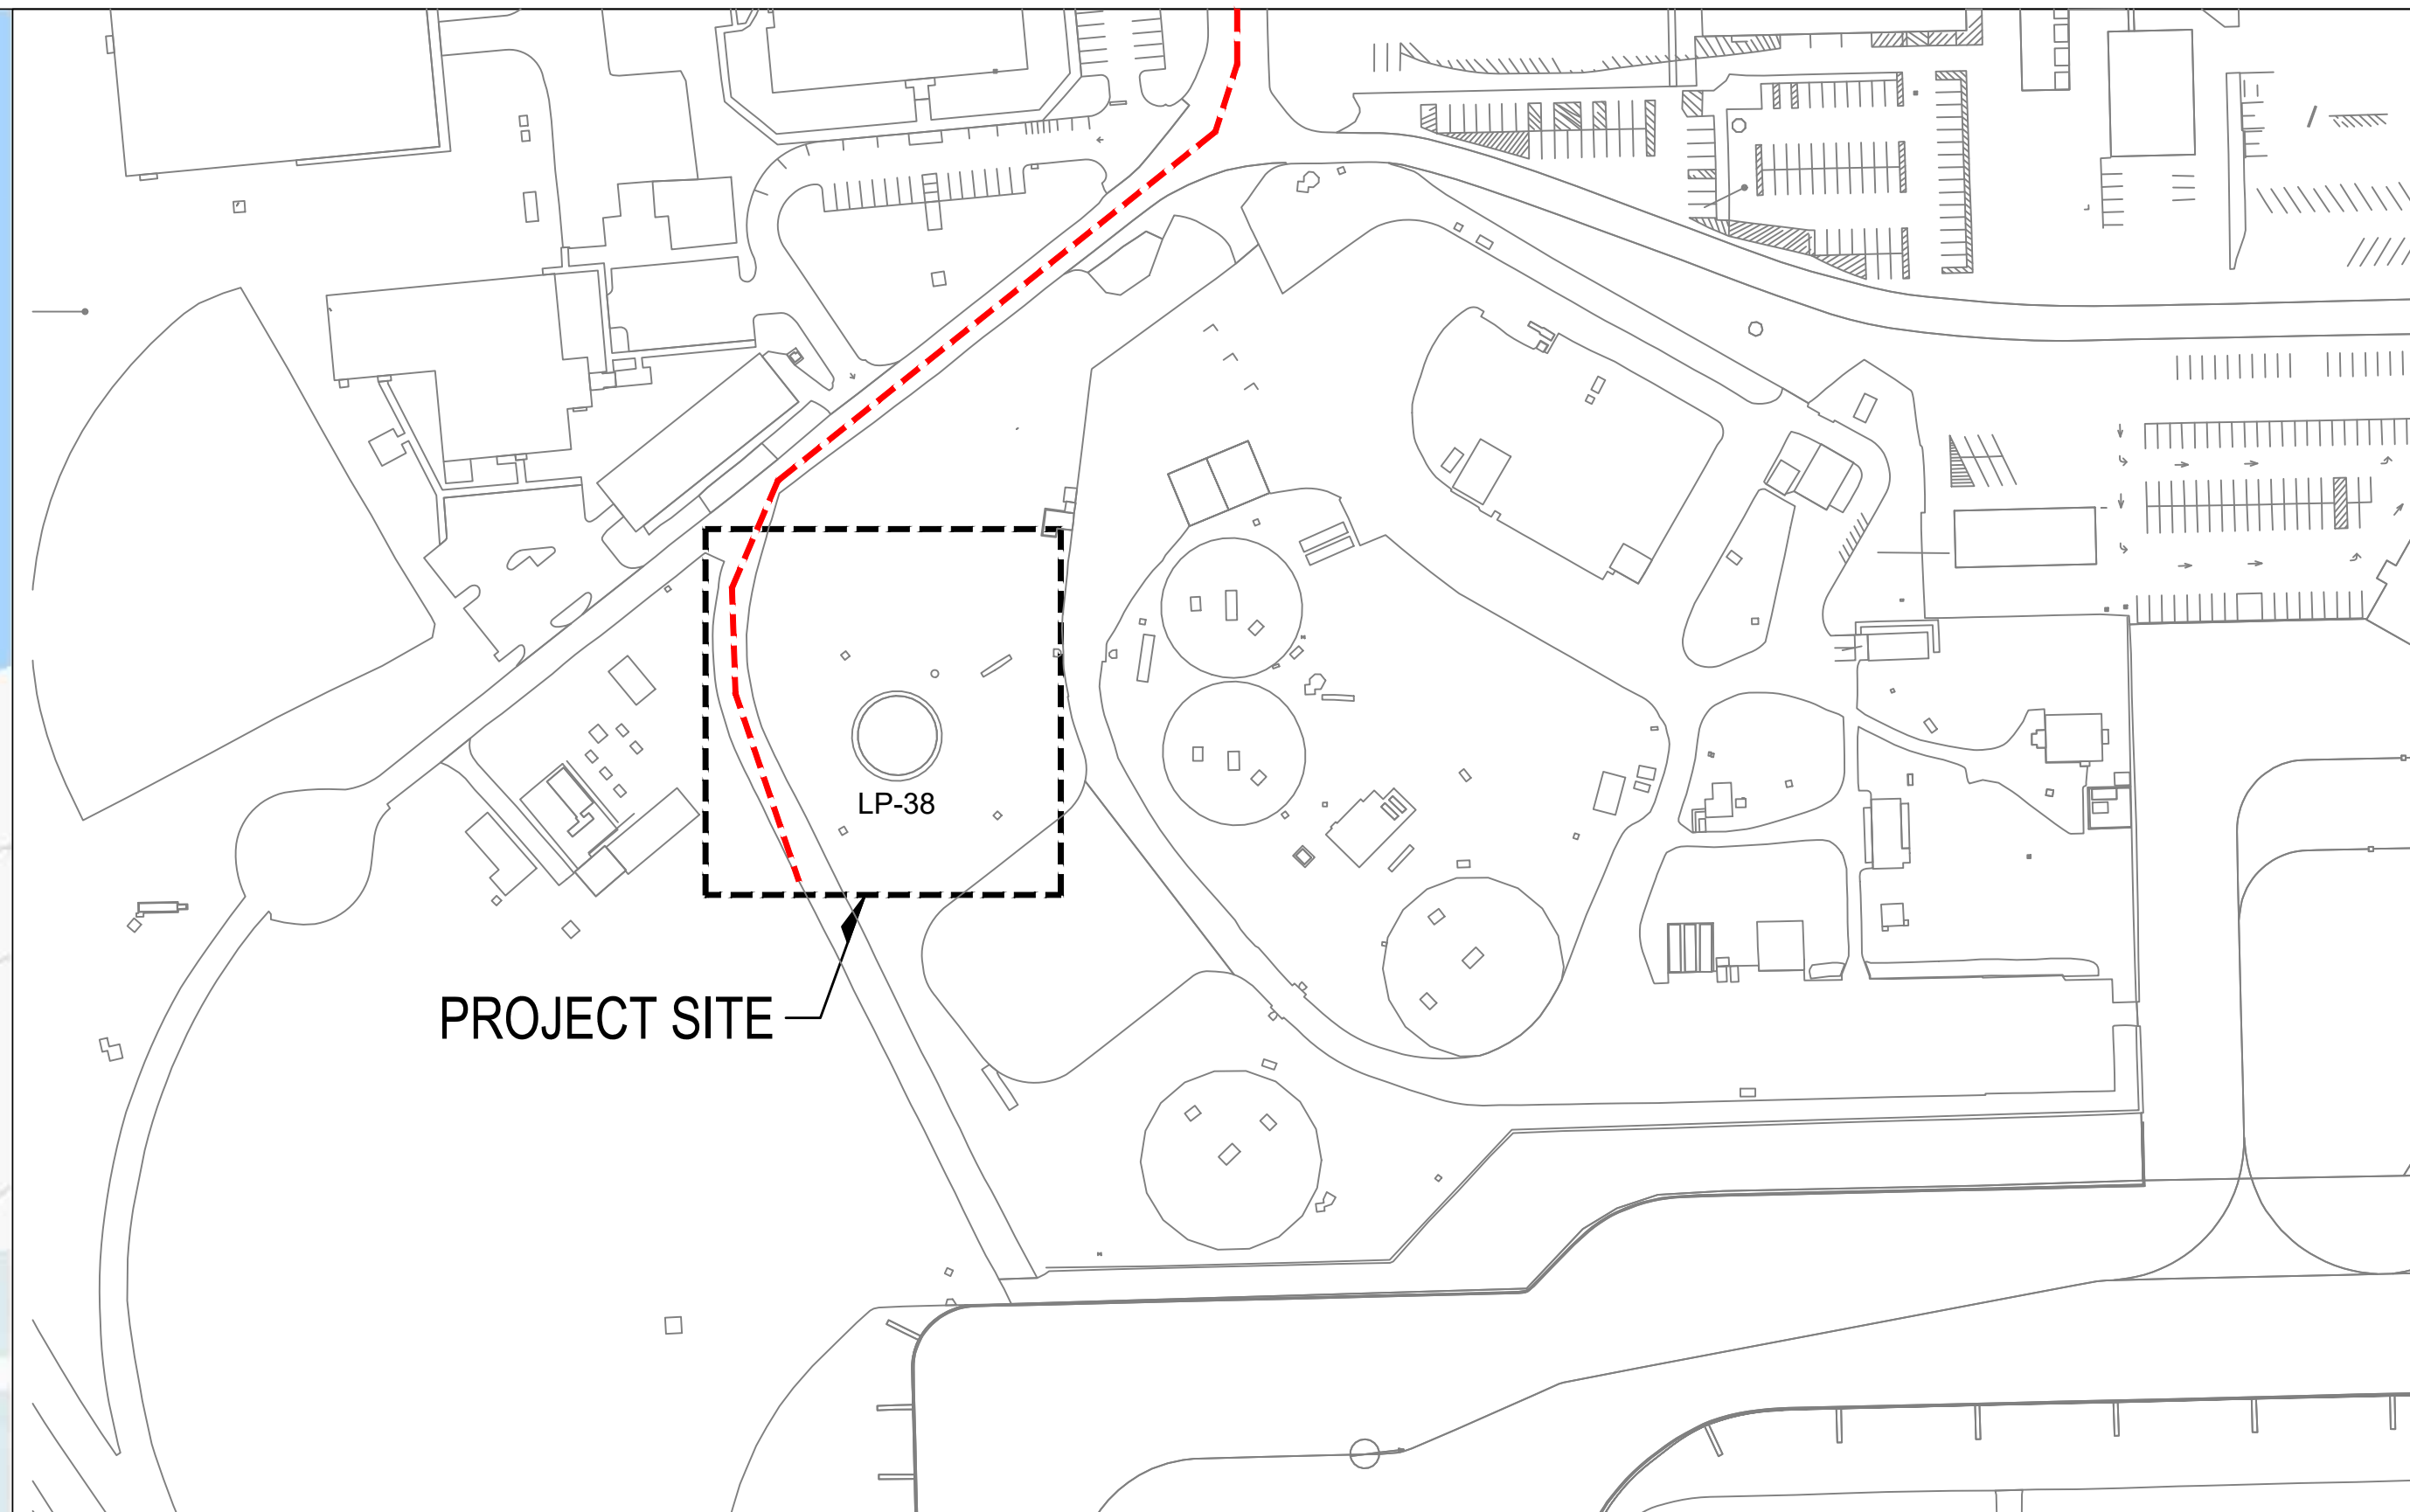

A3 LOCATION MAP
SCALE: NTS

1/26/26
DATE
FINAL SET
REVISION

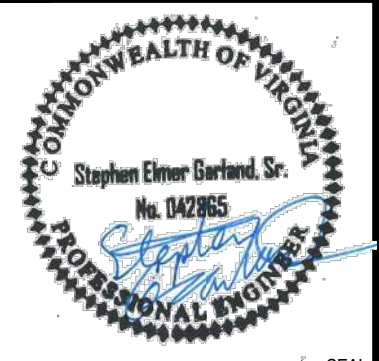

APPROVED
James M. Smith
FOR COMMANDER NAVFAC
ACTIVITY: BILL BOUNDS, CL

SATISFACTORY TO DATE: 14 JAN 2026					
DES	SG	DRW	SD	CHK	RB
PM/DM: W. WITHAM, P.E.					
BRANCH MANAGER: W. WITHAM, P.E.					
CHIEF ENG/ARCH: J. MILLER, P.E.					
FIRE PROTECTION: N/A					

DEPARTMENT OF THE NAVY
NAVAL FACILITIES ENGINEERING SYSTEMS COMMAND
NAVAL FACILITIES ENGINEERING SYSTEMS COMMAND - MID-ATLANTIC
MIDANT DC CORE
NAVAL STATION
NAVAL STATION - NORFOLK VA
NORFOLK, VIRGINIA

SCALE: AS SHOWN
PROJECT NO.: 1766588
CONSTR. CONTR. NO.: N40085-22-D-0039
NAVFAC DRAWING NO.: 12940905
SHEET 1 OF 19

G-001

FILE NAME: P:\Projects\2024\21297-24020 NAVFAC Midant LP-38 Berm Recert\510-040\510-Arch\WD\A-DWG\1766586-G-002.dwg LAYOUT NAME: G-002 PLOTTED: Wednesday, February 11, 2026 - 9:14am USER: cmnoore

D

C

B

A

ABBREVIATIONS

A/C	ANGLE	CS	CAST STONE	FR	FRAME
A/C UNIT	AIR CONDITIONING UNIT	CSK	COUNTERSUNK	FRG	FORGED
AB	ANCHOR BOLT	CSMT	CASEMENT	FRMG	FRAMING
ABV	ABOVE	CT	CERAMIC TILE	FRT	FIRE-RETARDANT
AC	ALTERNATING CURRENT	CT	CURRENT TRANSFORMER	FS	FULL SIZE
ACC	ACCESSIBLE	C TO C	CENTER TO CENTER	FSTNR	FASTENER(S)
ACI	AMERICAN CONCRETE INSTITUTE	CTR	CENTER	FT	FEET
ACR	ACRYLIC PLASTIC	CU	CONDENSING UNIT	FTG	FOOTING
ACS DR	ACCESS DOOR	Cu	COPPER	FURG	FURRING
ACS PNL	ACCESS PANEL	CU FT	CUBIC FEET	FUT	FUTURE
ACSR	ALUMINUM CABLE STEEL REINFORCED	CUH	CABINET UNIT HEATER	FW	FIRE WATER
ACST	ACOUSTIC	CU YD	CUBIC YARDS	FWC	FABRIC WALL COVERING
ACT	ACOUSTICAL CEILING TILE	CV	CEILING VENT	G	NATURAL GAS
ADDM	ADDENDUM	CVH	CONDUCTIVE VINYL HOMOGENEOUS	GA	GAGE
ADH	ADHESIVE	(SHEET TYPE)		GAL	GALLON(S)
ADJ	ADJACENT, ADJOINING, ADJUSTABLE	CW	COLD WATER	GALV	GALVANIZED
ADO	AUTOMATIC DOOR OPERATOR	CYL	CYLINDER	GALV STL	GALVANIZED STEEL
AFF	ABOVE FINISHED FLOOR	d	PENNY (AS IN NAIL - 100)	GB	GRAB BAR
AGGR	AGGREGATE	DAT	DATUM	GC	GENERAL CONTRACTOR
AHR	ANCHOR	DB	DRY BULB	GEN	GENERAL
AHU	AIR HANDLING UNIT	DBL	DOUBLE	GF	GROUND FACE
AI	AREA INLET	DBL ACT DR	DOUBLE ACTING DOOR	GFCI	GROUND FAULT CIRCUIT INTERRUPTER
AIC	AMPERE INTERRUPTING CAPACITY	DCJ	DOWELED CONTROL JOINT	GFE	GOVERNMENT-FURNISHED EQUIPMENT
AISC	AMERICAN INSTITUTE OF STEEL CONSTRUCTION	DCJT	DUMMY CONTROL JOINT	GFE/CI	GOVERNMENT-FURNISHED EQUIPMENT
A.L.	ACTIVE LEAF	DEG	DEGREE		CONTRACTOR INSTALLED
ALT	ALTERNATE	DEMO	DEMOLITION	GI	GALVANIZED IRON
ALUM	ALUMINUM	DEPR	DEPRESSION	GIP	GALVANIZED IRON PIPE
AMB	AMBIENT	DEPT	DEPARTMENT	GKT	GASKET(ED)
AMP	AMPERE	DET	DETAIL	GL	GLASS
ANOD	ANODIZE	DF	DRINKING FOUNTAIN	GL BLK	GLASS BLOCK
ANSI	AMERICAN NATIONAL STANDARDS INSTITUTE	DGA	DENSE GRADED AGGREGATE	GLF	GLASS FIBER
APRPTD	APPROVED	DH	DUCT HUNG	GLZ	GLAZING
APPROX	APPROXIMATE	DH	DUCT HEATER	GLZ CMU	GLAZED CONCRETE MASONRY UNITS
ARCH	ARCHITECT	DIA	DIAMETER	G	GROUND
ARI	AMERICAN REFRIGERATION INSTITUTE	DIAG	DIAGONAL	GOVT	GOVERNMENT
ASB	ASBESTOS	DIM	DIMENSION	GPM	GALLONS PER MINUTE
ASC	ABOVE SUSPENDED CEILING	DISC	DISCONNECT	GPT	GYPSUM TILE
ASPH	ASPHALT	DISP	DISPENSER	GRAN	GRANITE
ATC	ACOUSTICAL TILE CEILING	DISTR PNL	DISTRIBUTION PANEL	GR LN	GRADE LINE
AUTO	AUTOMATIC	DIV	DIVISION	GRTG	GRATING
AVG	AVERAGE	DL	DEAD LOAD	GST	GLAZED STRUCTURAL TILE
AWG	AMERICAN WIRE GAUGE	DMPF	DAMP PROOFING	GSU	GLAZED STRUCTURAL UNITS
AWT	ACOUSTICAL WALL TREATMENT	DMPR	DAMPER	GWT	GROUT
BB	BULLETIN BOARD	DMT	DEMOUNTABLE	DWR	GLAZED WALL TILE
BC	BOOKCASE	DN	DOWN	GYP	GYPSUM
BD	BOARD	DR	DOOR	GYP BD	GYPSUM BOARD
BDRY	BOUNDARY	DR	DRAIN	GYP PLAS	GYPSUM PLASTER
BEJ	BRICK EXPANSION JOINT	DRB	DRAINBOARD	HB	HOSE BIBB
BEV	BEVEL	DR CL	DOOR CLOSER	HC	HOLLOW CORE
BITUM	BITUMINOUS	DS	DOUBLE STRENGTH (GLASS)	HCD	HALON CONTAINMENT DAMPER
BJT	BED JOINT	DSP	DOWNSPOUT	HCP	HANDICAPPED
BL	BUILDING LINE	DT	DRAIN TILE	HD	HEAD
BLDG	BUILDING	DVTL	DOVETAIL	HDO	HEAVY DUTY
BLW	BELOW	DWG	DRAWING	HDBD	HARDBOARD
BM	BENCHMARK	DWLS	DOWELS	HD JT	HEAD JOINT
BO	BOTTOM OF	DWR	DRAWER	HDR	HEADER
BOT	BOTTOM	DWTR	DUMBWATER	HDW	HARDWARE
BP	BACK PLASTER(ED)	DX	DIRECT EXPANSION	HDWD	HARDWOOD
BRCG	BRACING	E	EAST	HES	HIGH EARLY-STRENGTH CEMENT
BRDG	BRIDGING	EA	EACH	HEX	HEXAGON
BRG	BEARING	EAT	ENTERING AIR TEMPERATURE	HH	HANDHOLE
BRG PL	BEARING PLATE	EF	EACH FACE	HK(S)	HOOK(S)
BRK	BRICK	EJ	EXPANSION JOINT	HM	HOLLOW METAL
BRKT	BRACKET	EL	ELEVATION - GRADE OR BUILDING	HNDRL	HANDRAIL
BRZ	BRONZE	ELEC	ELECTRIC	HORIZ	HORIZONTAL
BS	BOTH SIDES	EM	EXPANDED METAL	HP	HIGH PRESSURE
BSMT	BASEMENT	EMD	ESTIMATED MAXIMUM DEMAND	HPT	HORSEPOWER
Btu	BRITISH THERMAL UNIT	EMER	EMERGENCY	HPT	HIGH POINT
BtuH	BTU PER HOUR	ENCL	ENCLOSE(URE)	HR	HOUR
BTWN	BETWEEN	ENR	ENTRANCE, ENTERING	HS	HIGH STRENGTH
BUR	BUILT-UP ROOFING	EP	ELECTRICAL PANELBOARD	HSGYP	HIGH-STRENGTH GYPSUM PLASTER
BW	BOTH WAYS	EPRF	EXPLOSION PROOF	HSPKG	HOUSEKEEPING
CAB	CABINET	EPY	EPOXY COATING	HT	HEIGHT
CAP	CAPACITY	EQ	EQUAL	HTG	HEATING
CB	CATCH BASIN	EQUIP	EQUIPMENT	HTR	HEATER
CCT	CUBICLE CURTAIN TRACK	ESCAL	ESCALATOR	HVAC	HEATING, VENTILATING AND AIR
CCTV	CLOSED CIRCUIT TELEVISION	EST	ESTIMATE(D)	CONDITIONING	
CE	COVER ELEVATION	EWG	ELECTRIC WATER COOLER	HYDR	HYDRAULIC
CEM	CEMENT	EWIT	ENTERING WATER TEMPERATURE	Hz	HERTZ
CEM PLAS	CEMENT PLASTER	EXC	EXCAVATE	IC	INTERCOM
CER	CERAMIC	EXH	EXHAUST	ID	INSIDE DIAMETER
CFI	CONDUCTIVE FLOORING	EXH A	EXHAUST AIR	IESNA	ILLUMINATING ENGINEERING SOCIETY OF
CFLG	COUNTERFLASHING	EXST	EXISTING	NORTH AMERICA	
CFM	CUBIC FEET PER MINUTE	EXP	EXPANSION	ILK	INTERLOCK
CG	CORNER GUARD	EXP	EXPOSED	IN	INCH
CH BD	CHALKBOARD	EXP BT	EXPANSION BOLT	INCN	INCINERATOR
CHFR	CHAMFER	EXT	EXTERIOR	INCL	INCLUDED
CHIM	CHIMNEY	F	FAHRENHEIT	INSF	INSULATING FILL
CHK	CHECK	FA	FIRE ALARM	INSUL	INSULATION
CHR PL	CHROME PLATED	FA	FRESH AIR	INT	INTERIOR
CI	CAST IRON	FAC	FIRE APPARATUS CLOSET	INTM	INTERMEDIATE
CI	CURB INLET	FAL	FRESH AIR INTAKE	INV	INVERT
CIP	CAST-IN-PLACE	F BRK	FIRE BRICK	IP	IRON PIPE
CIRC	CIRCULAR	FC	FOOT CANDLE	IPS	IRON PIPE SIZE
CJ	CONTROL JOINT	FC BRK	FACE BRICK	I.P.S.	INSIDE PIPE SIZE
CJ	CONSTRUCTION JOINT	FCG	FACING	JAN CLO	JANITOR'S CLOSET
CKT	CIRCUIT	FCJ	FLOOR CONSTRUCTION JOINT	J-BOX	JUNCTION BOX
CKT BRKR	CIRCUIT BREAKER	FCO	FLOOR CLEANOUT	JCT	JUNCTION
CL	CENTER LINE	FCU	FAN COIL UNIT	JST	JOIST
CLG	CEILING	FD	FLOOR DRAIN	JT	JOINT
CLG HT	CEILING HEIGHT	FDMPR	FIRE DAMPER	KIP	KILOPOUND (1000 POUNDS)
CLGL	CLEAR GLASS	FDN	FOUNDATION	KIT	KITCHEN
CLL	CONTRACT LIMIT LINE	FE	FIRE EXTINGUISHER	KOP	KNOCKOUT PANEL
CLOS	CLOSET	FEB	FIRE EXTINGUISHER BRACKET	KPL	KICKPLATE
CLOS	CLOSURE	FEC	FIRE EXTINGUISHER CABINET	KV	KILOVOLTS
CLR	CLEAR(ANCE)	FF	FACTORY FINISH	KVA	KILOVOLT AMPERES
CLWG	CLEAR WIRED GLASS	FGL	FIBERGLASS	KVAR	KILOVOLT AMPERES REACTIVE
cm	CENTIMETER(S)	FH	FIRE HYDRANT	KW	KILOWATT
CMP	CORRUGATED METAL PIPE	FH	FLAT HEAD	KWY	KEYWAY
CMPS	COMPOSITE	FHC	FIRE HOSE CABINET	LAB	LABORATORY
CMU	CONCRETE MASONRY UNIT	FHMS	FLAT HEAD MACHINE SCREW	LAD	LADDER
CND	CONDUIT	FHR	FIRE HOSE RACK	LAM	LAMINATE
CNL	CONDUCTIVE NEOPRENE LATEX	FHS	FIRE HOSE STATION	LAT	LEAVING AIR TEMPERATURE
CNR	CORNER	FHWS	FLAT HEAD WOOD SCREW	LAU	LAUNDRY
CNTR	COUNTER	FIG	FIGURE	LAV	LAVATORY
CO	CLEANOUT	FIN	FINISH	LB	LAG BOLT
CO2	CARBON DIOXIDE	FIN FLR	FINISH FLOOR	P	POUND
COL	COLUMN	FIXT	FIXTURE	LBL	LABEL
COM	COMMON	FJT	FLUSH JOINT	LBR	LUMBER
COMB	COMBUSTION	FLASH	FLASHING	LC	LIGHT CONTROL
COMPT	COMPARTMENT	FLR	FLOOR	LD	LOAD
CONC	CONCRETE	FLEX	FLEXIBLE	LDG	LOADING
CONN	CONNECT	FLG	FLOORING	LG	LENGTH
CONSTR	CONSTRUCTION	FLR PL	FLOOR PLATE	LH	LEFT HAND(ED)
CONTR	CONTINUE	FLUOR	FLUORESCENT	LIN	LINEAR
CONTR	CONTRACTOR	FN	FENCE	LKR	LOCKER
CORR	CORRIDOR	FOC	FACE OF CONCRETE	LL	LIVE LOAD
COV	COVER	FOF	FACE OF FINISH	LLD	LEAD-LINED DOOR
CPRS	COMPRESSIBLE	FOM	FACE OF MASONRY	LM	LUMEN
CPT	CARPET	FOS	FACE OF STUD	LMST	LIMESTONE
CRCMF	CIRCUMFERENCE	FP	FIRE PARTITION	LNTL	LINTEL
CRES	CORROSIVE RESISTANT STEEL	PP	PROOF	LONG	LONGITUDINAL
CRG	CROSS GRAIN	FPM	FEET PER MINUTE	LP	LIGHTPROOF
CRS	COURSE(S)	FR	FIRE RESISTANT	LPD	LIGHTPROOF DOOR

1

2

3



4

DRAWING INDEX

GENERAL	
G-001	COVER SHEET AND LOCATION MAPS
G-002	ABBREVIATIONS AND DRAWING INDEX
G-003	PROJECT NOTES AND SYMBOLS LEGEND

SURVEY	
V-001	TOPOGRAPHIC SURVEY
V-101	TOPOGRAPHIC SURVEY
V-102	TOPOGRAPHIC SURVEY
V-103	TOPOGRAPHIC SURVEY
V-104	TOPOGRAPHIC SURVEY

CIVIL	
CD100	DEMO PLAN NORTH
CD101	DEMO PLAN SOUTH
EC100	EPSC PLAN NORTH
EC101	EPSC PLAN SOUTH
EC102	EPSC DETAILS
CS100	SITE PLAN NORTH
CS101	SITE PLAN SOUTH
CG110	GRADING PLAN
C-500	CHAIN LINK FENCE & DETAIL
C-501	TYPICAL PERSONNEL GATE & BOLLARD DETAIL
C-502	TYPICAL CABLE REINFORCED CHAIN LINK FENCE GATE AND CABLE REINFORCING

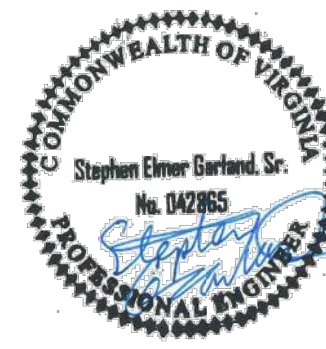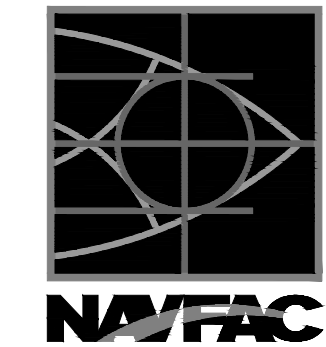

APPROVED
FOR COMMANDER NAVFAC
ACTIVITY BILL BOUNDS, DLA

SATISFACTORY TO DATE: 14 JAN 2026

DES SG DRW SD CHK RB

PMDEM W. WITHAM, P.E.

BRANCH MANAGER W. WITHAM, P.E.

CHIEF ENGINEER J. MILLER, P.E.

FIRE PROTECTION N/A

NAVFAC FACILITIES ENGINEERING SYSTEMS COMMAND - MID-ATLANTIC

NAVAL STATION - NORFOLK

NAVAL STATION

NORFOLK, VIRGINIA

LP-38 BERM RECERTIFICATION REPAIR

ABBREVIATIONS AND DRAWING INDEX

SCALE: AS SHOWN

PROJECT NO. 1766588

CONSTR. CONTR. NO. N40085-22-D-0039

NAVFAC DRAWING NO. 12940906

SHEET 2 OF 19

G-002

DRAWFORM REVISION: 14 SEP 2023

FILE NAME: P:\Projects\2024\21297-24020 NAVFAC Midlant LP-38 Berm Recert\500-CAD\510-Arch\DWG\1766588-G-003.dwg LAYOUT NAME: G-003 PLOTTED: Wednesday, February 11, 2026 - 9:19am USER: cmoore

SYMBOLS LEGEND

1

NOTE INDICATOR

NORTH

NORTH ARROW

0'5'10'20'30'

1/8"=1'-0"

DRAWING SCALE INDICATOR

#

TITLE VIEW

#

Scale: SCALE

GRID NUMBER/LETTER

DRAWING VIEW NUMBER

DRAWING VIEW SCALE

DRAWING REF. NUMBER

3

REVISION CLOUD AND NUMBER INDICATOR

REVISION NUMBER

LIMIT OF REVISION AREA

PROJECT GENERAL NOTES

1. MANY OF THE DETAILS CONTAINED HERE-IN ARE DEVELOPED BASED UPON DESIGN PERFORMANCE CRITERIA. MANY DETAILS ARE GENERIC IN NATURE AND DEPENDANT ON THE ACTUAL PRODUCT SELECTION MADE BY THE CONTRACTOR DURING BIDDING AND CONSTRUCTION. WHEN REQUESTED OR REQUIRED BY THE MANUFACTURER DUE TO THE CONFIGURATION OF THEIR PRODUCT(S), MINOR VARIATIONS FROM THE DETAILS SHOWN WILL BE CONSIDERED WHEN THEY MEET THE REQUIREMENTS OF THE CONTRACT DRAWINGS AND SPECIFICATIONS. THE CONTRACTING OFFICER WILL DETERMINE THE EQUIVALENCY OF ANY SUCH VARIATION. THE CONTRACTOR WILL SUBMIT AS A MINIMUM THE DETAILS SHOWN WITH ANY VARIATION TO THE DETAILS CONTAINED IN THE CONTRACT DOCUMENTS. OPTIONS TO THE DETAILS SHOWN WILL BE DEVELOPED AND INSTALLED AT NO ADDITIONAL COST TO THE GOVERNMENT. IF PROPOSED VARIATIONS TO THE DETAILS ARE NOT ACCEPTED, THE CONTRACTOR WILL EITHER INSTALL THE MATERIAL AS INDICATED ON THE CONTRACT DRAWINGS AND SPECIFICATIONS OR REVISE THE PROPOSED DETAILS AS DIRECTED BY THE CONTRACTING OFFICER.

2. IF THE CONTRACTOR ENCOUNTERS ANY UNFORESEEN SITE CONDITIONS DURING THE PERFORMANCE OF THE CONTRACT, INCLUDING BUT NOT LIMITED TO SUSPECTED ASBESTOS CONTAINING MATERIAL (ACM) OR LEAD-BASED PAINT, THE CONTRACTOR MUST CEASE EXECUTION OF WORK/OPERATIONS IN THE SUSPECT AREA, IMMEDIATELY EVACUATE ALL PERSONNEL AND NOTIFY THE CONTRACTING OFFICER. VERIFICATION OF THE SUSPECT MATERIAL WILL COMMENCE THROUGH SAMPLE AND ANALYSIS BY A CONTRACTOR QUALIFIED FOR SUCH, AS DIRECTED BY THE CONTRACTING OFFICER.

3. DO NOT SCALE DRAWINGS. IF DIMENSIONS ARE IN QUESTION, CONTACT THE CONTRACTING OFFICER'S REPRESENTATIVE.

4. PROVIDE SECURITY FENCE AROUND MATERIALS STORAGE AREA AND PROJECT FIELD OFFICE.

5. COORDINATE WITH BASE FOR CONSTRUCTION HAUL ROUTE, STAGING AND CONTRACTOR PARKING AREAS.

6. CONTRACTOR MUST PROVIDE AS-BUILT INFORMATION ON ALL CONDITIONS INSTALLED INCLUDING CERTIFIED TOPOGRAPHIC SURVEY. CERTIFIED SIGNED AND SEALED AS-BUILT TOPO SURVEY (GRADES) MUST BE BY VA PROFESSIONAL LAND SURVEYOR.

7. EXISTING CONDITIONS DIMENSIONS SHOWN ARE APPROXIMATE. CONTRACTOR MUST FIELD VERIFY ALL DIMENSIONS.

8. CONTRACTOR WILL COORDINATE ALL ACTIVITIES THAT GENERATE NOXIOUS ODORS WITH OWNER REPRESENTATIVE SO AS TO MINIMIZE THE NEGATIVE EFFECTS OF FUMES.

9. SECURE ALL CONSTRUCTION LOCATIONS AT ALL TIMES. CONTRACTOR IS RESPONSIBLE FOR JOBSITE SECURITY.

10. THE CONTRACTOR WILL PROVIDE SECURITY FENCE AND OTHER SAFETY MEASURES AS REQUIRED TO PROTECT THE OCCUPANTS AND VISITORS TO SURROUNDING BUILDINGS. ANY EXCAVATIONS WILL BE SUITABLY MARKED AND PROTECTED BY FENCING ADEQUATE TO PROVIDE A SAFE ENVIRONMENT. THE CONTRACTOR MAINTAINS THE SOLE RESPONSIBILITY AND LIABILITY FOR IMPLEMENTATION, DESIGN, AND MAINTENANCE OF ALL SAFETY FEATURES, INCLUDING BARRICADES, COVERED WALKWAYS, AND FENCES.

11. CONTRACTOR MUST VERIFY ALL EXISTING CONDITIONS PRIOR TO DEVELOPMENT OF SHOP DRAWINGS AND CONSTRUCTION.

12. THE WORK INCLUDES DEMOLITION. DUST AND FUMES FROM DEMOLISHED MATERIAL MAY ALSO BE CONSIDERED AS HAZARDOUS OR NOXIOUS AND MAY CONTAIN MATERIALS KNOWN OR THOUGHT TO BE HAZARDOUS.

13. CONTRACTOR MUST FIELD VERIFY ALL EXISTING CONDITIONS AND DIMENSIONS PRIOR TO BEGINNING ANY WORK. IF DEVIATIONS ARE DISCOVERED BETWEEN THE DRAWINGS AND ACTUAL CONDITIONS THE CONTRACTOR MUST NOTIFY THE CONTRACTING OFFICER IMMEDIATELY.

14. THE CONTRACTOR MUST FOLLOW ALL LOCAL, STATE AND FEDERAL GUIDELINES REGARDING THE DISPOSAL OF DEMOLITION MATERIAL.

15. THE DEMOLITION DRAWINGS ARE BASED ON AVAILABLE INFORMATION AND MAY NOT REPRESENT ALL CONDITIONS. THE CONTRACTOR MUST CAREFULLY REVIEW AND EXAMINE THE ACTUAL CONDITIONS ON SITE.

16. THE CONTRACTOR IS RESPONSIBLE TO PROTECT AND PRESERVE ALL ITEMS NOTED TO REMAIN.

17. WORK IS NEW, UNLESS INDICATED AS EXISTING OR AS DEMOLITION. COORDINATE CONSTRUCTION AND DEMOLITION. VERIFY AND COORDINATE DIMENSIONS AND CLEARANCES WITH THE WORK OF ALL TRADES. PROTECT EXISTING CONSTRUCTION TO REMAIN.

18. CONTRACT DOCUMENTS ARE COMPLEMENTARY, IN THAT ANY ITEM OF DEMOLITION OR CONSTRUCTION INDICATED ON ANY DRAWING OR SPECIFICATION, MUST BE CONSIDERED INDICATED ON ALL DOCUMENTS. IF WORK IS IN QUESTION, THEN CONTACT THE CONTRACTING OFFICER'S REPRESENTATIVE.

Schmidt PRIME LLP

931 West Garden Street
Pensacola, Florida 32502
P: 850-438-0050
schmidtconsultinggroup.com

A/E INFO

APPROVED
James M. Smith
FOR COMMANDER NAVFAC 3-1-26

ACTIVITY: BILL BOUNDS, DLA

SATISFACTORY TO DATE: 14 JAN 2026

DES: KML DRW: KML CHK: JVS

PM/DM: W. WITHAM, P.E.

BRANCH MANAGER: W. WITHAM, P.E.

CHIEF ENG/ARCH: J. MILLER, P.E.

FIRE PROTECTION: N/A

DEPARTMENT OF THE NAVY
NAVAL FACILITIES ENGINEERING SYSTEMS COMMAND - MID-ATLANTIC
MIDLANT DC CORE
NAVAL STATION

NAVAL FACILITIES ENGINEERING SYSTEMS COMMAND - MID-ATLANTIC
NAVAL STATION - NORFOLK VA
NORFOLK, VIRGINIA

LP-38 BERM RECERTIFICATION REPAIR

PROJECT NOTES AND SYMBOLS

SCALE:	AS SHOWN
PROJECT NO.:	1766588
CONSTR. CONTR. NO.:	N40085-22-D-0039
NAVFAC DRAWING NO.:	12940907
SHEET 3	OF 19
G-003	

DRAWFORM REVISION: 14 SEP 2023

1 2 3 4 5



SHEET FORMAT IS 22" X 34". IF PRINTED SHEET IS NOT 22" X 34", THEN IT IS NOT TO SCALE

NOTES:



1. THIS SURVEY WAS PREPARED WITHOUT THE BENEFIT OF A CURRENT TITLE REPORT AND THEREFORE MAY NOT SHOW ANY/ALL EASEMENTS OR RESTRICTIONS THAT MAY AFFECT THE PROPERTY AS SHOWN.
2. THIS PROPERTY APPEARS TO FALL IN FLOOD ZONE X AND SHADED X AS SHOWN ON PANEL 0000H OF THE FLOOD INSURANCE RATE MAPS FOR THE CITY OF NORFOLK, VIRGINIA, COMMUNITY NO.:S10104, DATED FEBRUARY 17, 2017. FLOOD ZONE INFORMATION SHOWN HEREON IS NOT GUARANTEED AND WAS APPROXIMATELY SCALED FROM THE FLOOD INSURANCE RATE MAPS FOR THE CITY/COUNTY INDICATED. MSA, P.C. IS NOT A PARTY IN DETERMINING THE REQUIREMENTS FOR FLOOD INSURANCE ON THE PROPERTY SHOWN. FOR FURTHER INFORMATION AND TO CONFIRM THE FLOOD ZONE FOR THIS PROPERTY, CONTACT THE LOCAL COMMUNITY FLOOD OFFICIAL. FLOOD ZONE DETERMINATION IS BASED ON THE FLOOD INSURANCE RATE MAPS AND DOES NOT IMPLY THAT THIS PROPERTY WILL OR WILL NOT BE FREE FROM FLOODING OR DAMAGE.
3. NORTH MERIDIAN SHOWN HEREON IS BASED ON VIRGINIA STATE PLANE COORDINATE SYSTEM, SOUTH ZONE NAD83 (2011) (EPOCH 2010.00), AND WAS GPS DERIVED USING GNSS NETWORK RTK METHODS, WITH REFERENCE TO GPS CONTINUOUSLY OPERATING REFERENCE STATIONS, AND CORRECTION SERVICES PROVIDED BY HXGN SMARTNET (SMARTNET NORTH AMERICA). COORDINATE VALUES AND LENGTHS/DISTANCES SHOWN ARE EXPRESSED IN U.S. SURVEY FEET.
4. ELEVATIONS SHOWN HEREON ARE BASED ON NAD83 AND WERE GPS DERIVED USING GNSS NETWORK RTK METHODS, WITH REFERENCE TO GPS CONTINUOUSLY OPERATING REFERENCE STATIONS USING GEOID18, AND CORRECTION SERVICES PROVIDED BY HXGN SMARTNET (SMARTNET NORTH AMERICA).
5. THIS SURVEY DOES NOT ADDRESS THE EXISTENCE OR NONEXISTENCE OF WETLANDS, ENVIRONMENTAL HAZARDS, CEMETERIES OR ANY UNDERGROUND STRUCTURE NOT OBSERVED DURING THE COURSE OF THE SURVEY.
6. LOCATION OF UNDERGROUND NON-GRAVITY UTILITIES SHOWN ON THIS SURVEY ARE BASED ON SURFACE INDICATIONS OF SUBTERRANEAN USE, PAINT MARKINGS FIELD LOCATED BY MSA, AND TAKEN FROM PLANS PROVIDED BY OTHERS. THIS SURVEY DOES NOT GUARANTEE THE EXISTENCE OR NONEXISTENCE OF UNDERGROUND UTILITIES.
7. THIS TOPOGRAPHIC SURVEY WAS COMPLETED UNDER THE DIRECT AND RESPONSIBLE CHARGE OF JEFFREY J. VIERREITHER, L.S. (LIC. NO. 2306) FROM AN ACTUAL GROUND/AIRBORNE SURVEY MADE UNDER MY SUPERVISION; THAT THE IMAGERY AND/OR ORIGINAL DATA WAS OBTAINED ON 6-16-2025 AND 9-12-2025; AND THAT THIS PLAT, MAP OR DIGITAL GEOSPATIAL DATA INCLUDING METADATA MEETS MINIMUM ACCURACY STANDARDS UNLESS OTHERWISE NOTED.

LEGEND	
SYMBOL / ABBREVIATION	DESCRIPTION
WM	WATER METER
FH	FIRE HYDRANT
FDC	FIRE DEPARTMENT CONNECTION
WELL	WELL
MWELL	MONITOR WELL
WMH	WATER MANHOLE
WV	WATER VALVE
SP	SPIGOT
SMH	SANITARY MANHOLE
SCD	SANITARY CLEANOUT
SV	SANITARY VALVE
FMV	FORCE MAIN VALVE
LP	LIGHT POLE
GLIGHT	GROUND LIGHT
GW	GUY WIRE
TR	TRANSFORMER
EM	ELECTRIC METER
PP	POWER POLE
EB	ELECTRIC BOX
COMB	COMMUNICATIONS BOX
TPED	TELEPHONE PEDESTAL
TMH	TELEPHONE MANHOLE
CPED	CABLE TV PEDESTAL
CTVB	CABLE TV BOX
GM	GAS METER
GV	GAS VALVE
FC	FILLER CAP
DI1	DROP INLET 1
DI2	DROP INLET 2
DI3	DROP INLET 3
CB	CATCH BASIN
RD	ROOF DRAIN
SC	STORM CLEANOUT
STM	STORM MANHOLE
YD	YARD DROP INLET
FES	FARED-END SECTION
PE	PIPE END (CONTINUES)
AC	AC UNIT
MH	MANHOLE
POST	POST
BOL	BOLLARD
WITPOST	WITNESS POST
BORING	BORING
SIGN	SIGN
MB	MAIL BOX
EVERGREEN.....	
TREES	
DECIDUOUS	
BUSH/HEDGE	
WOODS LINE / WOODED	
	CURB AND GUTTER
	CONCRETE
	PAVEMENT
	BRICK
	GRAVEL
	FENCE
	GUARDRAIL
	PROPERTY LINE
	RIGHT-OF-WAY LINE
	BUILDINGS
	TOP OF BANK
	TOP OF SLOPE
	C. OF DITCH
	C. OF SWALE
	WATER/HYDROGRAPHIC FEATURE
	WETLANDS
	STORM SEWER
	WATER LINE
	SANITARY SEWER
	PIPE LABEL (SIZE, TYPE, ID)
	UNDERGROUND CABLE
	OVERHEAD CABLE
	OVERHEAD TELEPHONE
	UNDERGROUND FIBER OPTIC
	UNDERGROUND TELEPHONE
	UNDERGROUND GAS
	OVERHEAD ELECTRIC
	UNDERGROUND ELECTRIC
	FORCE MAIN
	STEAK
	UNKNOWN UTILITY
	UNDERGROUND TRAFFIC CONTROL
	TEMPORARY BENCHMARK (TBM)
	ELEVATIONS
	UTILITY STRUCTURE ID
	TO 10.00.....TOP OF CURB ELEVATIONS
	FL 9.50.....FLOW LINE ELEVATIONS
	TW 10.00.....TOP OF WALL ELEVATIONS
	TP 10.00.....TOP OF PIPE ELEVATIONS
	TH.....TEST HOLE W/D NO.

FB:635, PG 42

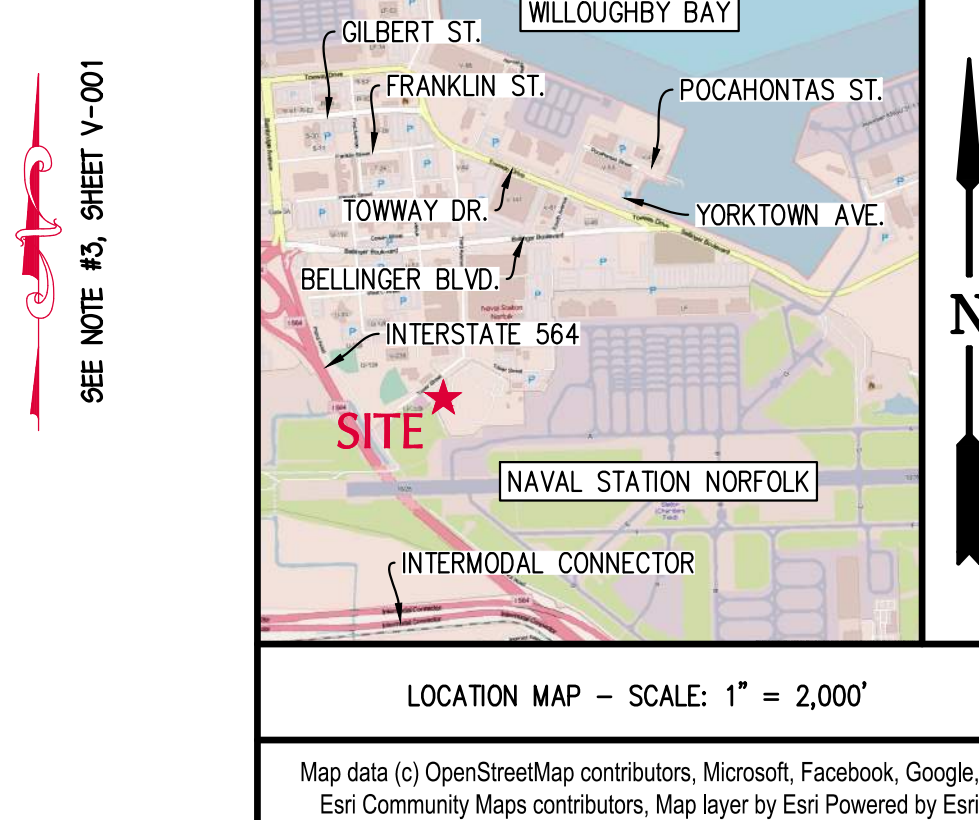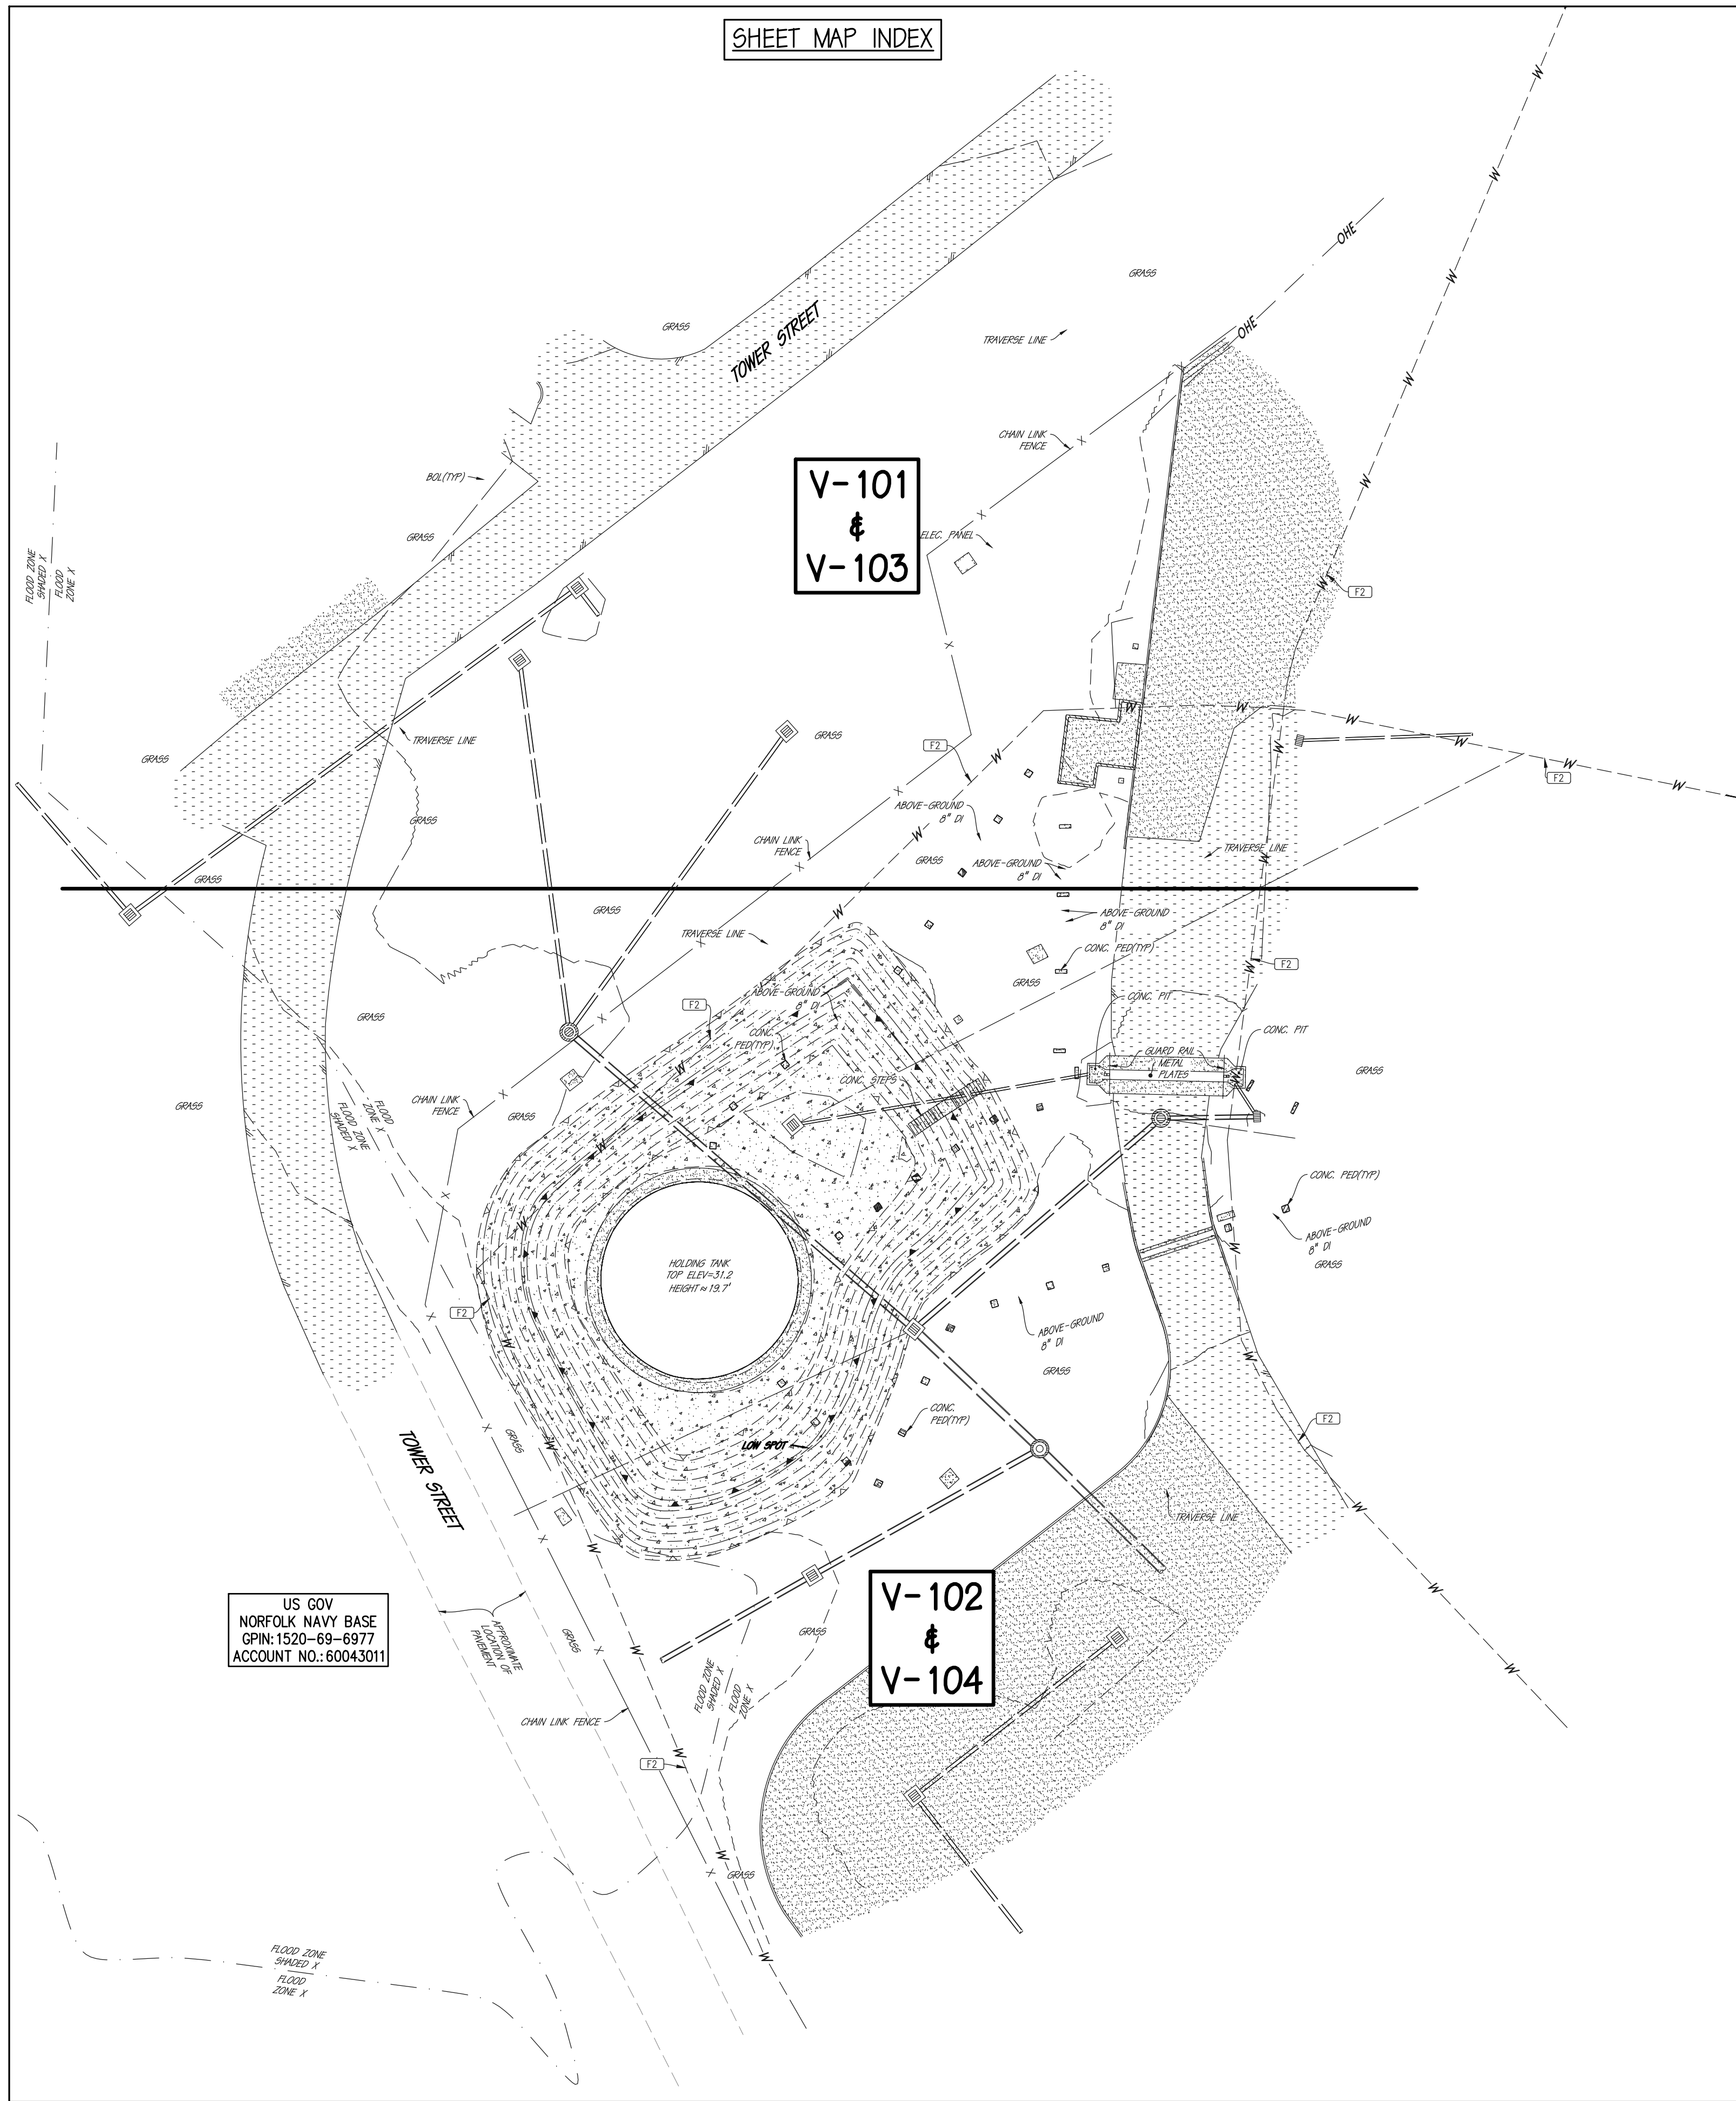

VOLUME CALCULATIONS
TANK VOLUME = 1,805.80 CY OR 48,757 CF
BERM VOLUME (@ LOW SPOT; ELEV. 15.2) = 1,393.28 CY OR 37,619 CF

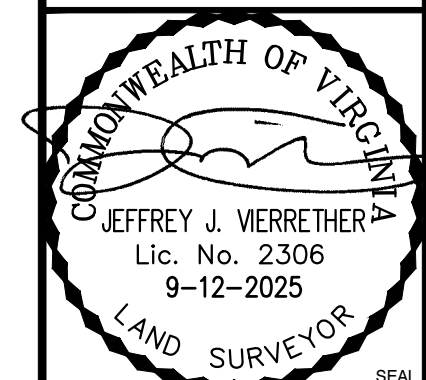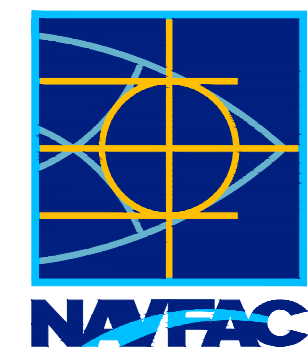[illegible]

APPROVED		XERO COPY	
			
FOR COMMANDER NAVFAC		3-1-26	
ACTIVITY - BILL BOUNDS, DLA			
SATISFACTORY TO DATE 14 JAN 2026			
DES	DRW WGS	CHK	JJV
PM/DM - W. WITHAM, P.E.			
BRANCH MANAGER - W. WITHAM, P.E.			
CHIEF ENGINEER - J. MILLER, P.E.			
STAFF ENGINEER - W. WITHAM, P.E.			

DEPARTMENT OF THE NAVY
NAVAL FACILITIES ENGINEERING SYSTEMS COMMAND - MID-ATLANTIC
NAVAL STATION - NORFOLK, VA
NAVAL FACILITIES ENGINEERING SYSTEMS COMMAND
FIRE PROTECTION DIVISION

SCALE: 1"=30'
EPROJECT NO.: 1766588
CONSTR. CONTR. NO. N40085-22-D-0039
NAVFAC DRAWING NO. 12940908
SHEET 4 OF 19

DRAWFORM REVISION: 14 SEP 2020




ENGINEERS | SCIENTISTS | SURVEYORS

5032 ROUSE DRIVE, SUITE 200 | VIRGINIA BEACH, VA 23462 | 757.490.9264 | MSAONLINE.CO
MSA PROJECT NO.: 23184B DATE: 9-19-2025

FILE NAME: C:\Users\BILL\OneDrive\AppData\Local\Temp\AepPublish_27348\231848 Topographic Survey.dwg LAYOUT NAME: V-101 PLOTTED: Tuesday, October 07, 2025 - 1:28pm USER: bill.setring

SEE SHEET V-103 FOR TOP-OF-PIPE
ELEVATIONS OF THE ABOVE-GROUND 8" DI PIPES


SEE NOTE #3, SHEET V-001

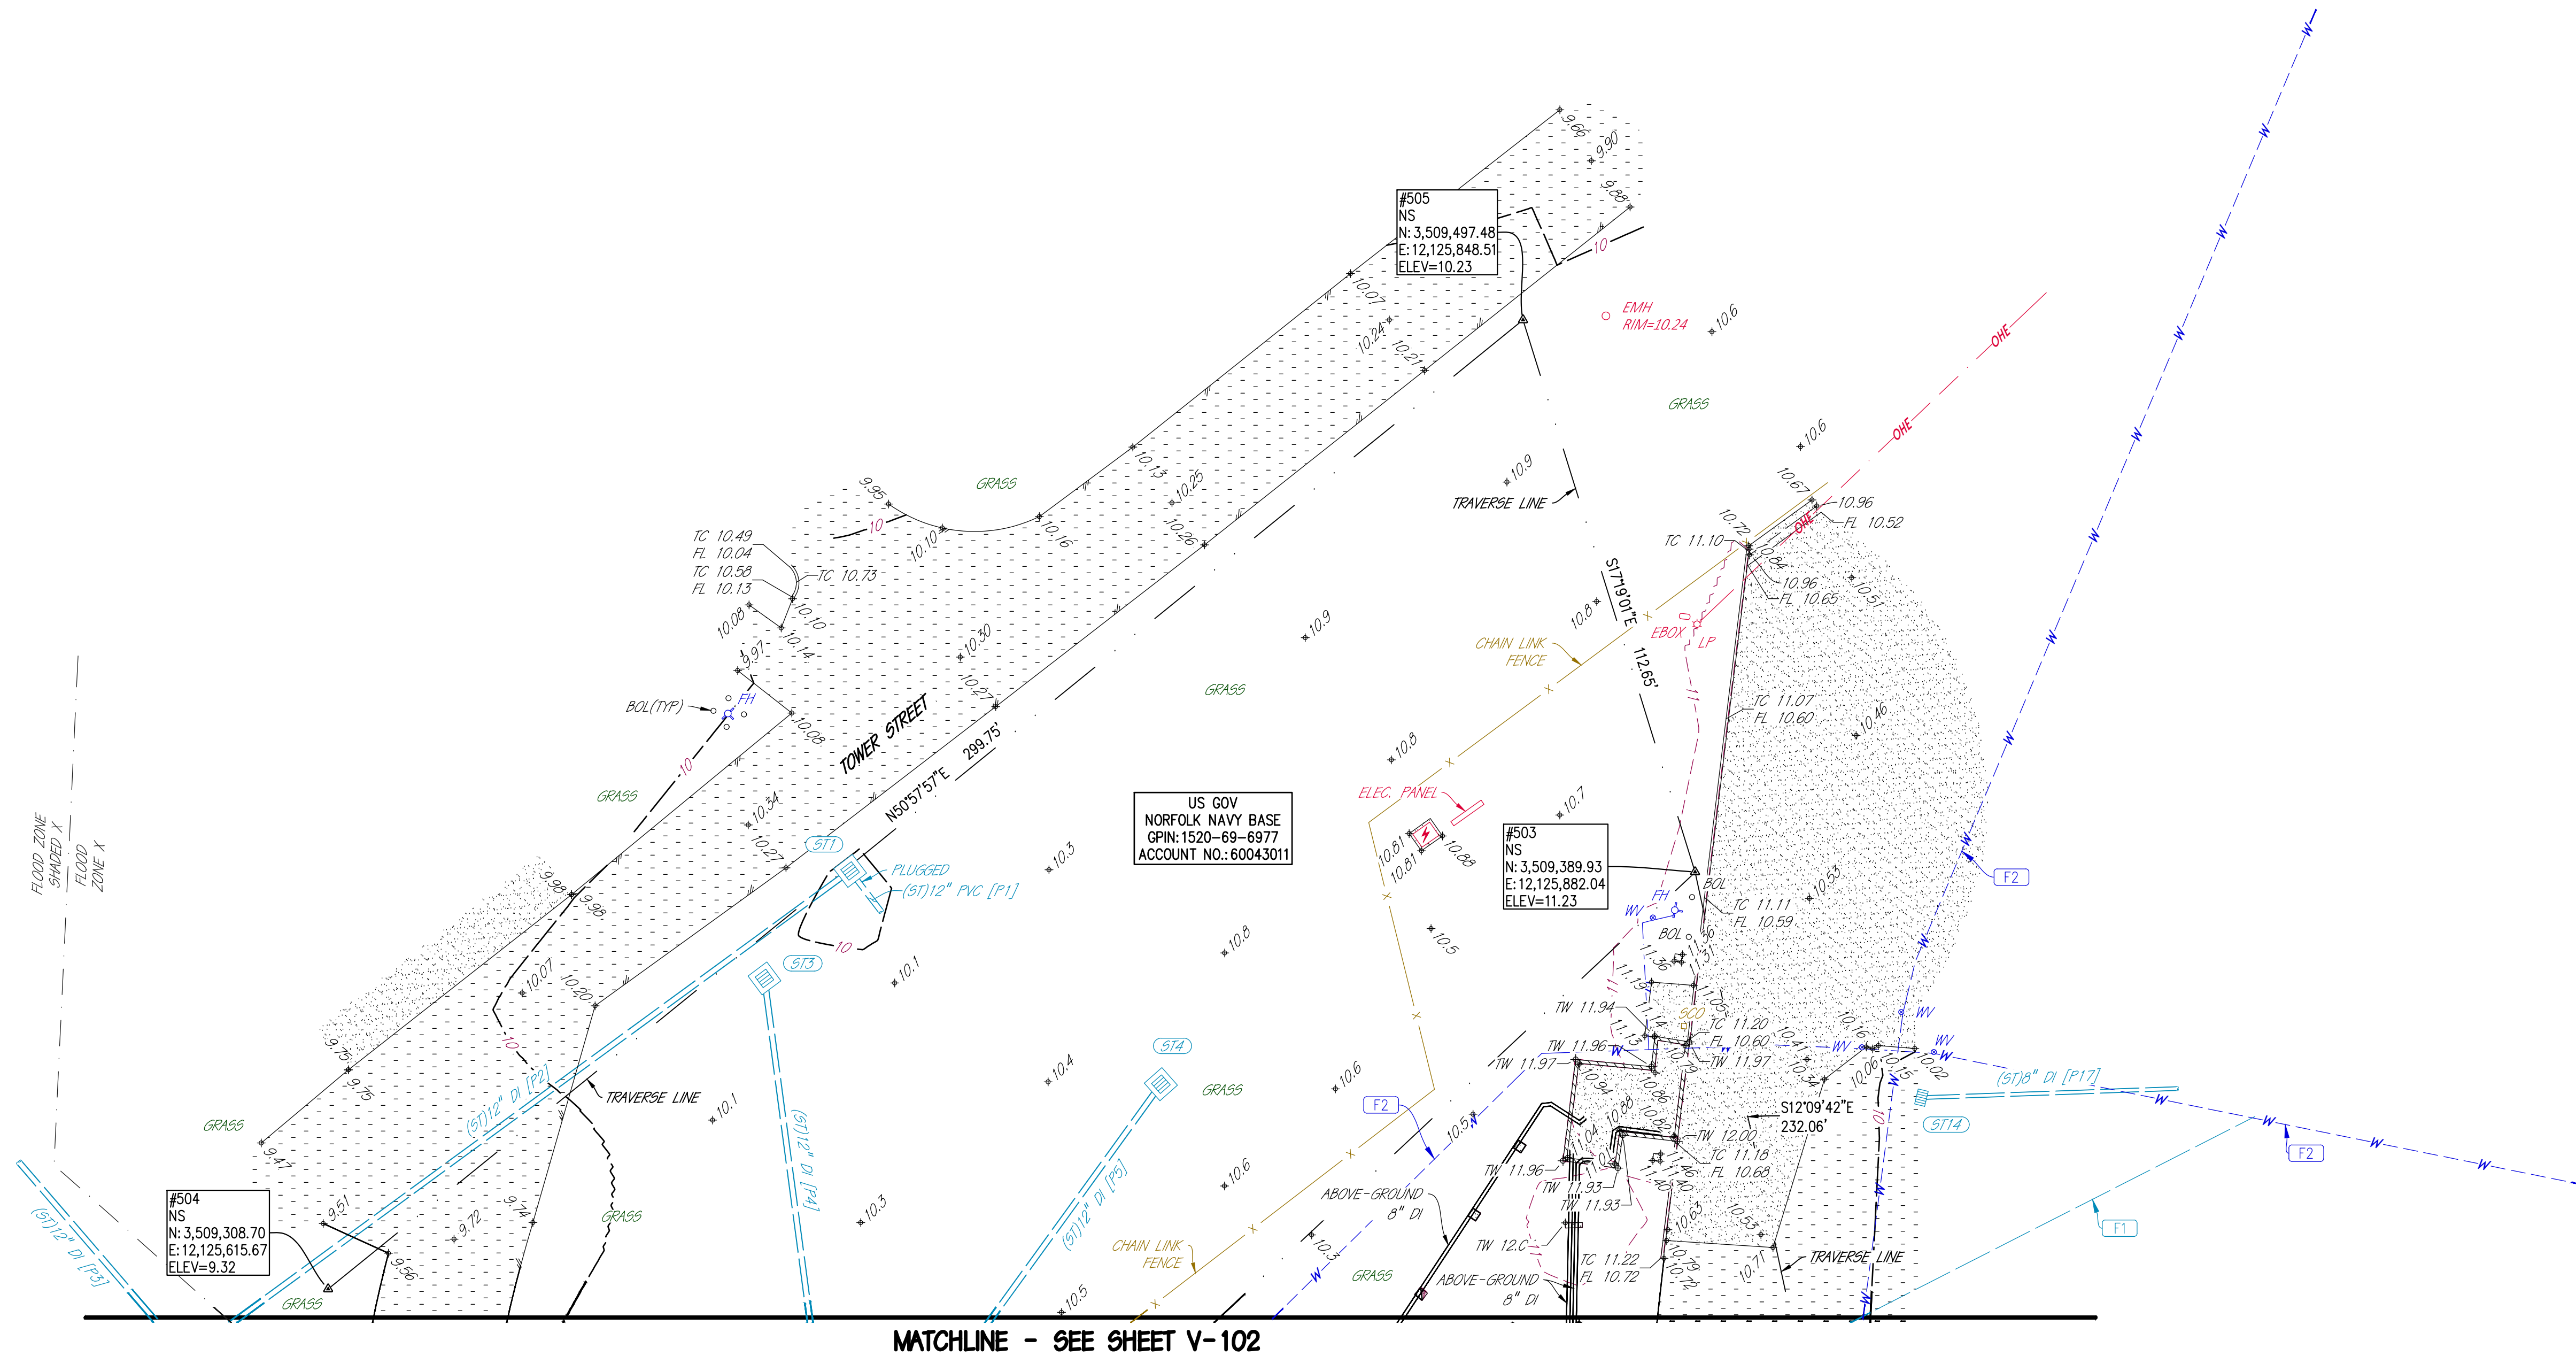

EXISTING STORM SEWER STRUCTURE TABLE		
ID	TYPE	RIM & INVERT
S11	DI1	RIM=9.89 INV [P2] (OUT,SW)=6.03 (12" DI)
S13	DI1 (FULL OF SEDIMENT)	RIM=10.07 INV [P4] (OUT,S)=7.28 (12" DI)
S14	DI1 (FULL OF SEDIMENT)	RIM=10.09 INV [P5] (OUT,SW)=7.30 (12" DI)
S14	DI3	RIM=9.72 INV [P17] (OUT,E)=6.39 (8" DI)

EXISTING STORM SEWER PIPE TABLE				
STRUCTURE TO STRUCTURE	LENGTH	SIZE/TYPE @ SLOPE	[10]	
S11 TO S12	160 LF	12" DI @ 0.76%	P2	
S13 TO S15	108 LF	12" DI @ 1.37%	P4	
S14 TO S15	107 LF	12" DI @ 1.41%	P5	

- EXISTING FEATURES KEYNOTES**
- F1** STORM PIPE
(PER PLANS PROVIDED BY OTHERS)
 - F2** WATERLINE
(PER PLANS PROVIDED BY OTHERS)

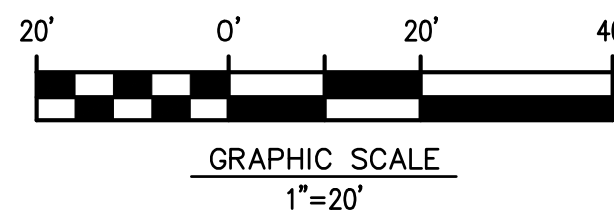

5032 ROUSE DRIVE, SUITE 200 | VIRGINIA BEACH, VA 23462 | 757.490.9264 | MSAONLINE.COM
MSA PROJECT NO.: 231848 DATE: 9-19-2025

DATE	
DESCRIPTION	
MARK	
NAVAC	
COMMONWEALTH OF VIRGINIA	
JEFFREY J. VIERRETH	
Lic. No. 2306	
9-12-2025	
LAND SURVEYOR	
Schmidt PRIME	
901 West Garden Street	
Pensacola, Florida 32502	
P: 850-438-0050	
schmidtconsultinggroup.com	
APPROVED	
FOR COMMANDER NAVAC	
ACTIVITY: BILL BOUNDS, DLA	
SATISFACTORY TO DATE: 14 JAN. 2026	
DES: DRW WGS CHK JJV	
PM/DM: W. WITHAM, P.E.	
BRANCH MANAGER: W. WITHAM, P.E.	
CHIEF ENGINEER: J. MILLER, P.E.	
FIRE PROTECTION: N/A	
NAVAL FACILITIES ENGINEERING SYSTEMS COMMAND	
NAVAL FACILITIES ENGINEERING SYSTEMS COMMAND - MID-ATLANTIC	
INSTANT DC CORE	
NAVAL STATION - NORFOLK	
NAVAL STATION	
NORFOLK, VIRGINIA	
LP-38 BERM RECERTIFICATION	
TOPOGRAPHIC SURVEY	
SCALE: 1"=20'	
PROJECT NO.: 1766588	
CONSTR. CONTR. NO.: N40085-22-D-0039	
NAVAC DRAWING NO.: 12940909	
SHEET 5 OF 19	
V-101	
DRAWFORM REVISION: 14 SEP 2023	

SEE SHEET V-104 FOR TOP-OF-PIPE
ELEVATIONS OF THE ABOVE-GROUND 8" DI PIPES


MATCHLINE - SEE SHEET V-101

SEE NOTE #3, SHEET V-001

EXISTING STORM SEWER STRUCTURE TABLE		
ID	TYPE	RIM & INVERT
ST2	DI1	RIM=8.61 INV [P2] (N,N)=4.82 (12" DI) INV [P3] (OUT,NW)=4.87 (12" DI)
ST5	DI2	RIM=9.13 INV [P4] (N,N)=5.79 (12" DI) INV [P5] (N,N)=5.79 (12" DI) INV [P6] (OUT,SE)=5.79 (18" RCP)
ST6	DI1	RIM=9.24 INV [P6] (N,N)=5.33 (18" RCP) INV [P10] (N,N)=5.33 (15" RCP) INV [P11] (OUT,SE)=5.33 (24" RCP)
ST7	DI1	RIM=9.52 INV [P7] (OUT,E)=6.82 (8" DI)
ST8	PIPE END	RIM=8.54 INV [P8] (OUT,SE)=7.62 (8" DI)
ST9	DI3	RIM=8.75 INV [P8] (N,N)=6.91 (8" DI) INV [P9] (OUT,W)=6.09 (12" RCP)
ST10	DI2	RIM=10.04 INV [P9] (N,N)=6.06 (12" RCP) INV [P10] (OUT,SW)=6.06 (15" RCP)
ST11	STMH	RIM=9.25 INV [P11] (N,N)=5.01 (24" RCP) INV [P13] (N,N)=5.85 (15" RCP) INV [P14] (OUT,SE)=5.01 (24" RCP)
ST12	DI1	RIM=8.74 INV [P12] (N,N)=6.04 (15" RCP) INV [P13] (OUT,NE)=6.04 (15" RCP)
ST13	DI1	RIM=8.59 INV [P15] (N,N)=4.80 (12" DI) INV [P16] (OUT,SE)=4.77 (12" DI)
ST15	DI1	RIM=8.63 INV [P15] (OUT,SW)=5.35 (12" DI)

EXISTING STORM SEWER PIPE TABLE			
STRUCTURE TO STRUCTURE	LENGTH - SIZE/TYPE @ SLOPE	[ID]	
ST1 TO ST2	160 LF - 12" DI @ 0.76%	P2	
ST3 TO ST5	108 LF - 12" DI @ 1.37%	P4	
ST4 TO ST5	107 LF - 12" DI @ 1.41%	P5	
ST5 TO ST6	132 LF - 18" RCP @ 0.35%	P6	
ST6 TO ST11	50 LF - 24" RCP @ 0.64%	P11	
ST8 TO ST9	11 LF - 8" DI @ 6.22%	P8	
ST9 TO ST10	28 LF - 12" RCP @ 0.11%	P9	
ST10 TO ST6	94 LF - 15" RCP @ 0.78%	P10	
ST12 TO ST11	75 LF - 15" RCP @ 0.25%	P13	
ST15 TO ST13	74 LF - 12" DI @ 0.74%	P15	

- EXISTING FEATURES KEYNOTES**
- F1** STORM PIPE
(PER PLANS PROVIDED BY OTHERS)
- F2** WATERLINE
(PER PLANS PROVIDED BY OTHERS)

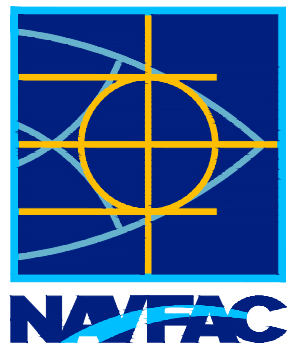

APPROVED
Paul M. Smith
FOR COMMANDER NAFAC
ACTIVITY: BILL BOUNDS, DLA

SATISFACTORY TO DATE: 14 JAN. 2025

DES: *WGS* CHK: *JJV*
PM/DM: W. WITHAM, P.E.
BRANCH MANAGER: W. WITHAM, P.E.
CHIEF ENGINEER: J. MILLER, P.E.
FIRE PROTECTION: N/A


NAVAL FACILITIES ENGINEERING SYSTEMS COMMAND
NAVAL STATION - MID-ATLANTIC
NAVAL STATION - NORFOLK
NAVAL STATION - NORFOLK, VIRGINIA
LP-38 BERM RECERTIFICATION
TOPOGRAPHIC SURVEY

SCALE: 1"=20'
PROJECT NO.: 1766588
CONSTR. CONTR. NO.: N40085-22-D-0039
NAVFAC DRAWING NO.: 129409010
SHEET 6 OF 19
V-102



ENGINEERS | SCIENTISTS | SURVEYORS

5032 ROUSE DRIVE, SUITE 200 | VIRGINIA BEACH, VA 23462 | 757.490.9264 | MSAONLINE.COM
MSA PROJECT NO.: 231848 DATE: 9-19-2025

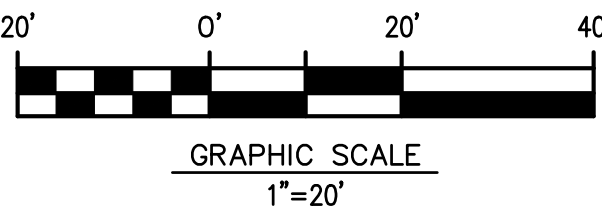




STRUCTURE TO STRUCTURE	LENGTH - SIZE/TYPE @ SLOPE	[10]
ST1 TO ST2	160 LF - 12" DI @ 0.76%	P2
ST3 TO ST5	108 LF - 12" DI @ 1.37%	P4
ST4 TO ST5	107 LF - 12" DI @ 1.41%	P5

20' 0' 20' 40'

GRAPHIC SCALE

1"=20'

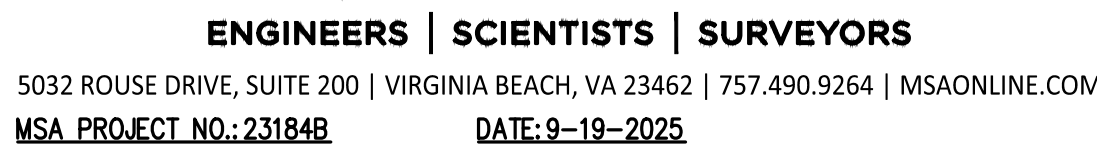[illegible]

DETAIL SHEET SHOWING TOP-OF-PIPE
ELEVATIONS OF THE ABOVE-GROUND 8" DI PIPES

MATCHLINE - SEE SHEET V-103



SEE NOTE #3, SHEET V-001

EXISTING STORM SEWER STRUCTURE TABLE		
ID	TYPE	RIM & INVERT
ST2	DI1	RIM=8.61 INV [P2] (IN,NE)=4.82 (12" DI) INV [P3] (OUT,NW)=4.87 (12" DI)
ST5	DI2	RIM=9.13 INV [P4] (IN,N)=5.79 (12" DI) INV [P5] (IN,NE)=5.79 (12" DI) INV [P6] (OUT,SE)=5.79 (18" RCP)
ST6	DI1	RIM=9.24 INV [P6] (IN,NW)=5.33 (18" RCP) INV [P10] (IN,NE)=5.33 (15" RCP) INV [P11] (OUT,SE)=5.33 (24" RCP)
ST7	DI1	RIM=9.52 INV [P7] (OUT,E)=6.82 (8" DI)
ST8	PIPE END	RIM=8.54 INV [P8] (OUT,SE)=7.62 (8" DI)
ST9	DI3	RIM=8.75 INV [P8] (IN,NW)=6.91 (8" DI) INV [P9] (OUT,W)=6.09 (12" RCP)
ST10	DI2	RIM=10.04 INV [P9] (IN,E)=6.06 (12" RCP) INV [P10] (OUT,SW)=6.06 (15" RCP)
ST11	STMH	RIM=9.25 INV [P11] (IN,NW)=5.01 (24" RCP) INV [P13] (IN,SW)=5.85 (15" RCP) INV [P14] (OUT,SE)=5.01 (24" RCP)
ST12	DI1	RIM=8.74 INV [P12] (IN,SW)=6.04 (15" RCP) INV [P13] (OUT,NE)=6.04 (15" RCP)
ST13	DI1	RIM=8.59 INV [P15] (IN,NE)=4.80 (12" DI) INV [P16] (OUT,SE)=4.77 (12" DI)
ST15	DI1	RIM=8.68 INV [P15] (OUT,SW)=5.35 (12" DI)

EXISTING STORM SEWER PIPE TABLE		
STRUCTURE TO STRUCTURE	LENGTH - SIZE/TYPE @ SLOPE	[ID]
ST1 TO ST2	160 LF - 12" DI @ 0.76%	P2
ST3 TO ST5	108 LF - 12" DI @ 1.37%	P4
ST4 TO ST5	107 LF - 12" DI @ 1.41%	P5
ST5 TO ST6	132 LF - 18" RCP @ 0.35%	P6
ST6 TO ST11	50 LF - 24" RCP @ 0.64%	P11
ST8 TO ST9	11 LF - 8" DI @ 6.22%	P8
ST9 TO ST10	28 LF - 12" RCP @ 0.11%	P9
ST10 TO ST6	94 LF - 15" RCP @ 0.75%	P10
ST12 TO ST11	75 LF - 15" RCP @ 0.25%	P13
ST15 TO ST13	74 LF - 12" DI @ 0.74%	P15

EXISTING FEATURES KEYNOTES

- F1 STORM PIPE
(PER PLANS PROVIDED BY OTHERS)
- F2 WATERLINE
(PER PLANS PROVIDED BY OTHERS)

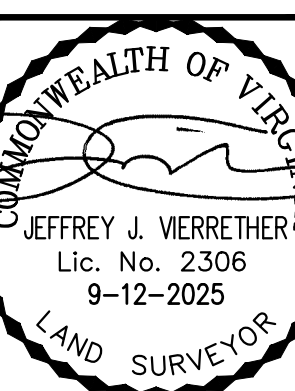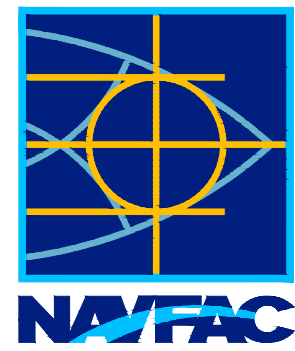

APPROVED
FOR COMMANDER NAVFAC
ACTIVITY: BILL BOUNDS, DLA

SATISFACTORY TO DATE: 14 JAN. 2026

DES: DRW WGS CHK: JIV

PM/DM: W. WITHAM, P.E.

BRANCH MANAGER: W. WITHAM, P.E.

CHIEF ENGINEER: J. MILLER, P.E.

FIRE PROTECTION: N/A

DEPARTMENT OF THE NAVY

NAVAL FACILITIES ENGINEERING SYSTEMS COMMAND

NAVAL STATION - MID-ATLANTIC

NAVAL STATION - NORFOLK

NORFOLK, VIRGINIA

NAVAL STATION

LP-38 BERM RECERTIFICATION

TOPOGRAPHIC SURVEY

SCALE: 1"=20'

PROJECT NO.: 1766588

CONSTR. CONTR. NO.: N40085-22-D-0039

NAVFAC DRAWING NO.: 12940912

SHEET 8 OF 19

V-104


DRAWING REVISION: 14 SEP 2023



ENGINEERS | SCIENTISTS | SURVEYORS

5032 ROUSE DRIVE, SUITE 200 | VIRGINIA BEACH, VA 23462 | 757.490.9264 | MSAONLINE.COM

MSA PROJECT NO.: 231848 DATE: 9-19-2025

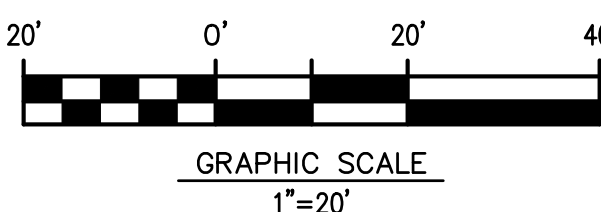

FILE NAME: P:\Projects\2024\21297-24020 NAVFAC Midant LP-38 Berm Recert\500-500\591-Civil\231848 DEMO AND EXISTING CONDITIONS PLAN.dwg LAYOUT NAME: CD-100-DEM0 PLAN PLOTTED: Wednesday, February 11, 2026 - 9:54am USER: cmoore



- # DEMOLITION KEY NOTES:
- NOTE: NOT ALL KEYNOTES APPLY TO EACH SHEET
- EXISTING BERM FOR TANK CONTAINMENT.
 - EXISTING ACCESS STAIR TO REMAIN AND BE PROTECTED DURING CONSTRUCTION.
 - EXISTING CONCRETE PIPE SUPPORTS TO REMAIN, AND BE PROTECTED DURING CONSTRUCTION.
 - EXISTING TANK PIPING TO REMAIN AND BE PROTECTED DURING CONSTRUCTION.
 - EXISTING STORM INLET TO REMAIN AND BE PROTECTED DURING CONSTRUCTION.
 - EXISTING STORM LINE THAT WAS IDENTIFIED AS ABANDONED IN ORIGINAL CONSTRUCTION DRAWINGS FOR TANK AND BERM CONSTRUCTION. CONTRACTOR TO FIELD VERIFY IF LINE IS ACTIVE OR NOT. PROTECT IN PLACE DURING CONSTRUCTION.
 - EXISTING TANK TO REMAIN AND BE PROTECTED DURING CONSTRUCTION.
 - EXISTING STORM SEWER INLET STRUCTURE TO BE REMOVED, AND REPLACED WITH WATERTIGHT MANHOLE (MIN. 72" DIA.). EXCAVATION BACKFILLED.
 - EXISTING BERM LINER TO BE CUT AND PREPPED FOR NEW LINER ATTACHMENT BASE ON NEW LINER MANUFACTURE SPECIFICATIONS.
 - EXISTING BERM AND LINER SECTION TO BE REMOVED FOR EXPANSION SECTION.
 - EXISTING SECURITY FENCE TO BE REMOVED, NEW SECURITY FENCE TO BE PLACED BEFORE EXISTING FENCE DEMOLITION BEGINS TO MAINTAIN SECURE AREA, CONTRACTOR TO SUBMIT A PHASING SCHEDULE AND COORDINATE WITH BASE.
 - CONTRACTOR TO COORDINATE CAPPING/REMOVAL OF MONITORING WELL AND VALVE BOX WITH CONTRACTING OFFICER.

SHEET LEGEND			
SYMBOL/ABBREVIATION - DESCRIPTION			
WM	- WATER METER	FH	- FIRE HYDRANT
FDC	- FIRE DEPARTMENT CONNECTION	WELL	- WELL
MONWELL	- MONITOR WELL	WATER MANHOLE	- WATER MANHOLE
WV	- WATER VALVE	SPIGOT	- SPIGOT
SMH	- SANITARY MANHOLE	SCO	- SANITARY CLEANOUT
SV	- SANITARY VALVE	FMV	- FORCE MAIN VALVE
LP	- LIGHT POLE	GL	- GROUND LIGHT
GW	- GUY WIRE	TR	- TRANSFORMER
EM	- ELECTRIC METER	PP	- POWER POLE
EB	- ELECTRIC BOX	COMM BOX	- COMMUNICATIONS BOX
TEPE	- TELEPHONE PEDESTAL	TMH	- TELEPHONE MANHOLE
CPED	- CABLE TV PEDESTAL	CTV BOX	- CABLE TV BOX
GM	- GAS METER	GV	- GAS VALVE
FC	- FILLER CAP	DI1	- DROP INLET 1
DI2	- DROP INLET 2	DI3	- DROP INLET 3
RD	- ROOF DRAIN	SC	- CATCH BASIN
STMA	- STORM MANHOLE	YDI	- YARD DROP INLET
FES	- FARED-END SECTION	PE	- PIPE END (CONTINUES)
AC	- AC UNIT	MH	- MANHOLE
POST	- POST	BOL	- BOLLARD
WITPOST	- WITNESS POST	BORING	- BORING
SIGN	- SIGN	MB	- MAIL BOX
EVERGREEN TREES	- EVERGREEN TREES	BUSH/HEDGE	- BUSH/HEDGE
DECIDUOUS	- DECIDUOUS	WOODS LINE	- WOODS LINE
WOODED	- WOODED		

CURB AND GUTTER	
CONCRETE	
PAVEMENT	
BRICK	
GRAVEL	
FENCE	
GUARDRAIL	
PROPERTY LINE	
RIGHT-OF-WAY LINE	
BUILDINGS	
TOP OF BANK	
TOP OF SLOPE	
OF DITCH	
OF SWALE	
WATER/HYDROGRAPHIC FEATURE	
STORM SEWER	
PIPE LABEL (SIZE, TYPE, ID)	
WATER LINE	
SANITARY SEWER	
PIPE LABEL (SIZE, TYPE, ID)	
UNDERGROUND CABLE	
OVERHEAD CABLE	
OHT	
OVERHEAD TELEPHONE	
UNDERGROUND FIBER OPTIC	
UNDERGROUND TELEPHONE	
UNDERGROUND GAS	
OVERHEAD ELECTRIC	
UNDERGROUND ELECTRIC	
FORCE MAIN	
STEAM LINE	
UNKNOWN	
UNDERGROUND UNKNOWN UTILITY	
UNDERGROUND TRAFFIC CONTROL	
LIMITS OF DISTURBANCE	
SILT FENCE	

Scale: 1:10'

0 10 20 FEET

DEM0 PLAN NORTH

DATE	1/28/26
DESCRIPTION	FINAL SET
MARK	

APPROVED

FOR COMMANDER NAVFAC

ACTIVITY BILL BOUNDS DLA

CATISFACTORY TO DATE: 14 JAN 2026

SG	PAE	RB
----	-----	----

PM/DM W. WITHAM, P.E.

BRANCH MANAGER W. WITHAM, P.E.

CHIEF ENGINEER/ARCH-J. MILLER, P.E.

FIRE PROTECTION N/A

NAVFAC FACILITIES ENGINEERING SYSTEMS COMMAND - MID-ATLANTIC

NAVAL STATION - NORFOLK

NORFOLK, VIRGINIA

LP-38 BERM RECERTIFICATION REPAIR

DEM0 PLAN NORTH

CD100

DRAWING NO. 12940913

SHEET 9 OF 19

DRAWING REVISION: 14 SEP 2023

DEMO PLAN NORTH

0 10 20 FEET

SCALE:	
EPROJECT NO.:	1766588
CONSTR. CONTR. NO.	N40085-22-D-0039
NAVFAC DRAWING NO.	12940914
SHEET 10	OF 19
CD101	
DRAWFORM REVISION: 14 SEP 2023	

FILE NAME: P:\Projects\2024\21297-24020 NAVFAC Midant LP-38 Berm Recert\500-000\591-Civil\231848_ESPC PLAN.dwg LAYOUT NAME: EC-100 PLOTTED: Wednesday, February 11, 2026 - 9:58am USER: amore



- # EPSC KEY NOTES:**
- NOTE: NOT ALL KEYNOTES APPLY TO EACH SHEET
1. PROPOSED CONSTRUCTION SITE GATE.
 2. CONSTRUCTION FENCE TO TIE INTO AND CONTINUE FROM EXTENTS OF EXISTING SECURITY FENCE DEMO. CONTRACTOR TO PLACE CONSTRUCTION FENCE IN SUCH A MANNER THAT WILL NOT DAMAGE OR IMPACT THE EXISTING SECURITY FENCE THAT COULD COMPROMISE THE SECURE AREA. REF. DRAWING C-500.
 3. MAINTAIN STORM INLET PROTECTION FOR STORM WATER INLET UNTIL CONSTRUCTION ON STRUCTURE AND PIPE IS COMPLETE. REFER TO VDOT DETAILS 113.09 AND 113.10

SITE BMP PLAN

THE PHASES LISTED BELOW AND CONTROLS SHOWN ON PLANS ARE A GENERAL OVERVIEW AND MAY BE ADJUSTED IN THE FIELD DUE TO CONSTRUCTION ACTIVITIES AND CONSTRUCTION MEANS AND METHODS.

PHASE I - BMP PLAN (CLEARING & GRUBBING; DEMOLITION). ERECT EROSION CONTROL MEASURE (SILT FENCE) ALONG THE DOWN SLOPE SIDE OF THE PROJECT PERIMETER. INSTALL INLET PROTECTION AT DOWN SLOPE STORM SEWER STRUCTURES (WHERE APPLICABLE). CONTRACTOR MAY MARKUP NEW LOCATION AND DATE THE CHANGE ON A PAPER COPY OF THE BMP PLAN ONSITE.

PHASE II - BMP PLAN (EARTHWORK). DURING THIS PHASE OF CONSTRUCTION ACTIVITIES, SILT FENCE MUST BE REMOVED, RELOCATED, AND OR ADDED AS CONSTRUCTION PROGRESSES. CONTRACTOR MAY MARKUP NEW LOCATION AND DATE THE CHANGE ON A PAPER COPY OF THE BMP PLAN ONSITE. MAINTAIN THE SILT FENCE ALONG THE DOWN SLOPE PROJECT PERIMETER.

PHASE III - BMP PLAN (SUBSTANTIAL SITE CONSTRUCTION COMPLETION). MAINTAIN THE SILT FENCE ALONG THE DOWN SLOPE PROJECT PERIMETER, WHERE NORMAL SEED AND MULCH COVER METHODS ARE INEFFECTIVE, OR ON SLOPES 3:1 OR STEEPER, INSTALL EROSION CONTROL MATTING, 6 MONTH LONGEVITY. MAINTAIN INLET PROTECTION. CONTRACTOR MAY MARKUP NEW LOCATION AND DATE THE CHANGE ON A PAPER COPY OF THE BMP PLAN ONSITE. FINISH CONSTRUCTION AND SEED AND MULCH COVER A 10' BUFFER AROUND NEW WORK AFTER CONCRETE HAS BEEN INSTALLED.

PHASE IV - BMP PLAN (FINAL CONSTRUCTION). REMOVE SILT FENCE AND OTHER CONTROLS THAT ARE INHIBITING FINAL CONSTRUCTION AND ARE NO LONGER NEEDED. CONTRACTOR MAY MARKUP NEW LOCATION (AND/OR AREAS OF BMPs REMOVED) AND DATE THE CHANGE ON A PAPER COPY OF THE BMP PLAN ONSITE. FINALLY, REMOVE ANY REMAINING EROSION CONTROL MEASURES AND PROTECT ANY REMAINING DISTURBED AREAS WITH SEED AND MULCH COVER.

ALL ESC/BMP DETAILS MUST REFER TO VDOT DETAILS.

NPDES NOI INFORMATION	
AREA OF SITE: 0.80 ACRES	
AREA OF DISTURBANCE: 0.45 ACRES	
SHEET LEGEND	
GRAPHIC	DESCRIPTION
	SILT FENCE REFER TO VDOT 113.07
	LIMITS OF DISTURBANCE
	CONSTRUCTION LIMIT
	INLET PROTECTION
	6" CHAIN LINK CONSTRUCTION FENCE
	CONSTRUCTION ENTRANCE
	LINER
	TEMPORARY SLOPE STABILIZATION: REFER TO VDOT DETAIL 113.02
	PERMANENT SLOPE STABILIZATION: REFER TO VDOT DETAIL 113.05
	INLET PROTECTION: REFER TO VDOT DETAIL 113.10

EPSC PLAN NORTH

1:10'

0 10 20 FEET

DATE	1/28/26
FINAL SET	
DESCRIPTION	
MARK	

Schmidt PRIME
911 West Garden Street
Pensacola, Florida 32502
P: 850-438-0050
schmidtconsultinggroup.com

APPROVED

FOR COMMANDER NAVFAC 2-1-26

ACTIVITY: BILL BOUNDS, DLA

SATISFACTORY TO DATE: 14 JAN 2025

SG	PAE	RB
----	-----	----

PM/DM: W. WITHAM, P.E.
BRANCH MANAGER: W. WITHAM, P.E.
CHIEF ENG/ARCH: J. MILLER, P.E.
FIRE PROTECTION: N/A

NAVAL FACILITIES ENGINEERING SYSTEMS COMMAND
NAVAL FACILITIES ENGINEERING SYSTEMS COMMAND - MID-ATLANTIC
MIDANT DC CORE
NAVAL STATION SHIPYARD
NAVAL STATION - NORFOLK
NORFOLK, VIRGINIA


LP-38 BERM RECERTIFICATION REPAIR

EPSC PLAN NORTH

EC-100

DRAWING REVISION: 14 SEP 2023

FILE NAME: P:\Projects\2024\21297-24020 NAVFAC Midant LP-38 Berm Recert\500-CAD\591-Civil\231848_EPSC PLAN.dwg LAYOUT NAME: EC-101 PLOTTED: Wednesday, February 11, 2026 - 10:01am USER: emore

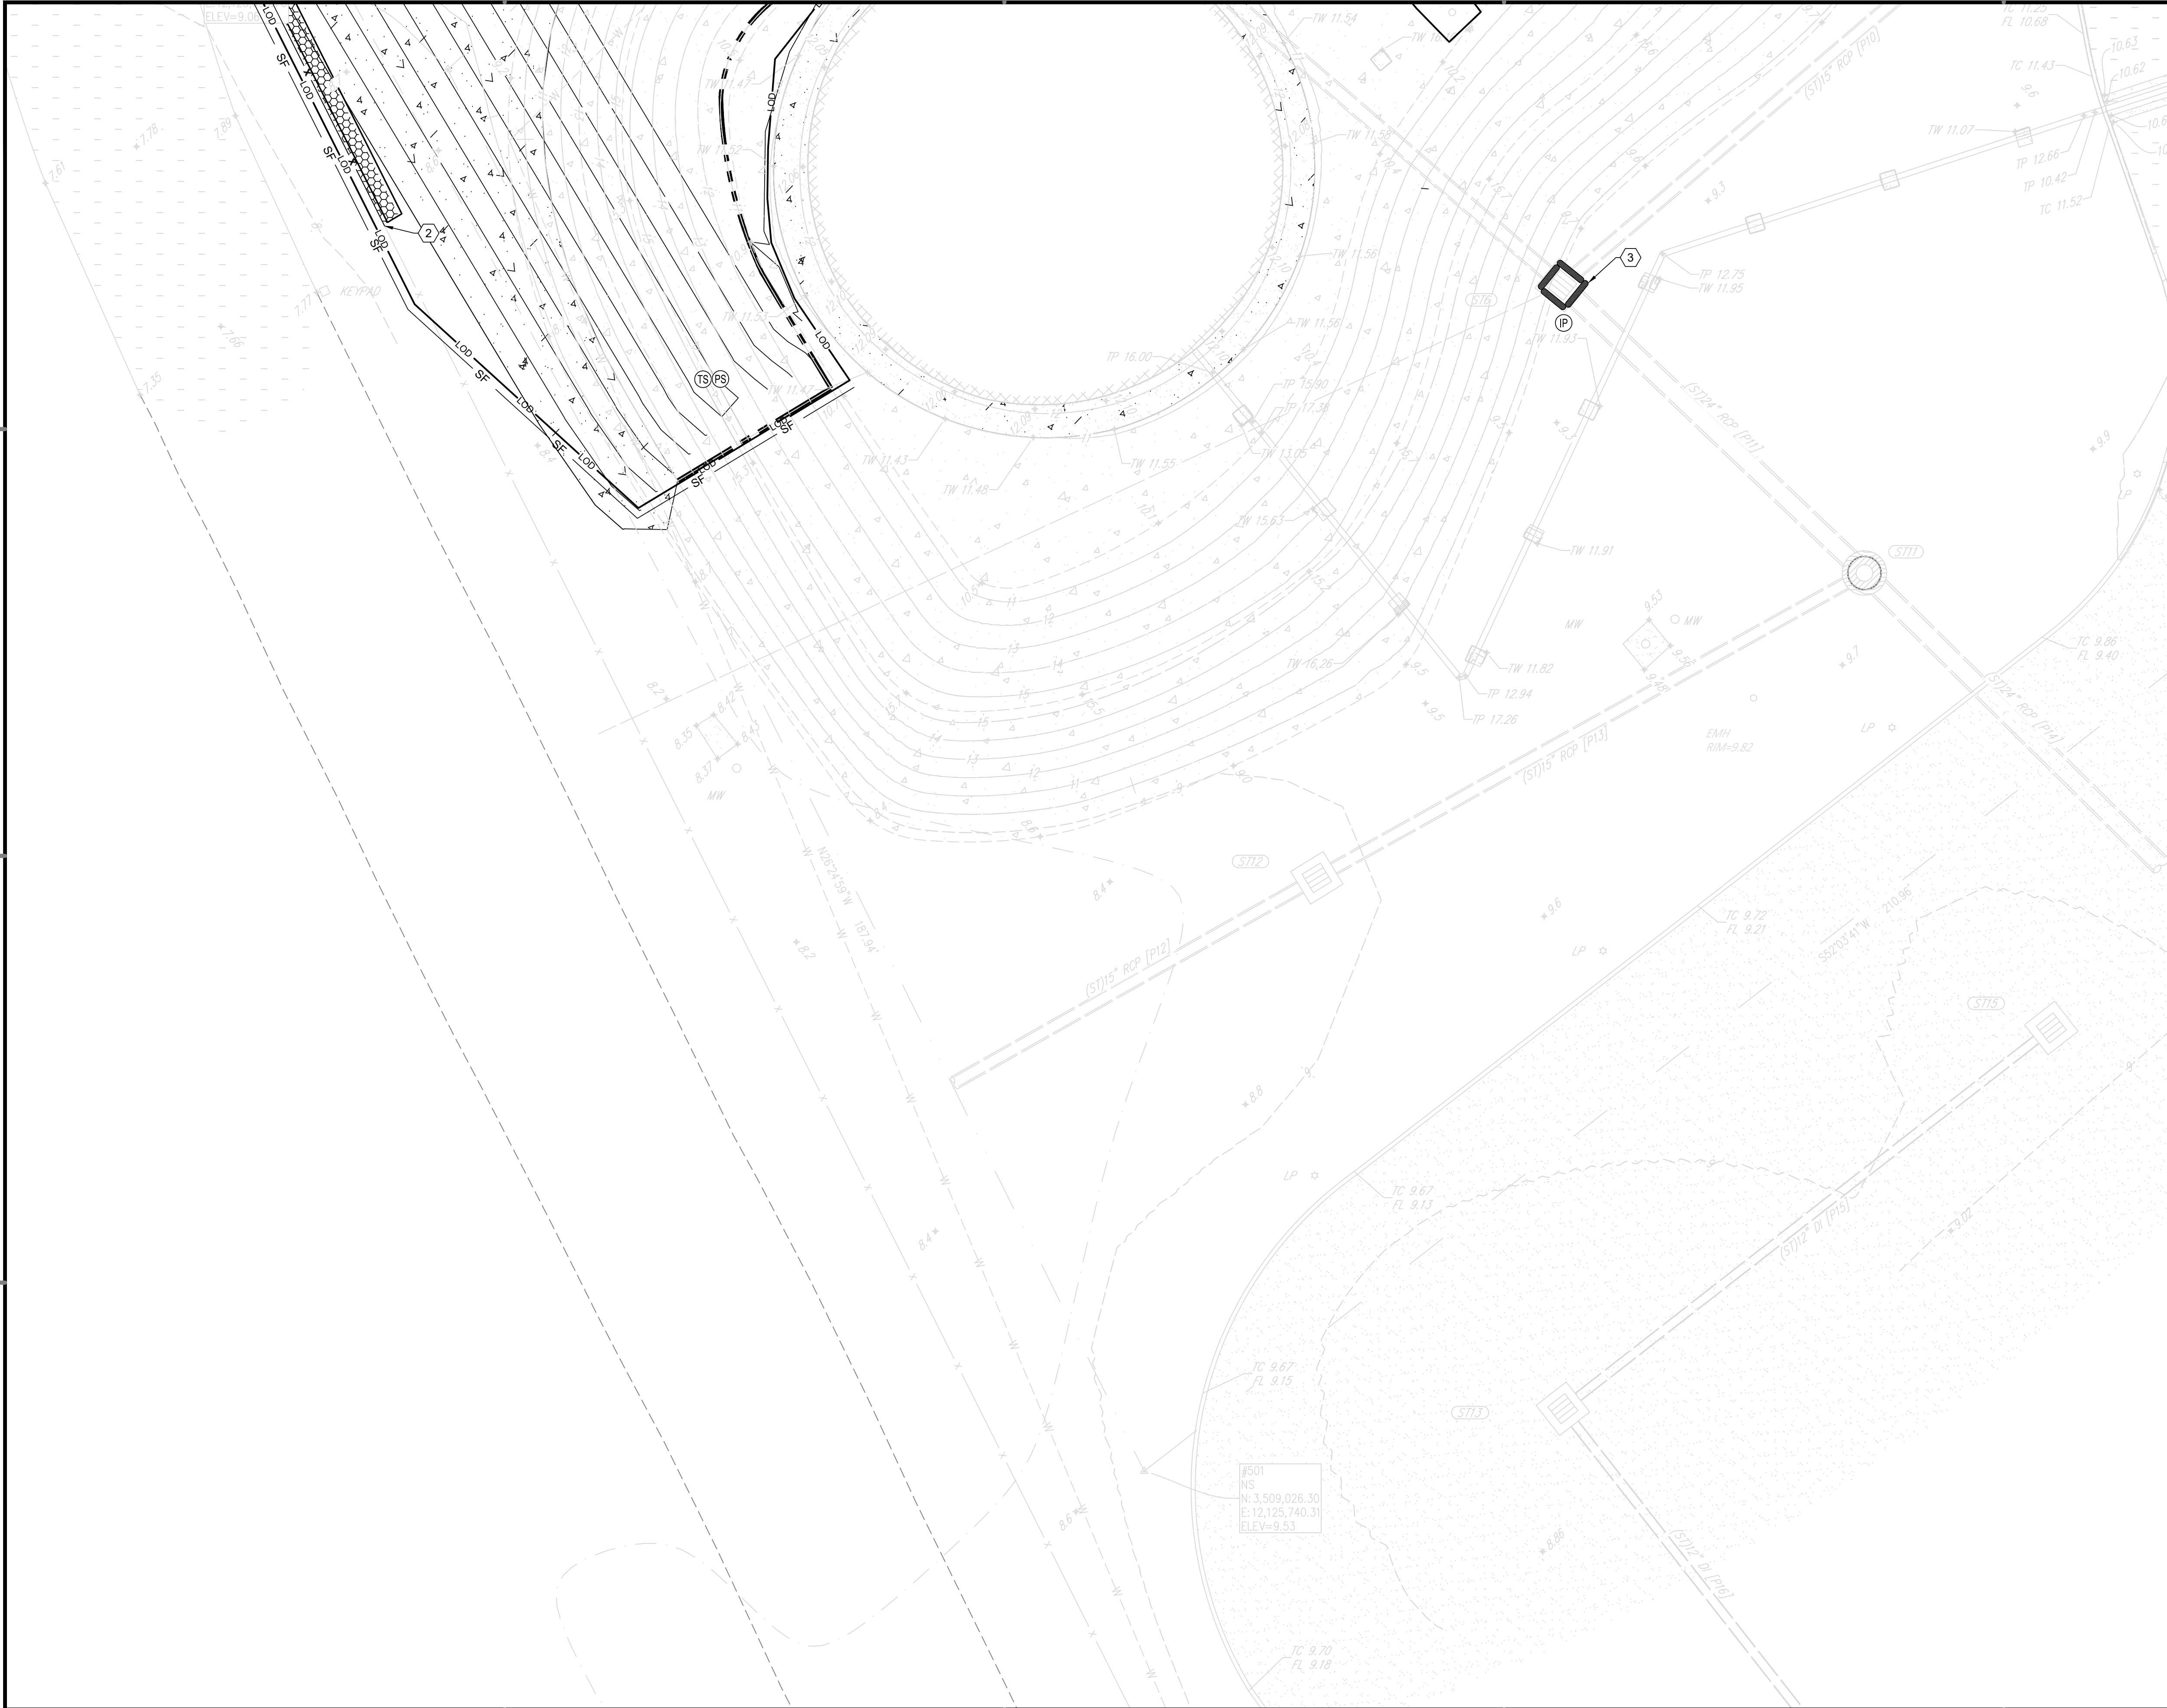

- # EPSC KEY NOTES:
- NOTE: NOT ALL KEYNOTES APPLY TO EACH SHEET
1.

PROPOSED CONSTRUCTION SITE GATE.
2.

CONSTRUCTION FENCE TO TIE INTO AND CONTINUE FROM EXTENTS OF EXISTING SECURITY FENCE DEMO. CONTRACTOR TO PLACE CONSTRUCTION FENCE IN SUCH A MANNER THAT WILL NOT DAMAGE OR IMPACT THE EXISTING SECURITY FENCE THAT COULD COMPROMISE THE SECURE AREA. REF DRAWING C-500.
3.

MAINTAIN STORM INLET PROTECTION FOR STORM WATER INLET UNTIL CONSTRUCTION ON STRUCTURE AND PIPE IS COMPLETE. REFER TO VDOT DETAILS 113.09 AND 113.10

EPSC GENERAL NOTES:

THE CONTRACTOR IS REQUIRED TO FURNISH A MINIMUM OF 6" TOPSOIL IN ANY LANDSCAPE / LAWN / AREAS DISTURBED BY CONSTRUCTION. IT IS THE CONTRACTOR'S RESPONSIBILITY TO DETERMINE THE AMOUNT OF TOPSOIL REQUIRED AND INCLUDE IT IN THE BID. TOPSOIL MUST BE INCIDENTAL TO CONTRACT.

SITE BMP PLAN

THE PHASES LISTED BELOW AND CONTROLS SHOWN ON PLANS ARE A GENERAL OVERVIEW AND MAY BE ADJUSTED IN THE FIELD DUE TO CONSTRUCTION ACTIVITIES AND CONSTRUCTION MEANS AND METHODS.

PHASE I - BMP PLAN (CLEARING & GRUBBING; DEMOLITION). ERECT EROSION CONTROL MEASURE (SILT FENCE) ALONG THE DOWN SLOPE SIDE OF THE PROJECT PERIMETER. INSTALL INLET PROTECTION AT DOWN SLOPE STORM SEWER STRUCTURES (WHERE APPLICABLE). CONTRACTOR MAY MARKUP NEW LOCATION AND DATE THE CHANGE ON A PAPER COPY OF THE BMP PLAN ONSITE.

PHASE II - BMP PLAN (EARTHWORK). DURING THIS PHASE OF CONSTRUCTION ACTIVITIES, SILT FENCE MUST BE REMOVED, RELOCATED, AND OR ADDED AS CONSTRUCTION PROGRESSES. CONTRACTOR MAY MARKUP NEW LOCATION AND DATE THE CHANGE ON A PAPER COPY OF THE BMP PLAN ONSITE. MAINTAIN THE SILT FENCE ALONG THE DOWN SLOPE PROJECT PERIMETER.

PHASE III - BMP PLAN (SUBSTANTIAL SITE CONSTRUCTION COMPLETION). MAINTAIN THE SILT FENCE ALONG THE DOWN SLOPE PROJECT PERIMETER. WHERE NORMAL SEED AND MULCH COVER METHODS ARE INEFFECTIVE, OR ON SLOPES 3:1 OR STEEPER, INSTALL EROSION CONTROL MATTING, 6 MONTH LONGEVITY. MAINTAIN INLET PROTECTION. CONTRACTOR MAY MARKUP NEW LOCATION AND DATE THE CHANGE ON A PAPER COPY OF THE BMP PLAN ONSITE. FINISH CONSTRUCTION AND SEED AND MULCH COVER A 10' BUFFER AROUND NEW WORK AFTER CONCRETE HAS BEEN INSTALLED.

PHASE IV - BMP PLAN (FINAL CONSTRUCTION). REMOVE SILT FENCE AND OTHER CONTROLS THAT ARE INHIBITING FINAL CONSTRUCTION AND ARE NO LONGER NEEDED. CONTRACTOR MAY MARKUP NEW LOCATION (AND/OR AREAS OF BMPS REMOVED) AND DATE THE CHANGE ON A PAPER COPY OF THE BMP PLAN ONSITE. FINALLY, REMOVE ANY REMAINING EROSION CONTROL MEASURES AND PROTECT ANY REMAINING DISTURBED AREAS WITH SEED AND MULCH COVER.

ALL ESC/BMP DETAILS MUST REFER TO VDOT DETAILS.

APPROVED

FOR COMMANDER NAVFAC 8-1-26

ACTIVITY: BIL BOUNDS, OLA

SATISFACTORY TO DATE: 14 JAN, 2026

SG

PAC

RB

PM/DM W. WITHAM, P.E.

BRANCH MANAGER W. WITHAM, P.E.

CHIEF ENG/ARCH-J. MILLER, P.E.

FIRE PROTECTION N/A

NPDES NOI INFORMATION	
AREA OF SITE: 0.80 ACRES	
AREA OF DISTURBANCE: 0.45 ACRES	
SHEET LEGEND	
GRAPHIC	DESCRIPTION
	SILT FENCE
	REFER TO VDOT 113.07
	LIMITS OF DISTURBANCE
	CONSTRUCTION LIMIT
	INLET PROTECTION
	6' CHAIN LINK CONSTRUCTION FENCE
	CONSTRUCTION ENTRANCE
	LINER
	TEMPORARY SLOPE STABILIZATION: REFER TO VDOT DETAIL 113.02
	PERMANENT SLOPE STABILIZATION: REFER TO VDOT DETAIL 113.05
	INLET PROTECTION: REFER TO VDOT DETAIL 113.10

A1

EPSC PLAN NORTH

1:10'

0

10

20

FEET

1/26/26

DATE

FINAL SET

DESCRIPTION

MARK

DESCRIPTION

APPROVED

FOR COMMANDER NAVFAC 8-1-26

ACTIVITY: BIL BOUNDS, OLA

SATISFACTORY TO DATE: 14 JAN, 2026

SG

PAC

RB

PM/DM W. WITHAM, P.E.

BRANCH MANAGER W. WITHAM, P.E.

CHIEF ENG/ARCH-J. MILLER, P.E.

FIRE PROTECTION N/A

NAVFACILITIES ENGINEERING SYSTEMS COMMAND

NAVAL FACILITIES ENGINEERING SYSTEMS COMMAND - MID-ATLANTIC

MIDANT DC CORE

NAVAL STATION SHIPYARD

NAVAL STATION - NORFOLK

NORFOLK, VIRGINIA

LP-38 BERM RECERTIFICATION REPAIR

EPSC PLAN SOUTH

SCALE:

PROJECT NO.: 1766588

CONSTR. CONTR. NO. N40085-22-D-0039

NAVFAC DRAWING NO. 12940916

SHEET 12 OF 19

EC-101

DRAWFORM REVISION: 14 SEP 2023


DRAWFORM REVISION: 14 SEP 2023



0 10 20 FEET

DRAWFORM REVISION: 14 SEP 2023

FILE NAME: P:\Projects\2024\21297-24020 NAVFAC Midant LP-38 Berm Recert\500-C00\591-C00\231848 SITE PLAN.dwg LAYOUT NAME: C-101 PLOTTED: Wednesday, February 11, 2026 - 10:07am USER: cmoore

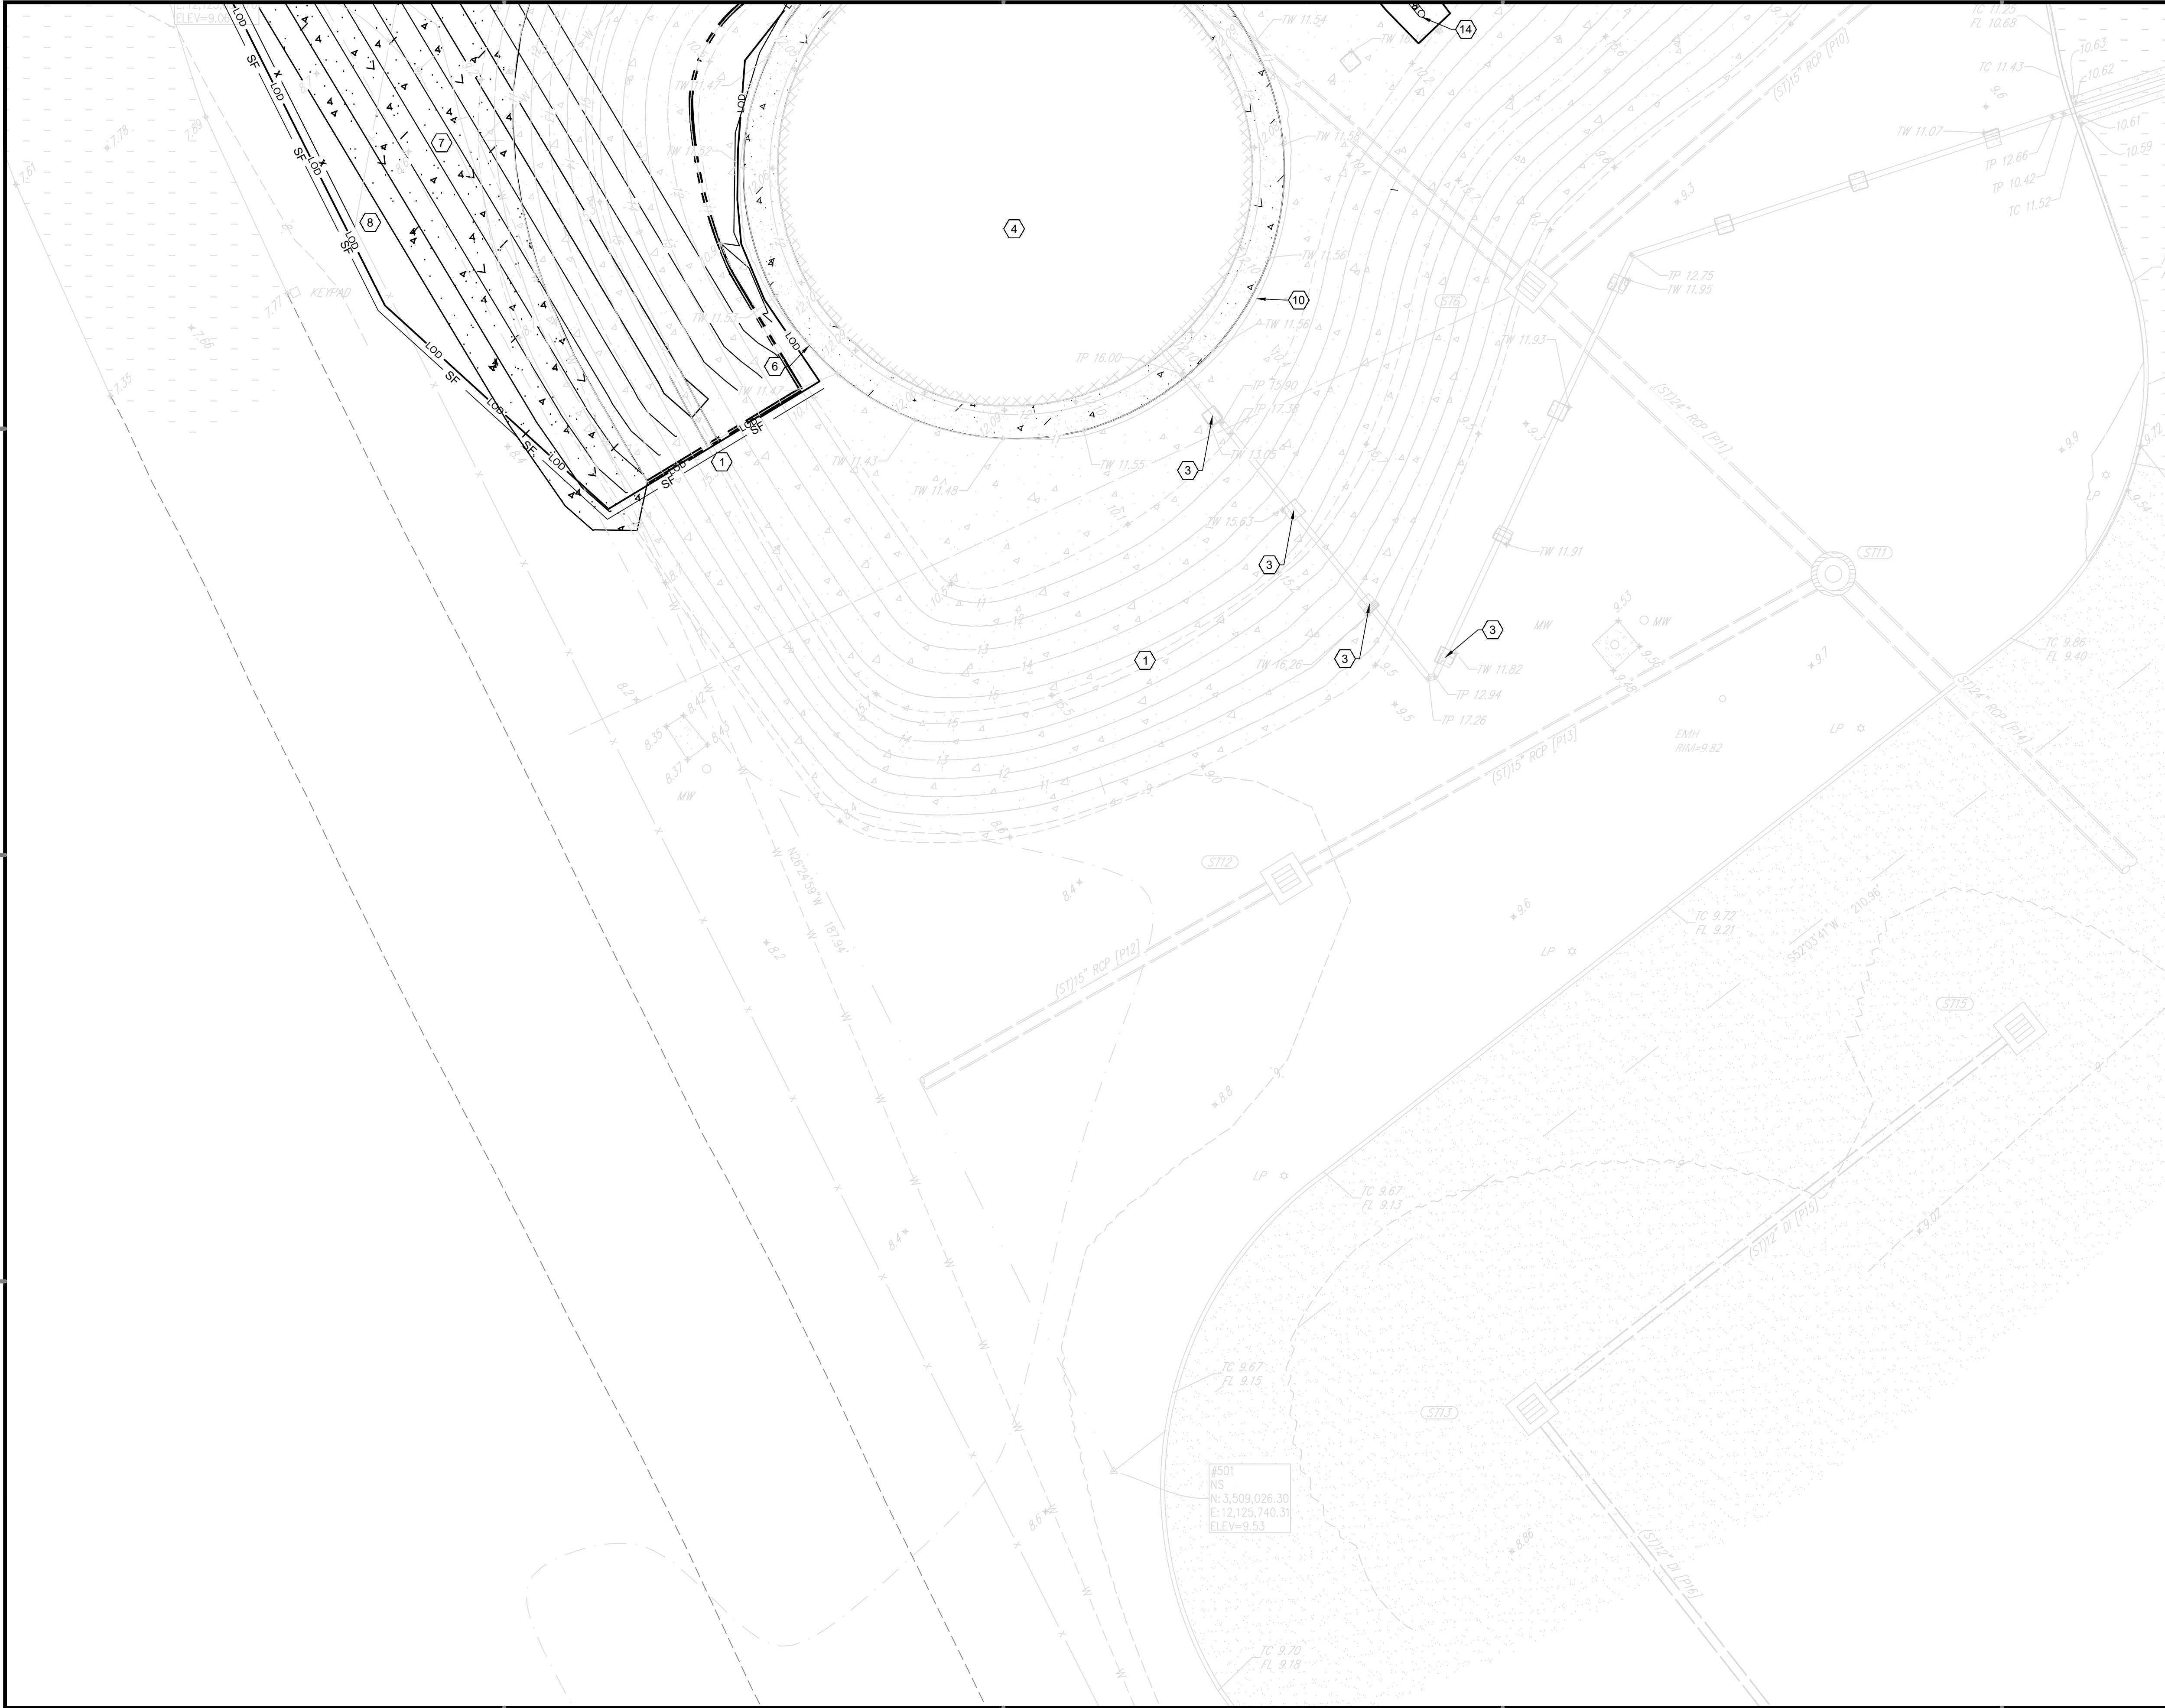

- ### KEY NOTES:
- EXISTING BERM VOLUME TO BE ADJUSTED AND BERM SIZE TO INCREASED TO MEET REQUIREMENTS FOR TANK CONTAINMENT
 - EXISTING ACCESS STAIR FOR BERM TO REMAIN, AND PROTECTED DURING CONSTRUCTION.
 - EXISTING CONCRETE PIPE SUPPORTS TO REMAIN, AND BE PROTECTED DURING CONSTRUCTION.
 - EXISTING TANK TO REMAIN AND PROTECTED DURING CONSTRUCTION.
 - WATERTIGHT STORM SEWER STRUCTURE TO BE ADDED TO REPLACE EXISTING STORM WATER INLET STRUCTURE (MIN. 72" DIA.).
 - REPAIR TANK CONC. APRON. AND TANK FOUNDATION BY REMOVING APPROX. 80 L.F. OF DETERIATING CONC. SEALANT AND REPLACING WITH NEW. SCRAPE CLEAN PRIOR TO RESEALING.
 - EXISTING LINER TO BE EXTENDED FOR BERM AND INTERIOR CONTAINMENT AREA, INCREASE AND ARMORED WITH AGGREGATE (MATCH EXISTING) REFER TO NOTE ON THIS SHEET AND LINER DETAIL.
 - NEW SECURITY FENCE TO BE CONSTRUCTED BEFORE EXISTING SECURITY FENCE IS REMOVED TO MAINTAIN SECURE AREA, CONTRACTOR TO SUBMIT A PHASING SCHEDULE AND COORDINATE WITH RELEVANT BASE MANAGERS. SEE DETAILS ON C-500.
 - EXISTING STORM SEWER STRUCTURE TO BE MODIFIED, SEE "SPRING BOX" DETAIL (REF. C3/CG501).
 - GROUT VOID CONTINUOUSLY BENEATH THE EXISTING APRON. CUT CLEAN JOINTS AND FILL AND SEAL WITH JOINT SEALANT (220 L.F.).
 - CONTRACTOR TO CLEAN OUT CLOGGED CATCH BASINS AND PIPING OF ALL DEBRIS TO PROVIDE FULL FLOW FUNCTION. AFTER COMPLETION, CONTRACTOR TO CCTV THE PIPES AND PROVIDE FOOTAGE TO THE OWNER/ENGINEER.
 - CONTRACTOR TO INSTALL FRENCH DRAIN WITH 4"Ø HDPE PIPING. REFER TO DETAIL C4/C-501.
 - GRAVEL FILL TO MATCH EXISTING (6" COMPACTED SAND AND 8" CRUSHED STONE TOPPING PER SPECIFICATIONS). SEE DETAIL C1/C-501.
 - HDPE CLEANOUT AND CAP.

- ### GENERAL NOTES:
- GROUT UNDER APRON (COMPLETELY FILL VOID) EXISTING ACCESS STAIR FOR BERM TO REMAIN, AND PROTECTED DURING CONSTRUCTION.
 - EXISTING CONCRETE PIPE SUPPORTS TO REMAIN, AND BE PROTECTED DURING CONSTRUCTION.
 - EXISTING TANK TO REMAIN AND PROTECTED DURING CONSTRUCTION.
 - REPAIR TANK CONCRETE UNDER APRON (COMPLETELY FILL UNDER VOID.)

SITE PLAN SOUTH

1:10'

0 10 20 FEET

DATE		1/28/26
FINAL SET		DESCRIPTION
MARK		

Schmidt PRIME
911 West Garden Street
Pensacola, Florida 32502
P: 850-438-0050
schmidtconsultinggroup.com

APPROVED

John M. S. M.

FOR COMMANDER NAVFAC 8-1-26

ACTIVITY: BILL BOUNDS, DLA

SATISFACTORY TO DATE: 14 JAN. 2026

SG	PAE	RB
----	-----	----

PM/DM: W. WITHAM, P.E.

BRANCH MANAGER: W. WITHAM, P.E.

CHIEF ENG/ARCH: J. MILLER, P.E.

FIRE PROTECTION: N/A

DEPARTMENT OF THE NAVY

NAVAL FACILITIES ENGINEERING SYSTEMS COMMAND

MIDANT DC CORE

NAVAL STATION SHIPYARD

NAVAL STATION - NORFOLK

NORFOLK, VIRGINIA

LP-38 BERM RECERTIFICATION REPAIR

SITE PLAN SOUTH

SCALE:

PROJECT NO.: 1766588

CONSTR. CONTR. NO.: N40085-22-D-0039


NAVFAC DRAWING NO.: 12940919

SHEET 15 OF 19

CS101

DRAWFORM REVISION: 14 SEP 2023

FILE NAME: P:\Projects\2024\21297-24020 NAVFAC Midant LP-38 Berm Recert\500-500\591-Civil\231848 GRADING PLAN.dwg PLOTTED: Wednesday, February 11, 2026 - 10:14am USER: amore


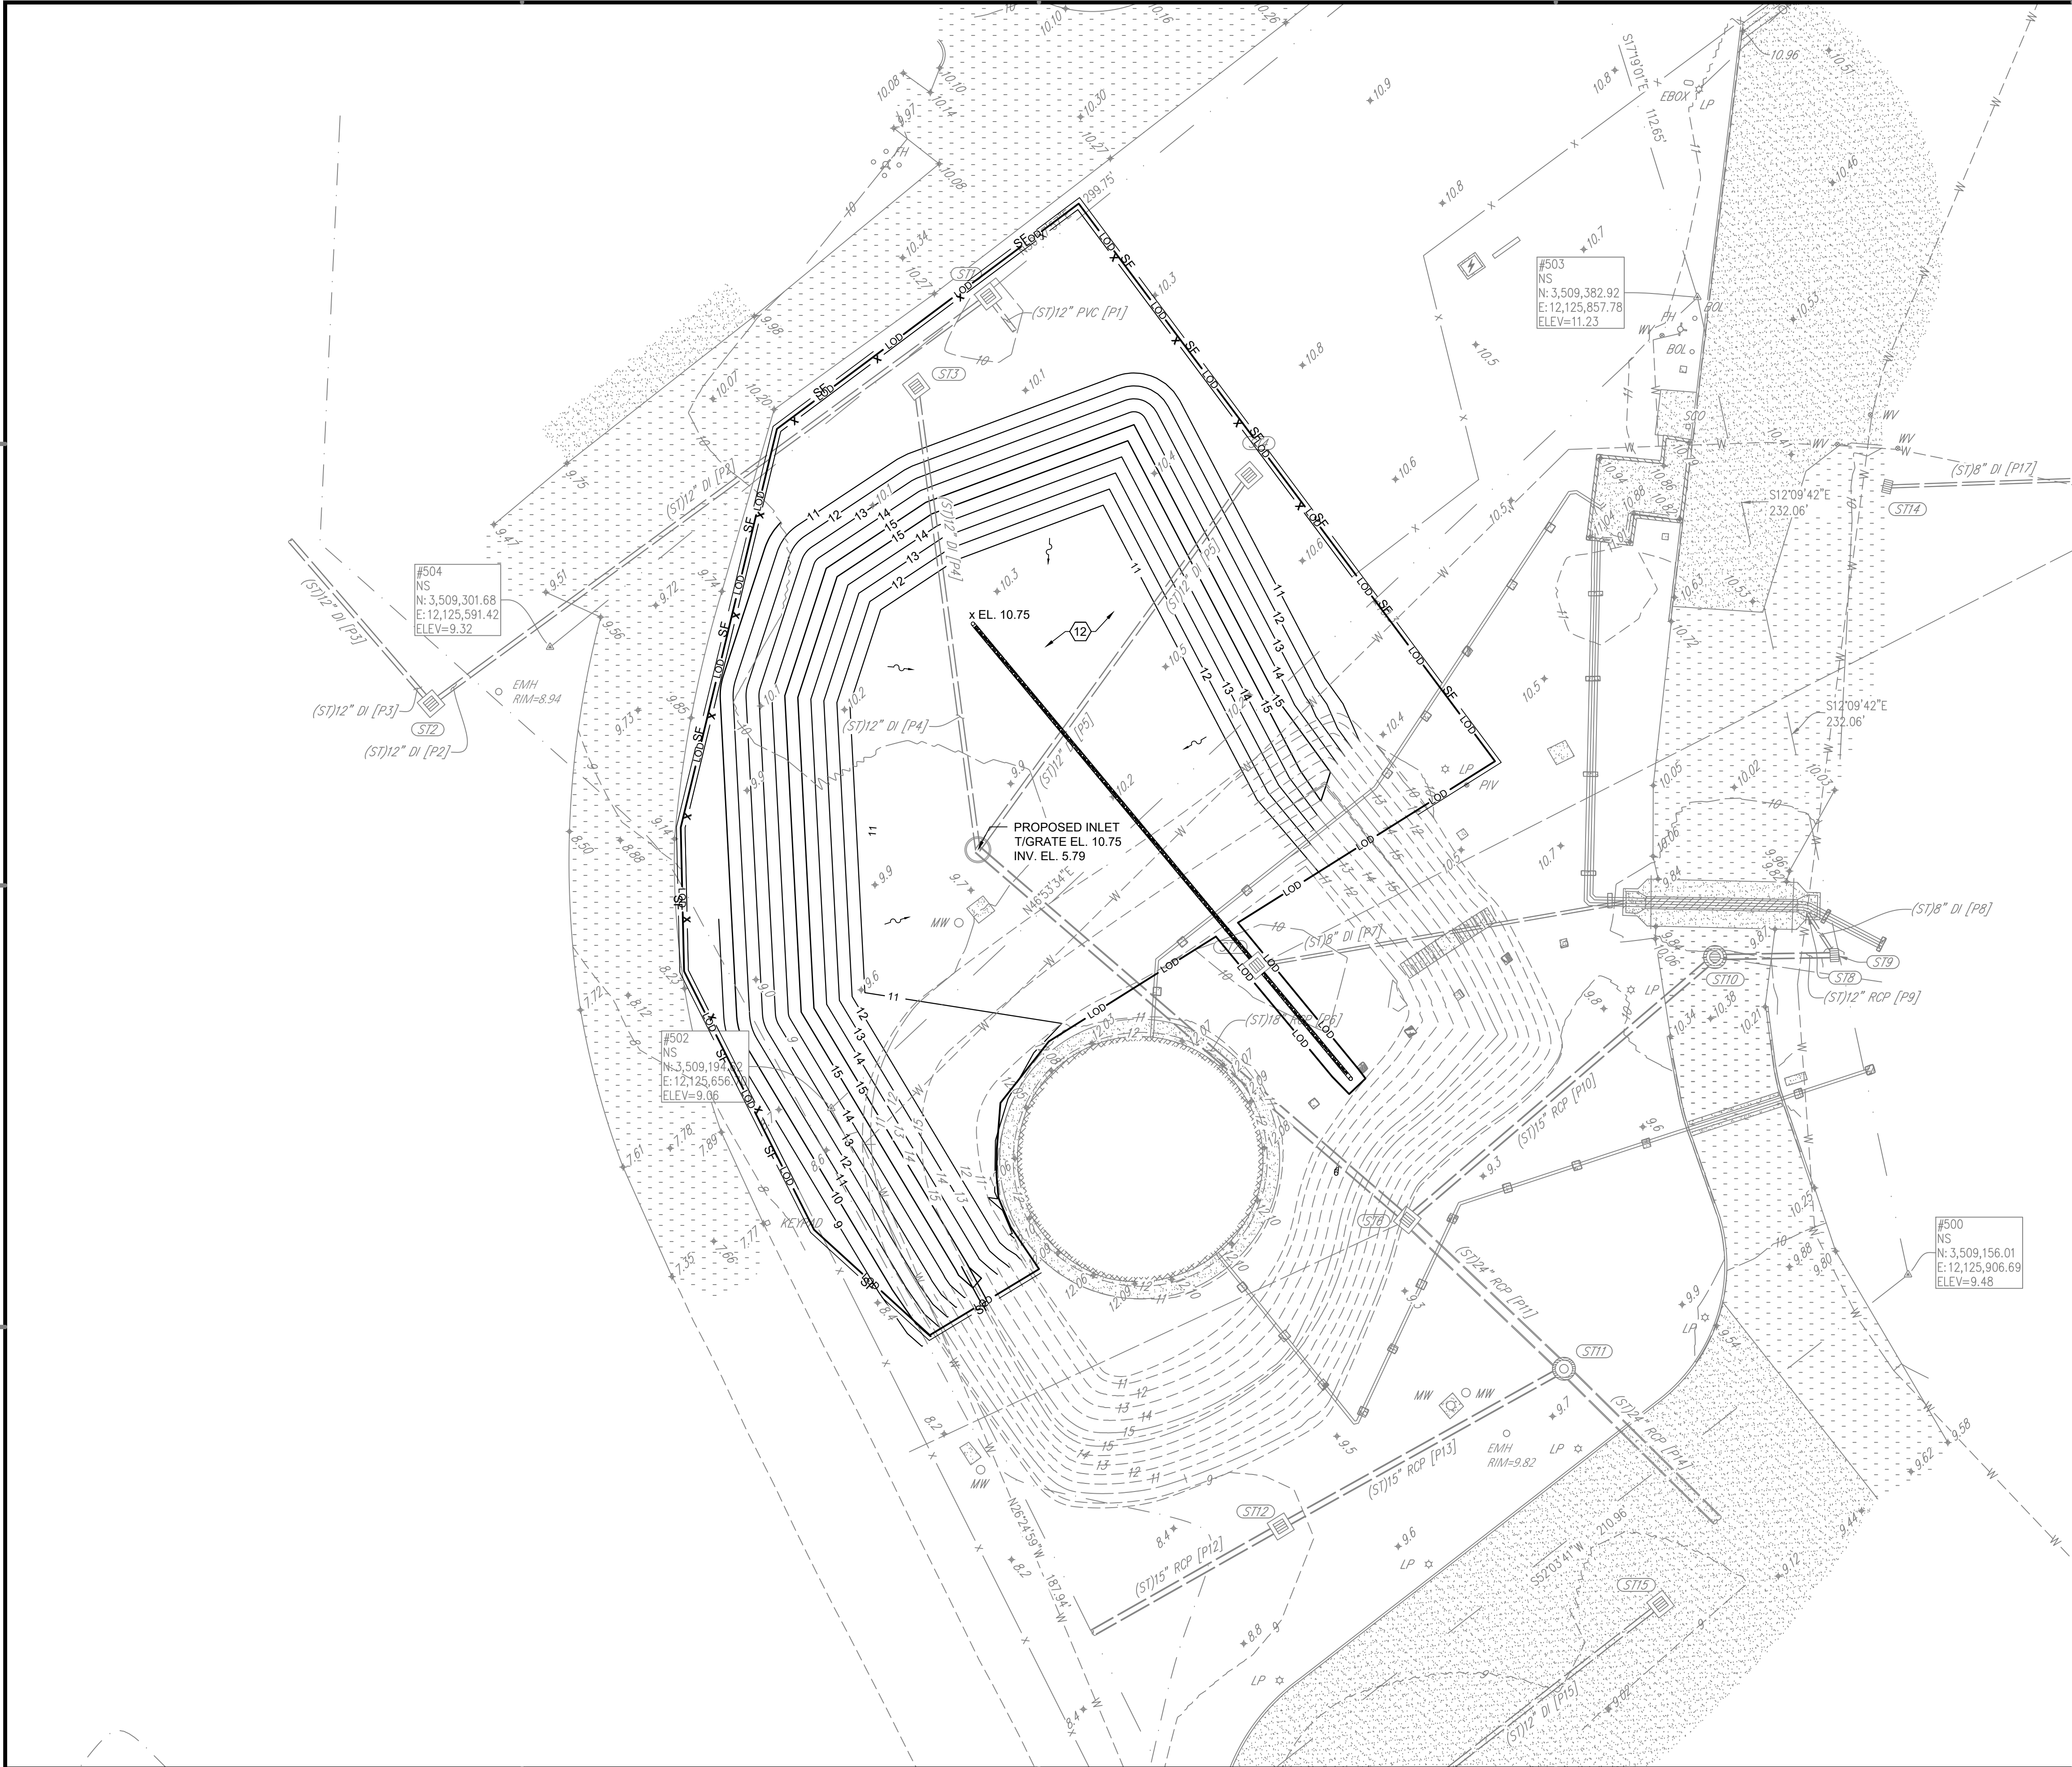


GRADING NOTES:

- IT IS THE CONTRACTOR'S RESPONSIBILITY TO PERFORM ANY ADDITIONAL GEOTECHNICAL EXPLORATIONS TO DETERMINE THE TOPSOIL, UNSUITABLE MATERIAL, ROCK LIMITS, OR ANY INFORMATION PERTINENT TO PERFORM THE CONSTRUCTION. ALL THE NECESSARY EARTH WORK SHOULD BE INCLUDED AS PART OF THE BID. VARIOUS GEOLOGICAL SITUATIONS ENCOUNTERED NATURAL OR MAN MADE MUST BE THE RESPONSIBILITY OF THE CONTRACTOR AND THE REMEDIAL MEASURES WOULD BE THE CONTRACTOR'S RESPONSIBILITY AND ANY UNCLASSIFIED EXCAVATION IS CONSIDERED INCIDENTAL TO CONSTRUCTION.
- WHEN MATERIALS WHICH ARE UNSUITABLE FOR SUBGRADE, OR OTHER ROADWAY PURPOSES, OCCUR WITHIN THE LIMITS OF STREET CONSTRUCTION, THE CONTRACTOR MUST BE REQUIRED TO EXCAVATE SUCH MATERIAL BELOW THE GRADE SHOWN ON PLANS, AND THE AREAS SO EXCAVATED MUST BE BACKFILLED WITH APPROVED SUITABLE MATERIALS. THE EXTENT OF UNDERCUTTING AND BACKFILLING MUST BE DETERMINED BY THE CONTRACTOR'S GEOTECHNICAL ENGINEER.
- THE CONTRACTOR MUST REMOVE ALL UNSUITABLE MATERIALS FROM THE SITE, BURYING OF UNSUITABLE MATERIAL ON SITE MUST NOT BE PERMITTED. ALL EXCAVATED MATERIALS MUST BECOME PROPERTY OF THE CONTRACTOR AND MUST BE REMOVED FROM THE SITE. ALL UNSUITABLE MATERIALS REMOVED FROM THE SITE MUST BE DISPOSED OF ACCORDING TO STATE AND FEDERAL LAWS. UNSUITABLE MATERIALS INCLUDE FROZEN SOIL, SOFT UNSTABLE MATERIAL AND MISCELLANEOUS FILL OR ANY MATERIAL CLASSIFIED AS UNSUITABLE BY THE CONTRACTOR'S GEOTECHNICAL ENGINEER.
- DURING WET AND RAINY PERIODS, AERATION IS NECESSARY FOR FILL MATERIALS TO ACHIEVE THE REQUIRED MOISTURE CONTENT. DURING DRY PERIODS, WATER MAY NEED TO BE ADDED TO ACHIEVE THE PROPER MOISTURE CONTENT FOR COMPACTION. WHEN CLAY SOILS ARE ENCOUNTERED IT MAY BE NECESSARY FOR AERATION DURING THE SUMMER PERIODS AS WELL. BORROW MATERIAL MUST NOT BE PLACED OVER FROZEN/SATURATED MATERIALS OR UNSUITABLE MATERIAL. DUST MUST BE CONTROLLED BY WATERING.
- THE CONTRACTOR IS REQUIRED TO FURNISH A MINIMUM OF 6" TOPSOIL IN ANY LANDSCAPE/LAWN/AREAS DISTURBED BY CONSTRUCTION. IT IS THE CONTRACTOR'S RESPONSIBILITY TO DETERMINE THE AMOUNT OF TOPSOIL REQUIRED AN INCLUDE IT IN THE BID, TOPSOIL MUST BE INCIDENTAL TO CONTRACT.
- COMPACTION TESTS MUST BE PERFORMED BY A QUALIFIED GEOTECHNICAL ENGINEER, THE COST FOR SAME MUST BE BORNE EXCLUSIVELY BY THE CONTRACTOR. THE CONTRACTOR'S GEOTECHNICAL ENGINEER MUST BE ON-SITE DURING FILLING OPERATIONS AND THE CONTRACTOR MUST FOLLOW ALL RECOMMENDATIONS REGARDING FILL PLACEMENT.
- CUT SLOPES (EXCAVATION) MUST BE CONSTRUCTED AS SHOWN ON THE PLANS NOT EXCEEDING A MAXIMUM OF 3:1 (HORIZONTAL / VERTICAL).
- FILL SLOPES (EMBANKMENT) MUST BE CONSTRUCTED AS SHOWN ON THE PLANS NOT EXCEEDING A MAXIMUM OF 2.5:1 (HORIZONTAL / VERTICAL).
- THE CONTRACTOR'S GEOTECHNICAL ENGINEER MAY REQUIRE ADDITIONAL WORK BASED ON ACTUAL FIELD CONDITIONS. THE CONTRACTOR MUST FOLLOW ALL GUIDELINES SET FORTH BY THE CONTRACTOR'S GEOTECHNICAL ENGINEER.
- ALL AREAS THAT ARE TO BE SEEDED OR SODDED MUST BE BOX GRADED REMOVING ROCK, CLODDED DIRT, STUMPS, ROOTS AND AND ALL OBJECTS LARGER THAN 2 INCHES.
- GRAVEL FILL TO MATCH EXISTING (6" COMPACTED SAND AND 8" CRUSHED STONE TOPPING PER SPECIFICATIONS), SEE DETAIL C4/C-501.
- CONTRACTOR TO PROVIDE SEEING AS SOON AS POSSIBLE. SEEING USED MUST BE A TYPE THAT WILL NOT EFFECT THE BIRD POPULATION IN A NEGATIVE MANNER.

BASIN VOLUME:

- PROPOSED BASIN VOLUME AT ELEVATION 14.25 WITH VOLUME OF TANK AT ELEVATION 14.25 (SEE VOLUME DIAGRAM 1 FOR MORE INFORMATION):
 - 70,603 FT³
- EXISTING BASIN VOLUME AT ELEVATION 14.25 WITH TANK COMPLETELY EMPTY(SEE VOLUME DIAGRAM 2 FOR MORE INFORMATION):
 - 62,310 FT³ ~ 124% OF TANK VOLUME

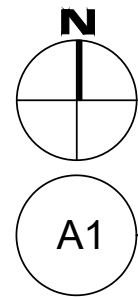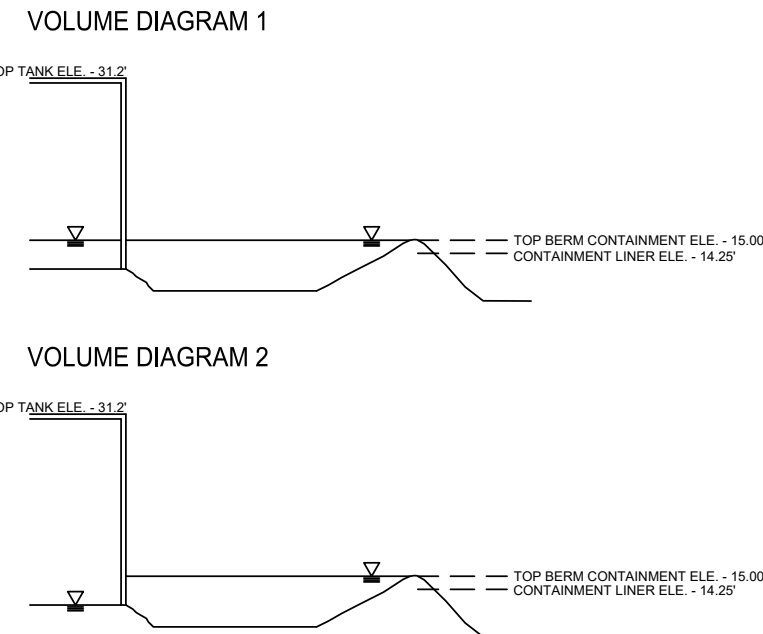

GRADING PLAN NORTH



DATE 1/28/26	
FINAL SET	DESCRIPTION
MARK	
APPROVED FOR COMMANDER NAVFAC 8-1-26	
ACTIVITY: BILL BOUNDS, DLA	
SATISFACTORY TO DATE: 14 JAN 2026	
SG	PAE
PM/DM: W. WITHAM, P.E.	
BRANCH MANAGER: W. WITHAM, P.E.	
CHIEF ENGINEER/ARCH: J. MILLER, P.E.	
FIRE PROTECTION: N/A	
DEPARTMENT OF THE NAVY NAVAL FACILITIES ENGINEERING SYSTEMS COMMAND - MID-ATLANTIC NAVAL STATION - NORFOLK NAVAL STATION SHIPYARD NORFOLK, VIRGINIA	
LP-38 BERM RECERTIFICATION REPAIR GRADING PLAN	
SCALE: PROJECT NO.: 1766588 CONSTR. CONTR. NO.: N40085-22-D-0039 NAVFAC DRAWING NO.: 12940920 SHEET 16 OF 19	
CG110 DRAWFORM REVISION: 14 SEP 2023	


FILE NAME: P:\Projects\2024\21297-24020 NAVFAC Midlant LP-38 Berm Recert\500-501-Civil\231848_SITE PLAN.dwg LAYOUT NAME: C-501 PLOTTED: Wednesday, February 11, 2026 - 10:11am USER: cmoore

D

C


B

A

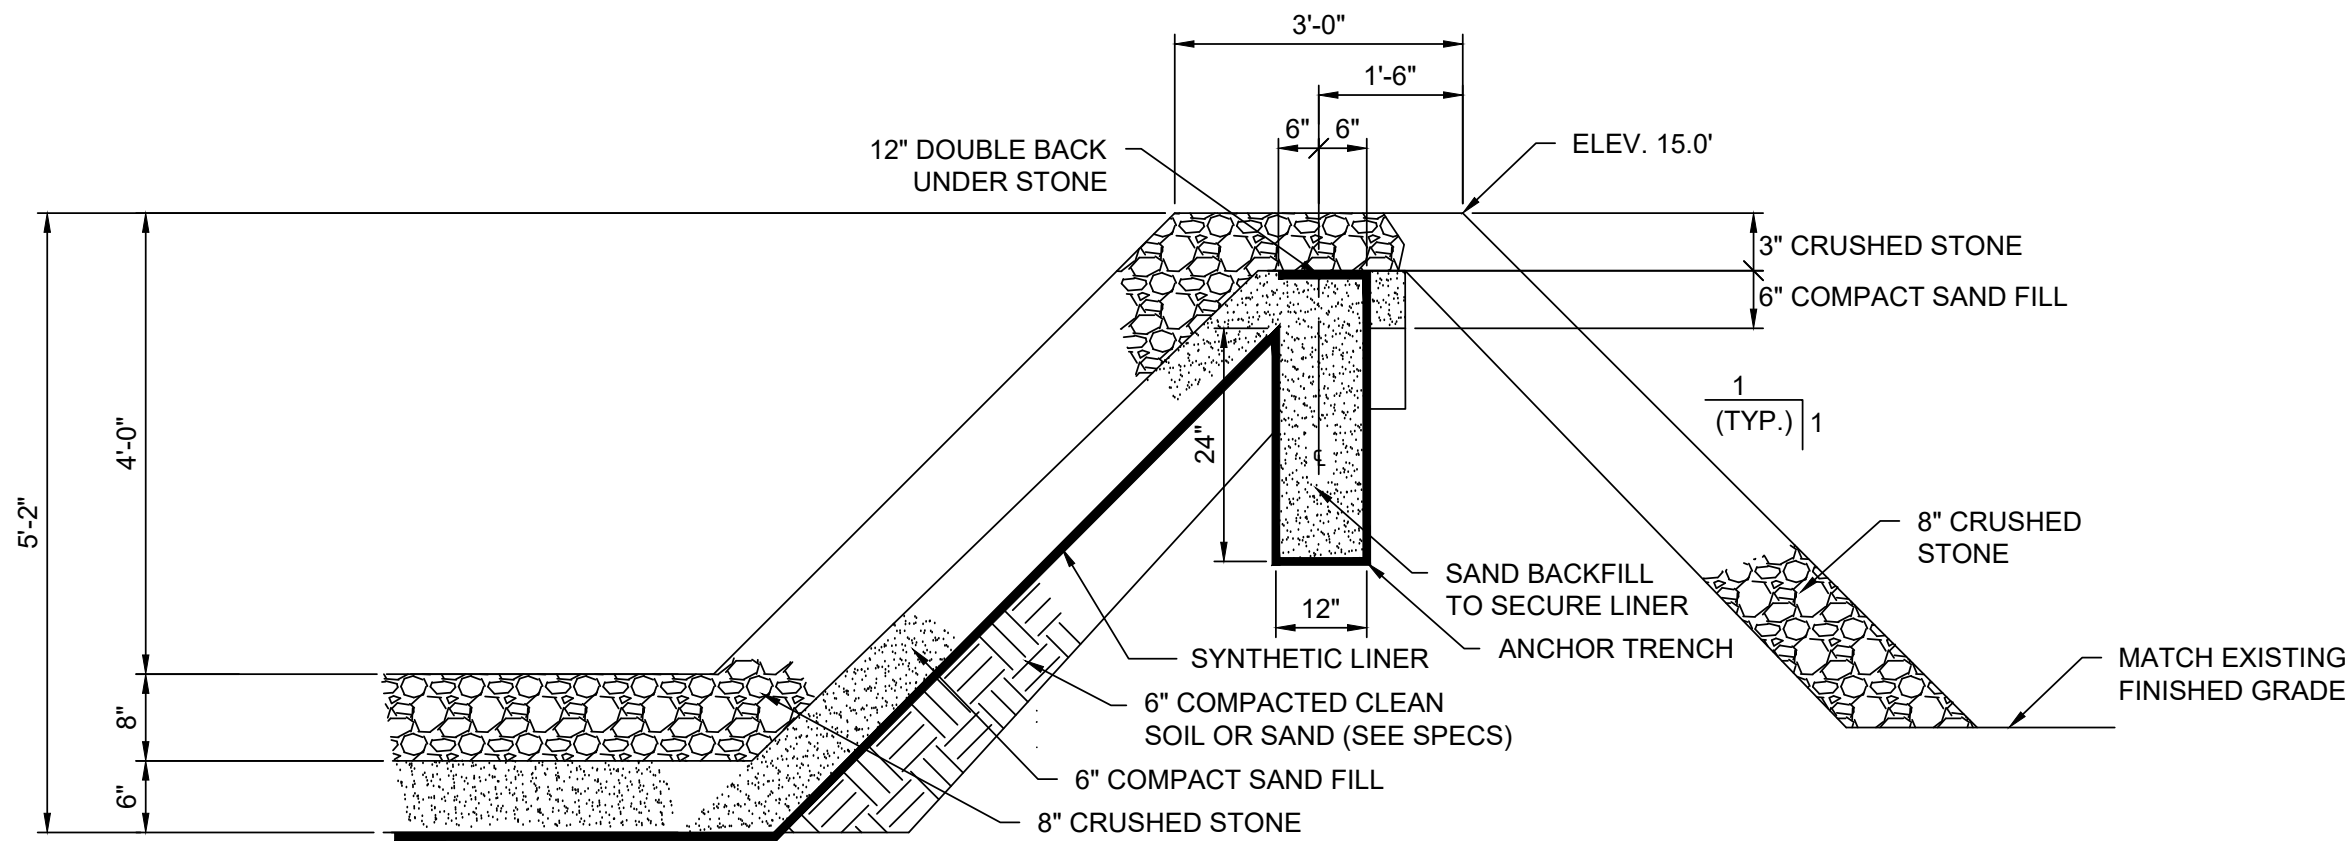


CONTAINMENT BERM DETAIL

NOT TO SCALE
C1
CS100

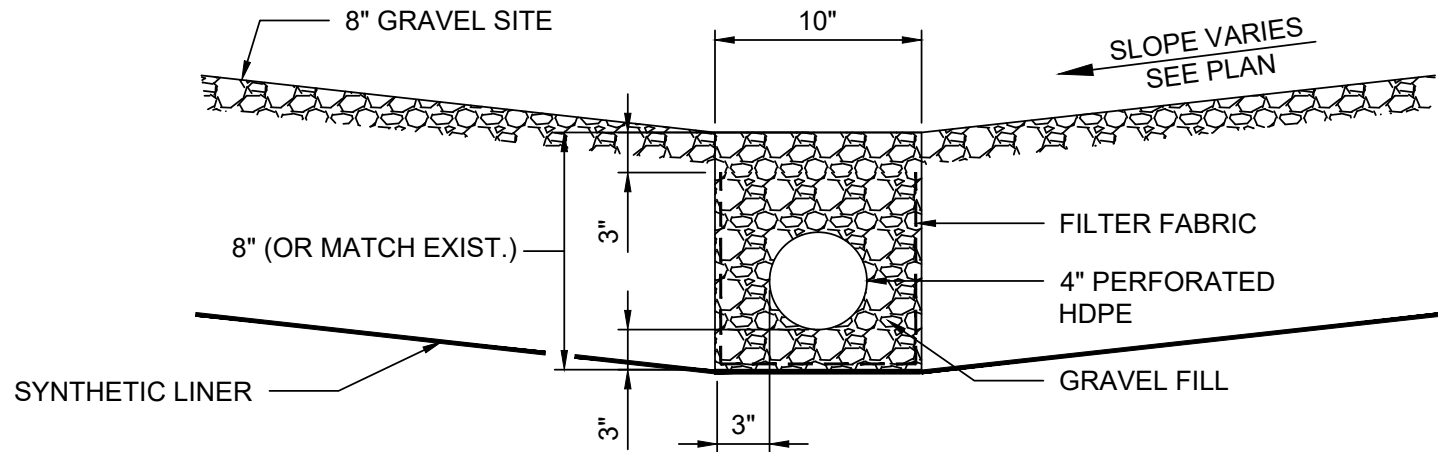

FRENCH DRAIN DETAIL


NOT TO SCALE
C4
CS100

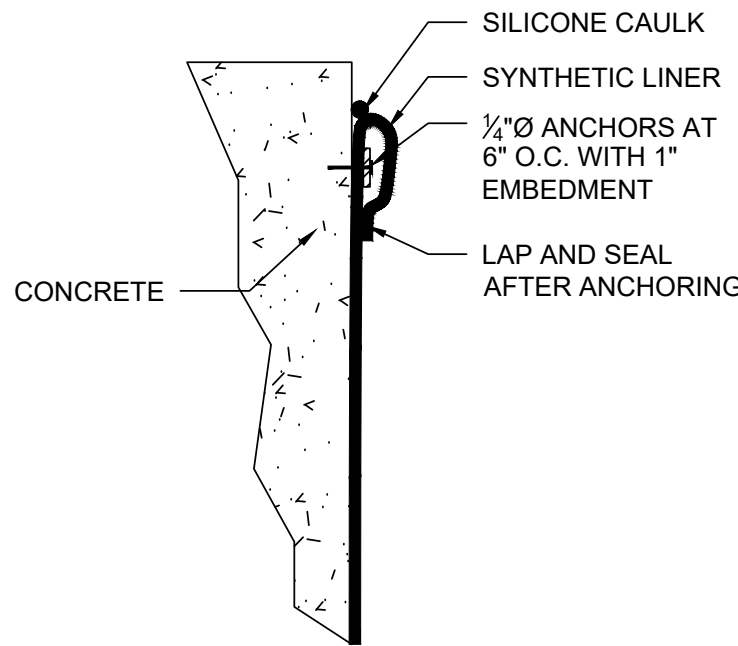

MEMBRANE ANCHORAGE DETAIL

NOT TO SCALE
B1
CS100

DATE	1/28/26
MARK	
DESCRIPTION	
FINAL SET	

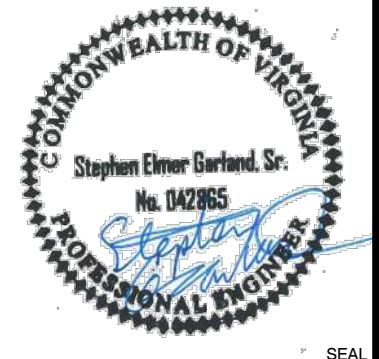



Schmidt PRIME
951 West Garden Street
Pensacola, Florida 32502
P: 850-438-0050
schmidtconsultinggroup.com

AVE INFO

APPROVED
John M. S. Miller
FOR COMMANDER NAVFAC
8-1-26

ACTIVITY: BILL BOUNDS, DLA

SATISFACTORY TO DATE: 14 JAN 2026

SG	PAE	RB
----	-----	----

PM/DM: W. WITHAM, P.E.

BRANCH MANAGER: W. WITHAM, P.E.

CHIEF ENGINEER/ARCH: J. MILLER, P.E.

FIRE PROTECTION: N/A

DEPARTMENT OF THE NAVY
NAVAL FACILITIES ENGINEERING SYSTEMS COMMAND
MIDLANT DC CORE
NAVAL STATION SHIPYARD

NAVAL FACILITIES ENGINEERING SYSTEMS COMMAND - MID-ATLANTIC
NAVAL STATION - NORFOLK
NORFOLK, VIRGINIA

LP-38 BERM RECERTIFICATION REPAIR

TYPICAL PERSONNEL GATE & BOLLARD DETAIL

SCALE:	
PROJECT NO.:	1766588
CONSTR. CONTR. NO.:	N40085-22-D-0039
NAVFAC DRAWING NO.:	12940922
SHEET 18	OF 19
C-501	

DRAWFORM REVISION: 14 SEP 2023

