




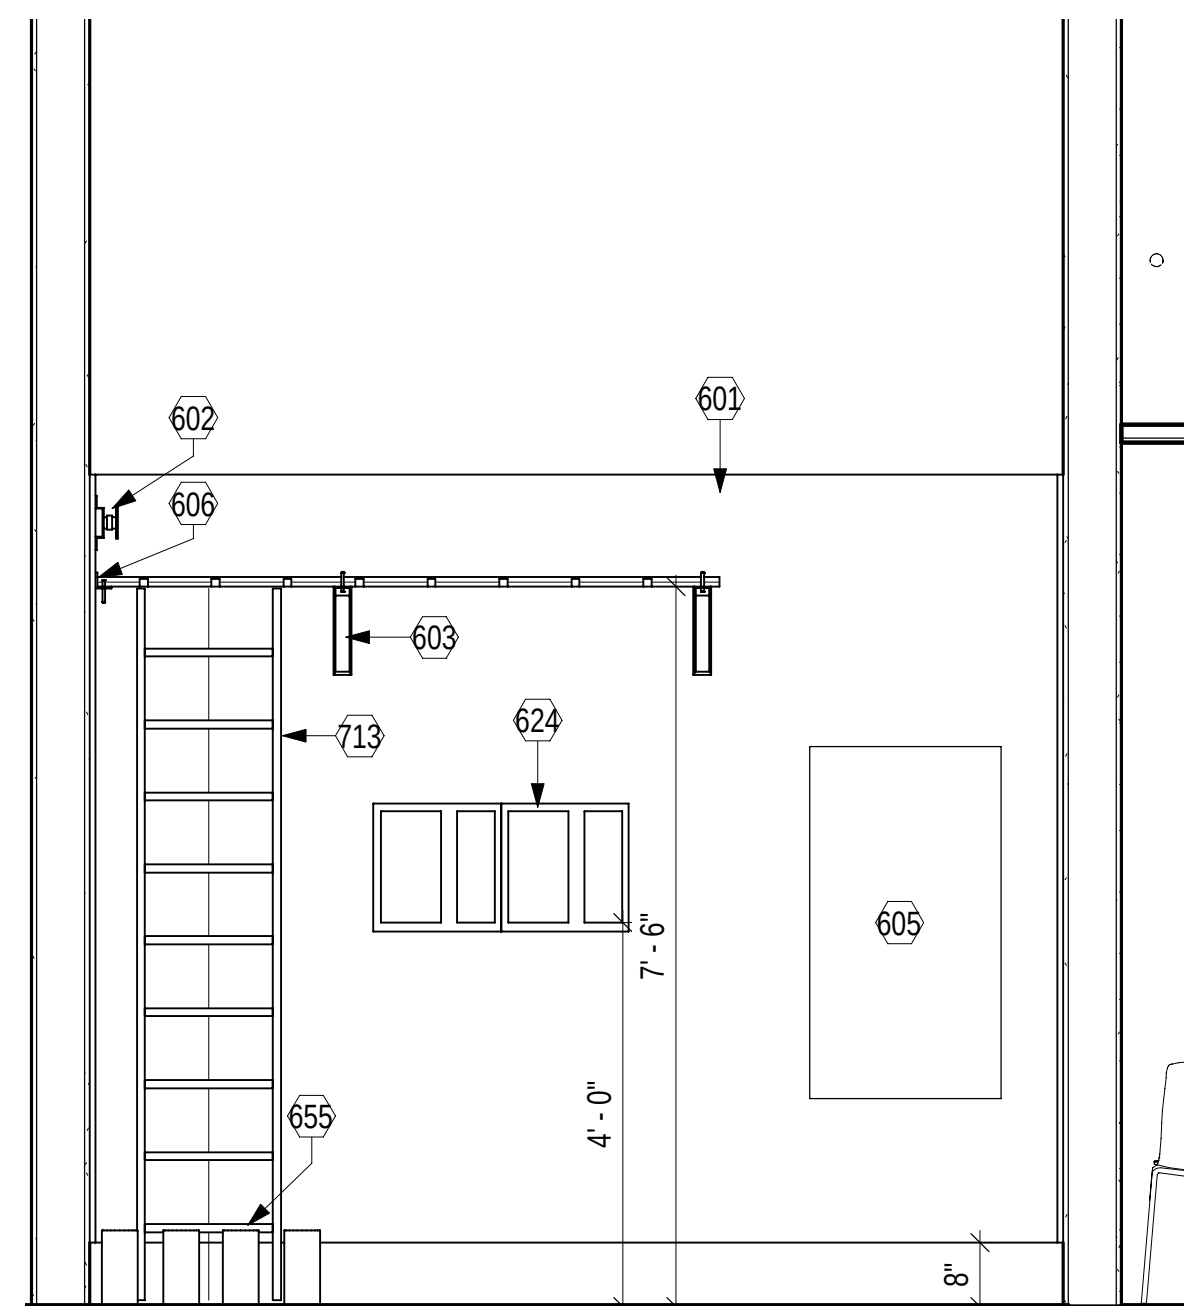


C1 TELECOM 105 - SOUTH ELEVATION
1/2" = 1'-0" (T-102)

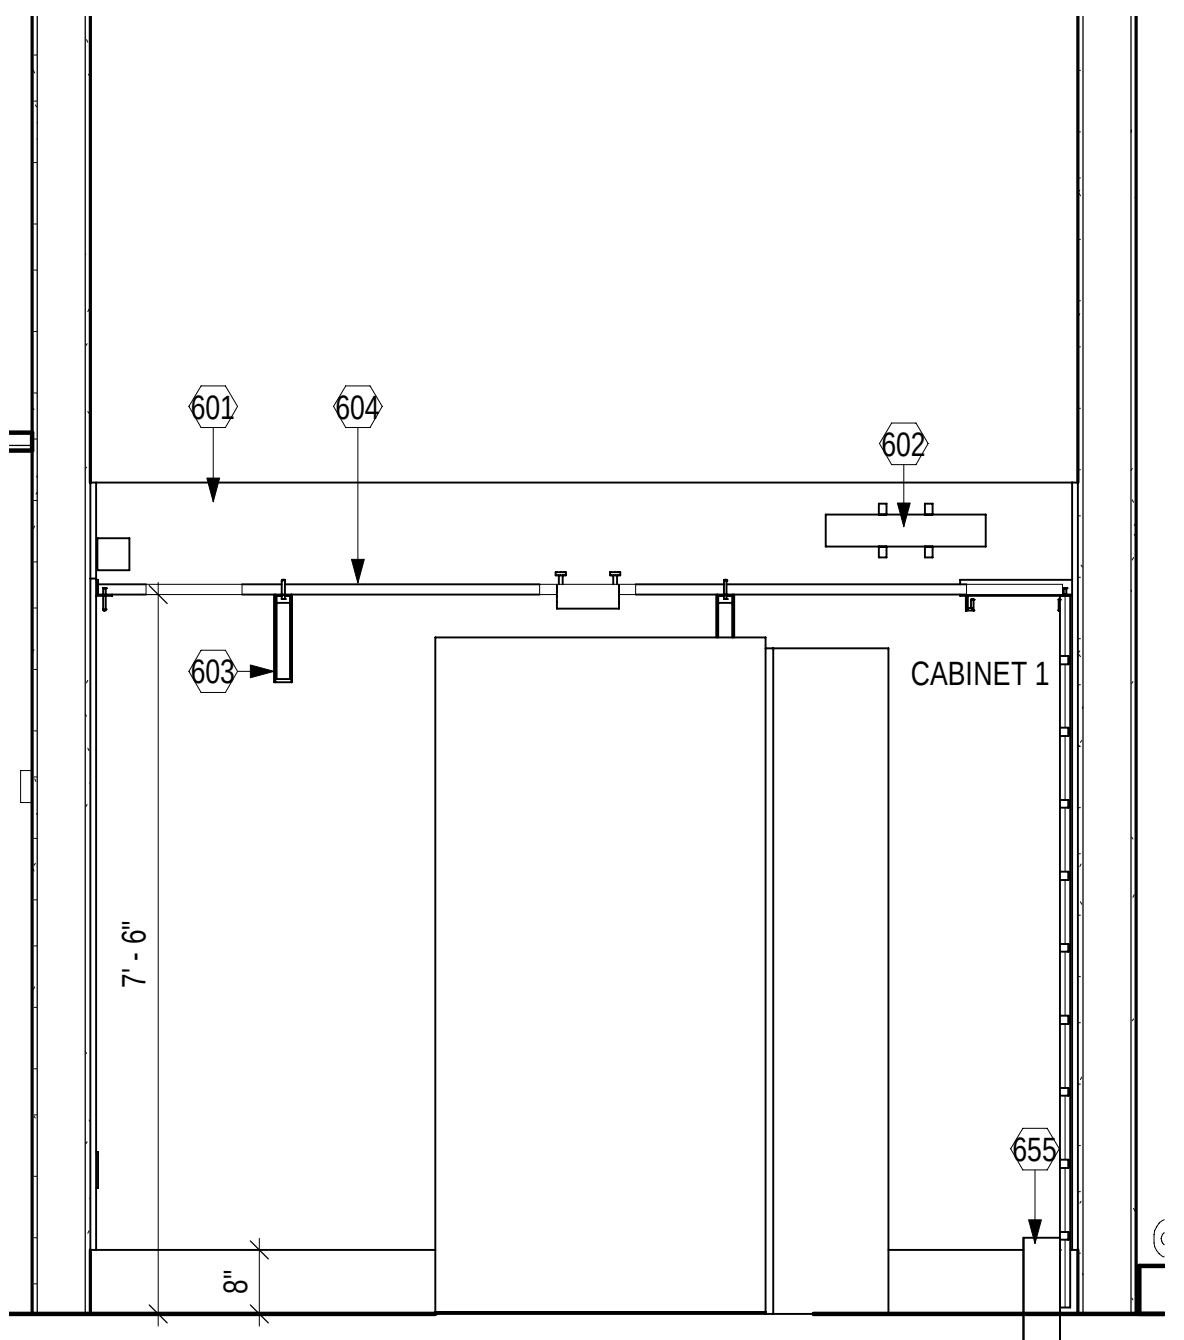

A1 TELECOM 105 EAST ELEVATION
1/2" = 1'-0" (T-102)

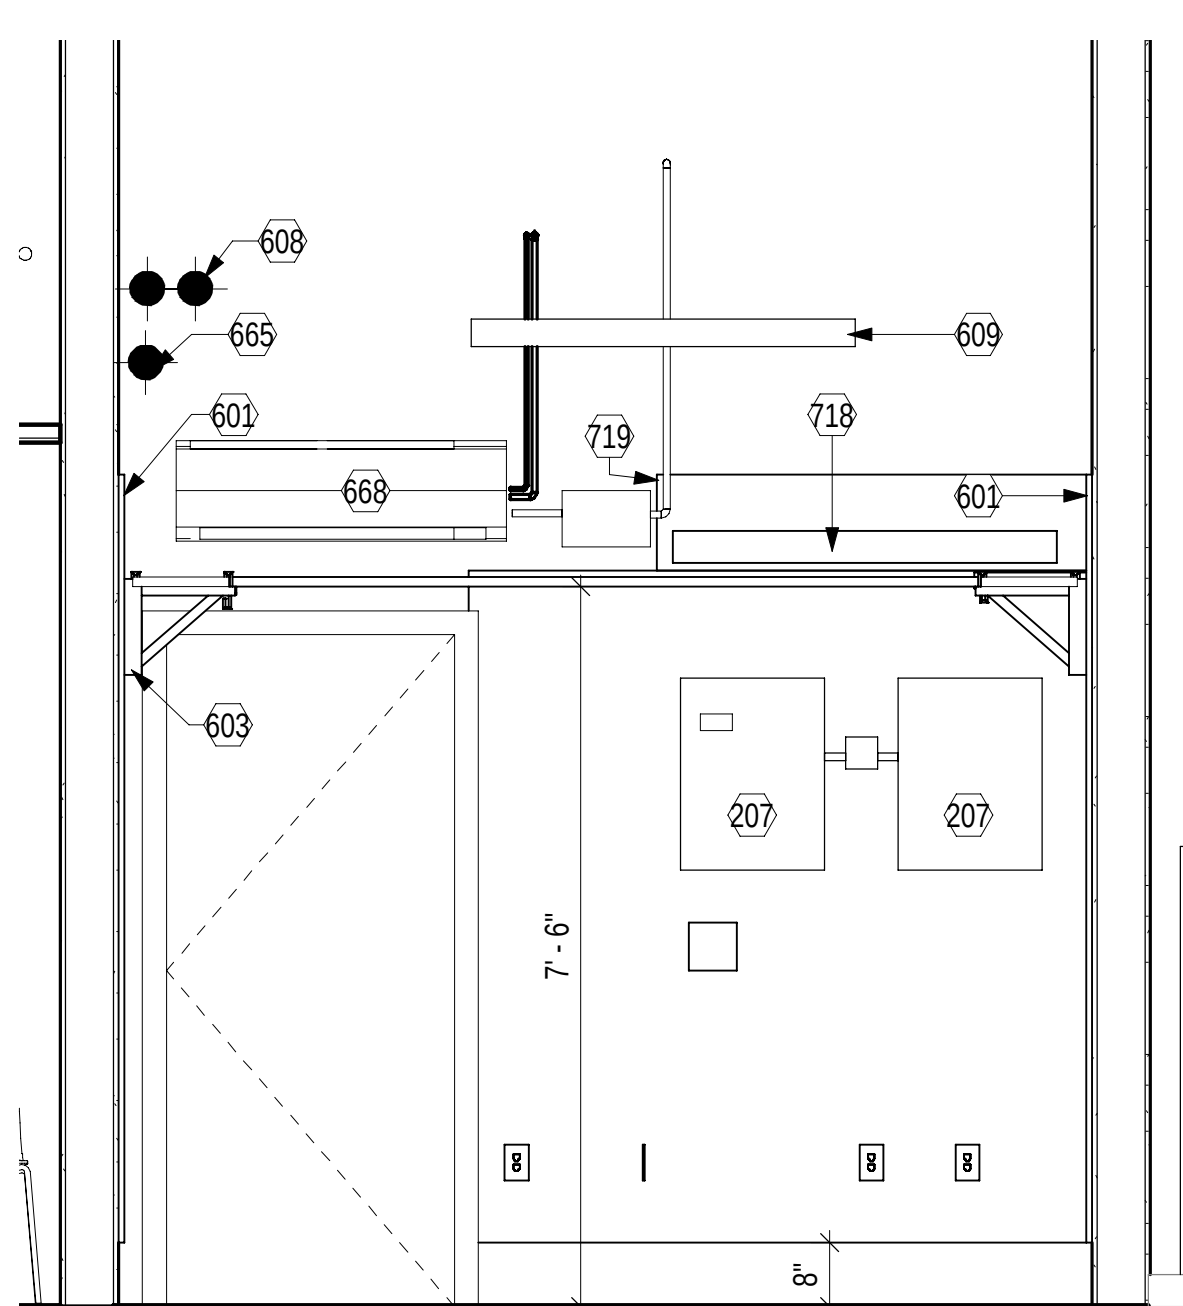

C3 TELECOM 105 - NORTH ELEVATION
1/2" = 1'-0" (T-102)

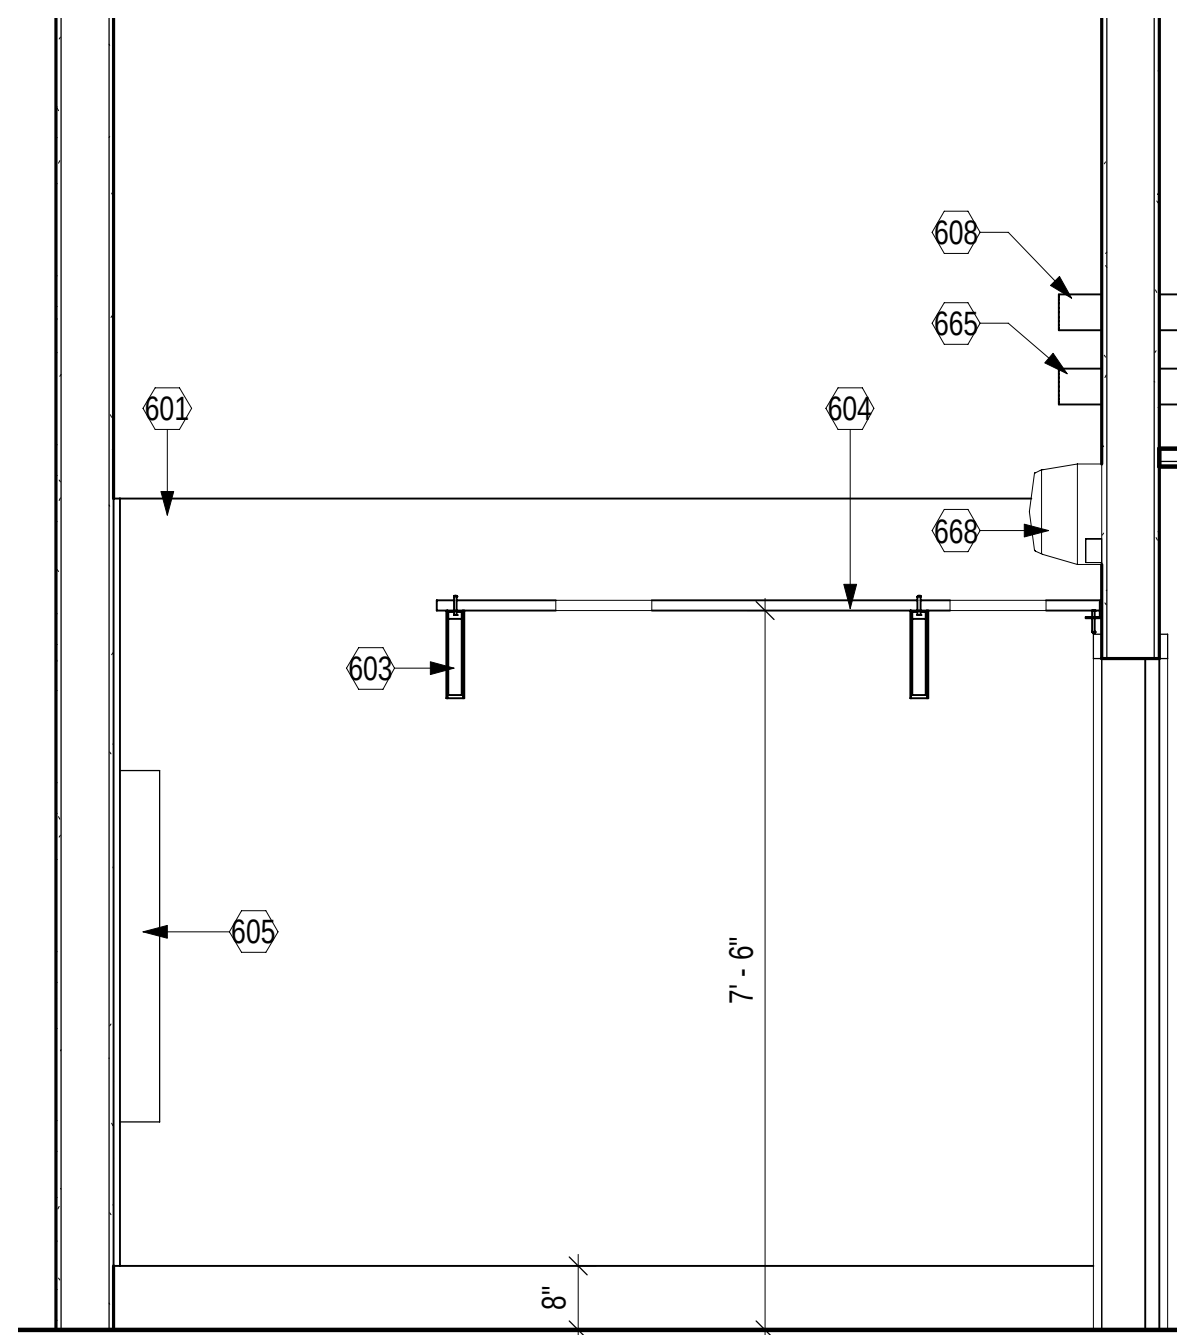



A3 TELECOM 105 - WEST ELEVATION
1/2" = 1'-0" (T-102)

GENERAL SHEET NOTES

- | | |
|---|---|
| A | REFER TO SHEET T-001 FOR TELECOM SYMBOLS AND ABBREVIATIONS. |
| B | BOND CABLE TRAY SECTIONS TOGETHER AND GROUND THE SYSTEM TO THE PBB/SBB. |
| C | TELECOMMUNICATIONS RACKS AND/OR CABINETS MUST BE BONDED TO THE PBB/SBB |
| D | TELECOMMUNICATIONS CONDUITS MUST BE BONDED TO THE PBB/SBB OR TO THE NEAREST CABLE TRAY OUTSIDE THE TR. |
| E | PROVIDE INFRASTRUCTURE FOR GOVERNMENT FURNISHED GOVERNMENT INSTALLED SECURITY INTRUSION DETECTION SYSTEM AND ACCESS CONTROL SYSTEM. PROVIDE JUNCTION BOXES AND CONDUIT WITH PULL STRINGS. |
| F | MAINTAIN SEPARATION BETWEEN ALL CLASSIFIED AND UNCLASSIFIED CABLING IN ACCORDANCE WITH CNSSM TEPREST-1-13. |

SHEET KEYNOTES

- 207 WALL SPACE ALLOCATED FOR ACCESS CONTROL PANELS.
PROVIDE DEDICATED 110VAC POWER FOR HARDWIRED
CIRCUIT MOUNTED AT 72" AFF
- 601 PROVIDE AC GRADE FIRE TREATED 3/4" PLYWOOD ON WALLS
AS SHOWN MOUNTED VERTICALLY 8" AFF . PAINT PLYWOOD
WITH 2 EVEN COATS OF FIRE RETARDANT PAINT ON ALL
SIDES. ATTACH USING AN ANCHORING SYSTEM SUITABLE
FOR THE WALL TYPE (TYPICAL)
- 602 GROUND AND BOND EQUIPMENT RACKS AND LADDER
PATHWAY TO PBB/SBB. INSTALL GROUND BAR AT HEIGHT
INDICATED.
- 603 TRI-ANGULAR SUPPORT FOR LADDER RACK SHALL BE
SPACED AT 5' ON CENTER. (TYPICAL)
- 604 PROVIDE 12" WIDE STEEL LADDER RACK WITH FITTINGS.
MOUNT LADDER RACK 8" AFF. (TYPICAL)
- 605 APPROXIMATE LOCATION OF ELECTRICAL PANEL BOARD.
MAINTAIN OPERATIONAL CLEARANCES PER NEC.
- 606 PROVIDE WALL ANGLE SUPPORT BRACKET FITTING USING
WALL ANCHORS SUITABLE FOR WALL TYPE. (TYPICAL)
- 608 PROVIDE FOUR INCH FIRE RATED SLEEVE SYSTEM FOR
COMMUNICATIONS CABLING CAPABLE OF 100 PERCENT
FILL.(TYPICAL)
- 609 MAINTAIN 12" CLEARANCE BETWEEN LIGHTING FIXTURES
AND COMMUNICATIONS CABLE. INCLUDE SPILL OUT FITTING
TO CONTROL CABLE BEND RADIUS.
- 624 PROVIDE WALL MOUNTED PRIMARY ENTRANCE PROTECTION
OF INCOMING/OUTGOING COPPER FEEDER CABLES.
- 655 ROUTE NEW 2X2 DUCTBANK BETWEEN THE NEW TMH01 AND
TELECOM RM 105 IN-GROUND AND BELOW THE OPERATIONS
BUILDING (BLDG A) SLAB. REF TS-101
- 665 PROVIDE 4" CONDUIT FOR CONNECTION BETWEEN SIPR OIS
107 AND TELECOM 105. INCLUDE 18" X 18" X 8" PULL BOX.
- 668 MECHANICAL EQUIPMENT - AC UNIT SHOWN FOR REFERENCE
AND COORDINATION.
- 713 PROVIDE 18"W VERTICAL STEEL LADDER RACK WITH FOOT
KIT, WALL BRACKETS, AND FITTINGS TO PROVIDE SECURE
PATHWAY BETWEEN ENTRY CONDUITS AND OVERHEAD
LADDER.
- 718 CONSOLIDATE SECURITY CONDUIT INTO METALLIC TROUGH
WITH COVER 4" X 4" X 4".
- 719 NOTCH PLYWOOD AROUND MECHANICAL EQUIPMENT.

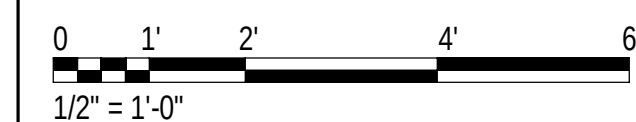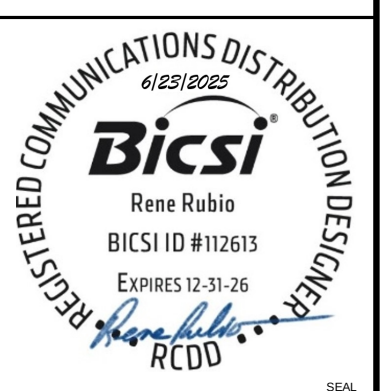[illegible]

Jacobs
1100 NORTH GLEBE ROAD
SUITE 500
ARLINGTON, VIRGINIA 22201
571.218.1000
FAX: 571.218.1600



				AE INFO	
APPROVED					
FOR COMMANDER NAVFAC					
ACTIVITY					
APPROVED BY LCDR ELIZABETH OLOKODE NAVFAC NLON FEAD DIRECTOR NEW LONDON, GROTON, CT					
SATISFACTORY TO DATE				05/27/2025	
DES	RR	DRW	RR	CHK	SA
PM/DM				SDS/RSF	
BRANCH MANAGER				WRB	
CHIEF ENGINEER				JWJ	
SIDE PROTECTION				LHM	

NAVAL FACILITIES ENGINEERING SYSTEMS COMMAND NAVAL FACILITIES ENGINEERING SYSTEMS COMMAND - MID-ATLANTIC NAVAL FACILITIES ENGINEERING SYSTEMS COMMAND - MID-ATLANTIC NAVAL STATION - NORFOLK, VA	GROTON, CONNECTICUT	P-1102 WEAPONS MAGAZINE & ORDNANCE OPERATIONS FACILITY OPERATIONS	TELECOMMUNICATIONS ELEVATIONS	RFTN
---	---------------------	--	-------------------------------	------

SCALE: AS NOTED		
EPROJECT NO.: 1667770		
CONSTR. CONTR. NO.		
NAVFAC DRAWING NO. 12894058		
SHEET 108	OF	140
T-202		

6/20/2025 1:09:58 PM
\\ac1vso1\user\pfd\ZEL628\TELECOM\BLOG-166770-T-81M_V21.rvt

T-401

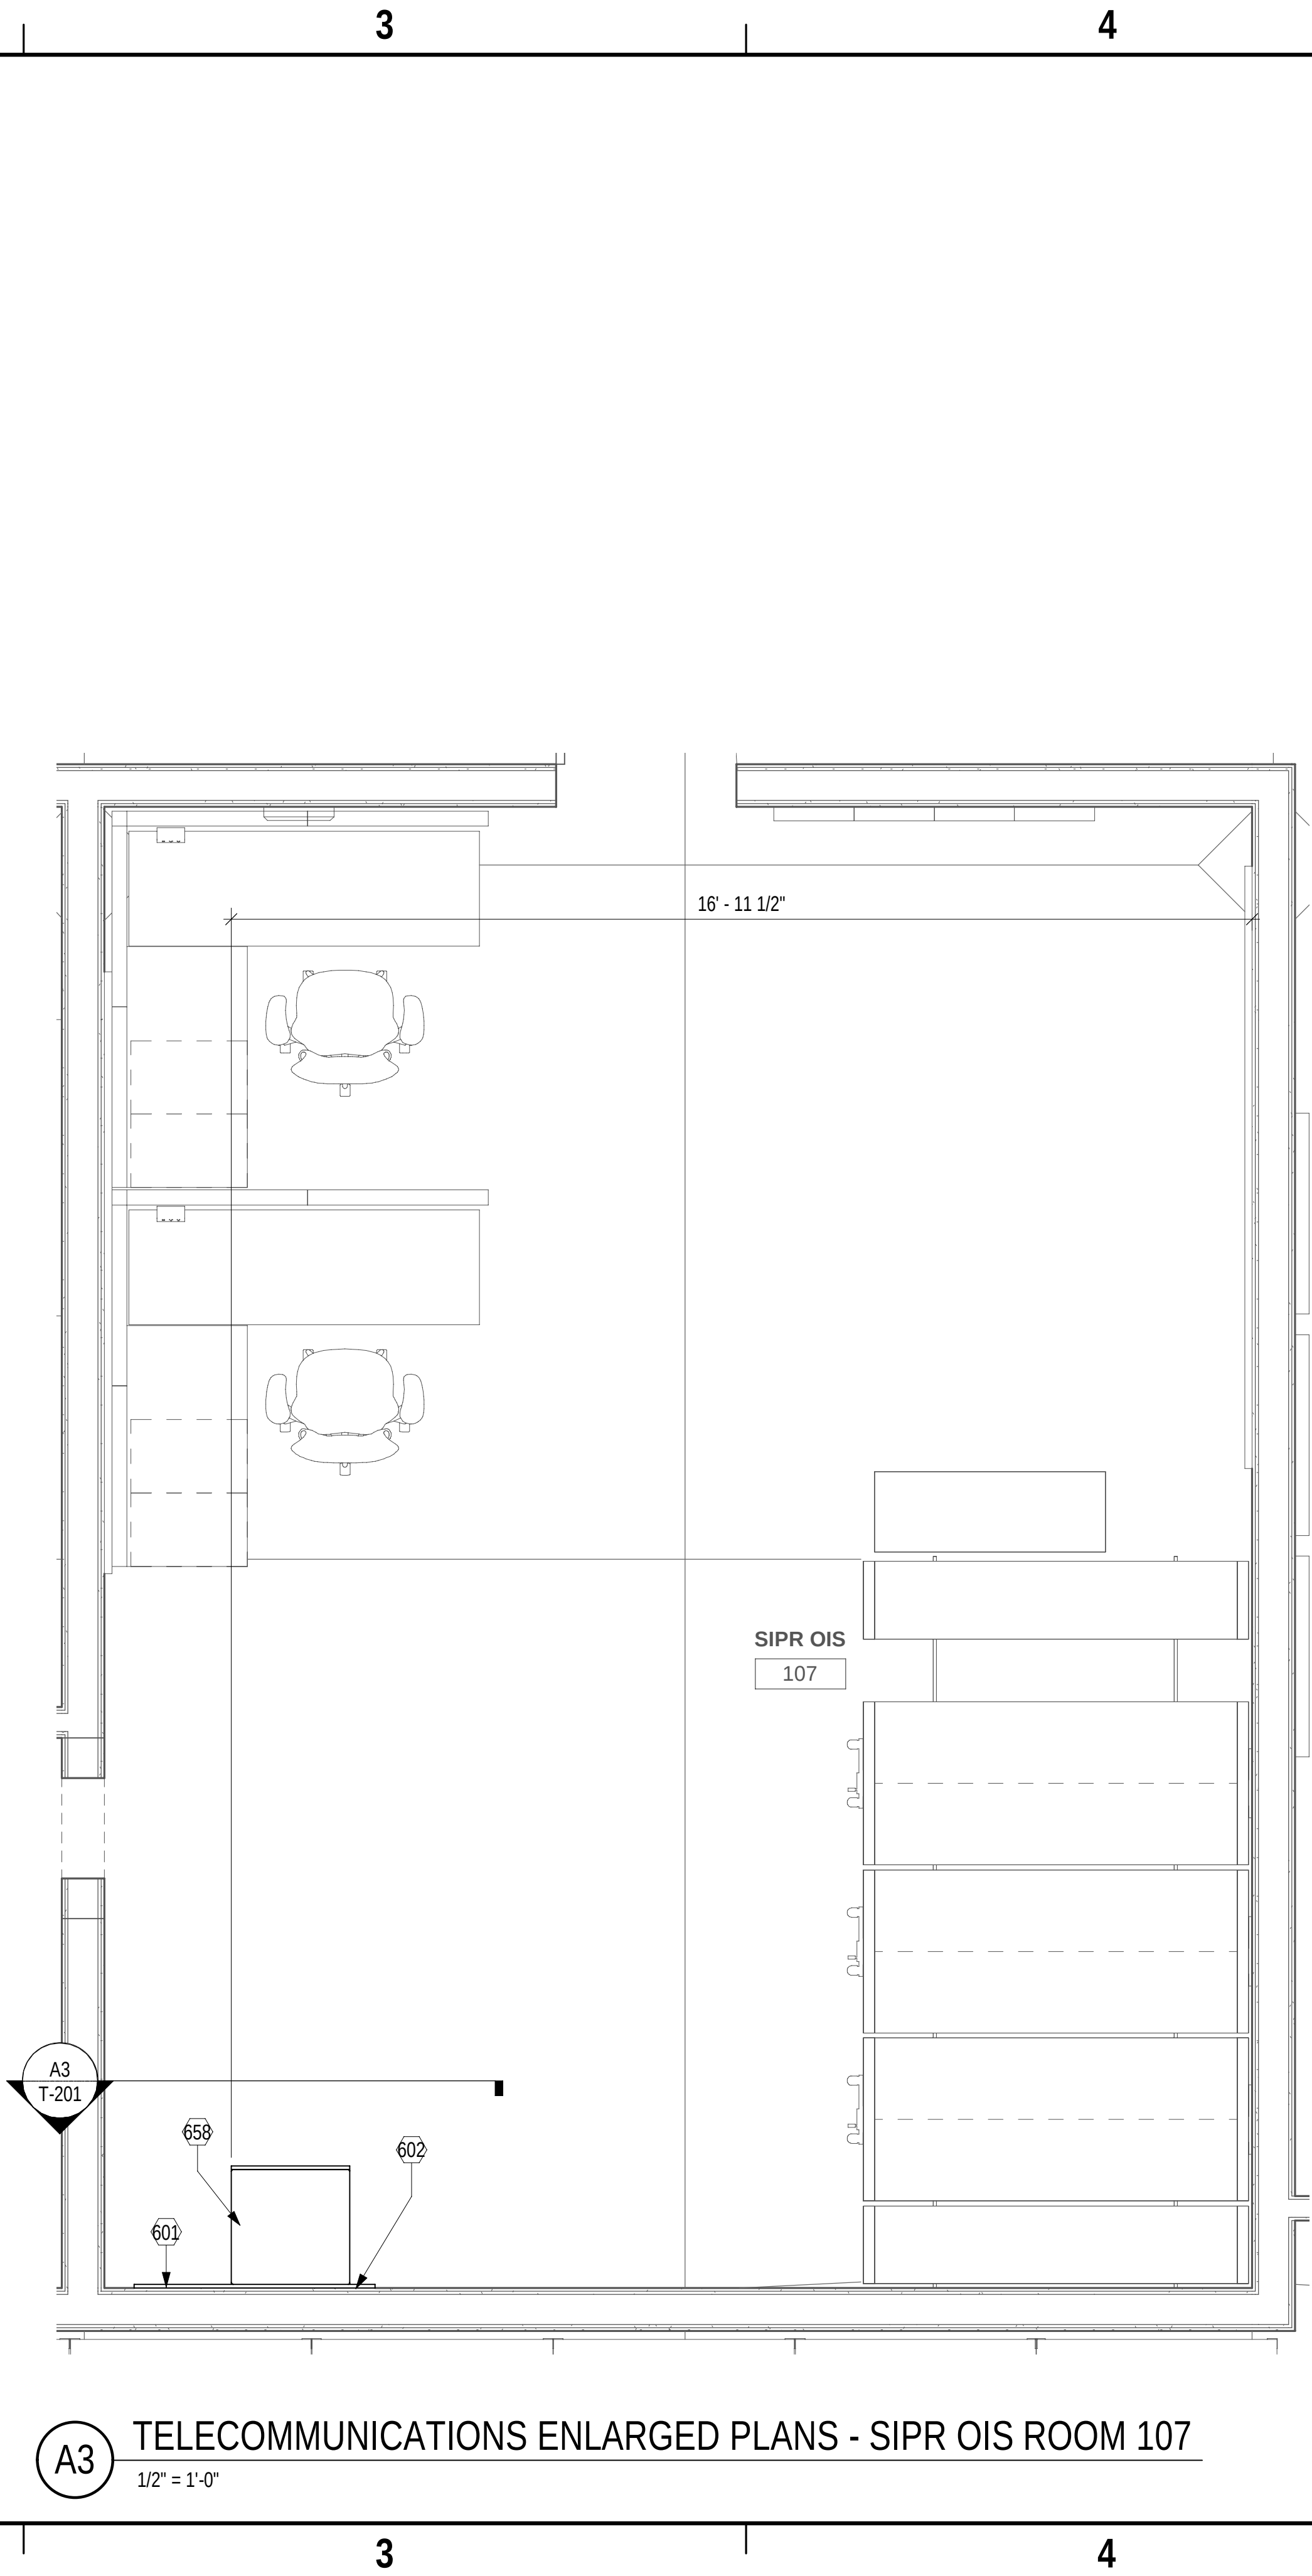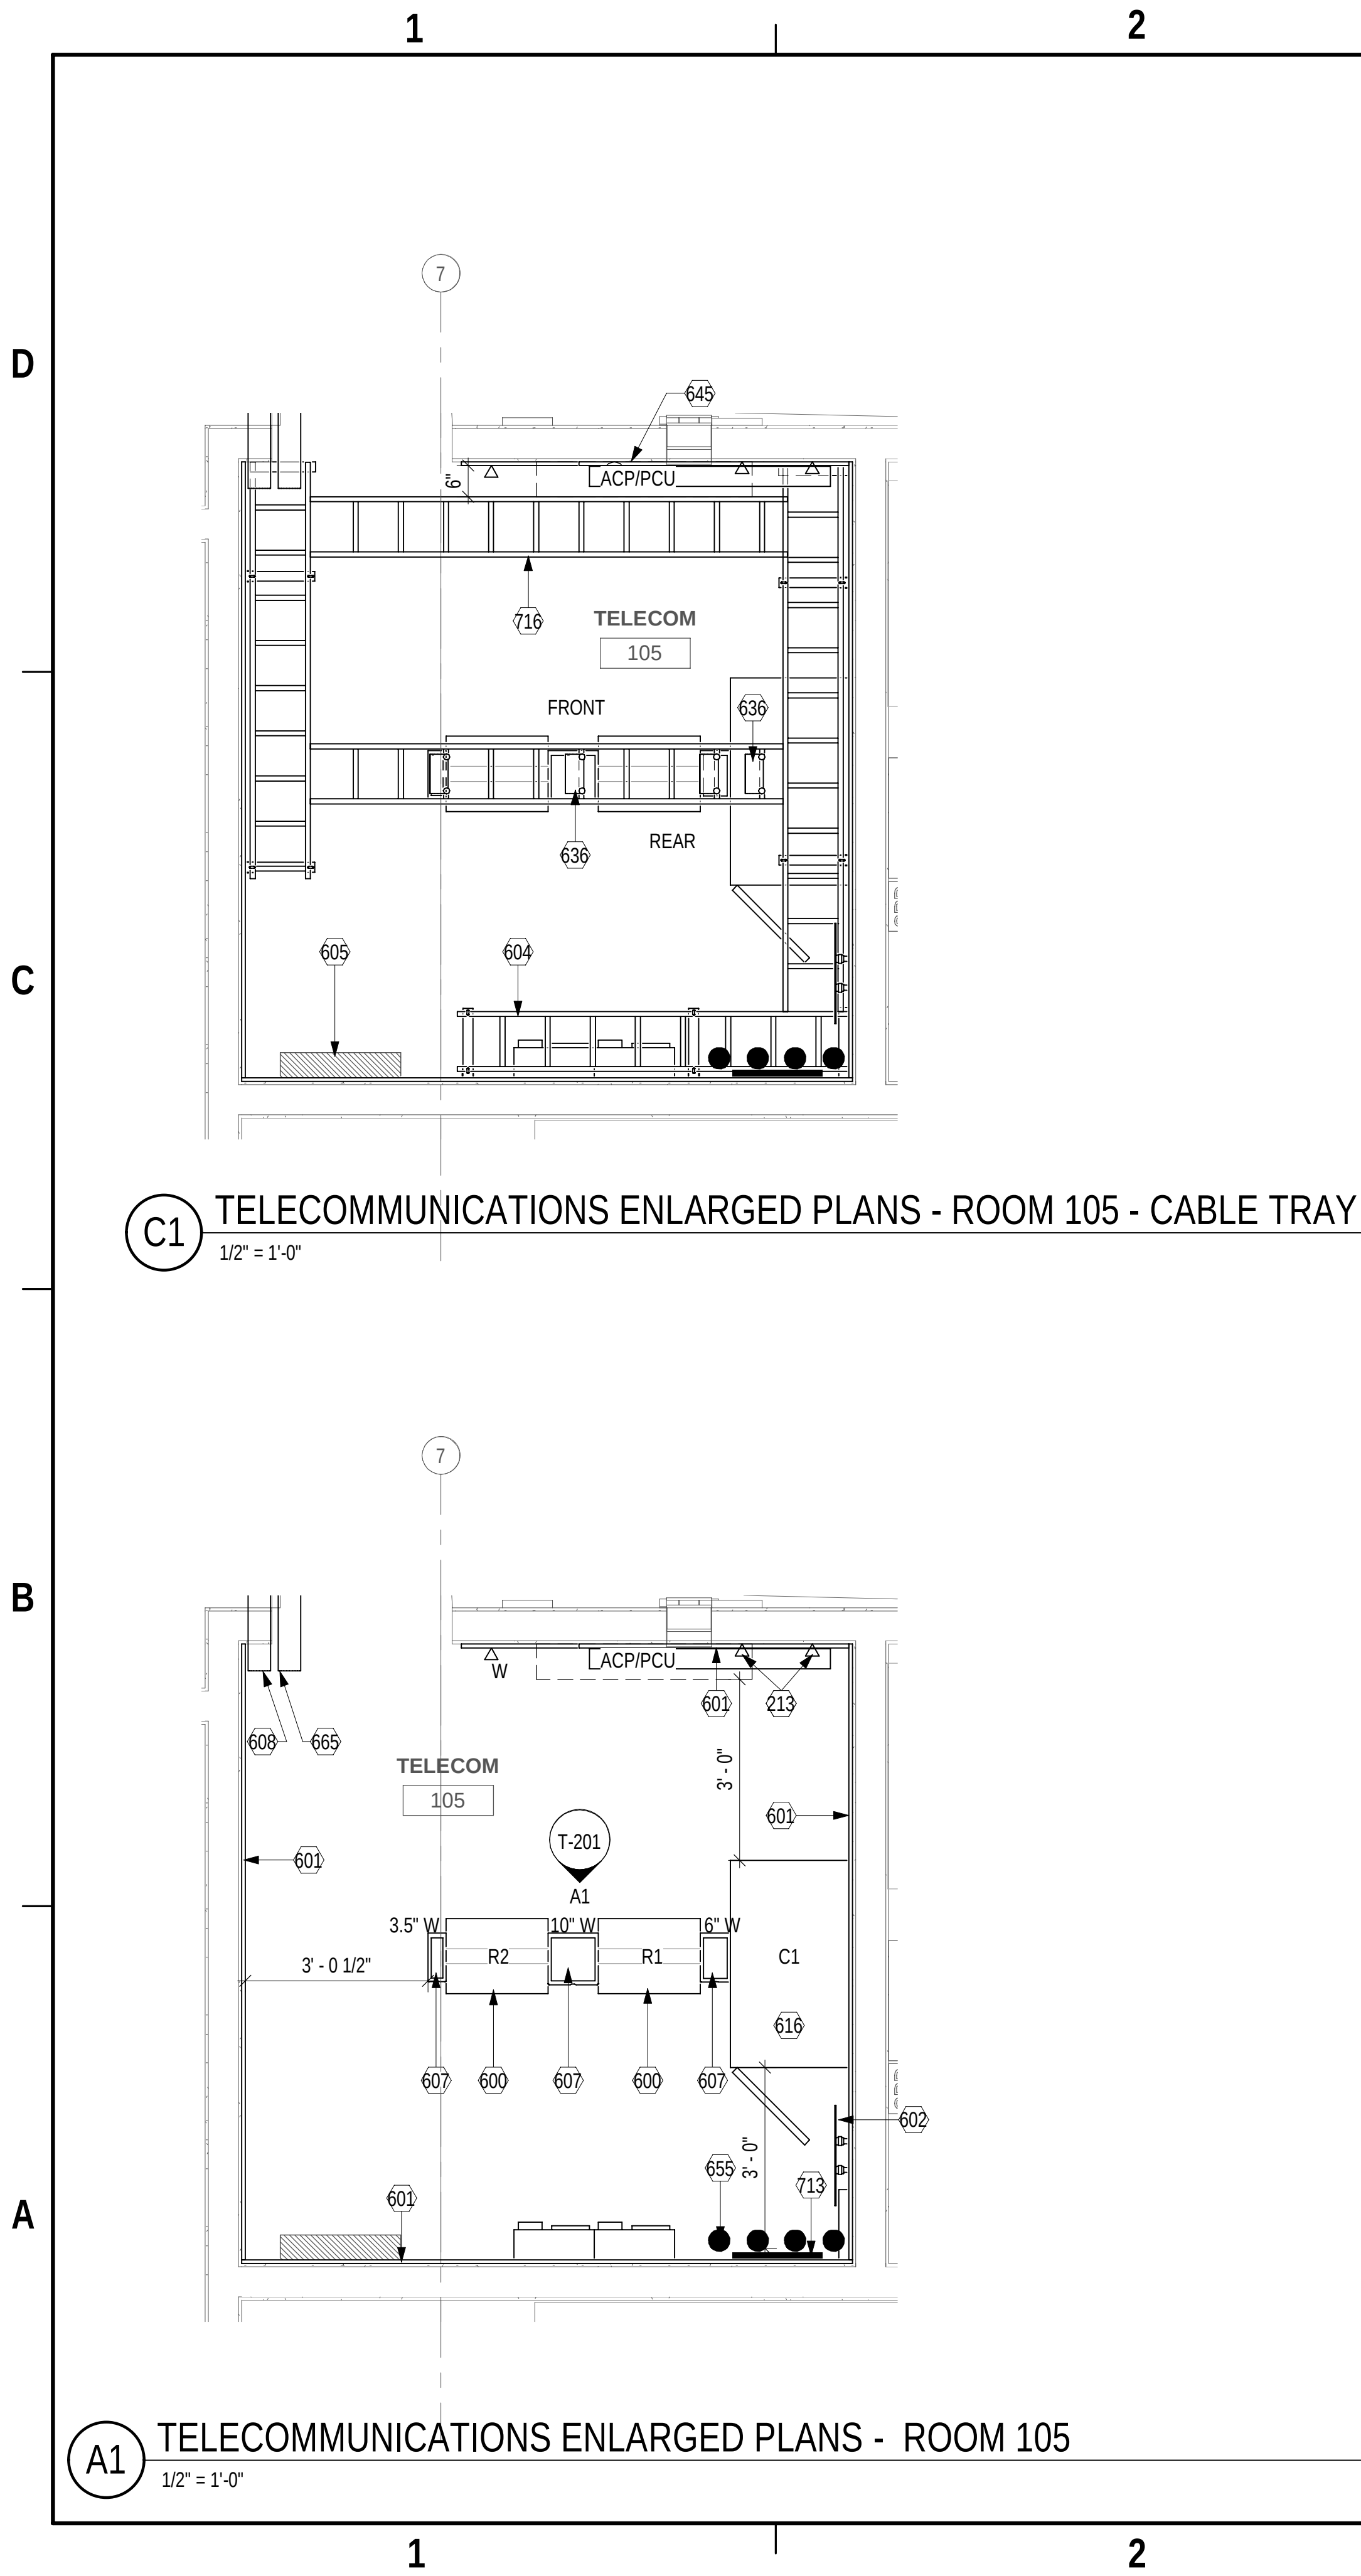


GENERAL SHEET NOTES



- A REFER TO SHEET T-001 FOR TELECOM SYMBOLS AND ABBREVIATIONS.
- B BOND CABLE TRAY SECTIONS TOGETHER AND GROUND THE SYSTEM TO THE PBB/SBB.
- C TELECOMMUNICATIONS RACKS AND/OR CABINETS MUST BE BONDED TO THE PBB/SBB
- D TELECOMMUNICATIONS CONDUITS MUST BE BONDED TO THE PBB/SBB OR TO THE NEAREST CABLE TRAY OUTSIDE THE TR.
- E PROVIDE INFRASTRUCTURE FOR GOVERNMENT FURNISHED GOVERNMENT INSTALLED SECURITY INTRUSION DETECTION SYSTEM AND ACCESS CONTROL SYSTEM. PROVIDE JUNCTION BOXES AND CONDUIT WITH PULL STRINGS.
- F MAINTAIN SEPARATION BETWEEN ALL CLASSIFIED AND UNCLASSIFIED CABLING IN ACCORDANCE WITH CNSSAM TEPMEST/1-13.

SHEET KEYNOTES

- 213 PROVIDE CATEGORY 6 WALL MOUNTED DATA OUTLETS FOR ESS EQUIPMENT. COORDINATE ROUGH IN HEIGHT WITH ESS PROVIDER.
- 600 PROVIDE TWO-POST EQUIPMENT RACK, 19" WIDE, UNIVERSAL, 84" HIGH, 45RU, BLACK, MARKED AND NUMBERED RACK UNITS, 1500LB LOAD CAPACITY. ANCHOR BASEPLATE ON ALL FOUR CORNERS TO CONCRETE SUBFLOOR. (TYPICAL)
- 601 PROVIDE AC GRADE FIRE TREATED 3/4" PLYWOOD ON WALLS AS SHOWN MOUNTED VERTICALLY 8" AFF. PAINT PLYWOOD WITH 2 EVEN COATS OF FIRE RETARDANT PAINT ON ALL SIDES. ATTACH USING AN ANCHORING SYSTEM SUITABLE FOR THE WALL TYPE (TYPICAL)
- 602 GROUND AND BOND EQUIPMENT RACKS AND LADDER PATHWAY TO PBB/SBB. INSTALL GROUND BAR AT HEIGHT INDICATED.
- 604 PROVIDE 12" WIDE STEEL LADDER RACK WITH FITTINGS. MOUNT LADDER RACK 8" AFF. (TYPICAL)
- 605 APPROXIMATE LOCATION OF ELECTRICAL PANEL BOARD. MAINTAIN OPERATIONAL CLEARANCES PER NEC.
- 607 PROVIDE DOUBLE-SIDED VERTICAL CABLE MANAGER PER SPECIFICATIONS. (TYPICAL)
- 608 PROVIDE FOUR INCH FIRE RATED SLEEVE SYSTEM FOR COMMUNICATIONS CABLING CAPABLE OF 100 PERCENT FILL.(TYPICAL)
- 616 FLOOR MOUNTED EQUIPMENT CABINET FOR NIPR NETWORK CABLING ONLY. MAINTAIN 3' MINIMUM CLEARANCE IN FRONT AND REAR OF CABINET. EQUIPPED WITH LOCKABLE FRONT AND REAR DOORS, INDIVIDUALLY KEYED, 84"H X 24"W X 36"D, FRONT AND REAR VERTICAL MOUNTING RAILS, GROUND BUS BAR BONDED TO THE TELECOM GROUNDING SYSTEM.
- 636 PROVIDE WATERFALL FITTING WHERE CABLING EXITS LADDER RACK TO MAINTAIN PROPER BEND RADIUS. (TYPICAL)
- 645 SPACE RESERVED FOR ACCESS CONTROL AND INTRUSION DETECTION EQUIPMENT. COORDINATE 110VAC POWER WITH E.C.
- 655 ROUTE NEW 2X2 DUCTBANK BETWEEN THE NEW TMH01 AND TELECOM RM 105 IN-GROUND AND BELOW THE OPERATIONS BUILDING (BLDG A) SLAB. REF TS-101
- 658 PROVIDE WALL-MOUNTED EQUIPMENT ENCLOSURE MOUNTED 6" AFF AS INDICATED. CABLING FOR SIPR DROPS ORIGINATES FROM A DEDICATED 24-PORT PATCH PANEL. PROVIDE TWO CAT6 DATA CABLES BETWEEN THE WALL CABINET AND TELECOM 105. COORDINATE POWER WITH EC.
- 665 PROVIDE 4" CONDUIT FOR CONNECTION BETWEEN SIPR OIS 107 AND TELECOM 105. INCLUDE 18" X 18" X 8" PULL BOX.
- 713 PROVIDE 18"W VERTICAL STEEL LADDER RACK WITH FOOT KIT, WALL BRACKETS, AND FITTINGS TO PROVIDE SECURE PATHWAY BETWEEN ENTRY CONDUITS AND OVERHEAD LADDER.
- 716 PROVIDE LADDER RACK TRAPEZE SUPPORT IN CENTER OF SECTION USING MIN 3/8" ALL THREAD ROD AND CORRECT HARDWARE. STAND OFF SECTION FROM WALL 6" TO ALLOW FOR SECURITY WIRING TROUGH ACCESS TO PANELS BELOW.

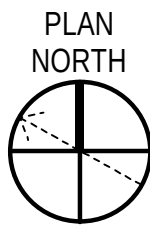

SYN	DESCRIPTION	DATE	APPR

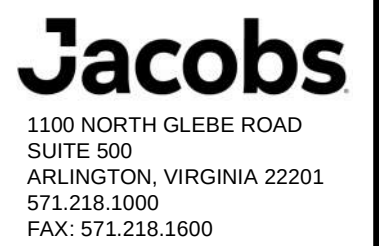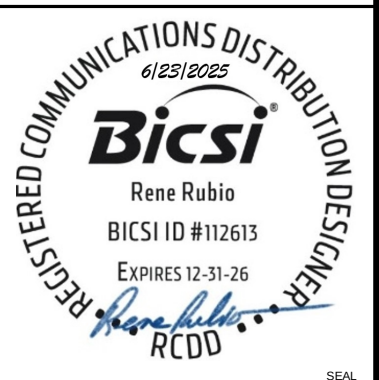

APPROVED

FOR COMMANDER NAVFAC

ACTIVITY APPROVED BY LCDR ELIZABETH CLOKODE NAVFAC NLON READ DIRECTOR NEW LONDON, GROTON, CT

SATISFACTORY TO DATE 05/27/2025

DES	RR	DRW	RR	CHK	SA
-----	----	-----	----	-----	----

PMIDM	SDS / RSF
-------	-----------

BRANCH MANAGER	WRB
----------------	-----

CHIEF ENGINEER	JWJ
----------------	-----

FIRE PROTECTION	HPN
-----------------	-----

DEPARTMENT OF THE NAVY
NAVAL FACILITIES ENGINEERING SYSTEMS COMMAND - MID-ATLANTIC
NAVAL STATION - NORFOLK, VA
NAVAL FACILITIES ENGINEERING SYSTEMS COMMAND - MID-ATLANTIC
NAVAL SUBMARINE BASE NEW LONDON
P-1102 WEAPONS MAGAZINE & ORDNANCE OPERATIONS FACILITY
GROTON, CONNECTICUT
OPERATIONS
TELECOMMUNICATIONS ENLARGED PLANS

SCALE: AS NOTED
EPROJCT NO.: 1667770
CONSTR. CONTR. NO.

NAVFAC DRAWING NO. 12894059

SHEET 109 OF 140

T-401



1


2

3


4

5

D

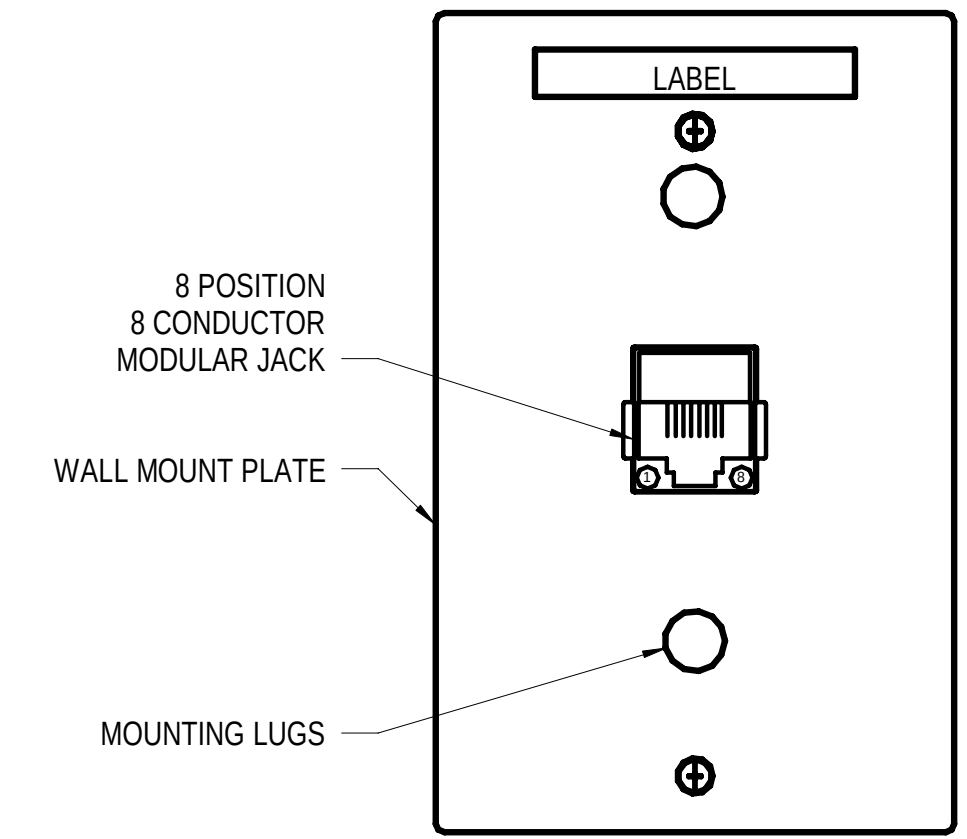

D1 WALL MOUNT PHONE FACEPLATE
NTS

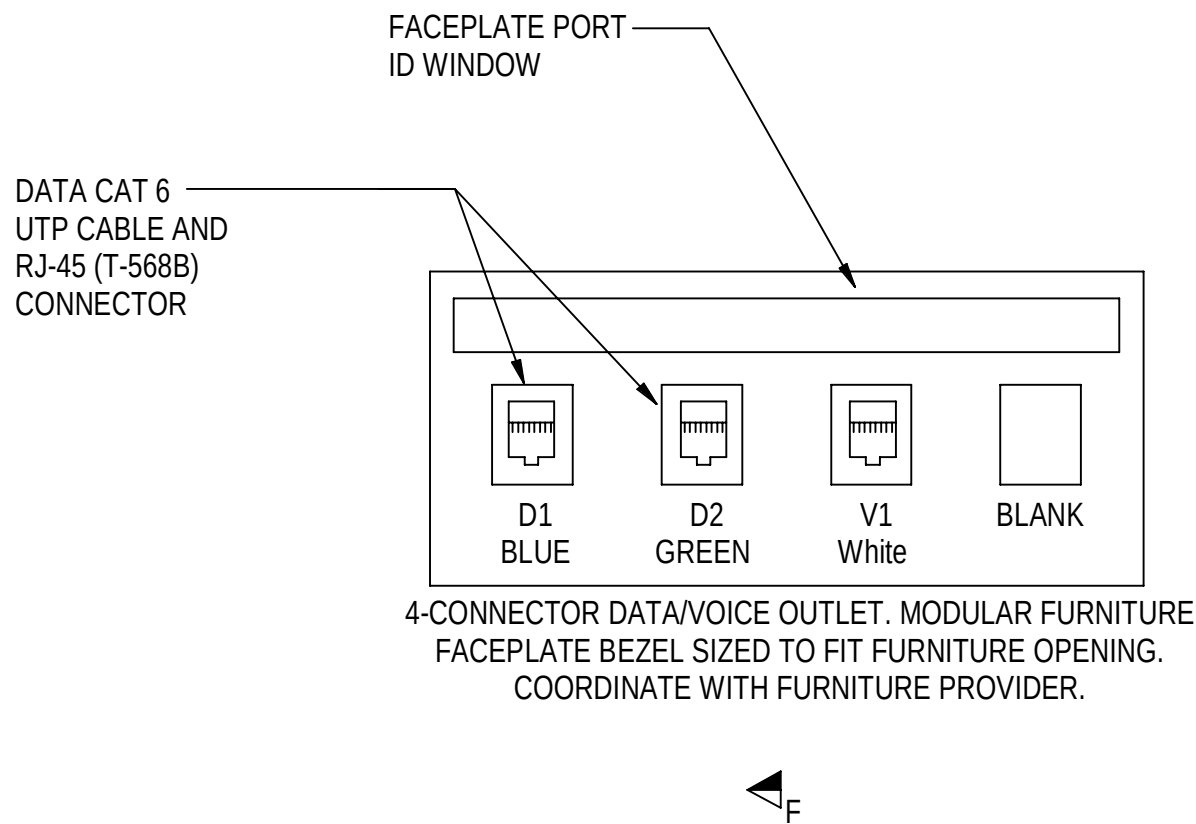

D2 MODULAR FURNITURE AND VOICE OUTLET
NTS

* UN-NUMBERED CUBICLE: WHEN A CUBICAL AREA IS FOUND UNNUMBERED, IT MUST BE NUMBERED CLOCK-WISE FROM NORTH. THE ASSIGNED NUMBERS WILL BE NOTED ON THE RED LINED FLOOR PLAN.

* IF WIRING CLOSET ROOM NUMBER IS NOT AVAILABLE, LABEL WIRING CLOSETS, M01 FOR MAIN 01, S01 FOR SUB-CLOSET 01, AND CLOCK-WISE FROM NORTH.


* IF ROOM NUMBERS ARE UNAVAILABLE, START NUMBERING ROOMS NORTH TO SOUTH, WEST TO EAST.

* DROP NUMBERS ARE IN SEQUENCE BY WIRING CLOSET.

* PATCH PANELS ARE IDENTIFIED BY A NUMBER FOLLOWED BY F FOR FRONT AND B FOR BACK AS NECESSARY


* NUMBERS NEXT TO JACKS ARE ALWAYS D1, D2, S1, S2, AND V2, AS THEY ARE PART OF THE CABLE ID CONVENTION AND NOT A PATCH PANEL NUMBER. D IS FOR DATA AND V FOR VOICE OVER IP.

NOTE: THIS NGEN WALL PLATE NAMING SCHEME SUPERCEDES ALL EXISTING LABELING SCHEMES IN PLACE.

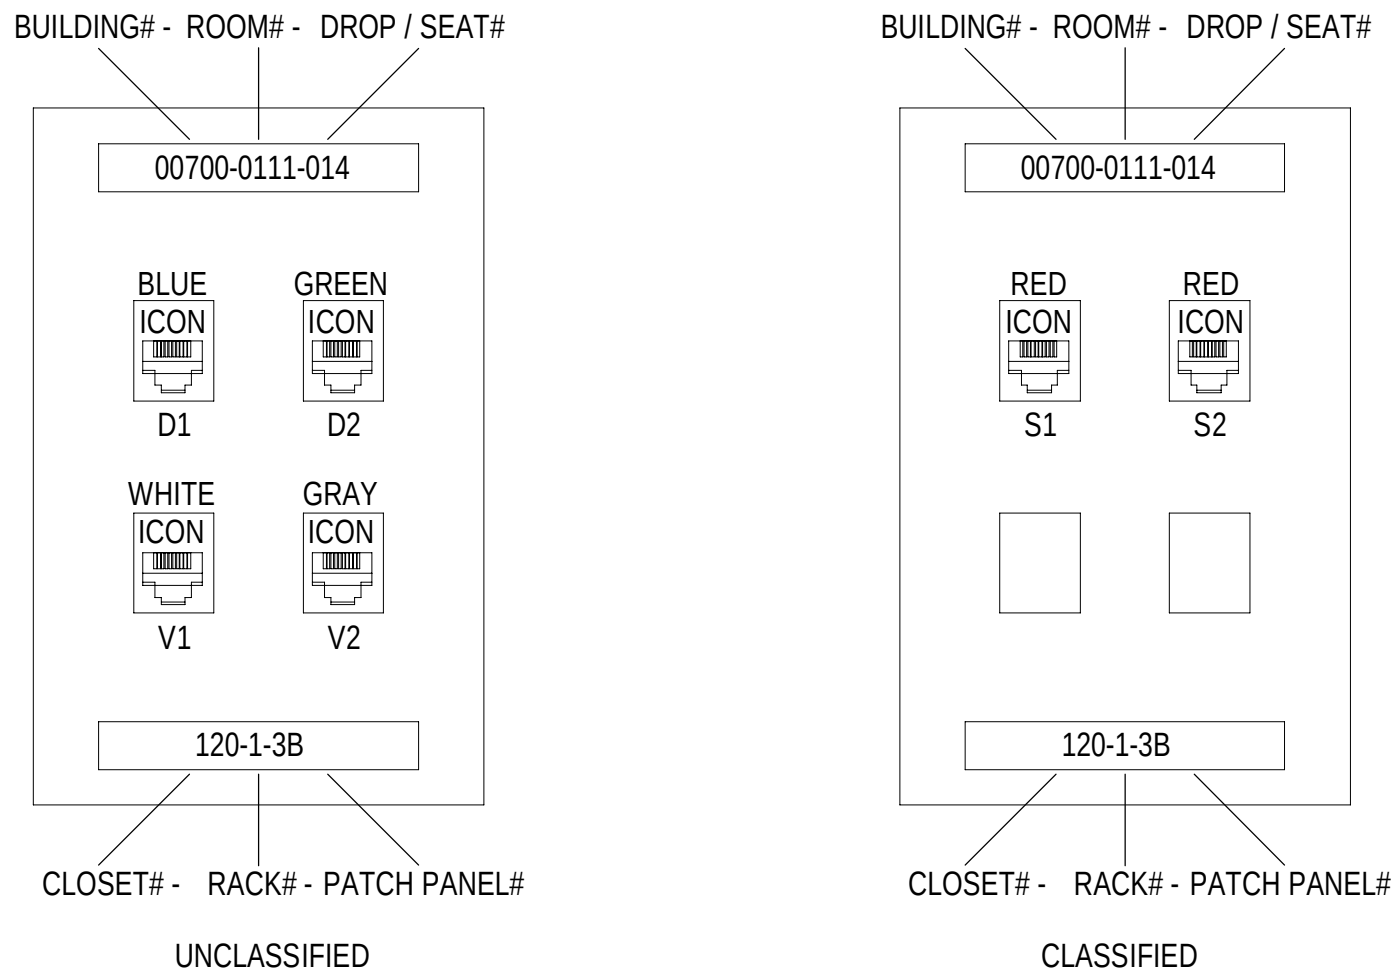


D4 WALL PLATE
NTS

C

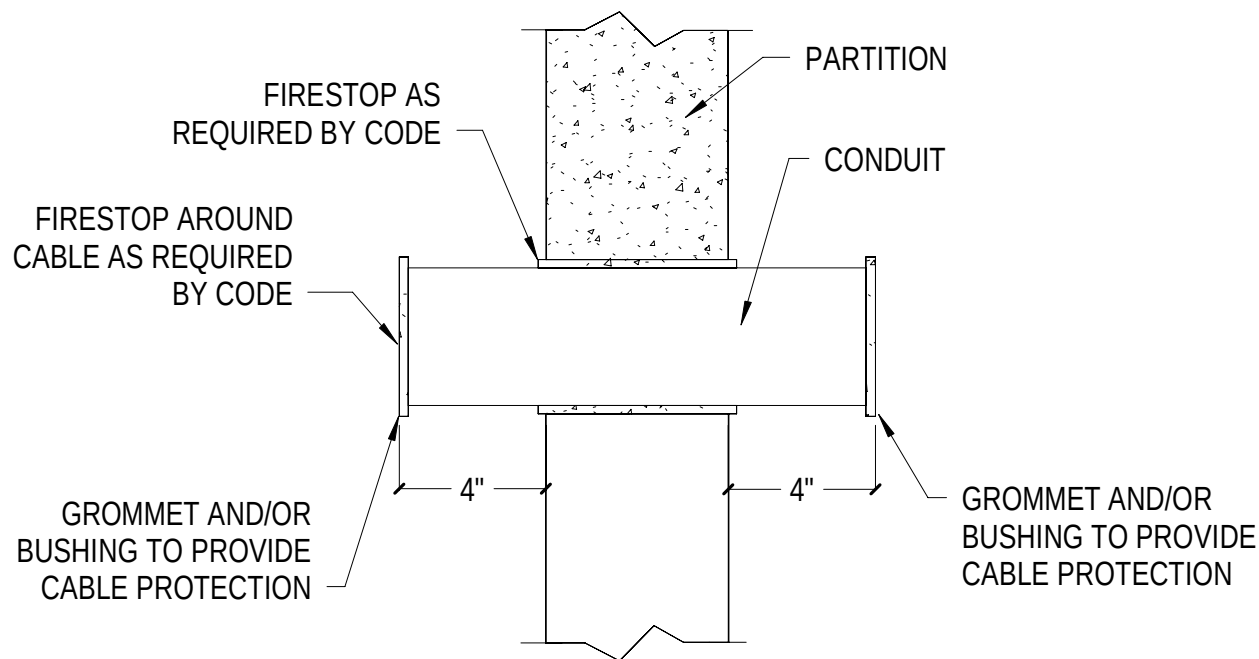


C1 TYPICAL SLEEVE IN RATED WALL
NTS

568A PIN CONFIGURATION	
PIN	WIRE COLOR
1	WHITE/ORANGE
2	ORNGE
3	WHITE/GREEN
4	BLUE
5	WHITE/BLUE
6	GREEN
7	WHITE/BROWN
8	BROWN

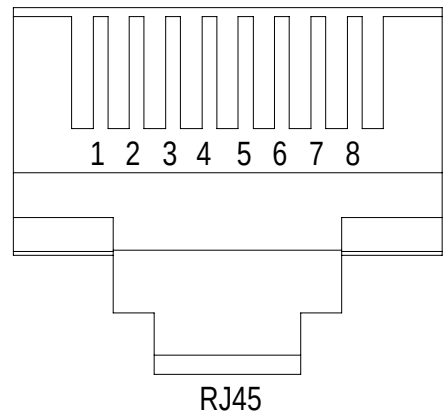


C2 568B PIN OUT CONFIGURATION
NTS


B

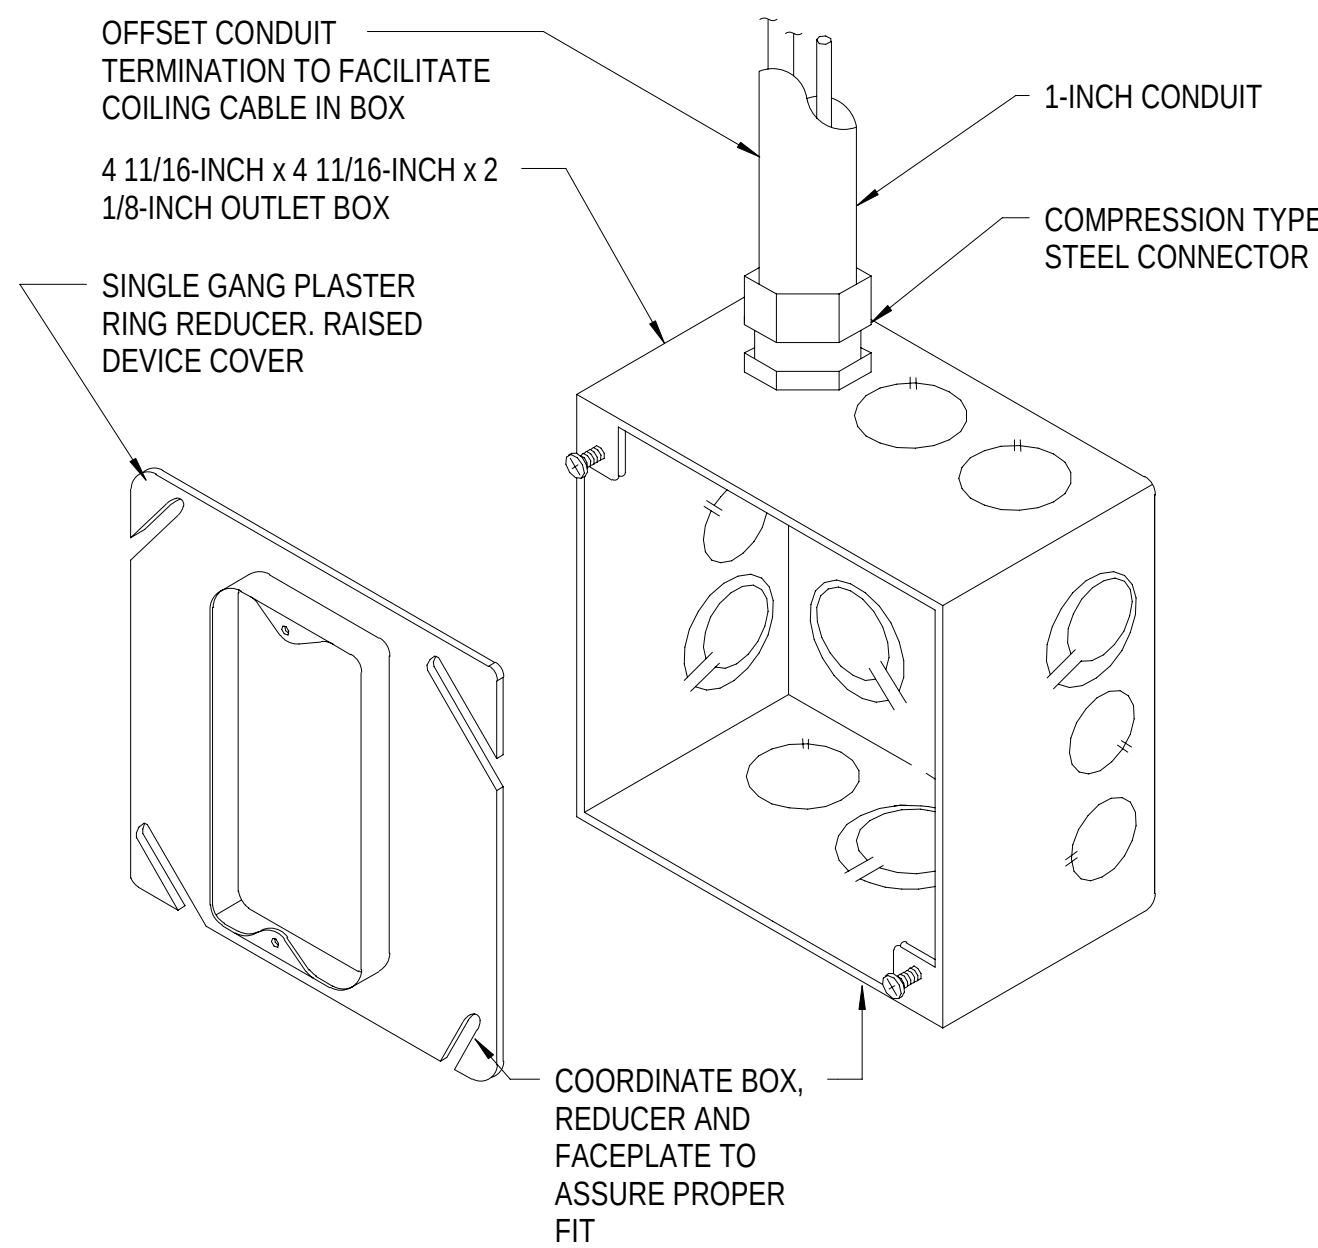


A1 WALL MOUNTED OUTLET BOX DETAIL
NTS

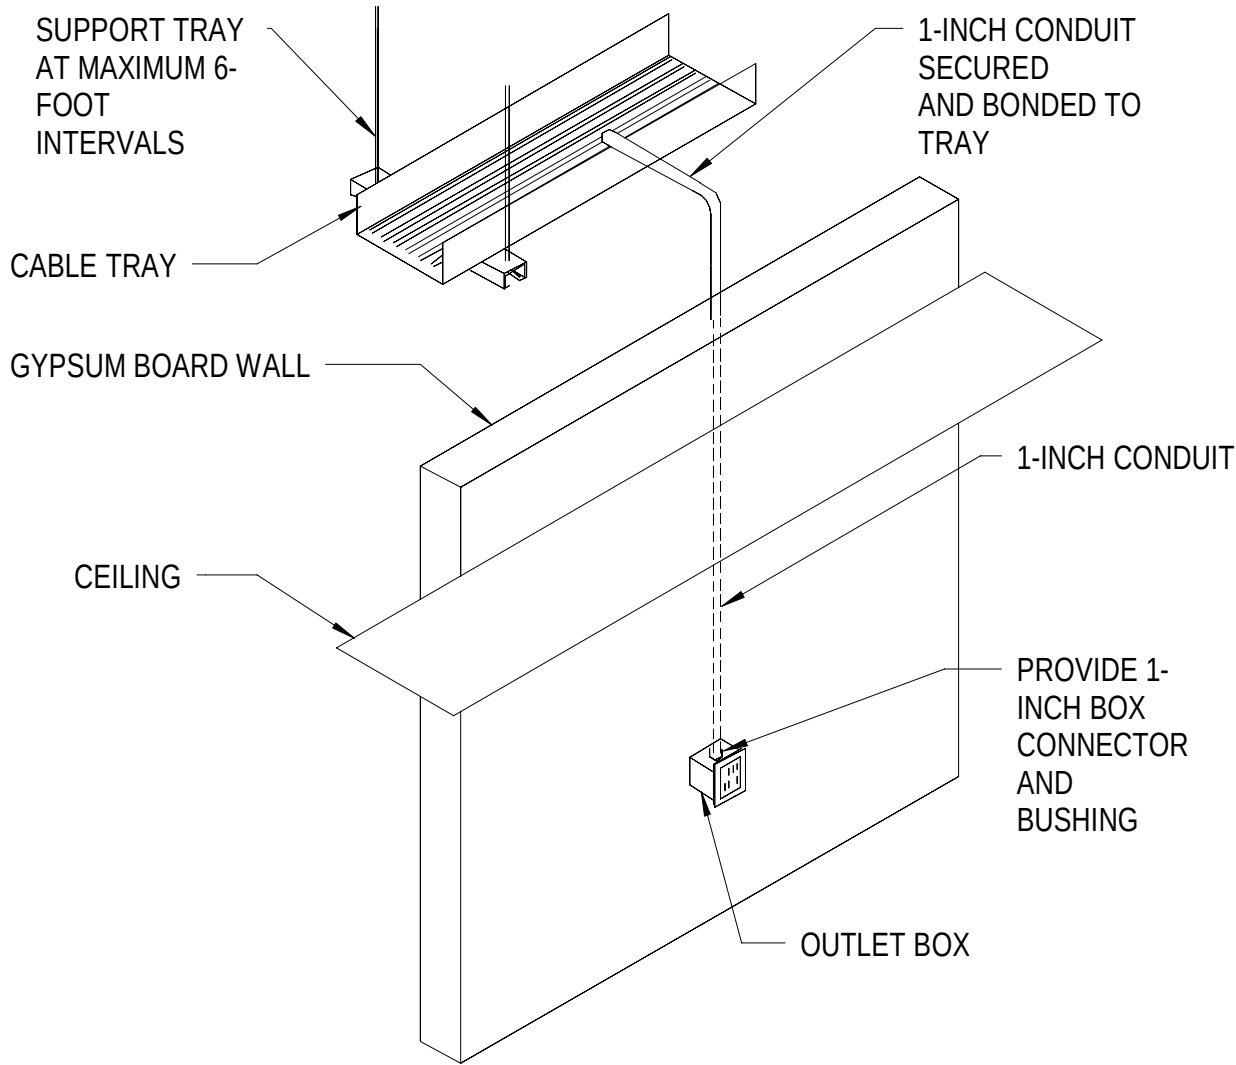

A2 TYPICAL OUTLET DROP
NTS

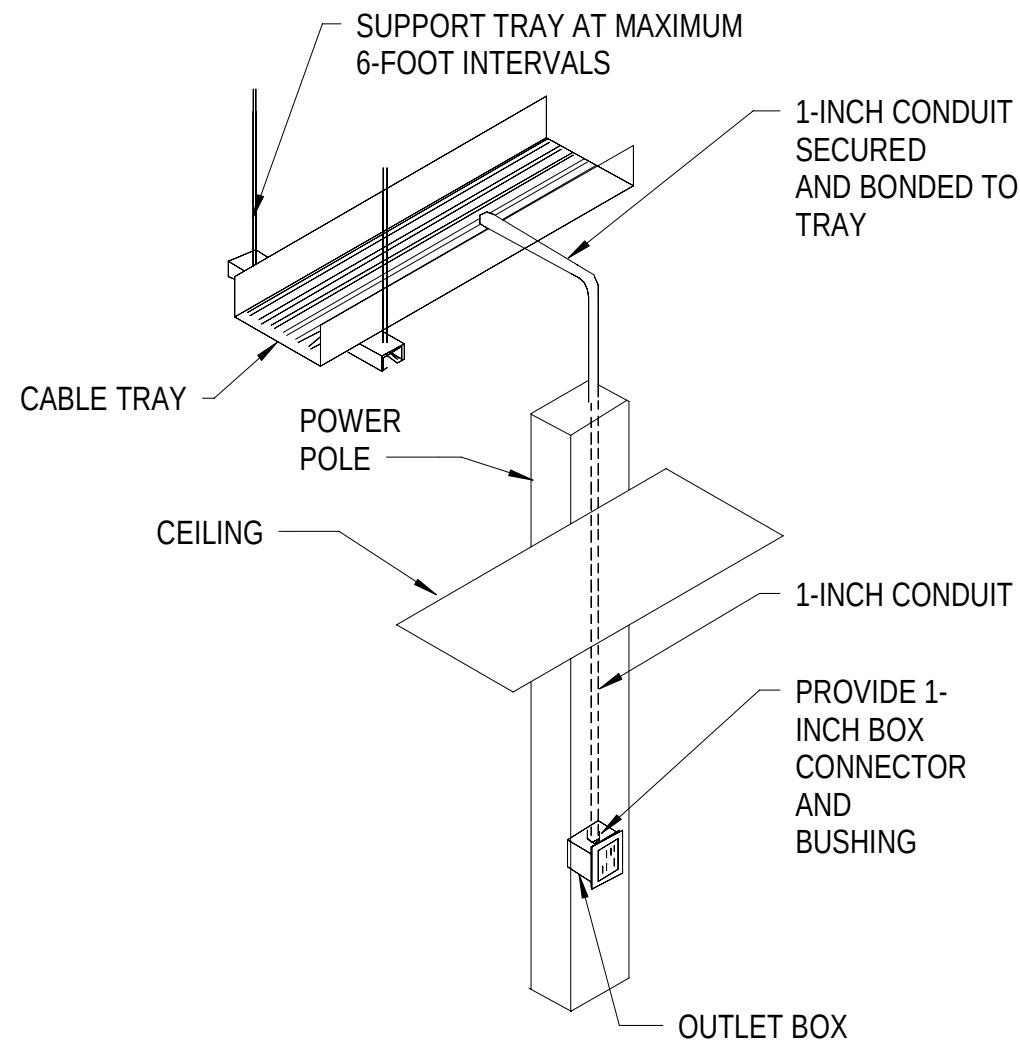

A4 TYPICAL POWER POLE OUTLET DROP
NTS

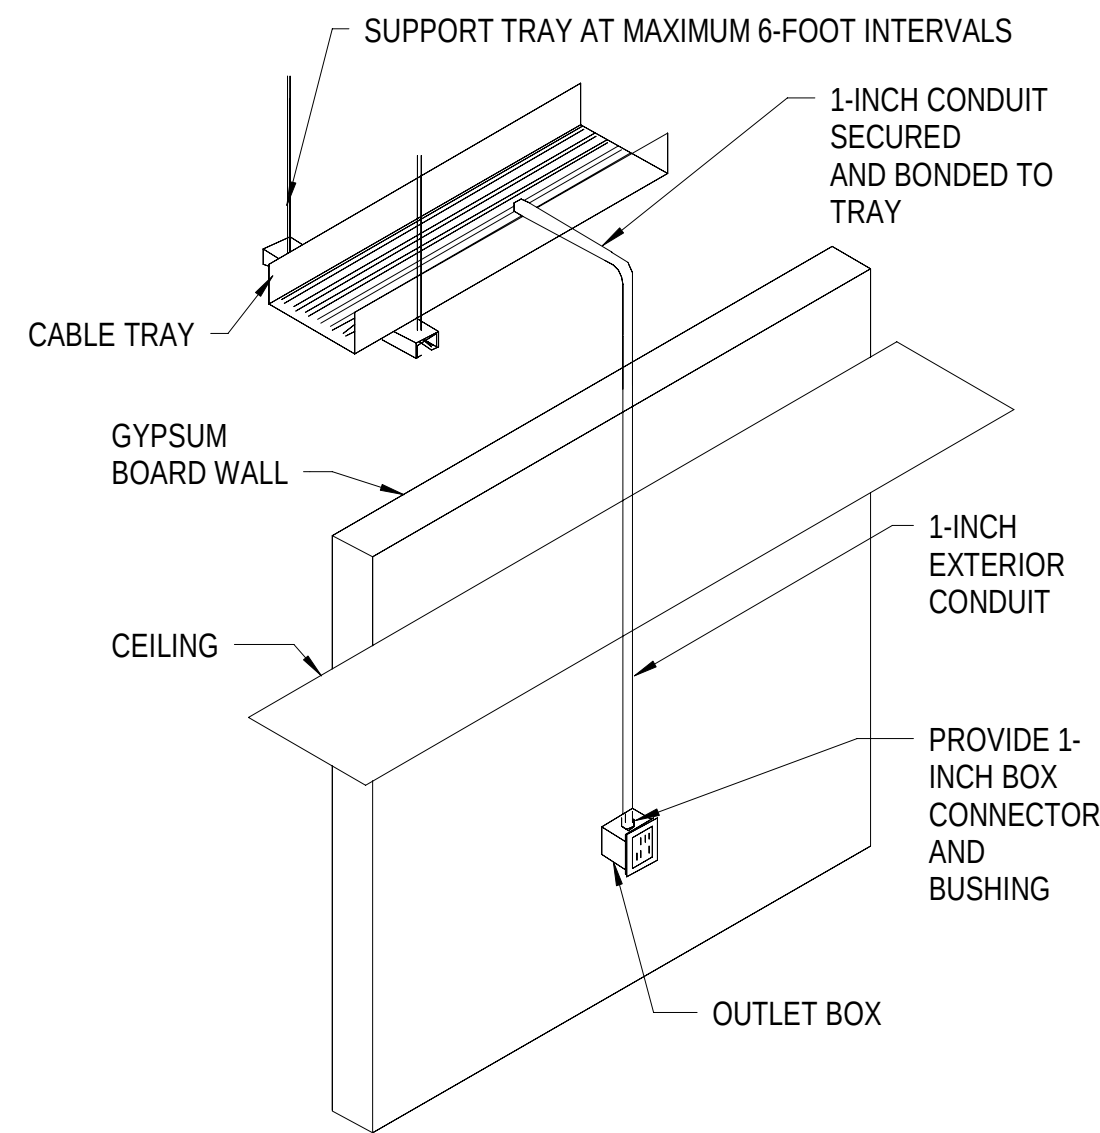

A5 TYPICAL SIPR OUTLET DROP
NTS


APPR DATE SYM DESCRIPTION

D

C

B

A

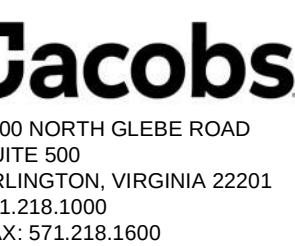

AE INFO

APPROVED

FOR COMMANDER NAVFAC

ACTIVITY APPROVED BY LCDR ELIZABETH CLOKODE NAVFAC NLON READ DIRECTOR NEW LONDON, GROTON, CT

SATISFACTORY TO DATE 05/27/2025

DES RR DRW RR CHK SA

PMOM SDS / RSF

BRANCH MANAGER WRB

CHIEF ENGINEER JWI

FIRE PROTECTION HPN

NAVAL FACILITIES ENGINEERING SYSTEMS COMMAND

NAVAL FACILITIES ENGINEERING SYSTEMS COMMAND - MID-ATLANTIC

NAVAL STATION - NORFOLK, VA

NAVAL FACILITIES ENGINEERING SYSTEMS COMMAND - MID-ATLANTIC

NAVAL SUBMARINE BASE NEW LONDON

GROTON, CONNECTICUT

P-1102 WEAPONS MAGAZINE & ORDNANCE OPERATIONS FACILITY

OPERATIONS

TELECOMMUNICATIONS DETAILS

SCALE: AS NOTED

EPROJECT NO.: 1667770

CONSTR. CONTR. NO.

NAVFAC DRAWING NO. 12894061

SHEET 111 OF 140

T-502

1


2

3

4


5



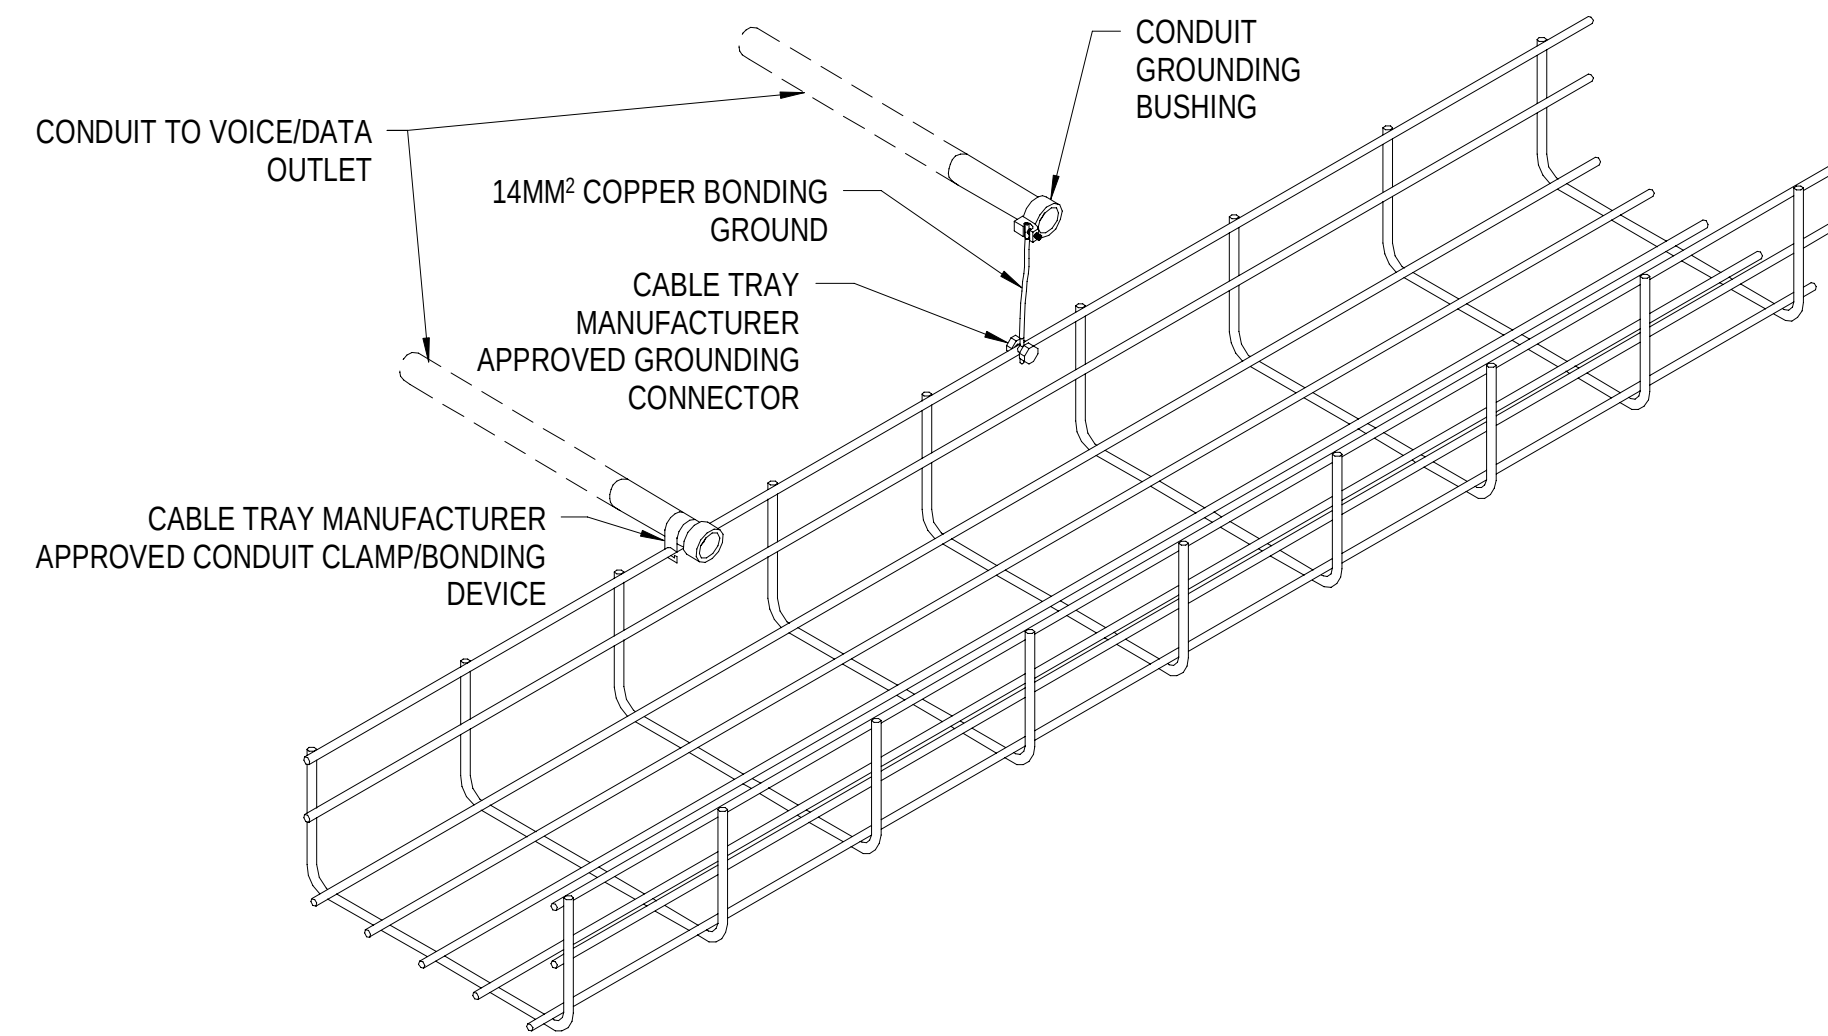


INSTALL WATERFALLS WHERE CABLES LEAVE THE TRAY IN ORDER TO PROVIDE PROPER BEND RADIUS.

C1 CABLE TRAY - BASKET TYPE2
NTS

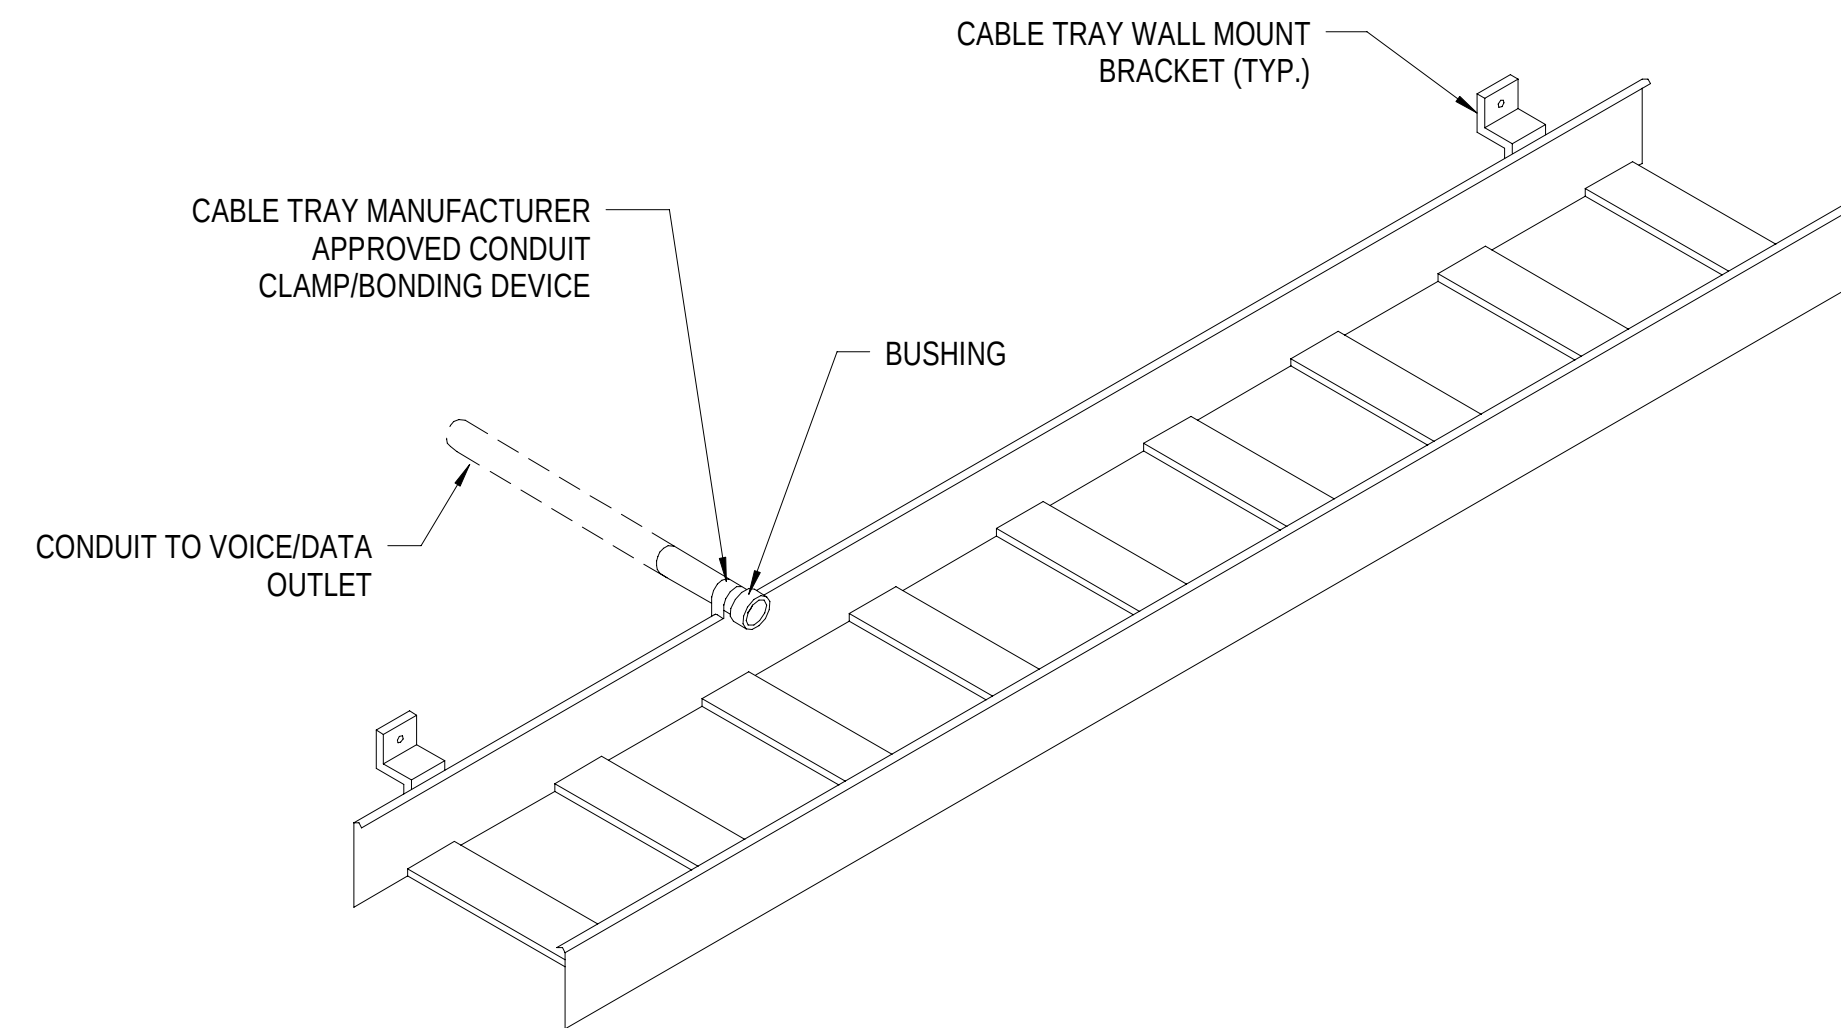


INSTALL WATERFALLS WHERE CABLES LEAVE THE TRAY IN ORDER TO PROVIDE PROPER BEND RADIUS


A1 CABLE TRAY - LADDER TYPE1
NTS

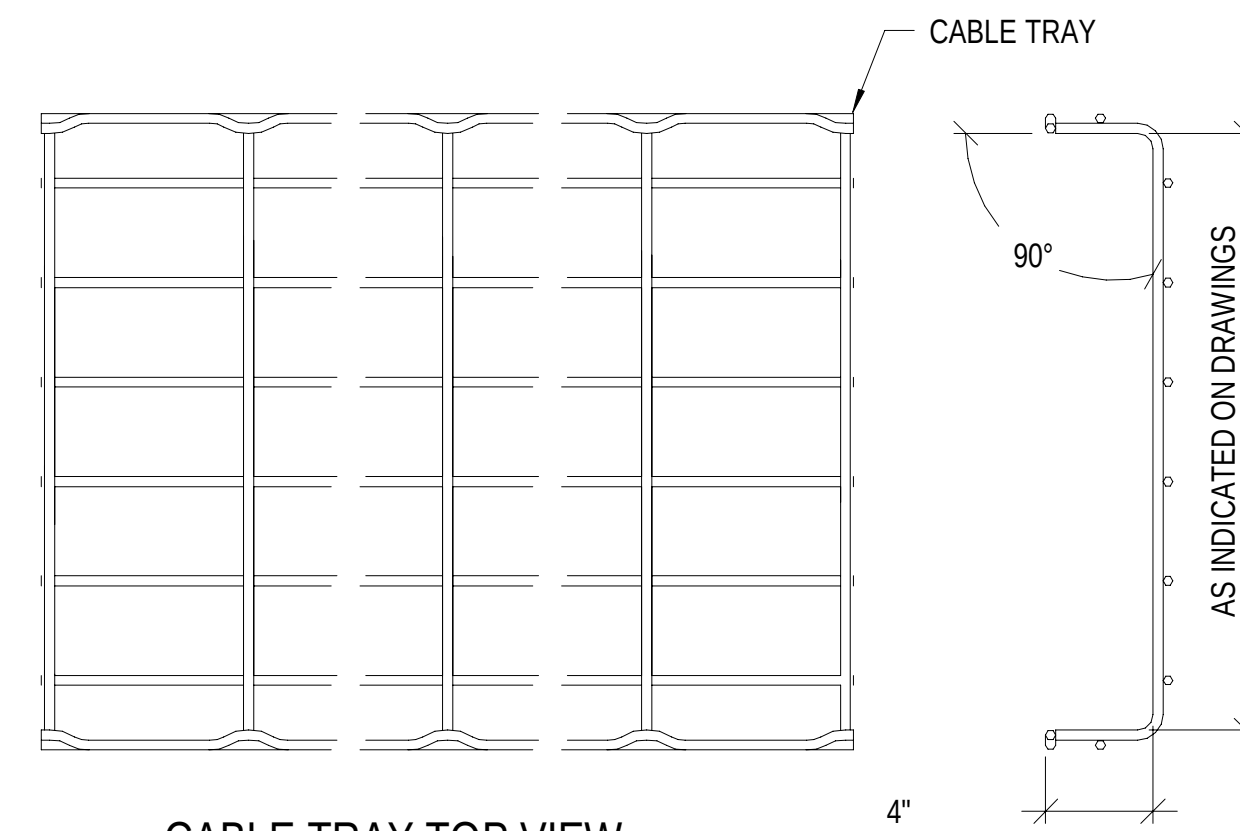


CABLE TRAY TOP VIEW

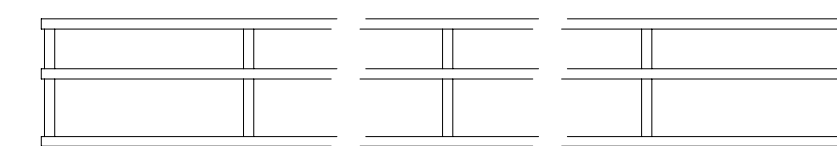

CABLE TRAY SIDE VIEW

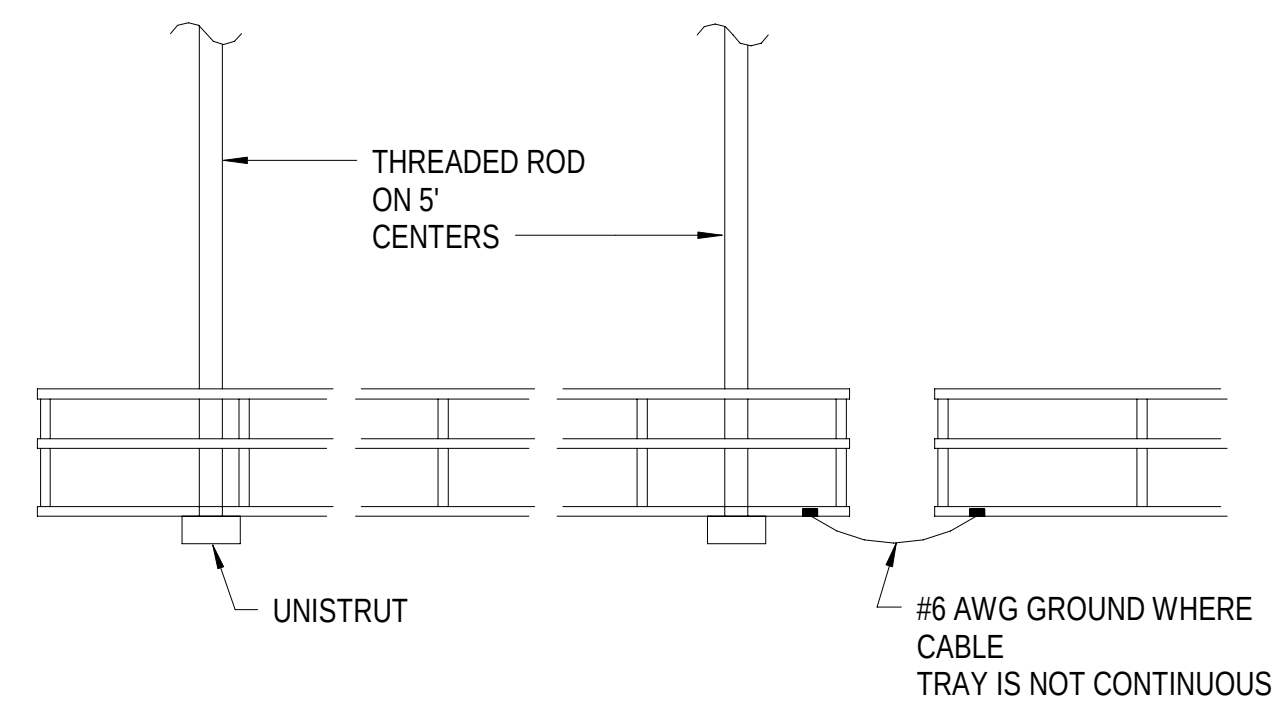

MOUNTING AND BONDING DETAIL

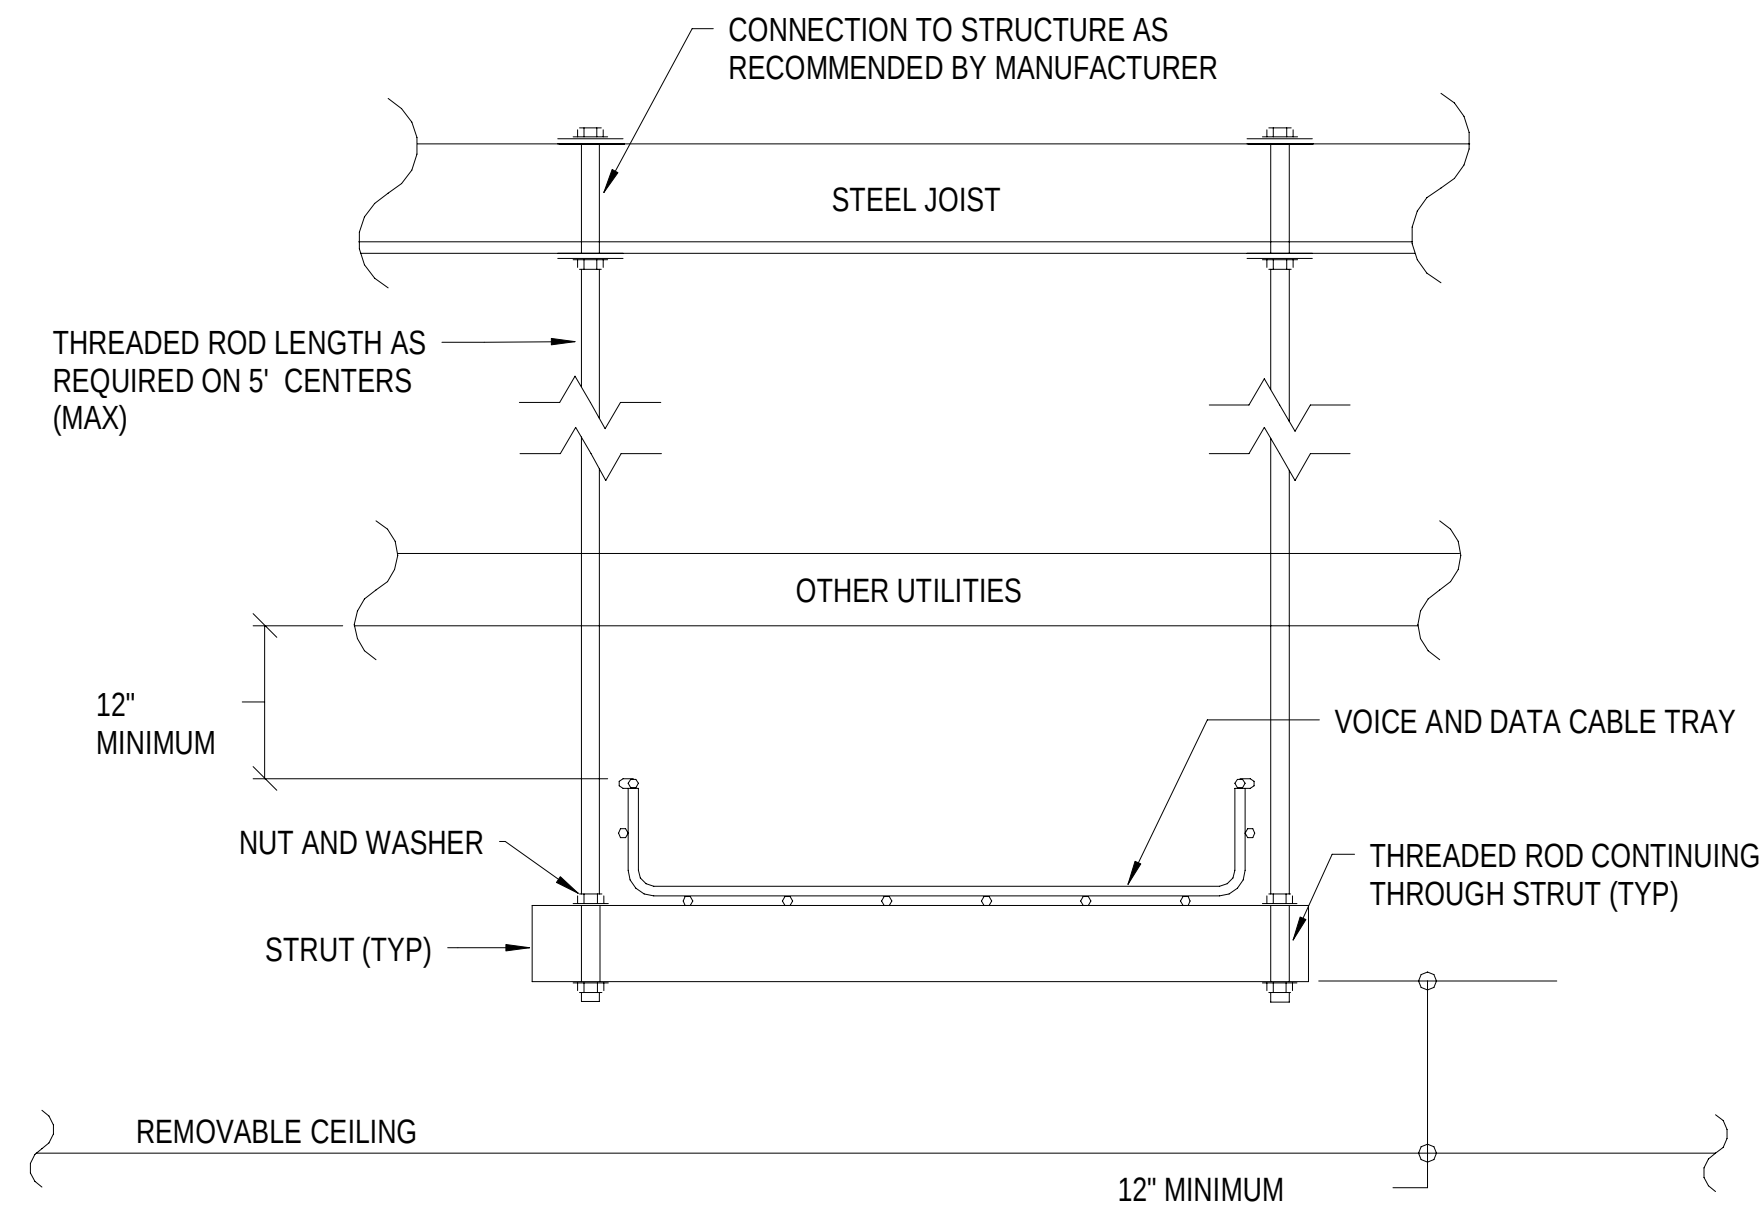

ABOVE CEILING MOUNTED CABLE TRAY

A3 TELECOM CABLE TRAY MOUNTING DETAILS

[illegible]

Jacobs
1100 NORTH GLEBE ROAD
SUITE 500
ARLINGTON, VIRGINIA 22201
571.218.1000
FAX: 571.218.1600

APPROVED:

FOR COMMANDER NAVFAC


ACTIVITY
APPROVED BY LCDR ELIZABETH
OLOKODE NAVFAC NLON FEAD
DIRECTOR NEW LONDON, GROTON, CT

DES	RR	DRW	RR	CHK	SA
PM/DM				SDS / RSF	
BRANCH MANAGER				WRB	
CHIEF ENG/ARCH				JWJ	
FIRE PROTECTION				HPN	

DEPARTMENT OF THE NAVY NAVAL FACILITIES ENGINEERING SYSTEMS COMMAND - MID-ATLANTIC MID-ATLANTIC NAVAL FACILITIES ENGINEERING SYSTEMS COMMAND NAVAL STATION - NORFOLK, VA	NAVAL SUBMARINE BASE NEW LONDON GROTON, CONNECTICUT P-1102 WEAPONS MAGAZINE & ORDNANCE OPERATIONS FACILITY OPERATIONS TELECOMMUNICATIONS DETAILS
--	---

SCALE: AS NOTED	
EPROJECT NO.:	1667770
CONSTR. CONTR. NO.	
NAVFAC DRAWING NO.	
12894063	
SHEET 113	OF 140

T-504

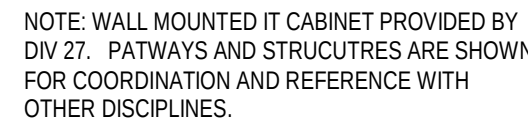

NTS

[illegible]**INFO**

FOR COMMANDER NAVFAC

DES	RR	DBW	RR	CHK	SA
-----	----	-----	----	-----	----

BRANCH MANAGER WRB

FIRE PROTECTION		FFN

COMM-
TIC
OL
CTH
LIT

ITEM
TITLE
UNIT - 1
CONC
FA

WG	III	STA	MO	O
----	-----	-----	----	---

GER

ALL	$\in C$	NC	SAL
-----	---------	----	-----

MS	AI	MS
----	----	----

YS	DR	AT	CA
----	----	----	----

IN	ON E O	MM
----	--------	----

NAME	LOG	GA	FILE
------	-----	----	------

El	En	N
----	----	---

NAME: _____
 ID: _____

OF	MA
FA	W

111

2	2	

CONSTR. CONTR. NO.

NAVFAC DRAWING NO.

SHEET	114	OF	140
-------	-----	----	-----

[illegible]

5

D1 DUCTBANK - (4) 4" 2X2
N.T.S.

C1 DUCTBANK - COUPLER CONNECTION
N.T.S.

A1 HANDHOLE DETAILS - TYPE 3

D2 DUCTBANK - (2) 4" 1X2
N.T.S.



- KEYED NOTES:
- ① USE PEA GRAVEL OR PIT RUN SAND. SEE SPECIFICATION SECTION 31 20 00.
 - ② COVER WITH 6" MAXIMUM THICK REINFORCED CONCRETE ON ALL SIDES (3000 PSI)
 - ③ INSTALL COMPACTED "SELECT BACKFILL" UP TO TOP OF DUCTBANK ELEVATION.

DUCTBANK - HANDHOLE CONNECTION

- NOTES:**
1. ELEVATION ABOVE SHOWS A TYPICAL SINGLE CONDUIT FOR ILLUSTRATION PURPOSES. REFER TO PLANS FOR ACTUAL QUANTITY OF CONDUITS.
 2. REFER TO TYPICAL UNDERGROUND CONDUIT SECTION DETAIL FOR CONCRETE ENCASEMENT REQUIREMENTS.
 3. REFER TO MANHOLE AND VAULT DETAILS FOR CONNECTION REQUIREMENTS.

DUCT BANK SECTION - CONDUIT ROUTING ELEVATION

B4 DUCTBANK - UNDER ROADWAY
N.T.S.

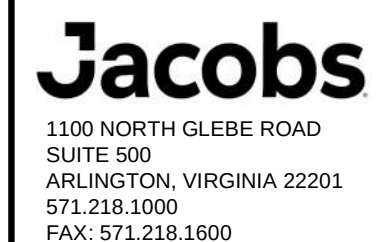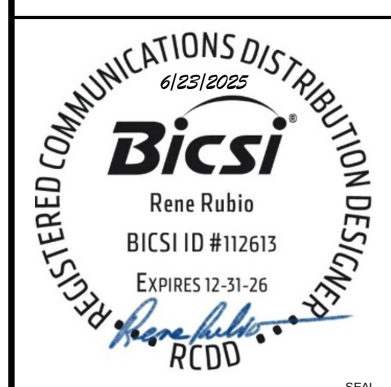
[illegible]

APPROVED				A/E INFO	
FOR COMMANDER NAVFAC					
ACTIVITY					
APPROVED BY LCDR ELIZABETH OLOKODE NAVFAC NLON FEAD DIRECTOR NEW LONDON, GROTON, CT					
SATISFACTORY TO DATE				05/27/2025	
DES	RR	DRW	RR	CHK	SA
PMDM				SDS / RSF	
BRANCH MANAGER				WRB	
CHIEF ENG/ARCH				1M/1	


DEPARTMENT OF THE NAVY	NAVAL FACILITIES ENGINEERING SYSTEMS COMMAND
NAVAL FACILITIES ENGINEERING SYSTEMS COMMAND - MID-ATLANTIC	
MID-ATLANTIC	NAVAL STATION - NORFOLK, VA
NAVAL SUBMARINE BASE NEW LONDON	GROTON, CONNECTICUT
P-1102 WEAPONS MAGAZINE & ORDNANCE OPERATIONS FACILITY OPERATIONS	
TELECOMMUNICATIONS DETAILS	

SCALE:	AS NOTED	
EPROJECT NO.:	1667770	
CONSTR. CONTR. NO.		
NAVFAC DRAWING NO.		
	12894066	
SHEET	116	OF 140
T-507		


5

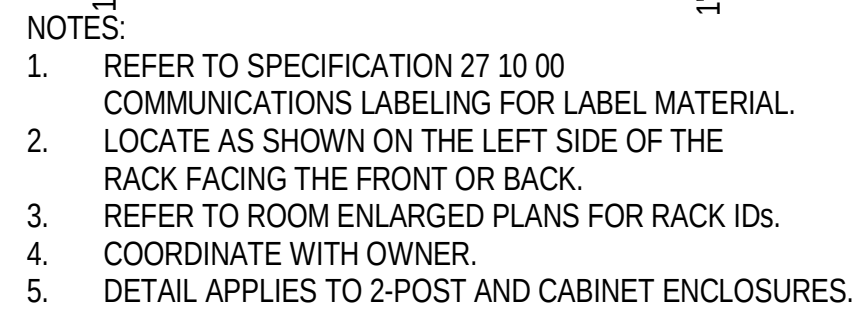


NTS

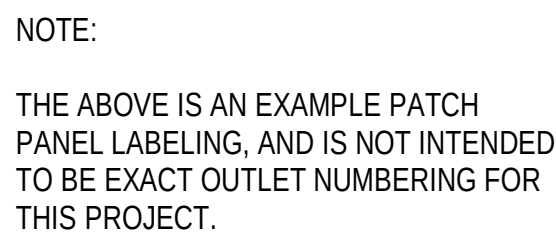

NTS

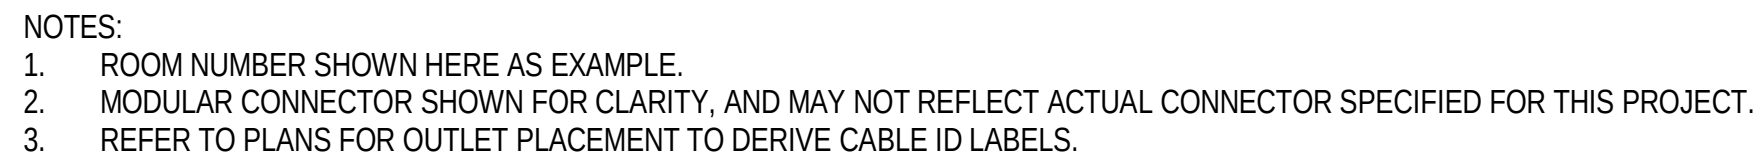

NTS

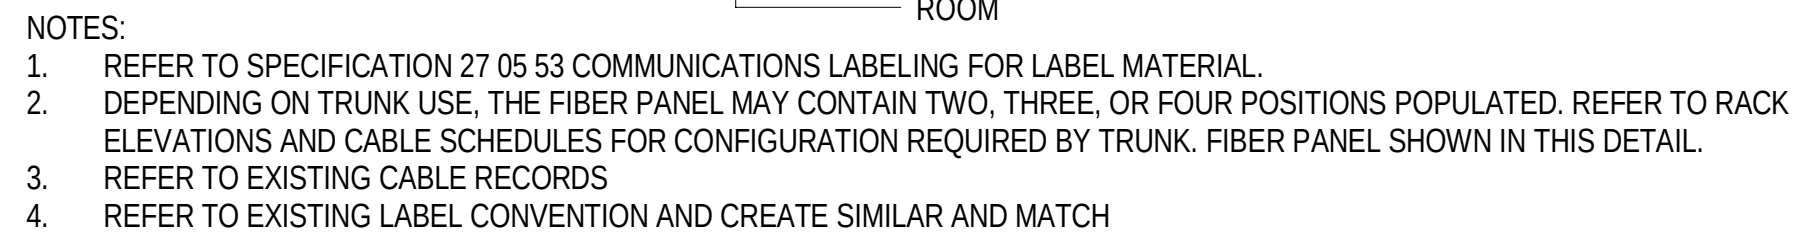

NTS



SCALE: AS NOTED		
EPROJECT NO.:		1667770
CONSTR. CONTR. NO.		
NAVFAC DRAWING NO.		
		12894069
SHEET	119	OF 140
T-510		


[illegible]

D

C

B

A

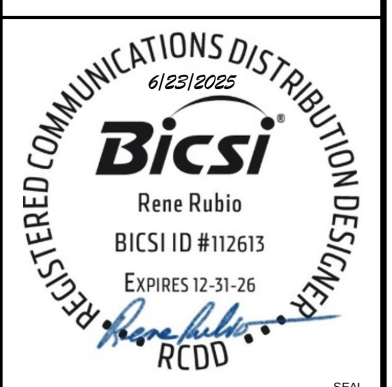[illegible]

Jacobs
1100 NORTH GLEBE ROAD
SUITE 500
ARLINGTON, VIRGINIA 22201
571.218.1000
FAX: 571.218.1600

				AE INFO	
APPROVED					
FOR COMMANDER NAVFAC					
ACTIVITY					
APPROVED BY LCDR ELIZABETH					
OLOKODE NAVFAC NLON FEAD					
DIRECTOR NEW LONDON, GROTON, CT					
SATISFACTORY TO DATE				05/27/2025	
DES	RR	DRW	RR	CHK	SA
PM/DM				SDS / RSF	
BRANCH MANAGER				WRB	
CHIEF ENGR/ACH				JWJ	
FIRE PROTECTION				HPN	

DEPARTMENT OF THE NAVY NAVAL FACILITIES ENGINEERING SYSTEMS COMMAND MID-ATLANTIC NAVAL SUBMARINE BASE NEW LONDON P-1102 WEAPONS MAGAZINE & ORDNANCE OPERATIONS FACILITY OPERATIONS	NAVAL FACILITIES ENGINEERING SYSTEMS COMMAND MID-ATLANTIC NAVAL STATION - NORFOLK, VA GROTON, CONNECTICUT
ONE LINE OSP RISER DIAGRAM	

SCALE: AS NOTED			
EPROJECT NO.:		1667770	
CONSTR. CONTR. NO.			
NAVFAC DRAWING NO.			
		12894072	
SHEET	122	OF	140
T-603			

109	FPD-B	70"	4'-0"
126	FPD-B	70"	5'-6"
127	FPD-A	60"	4'-0"
128	FPD-A	60"	4'-0"
129	FPD-A	60"	4'-0"
130	FPD-A	60"	4'-0"
131	FPD-E	86"	4'-0"
131	FPD-E	86"	4'-0"




Jacobs
100 NORTH GLEBE ROAD
SUITE 500
ARLINGTON, VIRGINIA 22201
TEL: 71.218.1000
FAX: 571.218.1600

APPROVED				AE INFO	
COMMANDER NAVFAC					
APPROVED BY LCDR ELIZABETH OLOKODE NAVFAC NLON FEAD DIRECTOR NEW LONDON, GROTON, CT					
FACTORY TO DATE				05/27/2025	
SJY	DRW	TLO	CHK	JFH	
M				SDS / RS	
CH MANAGER				WR	
ENGIARCH				JW	
PROTECTION				HP	

NAVAL FACILITIES ENGINEERING SYSTEMS COMMAND - MID-ATLANTIC
 MID-ATLANTIC
 NAVAL SUBMARINE BASE NEW LONDON
 GROTON, CONNECTICUT
 P-1102 WEAPONS MAGAZINE & ORDNANCE OPERATIONS FACILITY

E: AS NOTED			
PROJECT NO.:		1667770	
STR. CONTR. NO.			
FAC DRAWING NO.			
12894074			
ET	124	OF	140

6/20/2025 1:13:17 PM TA101
\\ac1vrs01\app\p\FDZ\EL628\TELEBLOG-166770-1-BN1_V21.rvt

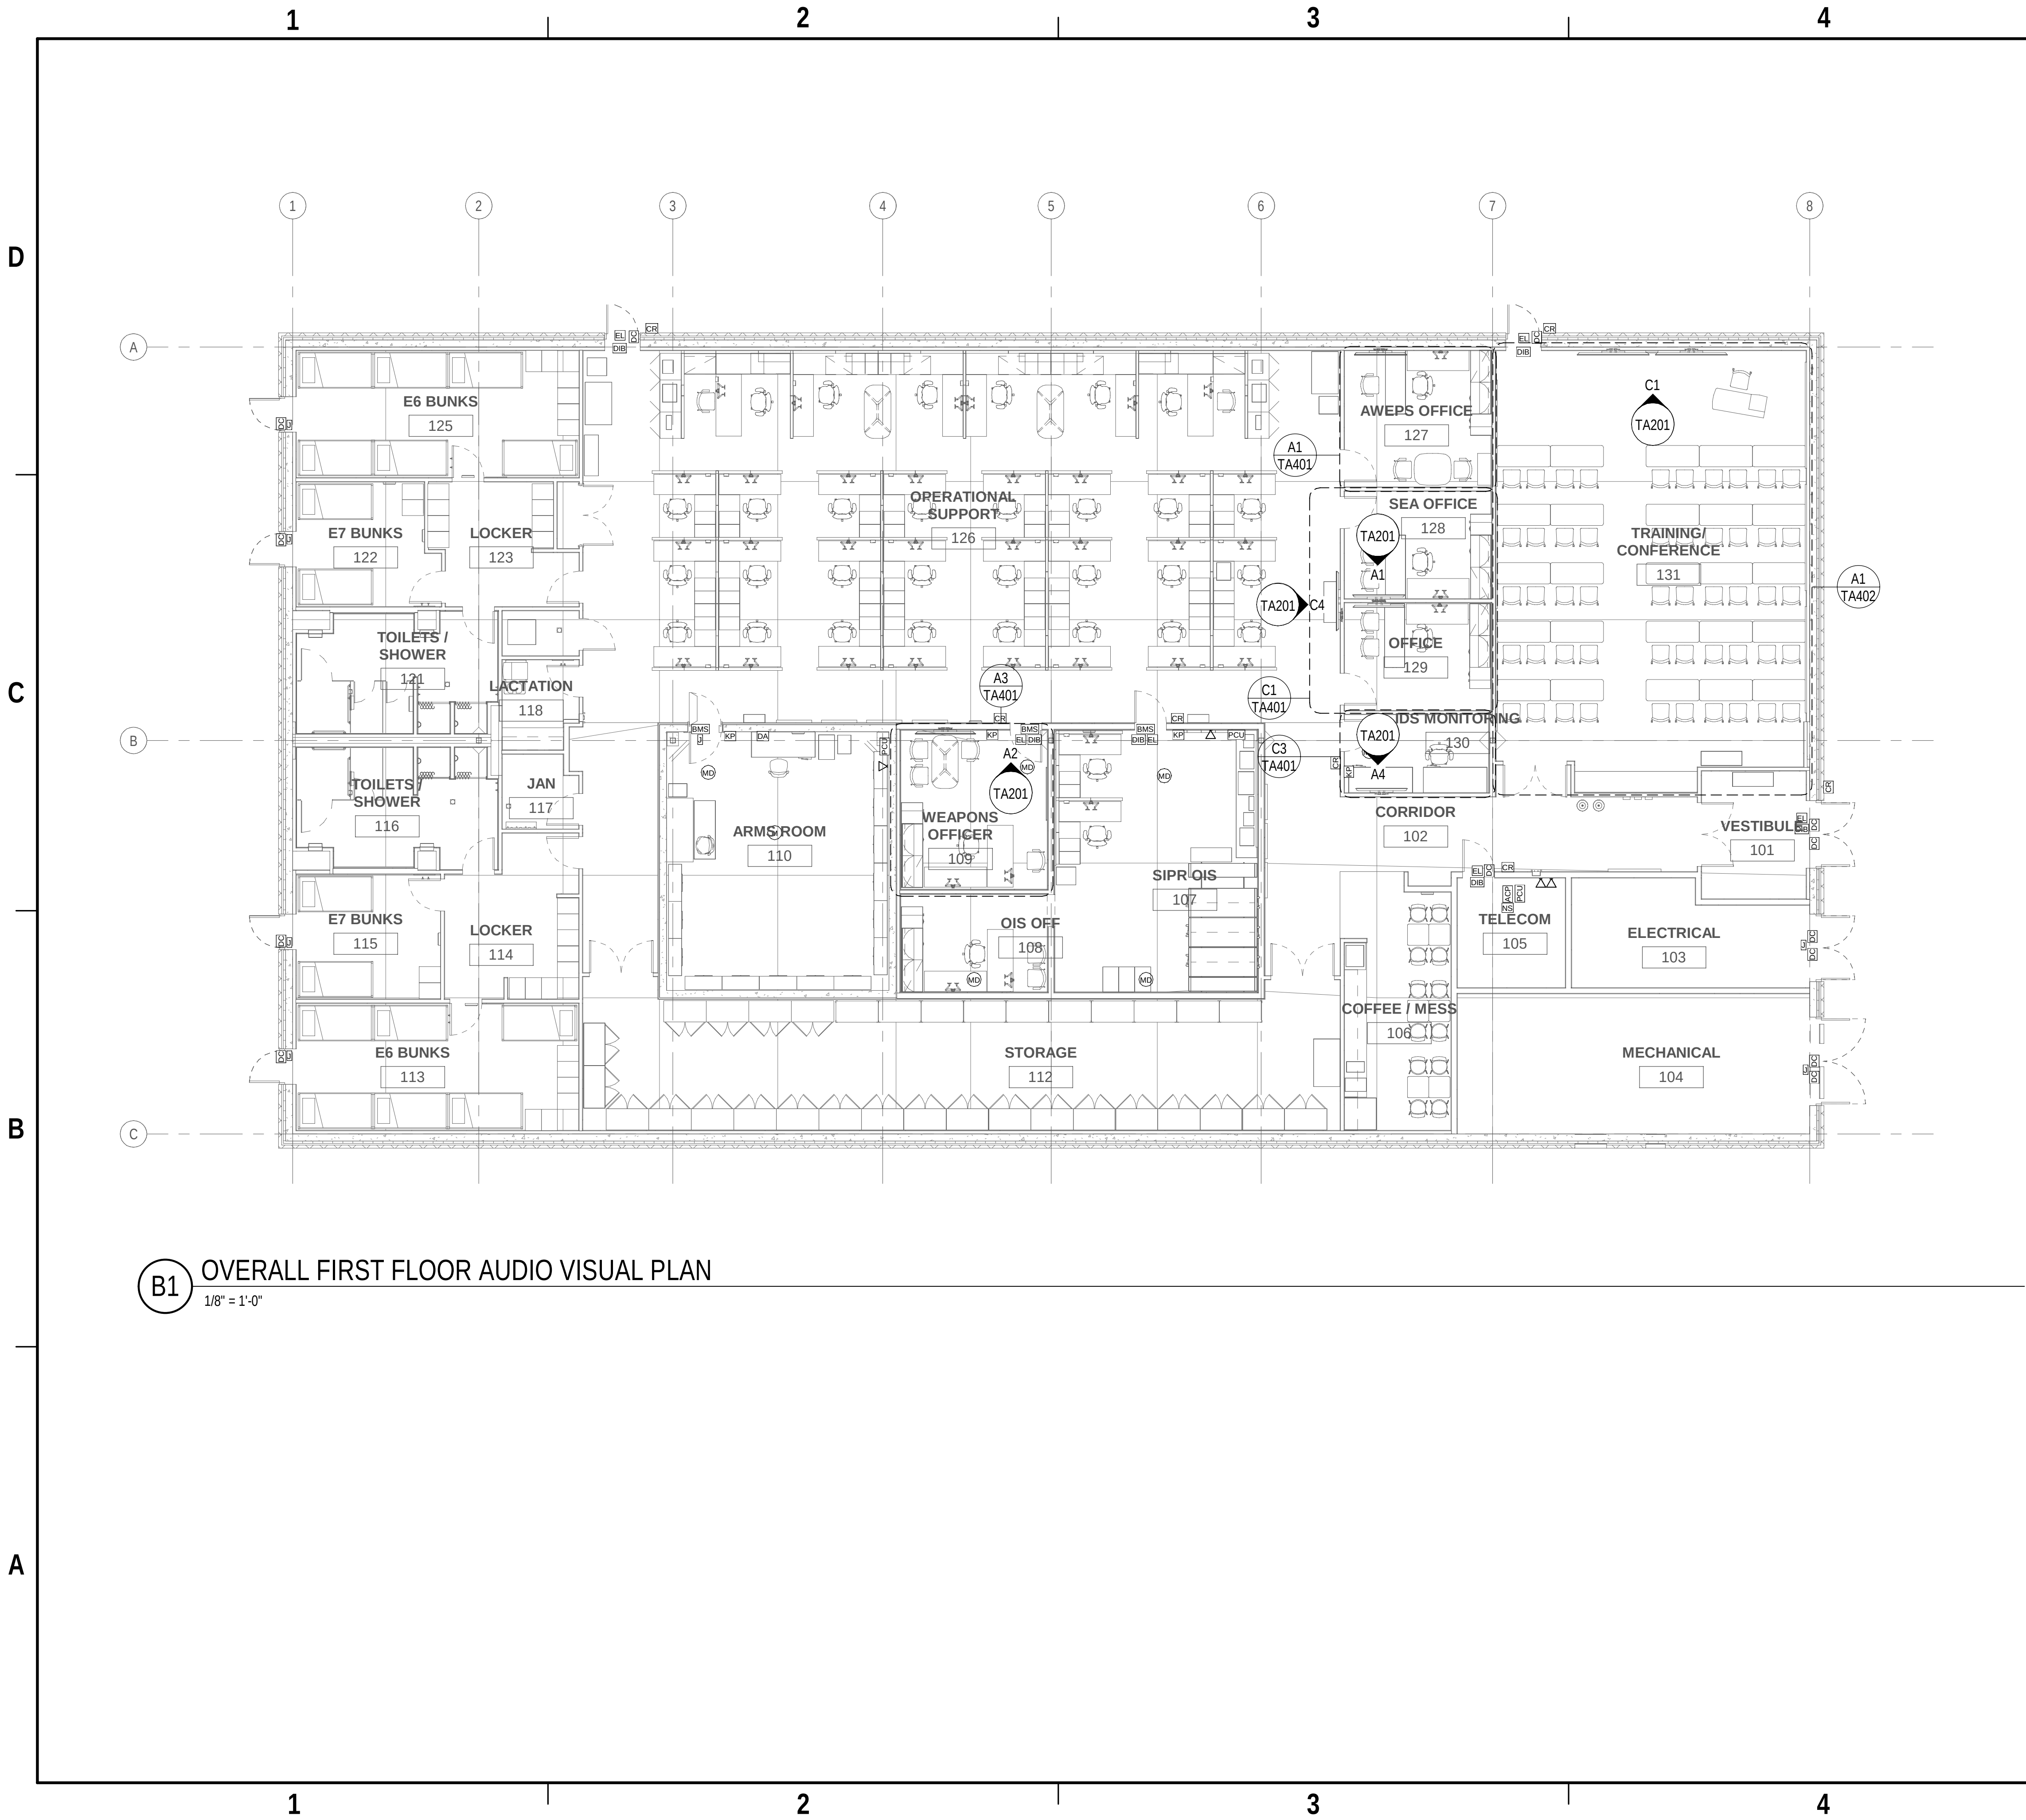

B1 OVERALL FIRST FLOOR AUDIO VISUAL PLAN
1/8" = 1'-0"

GENERAL SHEET NOTES

A. REFER TO SHEET TA001 FOR AUDIO VISUAL SYMBOLS AND ABBREVIATIONS.

SYN	DESCRIPTION	DATE	APPR




Jacobs
1100 NORTH GLEBE ROAD
SUITE 500
ARLINGTON, VIRGINIA 22201
571.218.1000
FAX: 571.218.1600

APPROVED	AE INFO
FOR COMMANDER NAVFAC	
ACTIVITY	APPROVED BY LCDR ELIZABETH CLOKODE NAVFAC NLON FEAD DIRECTOR NEW LONDON, GROTON, CT
SATISFACTORY TO DATE	05/27/2025
DES	SJY
DRW	TLO
CHK	JFH
PMOM	SDS / RSF
BRANCH MANAGER	WRB
CHIEF ENGINEER	JWJ
FIRE PROTECTION	HPN

DEPARTMENT OF THE NAVY
NAVAL FACILITIES ENGINEERING SYSTEMS COMMAND - MID-ATLANTIC
NAVAL STATION - NORFOLK, VA
NAVAL SUBMARINE BASE NEW LONDON
GROTON, CONNECTICUT
P-1102 WEAPONS MAGAZINE & ORDNANCE OPERATIONS FACILITY
OPERATIONS
AUDIO VISUAL FLOOR PLAN

SCALE: AS NOTED
PROJECT NO.: 1667770
CONSTR. CONTR. NO.
NAVFAC DRAWING NO. 12894075
SHEET 125 OF 140
TA101

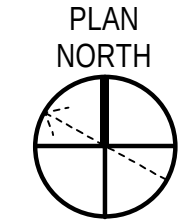

6/20/2025 1:13:29 PM TA201
\\ac1p501\app\pfd\21628\TELEBLOG-166770-T-BNL_V21.rvt




GENERAL SHEET NOTES

A REFER TO A_TA001 FOR SYMBOLS, ABBREVIATIONS AND GENERAL NOTES.

SHEET KEYNOTES

- 901 86" SMART DISPLAY WITH MOUNT AND BACKBOX. BOTTOM OF DISPLAY MOUNTED 48" A.F.F. SEE C1/A_TA501 FOR DETAIL.
902 70" DISPLAY WITH MOUNT AND OFFSET BACKBOX. BOTTOM OF DISPLAY MOUNTED AT 66" A.F.F. SEE C3/A_TA501 FOR DETAIL.
903 60" DISPLAY WITH MOUNT AND BACKBOX. BOTTOM OF DISPLAY MOUNTED AT 48" A.F.F. SEE C1/A_TA501 FOR DETAIL.
904 70" DISPLAY WITH MOUNT AND BACKBOX. BOTTOM OF DISPLAY MOUNTED AT 48" A.F.F. SEE C1/A_TA501 FOR DETAIL.
905 12 RU SPACE 27" DEEP AUDIO VISUAL EQUIPMENT RACK.

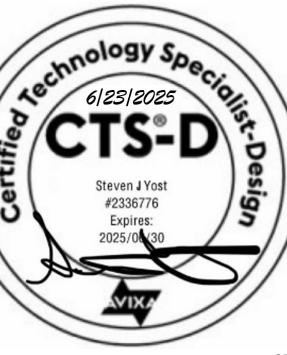

Jacobs
1100 NORTH GLEBE ROAD
SUITE 500
ARLINGTON, VIRGINIA 22201
571.218.1000
FAX: 571.218.1600

APPROVED

FOR COMMANDER NAVFAC

ACTIVITY APPROVED BY LCDR ELIZABETH
CLOKODE NAVFAC NLON FEAD
DIRECTOR NEW LONDON, GROTON, CT

SATISFACTORY TO DATE 05/27/2025

DES SJY DRW TLO CHK JFH

PMOM SDS / RSF

BRANCH MANAGER WRB

CHIEF ENGINEER JWJ

FIRE PROTECTION HPN

DEPARTMENT OF THE NAVY
NAVAL FACILITIES ENGINEERING SYSTEMS COMMAND - MID-ATLANTIC
NAVAL STATION - NORFOLK, VA
NAVAL SUBMARINE BASE NEW LONDON
GROTON, CONNECTICUT
P-1102 WEAPONS MAGAZINE & ORDNANCE OPERATIONS FACILITY
OPERATIONS

AUDIO VISUAL ELEVATIONS

SCALE: AS NOTED

PROJECT NO.: 1667770

CONSTR. CONTR. NO.


NAVFAC DRAWING NO. 12894076

SHEET 126 OF 140


TA201

6/20/2025 1:13:42 PM
\\ac1v950\\user\\jfd\\ZEL628\\TELEBLDG-16677D-1-BN_V21.rvt


TA401

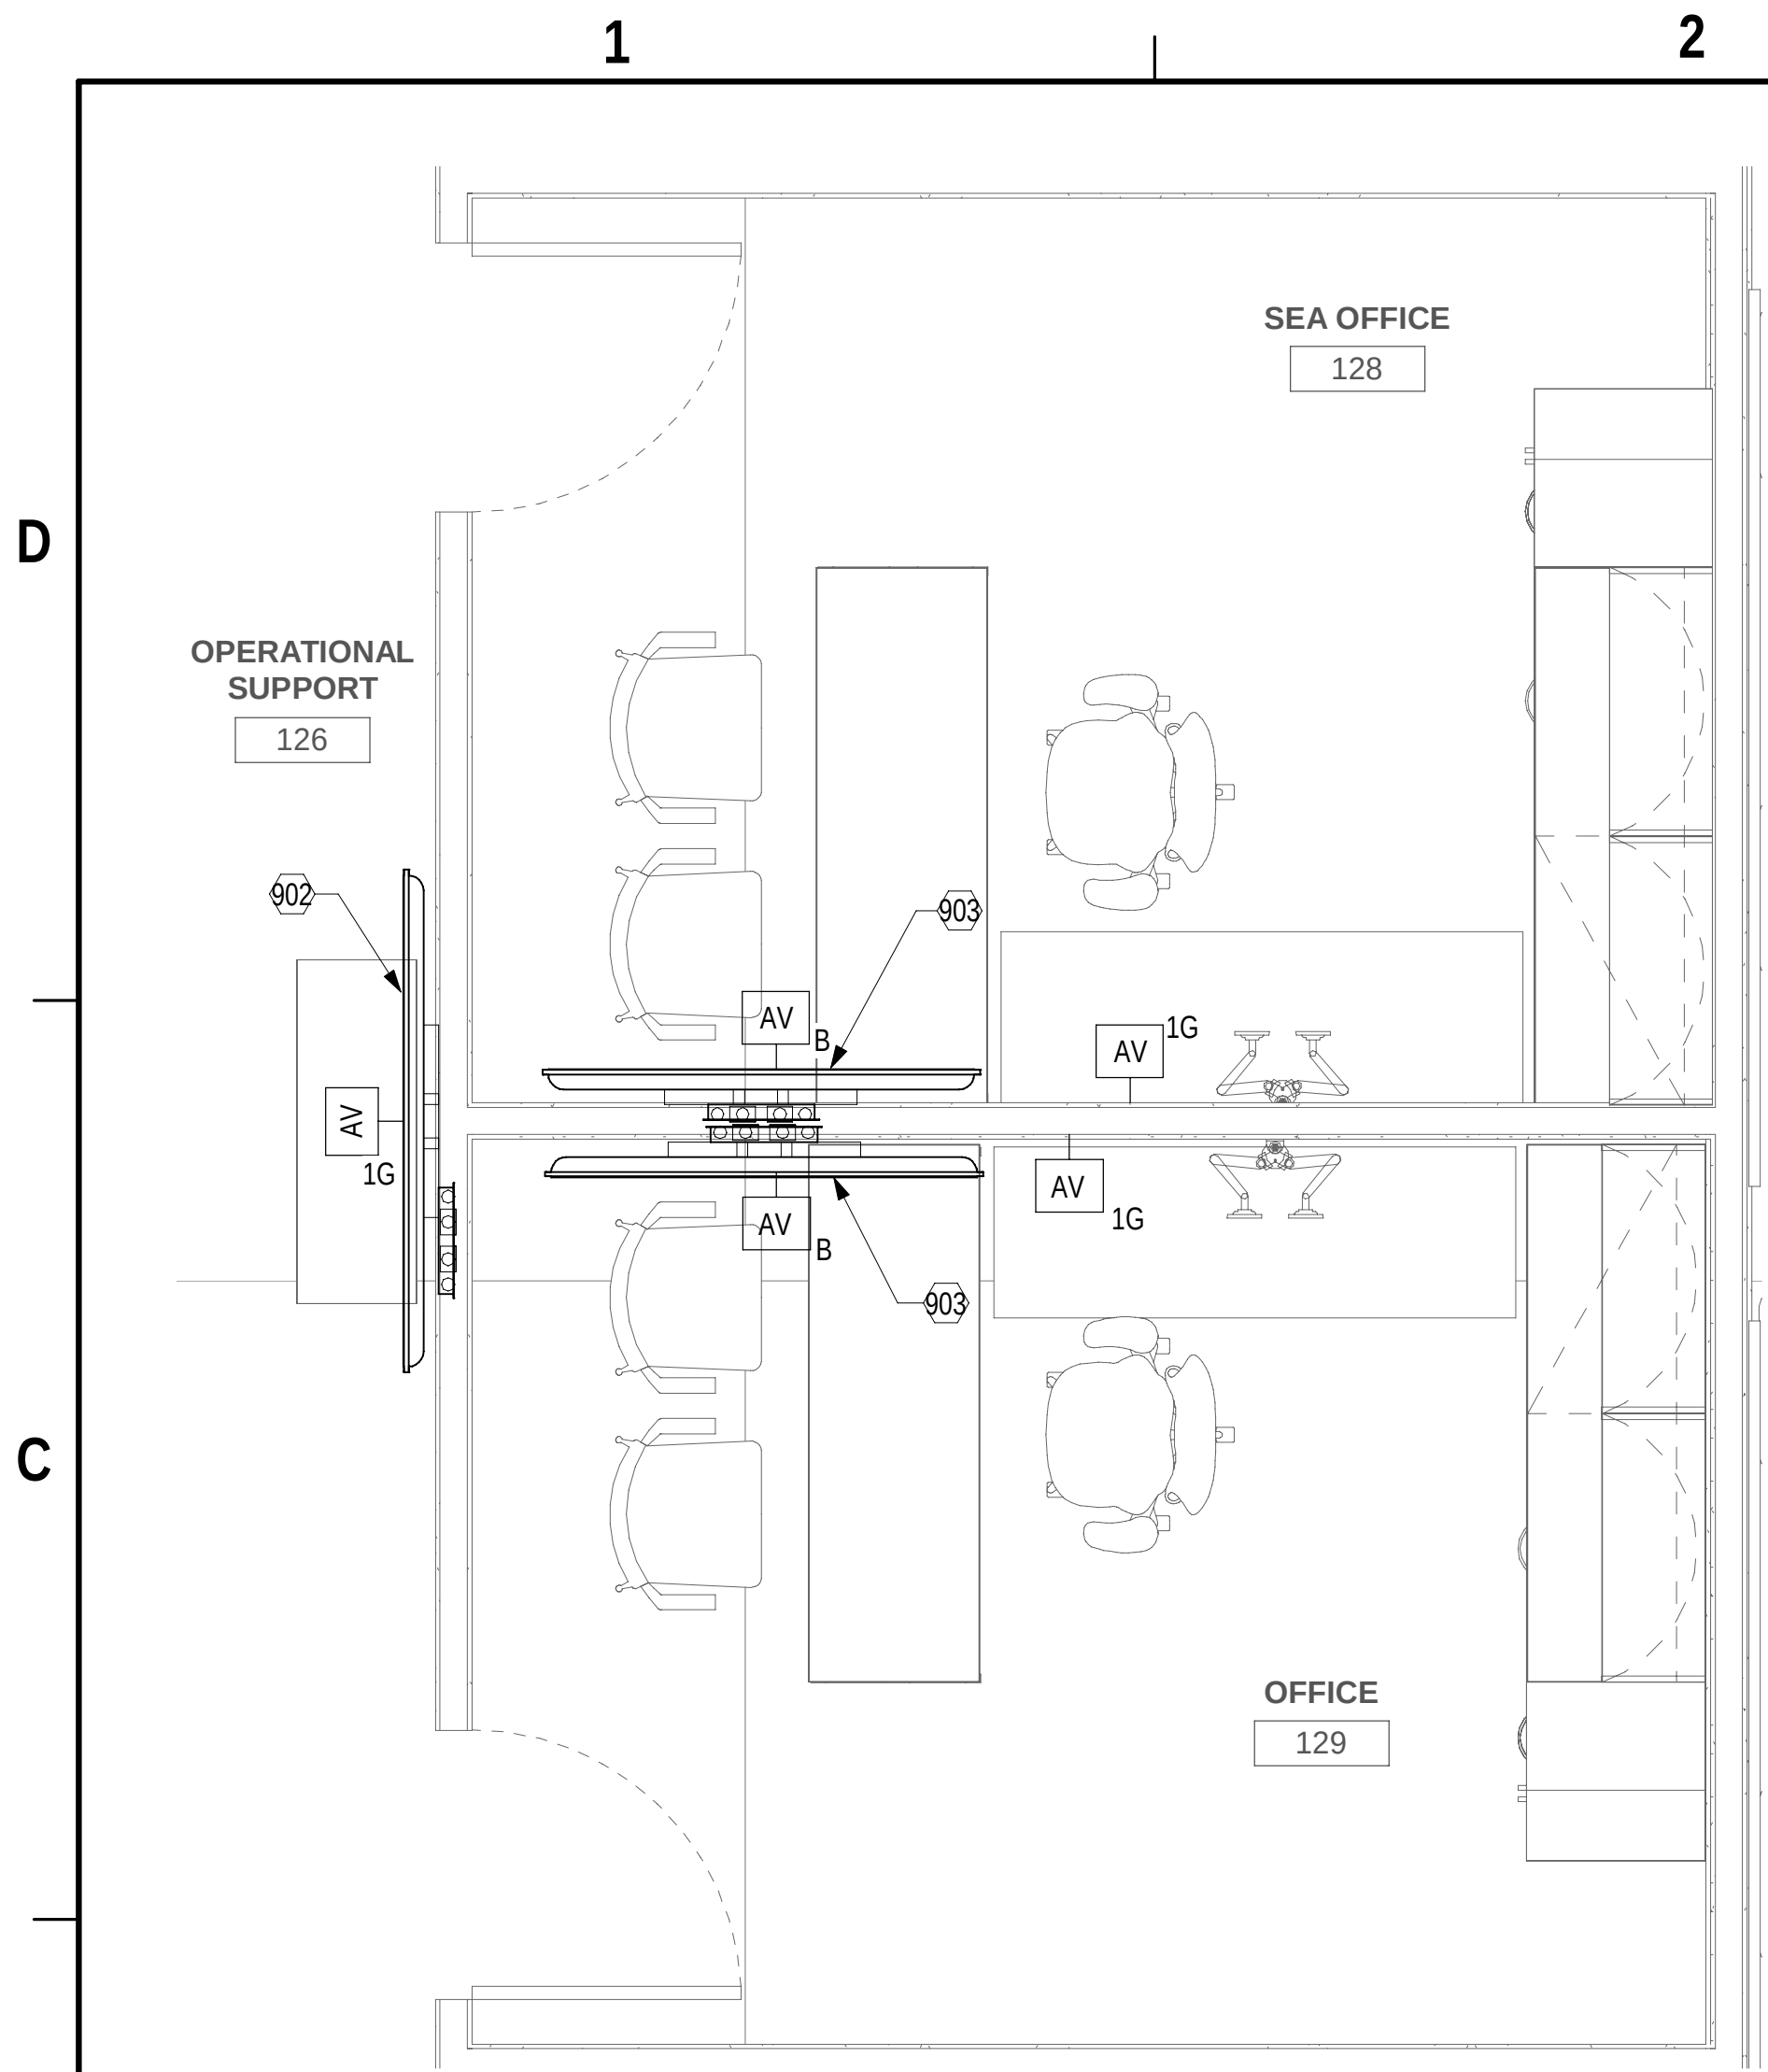


C1 AUDIO VISUAL ENLARGED PLAN - ROOMS 126, 128 & 129
1/2" = 1'-0" (TA101)

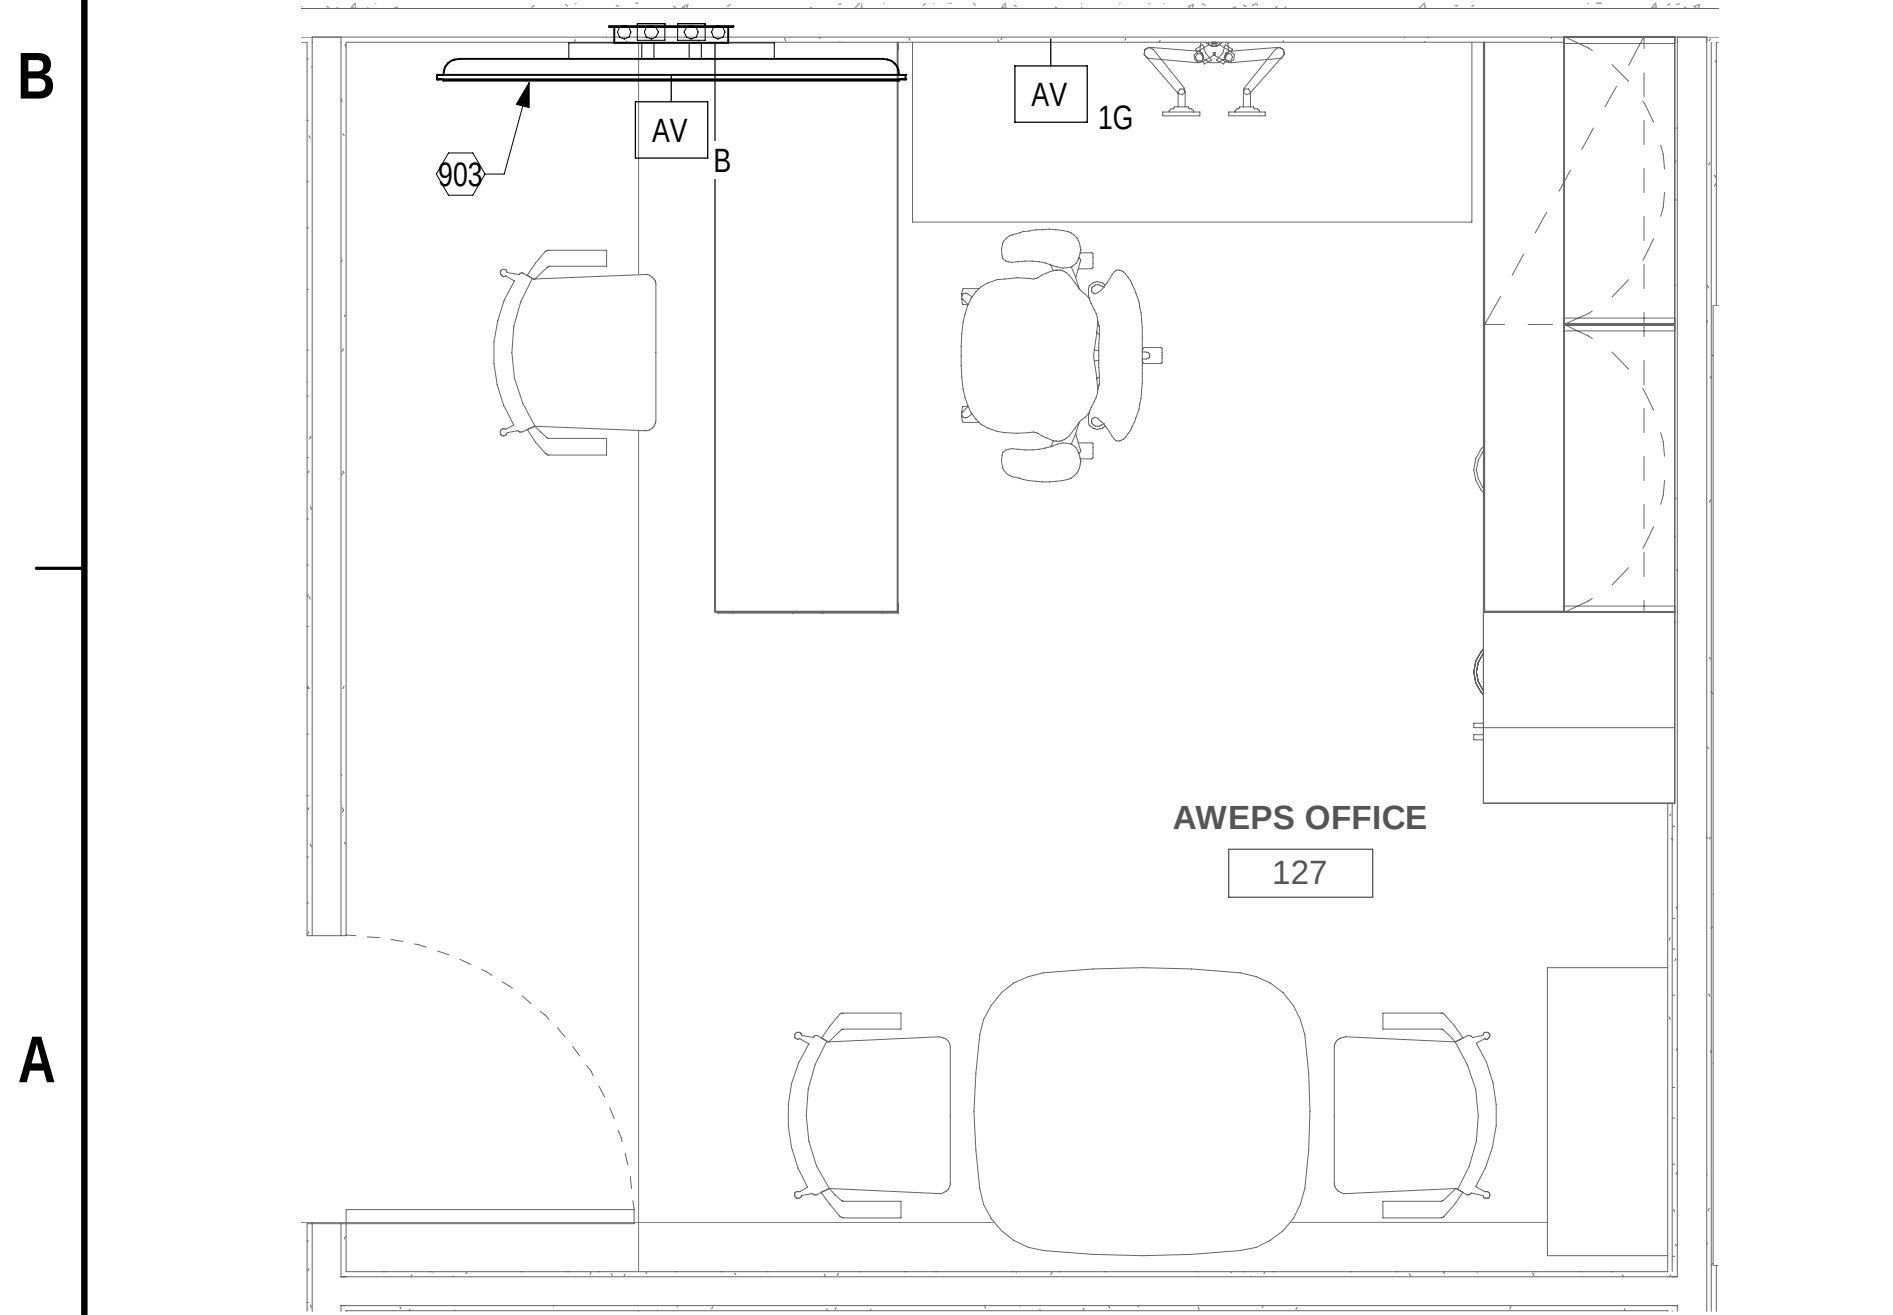

A1 AUDIO VISUAL ENLARGED PLAN - ROOM 127
1/2" = 1'-0" (TA101)

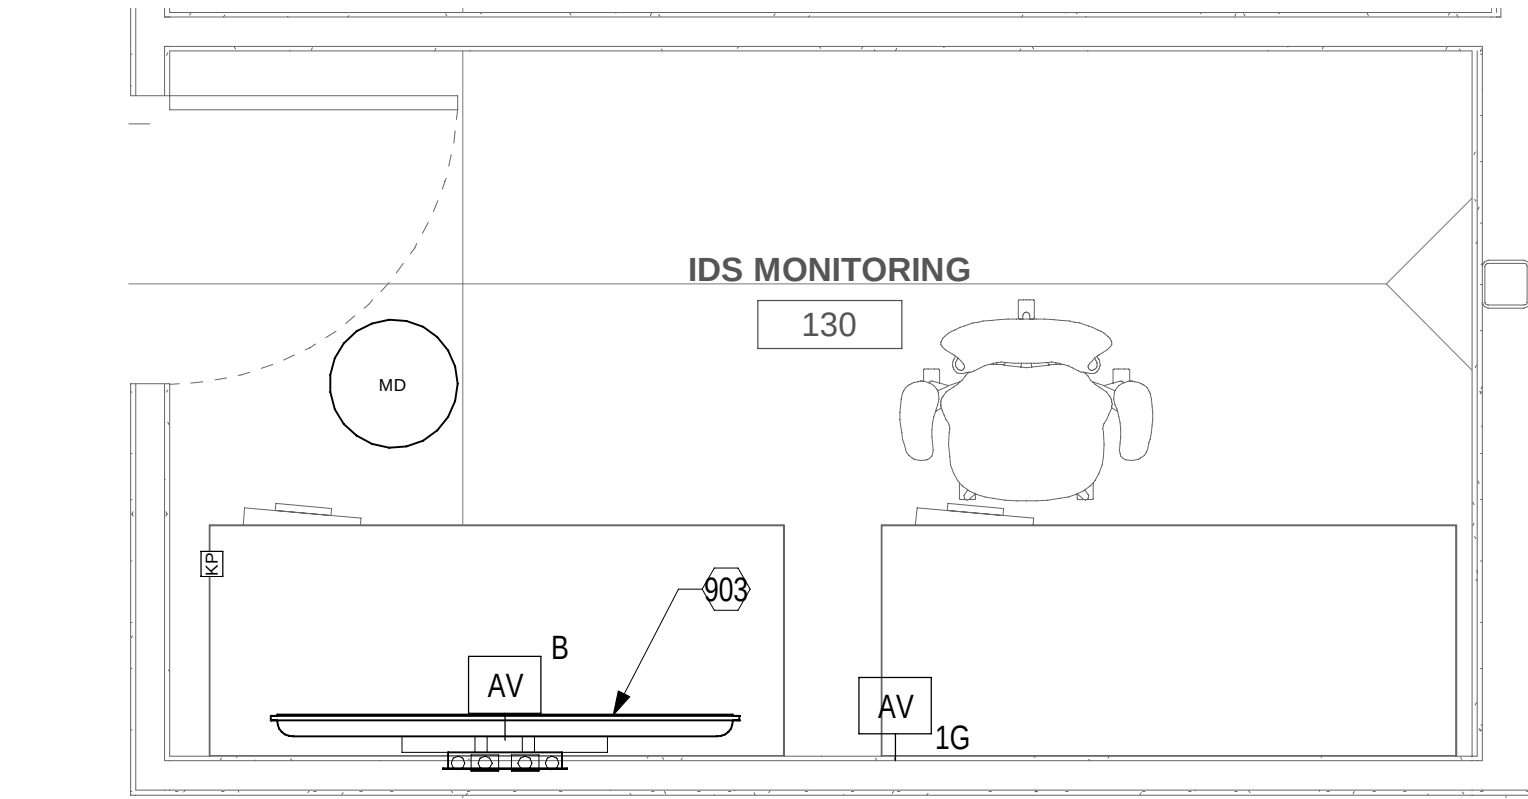

C3 AUDIO VISUAL ENLARGED PLAN - IDS MONITORING
1/2" = 1'-0" (TA101)

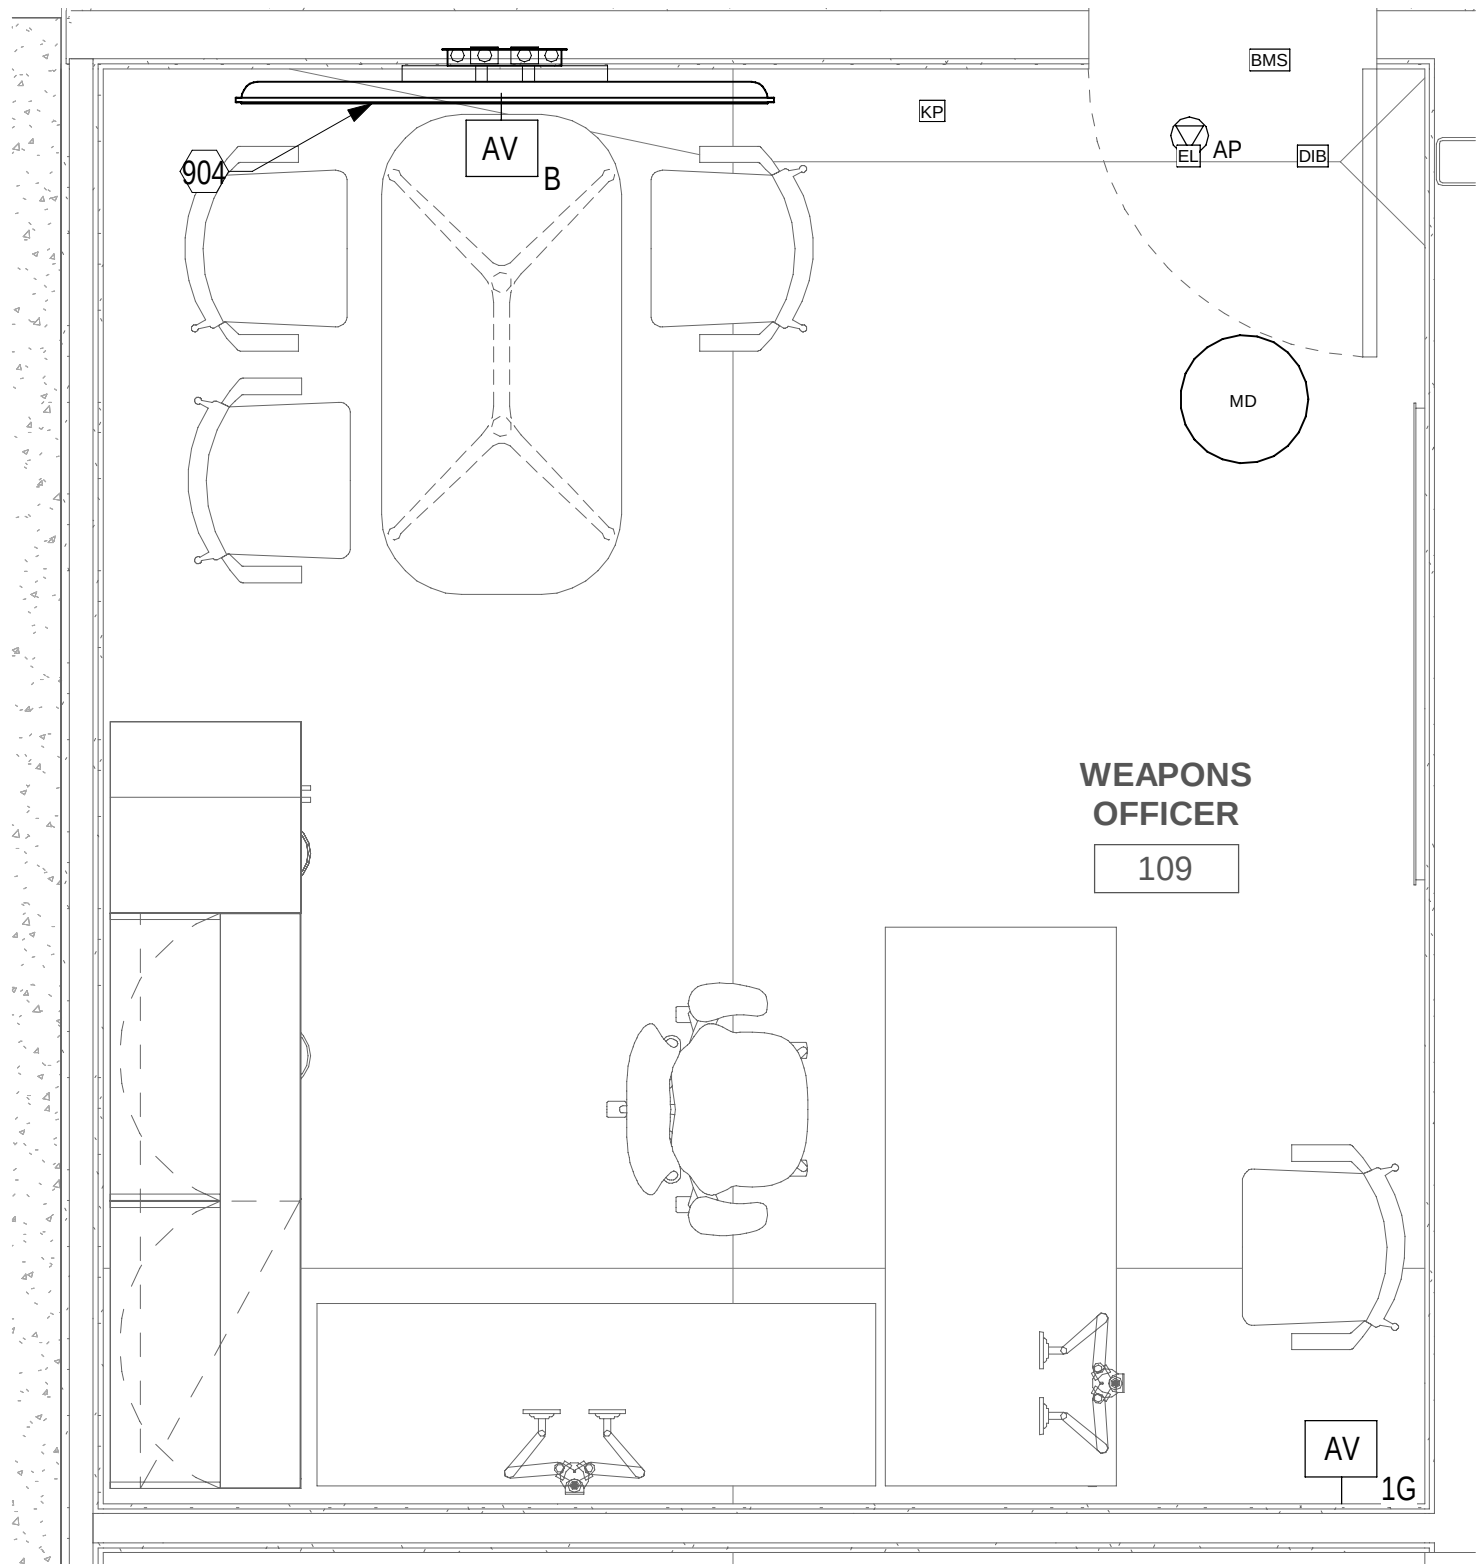

A3 AUDIO VISUAL ENLARGED PLAN - ROOM 109
1/2" = 1'-0" (TA101)

GENERAL SHEET NOTES

- REFER TO A_TA001 FOR SYMBOLS, ABBREVIATIONS AND GENERAL NOTES.

SHEET KEYNOTES

- 70" DISPLAY WITH MOUNT AND OFFSET BACKBOX. BOTTOM OF DISPLAY MOUNTED AT 66" A.F.F. SEE C3/A_TA501 FOR DETAIL.
- 60" DISPLAY WITH MOUNT AND BACKBOX. BOTTOM OF DISPLAY MOUNTED AT 48" A.F.F. SEE C1/A_TA501 FOR DETAIL.
- 70" DISPLAY WITH MOUNT AND BACKBOX. BOTTOM OF DISPLAY MOUNTED AT 48" A.F.F. SEE C1/A_TA501 FOR DETAIL.



Jacobs
1100 NORTH GLEBE ROAD
SUITE 500
ARLINGTON, VIRGINIA 22201
571.218.1000
FAX: 571.218.1600

APPROVED

FOR COMMANDER NAVFAC

ACTIVITY
APPROVED BY LCDR ELIZABETH
CLOKODE NAVFAC NLON FEAD
DIRECTOR NEW LONDON, GROTON, CT

SATISFACTORY TO DATE 05/27/2025

DES SJY DRW TLO CHK JFH

PMOM SDS / RSF

BRANCH MANAGER WRB

CHIEF ENGINEER JWI

FIRE PROTECTION HPN

NAVAL FACILITIES ENGINEERING SYSTEMS COMMAND

NAVAL FACILITIES ENGINEERING SYSTEMS COMMAND - MID-ATLANTIC

NAVAL STATION - NORFOLK, VA

NAVAL SUBMARINE BASE NEW LONDON

GROTON, CONNECTICUT

P-1102 WEAPONS MAGAZINE & ORDNANCE OPERATIONS FACILITY

OPERATIONS

AUDIO VISUAL ENLARGED PLANS

SCALE: AS NOTED

PROJECT NO.: 1667770

CONSTR. CONTR. NO.

NAVFAC DRAWING NO. 12894078

SHEET 128 OF 140

TA401

6/20/2025 1:13:52 PM
\\ac1vrs01\user\jfd\ZEL1628\TELEBLOG-1667701-18\NL_V21.rvt


TA402

A

B


C

D

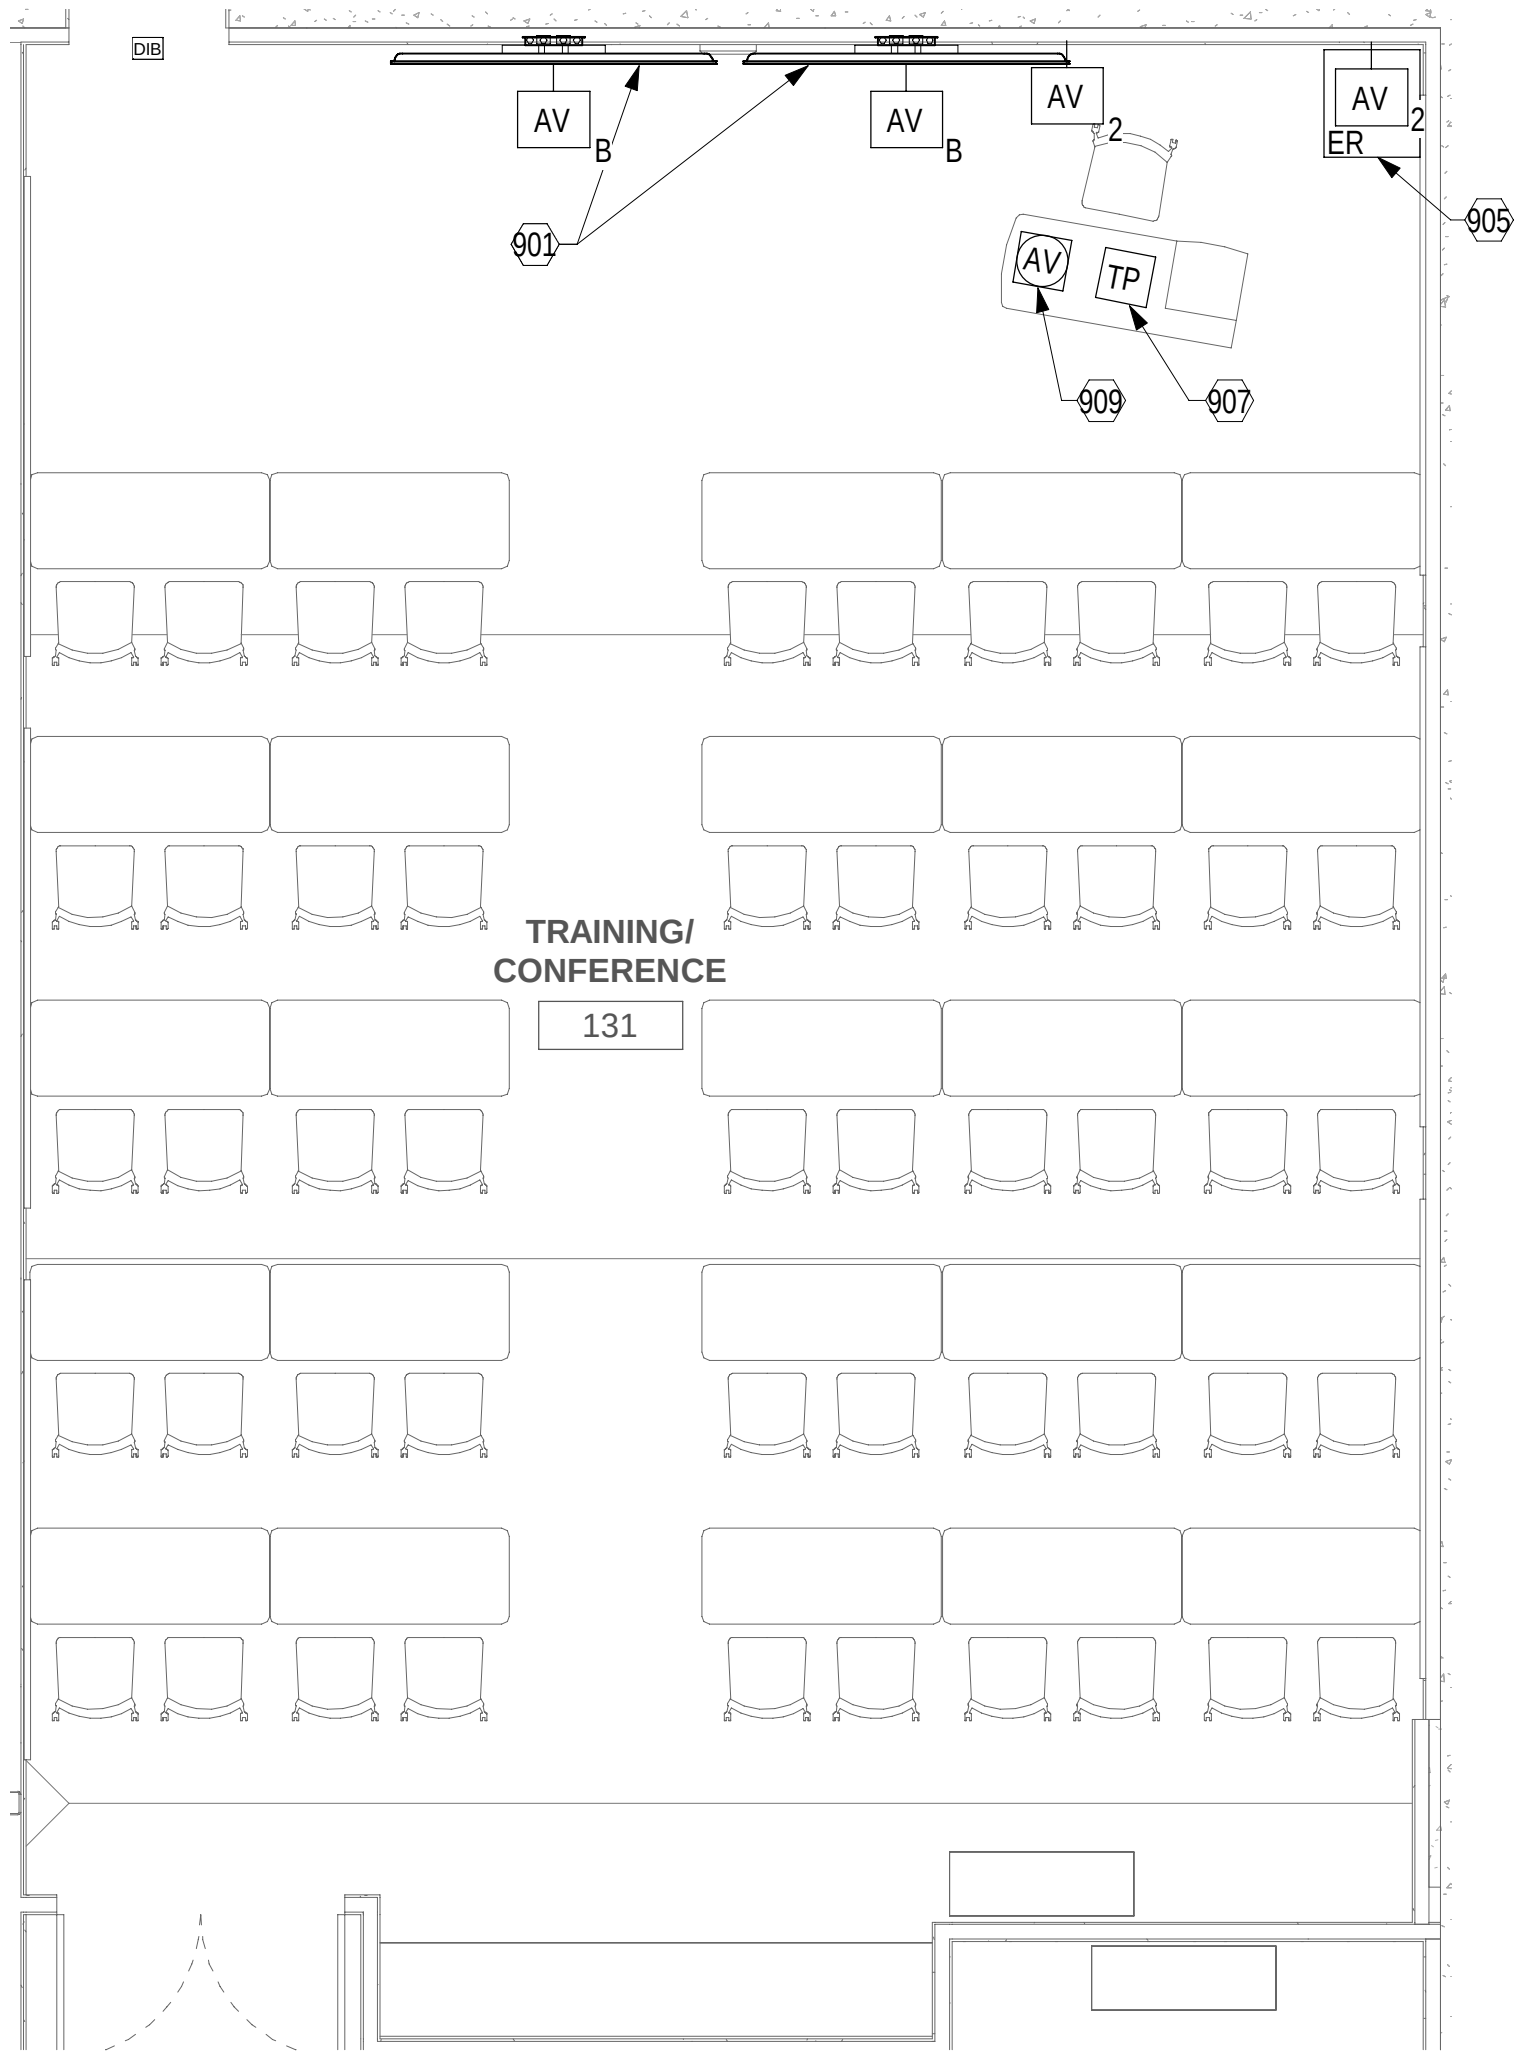

A1 AUDIO VISUAL ENLARGED PLANS - ROOM 131
1/4" = 1'-0" (TA101)

2

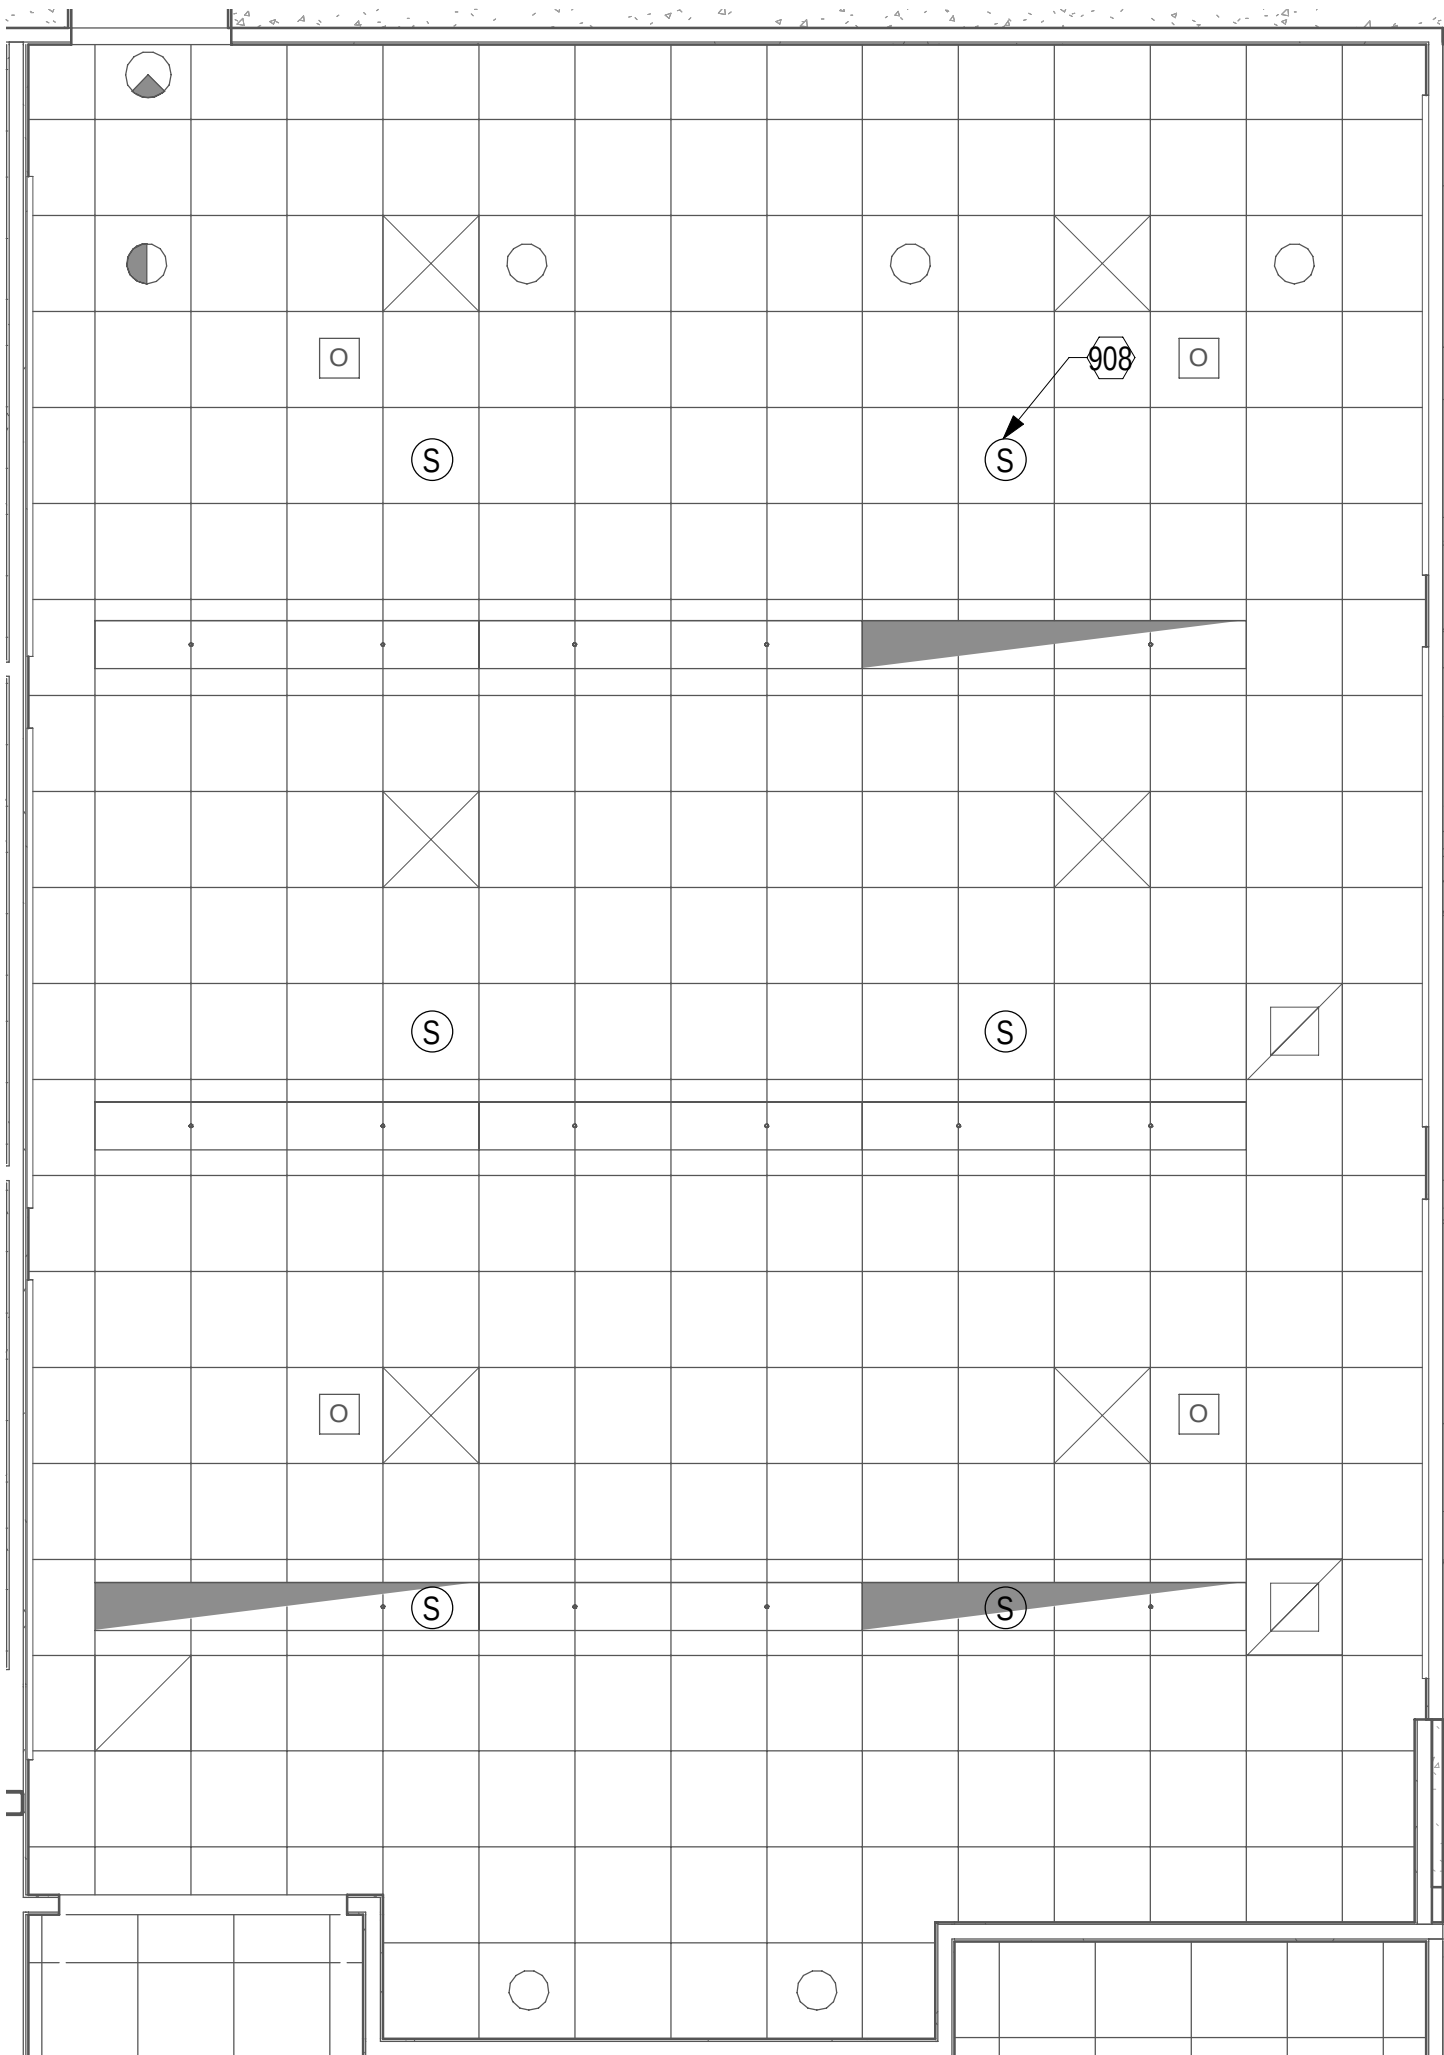

A3 AUDIO VISUAL ENLARGED PLANS - RCP ROOM 131
1/4" = 1'-0"

3

4

GENERAL SHEET NOTES

A. REFER TO TA001 FOR SYMBOLS, ABBREVIATIONS AND GENERAL NOTES.

SHEET KEYNOTES

- 901 86" SMART DISPLAY WITH MOUNT AND BACKBOX. BOTTOM OF DISPLAY MOUNTED 48" A.F.F. SEE C1/A_TA501 FOR DETAIL.
905 12 RU SPACE 27" DEEP AUDIO VISUAL EQUIPMENT RACK.
907 TABLE MOUNTED TOUCH CONTROL PANEL.
908 CEILING RECESSED LOUDSPEAKER.
909 REFER TO A1/TA502 FOR FLOORBOX DETAIL. AV CONDUIT PATHWAY STUBBED OUT TO OPEN CEILING.



Jacobs
1100 NORTH GLEBE ROAD
SUITE 500
ARLINGTON, VIRGINIA 22201
571.218.1000
FAX: 571.218.1600

APPROVED

FOR COMMANDER NAVFAC

ACTIVITY APPROVED BY LCDR ELIZABETH
CLOKODE NAVFAC NLON FEAD
DIRECTOR NEW LONDON, GROTON, CT

SATISFACTORY TO DATE 05/27/2025

DES SJY DRW TLO CHK JFH

PMOM SDS / RSF

BRANCH MANAGER WRB

CHIEF ENGINEER JWI

FIRE PROTECTION HPN

DEPARTMENT OF THE NAVY

NAVAL FACILITIES ENGINEERING SYSTEMS COMMAND

NAVAL FACILITIES ENGINEERING SYSTEMS COMMAND - MID-ATLANTIC

MID-ATLANTIC

NAVAL SUBMARINE BASE NEW LONDON

P-1102 WEAPONS MAGAZINE & ORDNANCE OPERATIONS FACILITY

GROTON, CONNECTICUT

OPERATIONS

AUDIO VISUAL ENLARGED PLANS

SCALE: AS NOTED

PROJECT NO.: 1667770


CONSTR. CONTR. NO.

NAVFAC DRAWING NO. 12894079


SHEET 129 OF 140

TA402


6/20/2025 1:13:56 PM
\\06119501\\06119501\\FDZEL1628\\TELEBLOG-1667770-18\\ML_V21.rvt
TA501

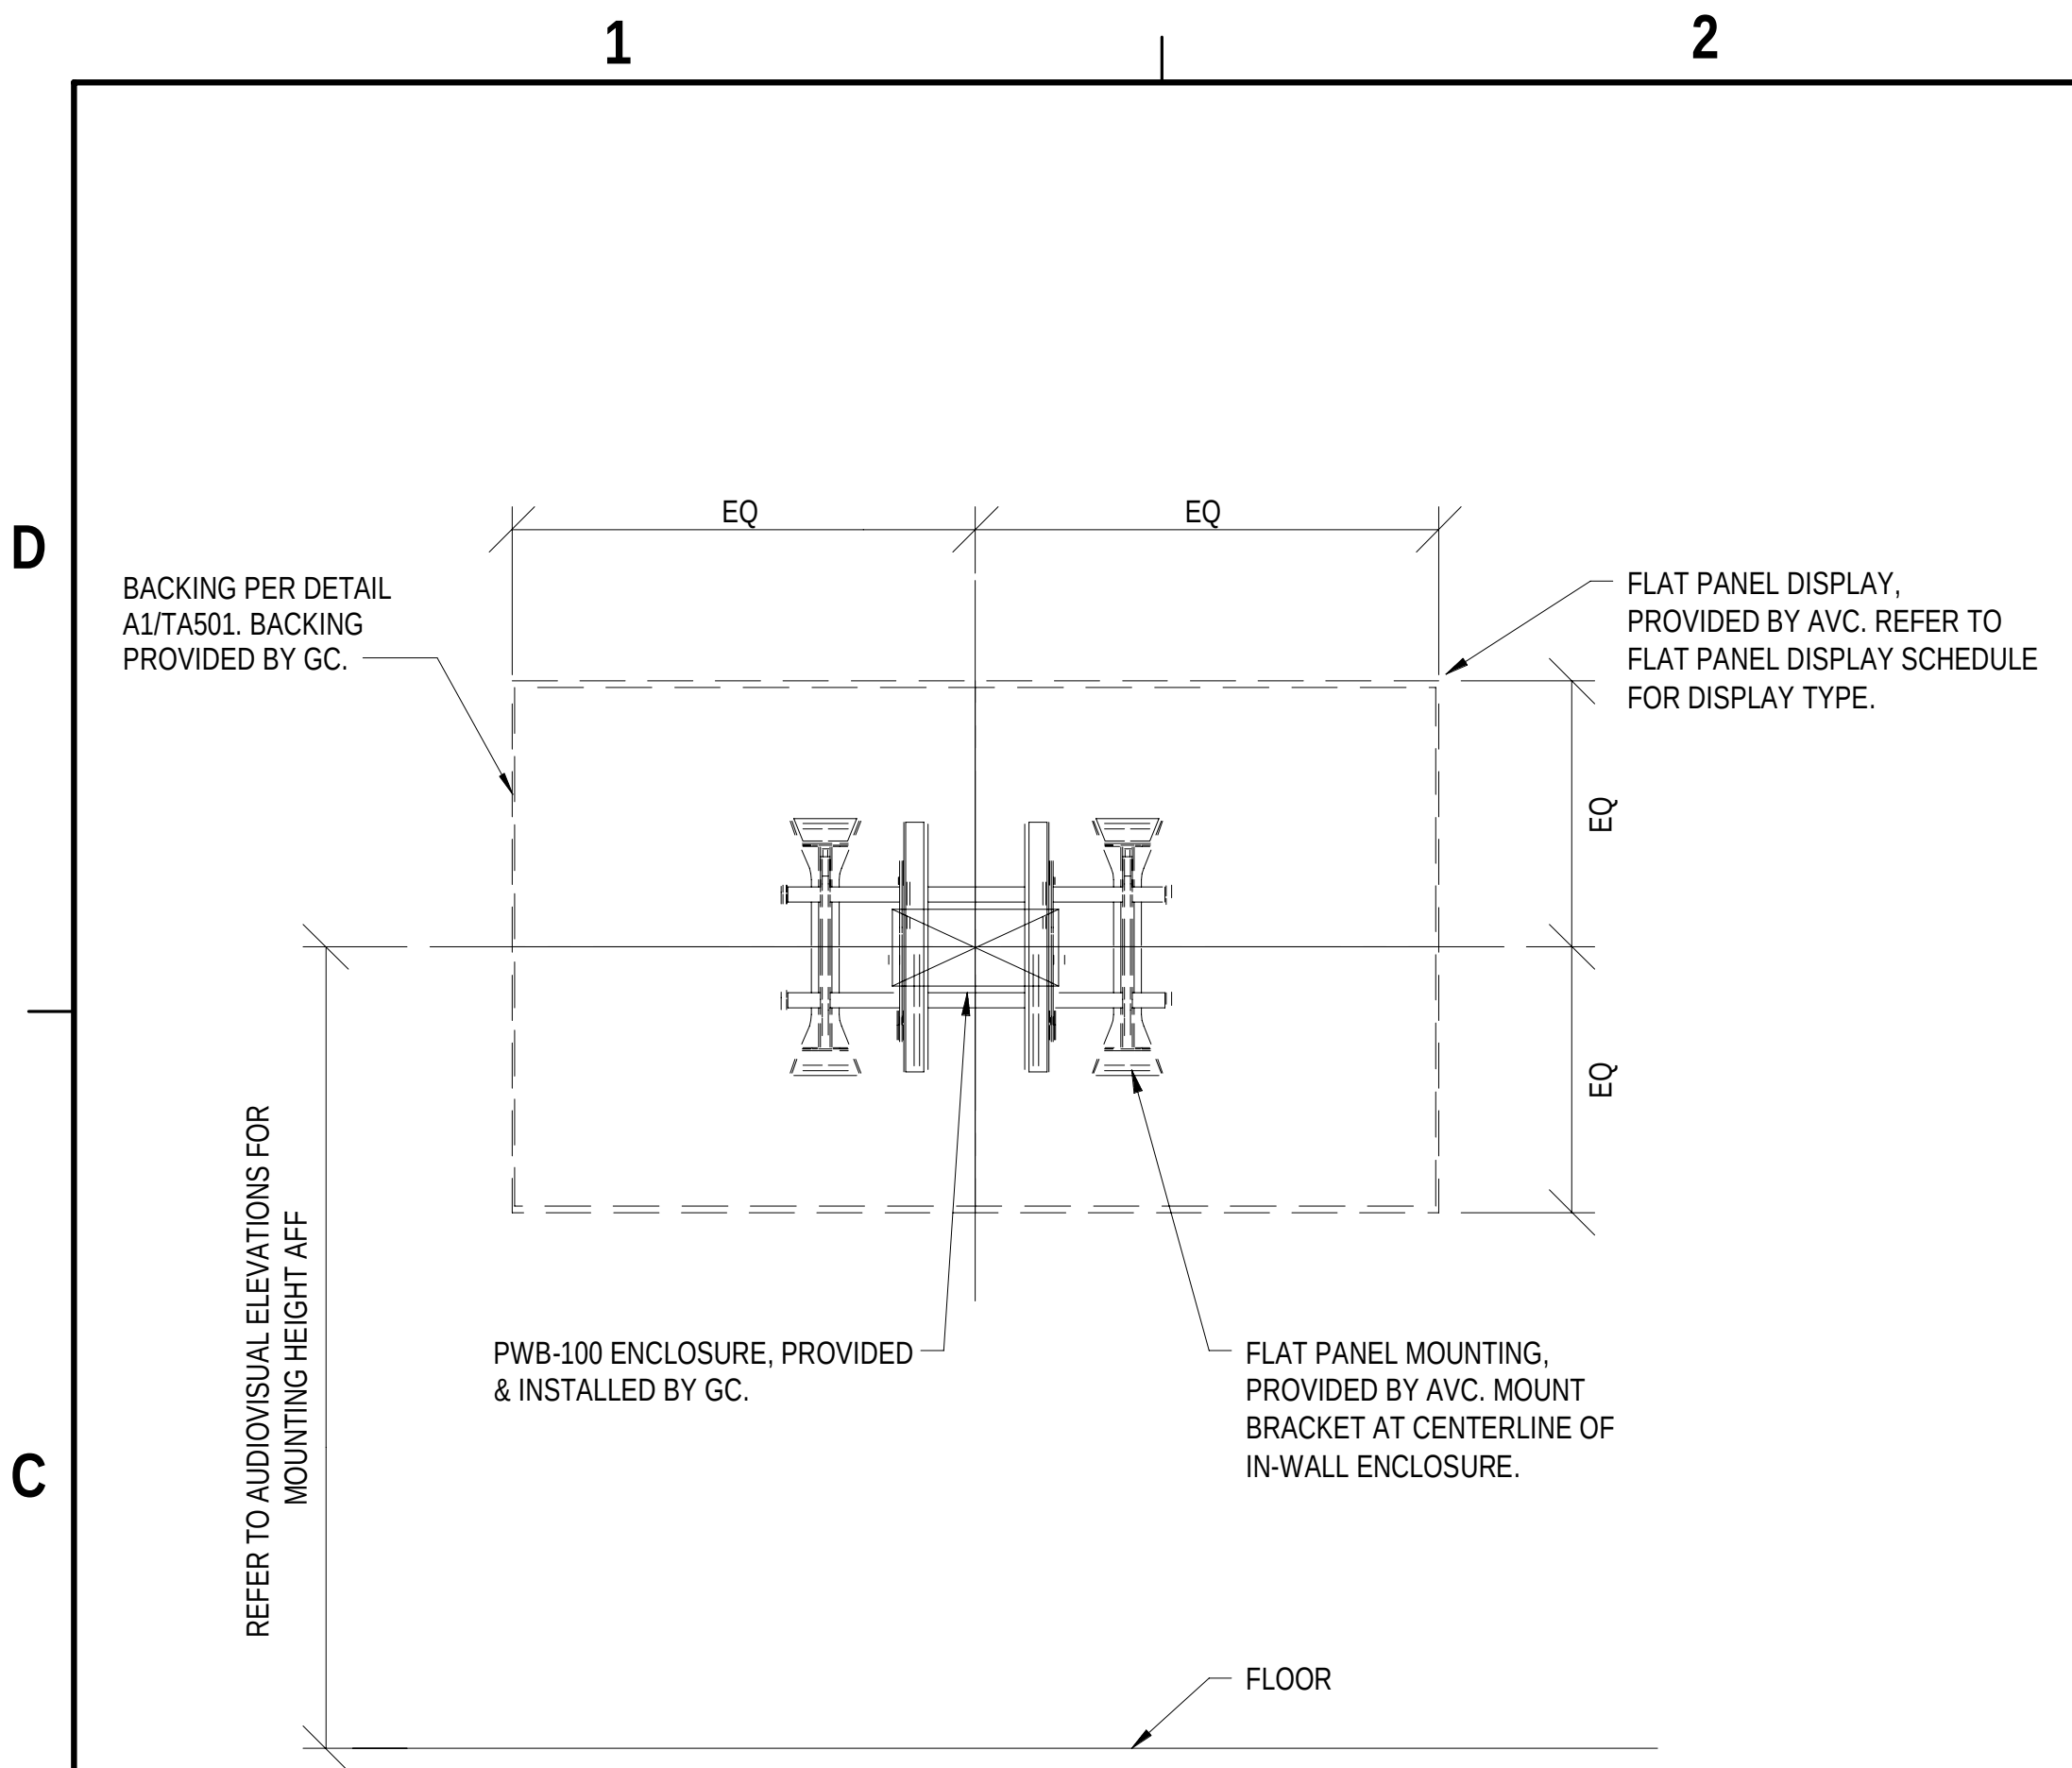


C1 FLAT PANEL DISPLAY BRACKET DETAIL
NTS

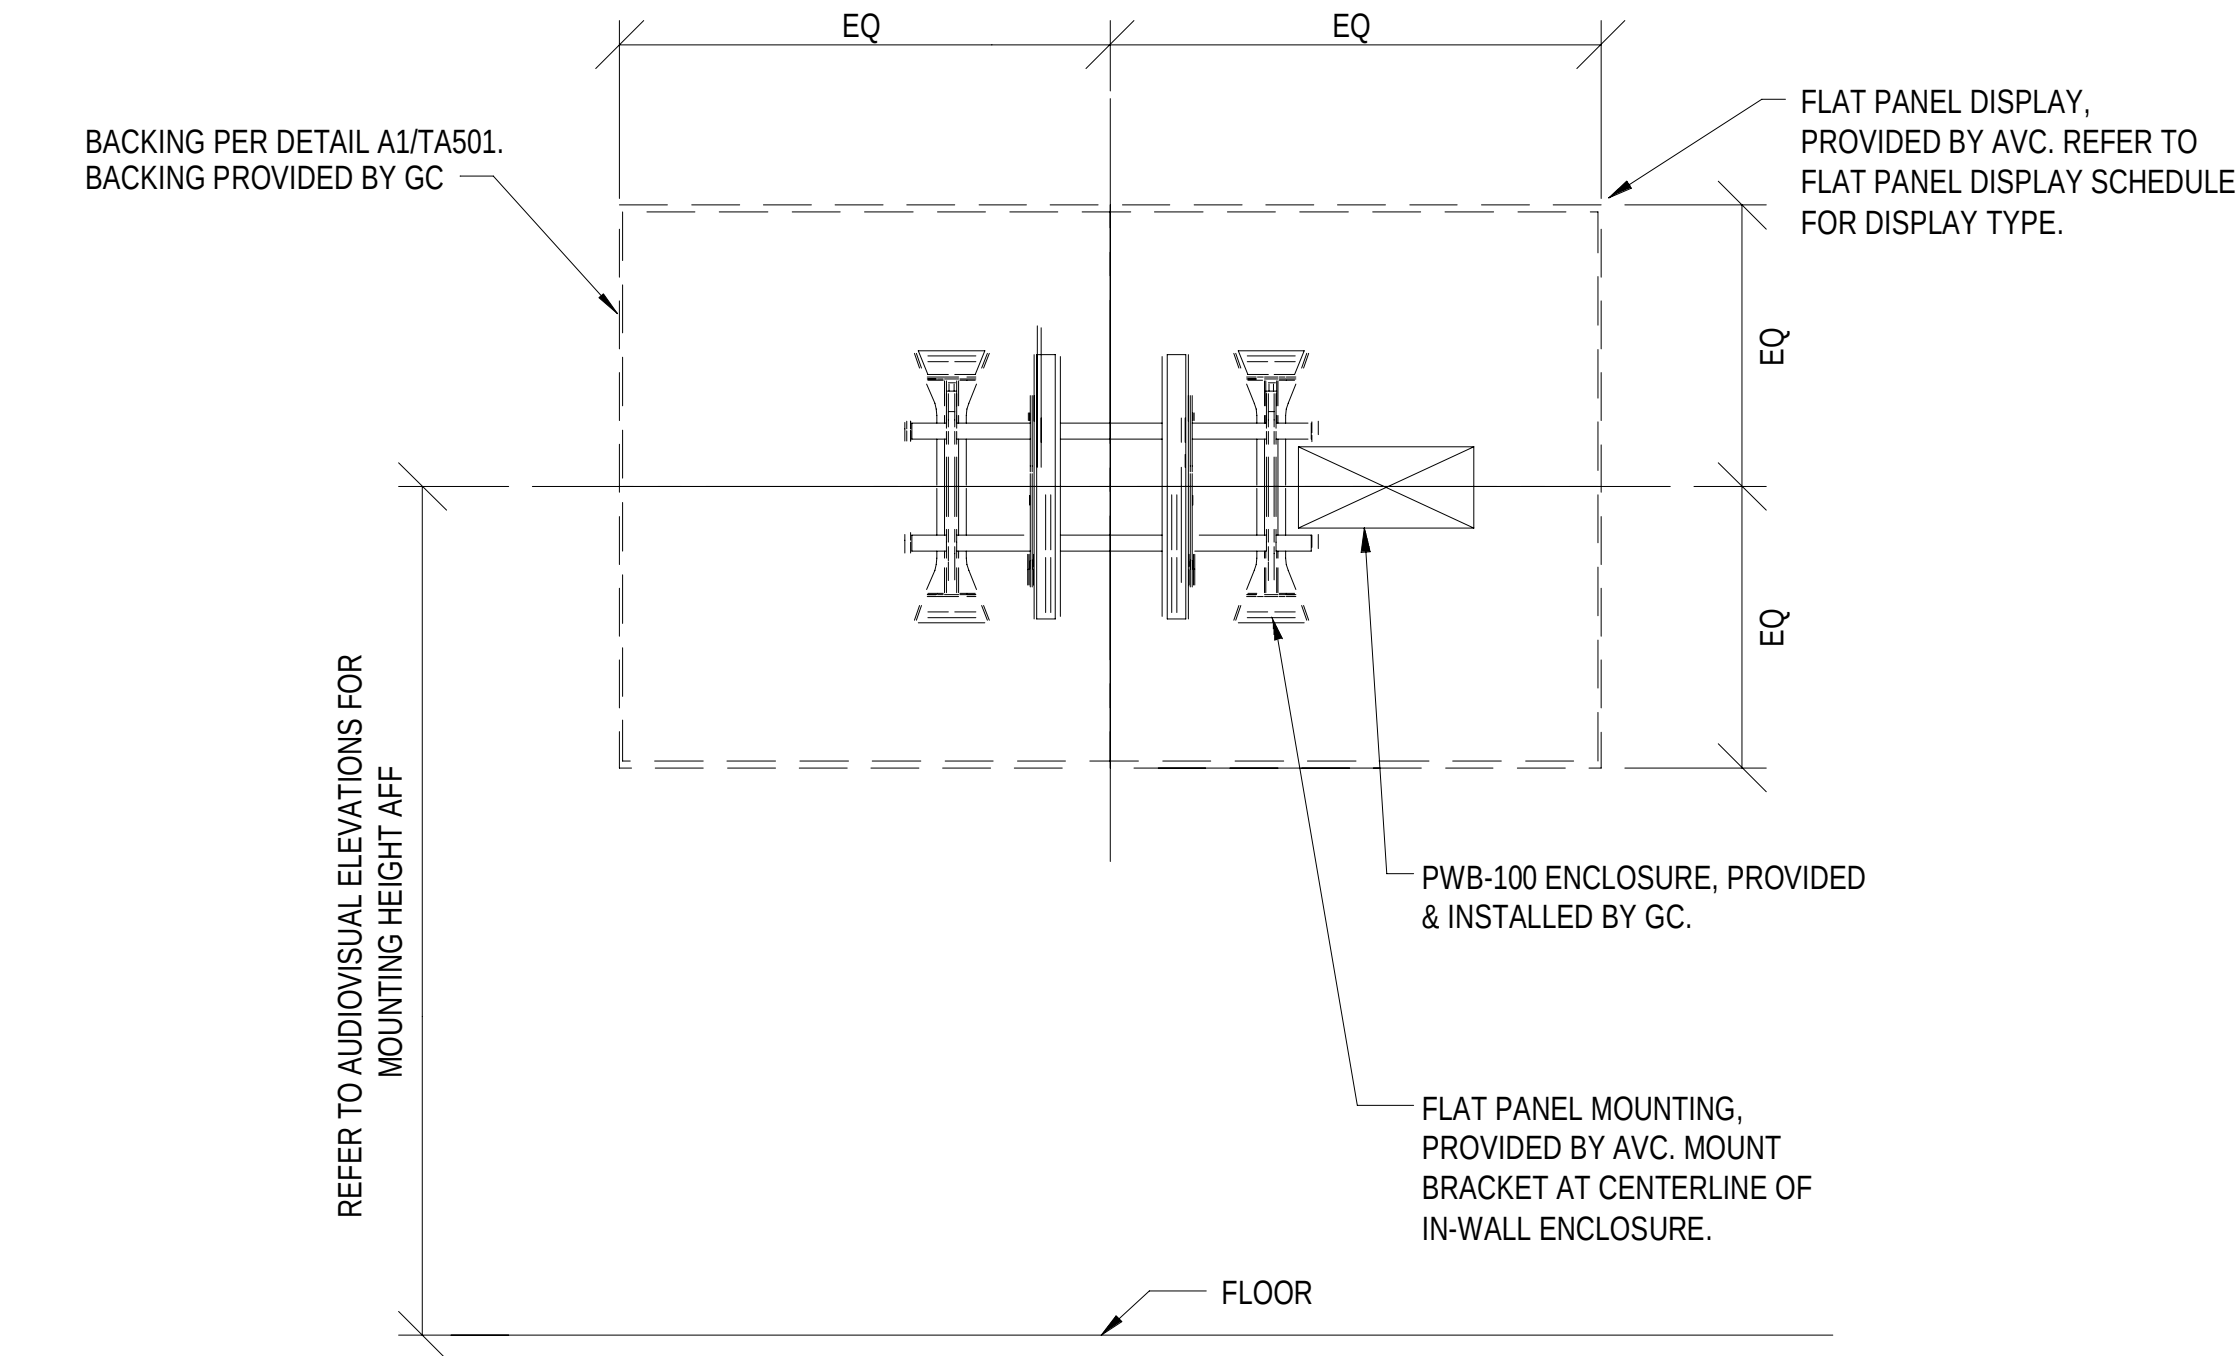

C3 FLAT PANEL DISPLAY BRACKET DETAIL ROOM 126
NTS

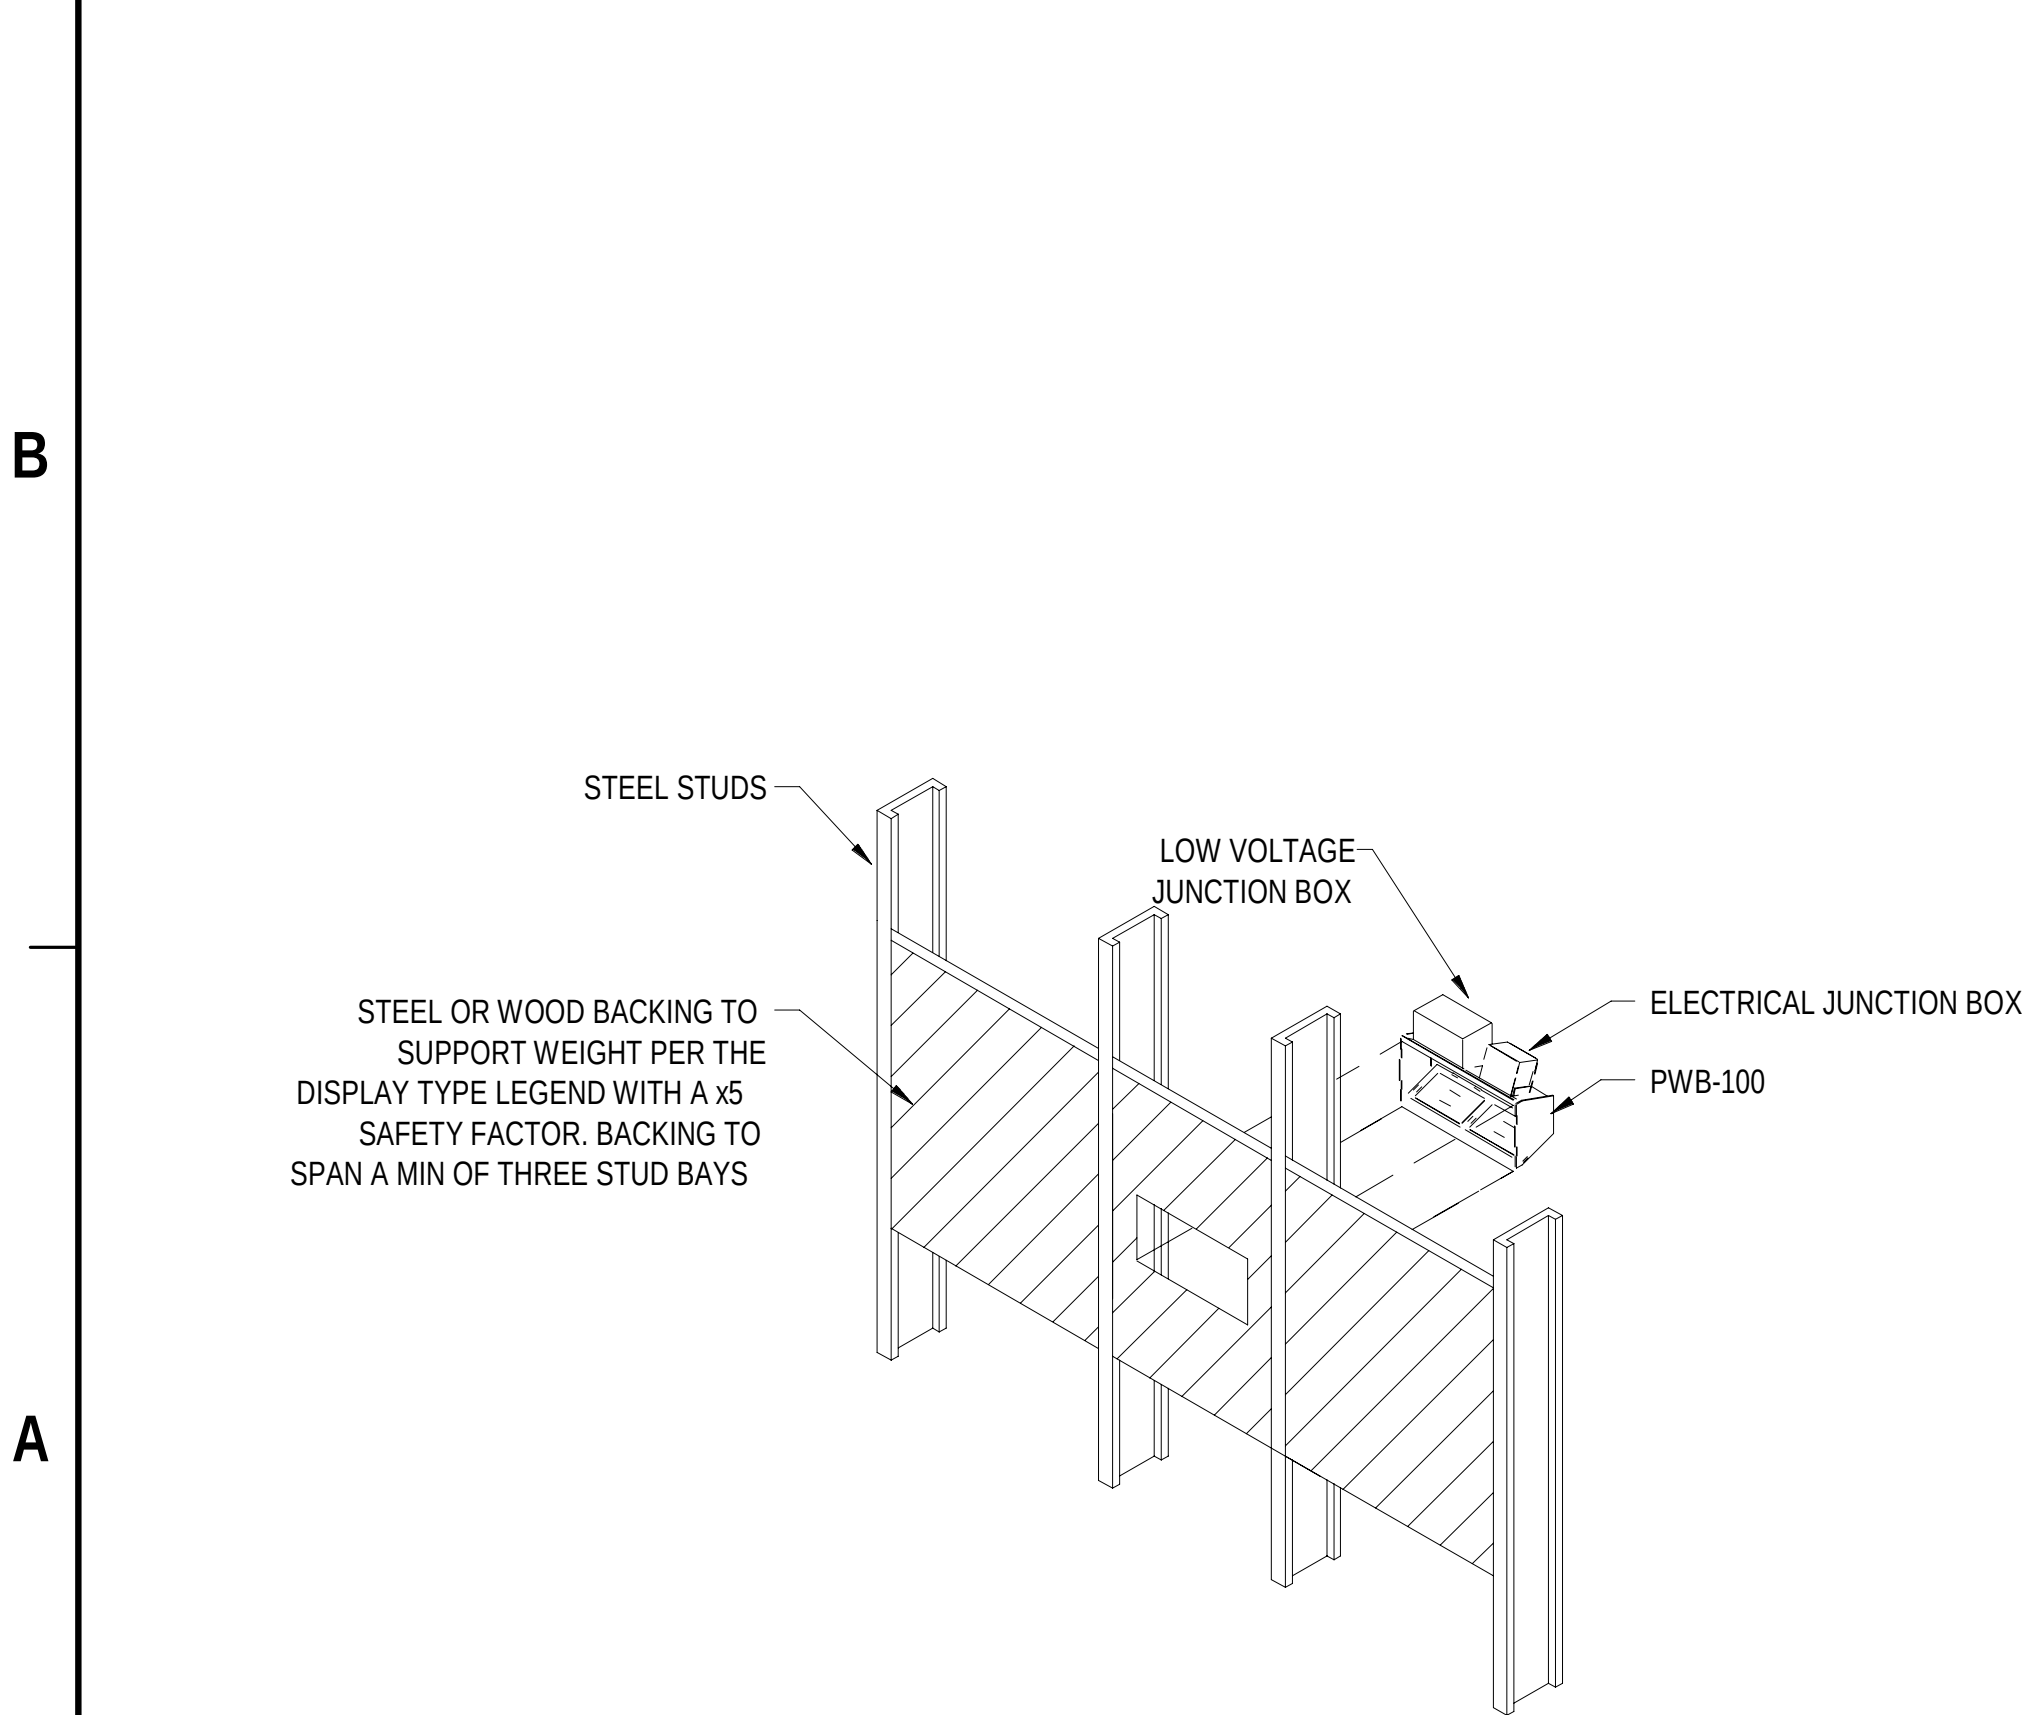

A1 BLOCKING DETAIL
NTS

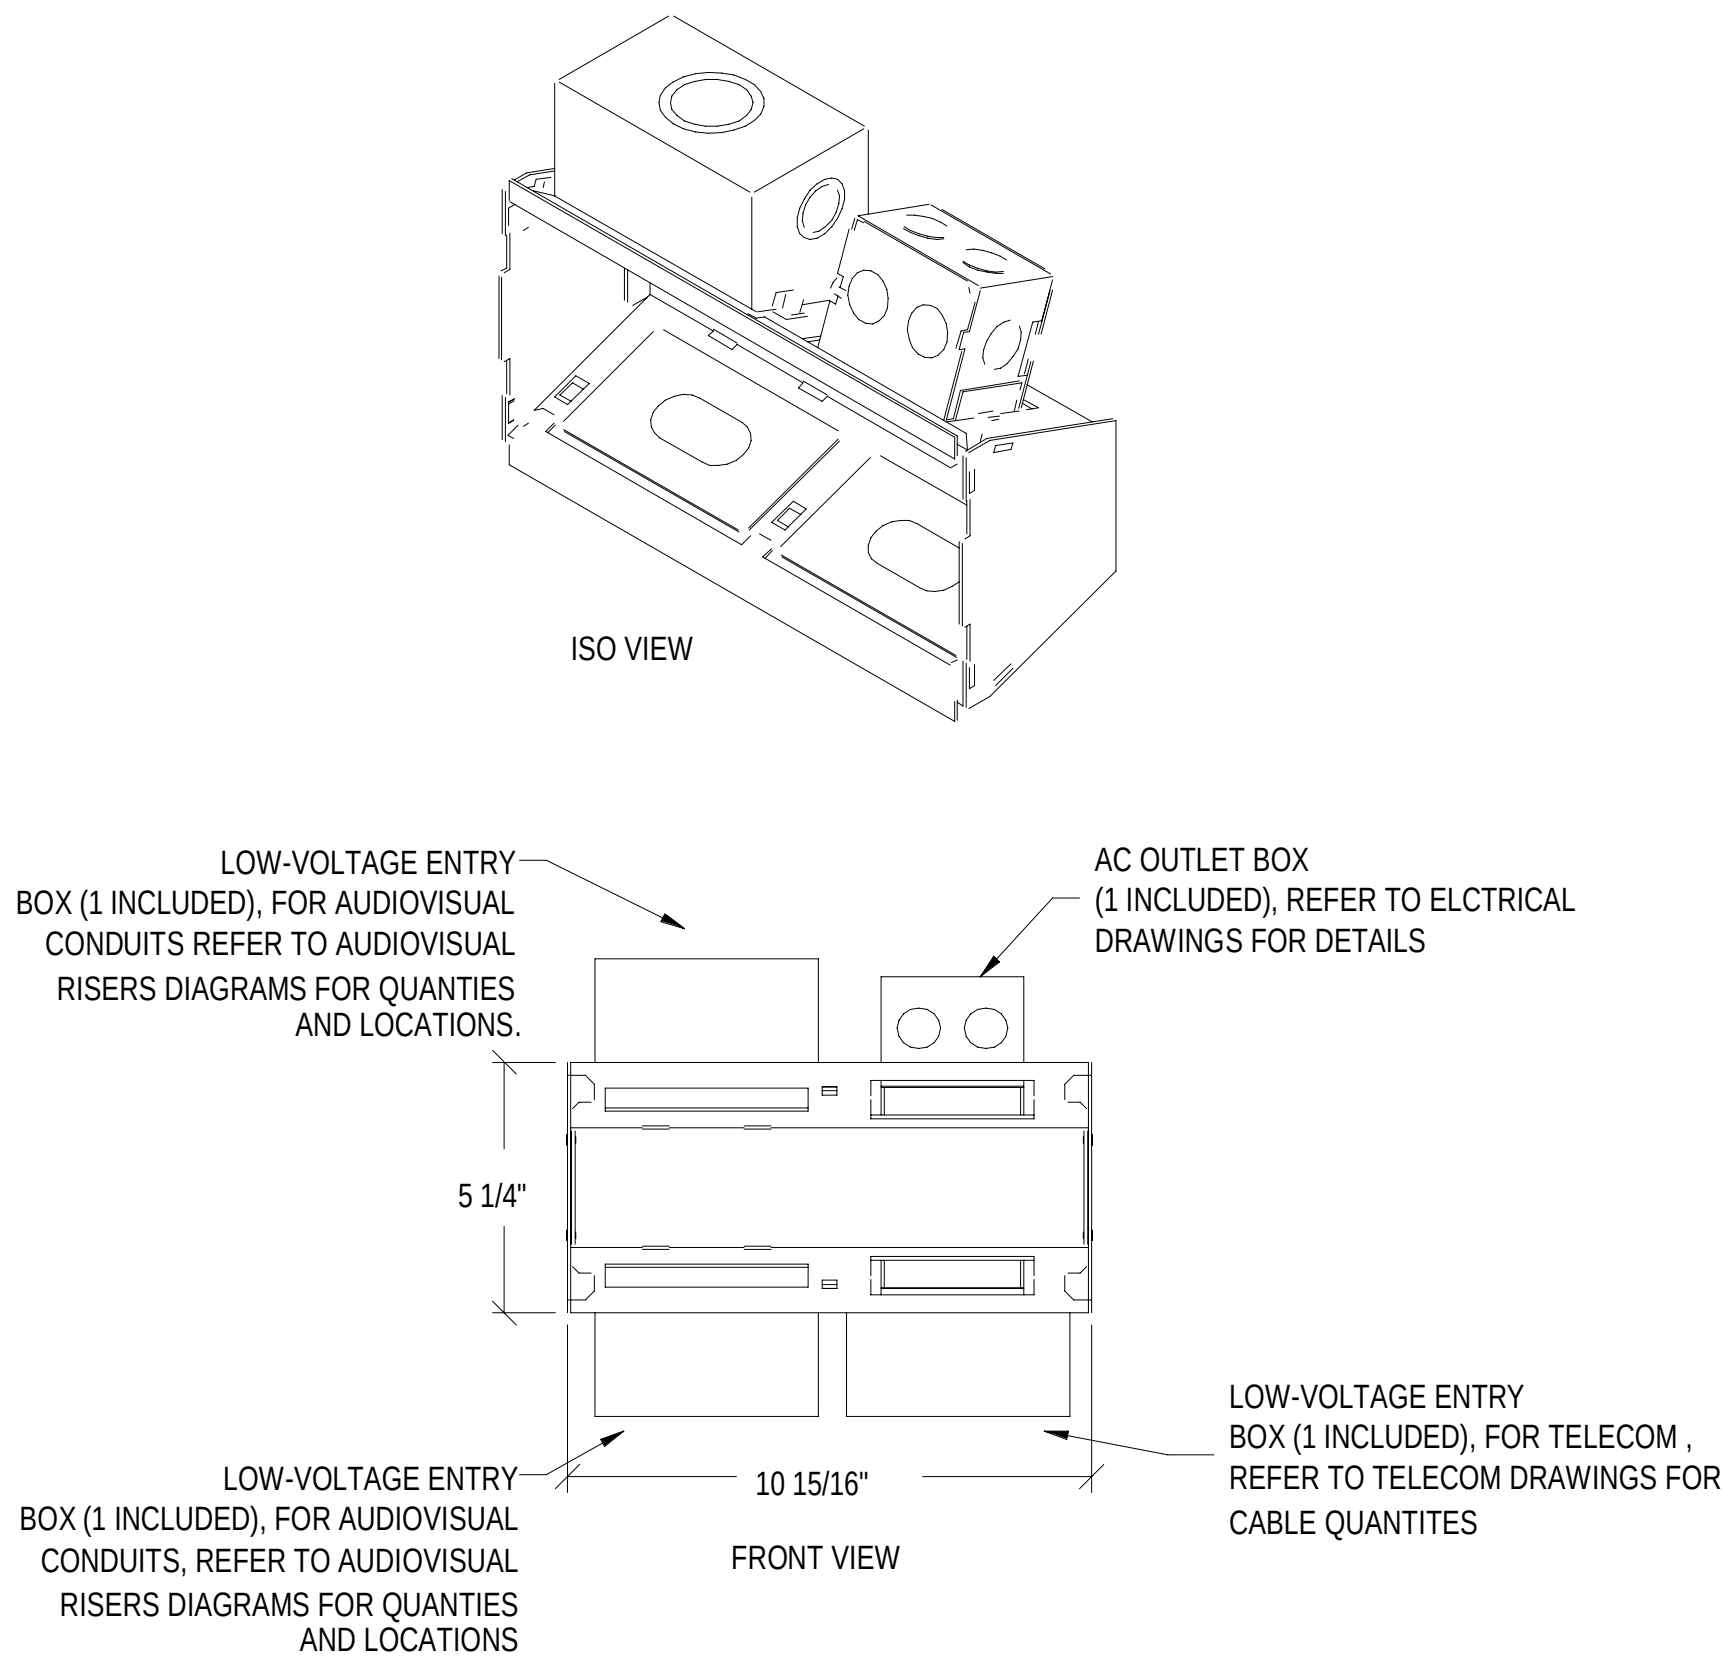

A3 PWB-100 DETAIL
NTS

GENERAL SHEET NOTES

A. REFER TO A_TA001 FOR SYMBOLS, ABBREVIATIONS AND GENERAL NOTES.

SHEET KEYNOTES

- BACKING MUST BE A MINIMUM OF 24" H X 48" W.
- SEE PARTITION TYPES FOR STUD SIZE AND MATERIAL.
- VERIFY LOCATIONS OF BACKING WITH PLANS AND ROOM ELEVATIONS.
- FLAT PANEL DISPLAYS AND MOUNTING BRACKETS BY THE AVC.



Jacobs
1100 NORTH GLEBE ROAD
SUITE 500
ARLINGTON, VIRGINIA 22201
571.218.1000
FAX: 571.218.1600

APPROVED

FOR COMMANDER NAVFAC

ACTIVITY
APPROVED BY LCDR ELIZABETH
CLOKODE NAVFAC NLON FEAD
DIRECTOR NEW LONDON, GROTON, CT

SATISFACTORY TO DATE 05/27/2025

DES SJY DRW TLO CHK JFH

PMOM SDS / RSF

BRANCH MANAGER WRB

CHIEF ENGINEER JWJ

FIRE PROTECTION HPN

DEPARTMENT OF THE NAVY

NAVAL FACILITIES ENGINEERING SYSTEMS COMMAND

NAVAL FACILITIES ENGINEERING SYSTEMS COMMAND - MID-ATLANTIC

MID-ATLANTIC

NAVAL SUBMARINE BASE NEW LONDON

P-1102 WEAPONS MAGAZINE & ORDNANCE OPERATIONS FACILITY

GROTON, CONNECTICUT

NAVAL STATION - NORFOLK, VA

NAVAL STATION - NORFOLK, VA

TA601


A

B


C

D

B1 AUDIO VISUAL FLOW DIAGRAM - TRAINING ROOM 131
NTS

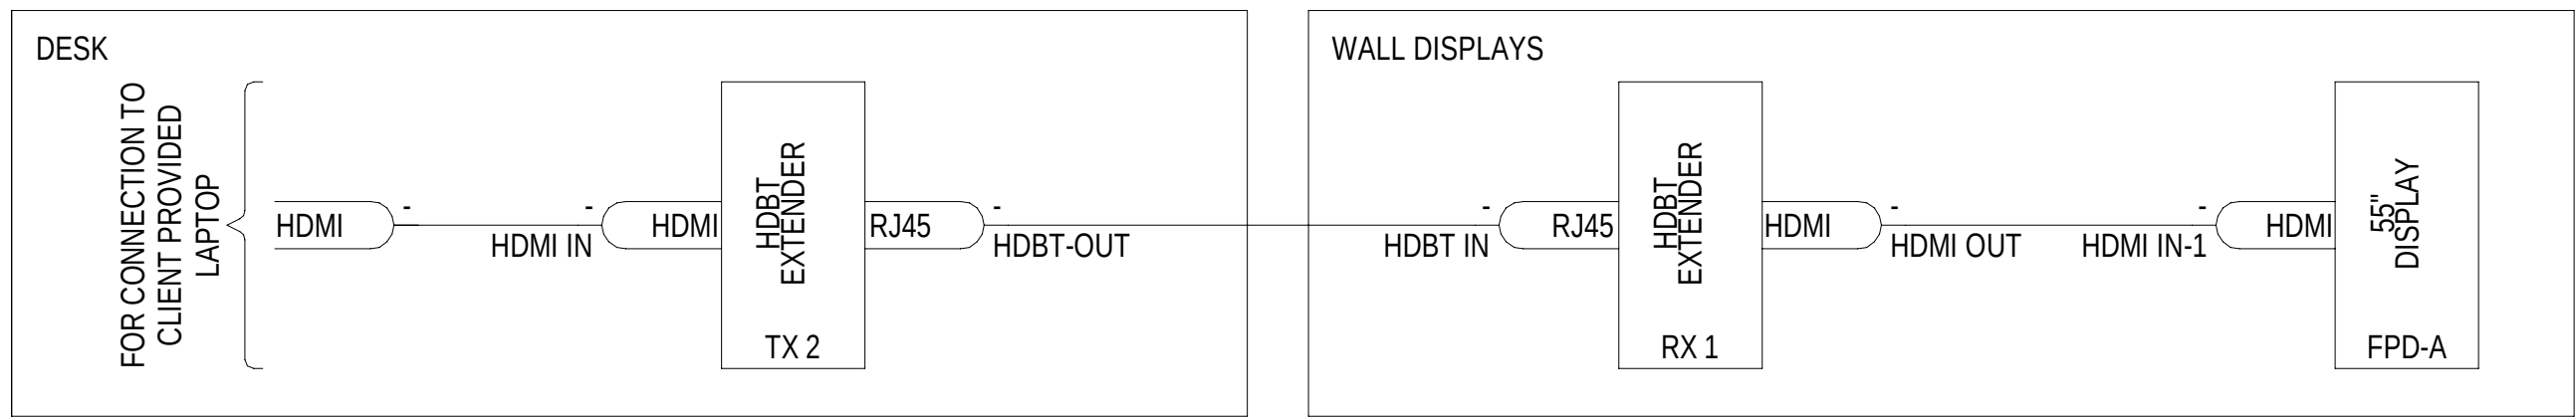

A1 AUDIO VISUAL FLOW DIAGRAM - OFFICE (TYPICAL)
NTS

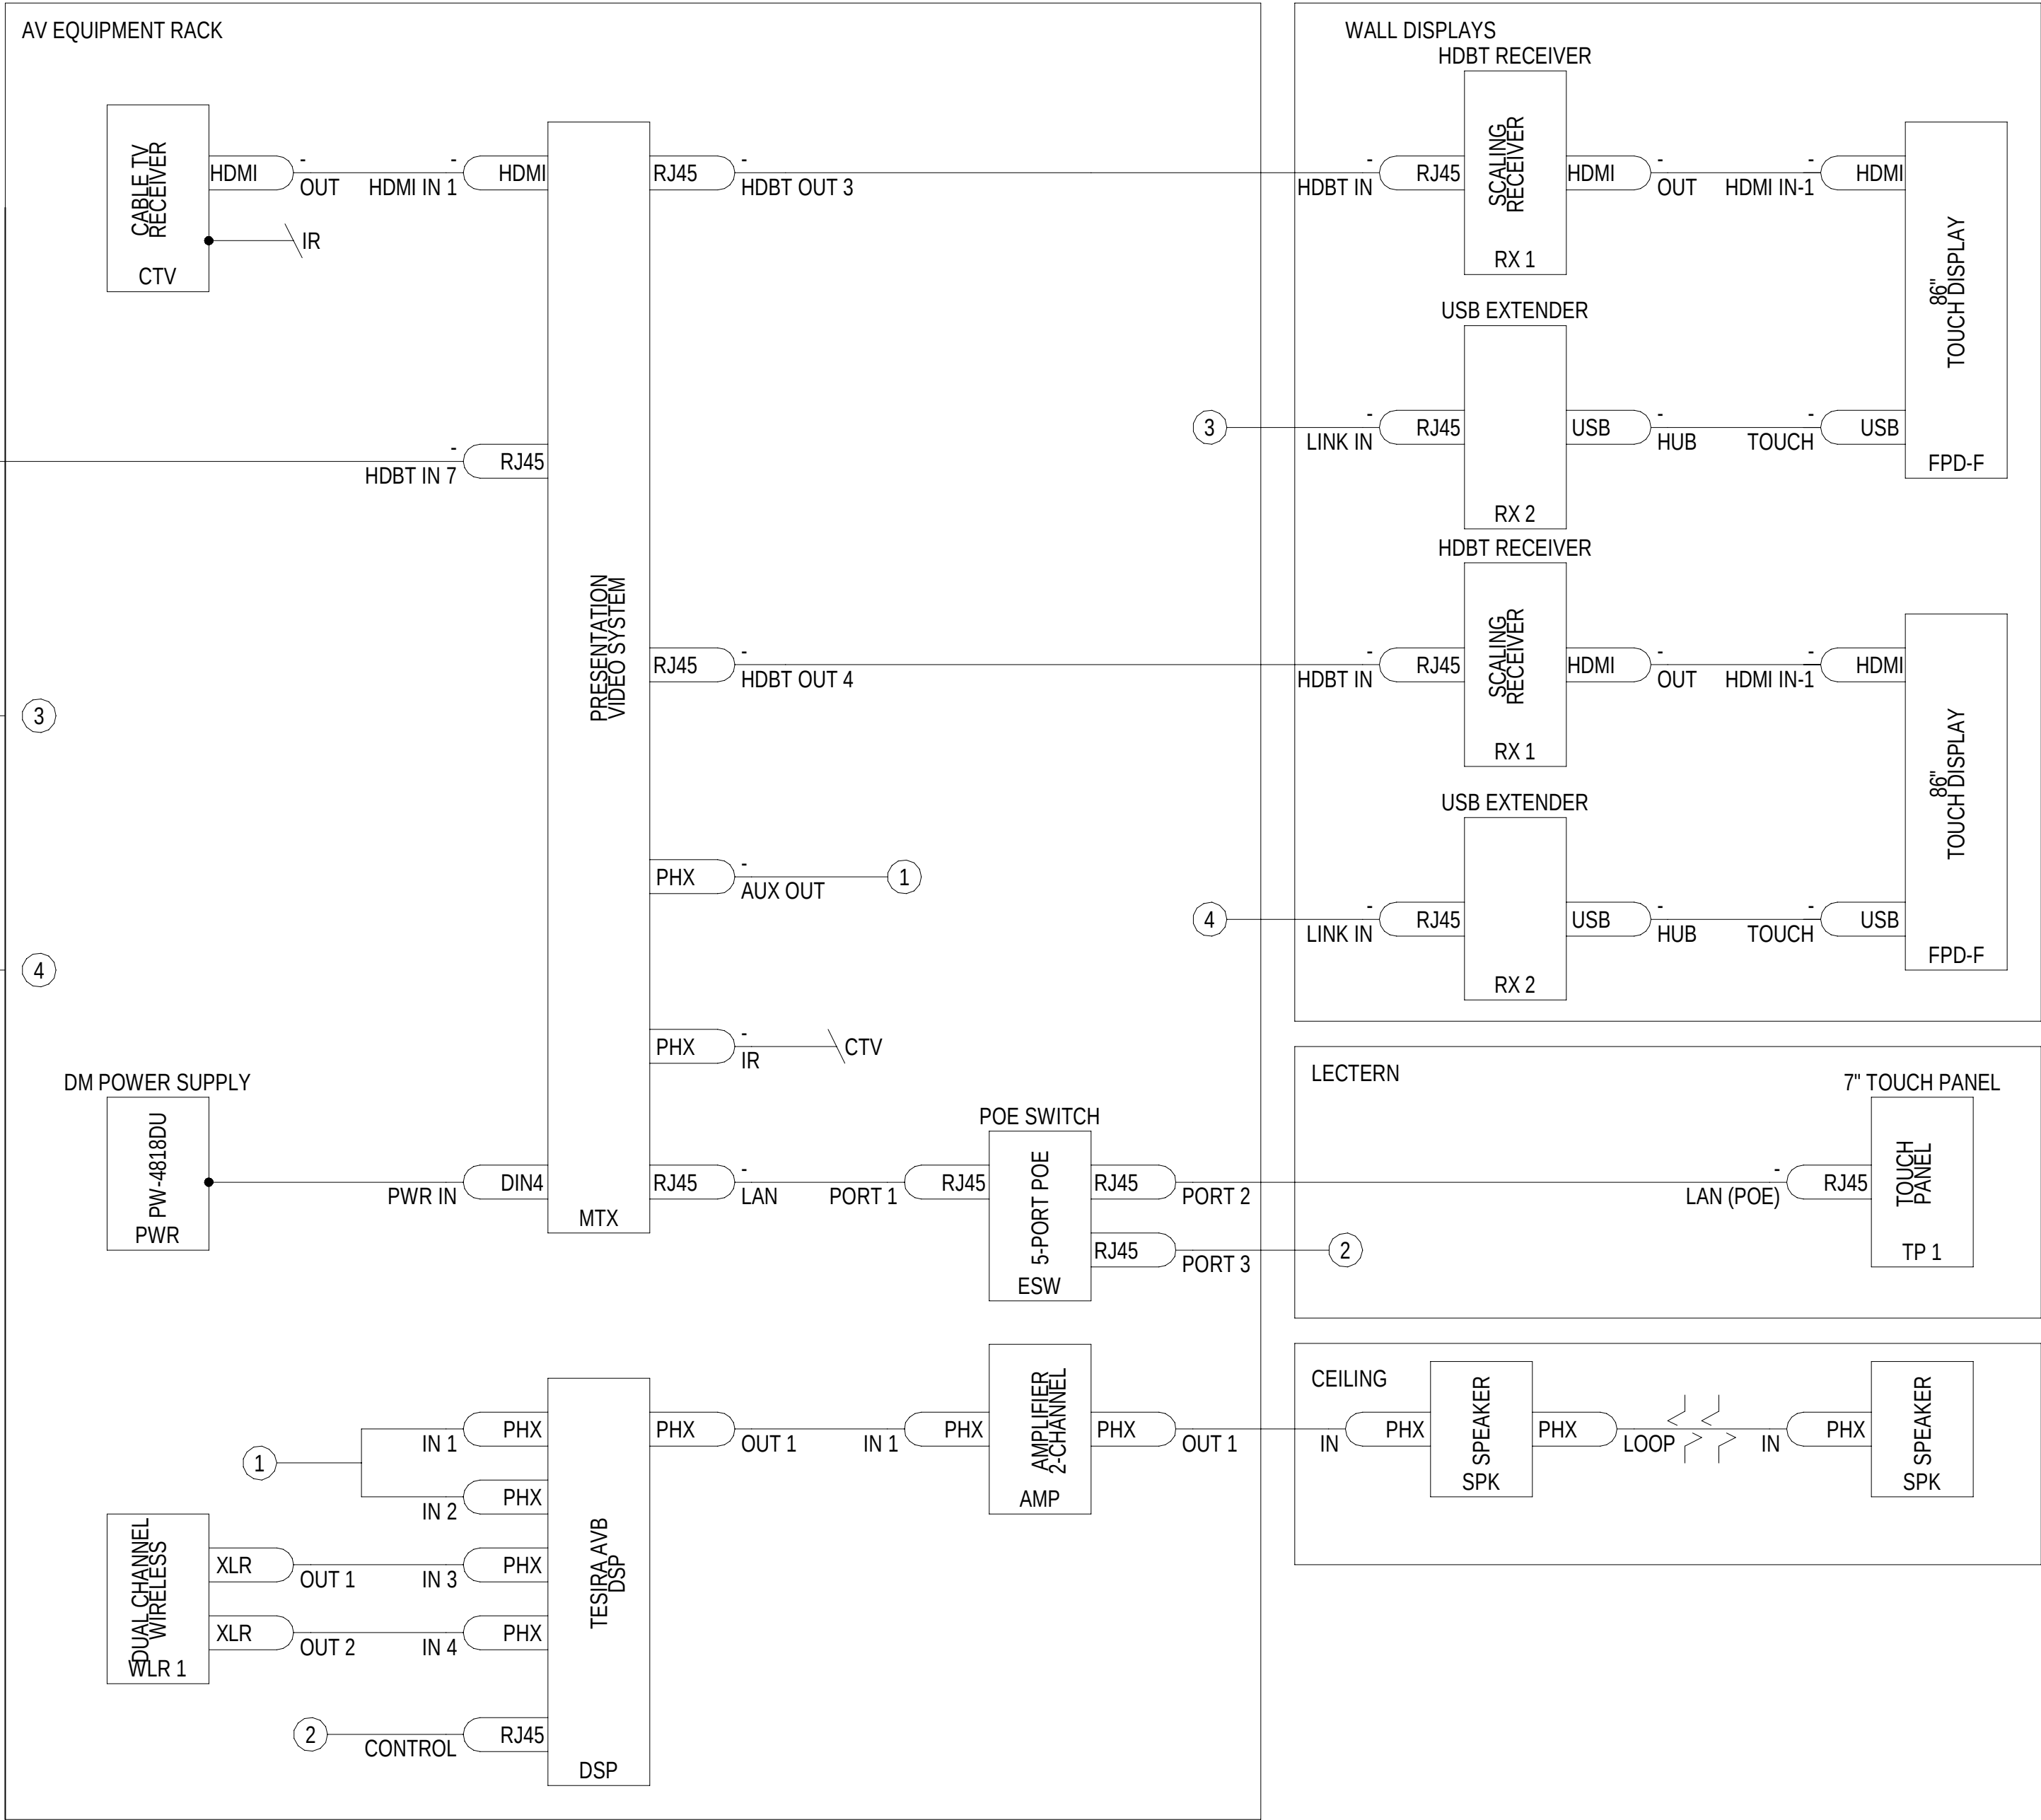

GENERAL SHEET NOTES

SHEET KEYNOTES

SYM	DESCRIPTION	DATE	APPR



Jacobs
1100 NORTH GLEBE ROAD
SUITE 500
ARLINGTON, VIRGINIA 22201
571.218.1000
FAX: 571.218.1600

APPROVED	AE INFO
FOR COMMANDER NAVFAC	
ACTIVITY	APPROVED BY LCDR ELIZABETH CLOKODE NAVFAC NLON READ DIRECTOR NEW LONDON, GROTON, CT
SATISFACTORY TO DATE	05/27/2025
DES	SJY
DRW	TLO
CHK	JFH
PMID	SDS / RSF
BRANCH MANAGER	WRB
CHIEF ENGINEER	JWJ
FIRE PROTECTION	HPN

DEPARTMENT OF THE NAVY	NAVAL FACILITIES ENGINEERING SYSTEMS COMMAND	MID-ATLANTIC	NAVAL STATION - NORFOLK, VA
NAVAL FACILITIES ENGINEERING SYSTEMS COMMAND	MID-ATLANTIC	NAVAL SUBMARINE BASE NEW LONDON	GROTON, CONNECTICUT
P-1102 WEAPONS MAGAZINE & ORDNANCE OPERATIONS FACILITY	OPERATIONS	AUDIO VISUAL DIAGRAMS	

SCALE: AS NOTED
EPROJECT NO.: 1667770
CONSTR. CONTR. NO.
NAVFAC DRAWING NO. 12894082
SHEET 132 OF 140
TA601

6/20/2025 11:51:19 PM
\\ac1vps01\app\p\FDZ\ELG28\TELEBLOG-166770-1-BN1_V21.rvt

TY101

A


D

C

B

B1 OVERALL FIRST FLOOR SECURITY PLAN

1/8" = 1'-0"

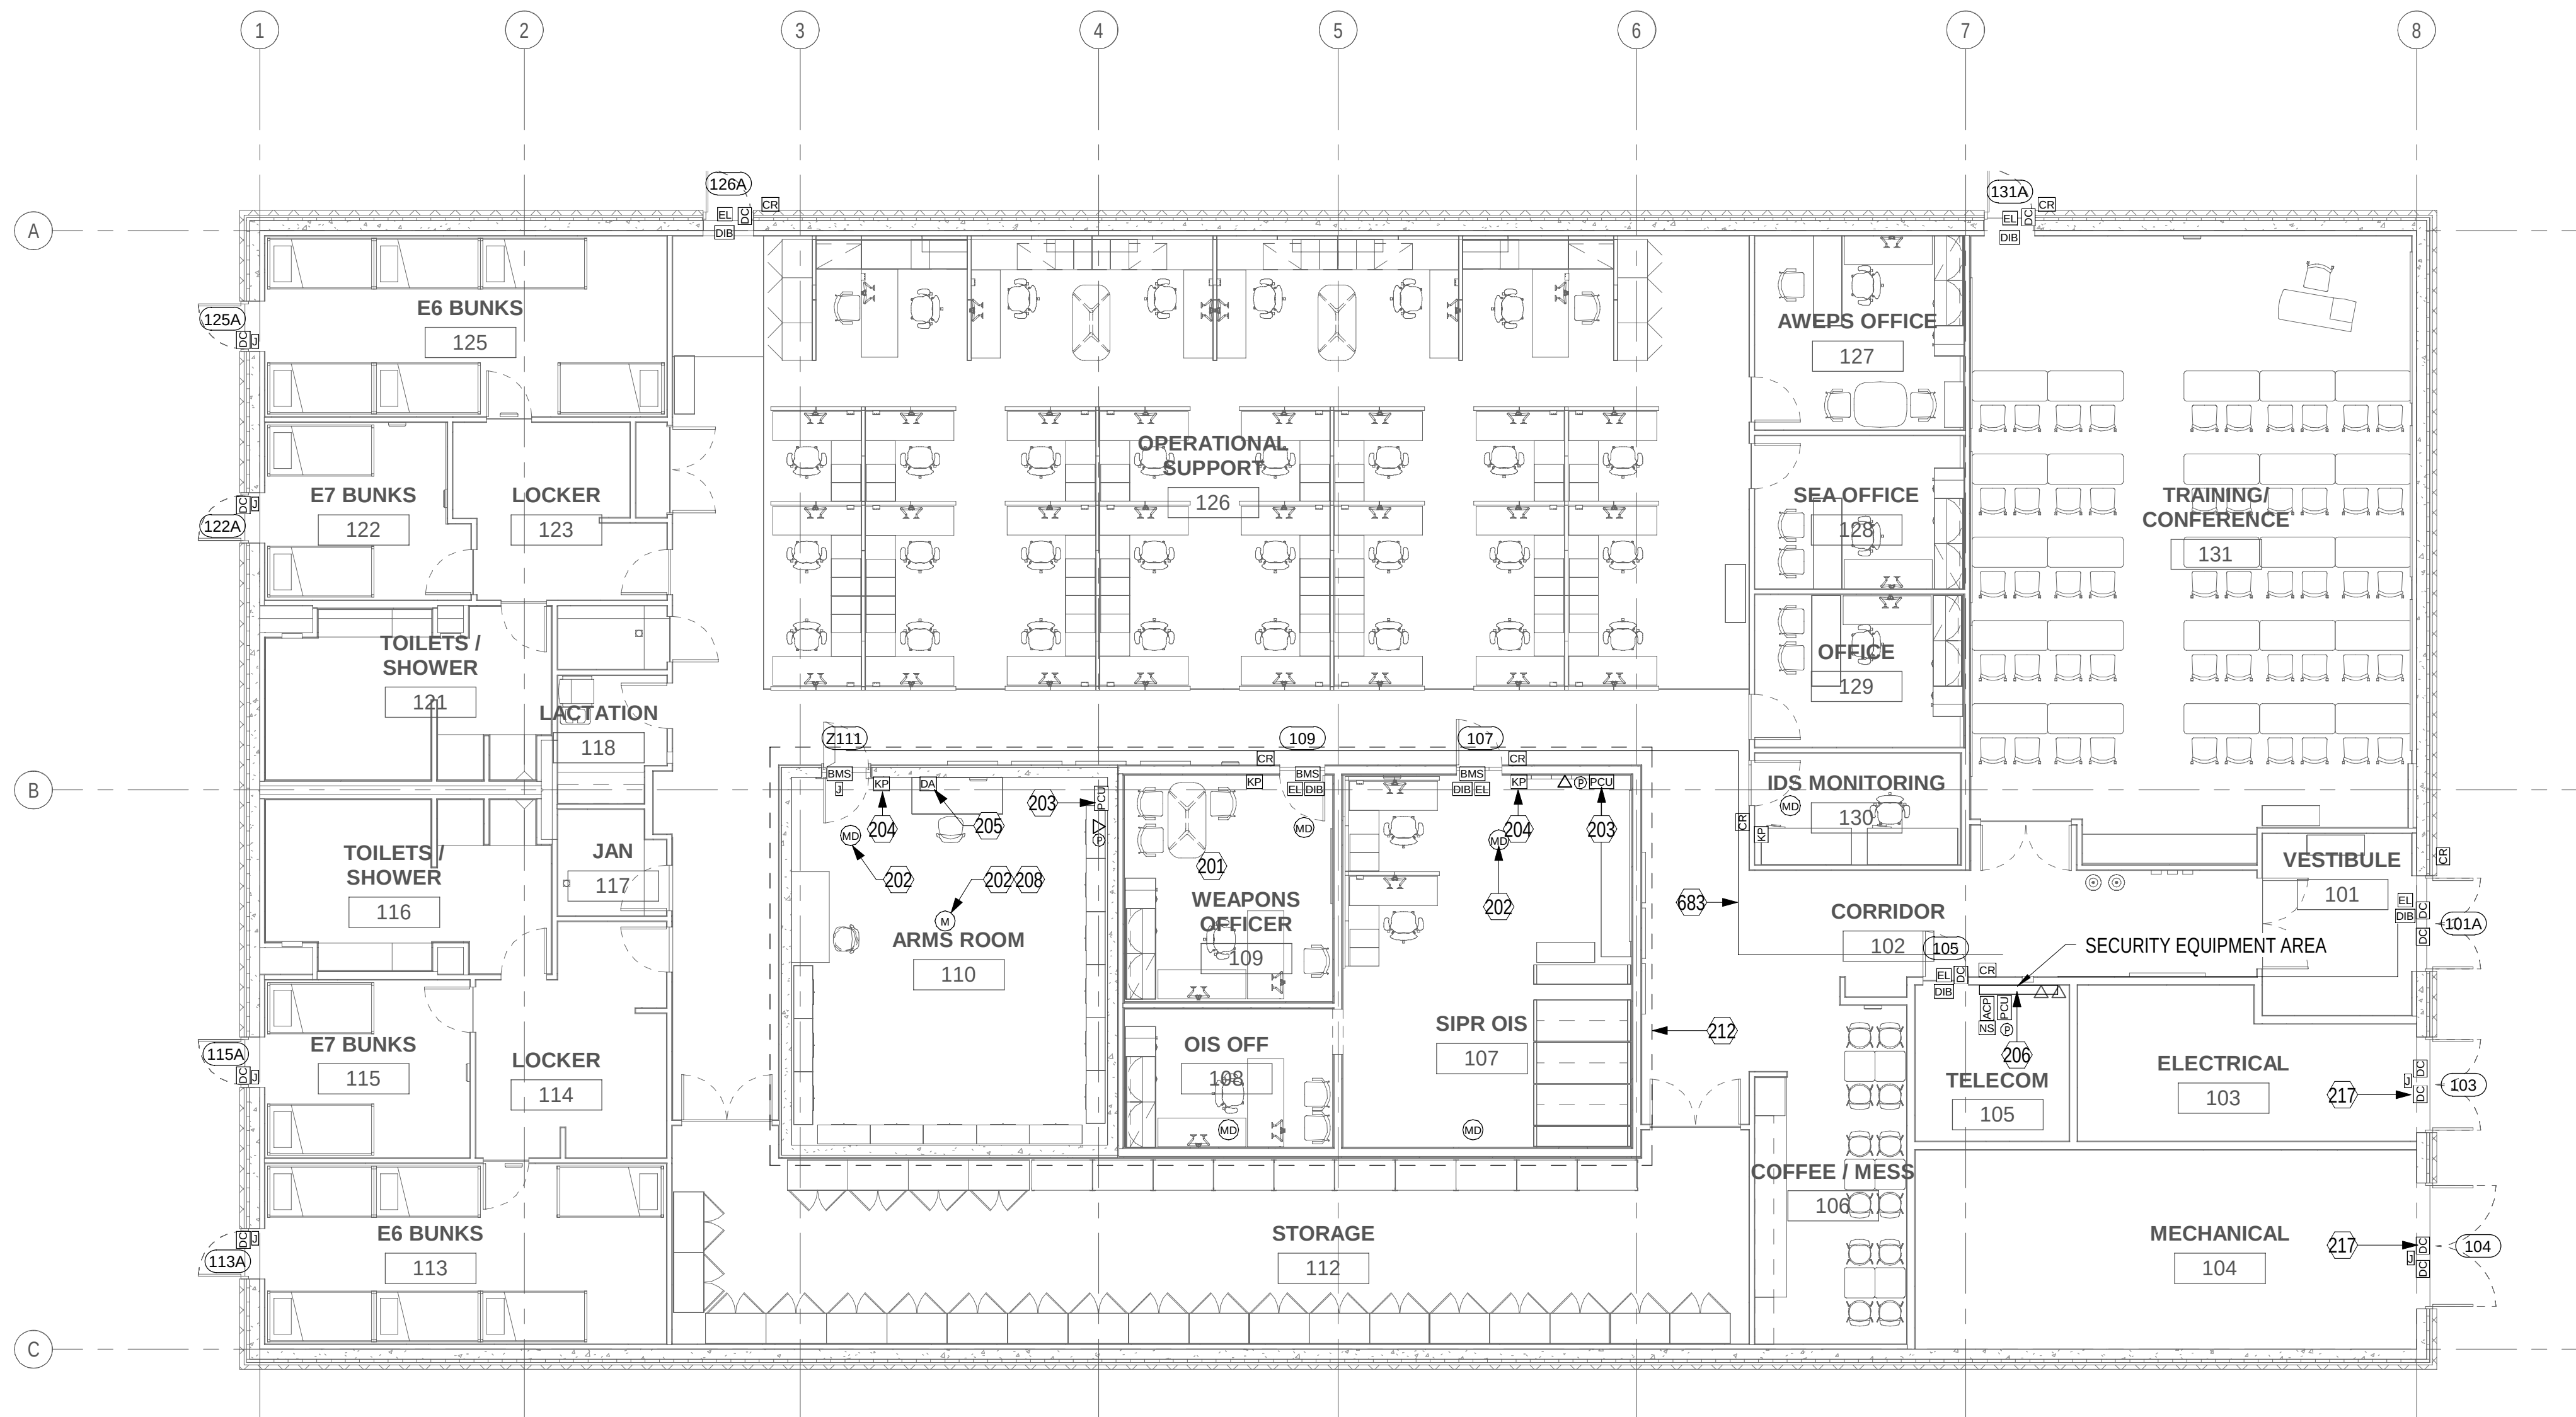


GENERAL SHEET NOTES


1. REFER TO SHEET TY001 FOR SECURITY SYMBOLS AND ABBREVIATIONS.
2. PROVIDE SEPARATE AND INDEPENDENT PATHWAYS FOR SECURITY CABLING.

SHEET KEYNOTES

- 201 SECURITY MONITORING PLACED IN THE WEAPONS DUTY OFFICE.
- 202 PROVIDE ROUGH-IN FOR CEILING MOUNTED MOTION DETECTOR.
- 203 SPACE ALLOCATED FOR PCU (CONTROL POINT FOR DEDICATED ROOM ACCESS CONTROL AND INTRUSION DETECTION PANELS) PROVIDE JUNCTION BOX ON WALL FOR HARD WIRED 110VAC POWER MOUNTED AT 84" AFF.
- 204 PROVIDE SINGLE GANG BACKBOX AND 1" CONDUIT TO DEDICATED IN ROOM PCU LOCATION FOR KEY PAD.
- 205 PROVIDE SINGLE GANG BACKBOX AND ONE INCH CONDUIT TO IN ROOM DEDICATED PCU PANEL FOR DURESS ALARM.
- 206 DEDICATED WALL SPACE ALLOCATED FOR ACCESS CONTROL PANELS. PROVIDE 110VAC POWER FOR HARDWIRED CIRCUIT MOUNTED AT 72" AFF. REF C3/T-402
- 208 LOCATE ABOVE CEILING.
- 212 DASHED LINE INDICATES BOUNDARY OF SECURE PERIMETER.
- 217 MONITORED DOORS ARE PLACED ON SCHEDULE FOR ALERTS TO ACCESS CONTROL SYSTEM.
- 683 PROPOSED PATHWAY ROUTING SHOWN FOR REFERENCE. ACTUAL MEANS AND METHODS BY CONTRACTOR - COORDINATE WITH FIELD CONDITIONS.

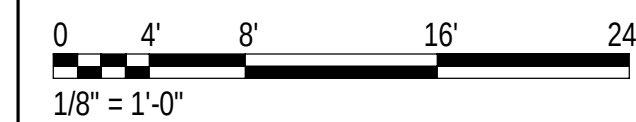

SYN	DESCRIPTION	DATE	APPR

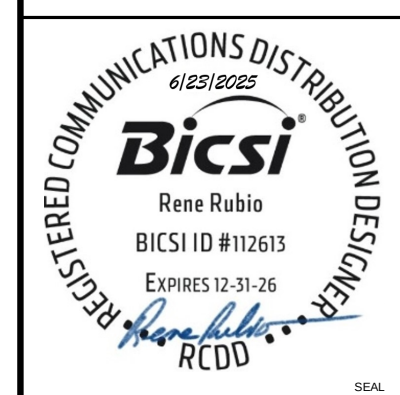

Jacobs
1100 NORTH GLEBE ROAD
SUITE 500
ARLINGTON, VIRGINIA 22201
571.218.1000
FAX: 571.218.1600

APPROVED	AE INFO
FOR COMMANDER NAVFAC	
ACTIVITY	APPROVED BY LCDR ELIZABETH CLOKODE NAVFAC NLON FEAD DIRECTOR NEW LONDON, GROTON, CT
SATISFACTORY TO DATE	05/27/2025
DES	MG
DRW	LA
CHK	RR
PMOM	SDS / RSF
BRANCH MANAGER	WRB
CHIEF ENGINEER	JWJ
FIRE PROTECTION	HPN

DEPARTMENT OF THE NAVY
NAVAL FACILITIES ENGINEERING SYSTEMS COMMAND - MID-ATLANTIC
NAVAL STATION - NORFOLK, VA
NAVAL SUBMARINE BASE NEW LONDON
P-1102 WEAPONS MAGAZINE & ORDNANCE OPERATIONS FACILITY
GROTON, CONNECTICUT
OPERATIONS
SECURITY FLOOR PLAN

SCALE: AS NOTED
EPROJECT NO.: 1667770
CONSTR. CONTR. NO.
NAVFAC DRAWING NO. 12894085
SHEET 135 OF 140
TY101

1

2


3

4


5

D

C

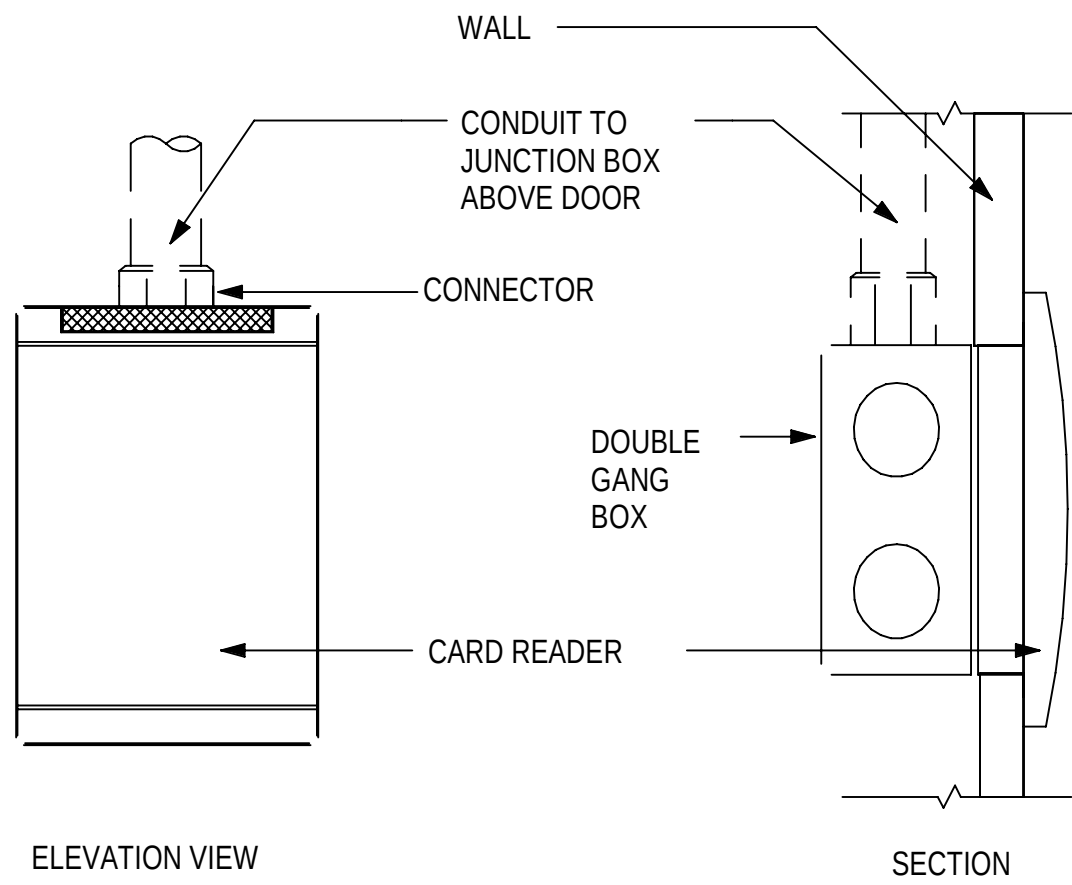


C1 CARD READER
NTS

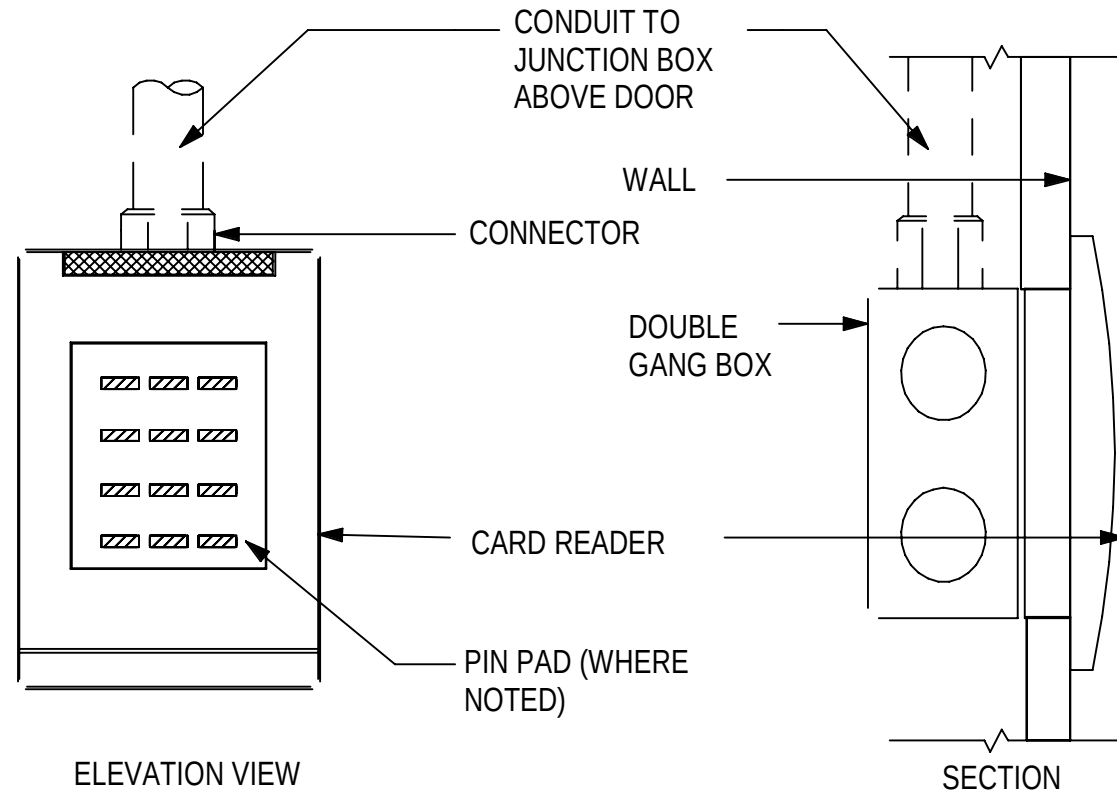


C3 CARD READER W/ PIN PAD
NTS

B

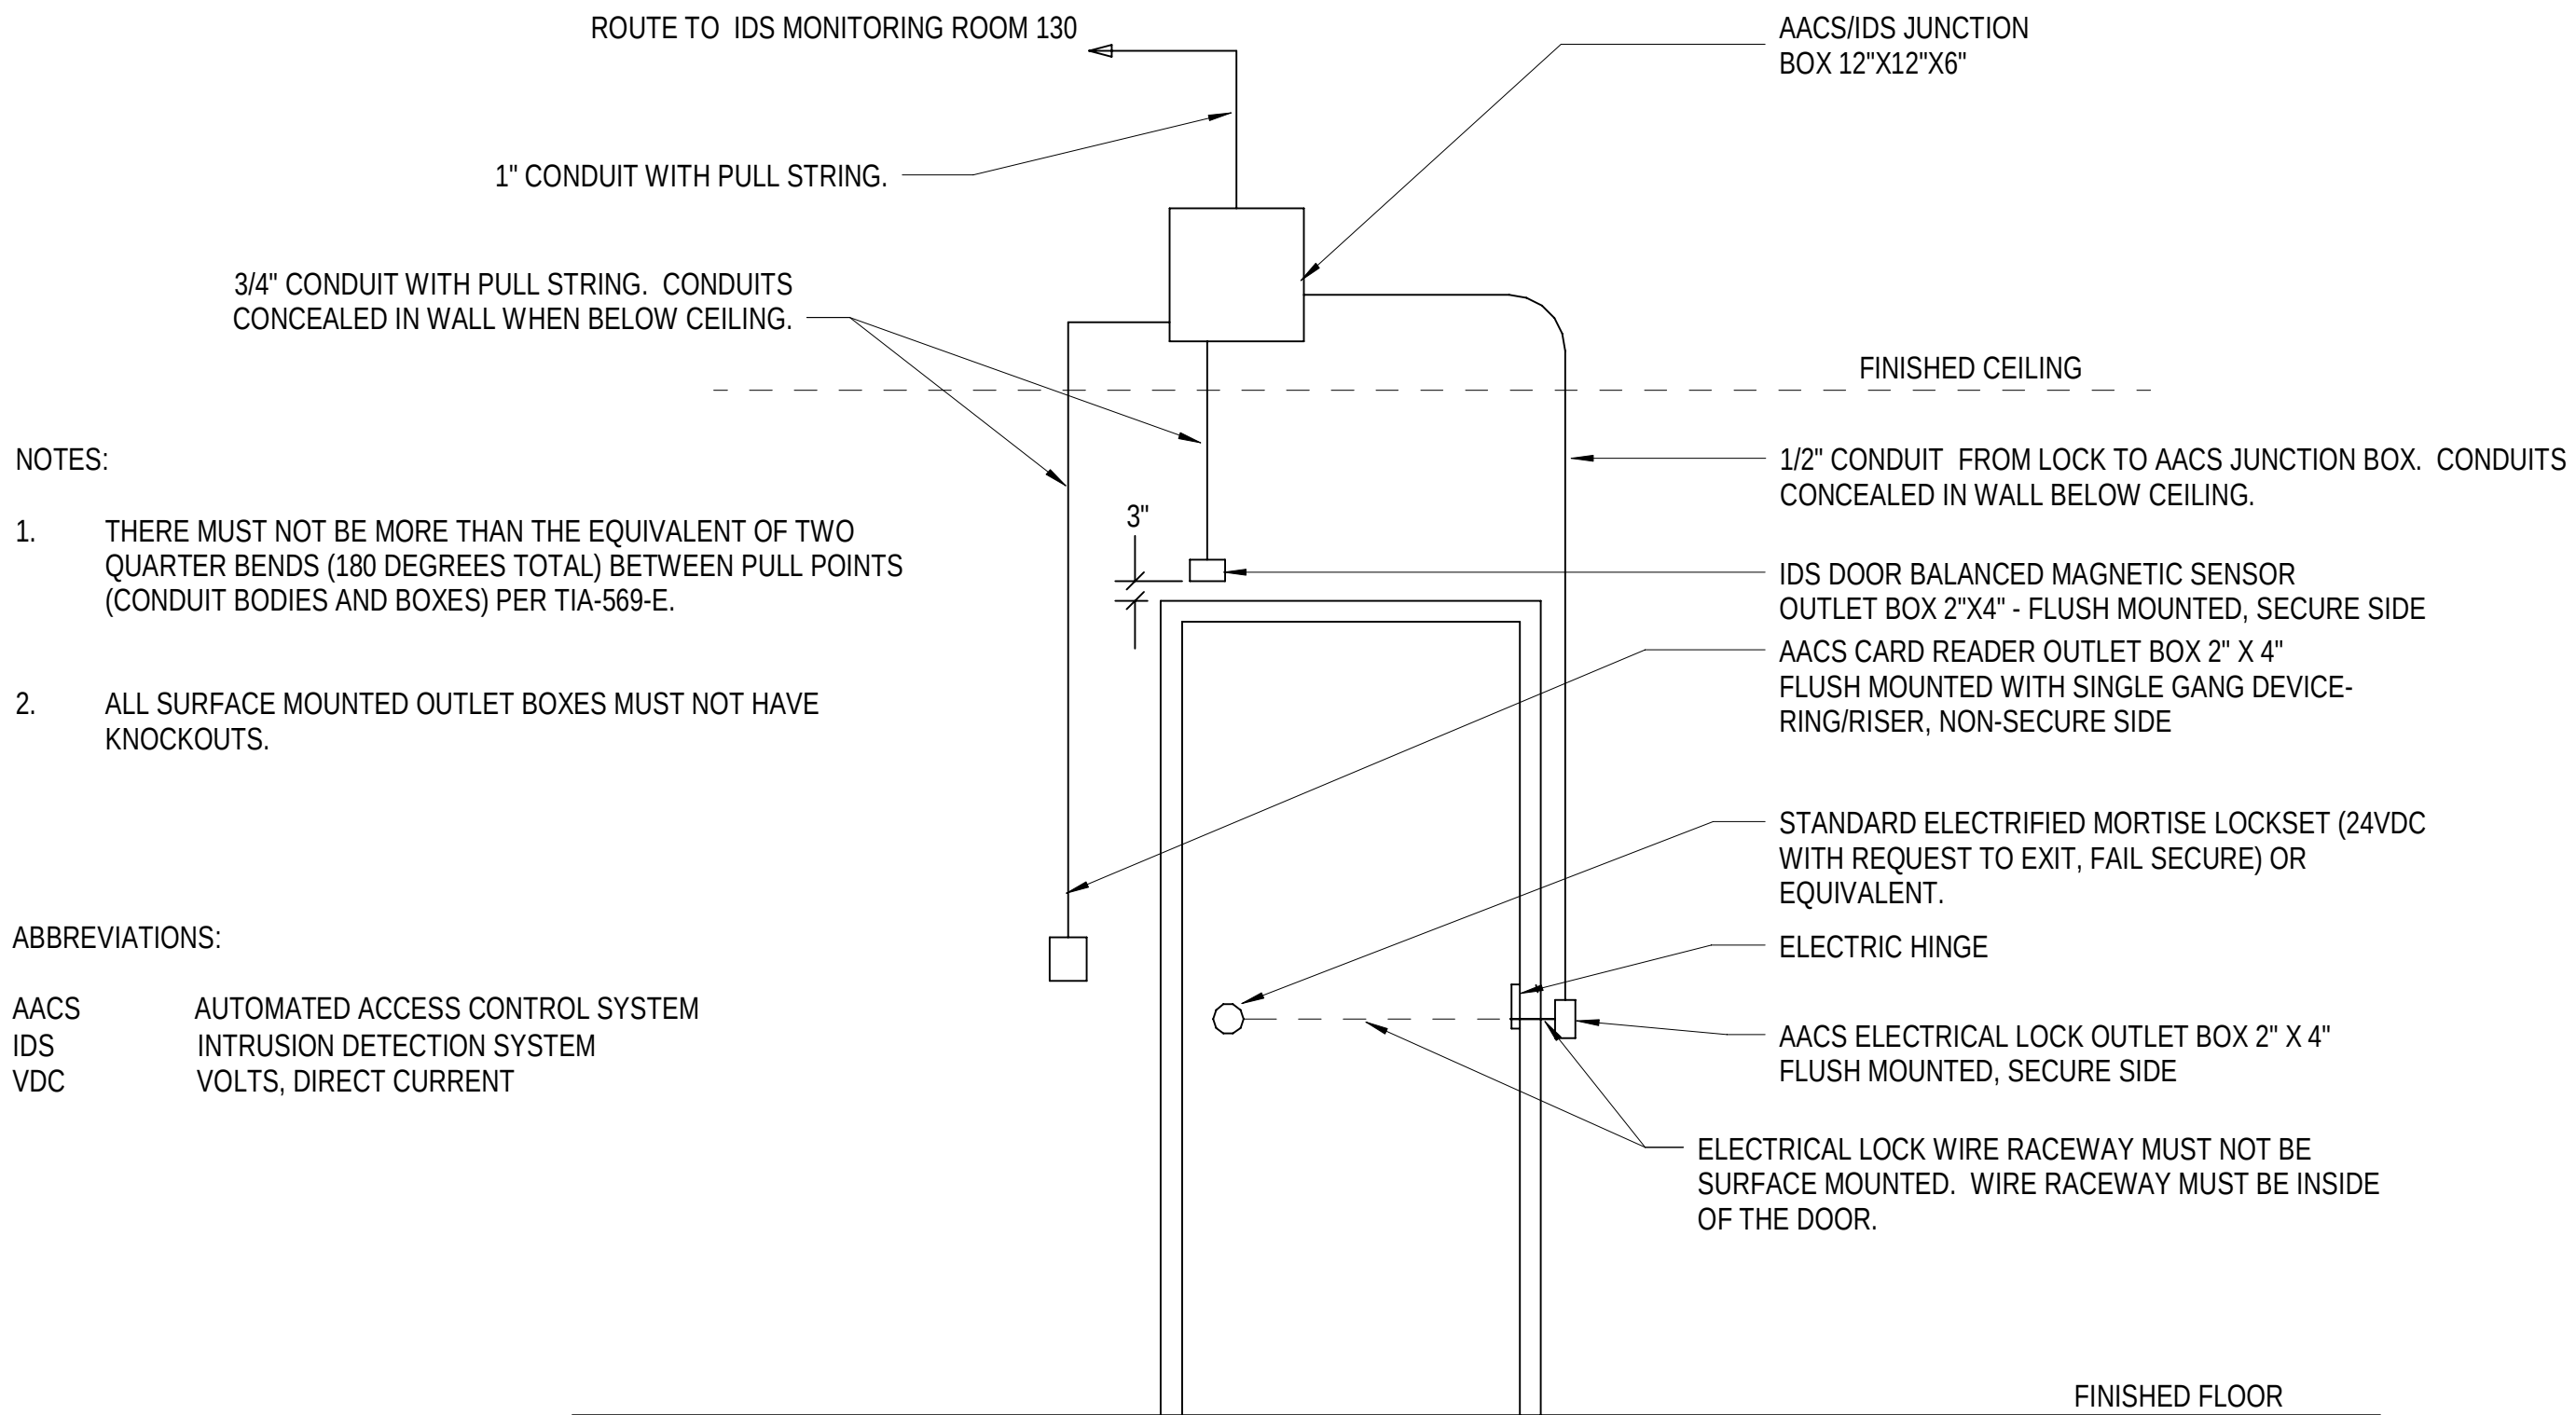

A1 SECURED SINGLE DOOR W/ CARD READER
NOT TO SCALE

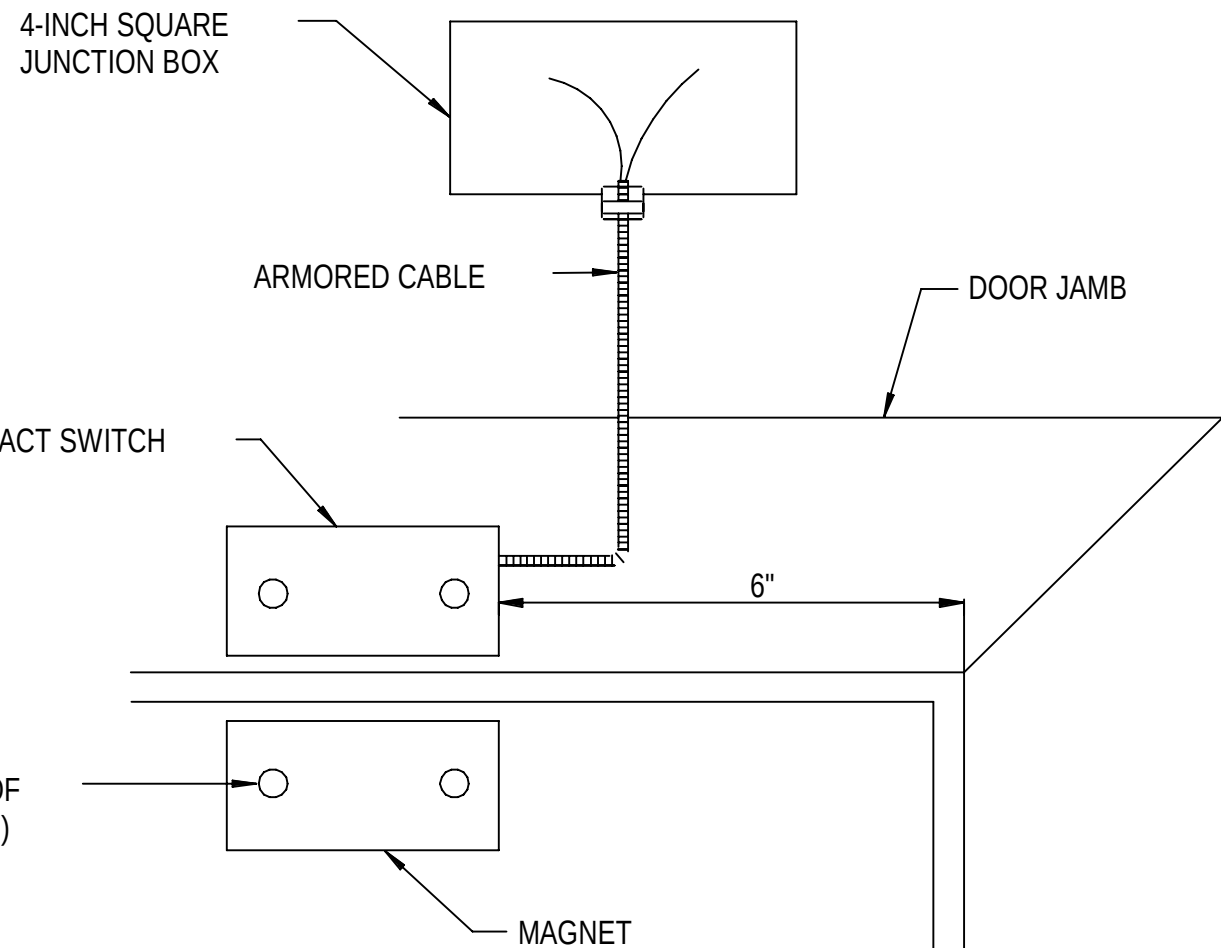


A3 SCREW MOUNT DOOR CONTACT
NTS

D

C

B

A

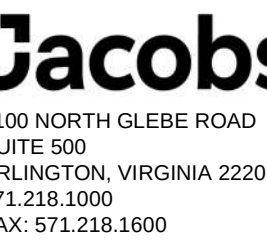

APPROVED

FOR COMMANDER NAVFAC

ACTIVITY APPROVED BY LCDR ELIZABETH
CLOKODE NAVFAC NLON READ
DIRECTOR NEW LONDON, GROTON, CT

SATISFACTORY TO DATE 05/27/2025

DES MG DRW LA CHK RR

PMIDM SDS / RSF

BRANCH MANAGER WRB

CHIEF ENGINEER JWJ

FIRE PROTECTION HPN

NAVAL FACILITIES ENGINEERING SYSTEMS COMMAND - MID-ATLANTIC
NAVAL STATION - NORFOLK, VA
GROTON, CONNECTICUT

NAVAL SUBMARINE BASE NEW LONDON
P-1102 WEAPONS MAGAZINE & ORDNANCE OPERATIONS FACILITY
OPERATIONS
SECURITY DETAILS

SCALE: AS NOTED
EPROJECT NO.: 1667770
CONSTR. CONTR. NO.
NAVFAC DRAWING NO. 12894086
SHEET 136 OF 140

TY501

1

2

3

4

5

