

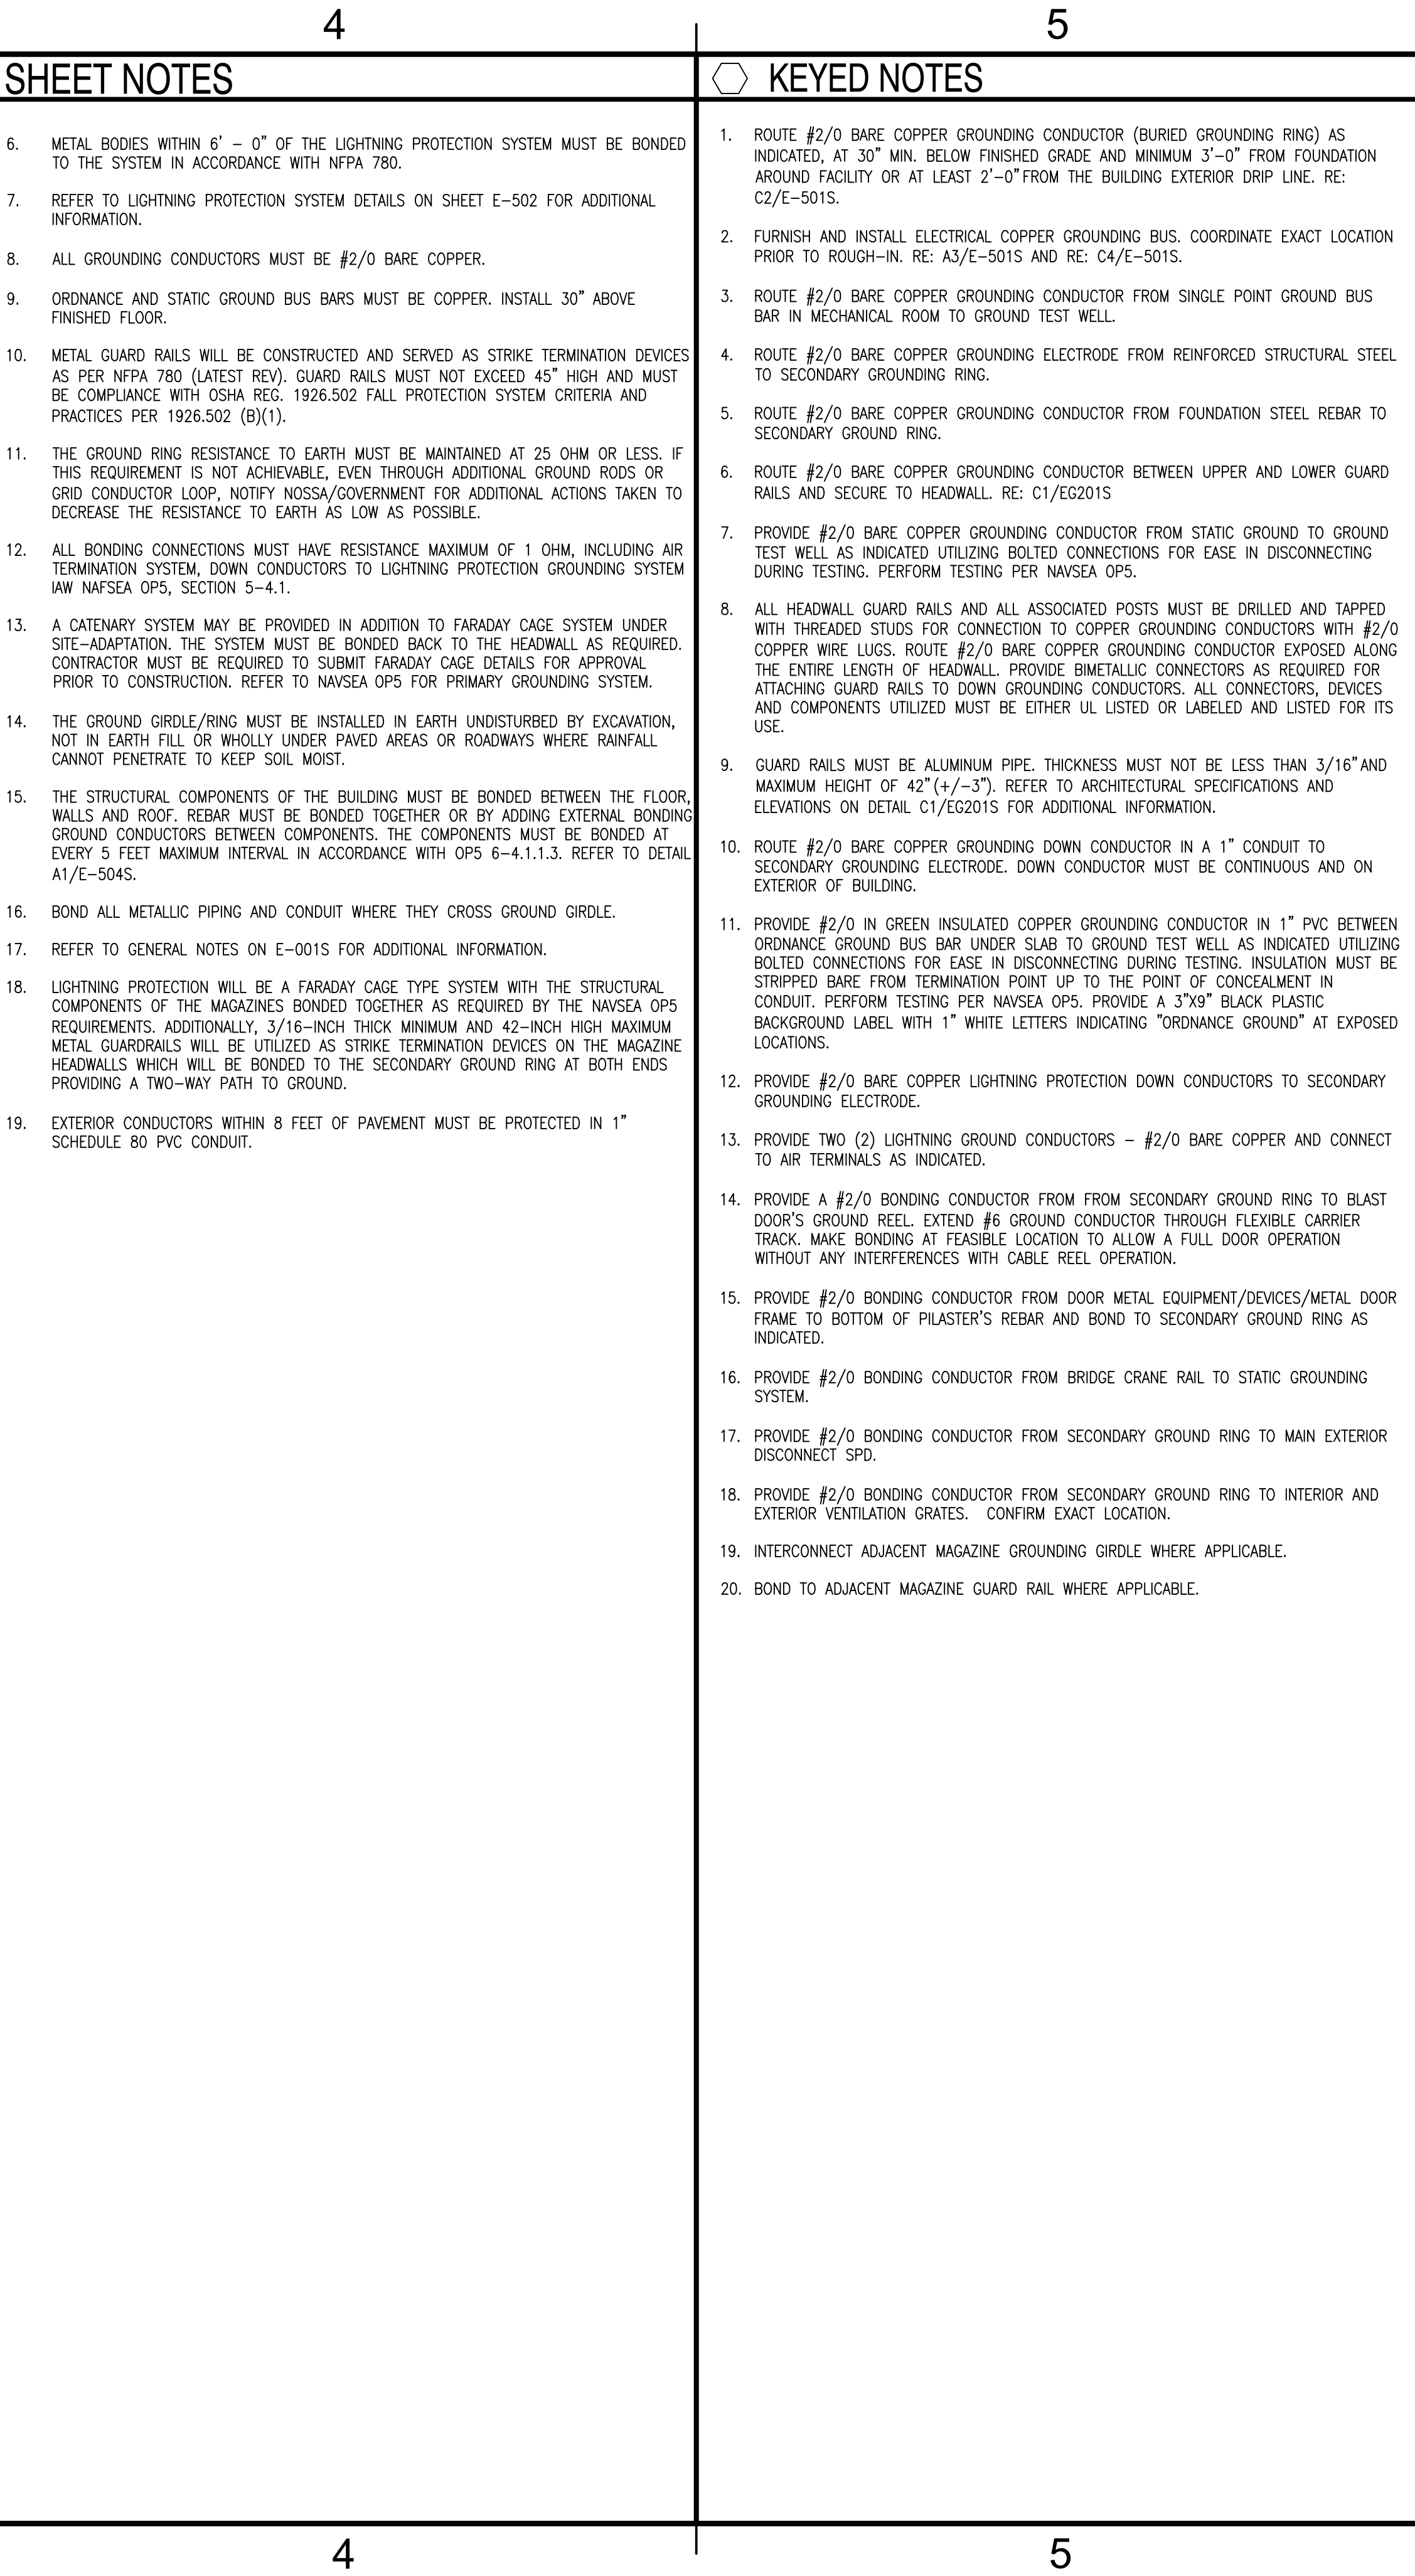
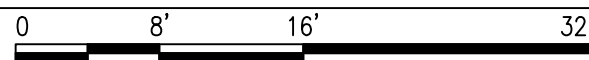


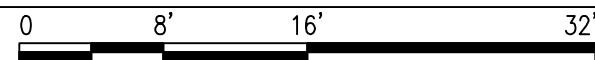

A vertical line with four tick marks. From bottom to top, the tick marks are labeled A, B, C, and D.

EG2015

FILE NAME: C:\pwworkspace\user003\pwworkspace\1381\EG202S.dwg LAYOUT NAME: EG202 - ELECTRICAL LIGHTNING ZONE PROTECTION ELEVATION PLOTTED: Thursday, June 12, 2025 - 8:52am USER: PHILLIH

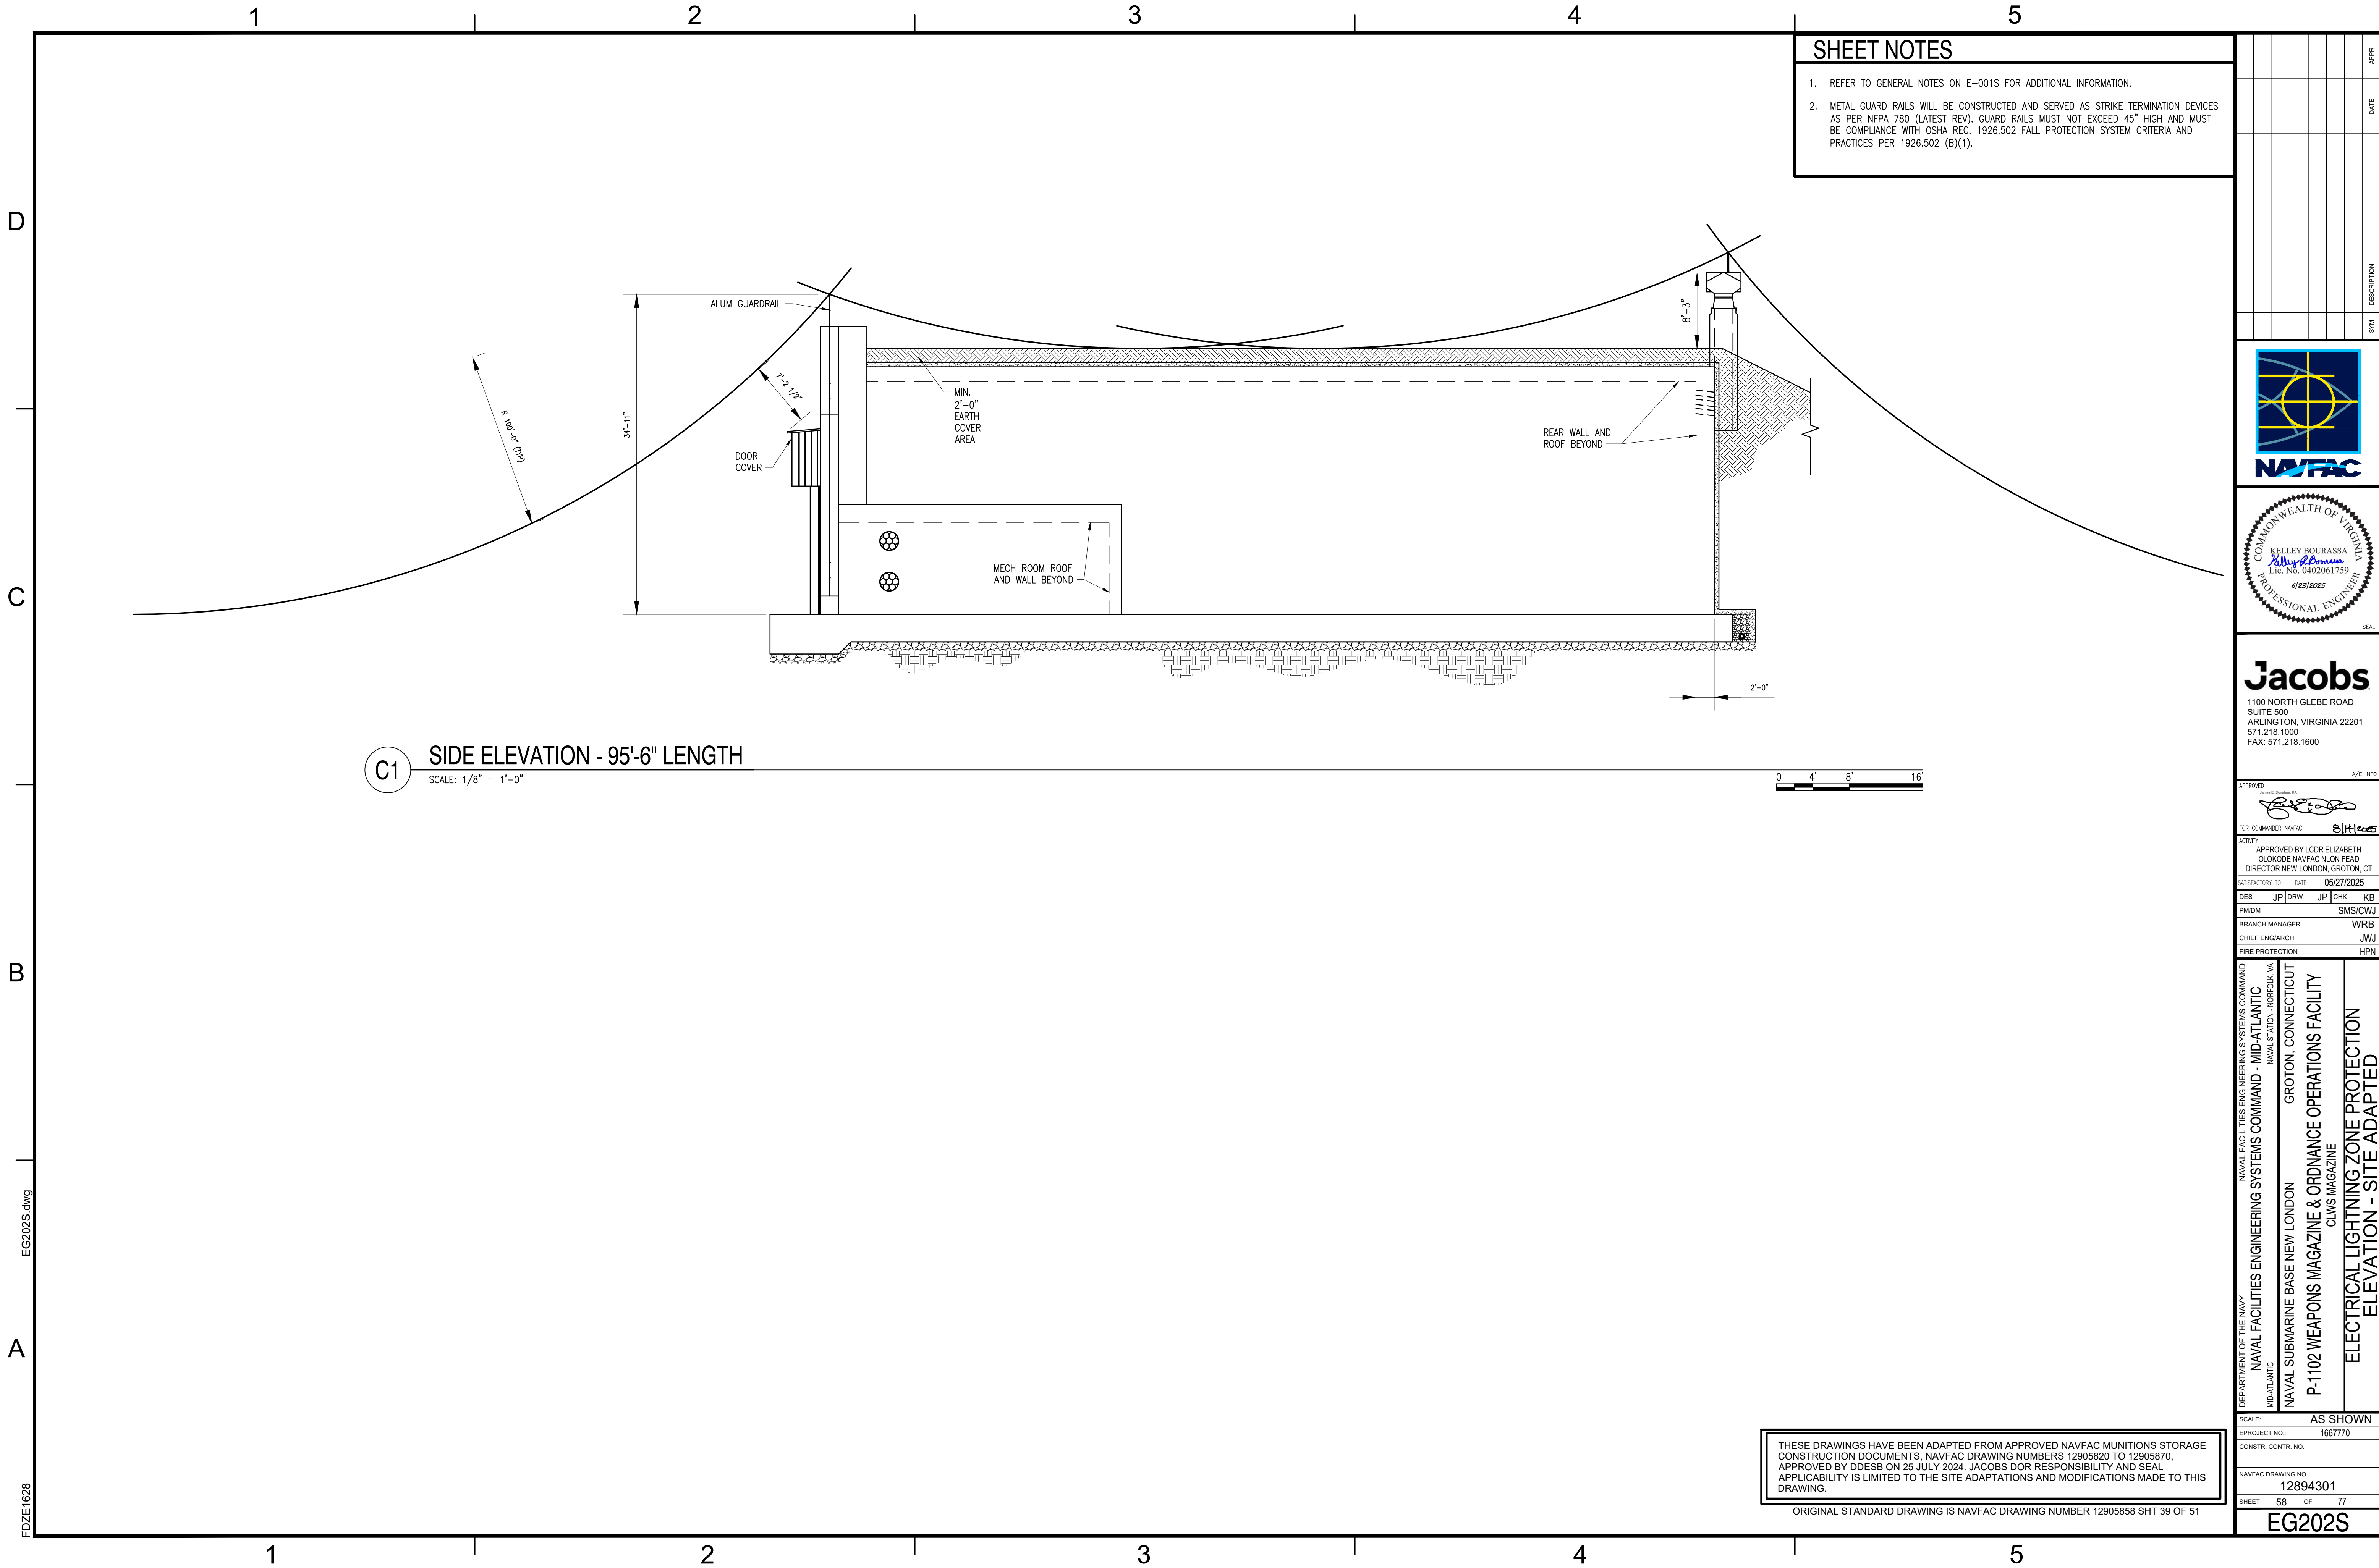

SHEET NOTES

- REFER TO GENERAL NOTES ON E-001S FOR ADDITIONAL INFORMATION.
- METAL GUARD RAILS WILL BE CONSTRUCTED AND SERVED AS STRIKE TERMINATION DEVICES AS PER NFPA 780 (LATEST REV). GUARD RAILS MUST NOT EXCEED 45" HIGH AND MUST BE COMPLIANCE WITH OSHA REG. 1926.502 FALL PROTECTION SYSTEM CRITERIA AND PRACTICES PER 1926.502 (B)(1).



Jacobs
1100 NORTH GLEBE ROAD
SUITE 500
ARLINGTON, VIRGINIA 22201
571.218.1000
FAX: 571.218.1600

APPROVED:
FOR COMMANDER NAVFAC

ACTIVITY:
APPROVED BY LCDR ELIZABETH
OLOKODE NAVFAC NLON FEAD
DIRECTOR NEW LONDON, GROTON, CT

SATISFACTORY TO DATE 06/27/2025

DES JPB DRW JPB CHK KB

PMDM SMS/CWJ

BRANCH MANAGER WRB

CHIEF ENGINEER JWW

FIRE PROTECTION HPN

DEPARTMENT OF THE NAVY
NAVAL FACILITIES ENGINEERING SYSTEMS COMMAND - MID-ATLANTIC
NAVAL STATION - GROTON, CT
NAVAL SUBMARINE BASE NEW LONDON
P-1102 WEAPONS MAGAZINE & ORDNANCE OPERATIONS FACILITY
CLWS MAGAZINE
ELECTRICAL LIGHTNING ZONE PROTECTION
ELEVATION - SITE ADAPTED

SCALE: AS SHOWN
EPROJECT NO.: 1667770
CONSTR. CONTR. NO.

NAVFAC DRAWING NO.: 12894301

SHEET 58 OF 77

EG202S

THESE DRAWINGS HAVE BEEN ADAPTED FROM APPROVED NAVFAC MUNITIONS STORAGE CONSTRUCTION DOCUMENTS, NAVFAC DRAWING NUMBERS 12905820 TO 12905870, APPROVED BY DDESB ON 25 JULY 2024. JACOBS DOR RESPONSIBILITY AND SEAL APPLICABILITY IS LIMITED TO THE SITE ADAPTATIONS AND MODIFICATIONS MADE TO THIS DRAWING.

ORIGINAL STANDARD DRAWING IS NAVFAC DRAWING NUMBER 12905858 SHT 39 OF 51


FILE NAME: C:\pwworkspace\12905859\12905859.dwg PLOTTED: Thursday, June 12, 2025 - 8:17am USER: PHILLUH

E-501S.dwg

FDZE1628

THESE DRAWINGS HAVE BEEN ADAPTED FROM APPROVED NAVFAC MUNITIONS STORAGE CONSTRUCTION DOCUMENTS, NAVFAC DRAWING NUMBERS 12905820 TO 12905870, APPROVED BY DDESB ON 25 JULY 2024. JACOBS DOR RESPONSIBILITY AND SEAL APPLICABILITY IS LIMITED TO THE SITE ADAPTATIONS AND MODIFICATIONS MADE TO THIS DRAWING.


ORIGINAL STANDARD DRAWING IS NAVFAC DRAWING NUMBER 12905859 SHT 40 OF 51

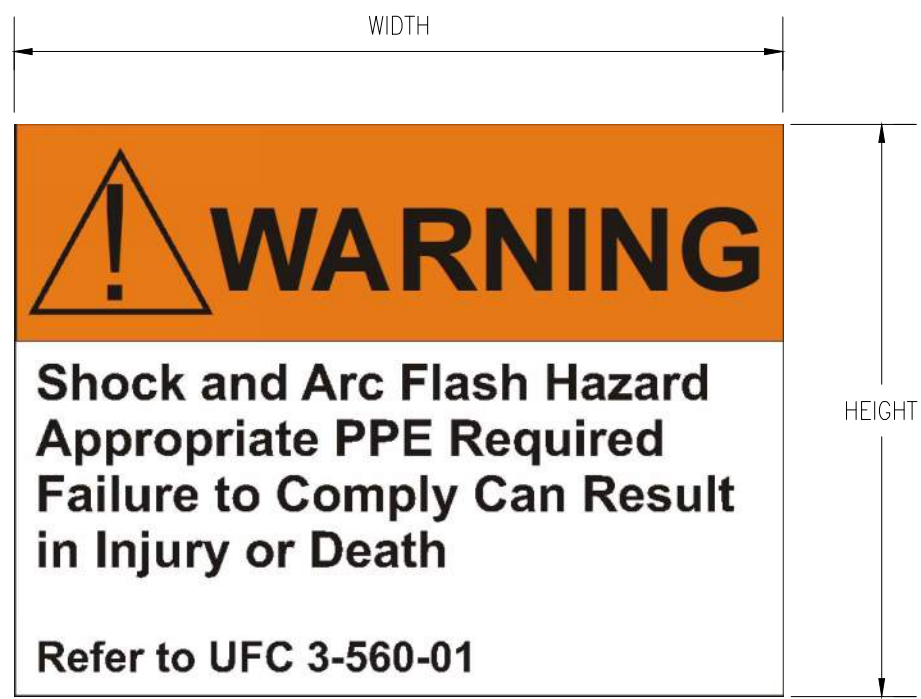

NOTES:


1. PROVIDE SELF-ADHESIVE VINYL LABEL TO AFFIX TO ELECTRICAL EQUIPMENT TO WARN OF ARC FLASH HAZARDS.
2. THE LABEL FORMAT AND TEXT CAN BE MODIFIED PROVIDED THAT THE INFORMATION REQUIRED BY UFC 3-501-01 IS INCLUDED.
3. THE LABEL MUST BE LOCATED ON THE EQUIPMENT TO BE CLEARLY VISIBLE TO QUALIFIED PERSONS BEFORE EXAMINATION, ADJUSTMENT, SERVICING, OR MAINTENANCE OF THE EQUIPMENT.
4. THE SIZE OF THE LABEL MUST BE MINIMUM:

EQUIPMENT TYPE	HEIGHT	WIDTH
INDOOR	2"	3"
OUTDOOR	3"	4.5"
5. A DOWNLOADABLE WINDOWS METAFILE IS AVAILABLE ON THE WHOLE BUILDING DESIGN GUIDE WEBSITE (WWW.WBDG.ORG) FOR USE IN A LABEL MAKING MACHINE.
 - A. THE FILE IS LOCATED ON THE "UFGS FORMS, GRAPHICS, AND TABLES" PAGE. TO NAVIGATE TO THIS LOCATION, FOLLOW: HOME > FEDERAL FACILITY CRITERIA > DEPARTMENT OF DEFENSE > UNITED FACILITIES GUIDE SPECIFICATIONS (UFGS) > UFGS FORMS, GRAPHICS, AND TABLES > ARCH FLASH WARNING LABELS.
 - B. ALTERNATIVELY, TYPE IN THE FOLLOWING ADDRESS IN INTERNET EXPLORER: [HTTPS://WWW.WBDG.ORG/FFG/NAVGRAPH/ARC_FLASH_WARNING_LABELS.ZIP](https://www.wbdg.org/ffg/navgraph/arc_flash_warning_labels.zip)

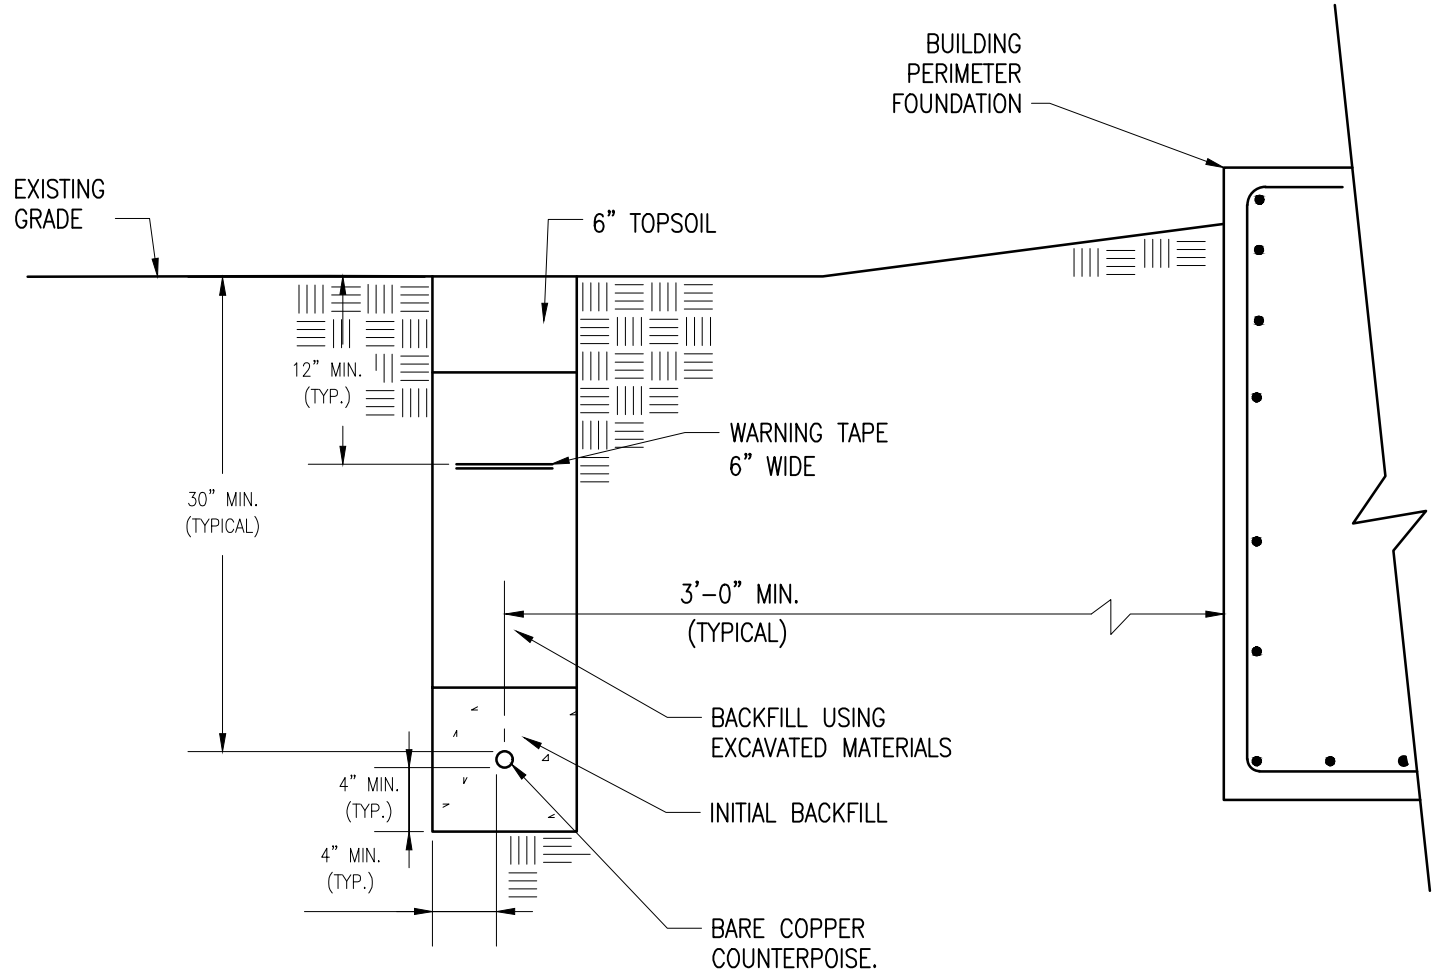


C2 TYPICAL GROUND RING INSTALLATION DETAIL

SCALE: NO SCALE

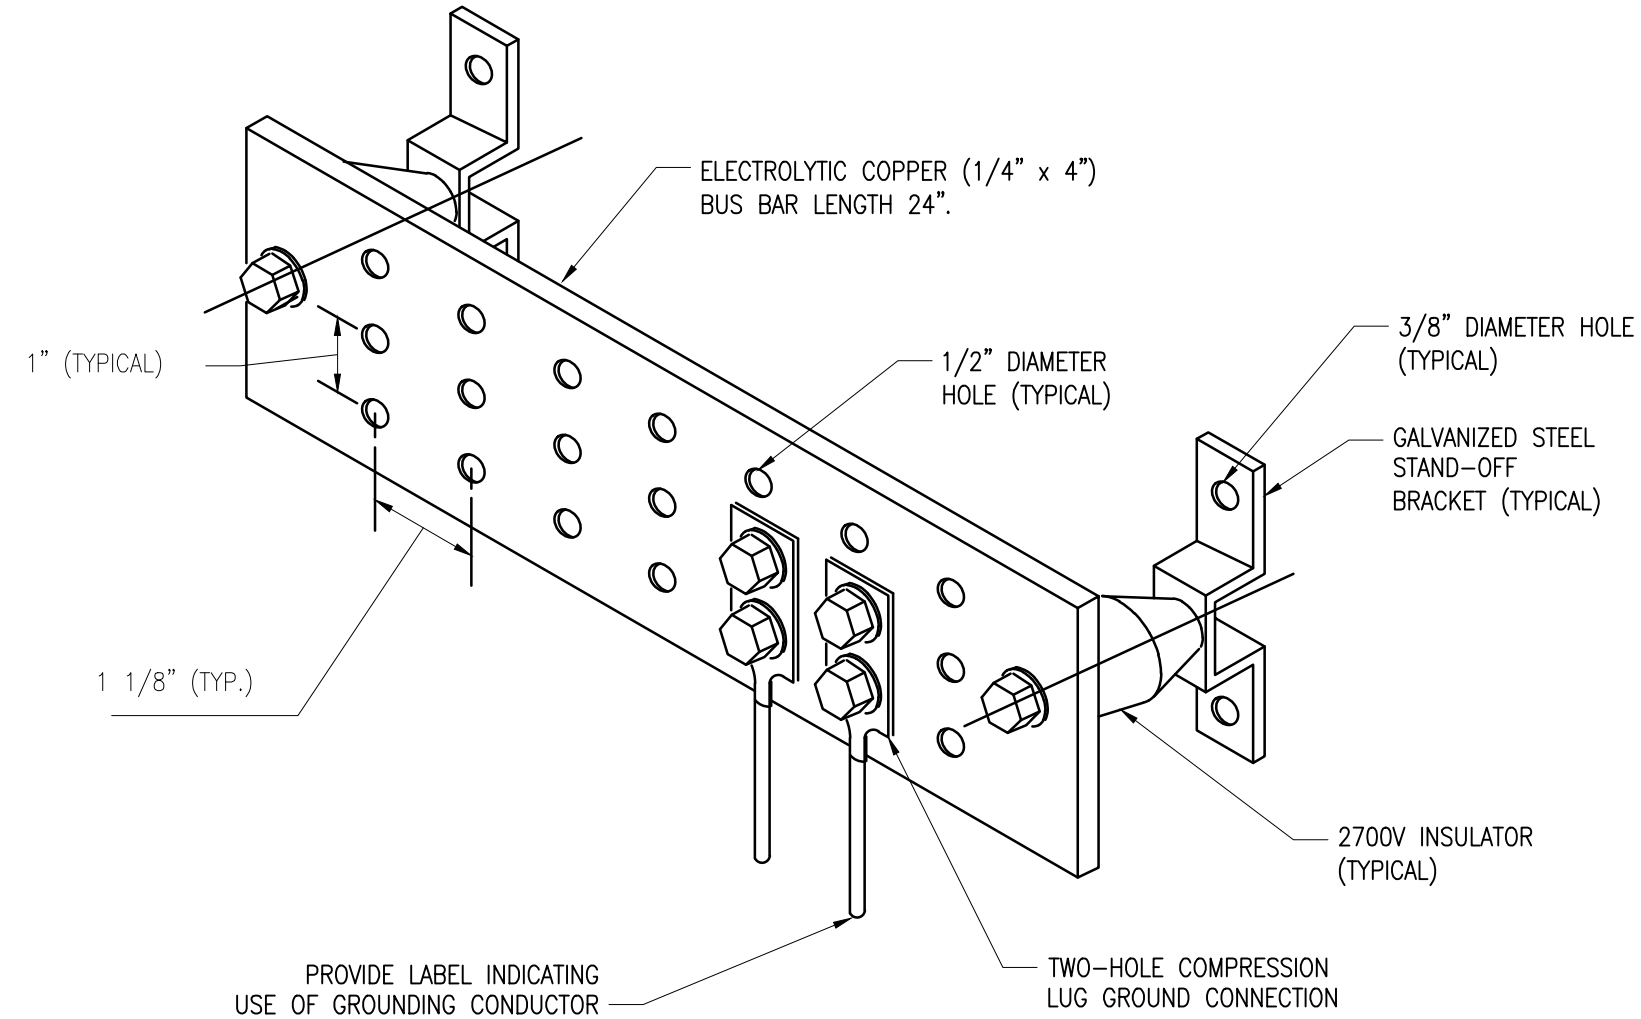


C4 SINGLE POINT GROUNDING BUS BAR (SPGB) BAR DETAIL - TYPICAL

SCALE: NO SCALE

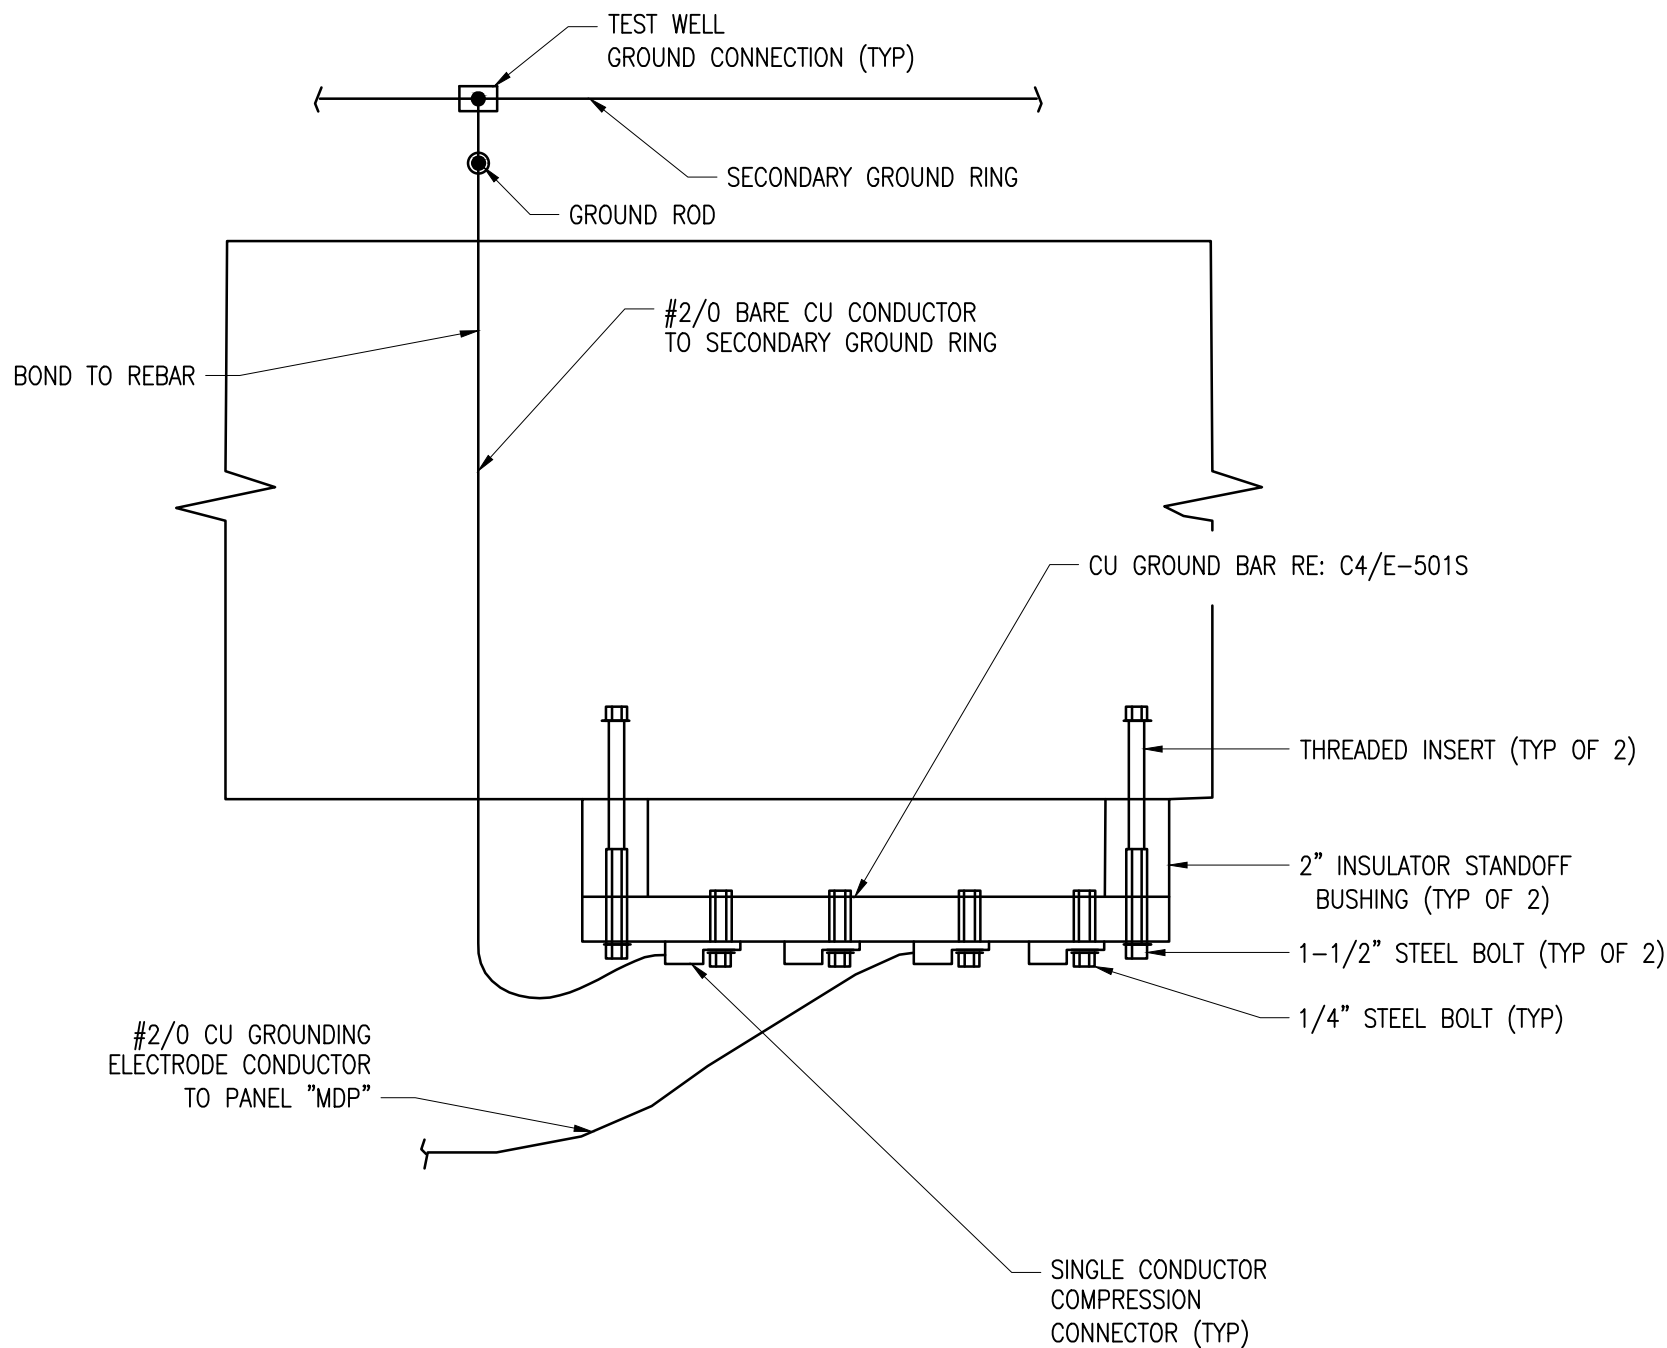

A3 SINGLE POINT GROUND BAR DETAIL



SCALE: NO SCALE

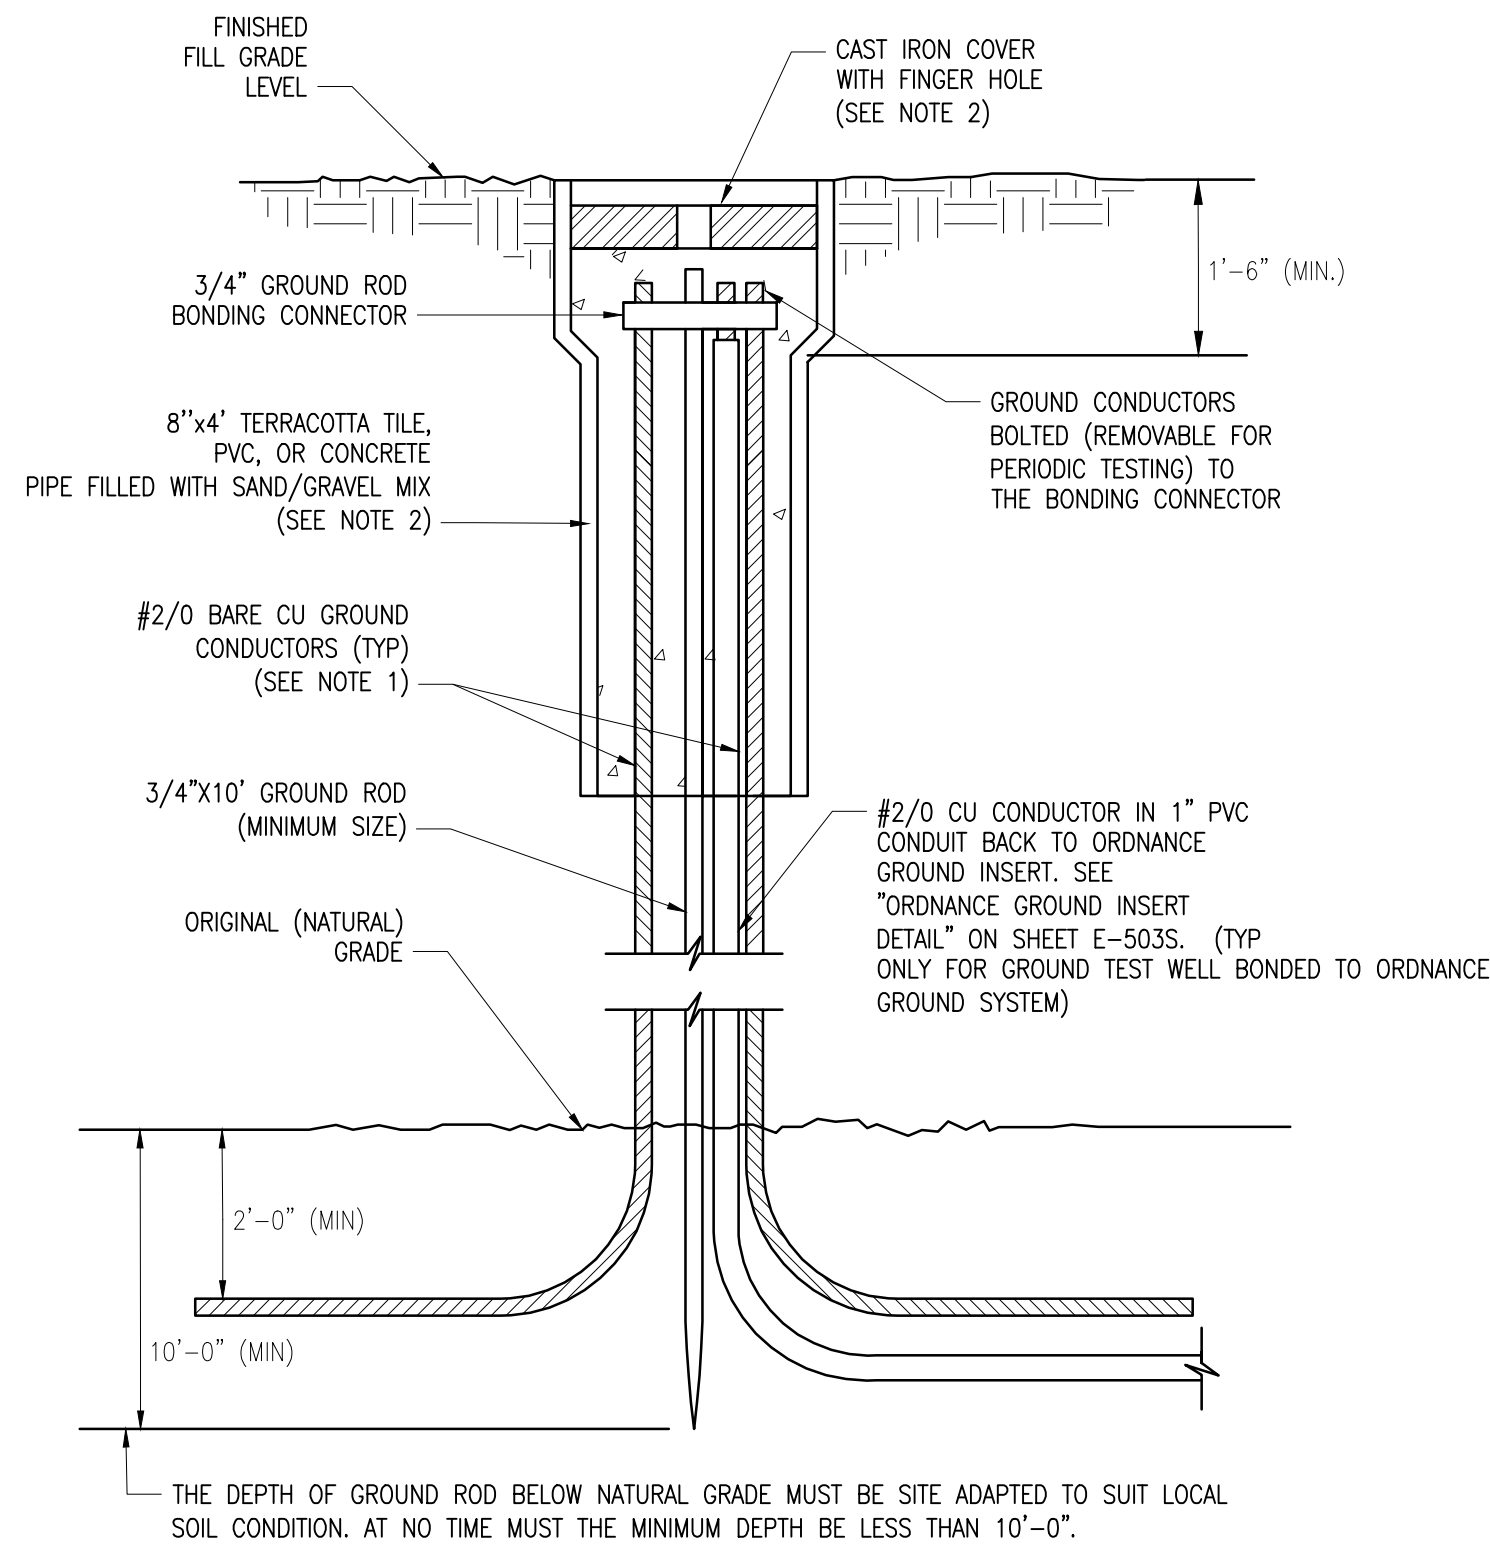


A4 GROUND TEST WELL INSTALLATION IN EARTH FILL

SCALE: NO SCALE

SYMBOL	DESCRIPTION	DATE	APPROVED

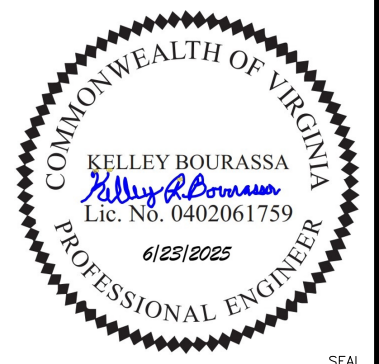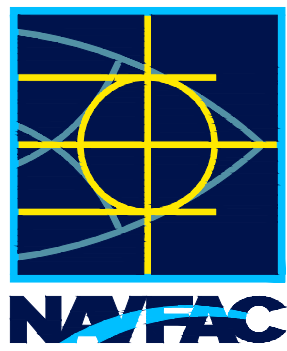

Jacobs
1100 NORTH GLEBE ROAD
SUITE 500
ARLINGTON, VIRGINIA 22201
571.218.1000
FAX: 571.218.1600

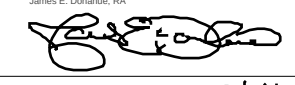APPROVED: 
FOR COMMANDER NAVFAC

ACTIVITY: APPROVED BY LCDR ELIZABETH OLOKODE NAVFAC NLON FEAD
DIRECTOR NEW LONDON, GROTON, CT

SATISFACTORY TO: DATE: 05/27/2025
DES: JP | DRW: JP | CHK: KB
PM/DM: SMS/CWJ
BRANCH MANAGER: WRB
CHIEF ENGINEER: JMWJ
FIRE PROTECTION: HPN

DEPARTMENT OF THE NAVY
NAVAL FACILITIES ENGINEERING SYSTEMS COMMAND
NAVAL FACILITIES ENGINEERING SYSTEMS COMMAND - MID-ATLANTIC
NAVAL STATION - NORFOLK VA
NAVAL SUBMARINE BASE NEW LONDON
GROTON, CONNECTICUT
P-1102 WEAPONS MAGAZINE & ORDNANCE OPERATIONS FACILITY
CLWS MAGAZINE
ELECTRICAL DETAILS - SITE ADAPTED

SCALE: NONE
EPROJECT NO.: 1667770
CONSTR. CONTR. NO.:
NAVFAC DRAWING NO.: 12894302
SHEET 59 OF 77
E-501S

FILE NAME: C:\pwworkspace\der003\pwworkspace\phillip\1711381\1711381-E-503S.dwg LAYOUT NAME: E-503 - ELECTRICAL DETAILS PLOTTED: Thursday, June 12, 2025 - 8:36am USER: PHILLIP

FDZE1628 E-503S.dwg

A


B

C

D


A1 STATIC GROUND INSERT DETAIL

SCALE: NO SCALE

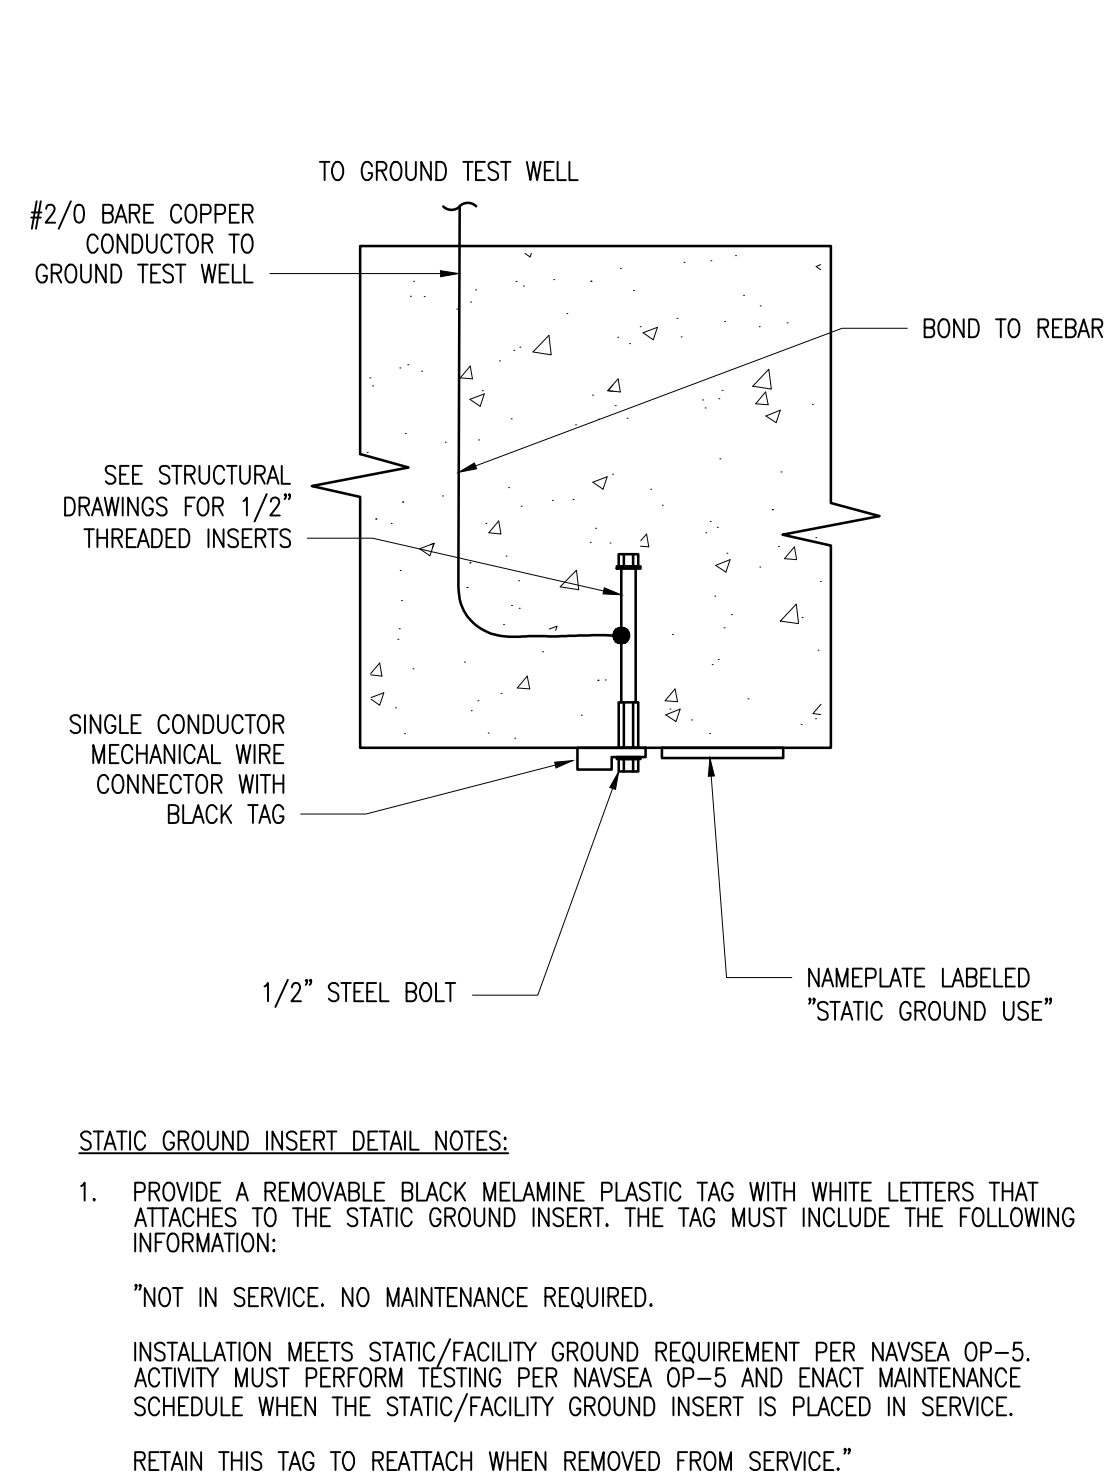


A2 ORDNANCE GROUND INSERT DETAIL

SCALE: NO SCALE

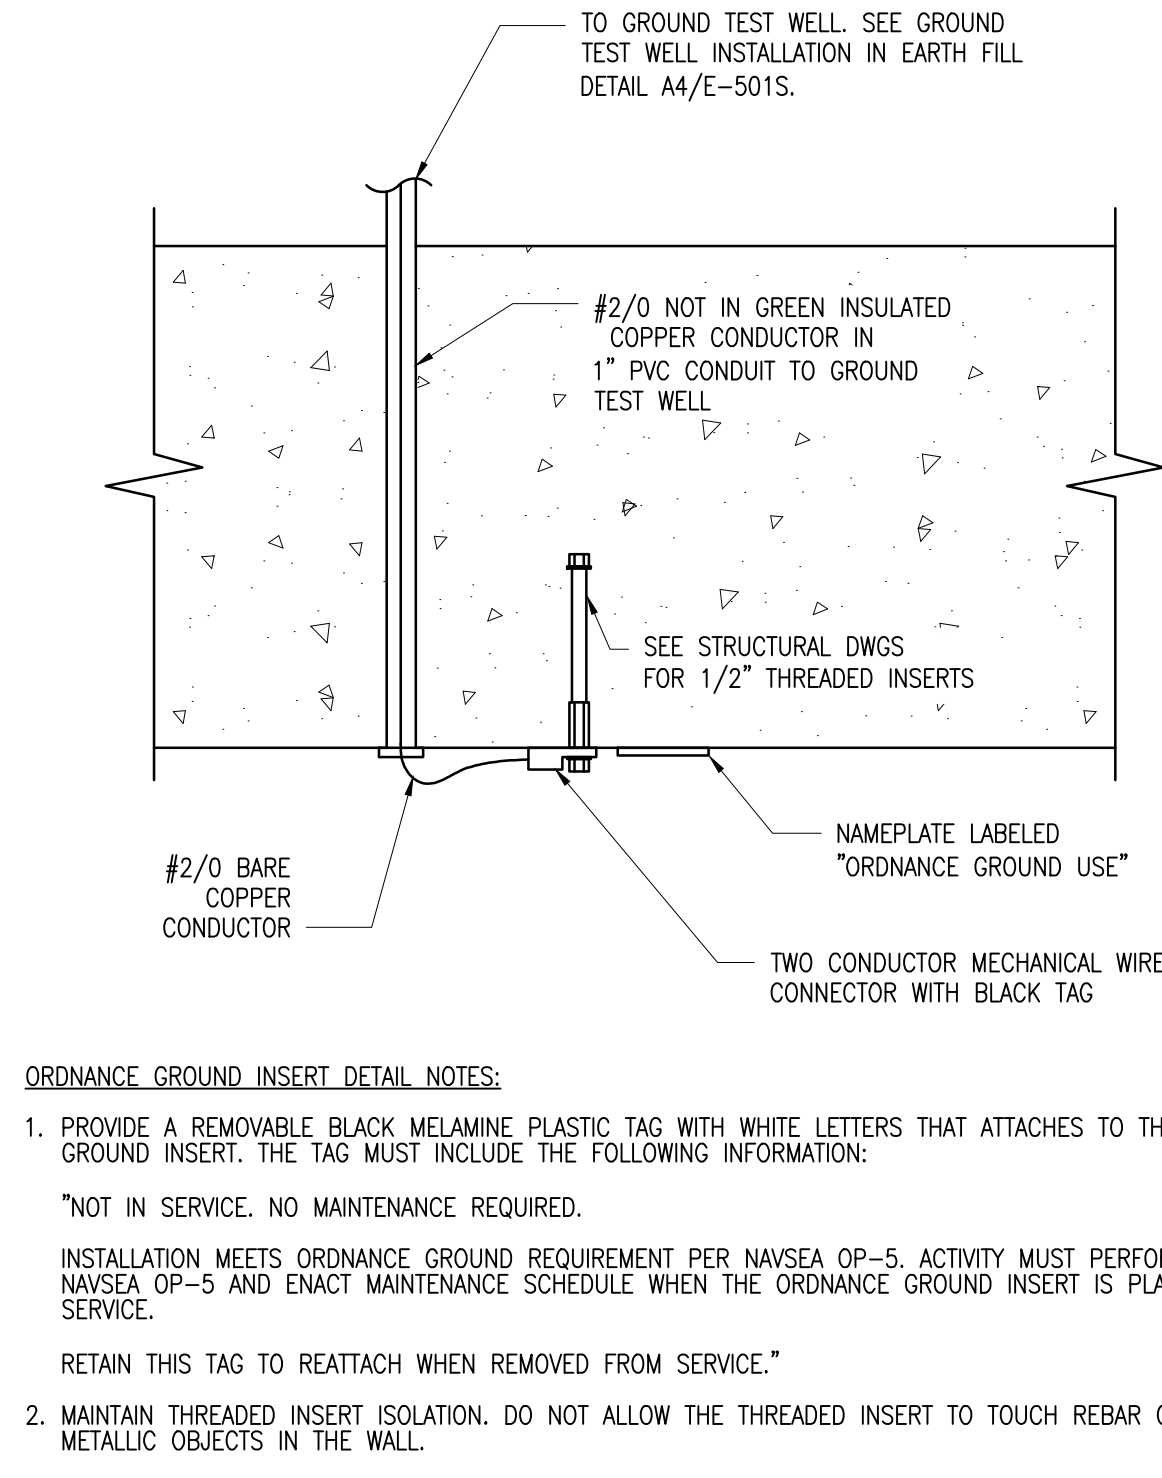

A4 LIGHTING CONTACTOR PANEL 'LCP#'

SCALE: NO SCALE

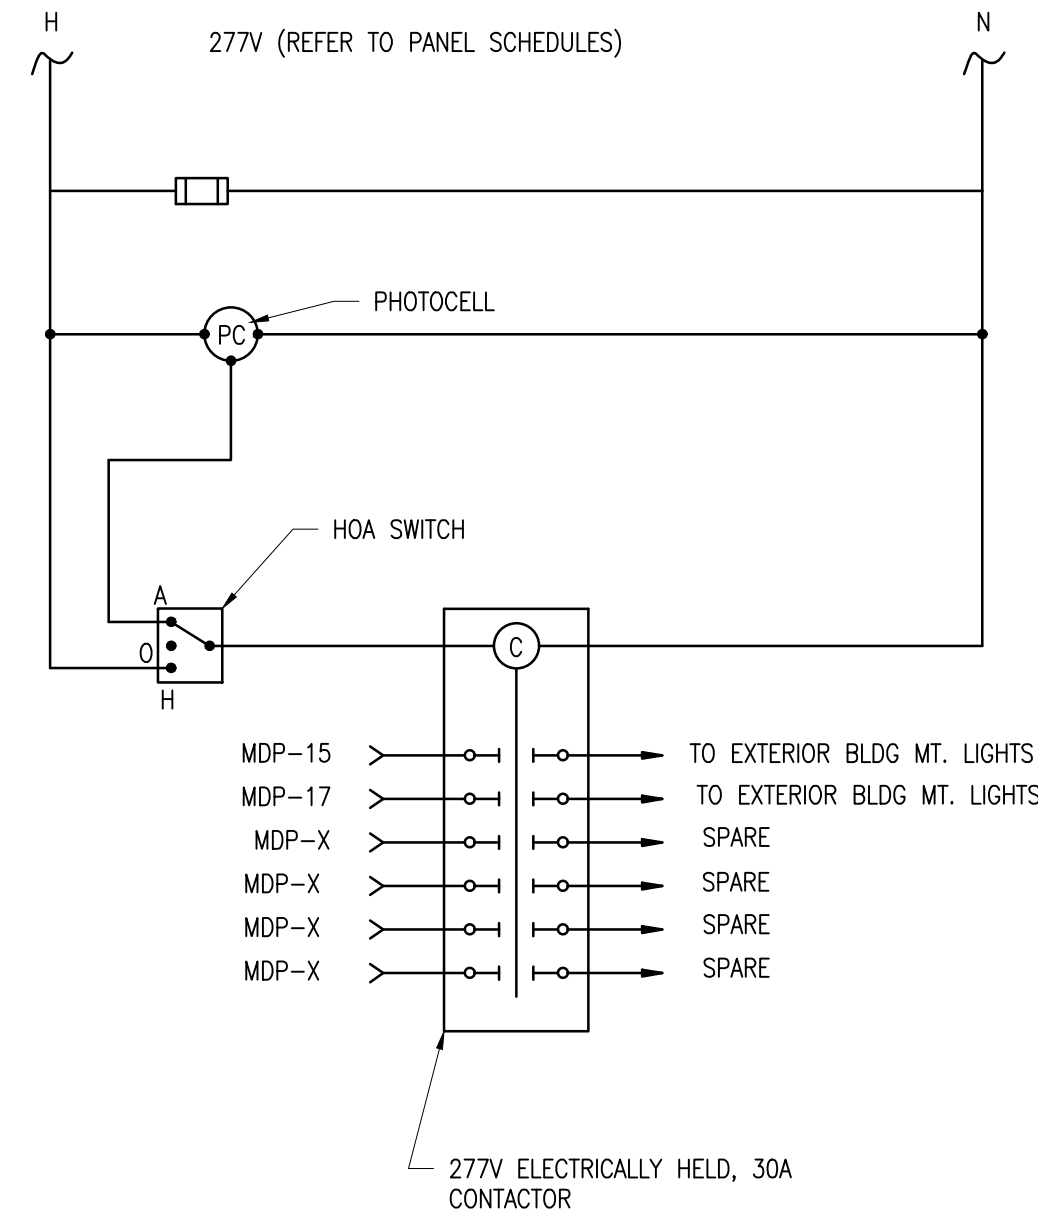


THESE DRAWINGS HAVE BEEN ADAPTED FROM APPROVED NAVFAC MUNITIONS STORAGE CONSTRUCTION DOCUMENTS. NAVFAC DRAWING NUMBERS: 129058820 TO 129058870, APPROVED BY DDESB ON 25 JULY 2024. JACOBS DOR RESPONSIBILITY AND SEAL APPLICABILITY IS LIMITED TO THE SITE ADAPTATIONS AND MODIFICATIONS MADE TO THIS DRAWING.

ORIGINAL STANDARD DRAWING IS NAVFAC DRAWING NUMBER 12905881 SHT 42 OF 51


C2 CONDUIT/PIPE GROUND CONNECTION

SCALE: NO SCALE

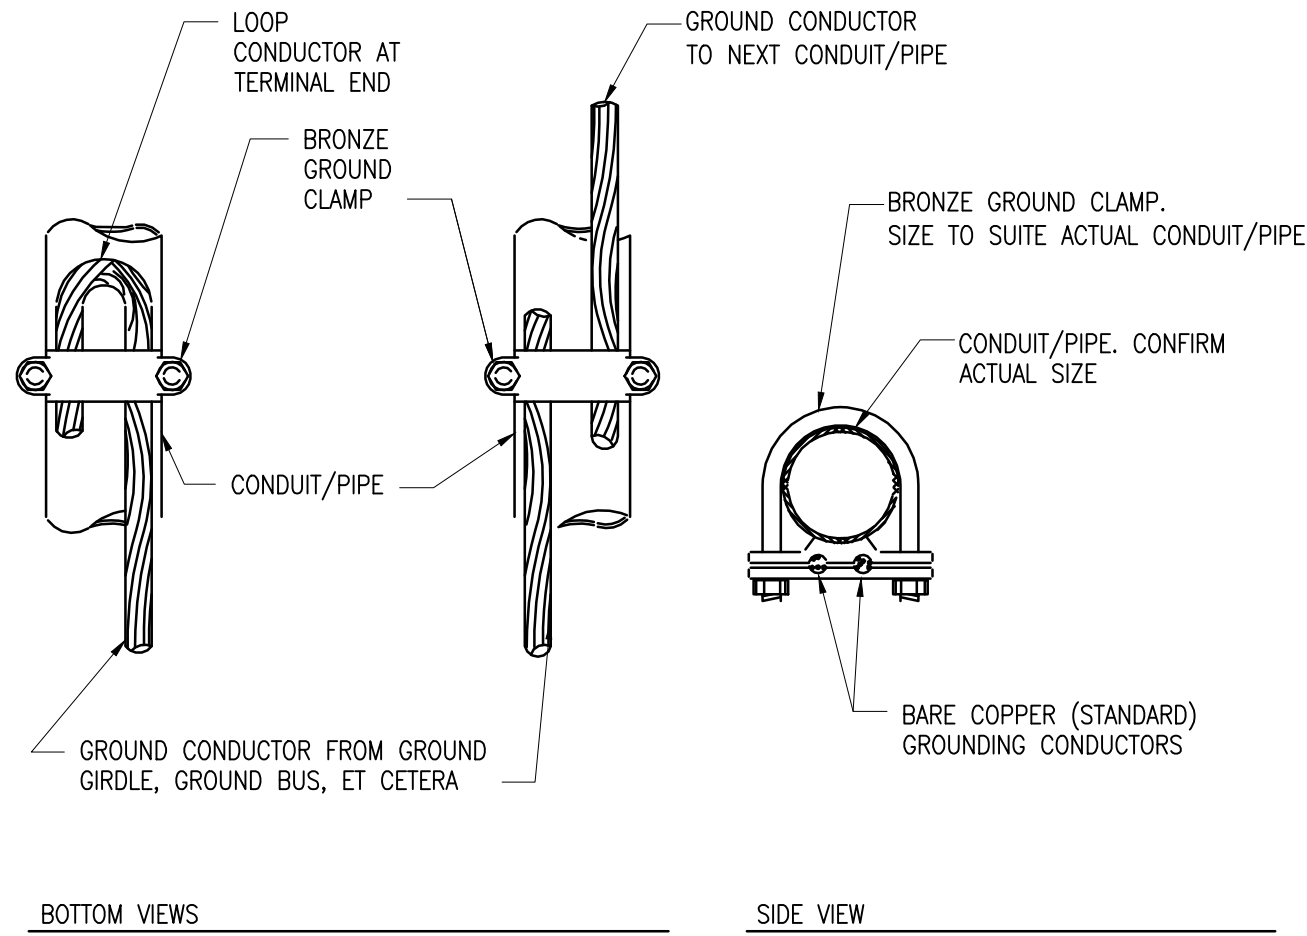

C4 GROUNDING CONDUCTOR SUPPORT DETAILS (TYPICAL FOR EXPOSED CONDUCTORS)

SCALE: NO SCALE

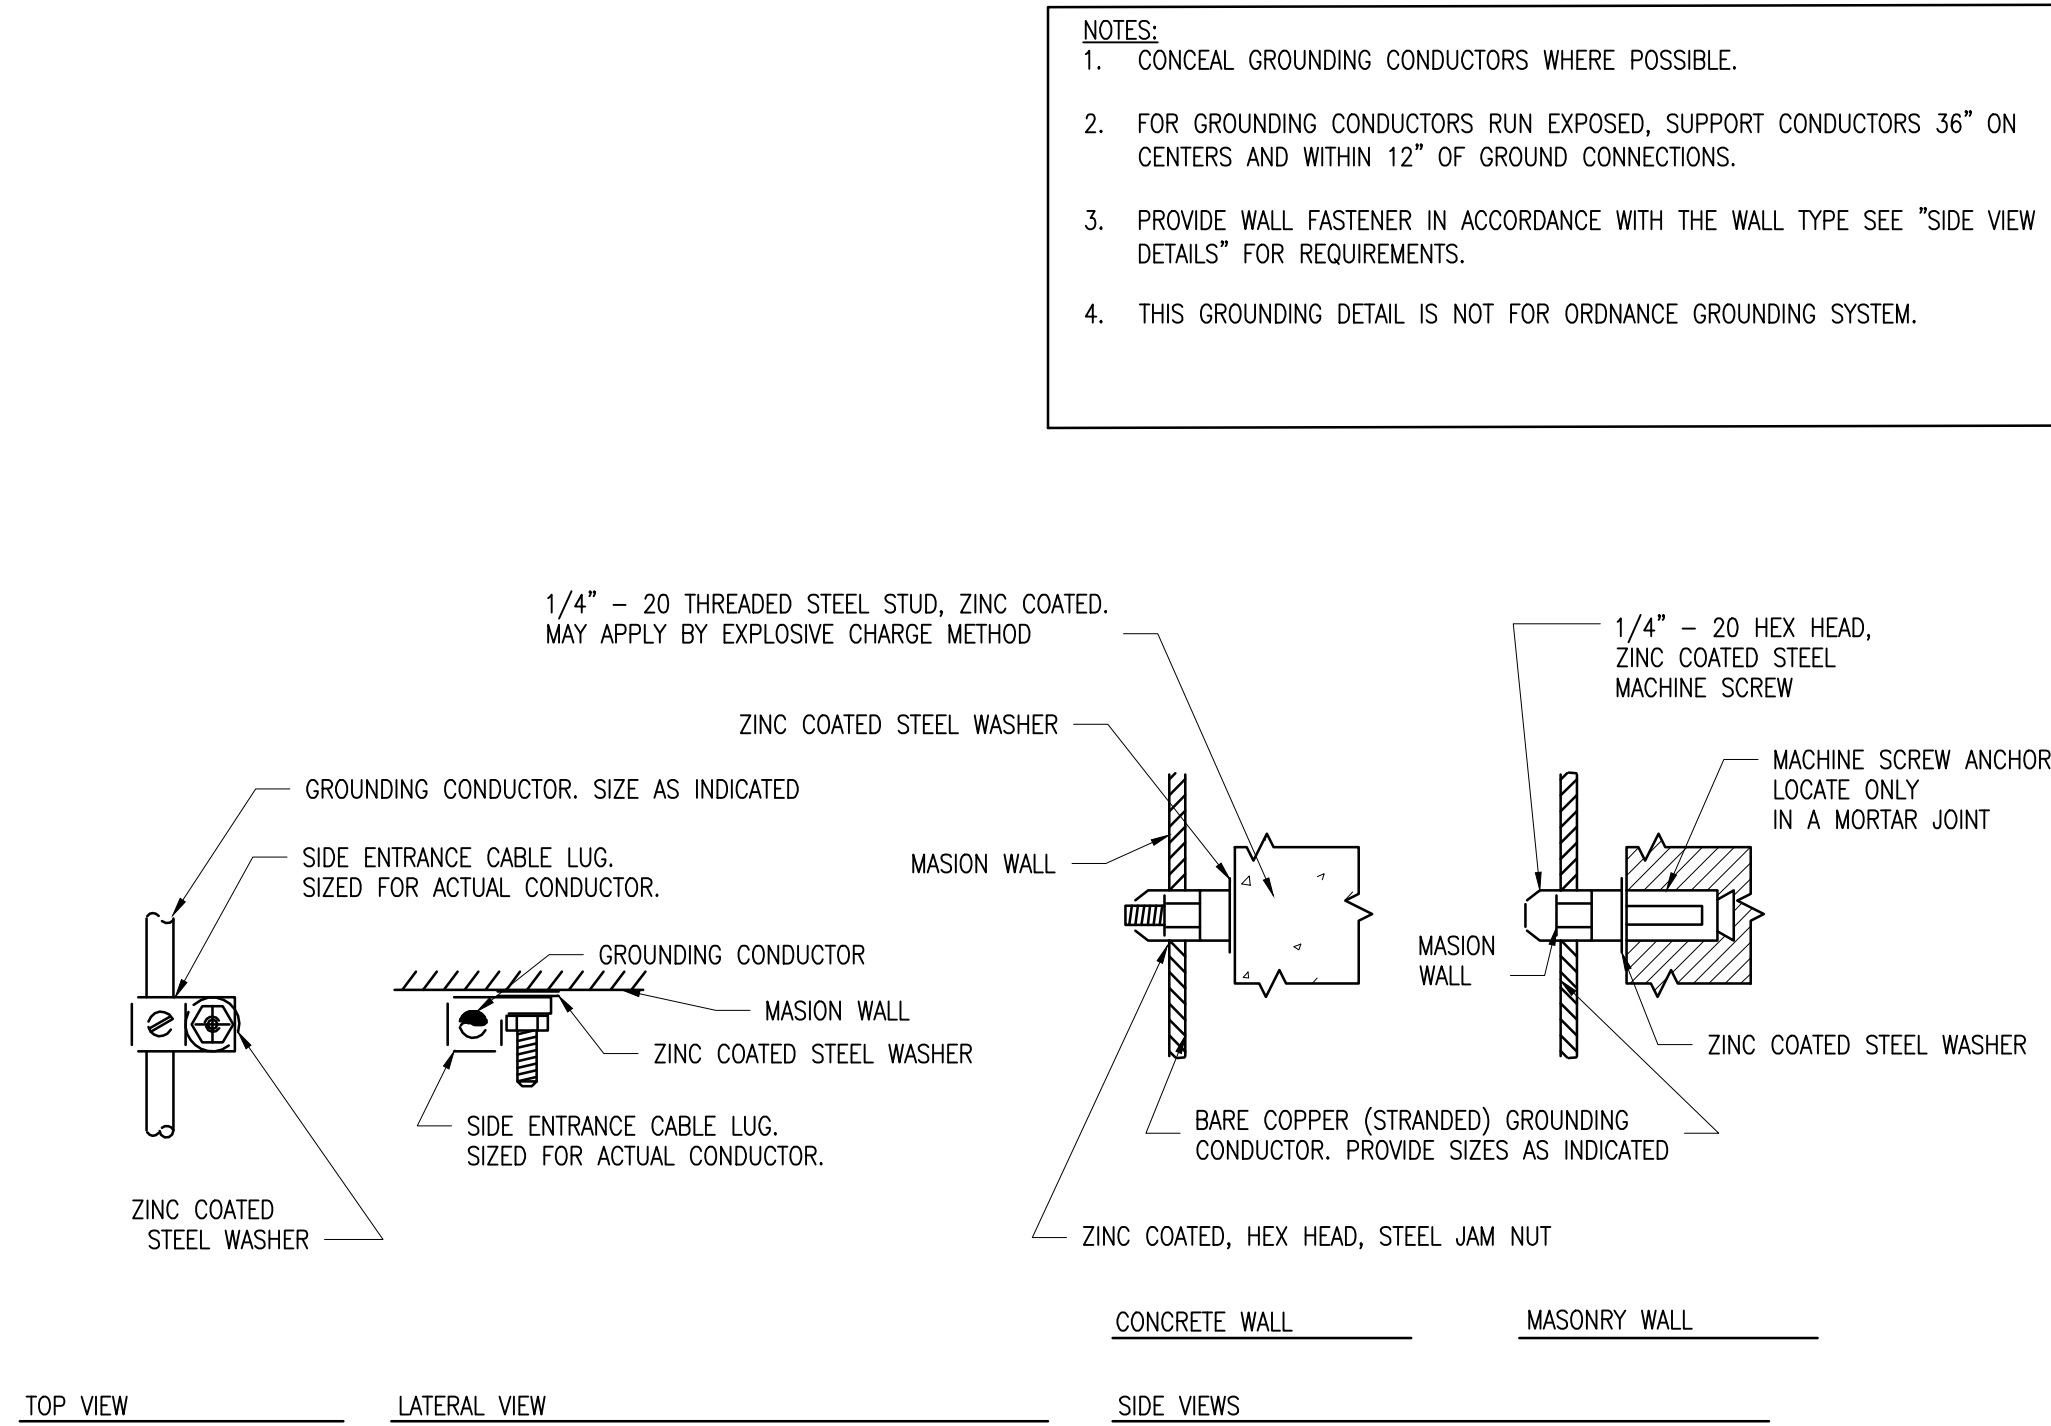

NOTES:

1. CONCEAL GROUNDING CONDUCTORS WHERE POSSIBLE.
2. FOR GROUNDING CONDUCTORS RUN EXPOSED, SUPPORT CONDUCTORS 36" ON CENTERS AND WITHIN 12" OF GROUND CONNECTIONS.
3. PROVIDE WALL FASTENER IN ACCORDANCE WITH THE WALL TYPE SEE "SIDE VIEW DETAILS" FOR REQUIREMENTS.
4. THIS GROUNDING DETAIL IS NOT FOR ORDNANCE GROUNDING SYSTEM.

APPROVED	DATE	APPR
FOR COMMANDER NAVFAC		
ACTIVITY	DATE	CHK
APPROVED BY LCDR ELIZABETH OLOKODE NAVFAC NLON FEAD DIRECTOR NEW LONDON, GROTON, CT	05/27/2025	KB
DES	JP	JP
PM/DM	SMS/CWJ	
BRANCH MANAGER	WRB	
CHIEF ENGINEER	JWJ	
FIRE PROTECTION	HPN	
DEPARTMENT OF THE NAVY	NAVAL FACILITIES ENGINEERING SYSTEMS COMMAND - MID-ATLANTIC	
NAVAL STATION - GROTON, CT	GROTON, CONNECTICUT	
NAVAL SUBMARINE BASE NEW LONDON	NAVAL WEAPONS MAGAZINE & ORDNANCE OPERATIONS FACILITY	
CLWS MAGAZINE		
ELECTRICAL DETAILS - SITE ADAPTED		
SCALE:	NONE	
PROJECT NO.:	1667770	
CONSTR. CONTR. NO.		
NAVFAC DRAWING NO.	12894304	
SHEET	61	OF 77
E-503S		

A

B

C

D



THIS DRAWING IS ISSUED WITH THE EXPRESSED AGREEMENT THAT THE DRAWING, AND INFORMATION THEREIN CONTAINED, ARE THE PROPERTY OF INDUSTRIAL DOOR CONTRACTORS INCORPORATED AND WILL NOT BE REPRODUCED OR COPIED IN WHOLE OR IN PART NOT USED FOR THE FABRICATION OR CONSTRUCTION OF MATERIALS EXCEPT UPON THE WRITTEN PERMISSION OF INDUSTRIAL DOOR CONTRACTORS INCORPORATED FIRST OBTAINED AND SPECIFIC AS TO USE.

ORIGINAL STANDARD DRAWING IS NAVFAC DRAWING NUMBER 12905863 SHT 44 OF 51

1. THE RELAY MUST BE INTERLOCKED TO MECHANICAL DOOR LATCH. RELAY MUST OPEN WHEN MECHANICAL DOOR IS UNLOCKED. DOOR POWER DISCONNECTED AND RELEASE THE DOOR CONTROL SYSTEM. THE KEY OVERRIDE SWITCH MUST CONTROL WHEN DOOR POWER DISCONNECTED.
2. THE RELAY MUST BE INTERLOCKED WITH ILD LOCKING SYSTEM SO THAT DOOR POWER WILL BE DISCONNECTED WHEN ILD IS IN 'CLOSE' POSITION OR IN 'LOCKING' POSITION. CONTRACTOR MUST COORDINATE WITH LOCAL AHJ FOR ADDITIONAL REQUIREMENT ON ILD SYSTEM CONNECTION. REFER TO KEYED NOTE 2/7101BS FOR ADDITIONAL INFORMATION.

NAVAL FACILITIES ENGINEERING SYSTEMS COMMAND - MID-ATLANTIC
MID-ATLANTIC
NAVAL SUBMARINE BASE NEW LONDON
GROTON, CONNECTICUT
NAVAL STATION - NORFOLK, VA
P-1102 WEAPONS MAGAZINE & ORDNANCE OPERATIONS FACILITY
CLWS MAGAZINE
ELECTRICAL DETAILS - SITE ADAPTED

FILE NAME: C:\pwworkspace\1381\1381-E-506S.dwg LAYOUT NAME: E-506 - ELECTRICAL DETAILS PLOTTED: Thursday, June 12, 2025 - 8:57am USER: PHILLIH

FDZ1628

E-506S.dwg

A

B



C

D

B1

DOOR EXTERIOR PLATE ELEVATION

SCALE: 1" = 1'-0"

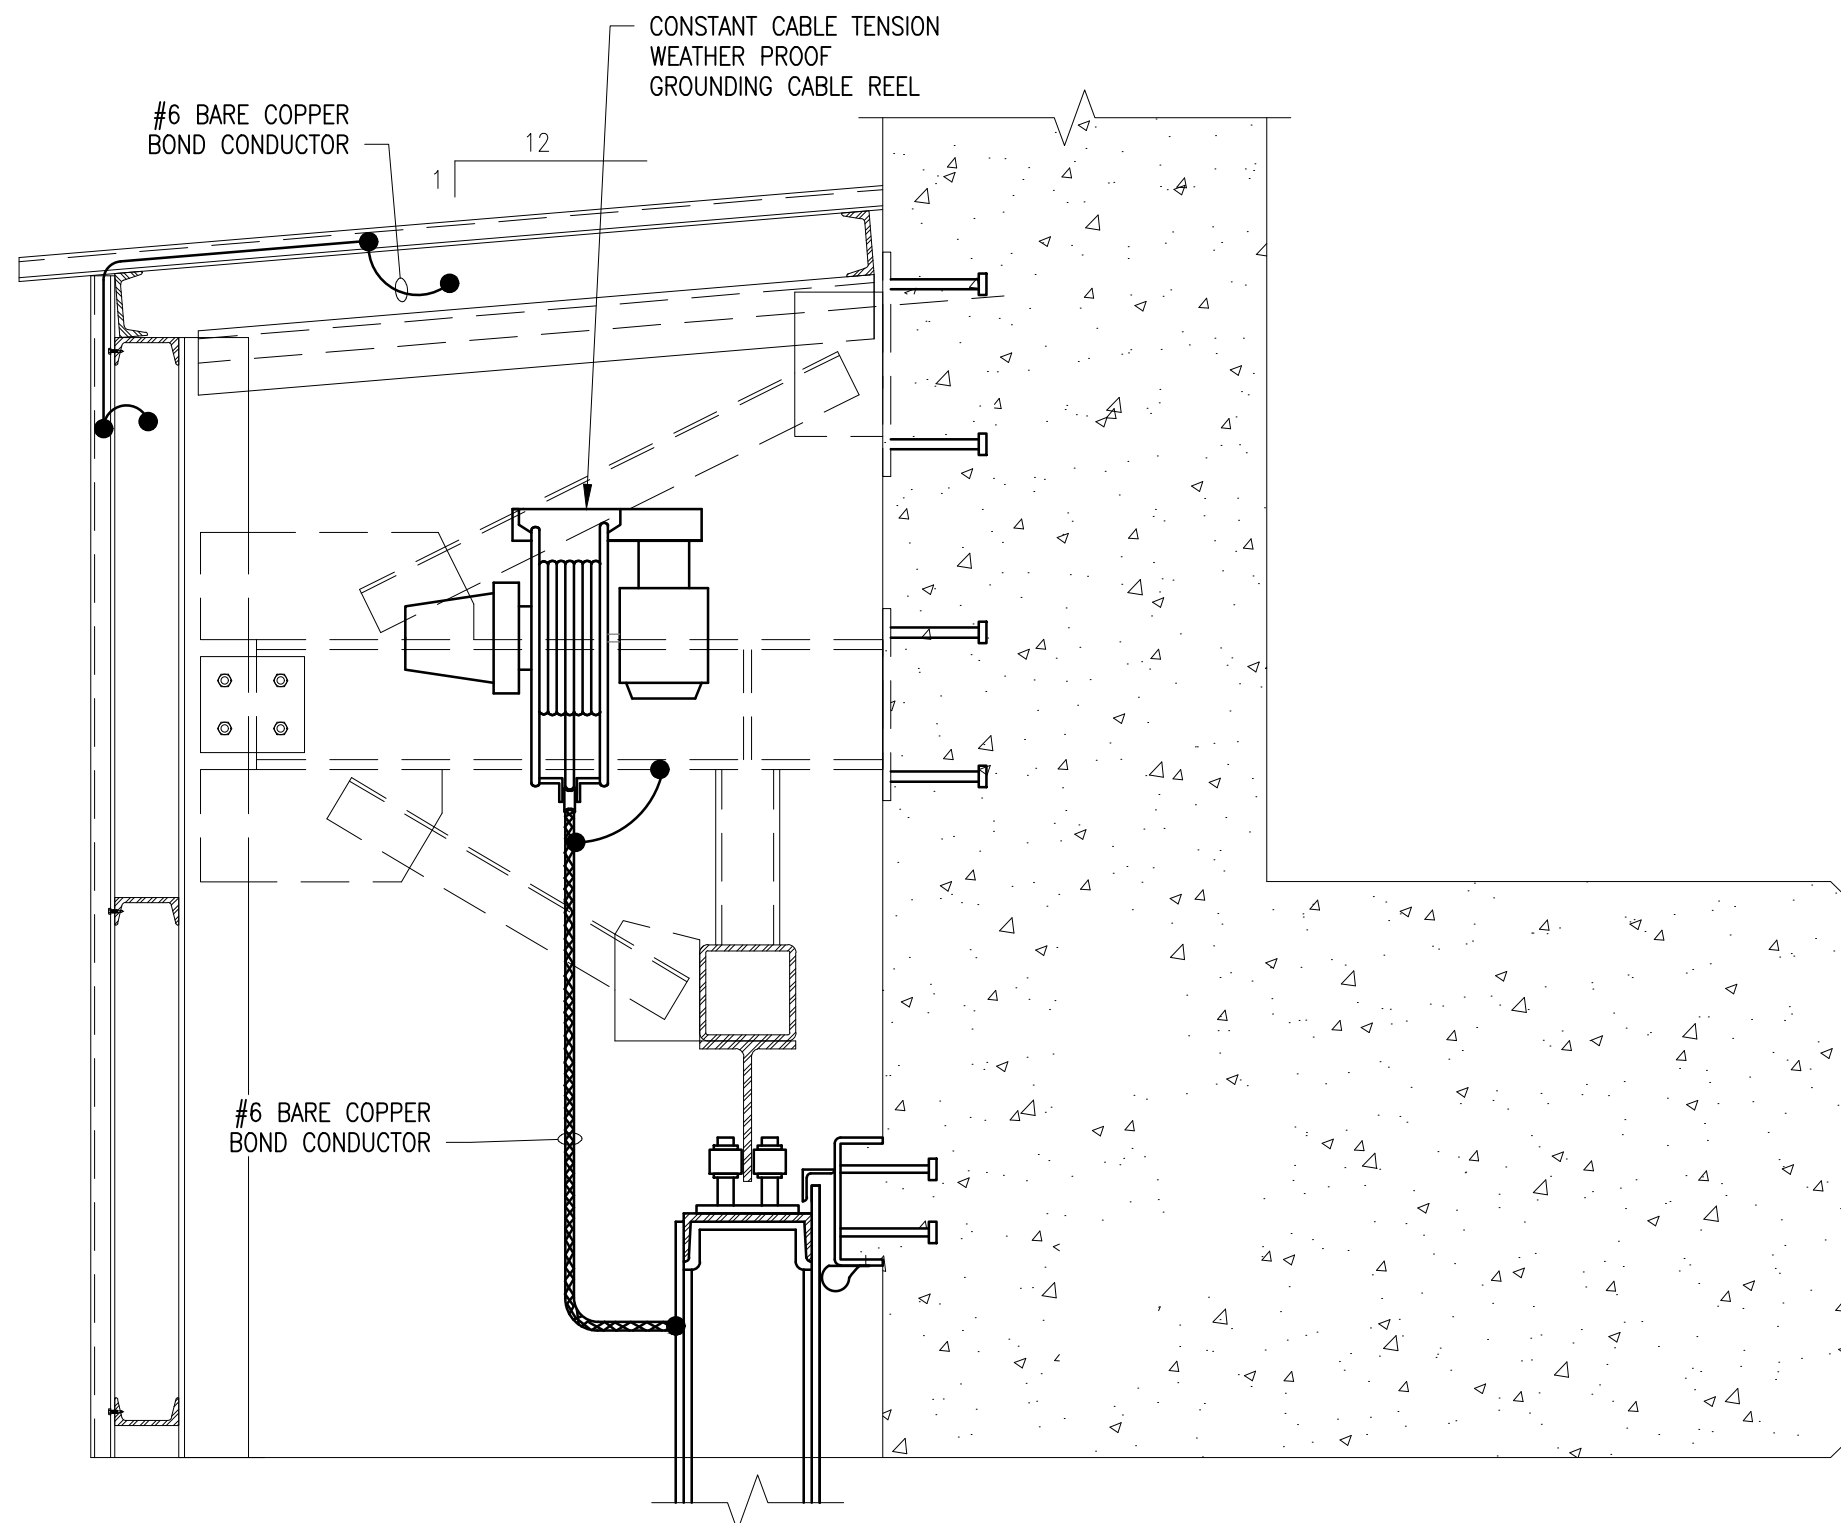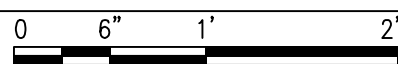

A2



DOOR DETAIL - GROUNDING

SCALE: NO SCALE

A4

DOOR DETAIL - POWER

SCALE: NO SCALE

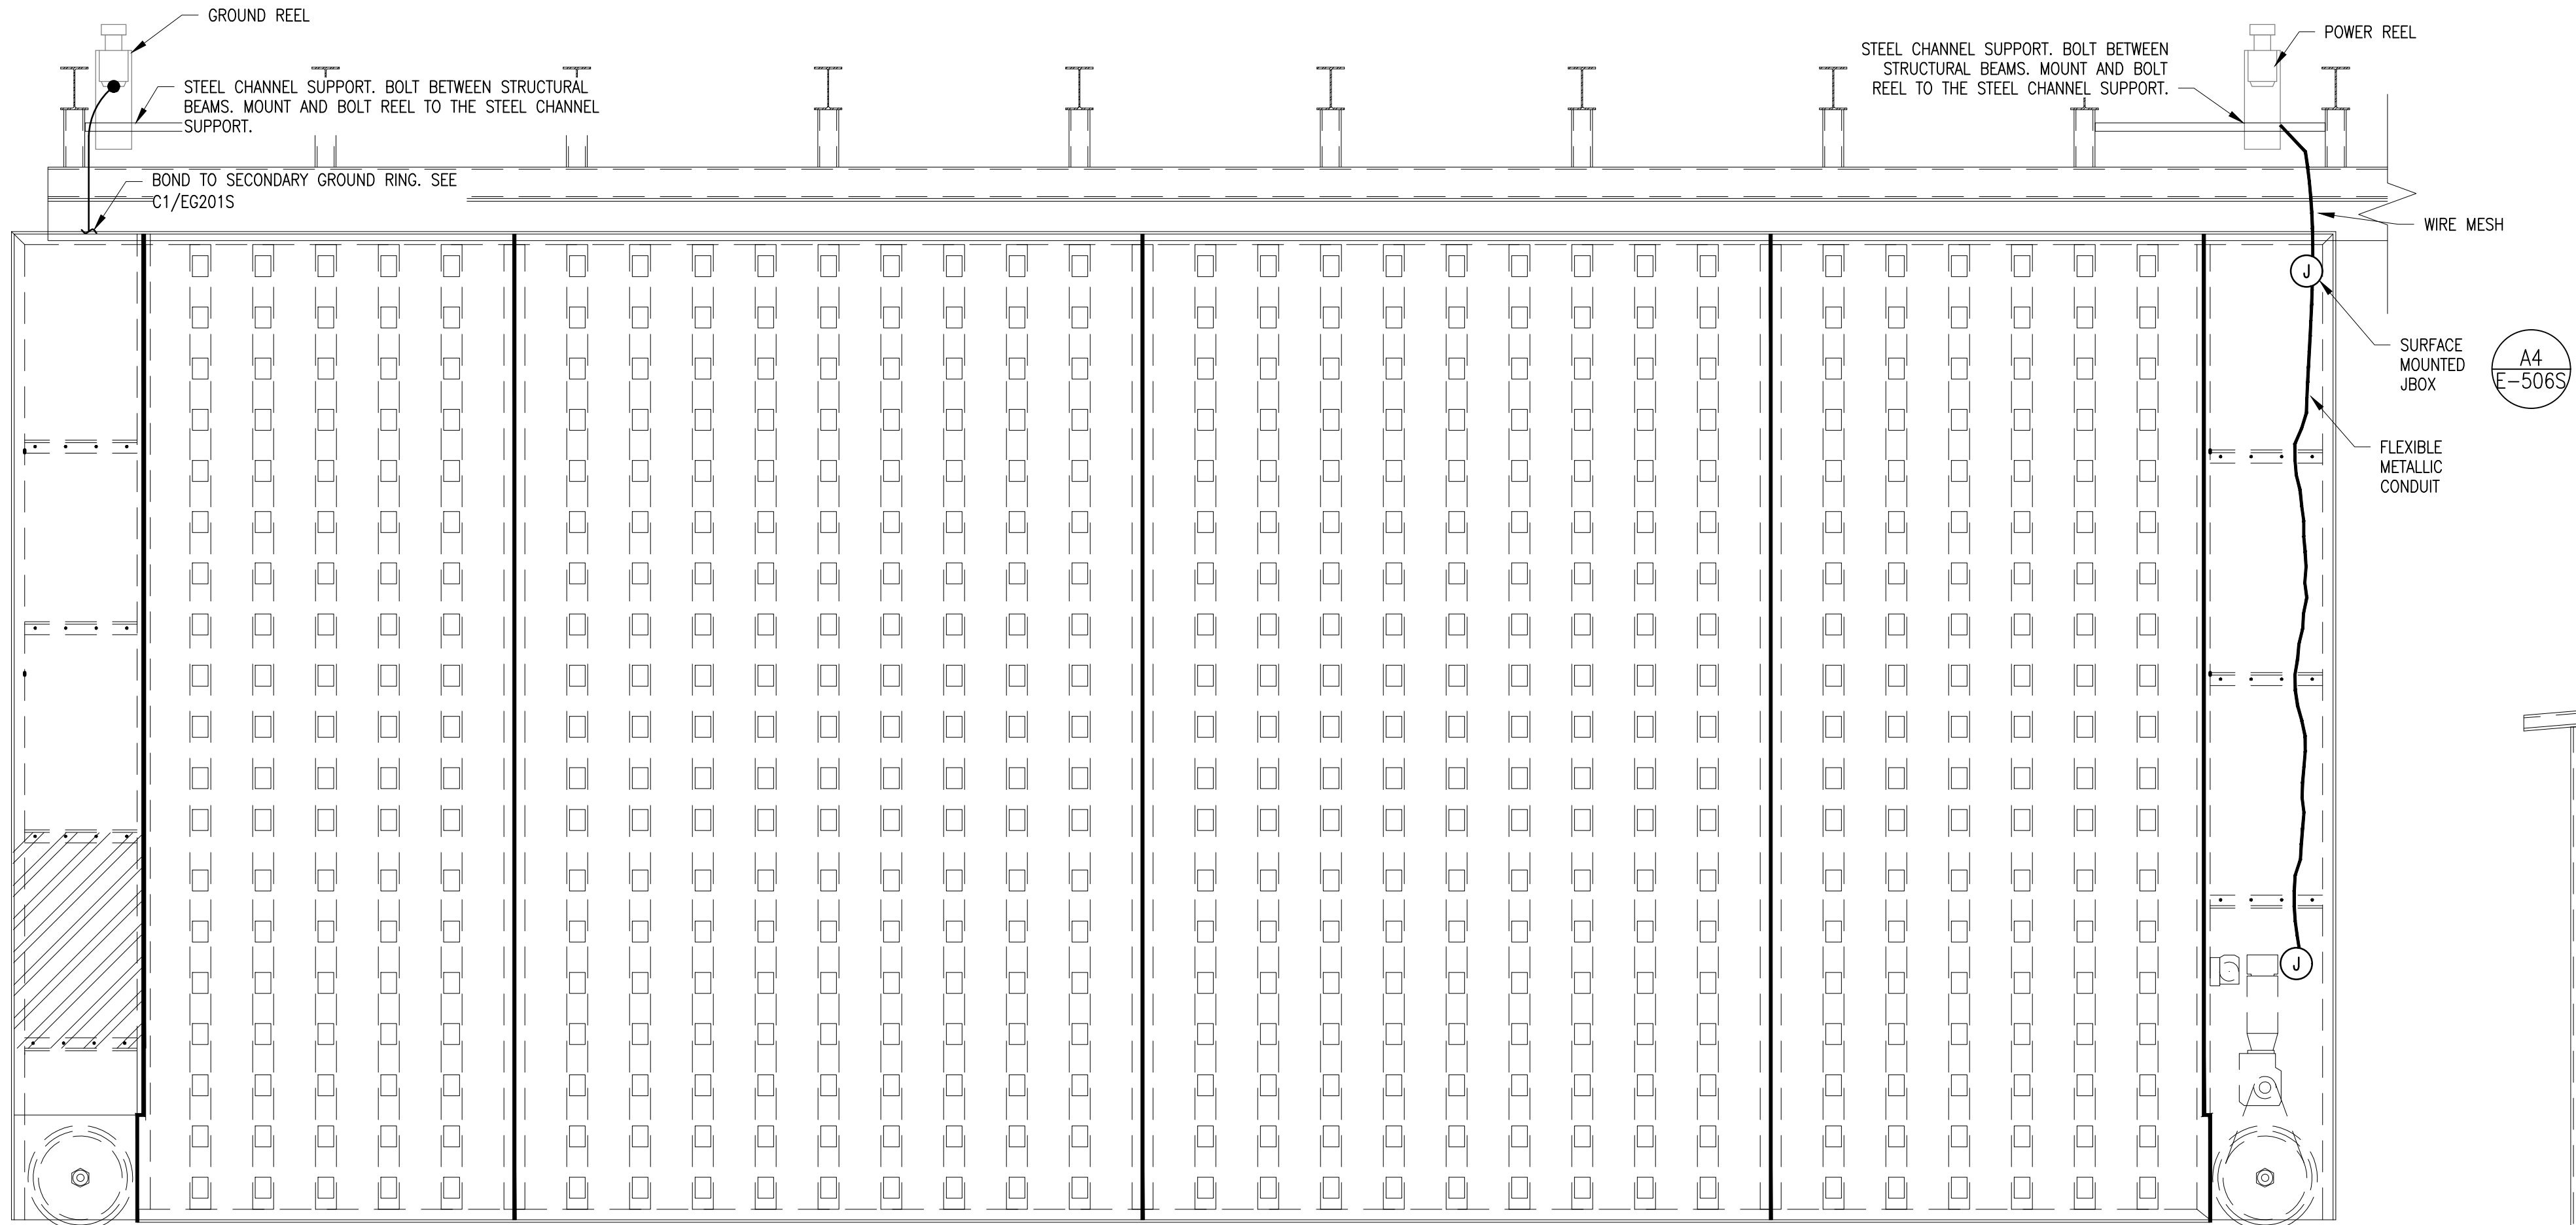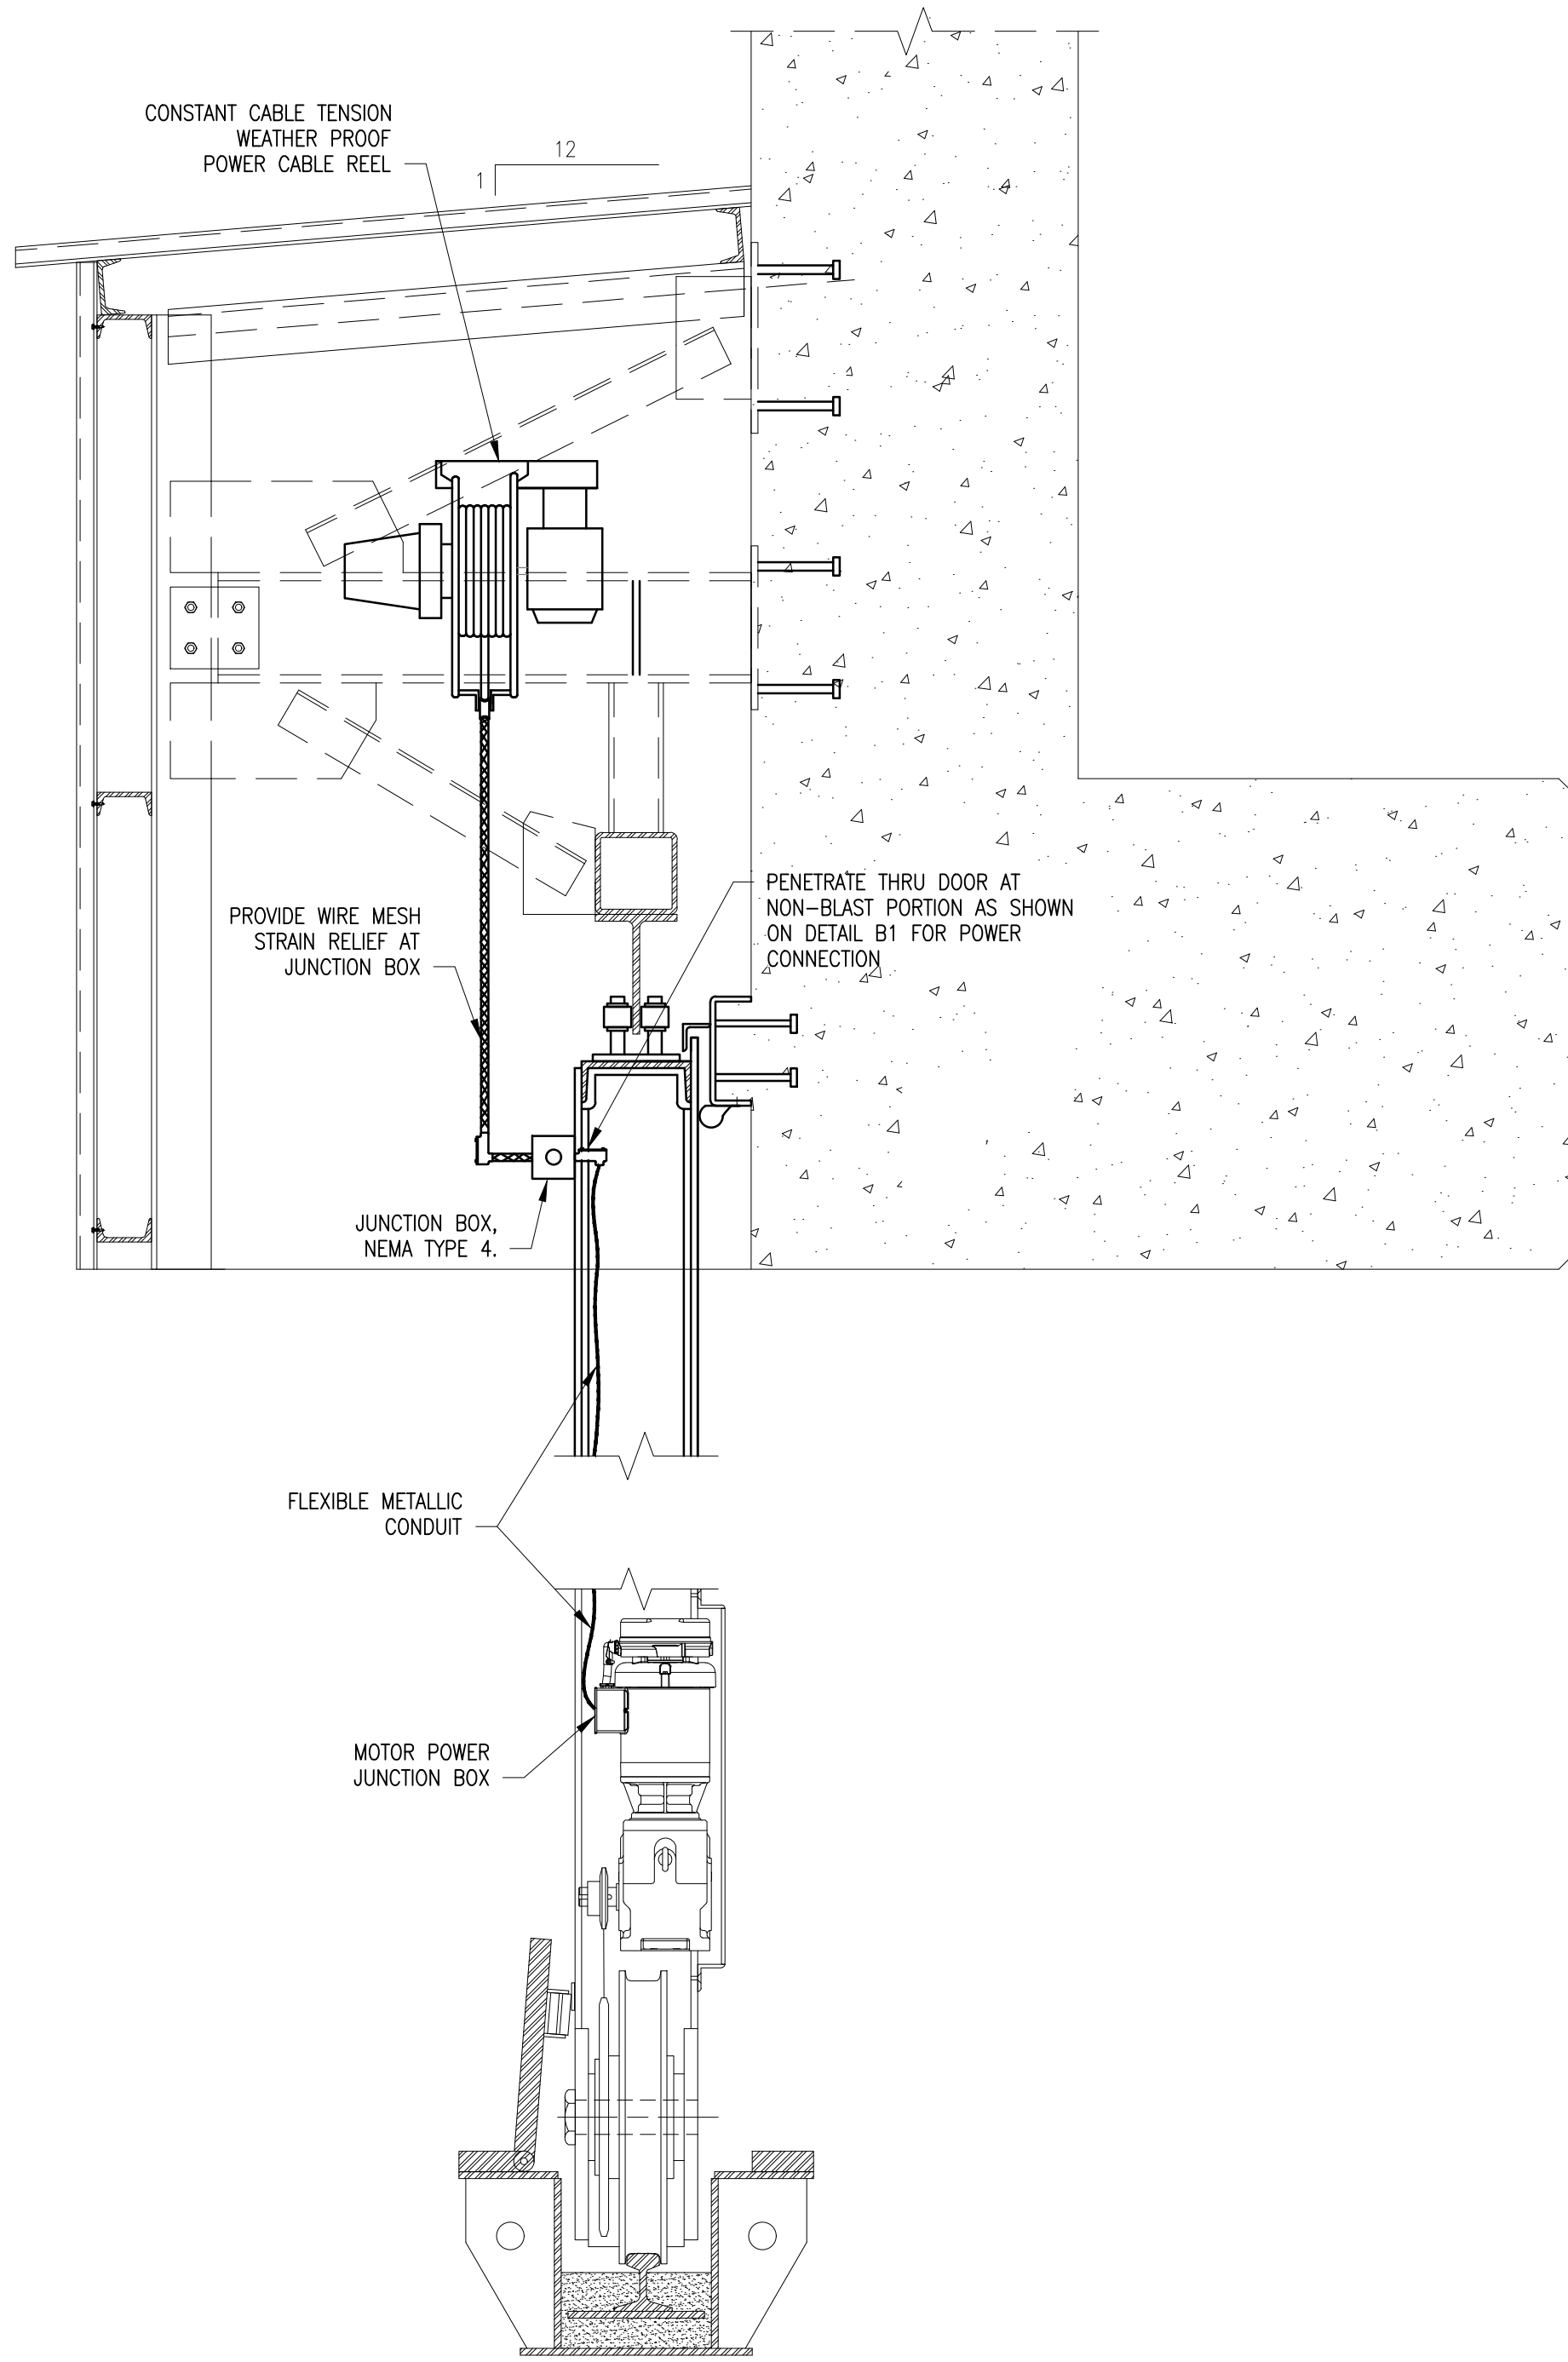

1

2

3

4

5

APPROVED
FOR COMMANDER NAVFAC

ACTIVITY
APPROVED BY LCDR ELIZABETH
CLOKODE NAVFAC NLON FEAD
DIRECTOR NEW LONDON, GROTON, CT

SATISFACTORY TO DATE 06/27/2025

DES JPI DRW JPI CHK KB

PMIDM SMS/CWU

BRANCH MANAGER WRB

CHIEF ENGINEER JWI

FIRE PROTECTION HPN

DEPARTMENT OF THE NAVY

NAVAL FACILITIES ENGINEERING SYSTEMS COMMAND

NAVAL FACILITIES ENGINEERING SYSTEMS COMMAND - MID-ATLANTIC

NAVAL STATION - GROTON, CT

NAVAL SUBMARINE BASE NEW LONDON

GROTON, CONNECTICUT

P-1102 WEAPONS MAGAZINE & ORDNANCE OPERATIONS FACILITY

CLWS MAGAZINE

ELECTRICAL DETAILS - SITE ADAPTED

SCALE: AS SHOWN

PROJECT NO.: 1667770

CONSTR. CONTR. NO.

NAVFAC DRAWING NO. 12894307

SHEET 64 OF 77

E-506S

COMMONWEALTH OF VIRGINIA

KELLEY BOURASSA

Lic. No. 0402061759

6/23/2025

PROFESSIONAL ENGINEER

SEAL

NAVAFAC

DATE

SYN

DESCRIPTION

APPR

FILE NAME: C:\pwworkspace\den003\jgs_phillip\1711351\1711351-E-601S.dwg LAYOUT NAME: E-601S - ELECTRICAL ONE-LINE PLOTTED: Thursday, June 12, 2025 - 8:57am USER: PHILLIP

D

C

B

A

FDZ1628


1

2

3

4

5

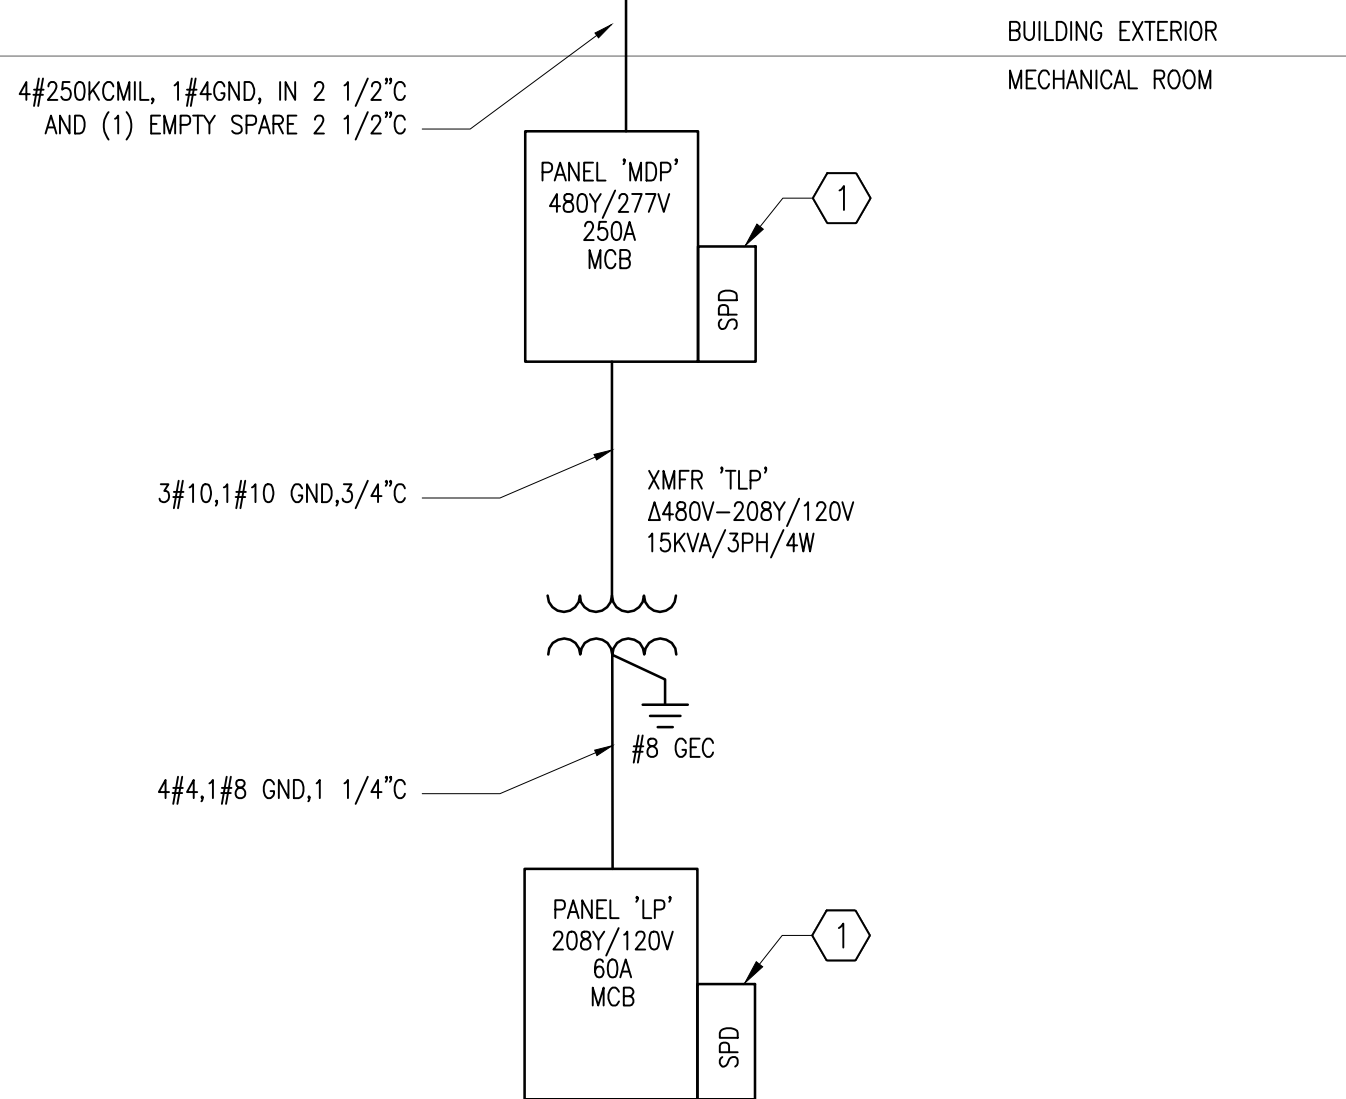

PANELBOARD "MDP" SCHEDULE	
NAME: MDP		ACCESSORY LUGS: NONE				VOLTAGE: 480Y/277				3-PHASE, 4-WIRE + G.				BUS AMPS: 250	
LOCATION: Mechanical Room		MOUNTING: Surface				NEUTRAL BUS: 100% RATED				GROUND BUS: EQUIPMENT ONLY				MAIN AMPS: 250	
		FED FROM: MDP								AIC: 10000				MCB	
NOTE	LOAD	CIRCUIT BREAKER			LOADS (VA)			CXT	LOADS (VA)			CIRCUIT BREAKER			NOTE	LOAD	
		FRM.	TRIP	POLE	A	B	C		A	B	C	FRM.	TRIP	POLE	
EQN	PWR - BLAST DOOR (2 HP)	100	20	3	942			1	2	16627			100	100	3	EQN	PWR - BRIDGE CRANE (25 TON)	
EQN						942		3	4		16627					EQN	
EQN							942	5	6			16627				EQN	
LTG	LTG - MAIN MAGAZINE	100	20	1	1044			7	8	17404			100	90	3	EQC	AHU#1	
LTG	LTG - MAIN MAGAZINE	100	20	1		1044		9	10		17404					EQC	
LTG	LTG - MAIN MAGAZINE	100	20	1			1044	11	12			17404				EQC	
LTG	LTG - MECH ROOM	100	20	1	300			13	14	3436			100	20	3	EQN	FORKLIFT BATTERY CHARGER	
LTG	LTG - EXTERIOR (TYPE C)	100	20	1		162		15	16		3436					EQN	
LTG	LTG - EXTERIOR (TYPE D)	100	20	1			204	17	18			3436				EQN	
LTG	LTG - LIGHTING CONTACTOR COIL	100	20	1	180			19	20	0			100	90	3	EQC	AHU#2 (REDUNDANT)	
EQN	UH-1	100	15	3		1666		21	22	0		0				EQC	
EQN							1666	23	24			0				EQC	
EQN						1666		25	26	1330			100	15	3	EQC	CU#1	
EQN	DOOR TRENCH SNOW MELT	100	20	1		3500		27	28		1330					EQC	
EQN	DRAIN PIPE HEAT TRACE	100	20	1			260	29	30			1330				EQC	
EQN	DRAIN PIPE HEAT TRACE	100	20	1	260			31	32	0			100	15	3	EQC	CU#2 (REDUNDANT)	
EQN	DRAIN PIPE HEAT TRACE	100	20	1		260		33	34		0					EQC	
EQN	DRAIN PIPE HEAT TRACE	100	20	1			260	35	36			0				EQC	
SUB	PANEL LP	100	30	3	2153			37	38				100	20	1	SPARE	SPARE	
SUB	THROUGH 15KVA XMFR					2693		39	40				100	20	1	SPARE	SPARE	
SUB							3036	41	42				100	20	1	SPARE	SPARE	
EQN	DRAIN PIPE HEAT TRACE	100	20	1	260			43	44				100	20	1	SPARE	SPARE	
EQN	DRAIN PIPE HEAT TRACE	100	20	1		260		45	46				100	20	1	SPARE	SPARE	
EQN	DRAIN PIPE HEAT TRACE	100	20	1			260	47	48				100	20	1	SPARE	SPARE	
EQN	DRAIN PIPE HEAT TRACE	100	20	1	260			49	50	0			100	30	3	REC	SPD	
SPARE	SPARE	100	20	1				51	52		0					REC	
SPARE	SPARE	100	20	1				53	54			0				REC	
SCHEDULE NOTES:		1 UON, PROVIDE 2#12 + 1#12G IN 3/4" FOR ALL 20A/1P BREAKERS.				7065				10527				7672				38797				38797				38797	
										CONNECTED LOAD (kVA)								DEMAND LOAD* (kVA)	
						PHASE A				45.9				L&A				0.0				LTG				4.0				EQC				58.3				L&A				0.0				LTG				4.0				EQC				49.6	
						PHASE B				49.3				DRY				0.0				REC				0.4				EQN				79.0				DRY				0.0				REC				0.4				EQN				67.1	
						PHASE C				46.5				RGE				0.0				KEQ				0.0				SPARE				35.4				RGE				0.0				KEQ				0.0				SPARE				26.6	

D

C

B

A

E-602S.dwg

FDZE1628

LIGHTING FIXTURE SCHEDULE

LIGHTING FIXTURE SCHEDULE								
MARK	DESCRIPTION	MOUNTING TYPE/HEIGHT (RE: E101BS)	LAMP TYPE	INPUT VA	COLOR TEMPERATURE	CRI	VOLTAGE	LUMINAIRE PLATE NUMBER
A	LED ARCHWAY PASSAGE FROSTED POLYCARBONATE ENCLOSURE 3500K 80 CRI 15000LM	STEM	LED	115 VA	3500 K	80	277 V	NL-11
B	LED ARCHWAY PASSAGE FROSTED POLYCARBONATE ENCLOSURE 3500K 80 CRI 6000LM	STEM/SURFACE	LED	50 VA	3500 K	80	277 V	NL-11
C	LED SINGLE-PIECE DIE-CAST ALUMINUM HOUSING 3500LM	WALL	LED	39 VA	4000 K	70	277 V	XL-17
D	LED DIE-CAST ALUMINUM HOUSING 12000LM	WALL	LED	102 VA	4000 K	70	277 V	XL-21
E	LED SINGLE-PIECE DIE-CAST ALUMINUM HOUSING 1500LM	WALL	LED	13 VA	4000 K	70	277 V	XL-17




LUMINAIRE REQUIREMENTS:

1. HOUSING – FIBERGLASS OR FIBERGLASS-REINFORCED POLYESTER OUTER HOUSING, WITH ALUMINUM COMPONENT TRAY AND HEAT SINK. OPTIONAL LENGTHS OF 4FT OR 8FT.
2. LENS – IMPACT-RESISTANT ACRYLIC OR OPTIONAL POLYCARBONATE, WITH CONTINUOUS CLOSED-CELL POLYURETHANE GASKET, SECURED WITH STAINLESS STEEL OR POLYCARBONATE LATCHES.
3. LIGHT SOURCE – SOLID STATE LEDS WITH MINIMUM 50K HOURS RATED LIFE AT L70, 3500K CCT UON, MINIMUM 80 CRI, MAXIMUM 4-STEP MACDAM ELLIPSE BINNING TOLERANCE FOR COLOR CONSISTENCY, AND MINIMUM EFFICACY OF 100 LUMENS/WATT. INITIAL LUMEN OUTPUT AS INDICATED IN LUMINAIRE SCHEDULE.
4. DRIVER – REPLACEABLE, INTEGRAL, HIGH-EFFICIENCY DRIVER WITH MINIMUM 0.9 PF, OPERATING VOLTAGE OF 120-277V, THERMAL MANAGEMENT, < 20% TOTAL HARMONIC DISTORTION. ON-OFF CONTROL, STEP-DIMMABLE OR FULLY DIMMABLE AS INDICATED.
5. CERTIFICATION – UL 598, WET LOCATION (IP65, IP66, IP67), DLC QUALIFIED, AND ROHS COMPLIANT. COMPLIES WITH LM79, LM80 AND TM21 TESTING STANDARDS. UL 924 WHEN EQUIPPED WITH EMERGENCY BATTERY BACK-UP.
6. MOUNTING – SURFACE-MOUNTED OR SUSPENDED FROM CEILING.
7. OPTIONS – EMERGENCY BACK-UP.
8. THIS SPECIFICATION IS A NON-PROPRIETARY GRAPHIC REPRESENTATION OF A LUMINAIRE THAT MAY MEET THE SPECIFICATION REQUIREMENTS. IT IS NOT INTENDED TO INDICATE A CERTAIN MANUFACTURER OR PREFERENCE.

LED ENCLOSED AND GASKETED

REVISED:	APRIL 2016	LIGHTING PLATE:	NL-11
----------	------------	-----------------	-------

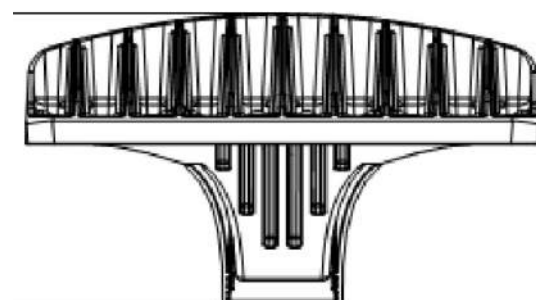

LUMINAIRE REQUIREMENTS:

1. HOUSING – DIE-CAST OR EXTRUDED ALUMINUM WITH INTEGRAL PASSIVE COOLING MECHANISM. HEAT SINK MUST BE INCORPORATED DIRECTLY INTO HOUSING OR DRIVER COMPARTMENT TO ENSURE MAXIMUM HEAT TRANSFER AND DISSIPATION.
2. FINISH – MULTI-STAGE PRE-TREATMENT, FINISHED WITH BAKED-ON POLYESTER POWDER COAT. FINISH MUST PASS 2500 HOUR SALT SPRAY TEST PER ASTM B117. STANDARD FINISH IS DARK BRONZE, WITH OTHER CUSTOM COLORS AVAILABLE.
3. POWER SUPPLY/LED DRIVER – CLASS 1 DRIVER MUST OPERATE AT 120/277 VOLTS, 50/60 HZ, WITH OTHER VOLTAGES OPTIONAL; POWER FACTOR GREATER THAN 0.9 AND THD LESS THAN 20% AT FULL LOAD. MINIMUM EFFICACY MUST BE 60 LM/W AT MAXIMUM 600mA OPERATING CURRENT.
4. LED OPTICAL ASSEMBLY – PRECISION MOLDED ACRYLIC LENS PROVIDED FOR MULTIPLE HIGH-POWERED LEADS PRODUCING NEMA TYPE III DISTRIBUTION OR AS OTHERWISE INDICATED. BUG UPLIGHT RATING OF U0, WITH GLARE RATING AS DETERMINED BY LIGHTING ZONE INSTALLED. MINIMUM COLOR RENDERING INDEX (CRI) MUST BE 70 FOR CORRELATED COLOR TEMPERATURE (CCT) OF 4000-4500 DEGREES K.
5. CERTIFICATION – UL AND/OR ETL LISTED FOR DAMP OR WET LOCATIONS AS INDICATED, AND RoHS COMPLIANT.
6. OPTIONS – VARIOUS LUMEN OUTPUT RATING AS INDICATED, AND 0-10 VOLT DIMMING DRIVER, MOUNTING BRACKET TYPE COMPATIBLE WITH BUILDING STRUCTURE.
7. OTHER – THE ABOVE SKETCH IS A NON-PROPRIETARY GRAPHIC REPRESENTATION OF A LUMINAIRE THAT MAY MEET THE SPECIFICATION REQUIREMENTS AND IS NOT INTENDED TO INDICATE A CERTAIN MANUFACTURER'S PREFERENCE. ALL DIMENSIONS ARE NOMINAL AND VARY PER MANUFACTURER. MANUFACTURER'S PREFERENCE. ALL DIMENSIONS ARE NOMINAL AND VARY PER MANUFACTURER.

LED WALL PACK

REVISED:	MARCH 2013	LUMINAIRE PLATE:	XL-17
----------	------------	------------------	-------



LUMINAIRE REQUIREMENTS:



1. HOUSING – DIE CAST ALUMINUM WITH INTEGRAL PASSIVE COOLING MECHANISM. HEAT SINK MUST BE INCORPORATED DIRECTLY INTO HOUSING TO ENSURE MAXIMUM HEAT TRANSFER AND DISSIPATION.
2. FINISH – MULTI-STAGE PRE-TREATMENT, FINISHED WITH BAKED-ON POLYESTER POWDER COAT. FINISH MUST PASS 2500 HOUR SALT SPRAY TEST PER ASTM B117. DARK BRONZE FINISH COLOR IS STANDARD.
3. POWER SUPPLY/LED DRIVER – CLASS 1 ELECTRONIC DRIVER MUST OPERATE AT 120/277 VOLTS, 50/60 HZ, WITH OTHER VOLTAGES OPTIONAL. POWER FACTOR MUST BE GREATER THAN 0.9 AND THE LESS THAN 20% AT FULL LOAD. MINIMUM EFFICACY MUST BE 60 LM/W AT MAXIMUM 600mA OPERATING CURRENT.
4. LED OPTICAL ASSEMBLY – MULTI-LED ARRAY OPTIMIZED FOR SPECIFIC DISTRIBUTION PATTERN AS INDICATED. MINIMUM COLOR RENDERING INDEX (CRI) OF 70 FOR CORRELATED COLOR TEMPERATURE OF 4000–4500 DEGREES K.
5. LENS – TEMPERED GLASS IN DIE-CAST ALUMINUM FRAME WITH SILICONE GASKET.
6. SURGE PROTECTION – 6 KV MINIMUM, COMPLIANT WITH ANSI C62.41.2.
7. CERTIFICATION – UL AND/OR ETL LISTED FOR WET LOCATIONS AND 2G VIBRATION STANDARD PER ANSI C136.32. OPTICAL ASSEMBLY MUST BE MINIMUM IP65 PER ANSI/IEC 60529.
8. OPTIONS – FINISH COLOR, OUTPUT DISTRIBUTION TYPE AND TRUNNION OR SLIPFITTER TYPE MOUNTING. MOUNTING BRACKET TYPE COMPATIBLE WITH BUILDING STRUCTURE.
9. OTHER – THE ABOVE SKETCH IS A NON-PROPRIETARY GRAPHIC REPRESENTATION OF A LUMINAIRE THAT MAY MEET THE SPECIFICATION REQUIREMENTS AND IS NOT INTENDED TO INDICATE A CERTAIN MANUFACTURER'S PREFERENCE. ALL DIMENSIONS ARE NOMINAL AND VARY PER MANUFACTURER.

LED FLOOD LUMINAIRE

REVISED:	MARCH 2013	LUMINAIRE PLATE:	XL-21
----------	------------	------------------	--------------

THESE DRAWINGS HAVE BEEN ADAPTED FROM APPROVED NAVFAC MUNITIONS STORAGE CONSTRUCTION DOCUMENTS, NAVFAC DRAWING NUMBERS 12905820 TO 12905870, APPROVED BY DDESB ON 25 JULY 2024. JACOBS DOR RESPONSIBILITY AND SEAL APPLICABILITY IS LIMITED TO THE SITE ADAPTATIONS AND MODIFICATIONS MADE TO THIS DRAWING.

ORIGINAL STANDARD DRAWING IS NAVFAC DRAWING NUMBER 12905866 SHT 47 OF 51

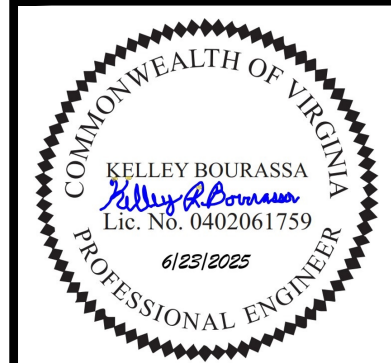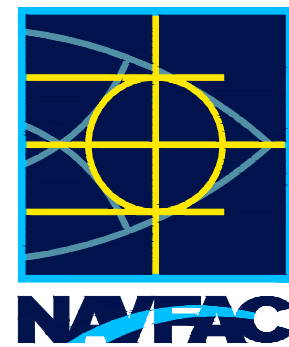[illegible]

Jacobs

1100 NORTH GLEBE ROAD
SUITE 500
ARLINGTON, VIRGINIA 22201
571.218.1000
FAX: 571.218.1600

APPROVED

James E. Donahue, RA



FOR COMMANDER NAVFAC

8/1/2005

ACTIVITY
APPROVED BY LCDR ELIZABETH
OLOKODE NAVFAC NLON FEAD
DIRECTOR NEW LONDON GROTON, CT

SATISFACTORY TO		DATE		05/27/2025	
DES	JP	DRW	JP	CHK	KB
PM/DM				SMS/CWJ	
BRANCH MANAGER				WRB	
CHIEF ENG/ARCH				JWJ	
FIRE PROTECTION				HPN	

NAVAL FACILITIES ENGINEERING SYSTEMS COMMAND ENGINEERING SYSTEMS COMMAND - MID-ATLANTIC NAVAL STATION - NORFOLK, VA	LONDON GROTON, CONNECTICUT	NAVIE & ORDNANCE OPERATIONS FACILITY CLWS MAGAZINE
SCHEDULES - SITE ADAPTED		

DEPARTMENT OF THE NAVY
NAVAL FACILITIES ENGINEERING
MID-ATLANTIC

NAVAL SUBMARINE BASE NEW LONDON
P-1102 WEAPONS MAGAZINE

ELECTRICAL SCHEMATIC

SCALE:	NONE	
EPROJECT NO.:	1667770	
CONSTR. CONTR. NO.		
NAVFAC DRAWING NO.	12894309	
SHEET	66	OF 77
E-602S		


D

C

B

A

FILE NAME: C:\pwworkspace\den003\jgs_phillip\A\1711381\1-E-801S.dwg LAYOUT NAME: E101B - ELECTRICAL FLOOR PLAN PLOTTED: Thursday, June 12, 2025 - 8:55am USER: PHILLIP

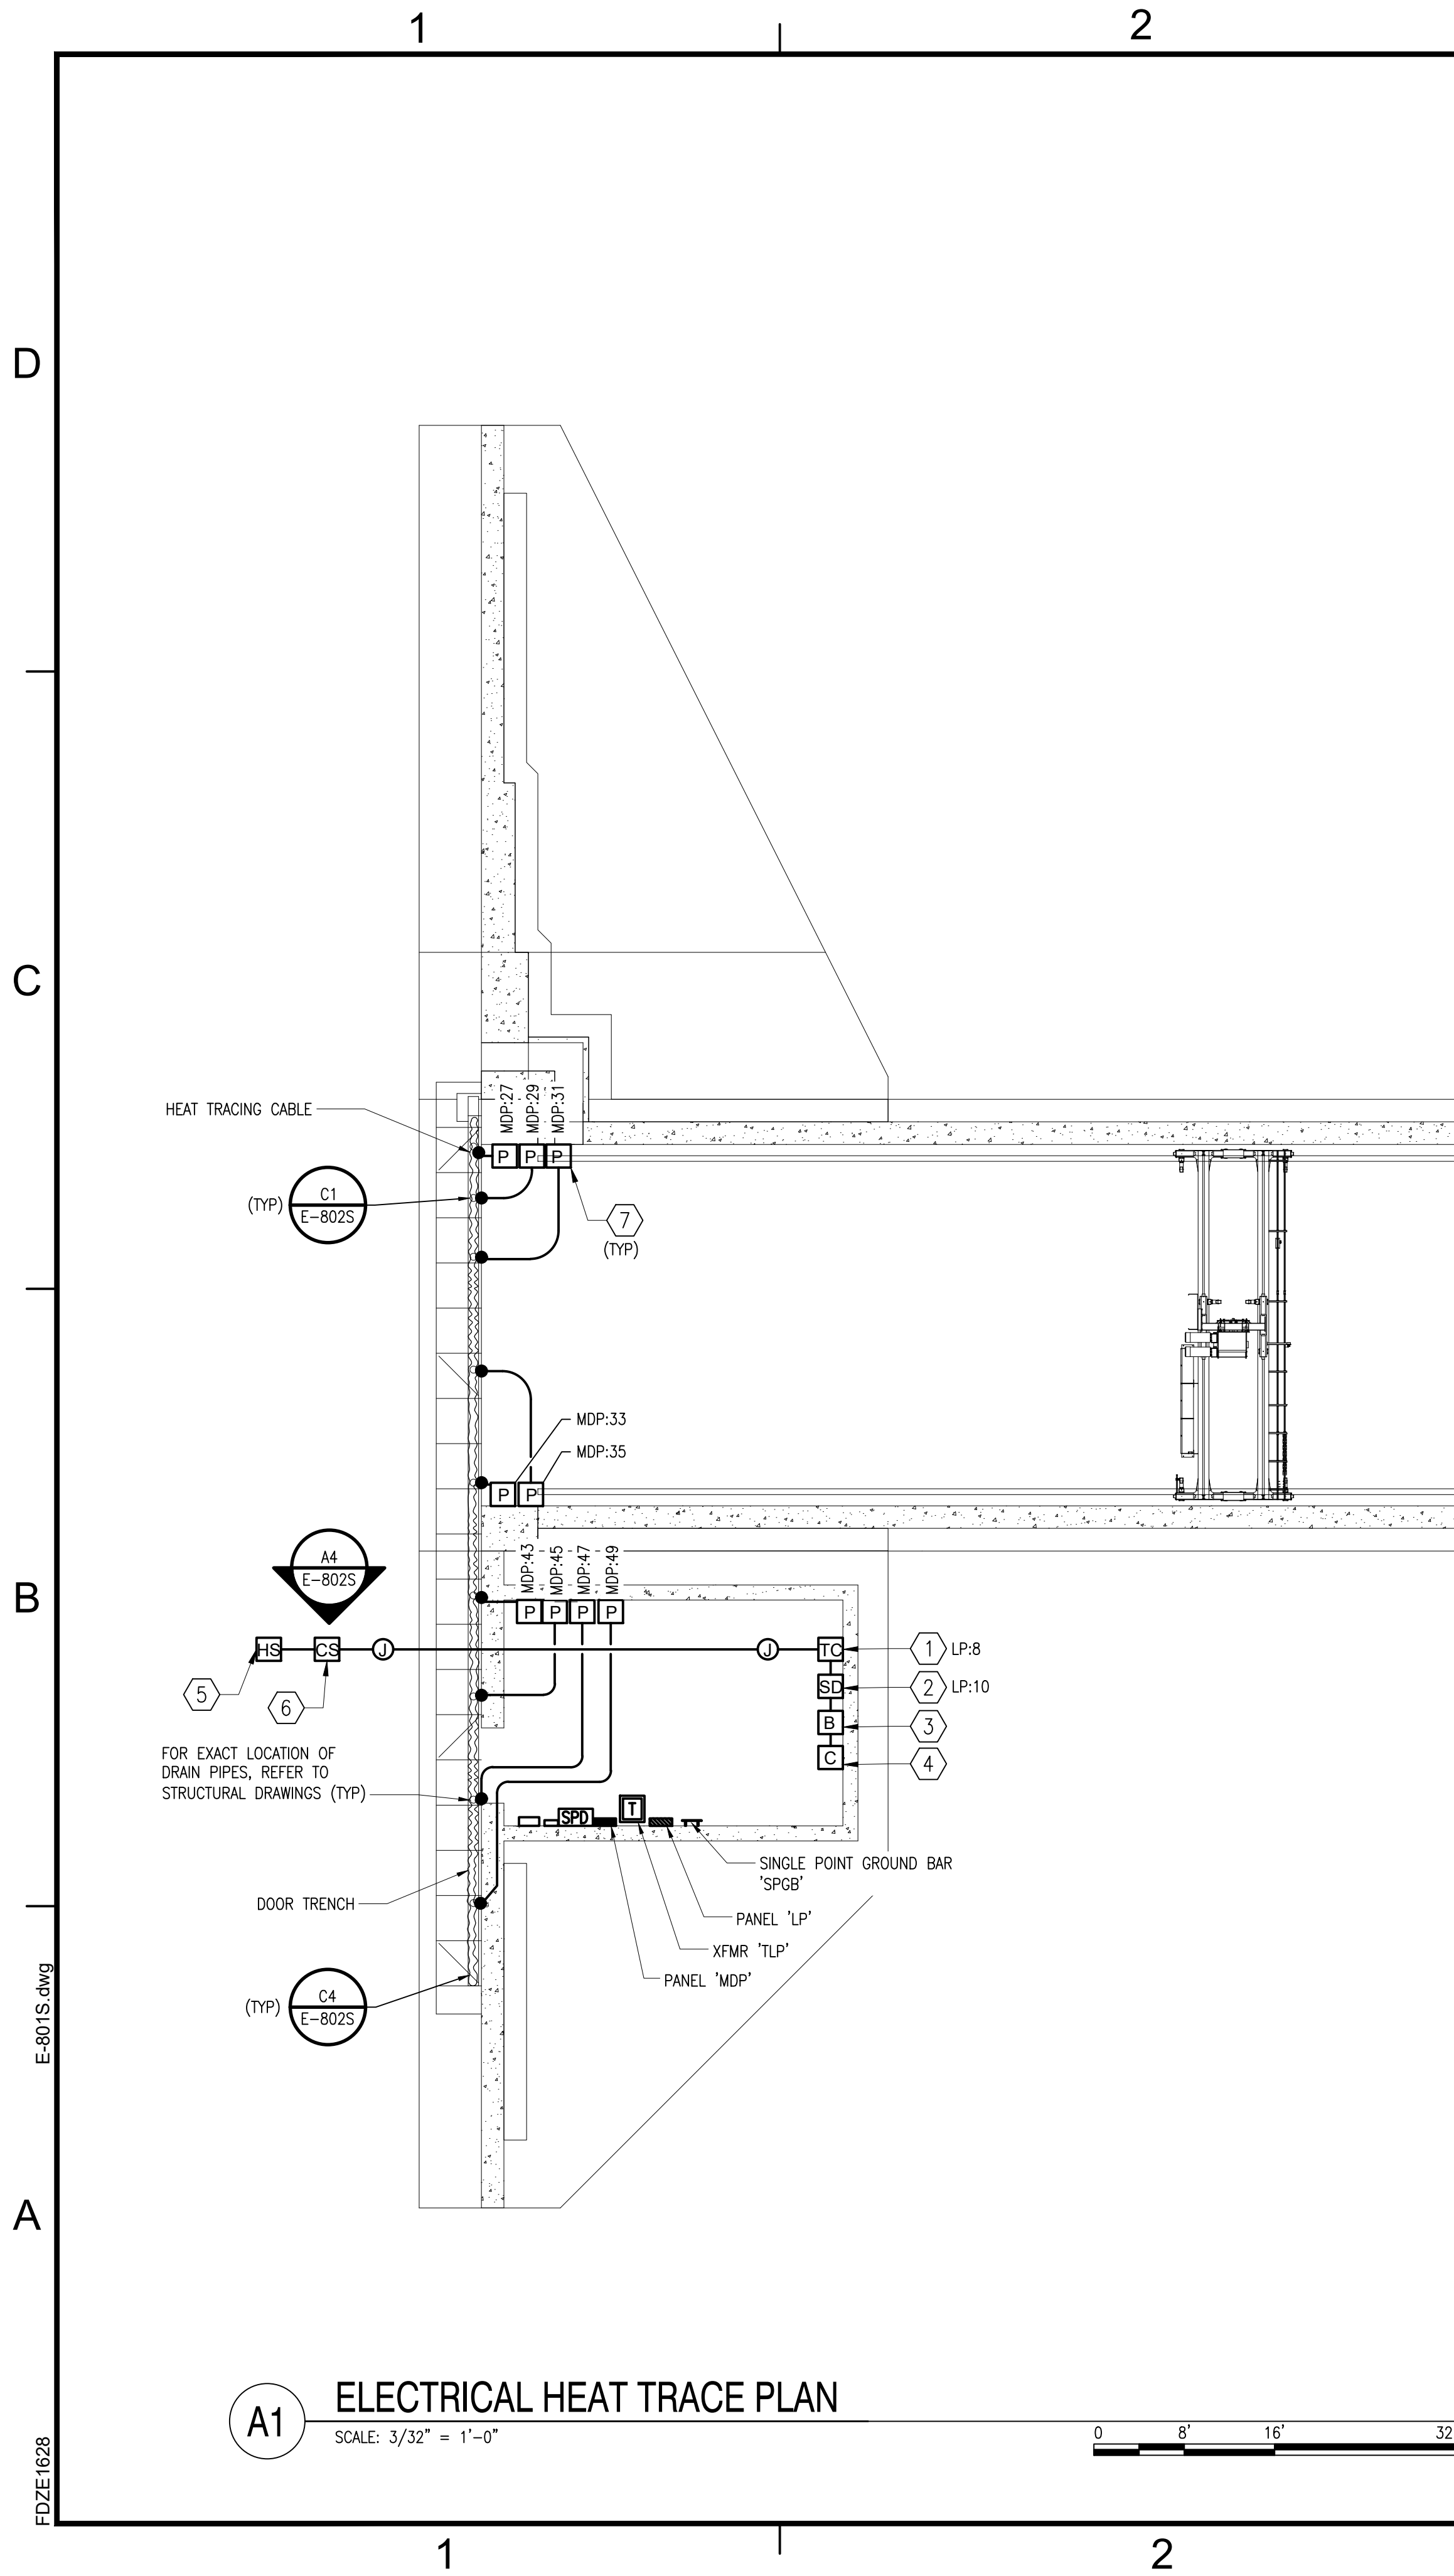

- ### SHEET NOTES
- COORDINATE WITH HEAT TRACE/SNOW MELT MANUFACTURER TO PROVIDE ALL MATERIALS, EQUIPMENT, POWER, AND CONTROLS WIRING FOR A FULLY FUNCTIONAL SYSTEM. SNOW MELT SYSTEM MUST BE CAPABLE OF SENSING TEMPERATURE AND DETECTING MOISTURE ON THE PAVEMENT.
 - HEAT TRACE LOADS FOR DRAIN PIPES ARE BASED ON 8W/LF. SNOWMELT LOAD FOR DOOR TRENCH IS BASED ON 50W/SF. REFER TO PANEL SCHEDULES FOR ADDITIONAL INFORMATION.
 - SNOW MELT AND HEAT TRACE SYSTEMS MUST HAVE 25 YEAR WARRANTY.
 - COORDINATE FINAL LOCATION OF ALL HEAT TRACE DEVICES WITH GOVERNMENT PRIOR TO INSTALLATION. LOCATIONS SHOWN ARE DIAGRAMMATIC FOR CIRCUITING PURPOSES ONLY. COORDINATE FINAL ROUTING OF HEAT TRACE CABLES FROM HEAT TRACE POWER BOX TO DOOR TRENCH AND EACH DRAIN PIPE.

- ### KEYED NOTES
- TEMPERATURE CONTROL PANEL.
 - AUTOMATIC SNOW DETECTOR CONTROL PANEL.
 - BYPASS SWITCH.
 - CONTACTOR.
 - HEAT SENSOR EMBEDDED IN PAVEMENT.
 - COLD SENSOR EMBEDDED IN PAVEMENT.
 - HEAT TRACING POWER BOX.

SYN	DESCRIPTION	DATE	APPR



Jacobs
1100 NORTH GLEBE ROAD
SUITE 500
ARLINGTON, VIRGINIA 22201
571.218.1000
FAX: 571.218.1600

APPROVED: [Signature]
FOR COMMANDER NAVFAC: [Signature]
ACTIVITY: APPROVED BY LCDR ELIZABETH OLOKODE NAVFAC NLON FEAD DIRECTOR NEW LONDON, GROTON, CT
SATISFACTORY TO: DATE: 06/27/2025
DES: JP | DRW: JP | CHK: KB
PMIDM: SMS/CWJ
BRANCH MANAGER: WRB
CHIEF ENGINEER: JWW
FIRE PROTECTION: HPN

DEPARTMENT OF THE NAVY
NAVAL FACILITIES ENGINEERING SYSTEMS COMMAND
NAVAL FACILITIES ENGINEERING SYSTEMS COMMAND - MID-ATLANTIC
NAVAL STATION - NORFOLK VA
NAVAL SUBMARINE BASE NEW LONDON
GROTON, CONNECTICUT
P-1102 WEAPONS MAGAZINE & ORDNANCE OPERATIONS FACILITY
CLWS MAGAZINE
ELECTRICAL HEAT TRACE PLAN

SCALE: AS SHOWN
PROJECT NO.: 1667770
CONSTR. CONTR. NO.
NAVFAC DRAWING NO.: 12894310
SHEET 67 OF 77
E-801S

FILE NAME: C:\pwr_work\dwg\003\jgs_phillip\A\0711381\1-E-802S.dwg LAYOUT NAME: E-802S - ELECTRICAL HEAT TRACE DETAILS PLOTTED: Thursday, June 12, 2025 - 8:54am USER: PHILLIP

FDZE1628


E-802S.dwg

A


B

C


D

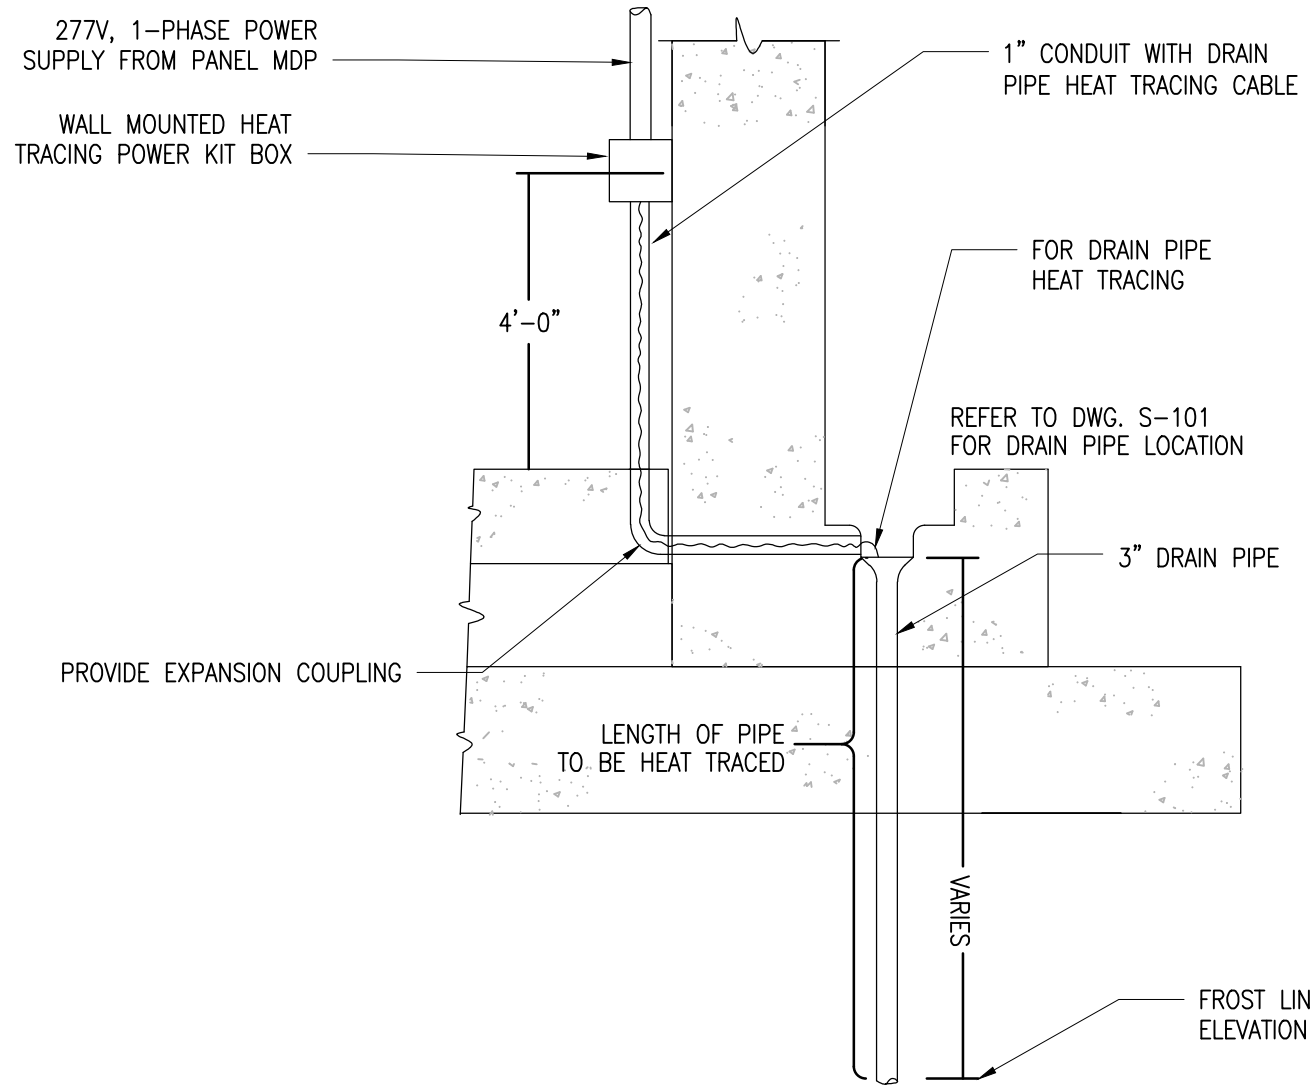


C1 DRAIN PIPE HEAT TRACING DETAIL
SCALE: NO SCALE

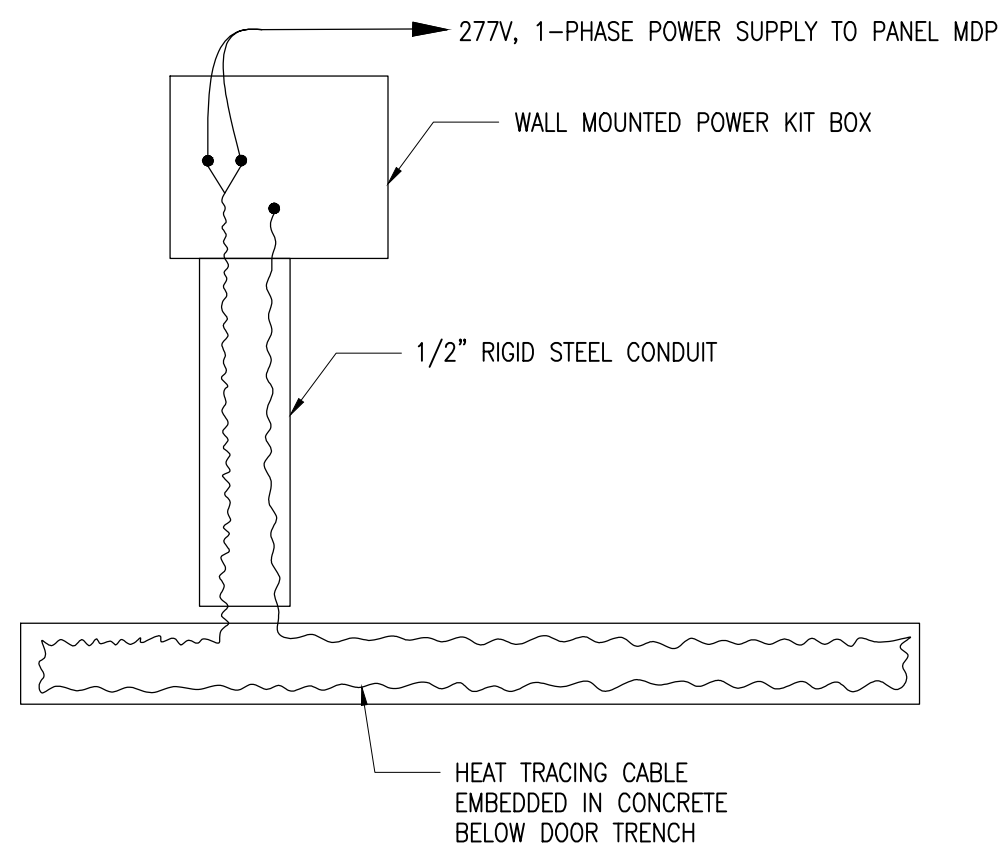

A1 TYPICAL DOOR TRENCH HEAT TRACING WIRING DETAIL
SCALE: NO SCALE

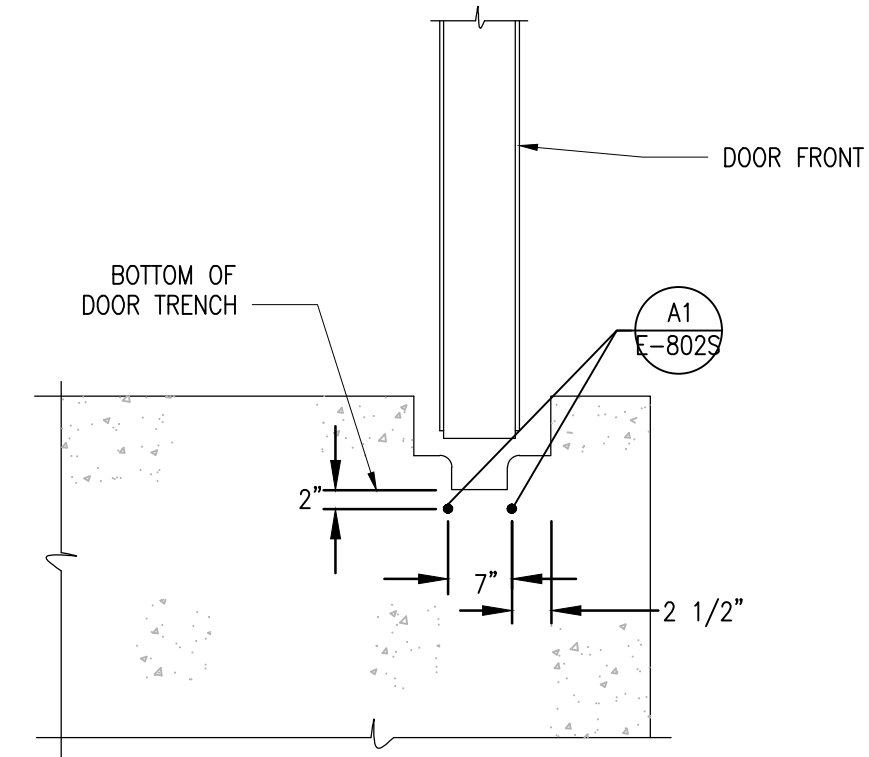


C4 HEAT TRACING CABLE DETAIL
SCALE: NO SCALE

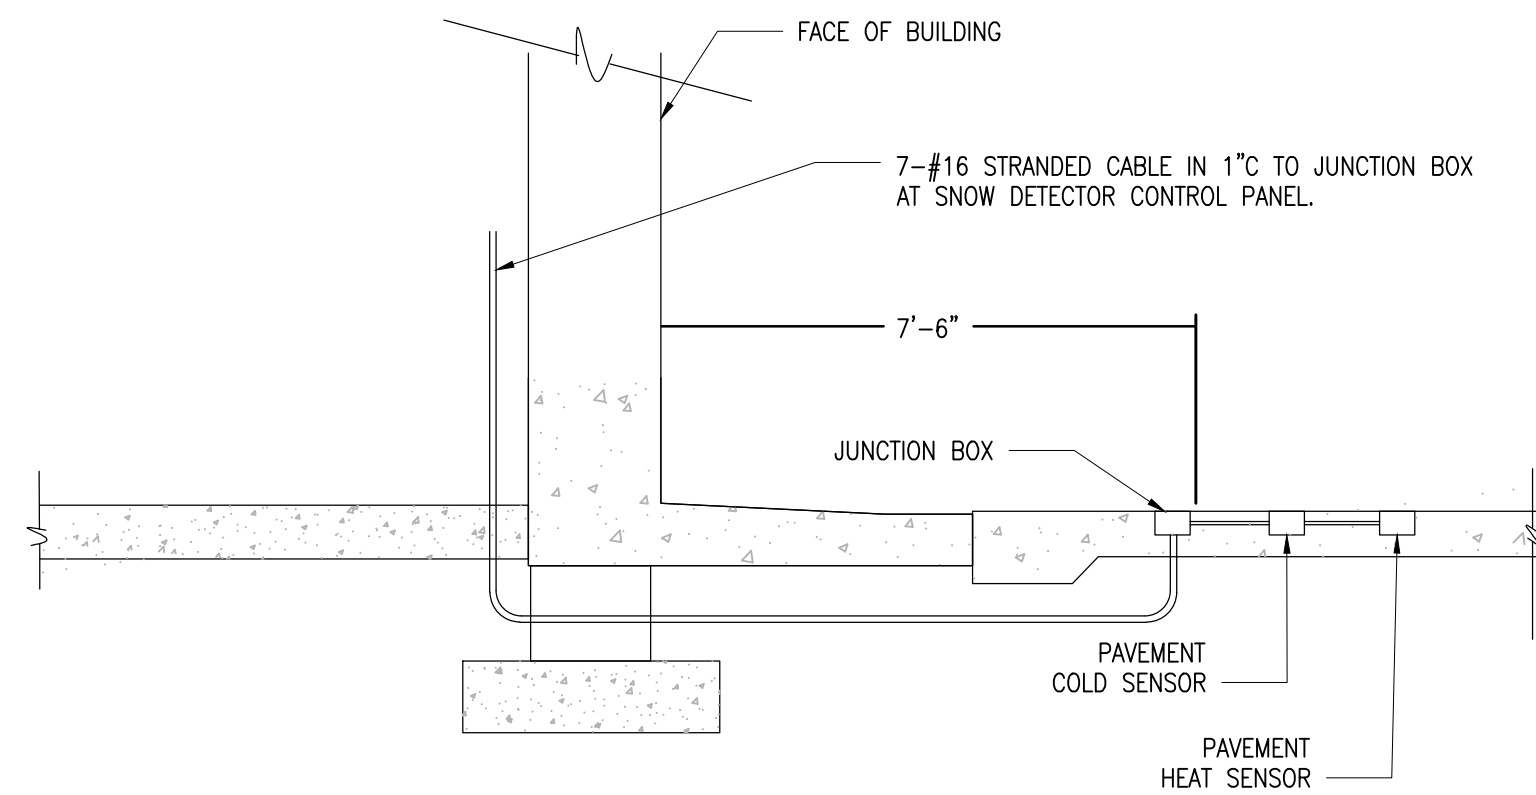

A4 SNOW DETECTOR LOCATION DETAIL
SCALE: NO SCALE

APPROVED	DATE	APPR
FOR COMMANDER NAVFAC		
ACTIVITY		
APPROVED BY LCDR ELIZABETH OLOKODE NAVFAC NLON FEAD DIRECTOR NEW LONDON, GROTON, CT		
SATISFACTORY TO	DATE	
DES	JP	DRW
PMDM	JP	CHK
BRANCH MANAGER	JP	KB
CHIEF ENGINEER	JP	WRB
FIRE PROTECTION	JP	HPN
NAVAL FACILITIES ENGINEERING SYSTEMS COMMAND		
NAVAL FACILITIES ENGINEERING SYSTEMS COMMAND - MID-ATLANTIC		
NAVAL STATION - GROTON, CT		
GROTON, CONNECTICUT		
NAVAL SUBMARINE BASE NEW LONDON		
P-1102 WEAPONS MAGAZINE & ORDNANCE OPERATIONS FACILITY		
CLWS MAGAZINE		
ELECTRICAL HEAT TRACE DETAILS		
SCALE:	NONE	
PROJECT NO.:	1667770	
CONSTR. CONTR. NO.		
NAVFAC DRAWING NO.	12894311	
SHEET	68	OF 77
E-802S		

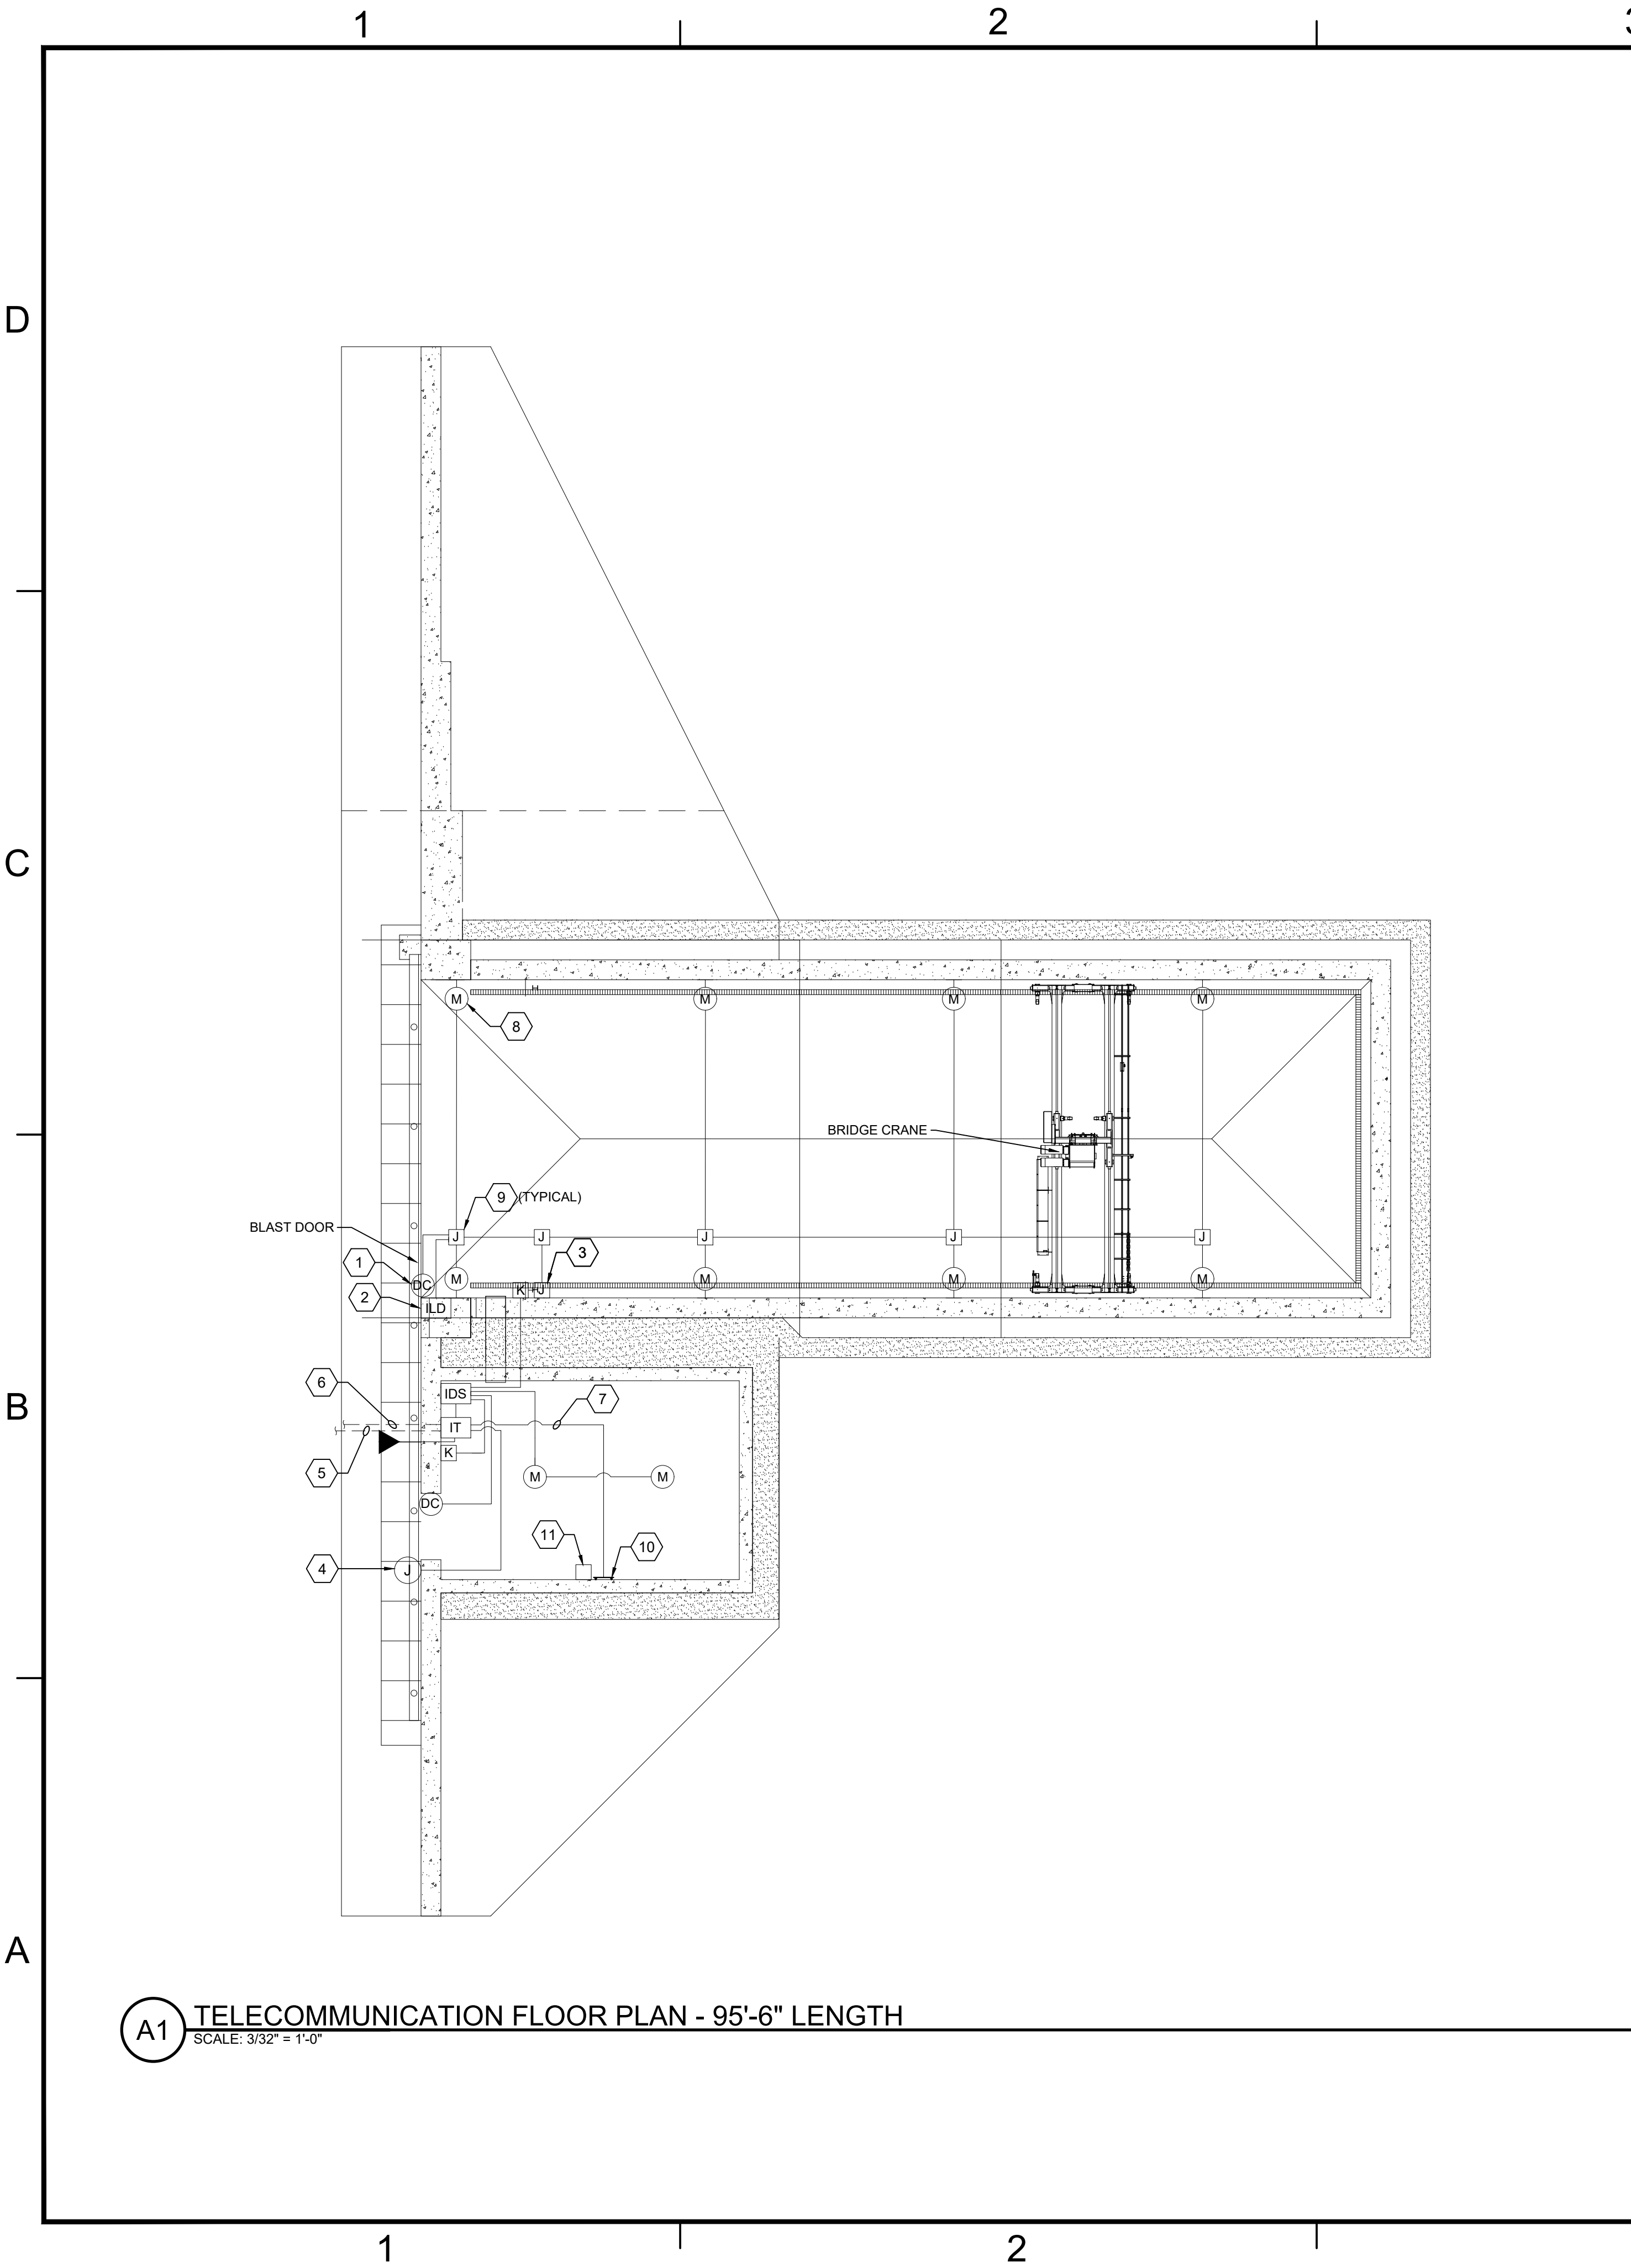


LEGEND	
Ⓢ	HIGH SECURITY BMS DOOR CONTACT
Ⓚ	KEYPAD
Ⓜ	MOTION DETECTOR, CEILING MOUNTED
Ⓜ	MOTION DETECTOR, WALL MOUNTED
Ⓝ	RECESSED JUNCTION BOX
Ⓝ	SURFACE JUNCTION BOX
IDS	IDS CONTROLLER
IT	IT CABINET
▼	PHONE OUTLET, SEE DETAIL A2/T501


- SHEET NOTES
1. ALL CONDUIT MUST BE RIGID GALVANIZED STEEL CONDUIT UNLESS INDICATED OTHERWISE.
 2. EXPOSED CONDUITS ON EXTERIOR WALLS MUST BE PROHIBITED.
 3. ECM AND MECHANICAL ROOM WILL BE SEPARATE IDS ZONES. PROVIDE DEVICES, CONTROLLERS, AND PROGRAMMING, AS REQUIRED.
 4. PROPOSED IDS VENDOR TO PERFORM COVERAGE CALCULATIONS, INCLUDING OBSTRUCTIONS, TO VERIFY QUANTITY AND LOCATION OF MOTION DETECTORS IN THE ECM AND MECHANICAL ROOM. FINAL LOCATIONS AND QUANTITIES OF MOTION DETECTORS TO BE INSTALLED PER IDS VENDOR SHOP DRAWINGS.
 5. ALL CONDUITS WILL BE MINIMUM 1" C UNLESS NOTED OTHERWISE. REFER TO T601 FOR CONDUIT SIZES.
 6. CONDUITS WILL BE EXPOSED INSIDE THE MAGAZINE AND MECHANICAL ROOM UNLESS INDICATED OTHERWISE. LOCATE CONDUITS AS HIGH AS POSSIBLE AND COORDINATE ROUTING WITH OTHER TRADES AND BRIDGE CRANE.

- KEYED NOTES
1. DOOR CONTACT FOR ECM DOOR. COORDINATE WITH DOOR MANUFACTURER FOR EXACT LOCATION AND ROUGH-IN REQUIREMENTS. COORDINATE WITH THE CONTRACTING OFFICER FOR THE CONNECTION OF THE BALANCED MAGNETIC SWITCH (BMS) ON THE DOOR.
 2. PROVIDE IDS CONNECTION TO THE ECM DOOR INTERNAL LOCKING DEVICE (ILD). COORDINATE WITH THE CONTRACTING OFFICER FOR THE CONNECTION OF THE ILD TO THE IDS SYSTEM BY NIWC.
 3. 8"X8"X4" JUNCTION BOX FOR ECM IDS COMPONENTS. PROVIDE 2" PVC-COATED RGC TO MECHANICAL ROOM FOR IDS WIRING.
 4. RECESSED ROUGH-IN FOR FUTURE CCTV CAMERA. PROVIDE 1" HOMERUN TO IT CABINET.
 5. EXTEND TWO 1-1/2" CONDUITS TO SITE POLE, LOCATION TO BE DETERMINED THROUGH COORDINATION WITH BASE SSO AND COMM SQUADRON, FOR POE IP CAMERA AND POE WIRELESS ACCESS POINT. POLE LOCATION AND CONDUIT ROUTE WILL BE LIMITED BY MAXIMUM CABLE LENGTH OF 295' FROM PATCH PANEL TO DEVICE. REFER TO DETAIL C1/T501 AND A1/T603.
 6. EXTEND TWO 4" CONDUITS TO NEAREST TELECOMM MANHOLE.
 7. HOMERUN TO SERVICE GROUNDING BAR.
 8. THE FIRST PAIR OF MOTION DETECTORS WILL BE INSTALLED 3' FROM THE INSIDE FACE OF THE MAGAZINE DOOR. ADDITIONAL PAIRS OF MOTION DETECTORS WILL BE EVENLY SPACED FOR COVERAGE OF THE INTERIOR SPACE, APPROXIMATELY 25' ON CENTER. MOTION DETECTORS WILL BE LOCATED ABOVE THE BRIDGE CRANE RAILS.
 9. SURFACE MOUNT ON BOTTOM OF STRUCTURAL CEILING. J-BOX LOCATIONS AND CONDUIT ROUTING TO BE COORDINATED WITH ALL TRADES AND BRIDGE CRANE TRAVEL.
 10. GROUND BAR. REFER TO E101A.
 11. EXTEND 1 INCH CONDUIT FROM WALL MOUNTED IT CABINET TO DDC PANEL FOR AHU CONTROLS. COORDINATE WITH MECHANICAL FOR EXACT ROUTING.


THESE DRAWINGS HAVE BEEN ADAPTED FROM APPROVED NAVFAC MUNITIONS STORAGE CONSTRUCTION DOCUMENTS, NAVFAC DRAWING NUMBERS 12877610 TO 12877660, APPROVED BY DDESB ON 17 MAY 2023. JACOBS DOR RESPONSIBILITY AND SEAL APPLICABILITY IS LIMITED TO THE SITE ADAPTATIONS AND MODIFICATIONS MADE TO THIS DRAWING.

APPR	DATE	SYN	DESCRIPTION
APPROVED:			
FOR COMMANDER NAVFAC:			
ACTIVITY: APPROVED BY LCDR ELIZABETH OLOKODE NAVFAC NLON FEAD DIRECTOR NEW LONDON, GROTON, CT			
SATISFACTORY TO: DATE: 05/27/2025			
DES	RR	DRW	TO
CHK	HF		
BRANCH MANAGER		SMS/CWJ	
WRB			
CHIEF ENGINEER		JWJ	
FIRE PROTECTION		HPN	
DEPARTMENT OF THE NAVY			
NAVAL FACILITIES ENGINEERING SYSTEMS COMMAND - MID-ATLANTIC			
NAVAL STATION - NORFOLK, VA			
GROTON, CONNECTICUT			
NAVAL SUBMARINE BASE NEW LONDON			
P-1102 WEAPONS MAGAZINE & ORDNANCE OPERATIONS FACILITY			
CLWS MAGAZINE			
TELECOMMUNICATION FLOOR PLAN B - SITE ADAPTED			
SCALE: NONE			
EPROJECT NO.: 1687770			
CONSTR. CONTR. NO.			
NAVFAC DRAWING NO. 12894313			
SHEET 70 OF 77			
T101BS			

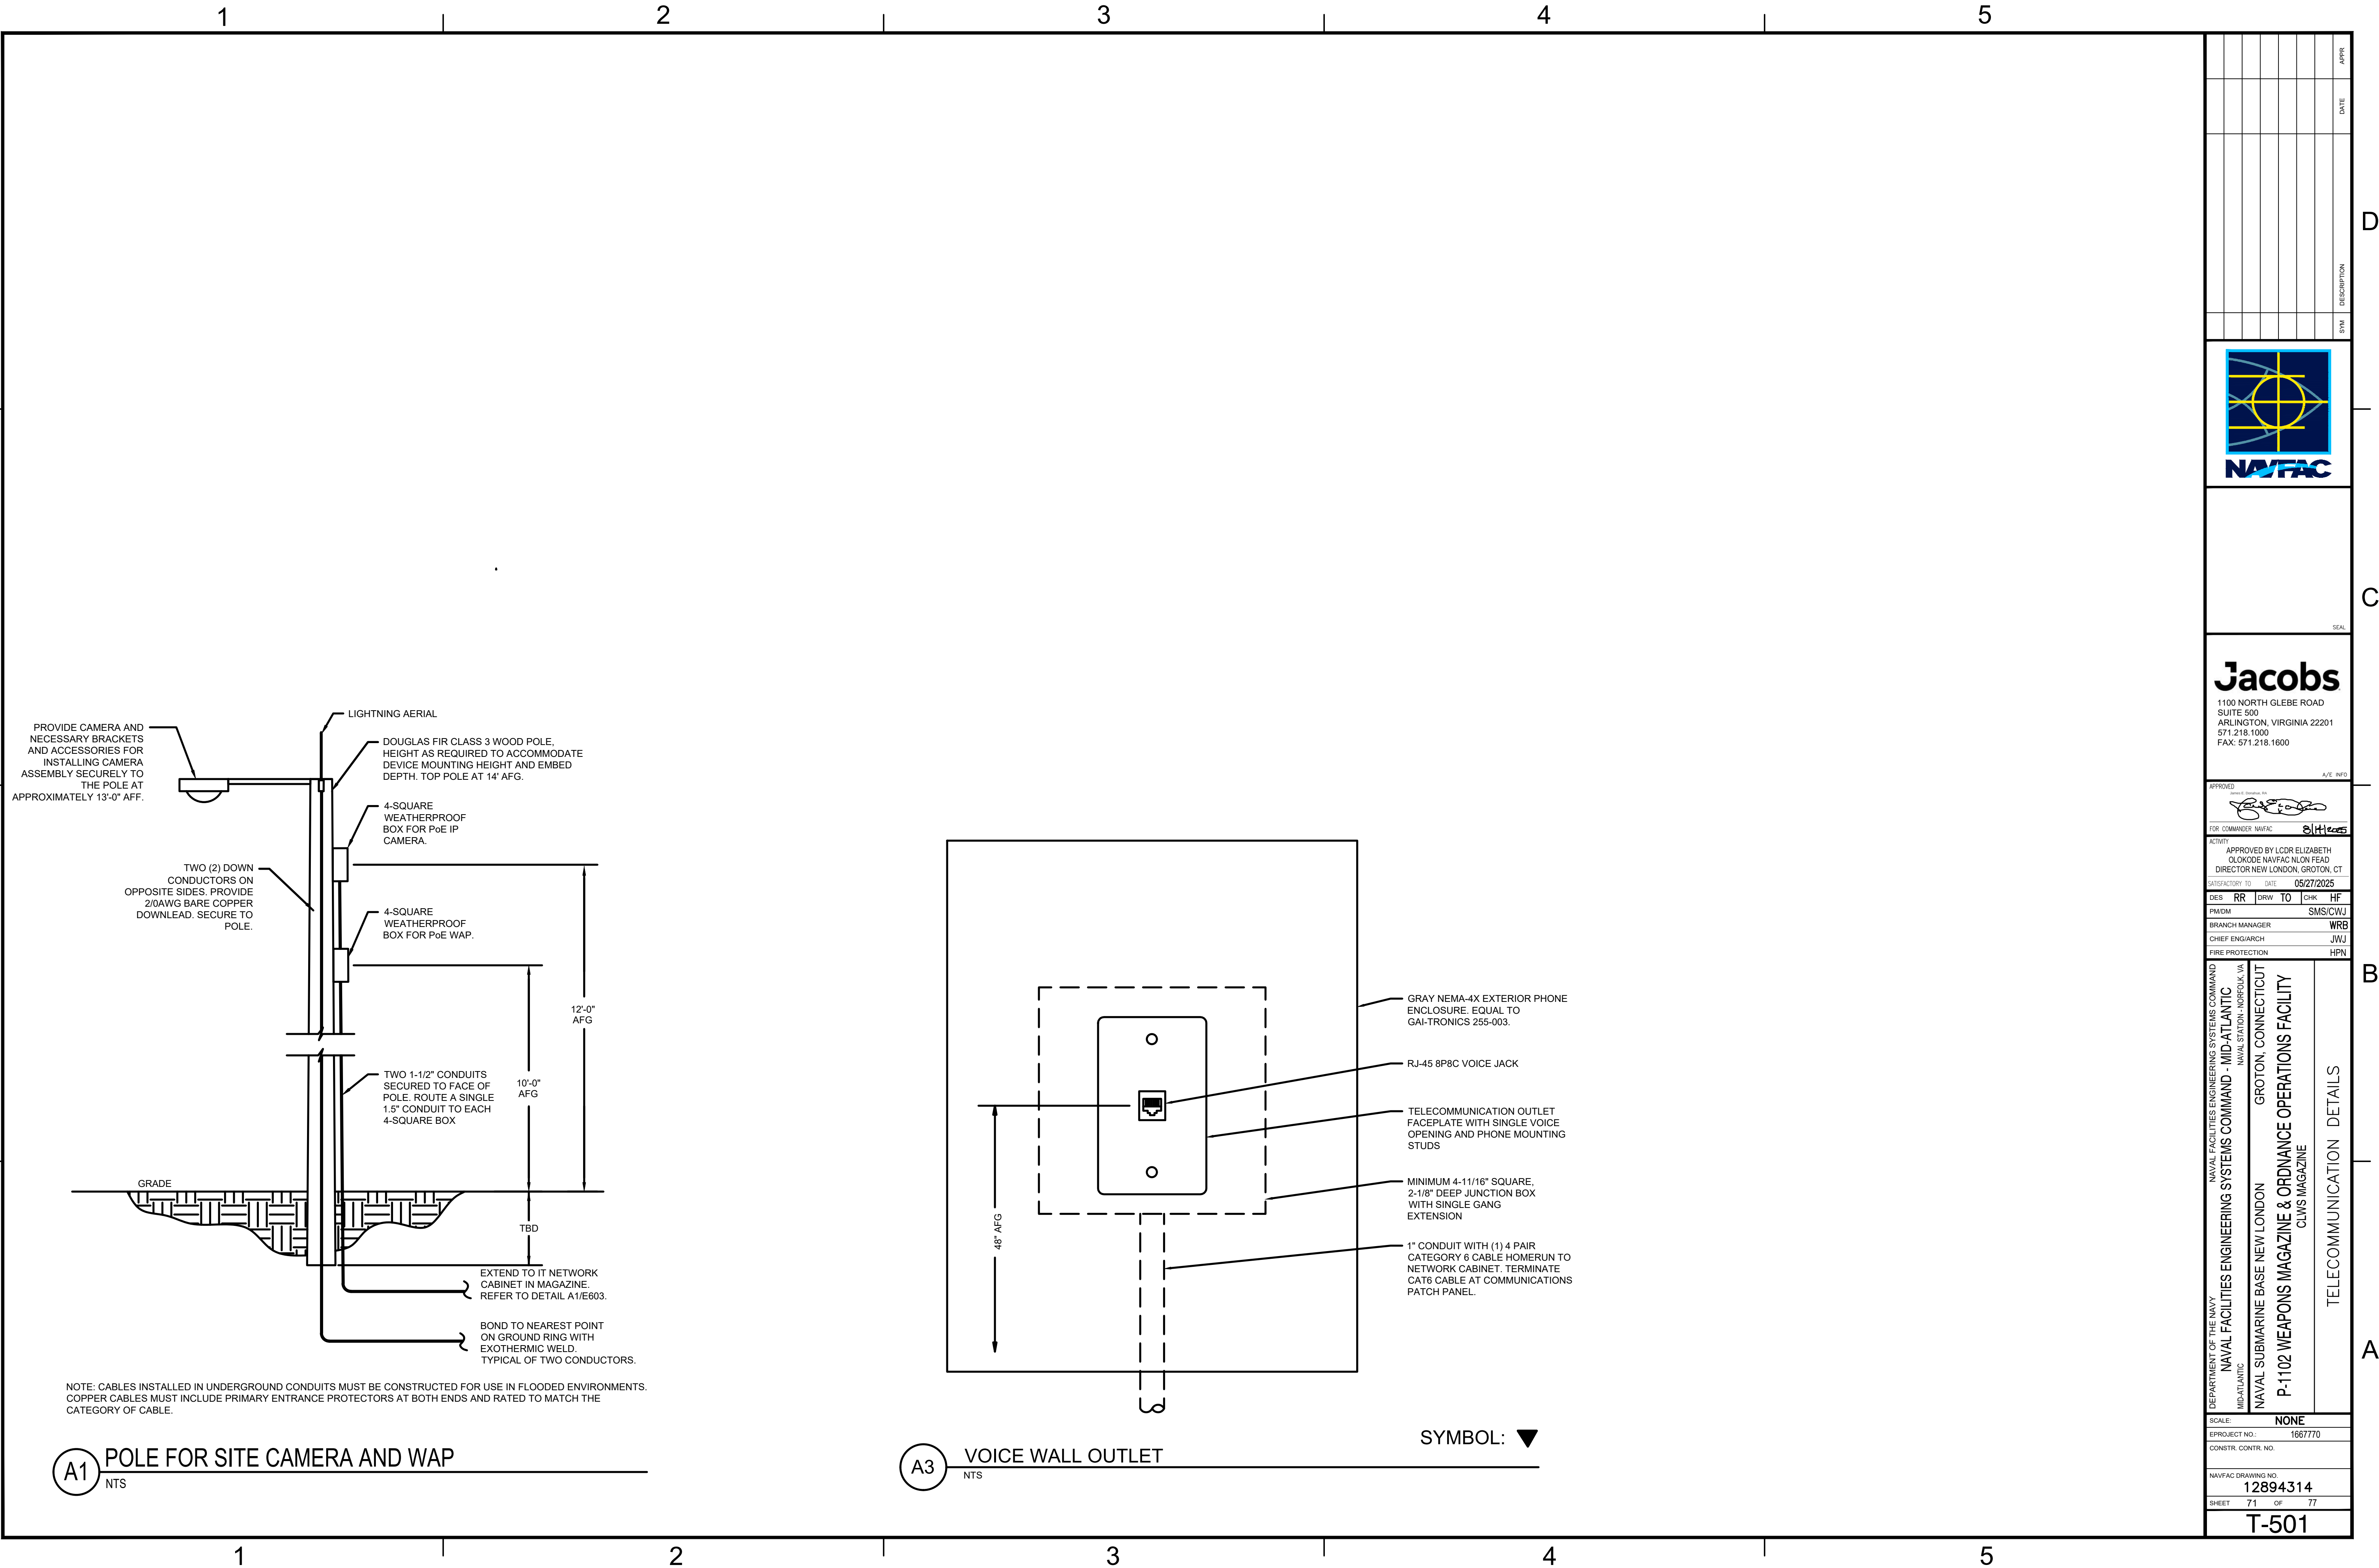

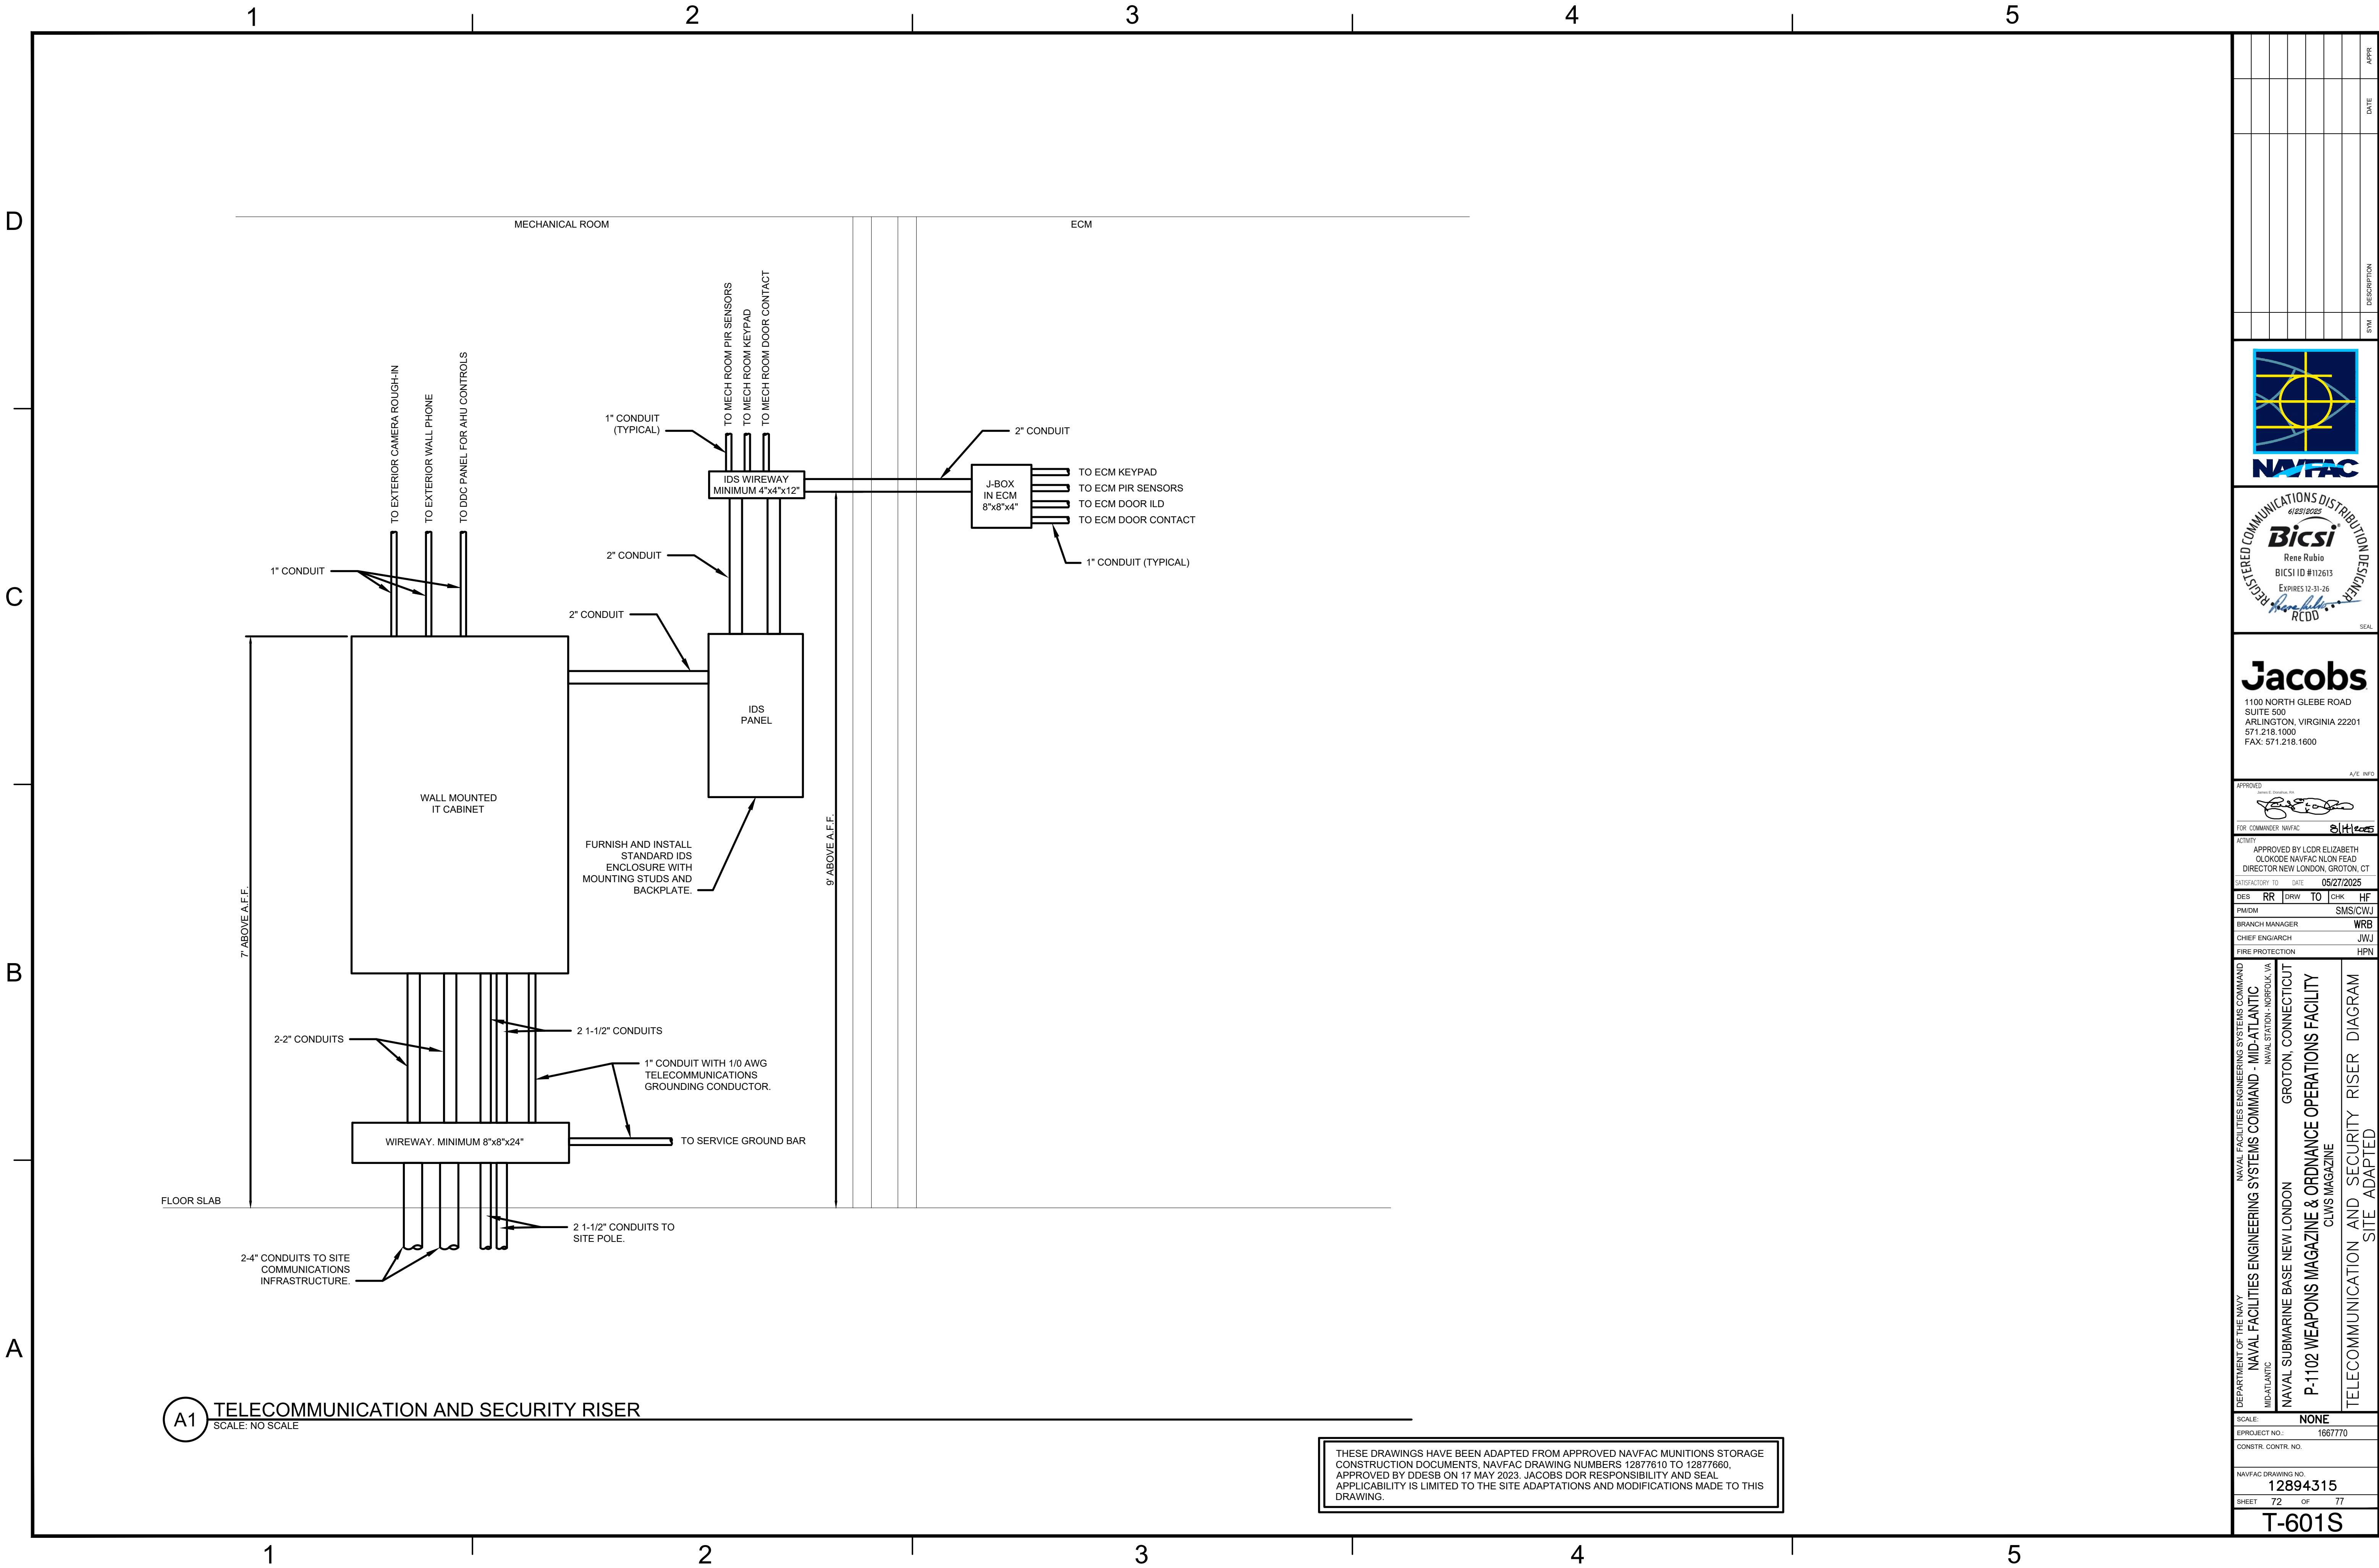

SYN	DESCRIPTION	DATE	APPR

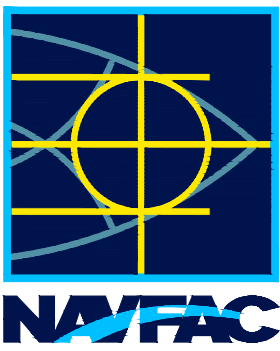

Jacobs

1100 NORTH GLEBE ROAD
SUITE 500
ARLINGTON, VIRGINIA 22201
571.218.1000
FAX: 571.218.1600

APPROVED
FOR COMMANDER NAVFAC

ACTIVITY
APPROVED BY LCDR ELIZABETH
OLOKODE NAVFAC NLON FEAD
DIRECTOR NEW LONDON, GROTON, CT

SATISFACTORY TO DATE 05/27/2025

DES RR DRW TO CHK HF

PMIDM SMS/CWJ

BRANCH MANAGER WRB

CHIEF ENGINEER JWJ

FIRE PROTECTION HPN

DEPARTMENT OF THE NAVY
NAVAL FACILITIES ENGINEERING SYSTEMS COMMAND - MID-ATLANTIC
NAVAL STATION - NORFOLK, VA
NAVAL SUBMARINE BASE NEW LONDON
GROTON, CONNECTICUT
P-1102 WEAPONS MAGAZINE & ORDNANCE OPERATIONS FACILITY
CLWS MAGAZINE
TELECOMMUNICATION AND SECURITY RISER DIAGRAM
SITE ADAPTED


SCALE: NONE
EPROJECT NO.: 1667770
CONSTR. CONTR. NO.

NAVFAC DRAWING NO.
12894315

SHEET 72 OF 77

T-601S

THESE DRAWINGS HAVE BEEN ADAPTED FROM APPROVED NAVFAC MUNITIONS STORAGE CONSTRUCTION DOCUMENTS, NAVFAC DRAWING NUMBERS 12877610 TO 12877660, APPROVED BY DDESB ON 17 MAY 2023. JACOBS DOR RESPONSIBILITY AND SEAL APPLICABILITY IS LIMITED TO THE SITE ADAPTATIONS AND MODIFICATIONS MADE TO THIS DRAWING.

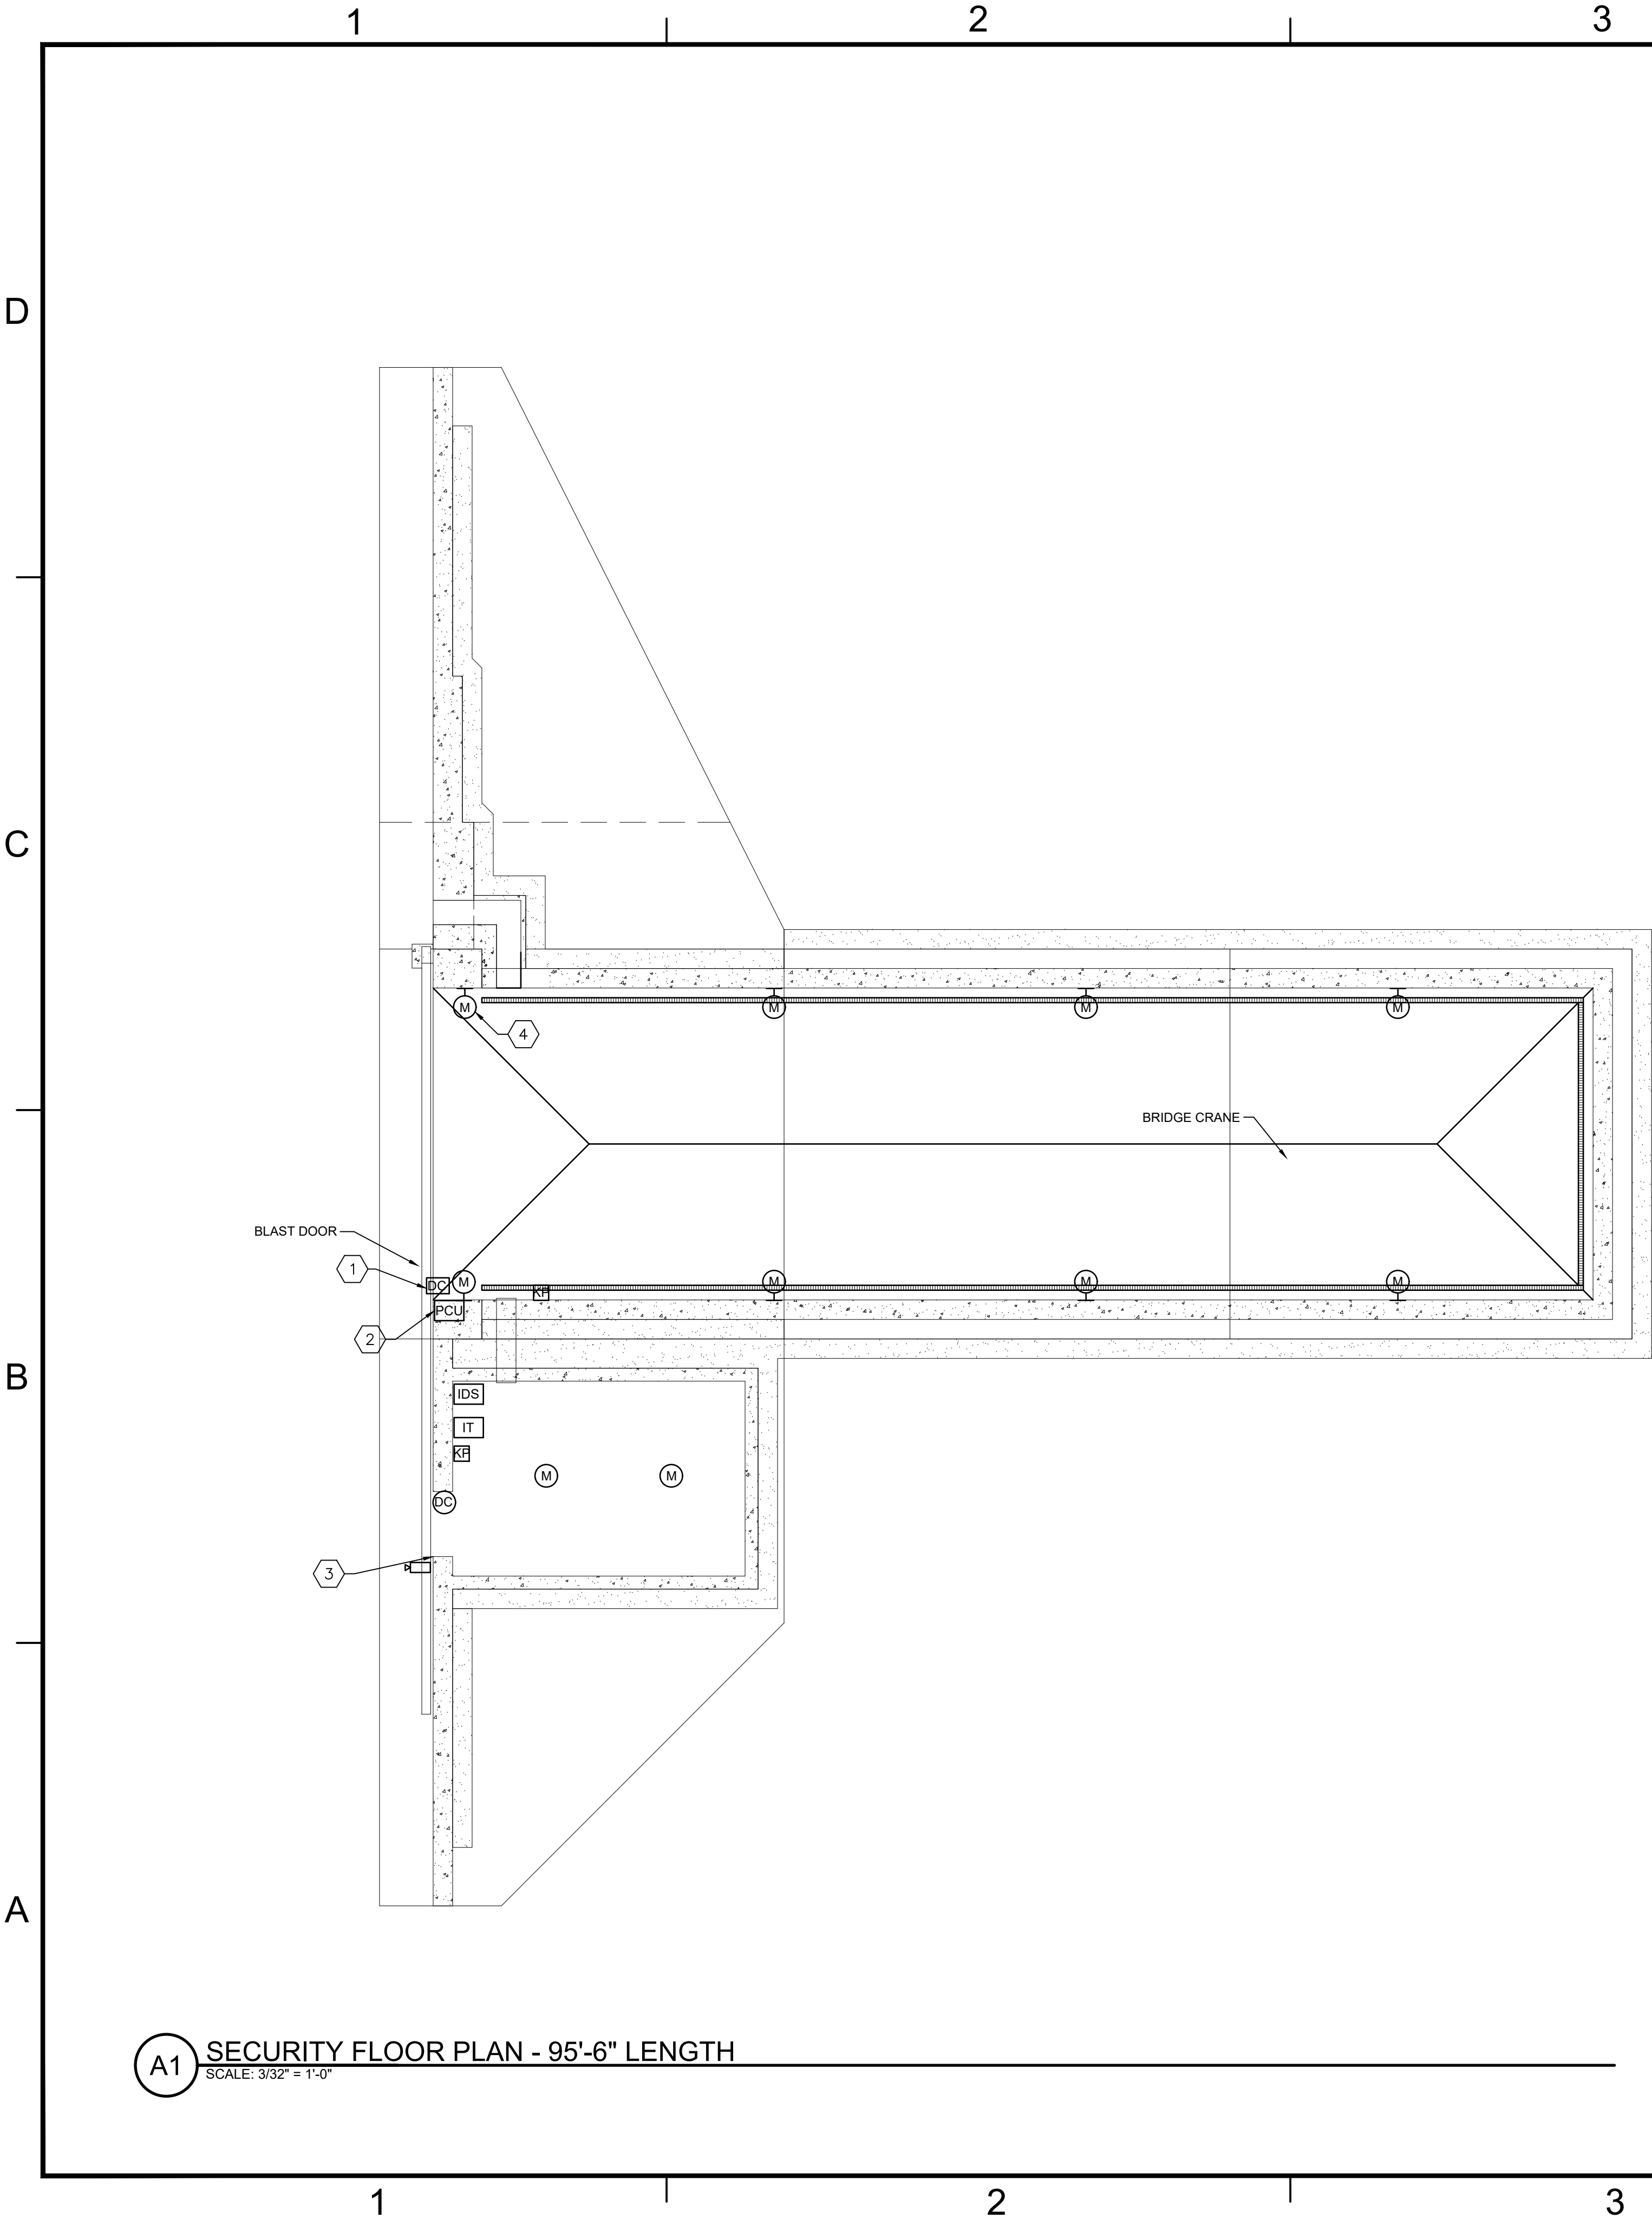

LEGEND	
	HIGH SECURITY BMS DOOR CONTACT
	KEYPAD
	MOTION DETECTOR, CEILING MOUNTED
	MOTION DETECTOR, WALL MOUNTED
	RECESSED JUNCTION BOX
	SURFACE JUNCTION BOX
	IDS CONTROLLER
	IT CABINET
	PHONE OUTLET, SEE DETAIL A2/T501

- SHEET NOTES
1. ALL CONDUIT MUST BE RIGID GALVANIZED STEEL CONDUIT UNLESS INDICATED OTHERWISE.

2. EXPOSED CONDUITS ON EXTERIOR WALLS MUST BE PROHIBITED.

3. ECM AND MECHANICAL ROOM WILL BE SEPARATE IDS ZONES. PROVIDE DEVICES, CONTROLLERS, AND PROGRAMMING, AS REQUIRED.

4. PROPOSED IDS VENDOR TO PERFORM COVERAGE CALCULATIONS, INCLUDING OBSTRUCTIONS, TO VERIFY QUANTITY AND LOCATION OF MOTION DETECTORS IN THE ECM AND MECHANICAL ROOM. FINAL LOCATIONS AND QUANTITIES OF MOTION DETECTORS TO BE INSTALLED PER IDS VENDOR SHOP DRAWINGS.

5. ALL CONDUITS WILL BE MINIMUM 1" C UNLESS NOTED OTHERWISE. REFER TO T601 FOR CONDUIT SIZES.

6. CONDUITS WILL BE EXPOSED INSIDE THE MAGAZINE AND MECHANICAL ROOM UNLESS INDICATED OTHERWISE. LOCATE CONDUITS AS HIGH AS POSSIBLE AND COORDINATE ROUTING WITH OTHER TRADES AND BRIDGE CRANE.

- KEYED NOTES
1. DOOR CONTACT FOR ECM DOOR. COORDINATE WITH DOOR MANUFACTURER FOR EXACT LOCATION AND ROUGH-IN REQUIREMENTS. COORDINATE WITH THE CONTRACTING OFFICER FOR THE CONNECTION OF THE BALANCED MAGNETIC SWITCH (BMS) ON THE DOOR.

2. PROVIDE IDS CONNECTION TO THE ECM DOOR INTERNAL LOCKING DEVICE (ILD). COORDINATE WITH THE CONTRACTING OFFICER FOR THE CONNECTION OF THE ILD TO THE IDS SYSTEM BY NIWC.

3. RECESSED ROUGH-IN FOR FUTURE CCTV CAMERA. PROVIDE 1" HOMERUN TO IT CABINET.

4. THE FIRST PAIR OF MOTION DETECTORS WILL BE INSTALLED 3' FROM THE INSIDE FACE OF THE MAGAZINE DOOR. ADDITIONAL PAIRS OF MOTION DETECTORS WILL BE EVENLY SPACED FOR COVERAGE OF THE INTERIOR SPACE, APPROXIMATELY 25' ON CENTER. MOTION DETECTORS WILL BE LOCATED ABOVE THE BRIDGE CRANE RAILS.

A1 SECURITY FLOOR PLAN - 95'-6" LENGTH
SCALE: 3/32" = 1'-0"

THESE DRAWINGS HAVE BEEN ADAPTED FROM APPROVED NAVFAC MUNITIONS STORAGE CONSTRUCTION DOCUMENTS, NAVFAC DRAWING NUMBERS 12877610 TO 12877660, APPROVED BY DDESB ON 17 MAY 2023. JACOBS DOR RESPONSIBILITY AND SEAL APPLICABILITY IS LIMITED TO THE SITE ADAPTATIONS AND MODIFICATIONS MADE TO THIS DRAWING.

APPR

DATE

SYN

DESCRIPTION

6/23/2025

Bicsi

Rene Rubio

BICS1 ID #112613

EXPIRES 12-31-26

REDD

Jacobs

1100 NORTH GLEBE ROAD
SUITE 500
ARLINGTON, VIRGINIA 22201
571.218.1000
FAX: 571.218.1600

APPROVED

FOR COMMANDER NAVFAC

ACTIVITY

SATISFACTORY TO

DATE

DES

MG

DRW

LA

CHK

RR

PMDM

BRANCH MANAGER

CHIEF ENGINEER

FIRE PROTECTION

NAVAL FACILITIES ENGINEERING SYSTEMS COMMAND

NAVAL FACILITIES ENGINEERING SYSTEMS COMMAND - MID-ATLANTIC

NAVAL SUBMARINE BASE NEW LONDON

NAVAL WEAPONS MAGAZINE & ORDNANCE OPERATIONS FACILITY

CLWS MAGAZINE

SECURITY FLOOR PLAN B - SITE ADAPTED

SCALE:

EPROJECT NO.:

CONSTR. CONTR. NO.

NAVFAC DRAWING NO.

SHEET

75

OF

77

TY101BS

