

6/20/2025 10:31:42 AM
\\ac1vps01\engineering\FD2E1628\AFCHBLDG-167770-A-BLM.rvt

G-002

A

B

C

D


LIST OF SHEETS

SHEET NO.		NAVFAC DWG. NO.	SHEET TITLE
NO.	SHEET		
GENERAL			
1	G-001	12893951	GENERAL COVER SHEET
2	G-002	12893952	GENERAL LIST OF SHEETS
3	G-101	12893953	GENERAL BUILDING CODE ANALYSIS
4	G-102	12893954	GENERAL FLOOR PLAN - LIFE SAFETY
5	G-103	12893955	CODE COMPLIANCE SITE PLAN - AREA A
STRUCTURAL			
6	S-001	12893956	GENERAL NOTES, ABBREVIATIONS & LEGEND
7	S-002	12893957	DESIGN CRITERIA & LOADS
8	S-003	12893958	MATERIAL NOTES
9	S-101	12893959	FOUNDATION & GROUND FLOOR PLAN
10	S-102	12893960	ROOF FRAMING PLANS
11	S-201	12893961	BUILDING ELEVATIONS
12	S-202	12893962	BUILDING ELEVATIONS
13	S-401	12893963	DUMPSTER ENCLOSURE
14	S-501	12893964	TYPICAL FOUNDATION & CONCRETE DETAILS
15	S-502	12893965	TYPICAL SLAB-ON-GROUND DETAILS
16	S-503	12893966	TYPICAL CONCRETE WALL DETAILS
17	S-504	12893967	TYPICAL STEEL DETAILS
18	S-505	12893968	TYPICAL JOIST DETAILS
19	S-510	12893969	SECTIONS & DETAILS
20	S-601	12893970	SCHEDULES
21	S-901	12893971	3D ISOMETRIC VIEWS
ARCHITECTURAL			
22	A-001	12893972	ARCHITECTURAL NOTES AND SYMBOLS
23	A-002	12893973	ARCHITECTURAL ACCESSIBILITY STANDARDS & MOUNTING HEIGHTS
24	A-003	12893974	ARCHITECTURAL AIR BARRIER INFORMATION
25	A-101	12893975	ARCHITECTURAL FLOOR PLAN
26	A-102	12893976	ARCHITECTURAL REFLECTED CEILING PLAN
27	A-103	12893977	ARCHITECTURAL ROOF PLAN
28	A-201	12893978	ARCHITECTURAL BUILDING ELEVATIONS
29	A-301	12893979	ARCHITECTURAL BUILDING SECTIONS
30	A-302	12893980	ARCHITECTURAL WALL SECTIONS
31	A-401	12893981	ARCHITECTURAL ENLARGED PLANS
32	A-501	12893982	ARCHITECTURAL EXTERIOR DETAILS
33	A-502	12893983	ARCHITECTURAL MISCELLANEOUS DETAILS
34	A-503	12893984	OPENING DETAILS
35	A-510	12893985	TYPICAL ROOF DETAILS
36	A-601	12893986	ARCHITECTURAL SCHEDULES
37	A-602	12893987	ARCHITECTURAL PARTITION TYPES
38	A-603	12893988	ARCHITECTURAL EXTERIOR MATERIAL SCHEDULE
INTERIORS			
39	I-101	12893989	FF&E PLAN & SCHEDULE
40	I-102	12893990	INTERIOR FINISH PLAN & ROOM FINISH SCHEDULE
41	I-103	12893991	SIGNAGE PLAN & SCHEDULE
42	I-401	12893992	OFFICE PLANS & ISOMETRIC VIEWS
43	I-402	12893993	WORKSTATION PLANS & ISOMETRIC VIEWS
44	I-403	12893994	INTERIOR ENLARGED PLANS & ELEVATIONS
45	I-404	12893995	INTERIOR ENLARGED PLANS & ELEVATIONS
46	I-405	12893996	INTERIOR ENLARGED PLANS & ELEVATIONS
47	I-501	12893997	INTERIOR DETAILS
48	I-502	12893998	SIGNAGE DETAILS
49	I-601	12893999	INTERIOR MATERIALS FINISH SCHEDULE

SHEET NO.		NAVFAC DWG. NO.	SHEET TITLE
NO.	SHEET		
FIRE PROTECTION			
50	FX001	12894000	FIRE SUPPRESSION SYMBOLS, LEGEND, ABBREVIATIONS AND NOTES
51	FX101	12894001	FIRE SUPPRESSION FLOOR PLAN
52	FX501	12894002	FIRE SUPPRESSION RISER AND DETAILS
FIRE ALARM			
53	FA001	12894003	FIRE ALARM AND MASS NOTIFICATION SYMBOLS, LEGEND, ABBREVIATIONS AND NOTES
54	FA101	12894004	FIRE ALARM AND MASS NOTIFICATION FLOOR PLAN
55	FA501	12894005	FIRE ALARM AND MASS NOTIFICATION RISER DIAGRAM, MATRIX, AND DETAILS
PLUMBING			
56	P-001	12894006	PLUMBING LEGEND AND GENERAL NOTES
57	P-101	12894007	PLUMBING SANITARY & VENT FLOOR PLAN
58	P-102	12894008	PLUMBING DOMESTIC WATER FLOOR PLAN
59	P-103	12894009	PLUMBING ROOF PLAN
60	P-104	12894010	PLUMBING RADON MITIGATION FLOOR PLAN
61	P-301	12894011	PLUMBING SECTIONS
62	P-401	12894012	PLUMBING ENLARGED PLANS - SANITARY & VENT
63	P-402	12894013	PLUMBING ENLARGED PLANS - DOMESTIC WATER
64	P-501	12894014	PLUMBING DETAILS
65	P-502	12894015	PLUMBING DETAILS
66	P-601	12894016	PLUMBING SCHEDULES
67	P-901	12894017	PLUMBING RISER DIAGRAMS - SANITARY WASTE & VENT
68	P-902	12894018	PLUMBING RISER DIAGRAMS - DOMESTIC WATER
MECHANICAL			
69	M-001	12894019	MECHANICAL LEGEND, ABBREVIATIONS AND NOTES
70	M-101	12894020	MECHANICAL FLOOR PLAN - DUCTWORK
71	MP101	12894021	MECHANICAL FLOOR PLAN - PIPING
72	M-301	12894022	MECHANICAL SECTIONS
73	M-401	12894023	MECHANICAL ENLARGED FLOOR PLAN
74	M-501	12894024	MECHANICAL DETAILS
75	M-502	12894025	MECHANICAL DETAILS
76	M-601	12894026	MECHANICAL SCHEDULES
77	M-800	12894027	MECHANICAL CONTROLS LEGEND AND ABBREVIATIONS
78	M-801	12894028	MECHANICAL CONTROL DIAGRAMS & SEQUENCES
79	M-802	12894029	MECHANICAL CONTROL DIAGRAMS & SEQUENCES
80	M-803	12894030	MECHANICAL CONTROL DIAGRAMS & SEQUENCES
81	M-804	12894031	MECHANICAL CONTROL DIAGRAMS & SEQUENCES
82	M-805	12894032	MECHANICAL CONTROL POINTS SCHEDULE
83	M-806	12894033	MECHANICAL CONTROL POINTS SCHEDULE
84	M-807	12894034	MECHANICAL CONTROL POINTS SCHEDULE
85	M-808	12894035	MECHANICAL CONTROL POINTS SCHEDULE
86	M-809	12894036	MECHANICAL CONTROL POINTS SCHEDULE

SHEET NO.		NAVFAC DWG. NO.	SHEET TITLE
NO.	SHEET		
ELECTRICAL			
87	E-001	12894037	ELECTRICAL GENERAL NOTES
88	E-002	12894038	ELECTRICAL ABBREVIATIONS
89	E-003	12894039	ELECTRICAL SYMBOLS
90	E-004	12894040	ELECTRICAL SYMBOLS
91	EG101	12894041	ELECTRICAL GROUNDING PLAN
92	EG102	12894042	ELECTRICAL LIGHTNING PROTECTION PLAN
93	EL101	12894043	ELECTRICAL LIGHTING PLAN
94	EP101	12894044	ELECTRICAL POWER PLAN
95	EP102	12894045	ELECTRICAL EQUIPMENT POWER PLAN
96	E-501	12894046	ELECTRICAL DETAILS
97	E-502	12894047	ELECTRICAL DETAILS
98	E-503	12894048	ELECTRICAL DETAILS
99	E-504	12894049	ELECTRICAL DETAILS
100	E-601	12894050	ELECTRICAL POWER SINGLE LINE DIAGRAM
101	E-701	12894051	LIGHTING FIXTURE AND CONTROLS SCHEDULES
102	E-702	12894052	ELECTRICAL PANEL SCHEDULES
103	E-703	12894053	ELECTRICAL PANEL SCHEDULES
104	E-704	12894054	ELECTRICAL FEEDER SCHEDULE
TELECOMMUNICATIONS			
105	T-001	12894055	TELECOMMUNICATIONS SYMBOLS, LEGEND, ABBREVIATIONS, AND NOTES
106	T-101	12894056	TELECOMMUNICATIONS FLOOR PLAN
107	T-201	12894057	TELECOMMUNICATIONS RACK ELEVATIONS
108	T-202	12894058	TELECOMMUNICATIONS ELEVATIONS
109	T-401	12894059	TELECOMMUNICATIONS ENLARGED PLANS
110	T-501	12894060	TELECOMMUNICATIONS DETAILS
111	T-502	12894061	TELECOMMUNICATIONS DETAILS
112	T-503	12894062	TELECOMMUNICATIONS DETAILS
113	T-504	12894063	TELECOMMUNICATIONS DETAILS
114	T-505	12894064	TELECOMMUNICATIONS DETAILS
115	T-506	12894065	TELECOMMUNICATIONS DETAILS
116	T-507	12894066	TELECOMMUNICATIONS DETAILS
117	T-508	12894067	TELECOMMUNICATIONS DETAILS
118	T-509	12894068	TELECOMMUNICATIONS DETAILS
119	T-510	12894069	TELECOMMUNICATIONS DETAILS
120	T-601	12894070	TELECOMMUNICATIONS RISER DIAGRAMS
121	T-602	12894071	TELECOMMUNICATIONS SCHEDULES
122	T-603	12894072	ONE LINE OSP RISER DIAGRAM
AUDIO VISUAL			
123	TA001	12894073	AUDIO VISUAL SYMBOLS, LEGEND, ABBREVIATIONS, AND NOTES
124	TA002	12894074	AUDIO VISUAL DISPLAY SCHEDULE
125	TA101	12894075	AUDIO VISUAL FLOOR PLAN
126	TA201	12894076	AUDIO VISUAL ELEVATIONS
127	TA202	12894077	AUDIO VISUAL ELEVATIONS
128	TA401	12894078	AUDIO VISUAL ENLARGED PLANS
129	TA402	12894079	AUDIO VISUAL ENLARGED PLANS
130	TA501	12894080	AUDIO VISUAL DETAILS
131	TA502	12894081	AUDIO VISUAL DETAILS
132	TA601	12894082	AUDIO VISUAL DIAGRAMS
133	TA602	12894083	AUDIO VISUAL DIAGRAMS
SECURITY			
134	TY001	12894084	SECURITY SYMBOLS, LEGEND, ABBREVIATIONS, AND NOTES
135	TY101	12894085	SECURITY FLOOR PLAN
136	TY501	12894086	SECURITY DETAILS
137	TY502	12894087	SECURITY DETAILS
138	TY503	12894088	SECURITY DETAILS
139	TY504	12894324	SECURITY DETAILS
140	TY601	12894323	SECURITY SCHEMATIC DESIGN

FILE NAME: C:\pwworker\den003\jgs_woods\00910659\P1102_G-103.dwg LAYOUT NAME: G-103 CODE COMPLIANCE SITE PLAN PLOTTED: Friday, June 20, 2025 - 11:17am USER: woodj

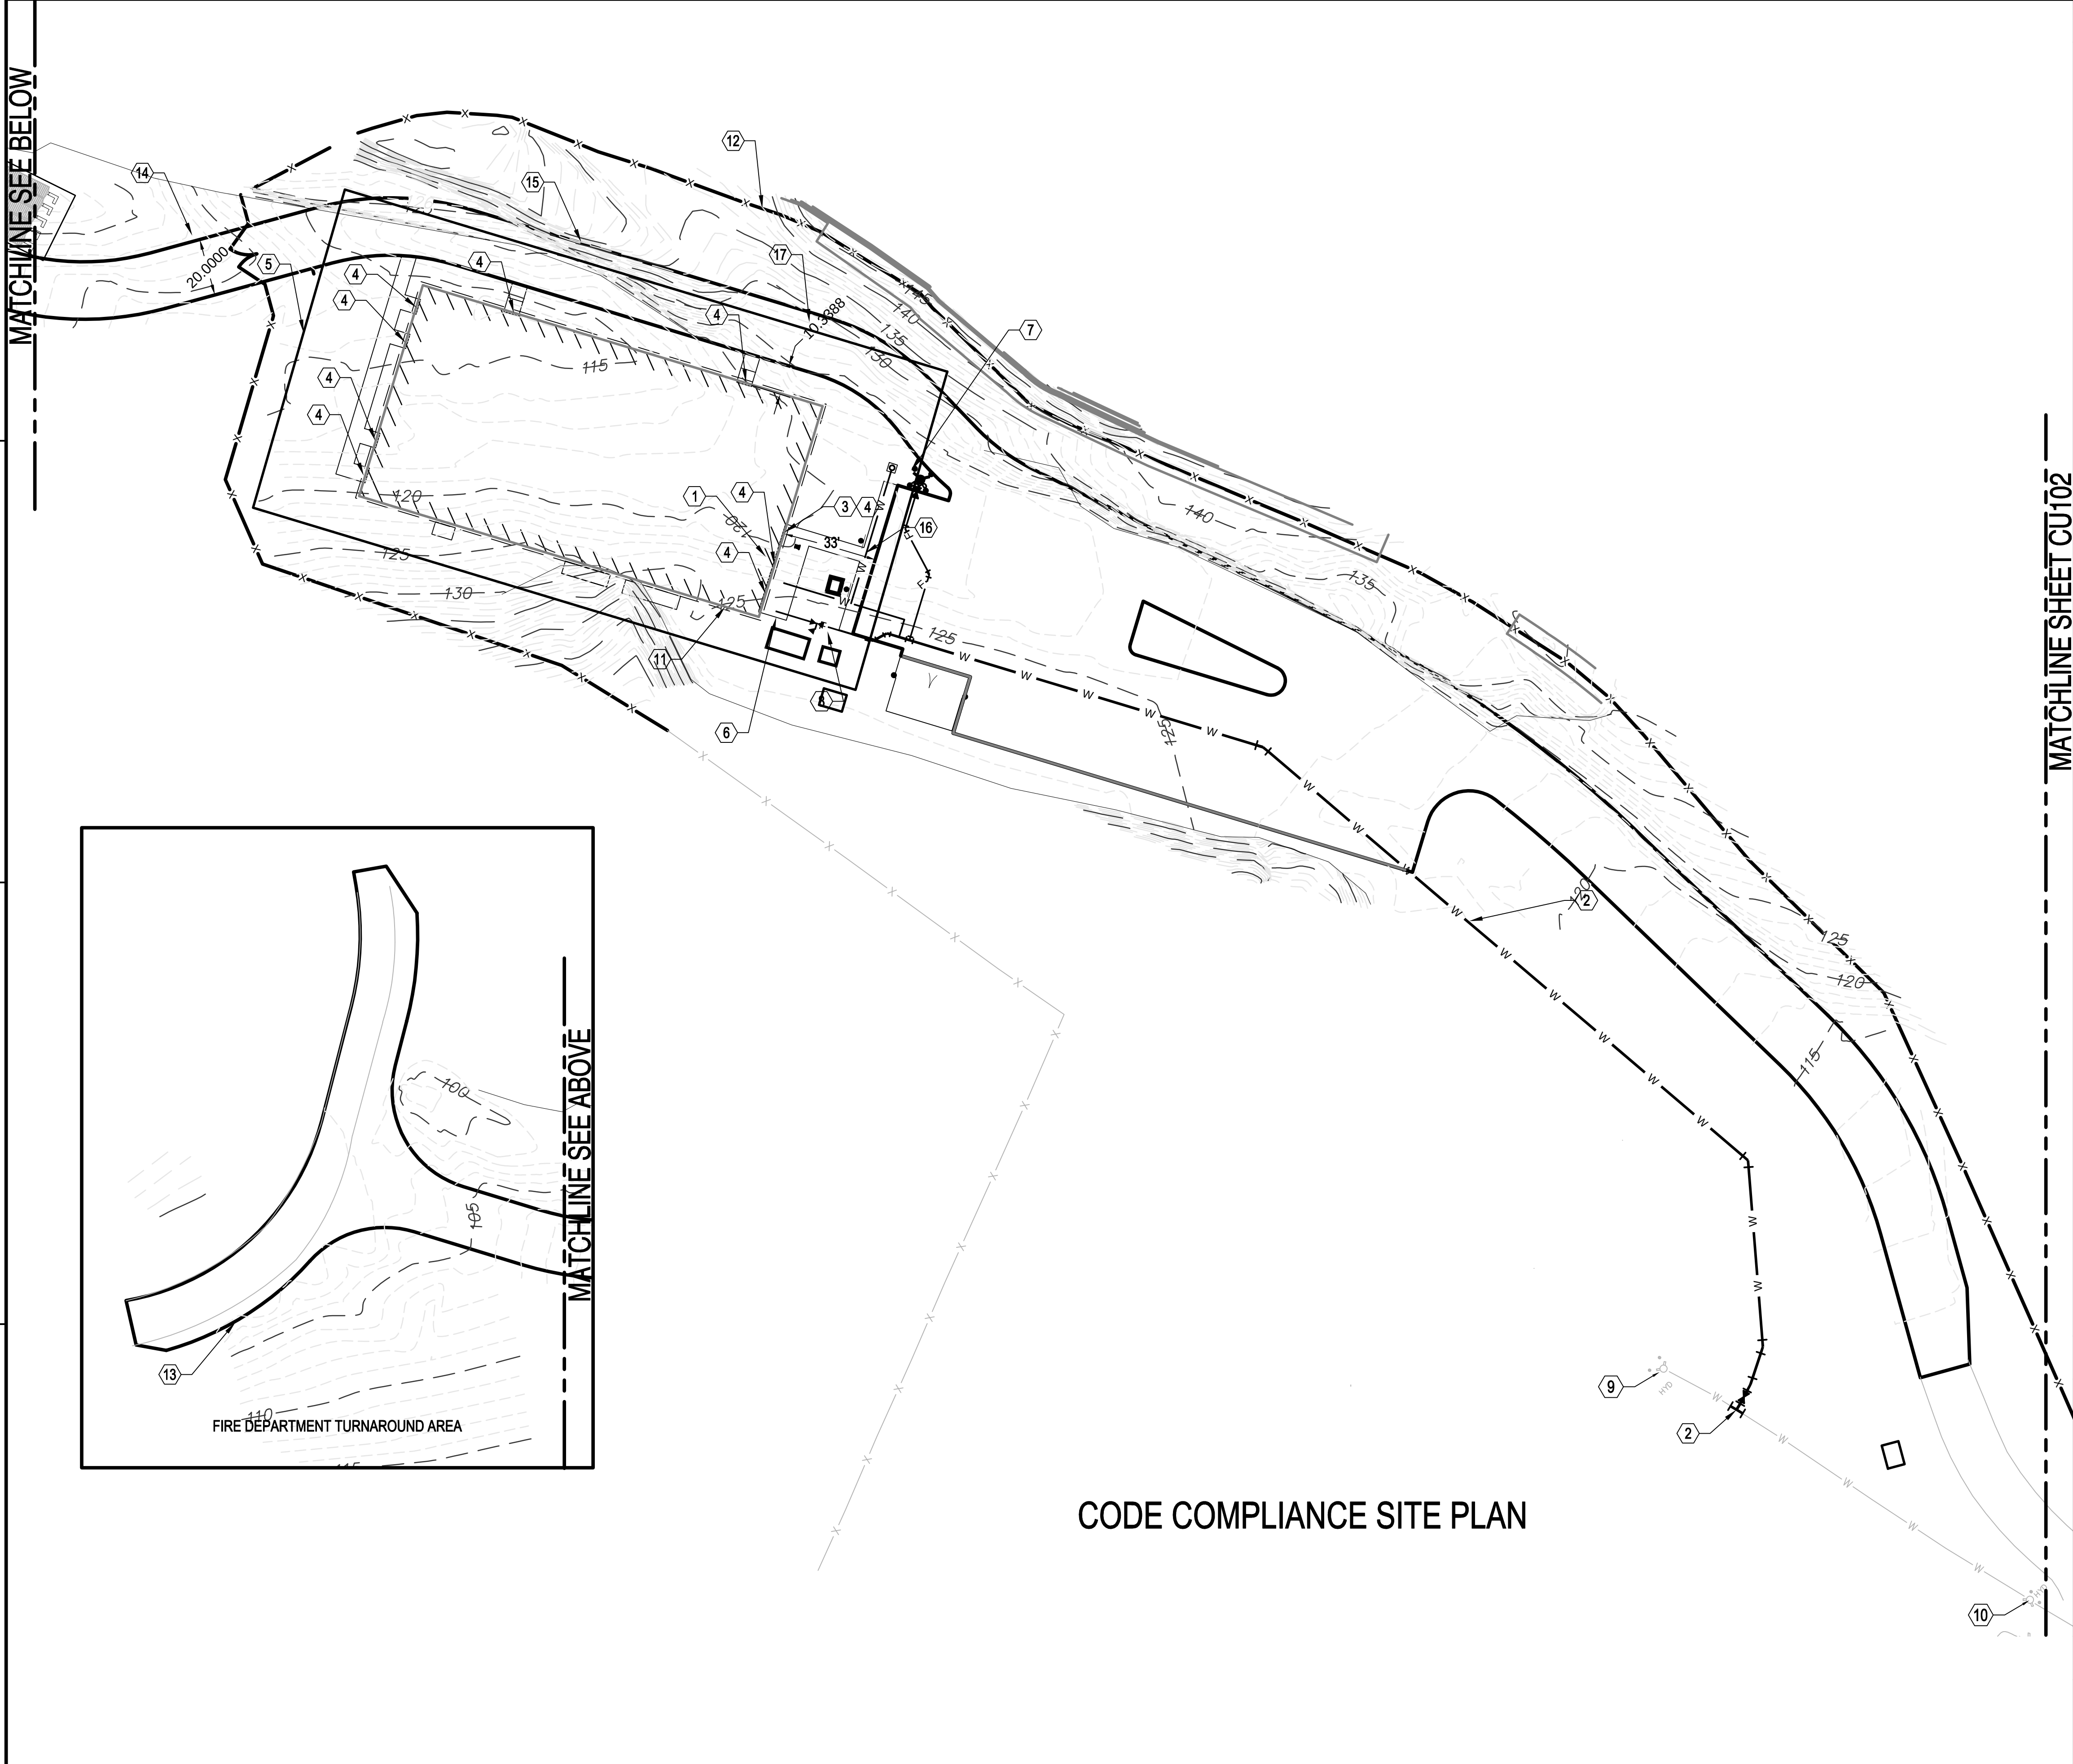

CODE COMPLIANCE SITE PLAN


GENERAL SHEET NOTES

- A. REFER TO SHEET C-001 FOR ADDITIONAL NOTES.
- B. REFER TO ARCHITECTURAL PLANS FOR ALL BUILDING DIMENSIONS.
- C. REFER TO SHEET CU101 FOR DETAILED UTILITY PLAN.

KEYED NOTES

- 1. FIRE ALARM/ MASS NOTIFICATION CONTROL PANEL (FMCP) LOCATION
- 2. 10" WATER MAIN
- 3. INTENDED MAIN FIRE DEPARTMENT ENTRANCE
- 4. EXIT DISCHARGE
- 5. ASSUMED PROPERTY LINE
- 6. INCOMING 6" WATER LINE
- 7. NEW FIRE HYDRANT
- 8. POST INDICATOR VALVE
- 9. EXISTING FIRE HYDRANT - FLOW HYDRANT 47
- 10. EXISTING FIRE HYDRANT - GAUGE HYDRANT 46
- 11. FIRE DEPARTMENT CONNECTION
- 12. CHAIN LINK FENCE
- 13. FIRE DEPARTMENT TURN- AROUND AREA
- 14. FIRE LANE WIDTH
- 15. FIRE DEPARTMENT VEHICLE ACCESS ROAD
- 16. DISTANCE FROM FIRE DEPARTMENT VEHICLE ACCESS TO MAIN FIRE DEPARTMENT ENTRANCE
- 17. CLOSEST DISTANCE FROM FIRE DEPARTMENT VEHICLE ACCESS TO ENTRANCE


KEYPLAN

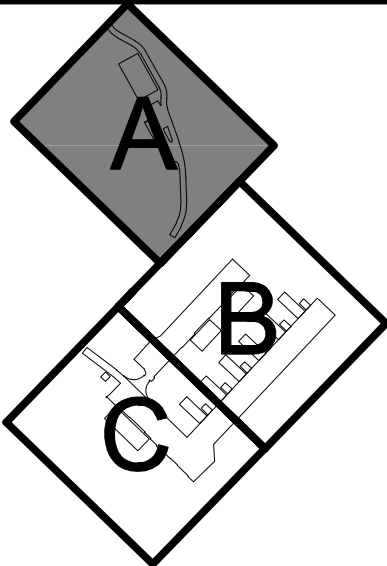

GRAPHIC SCALE



SYN	DESCRIPTION	DATE	APPR

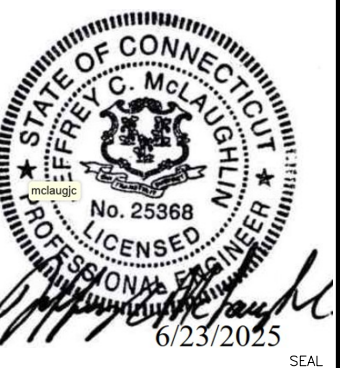

Jacobs
1100 NORTH GLEBE ROAD
SUITE 500
ARLINGTON, VIRGINIA 22201
571.218.1000
FAX: 571.218.1600

APPROVED: A/E INFO

FOR COMMANDER NAFAC

ACTIVITY: APPROVED BY LCDR ELIZABETH
OLOKODE NAFAC NLON FEAD
DIRECTOR NEW LONDON, GROTON, CT

SATISFACTORY TO DATE: 06/27/2025

DES: JM | DRW: CL | CHK: JB

PMIDM: SMS/CWJ

BRANCH MANAGER: HPN

CHIEF ENGINEER: JMW

FIRE PROTECTION: HPN

NAVAL FACILITIES ENGINEERING SYSTEMS COMMAND

NAVAL FACILITIES ENGINEERING SYSTEMS COMMAND - MID-ATLANTIC

NAVAL STATION - NORFOLK VA

GROTON, CONNECTICUT

NAVAL SUBMARINE BASE NEW LONDON

P-1102 WEAPONS MAGAZINE & ORDNANCE OPERATIONS FACILITY

OPERATIONS

CODE COMPLIANCE SITE PLAN - AREA A

DEPARTMENT OF THE NAVY

D

C

B

A

DESIGN CRITERIA & LOADS						
SUPERIMPOSED DEAD & LIVE LOADS (UNFACTORED - PSF)	TYPICAL ROOF					
	ROOF ABOVE MECH AND ELEC ROOMS					
	ARMS ROOM CEILING SLAB					
	TYPICAL FLOOR					
	MECH AND ELEC ROOM FLOOR					
ARMS ROOM FLOOR						
ROOF MEMBRANE & INSULATION	5	5	----	----	----	----
MEP	5	15	5	----	----	----
CEILING	10	----	----	----	----	----
HOUSEKEEPING PAD	----	----	----	----	50	----
1. TOTAL SDL	20	20	5	----	25	----
2. LIVE LOAD	20	20	125	100	125	150
3. BUILDING RISK CATEGORY	II					
4. SNOW						
a. SNOW IMPORTANCE FACTOR, Is	1.0					
b. GROUND SNOW LOAD, Pg	30 PSF					
c. TERRAIN ROUGHNESS	C					
d. ROOF EXPOSURE FACTOR, Ce	1.0 PARTIALLY EXPOSED					
e. THERMAL FACTOR, Ct	1.0					
f. ROOF SLOPE FACTOR, Cs	1.0					
g. FLAT-ROOF SNOW LOAD, Pf	21 PSF					
h. MINIMUM UNIFORM SNOW LOAD, Pm	20 PSF					
i. DESIGN SNOW LOAD W/ DRIFT	REFER TO FIGURE 1					
5. RAIN						
a. INTENSITY, i	2.75 IN/HR					
b. RAIN LOAD, R	11 PSF					
6. WIND						
a. ULTIMATE DESIGN WIND SPEED, V:	128 MPH					
b. ALLOWABLE STRESS WIND SPEED, V _{asd} :	99 MPH					
c. WIND EXPOSURE:	C					
d. INTERNAL PRESSURE COEF, GC _{pi}	±0.18 ENCLOSED					
e. MAIN WIND-FORCE RESISTING SYSTEM						
• 0 FT - ROOF:	31 PSF					
• PARAPET	70 PSF					
f. COMPONENTS & CLADDING	REFER TO TABLE 1					
7. EARTHQUAKE						
a. SEISMIC IMPORTANCE FACTOR	1.0					
b. SEISMIC SITE CLASSIFICATION	C					
c. MAPPED SPECTRAL ACCELERATION						
• SHORT PERIOD, S _s	0.190g					
• 1-SECOND PERIOD, S ₁	0.052g					
d. DESIGN SPECTRAL ACCELERATION						
• SHORT PERIOD, S _{0s}	0.165g					
• 1-SECOND PERIOD, S ₀₁	0.052g					
e. SEISMIC DESIGN CATEGORY	A					
f. MAIN BUILDING (EXTERIOR WALLS)						
• FORCE-RESISTING SYSTEM	ORDINARY REINFORCED CONCRETE SHEAR WALLS					
• RESPONSE MODIFICATION, R	4					
• SYSTEM OVERSTRENGTH, Q ₀	2.5					
• DEFLECTION AMPLIFICATION, C _d	4					
• ANALYSIS PROCEDURE	EQUIVALENT LATERAL FORCE					
• SEISMIC RESPONSE COEF, C _s	0.041					
• SEISMIC WEIGHT, W	435 KIPS					
• DESIGN BASE SHEAR	18 KIPS					
g. ARMS ROOM						
• FORCE-RESISTING SYSTEM	ORDINARY REINFORCED CONCRETE SHEAR WALLS					
• RESPONSE MODIFICATION, R	4					
• SYSTEM OVERSTRENGTH, Q ₀	2.5					
• DEFLECTION AMPLIFICATION, C _d	4					
• ANALYSIS PROCEDURE	EQUIVALENT LATERAL FORCE					
• SEISMIC RESPONSE COEF, C _s	0.041					
• SEISMIC WEIGHT, W	115 KIPS					
• DESIGN BASE SHEAR	5 KIPS					
8. FOUNDATIONS						
a. MINIMUM SOIL BEARING CAPACITY	4,000 PSF					
b. FROST DEPTH	38 IN					

FIGURE 1 - DESIGN ROOF SNOW LOAD W/ DRIFT


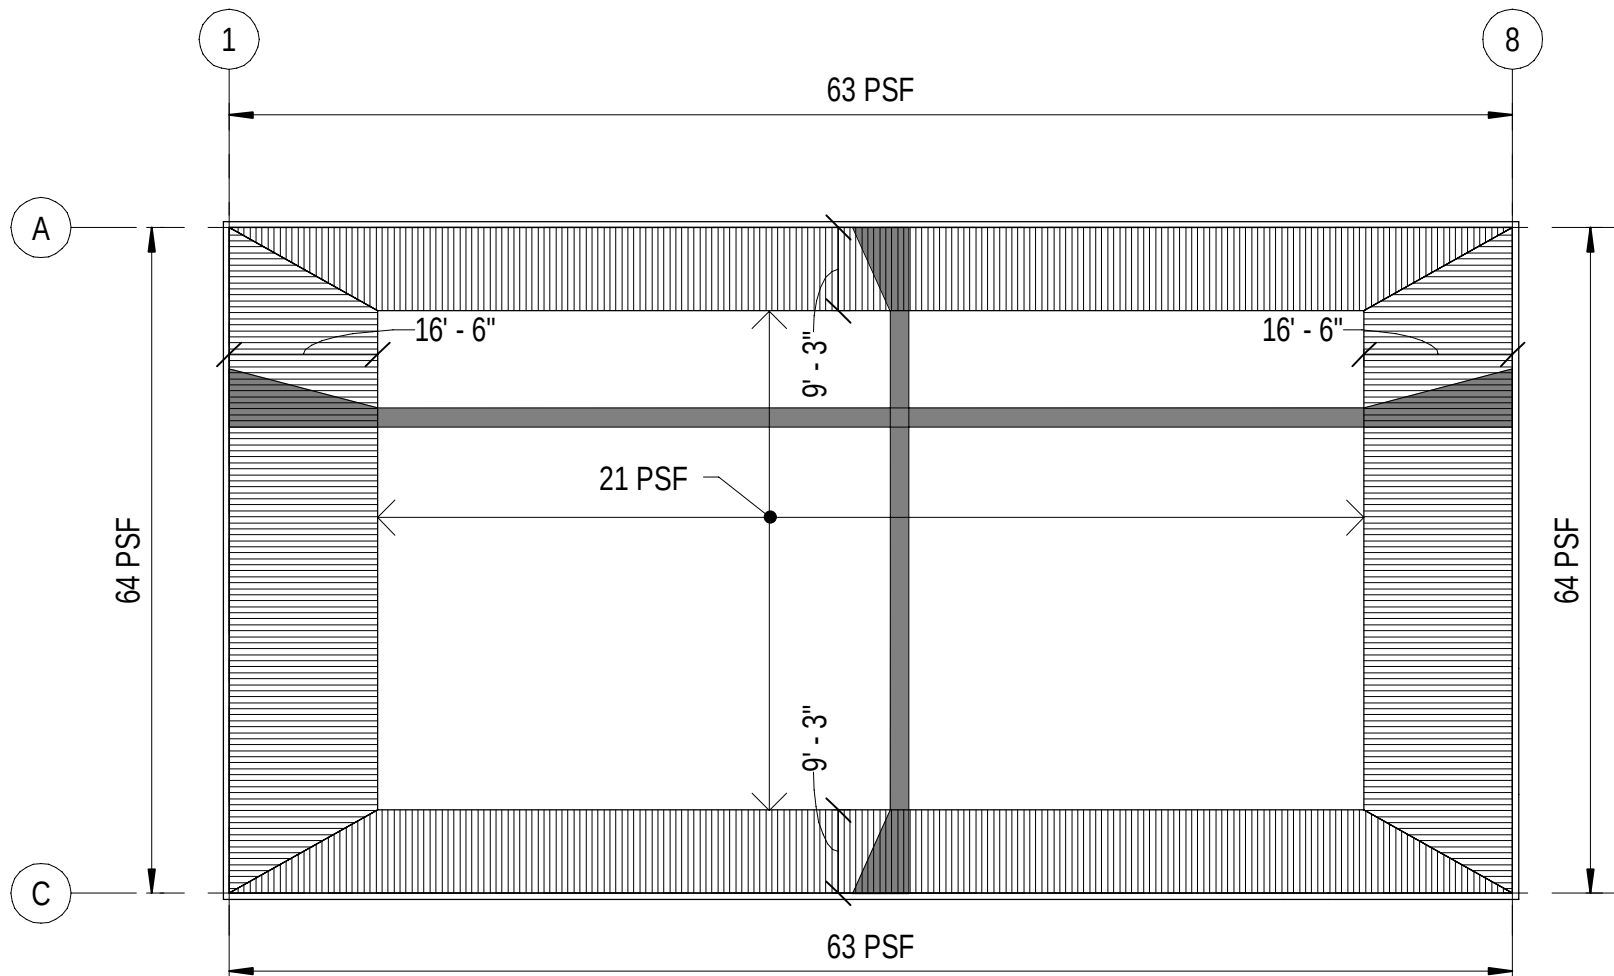


TABLE 1 - COMPONENTS & CLADDING WIND PRESSURE (PSF)

ZONE		EFFECTIVE WIND AREA (SF)					
		≤10	20	50	100	200	≥500
ROOF	1'	-34 / +16	-34 / +16	-34 / +16	-34 / +16	-29 / +16	-23 / +16
	1	-60 / +16	-56 / +16	-50 / +16	-46 / +16	-43 / +16	-37 / +16
	2	-79 / +16	-73 / +16	-67 / +16	-62 / +16	-57 / +16	-50 / +16
	3	-107 / +16	-97 / +16	-84 / +16	-73 / +16	-63 / +16	-50 / +16
WALLS	4w	-37 / +34	-36 / +33	-34 / +31	-32 / +29	-31 / +28	-29 / +26
	5w	-46 / +34	-43 / +33	-39 / +31	-36 / +29	-33 / +28	-29 / +26
PARAPET	4p	-81 / +35	-75 / +34	-69 / +32	-63 / +30	-58 / +28	-51 / +26
	5p	-110 / +35	-99 / +34	-86 / +32	-75 / +30	-65 / +28	-51 / +26

- FOR MEMBERS, THE EFFECTIVE WIND AREA IS THE SPAN LENGTH MULTIPLIED BY THE WIDTH, WHERE THE WIDTH EQUALS THE GREATER OF THE WIDTH TRIBUTARY TO THE MEMBER OR 1/3 THE SPAN LENGTH.
- FOR FASTENERS, THE EFFECTIVE WIND AREA MUST NOT BE TAKEN GREATER THAN THE AREA THAT IS TRIBUTARY TO AN INDIVIDUAL FASTENER.
- PRESSURES INDICATED ARE THE TOTAL APPLIED WIND PRESSURE AND INCLUDE BOTH THE INTERNAL AND EXTERNAL PRESSURES.
- WIND PRESSURES ARE FACTORED LOADS.
- POSITIVE VALUES INDICATE PRESSURE ACTING TOWARDS THE SURFACE AND NEGATIVE VALUES INDICATE PRESSURE ACTING AWAY FROM THE SURFACE.

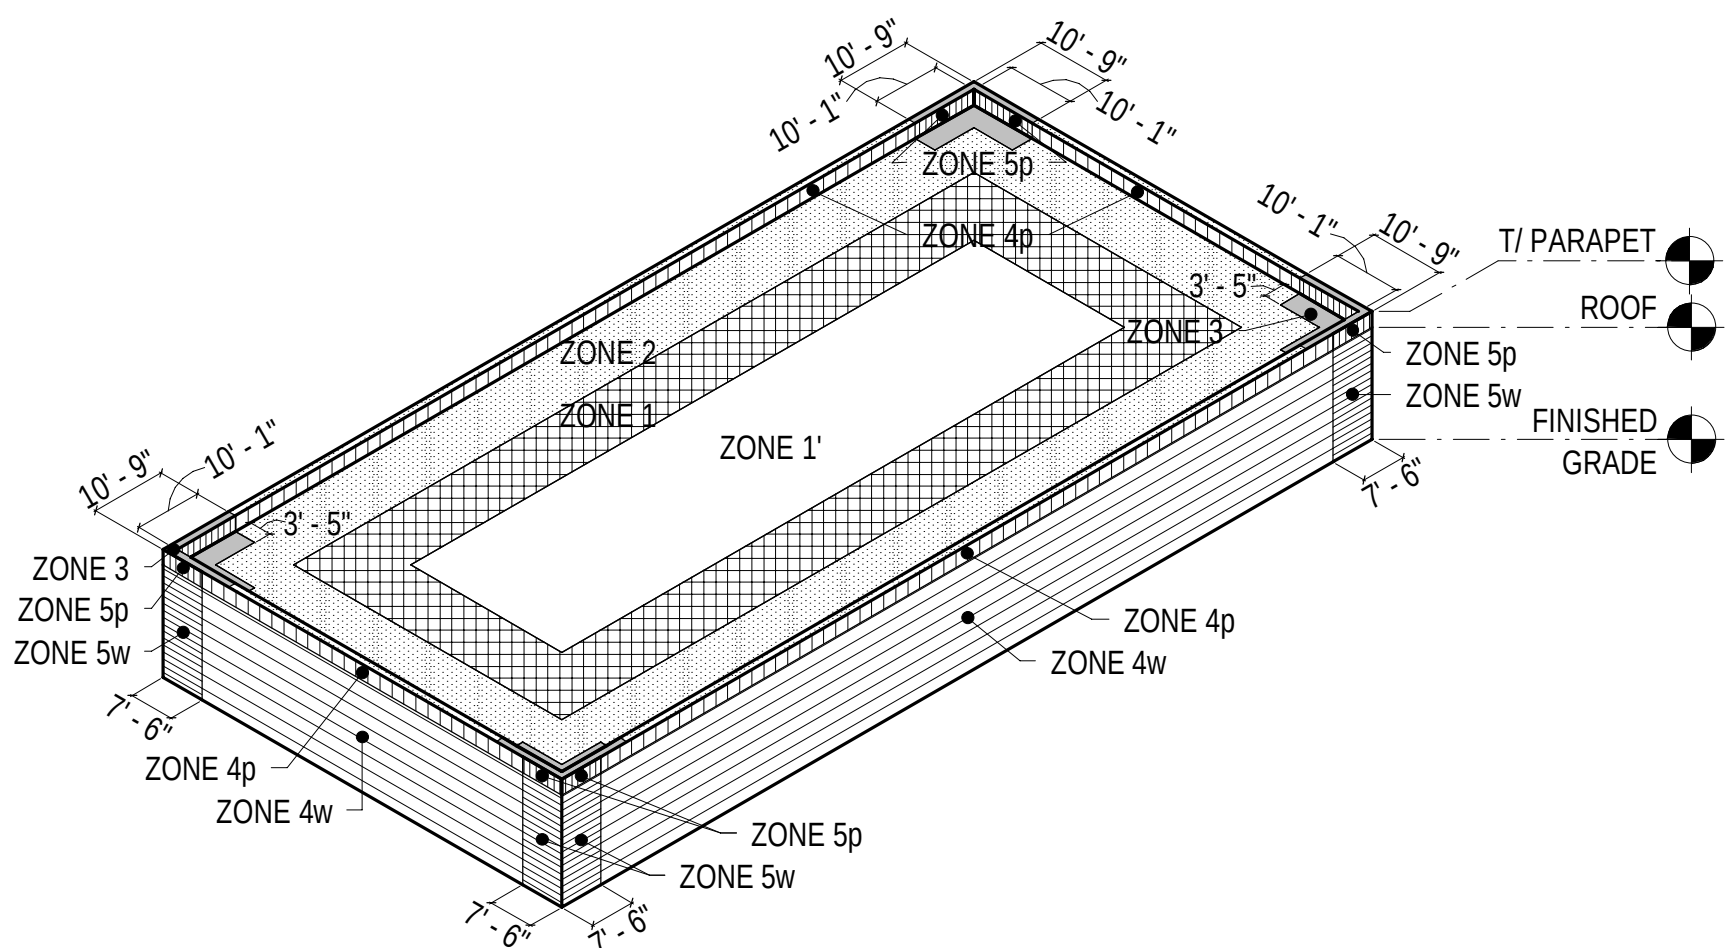

APPR

DATE

DESCRIPTION

SYM



Jacobs

1100 NORTH GLEBE ROAD
SUITE 500
ARLINGTON, VIRGINIA 22201
571.218.1000
FAX: 571.218.1600

APPROVED
AE INFO

FOR COMMANDER NAVFAC

ACTIVITY
APPROVED BY LCDR ELIZABETH
OLOKODE NAVFAC NLON READ
DIRECTOR NEW LONDON, GROTON, CT

SATISFACTORY TO DATE 05/27/2025

DES SK DRW SK CHK LP

PMID SMS/CWJ

BRANCH MANAGER NEK

CHIEF ENGINEER JMWJ

FIRE PROTECTION HPN

DEPARTMENT OF THE NAVY

NAVAL FACILITIES ENGINEERING SYSTEMS COMMAND

NAVAL FACILITIES ENGINEERING SYSTEMS COMMAND - MID-ATLANTIC

NAVAL STATION - NORFOLK, VA

NAVAL SUBMARINE BASE NEW LONDON

GROTON, CONNECTICUT

P-1102 WEAPONS MAGAZINE & ORDNANCE OPERATIONS FACILITY

OPERATIONS

DESIGN CRITERIA & LOADS

SCALE: AS NOTED

EPROJECT NO.: 1667770


CONSTR. CONTR. NO.

NAVFAC DRAWING NO.

12893957

SHEET 7 OF 140

6/20/2025 12:56:20 PM S-202
\\ac119d01\user\jfd\ZEL628\STRUBLDG-166770-S-BM_V21.rvt

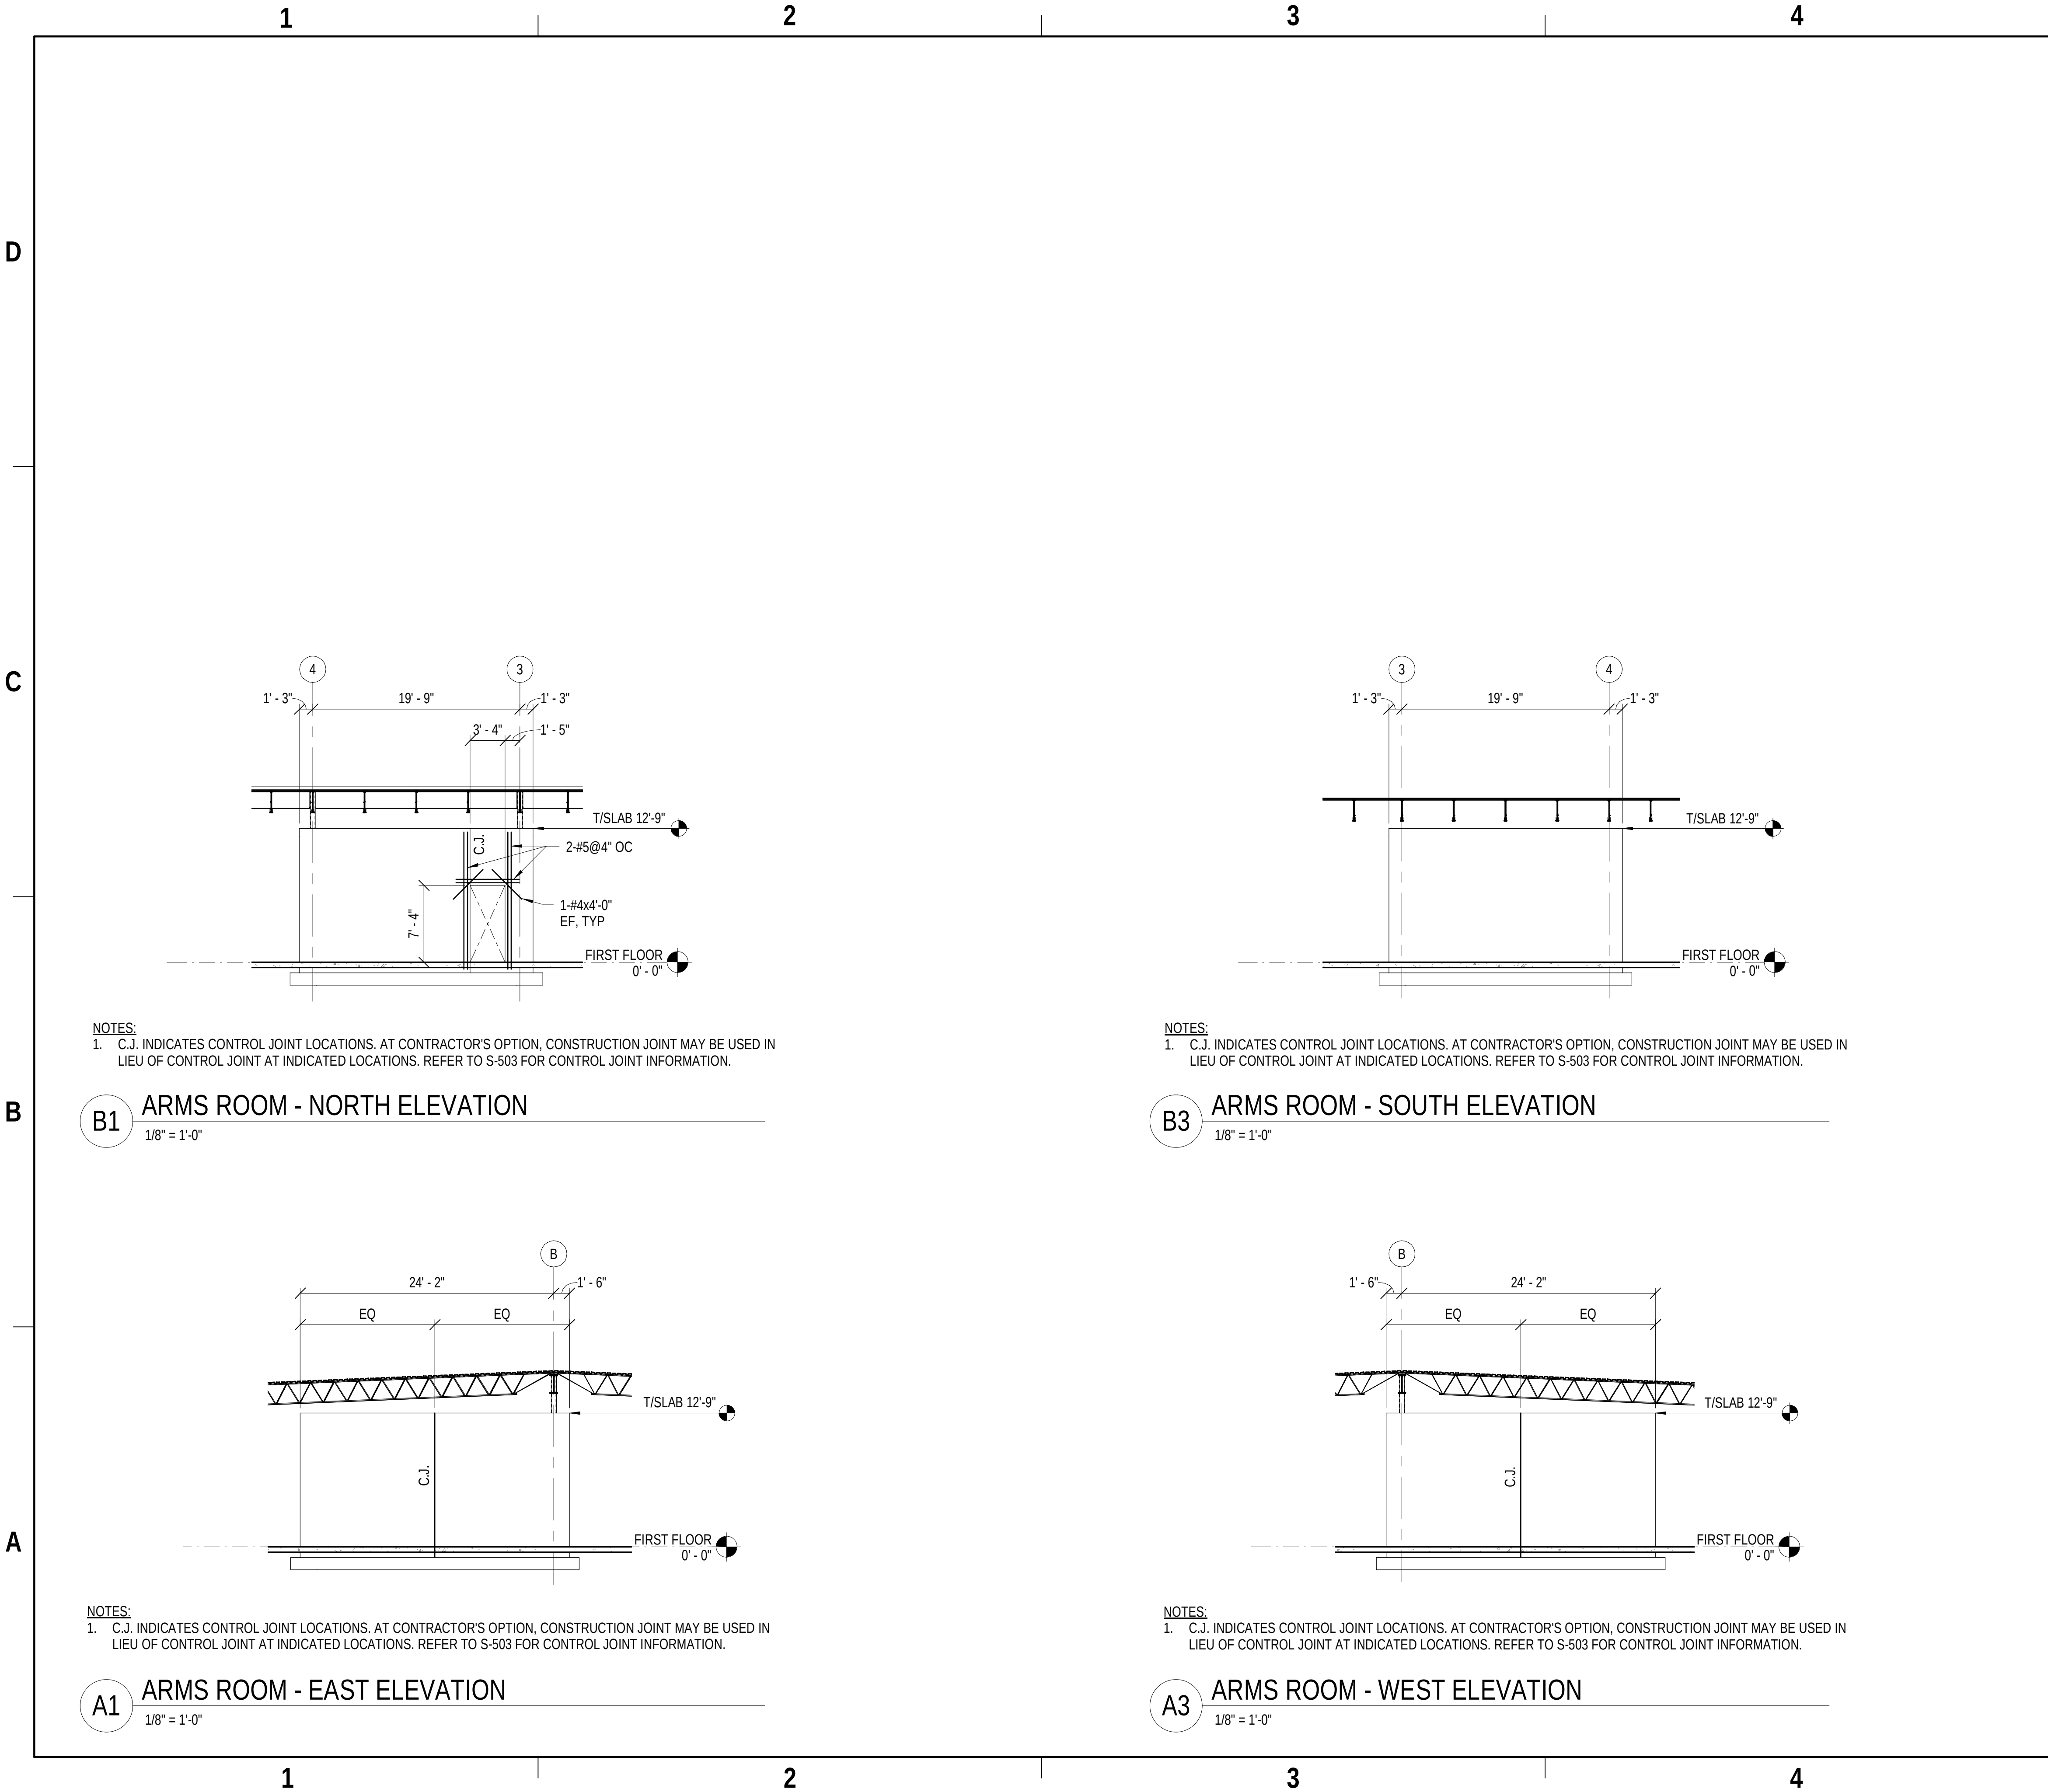

GENERAL SHEET NOTES

A. TOP OF FIRST FLOOR SLAB, REFERENCE DATUM, IS ELEVATION 0'-0". REFER TO CIVIL FOR THE ACTUAL FLOOR ELEVATION.

B. T/WALL FTG EL = [-2'-4"] UON.

C. T/COL FTG EL = [-1'-0"] UON.

D. REFER TO S-000 SERIES DRAWINGS FOR GENERAL NOTES, DESIGN LOADS AND ABBREVIATIONS.

E. REFER TO S-500 SERIES DRAWINGS FOR TYPICAL DETAILS.

F. "Fx" REFERS TO SPREAD FOOTING TYPE FOUNDATIONS AND "WFx" CONTINUOUS TYPE WALL FOUNDATIONS. REFER TO S-601 GEOMETRY AND REINFORCEMENT INFORMATION.

G. FOUNDATIONS MUST BE CENTERED ON ELEMENT BEING SUPPORTED UNLESS NOTED OTHERWISE.

H. REFER TO S-601 FOR SCHEDULES.

SHEET KEYNOTES

1100 NORTH GLEBE ROAD
SUITE 500
ARLINGTON, VIRGINIA 22201
571.218.1000
FAX: 571.218.1600

APPROVED				
FOR COMMANDER NAVFAC				
ACTIVITY APPROVED BY LCDR ELIZABETH CLOKODE NAVFAC NLON FEAD DIRECTOR NEW LONDON, GROTON, CT				
SATISFACTORY TO DATE 05/27/2025				
DES	JH	DRW	JT	CHK LP
PMOM SMS/CWJ				
BRANCH MANAGER NEK				
CHIEF ENGINEER JMWJ				
FIRE PROTECTION HPN				

DEPARTMENT OF THE NAVY
NAVAL FACILITIES ENGINEERING SYSTEMS COMMAND - MID-ATLANTIC
NAVAL STATION - NORFOLK, VA
MID-ATLANTIC
NAVAL SUBMARINE BASE NEW LONDON
GROTON, CONNECTICUT
P-1102 WEAPONS MAGAZINE & ORDNANCE OPERATIONS FACILITY
OPERATIONS
BUILDING ELEVATIONS

SCALE: AS NOTED

EPROJECT NO.: 1667770

CONSTR. CONTR. NO.


NAVFAC DRAWING NO. 12893962



SHEET 12 OF 140


S-202




- NOTES:
1. REFER TO CIVIL DRAWINGS FOR DUMPSTER ENCLOSURE LOCATION.
 2. "WFx" REFERS TO CONTINUOUS TYPE WALL FOUNDATIONS. REFER TO S-601 FOR GEOMETRY AND REINFORCEMENT INFORMATION.

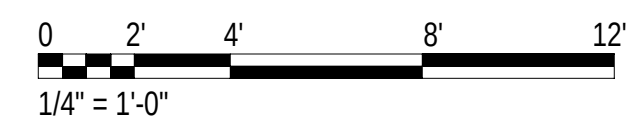


 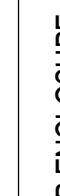DATE	SYNOPSIS DESCRIPTION	APPROVED
	SWM	 NAVFAC  SWM SEAL
 Jacobs 1100 NORTH GLEBE ROAD SUITE 500 ARLINGTON, VIRGINIA 22201 571.218.1000 FAX: 571.218.1600 AVE INFO		
APPROVED		
FOR COMMANDER NAVFAC ACTIVITY APPROVED BY LCDR ELIZABETH OLOKODE NAVFAC NILON HEAD DIRECTOR NEW LONDON, GROTON, CT SATISFACTORY TO DATE 05/27/2025 DES JH DRW JT CHK LP PMOM SMS/CWJ BRANCH MANAGER NEK CHIEF ENGINEER JWJ FIRE PROTECTION HPN		
DEPARTMENT OF THE NAVY	NAVAFACILITIES ENGINEERING SYSTEMS COMMAND - MID-ATLANTIC	P-1102 WEAPONS MAGAZINE & ORDNANCE OPERATIONS FACILITY
NAVAL SUBMARINE BASE NEW LONDON	GROTON, CONNECTICUT	DUMPSSTER ENCLOSURE
SCALE: AS NOTED PROJECT NO.: 1667770 CONSTR. CONTR. NO.		
NAVFAC DRAWING NO. 12893963		
SHEET 13	OF 36	140
S-401		

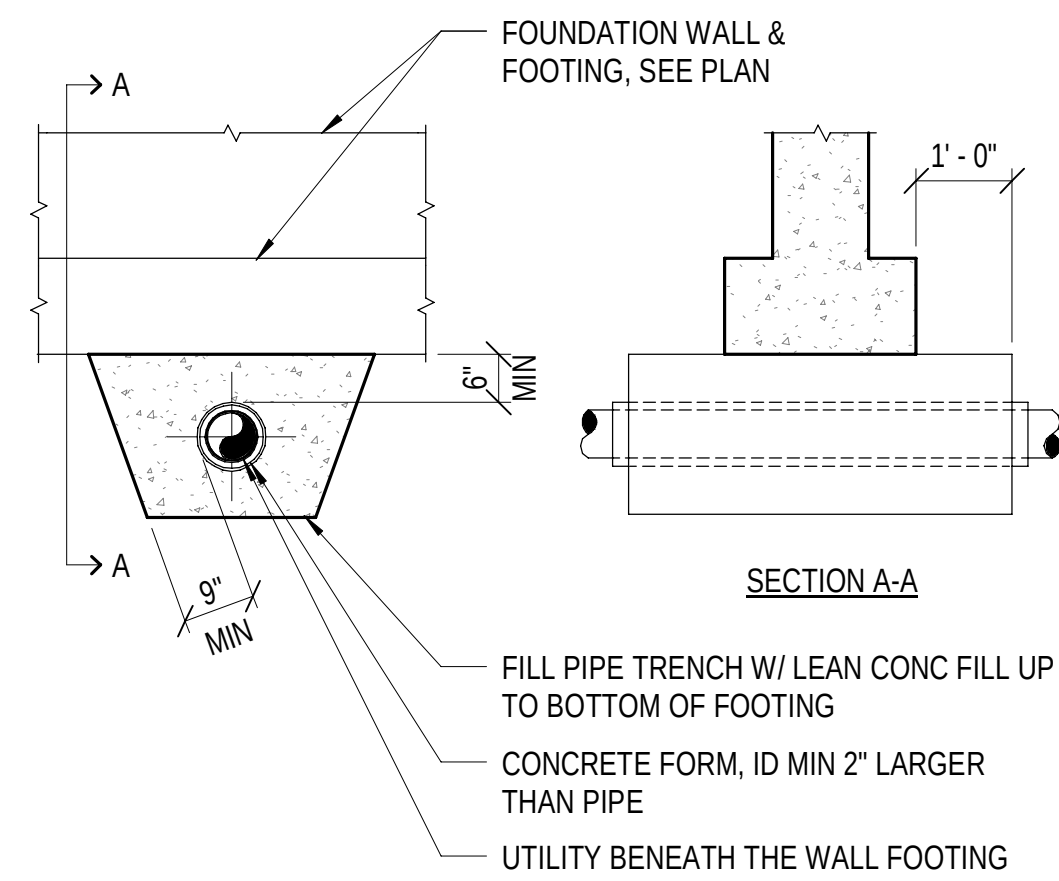

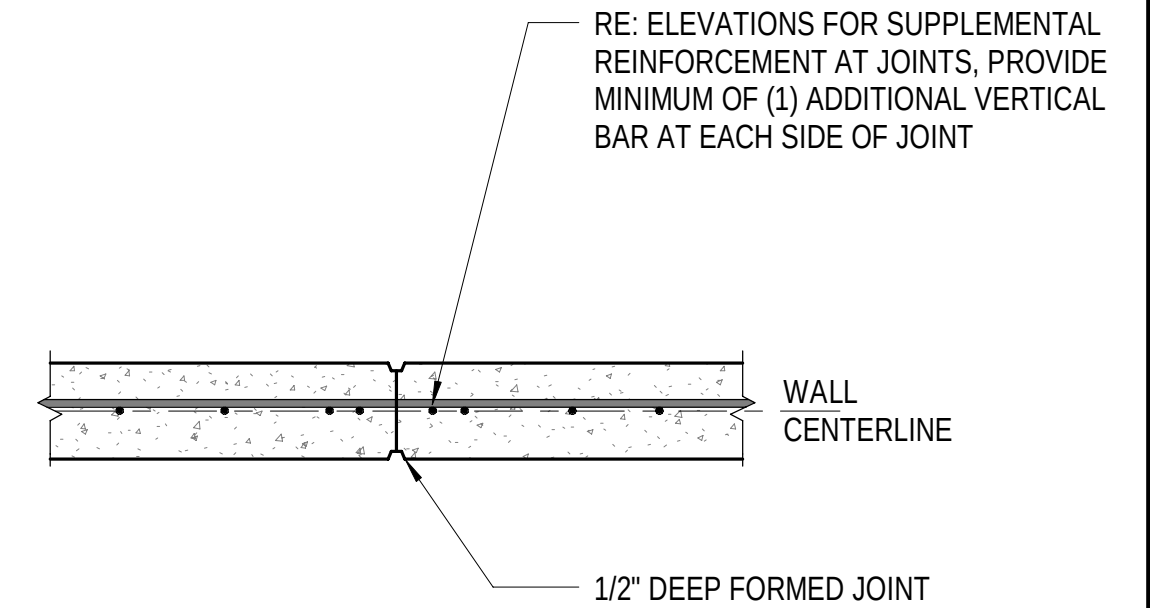


C4 CONCRETE WALL CONSTRUCTION JOINT

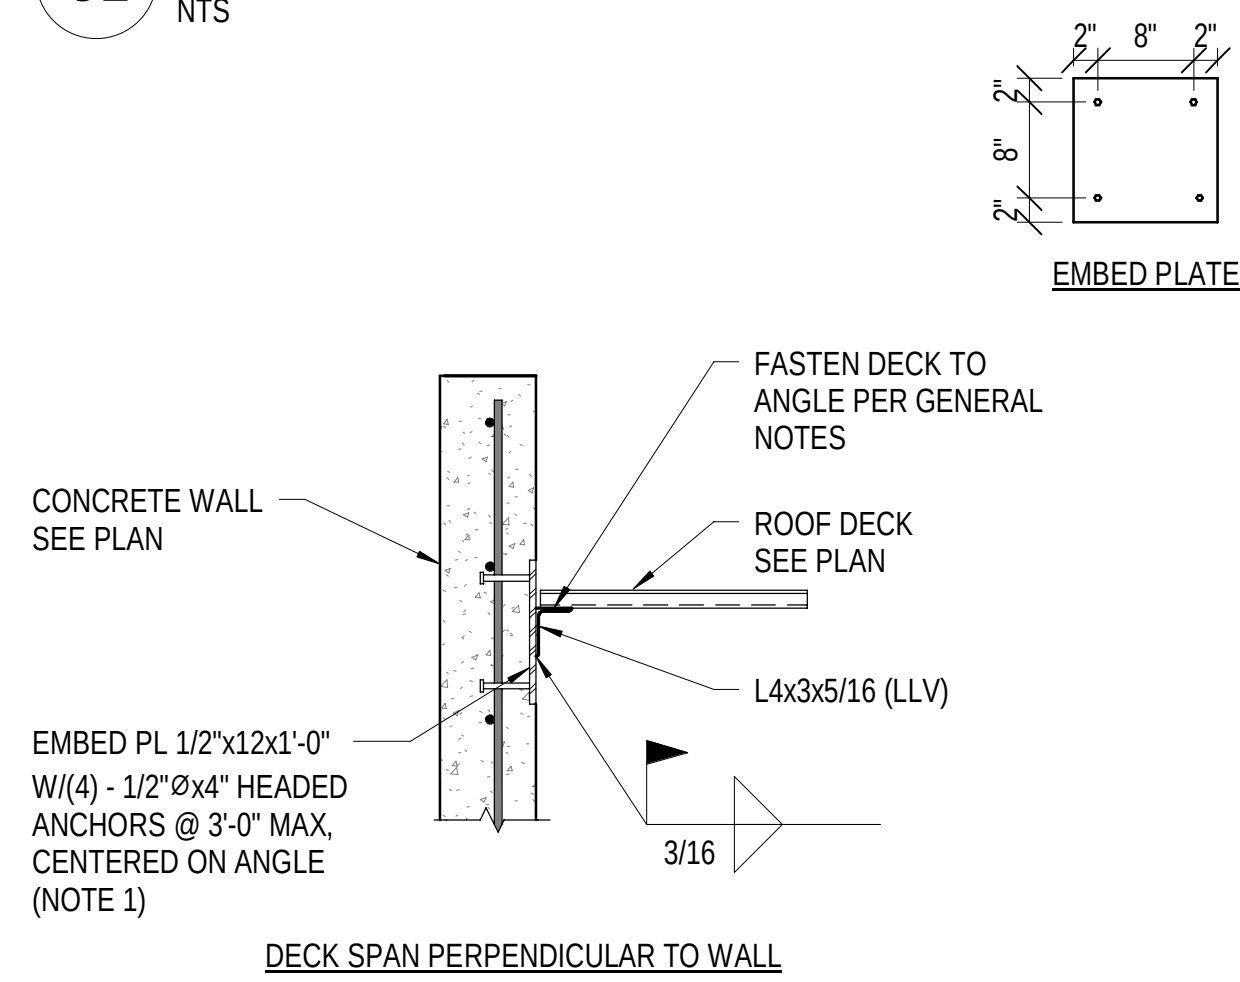


- NOTES:**
1. ADJUST LAYOUT OF DECK SUPPORT EMBEDS WITHOUT EXCEEDING MAXIMUM INDICATED SPACING TO PROVIDED CLEARANCE WITH BEAM SUPPORT EMBED PER B4/S-510.

B2 DECK END BEARING ON CONC WALL
NTS

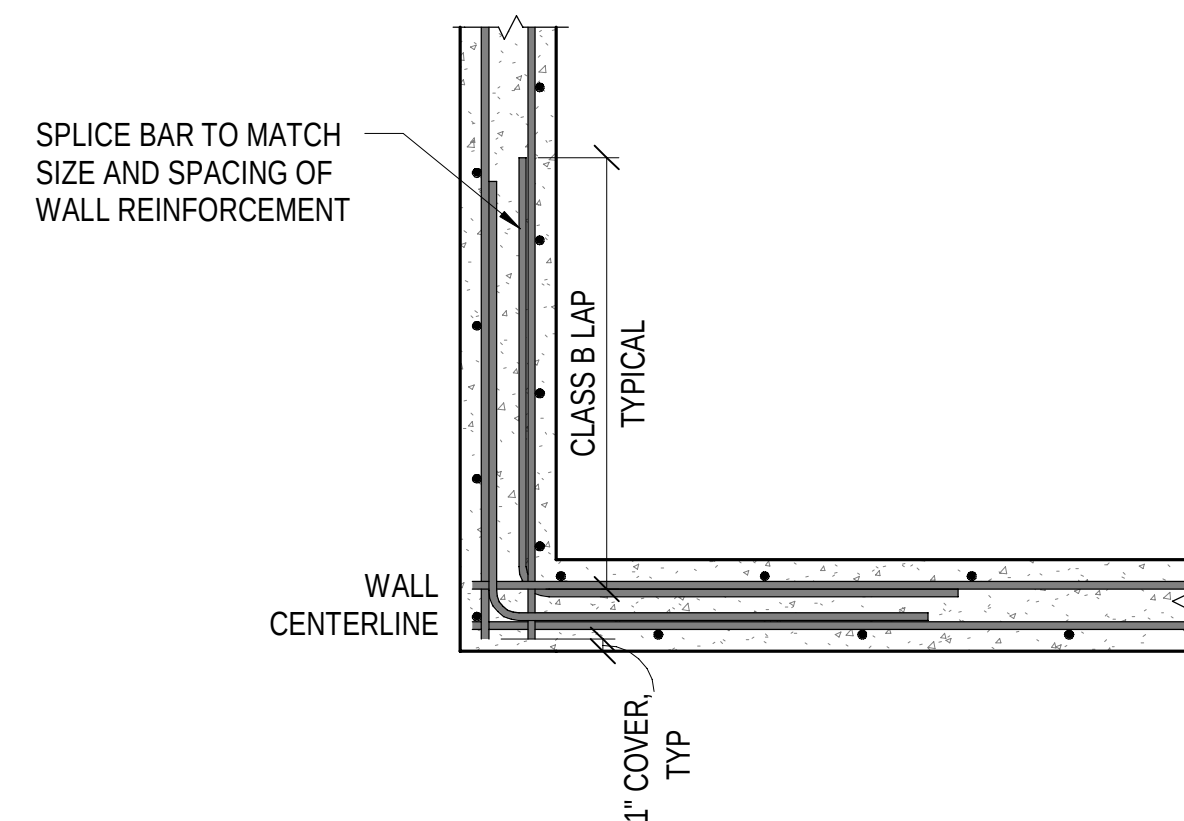


A2 ARMS ROOM WALL CORNER REINFORCEMENT

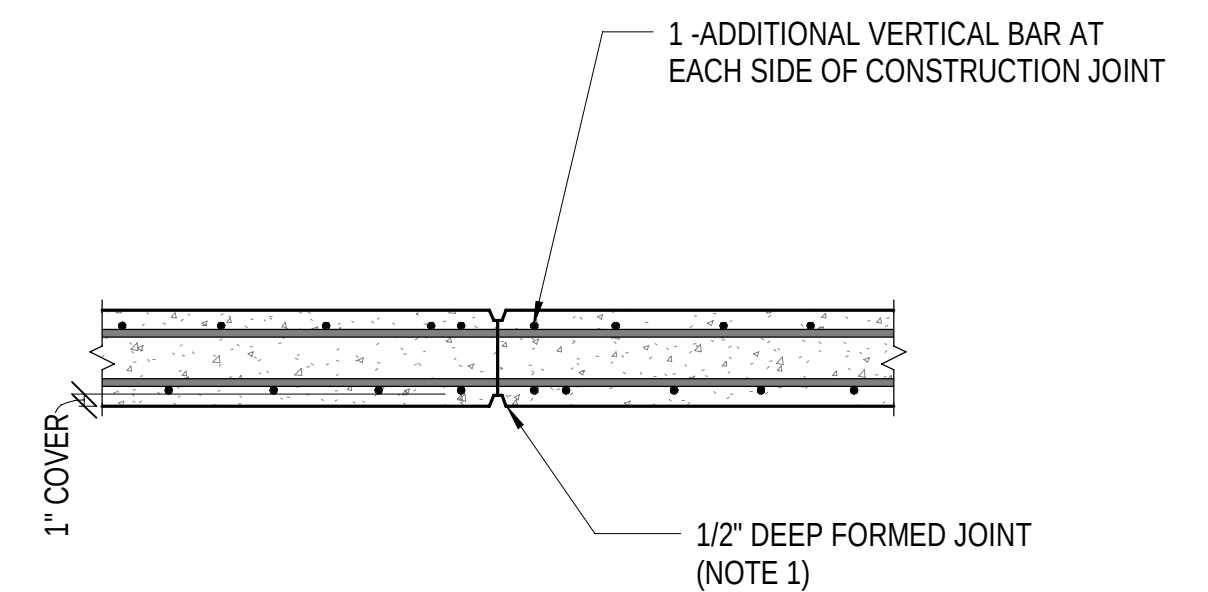

**CONCRETE WALL CONSTRUCTION JOINT
AT ARMS ROOM**


6/21/2025 2:21:53 AM S-510
\\ac1v90\\d\\enr\\FDZ\\E1628\\STR\\B\\LDG-166770-S-BM_V21.rvt

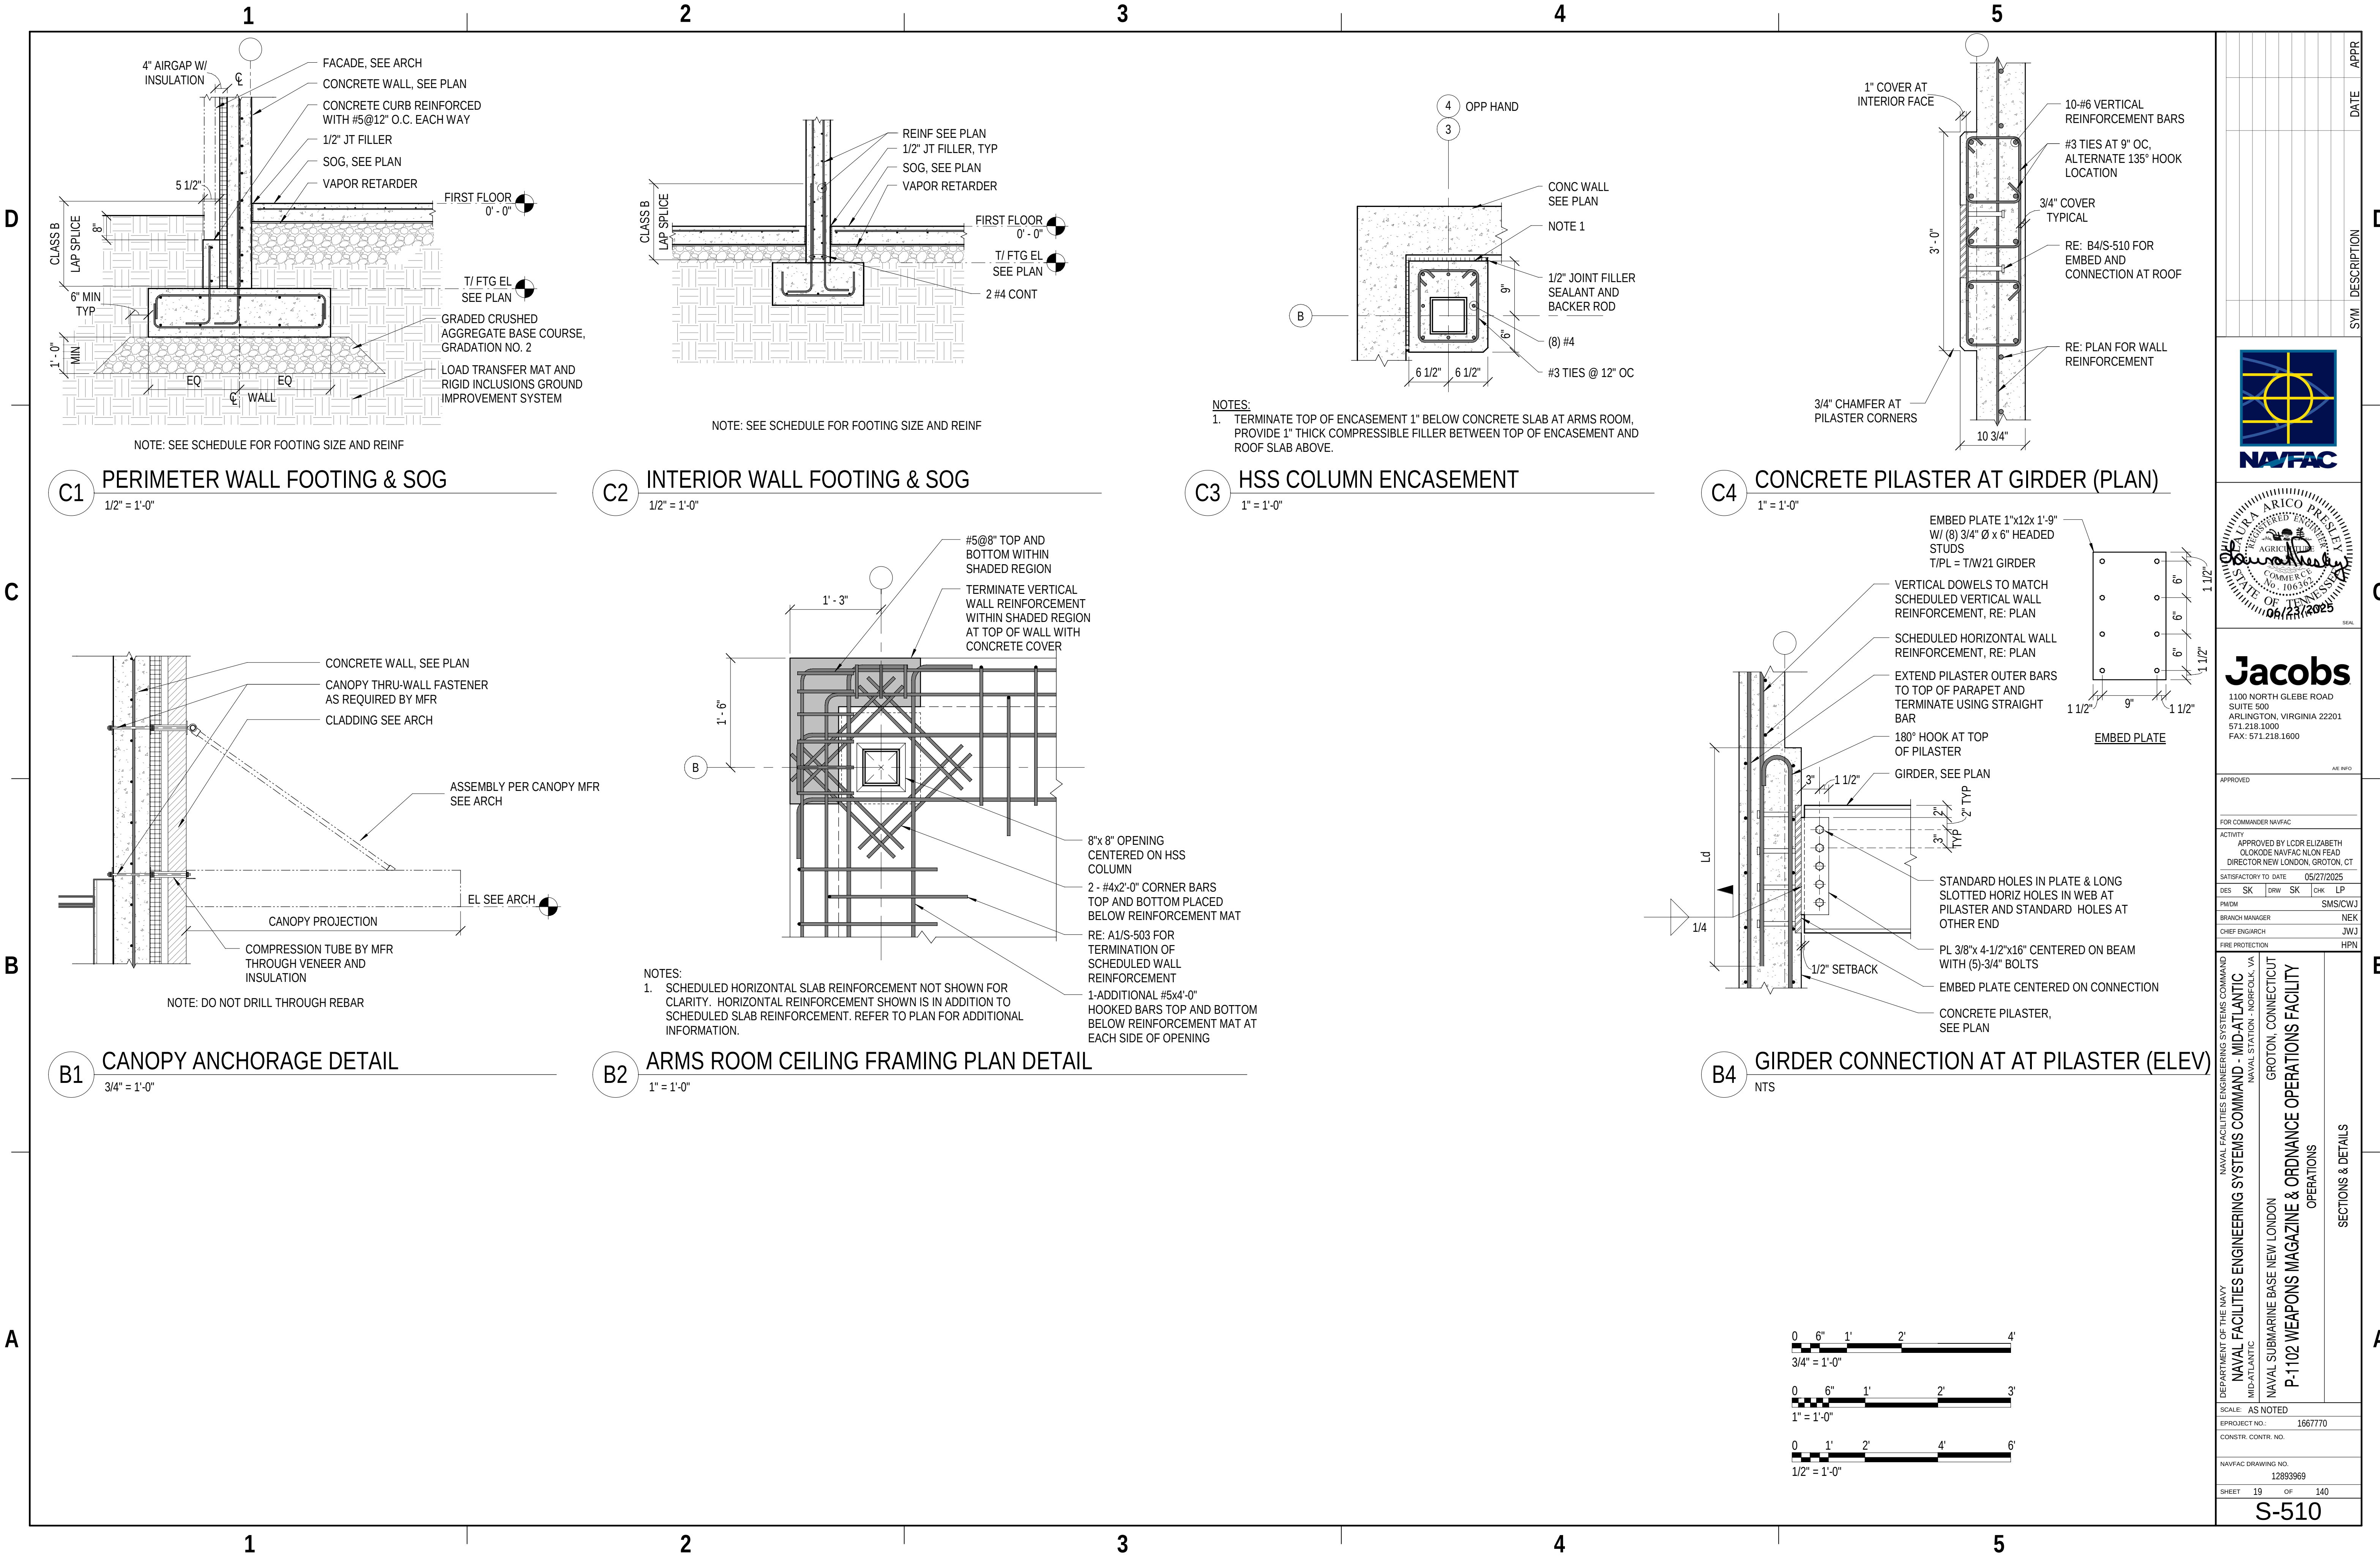


S-510

6/21/2025 2:21:53 AM
\\ac1v90\\d\\enr\\FDZ\\E1628\\STR\\B\\LDG-166770-S-BM_V21.rvt

5

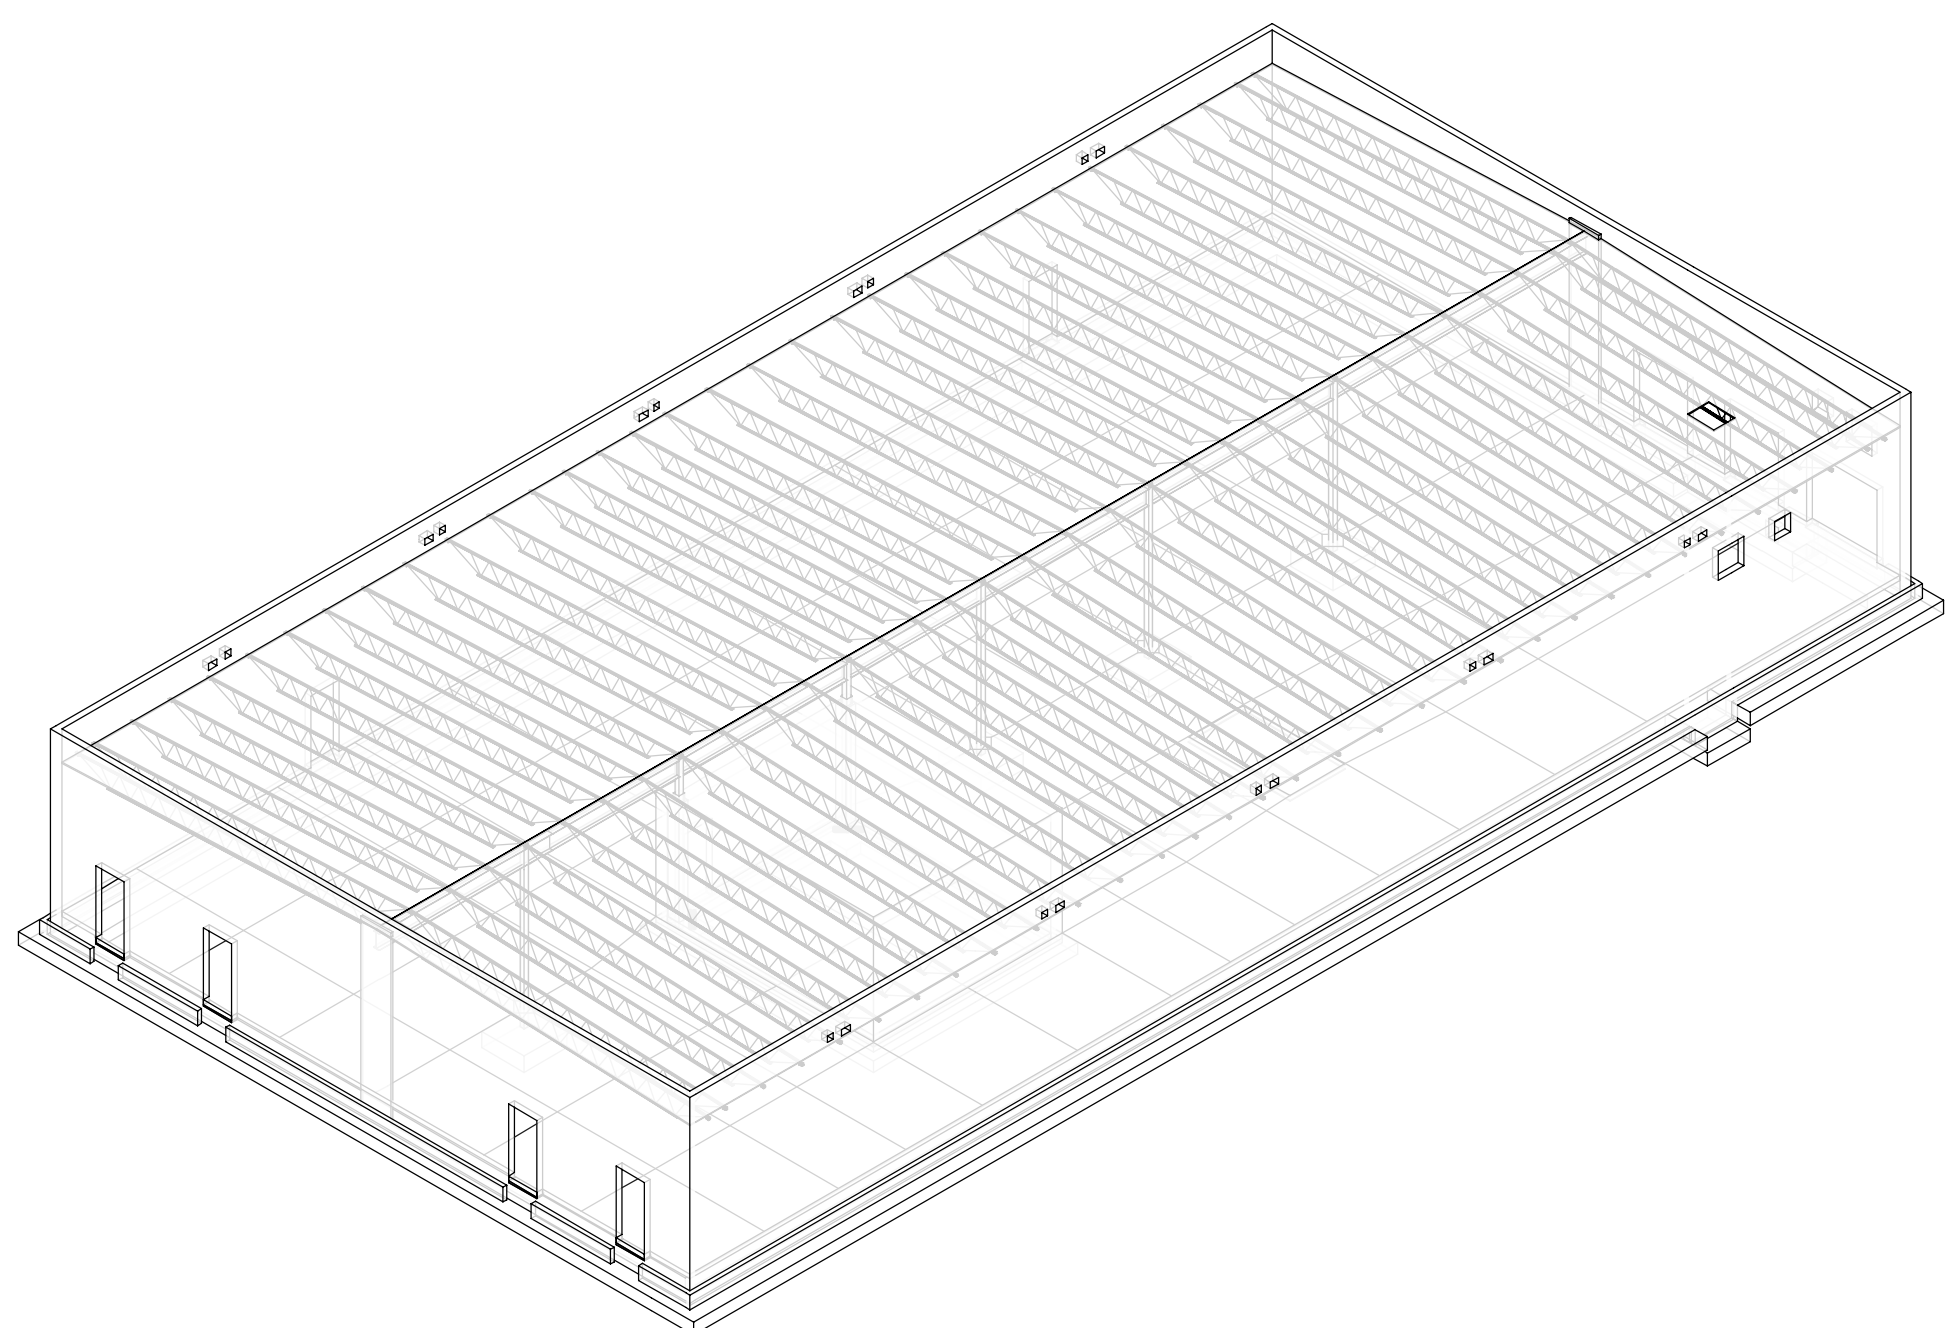

C3 SOUTHWEST ISOMETRIC

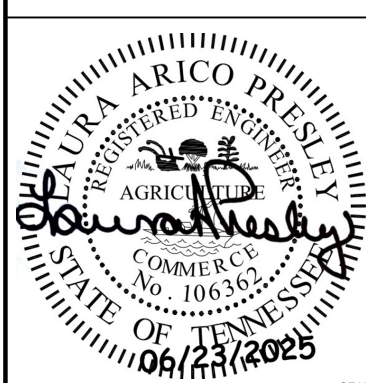

APPROVED				AE INFO	
FOR COMMANDER NAVFAC					
ACTIVITY					
APPROVED BY LCDR ELIZABETH OLOKODE NAVFAC NLON FEAD DIRECTOR NEW LONDON, GROTON, CT					
SATISFACTORY TO DATE				05/27/2025	
DES	JH	DRW	JT	CHK	LP
PMIDM				SMS/CW	
BRANCH MANAGER				NE	
CHIEF ENG/ARCH				JW	
FIRE PROTECTION				HP	


SCALE:	AS NOTED	
EPROJECT NO.:	1667770	
CONSTR. CONTR. NO.		
NAVFAC DRAWING NO.		
12893971		
SHEET	21	OF 140
S-901		

NOTE: ISOMETRICS ARE PROVIDED FOR REFERENCE ONLY. DO NOT SCALE FOR DIMENSIONS OR USE FOR CONSTRUCTION.

6/20/2025 10:32:16 AM
\\b1c1950\\l\\e\\p\\FDZ\\E1628\\AFCH\\B\\DG-1667770-A-B\\M.rvt


A-003

A

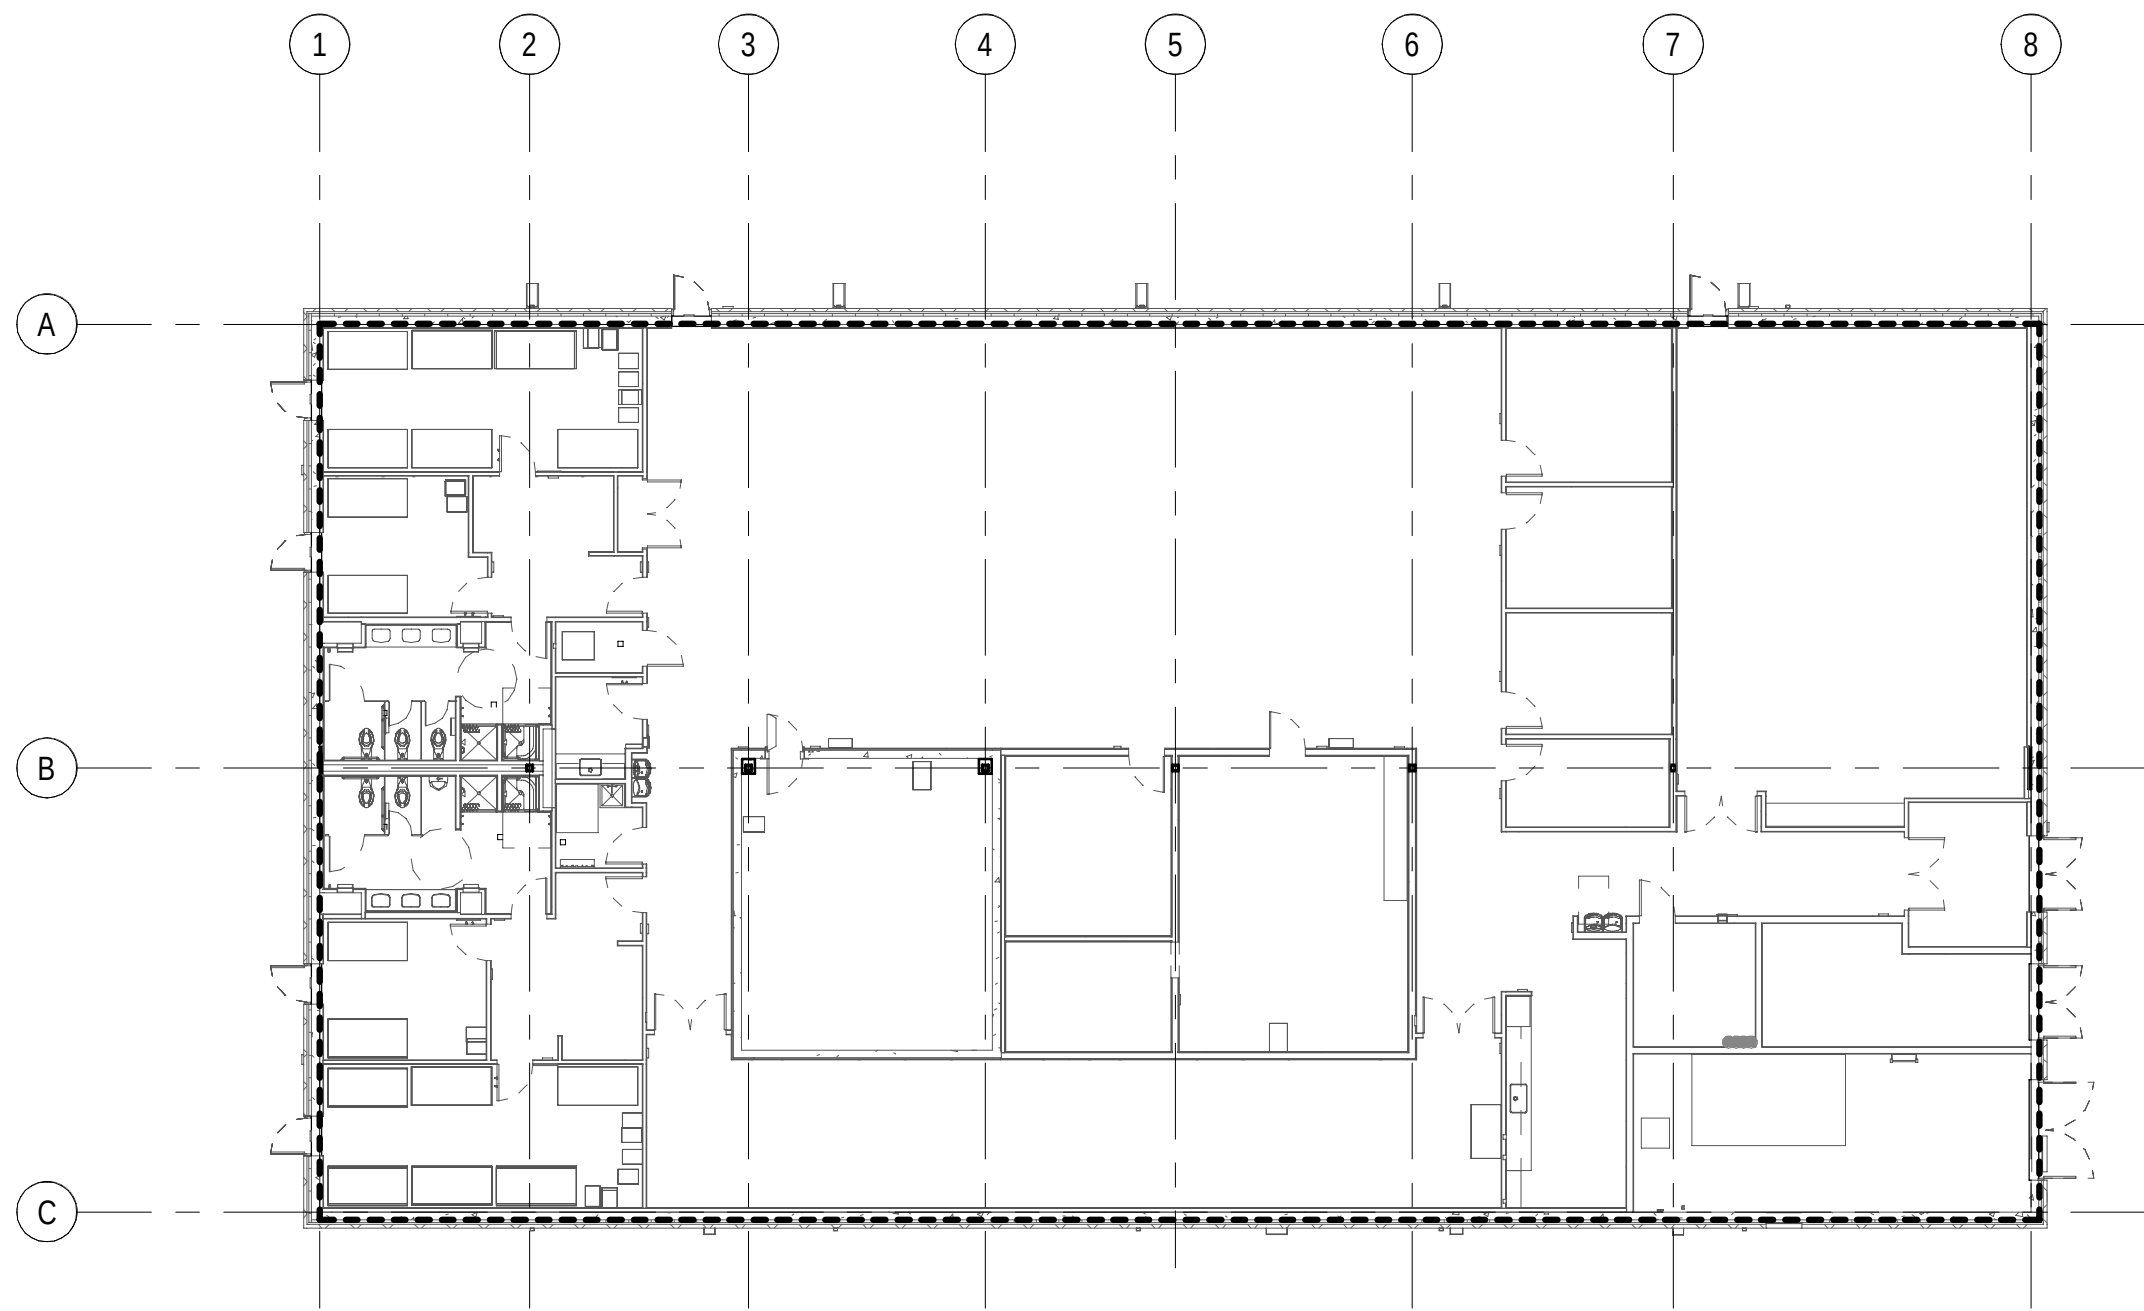


A1 FIRST FLOOR PLAN
1/16" = 1'-0"

B

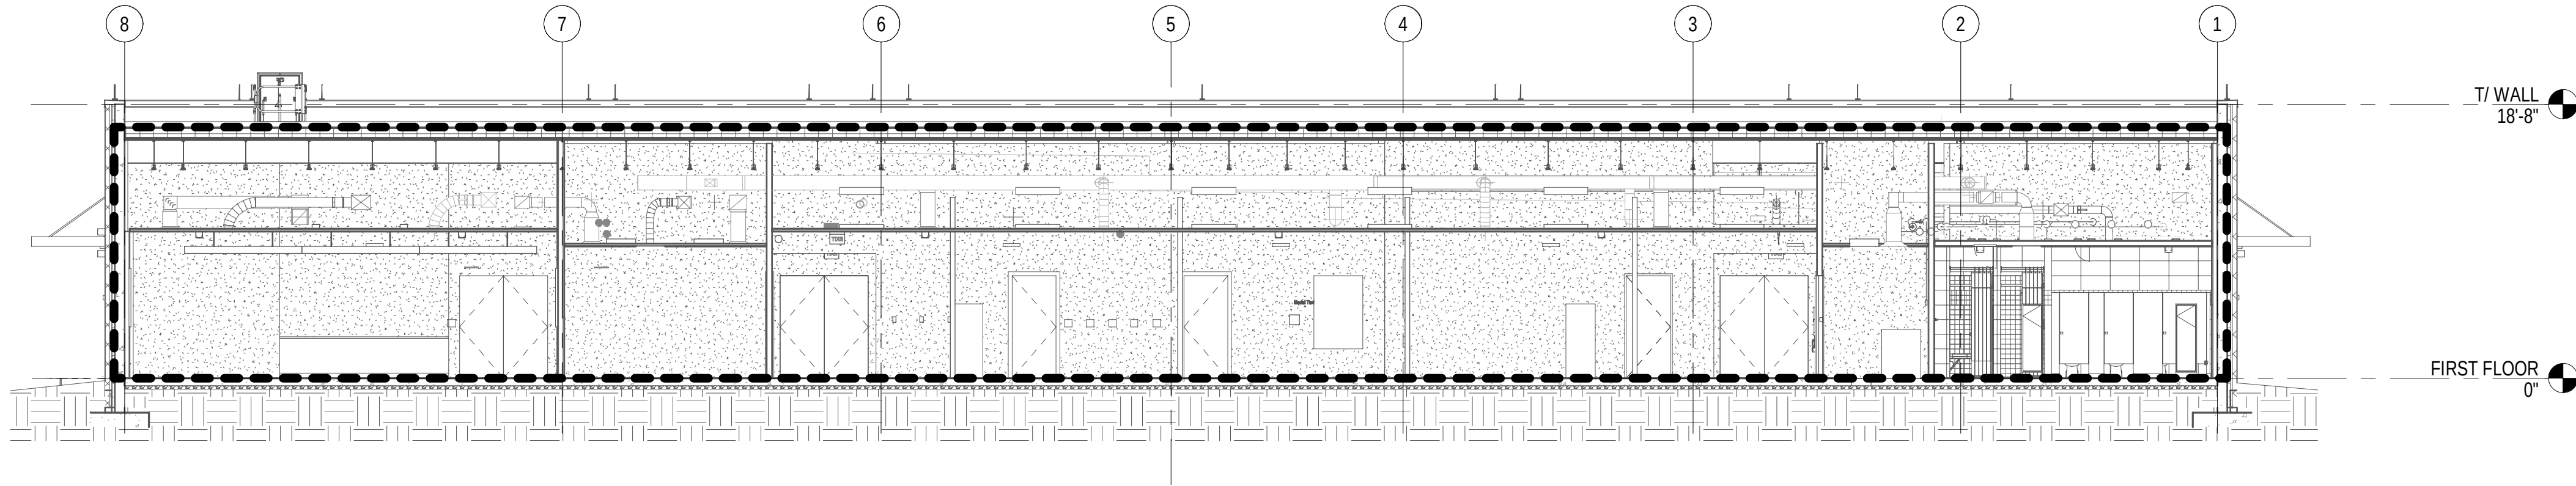

B1 EAST-WEST BUILDING SECTION
1/8" = 1'-0" (A-102)

C

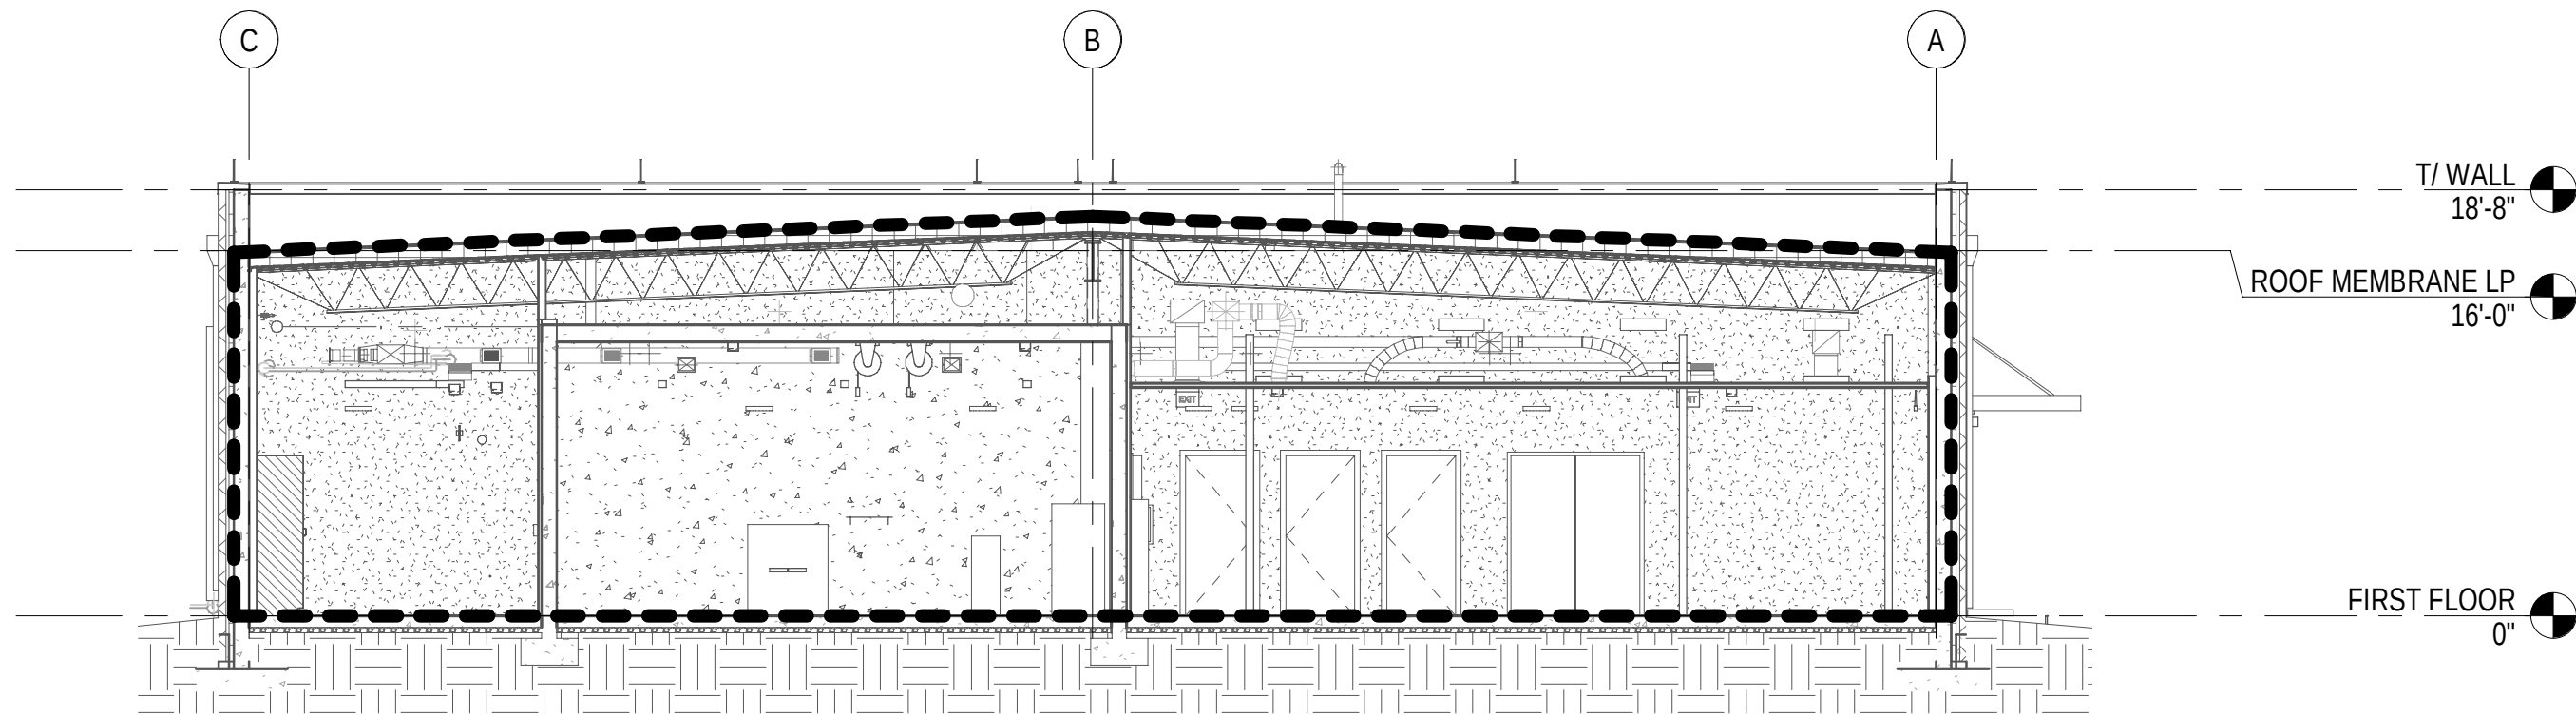

C1 NORTH-SOUTH BUILDING SECTION
1/8" = 1'-0"

D

GENERAL SHEET NOTES

- PROVIDE A COMPLETE PRELIMINARY DOCUMENTS REVIEW AND BUILDING ENVELOPE ASSESSMENT BY A PROFESSIONAL CERTIFIED ABAA AUDITOR. REFER TO SPEC SECTION 07 27 10.00 10
- CONCRETE FLOOR IS AN AIR BARRIER AT GRADE AND AS SUCH, CONCRETE FLOOR PENETRATIONS MUST BE SEALED.
- SEAL (CAULK) MECHANICAL, ELECTRICAL, FIRE ALARM BOXES AND FIRE ALARM DEVICES.
 - PROVIDE NON-COMBUSTIBLE INSULATION IN WALL AROUND BOXES, NON-COMBUSTIBLE INSULATION (OR CAULK) INSIDE CONDUIT AFTER WIRES ARE PULLED AT ELECTRICAL BOXES AND FIRE ALARM DEVICES FOR AIR TIGHT SEAL.
 - WHERE THERE IS NOT SUFFICIENT ACCESS TO SEAL THE BACK OF THE ELECTRICAL BOXES, USE HIGH PRESSURE DUCT SEALER TO PRESSURE SENSITIVE FOIL (FSK) DUCT TAPE FOR AIR TIGHT SEAL.
- IF AIR BARRIER ENVELOPE ZONES ARE ADJUSTED, GOVERNMENT APPROVAL IS REQUIRED FOR DEVIATIONS TO AIR BARRIER ZONES.
- THE AIR BARRIER MUST BE CONTIGUOUS AND CONNECTED ACROSS SURFACES OF THE ENCLOSED AIR BARRIER ENVELOPE INDICATED.
- PROVIDE AIR BARRIER TRANSITION MEMBRANE BETWEEN ADJACENT AIR BARRIER SYSTEMS. TRANSITION AIR BARRIER MEMBRANE MUST BE COMPATIBLE WITH BOTH AIR BARRIER MEMBRANES.
- PROVIDE A FLEXIBLE AIR BARRIER MEMBRANE BETWEEN BUILDING COMPONENTS WITH VARYING ANTICIPATED MOVEMENT AS A RESULT OF BUT NOT LIMITED TO DEFLECTION, THERMAL EXPANSION AND CONTRACTION, OR OTHER FACTORS ACTING UPON THE BUILDING JOINTS.
- REFER TO SPEC SECTIONS 07 05 23, 07 27 10.00 10, 07 27 19.01 & 07 27 26 FOR ADDITIONAL AIR BARRIER RELATED INFORMATION.

LEGEND

----- AIR BARRIER LOCATION

AIR BARRIER SQUARE FOOTAGE

AREA	SQ/FT
NORTH ELEVATION	2,759
SOUTH ELEVATION	2,759
EAST ELEVATION	1,456
WEST ELEVATION	1,456
FIRST FLOOR	11,142
ROOF	11,142

0 8' 16' 32' 48'
1/16" = 1'-0"

0 4' 8' 16' 24'
1/8" = 1'-0"

DATE	APPR
SYM	DESCRIPTION



Jacobs

1100 NORTH GLEBE ROAD
SUITE 500
ARLINGTON, VIRGINIA 22201
571.218.1000
FAX: 571.218.1600

APPROVED

FOR COMMANDER NAVFAC

ACTIVITY APPROVED BY LCDR ELIZABETH
CLOKODE NAVFAC NLON FEAD
DIRECTOR NEW LONDON, GROTON, CT

SATISFACTORY TO DATE 05/27/2025

DES PS DRW PS CHK WS

PMOM SMSI CWJ

BRANCH MANAGER DJD

CHIEF ENGINEER JWJ

FIRE PROTECTION HPN

NAVAL FACILITIES ENGINEERING SYSTEMS COMMAND - MID-ATLANTIC

NAVAL STATION - NORFOLK, VA

NAVAL SUBMARINE BASE NEW LONDON

GROTON, CONNECTICUT

P-1102 WEAPONS MAGAZINE & ORDNANCE OPERATIONS FACILITY

OPERATIONS

ARCHITECTURAL AIR BARRIER INFORMATION

A-003


SCALE: AS NOTED

EPROJECT NO.: 1667770

CONSTR. CONTR. NO.

NAVFAC DRAWING NO. 12893974

SHEET 24 OF 140

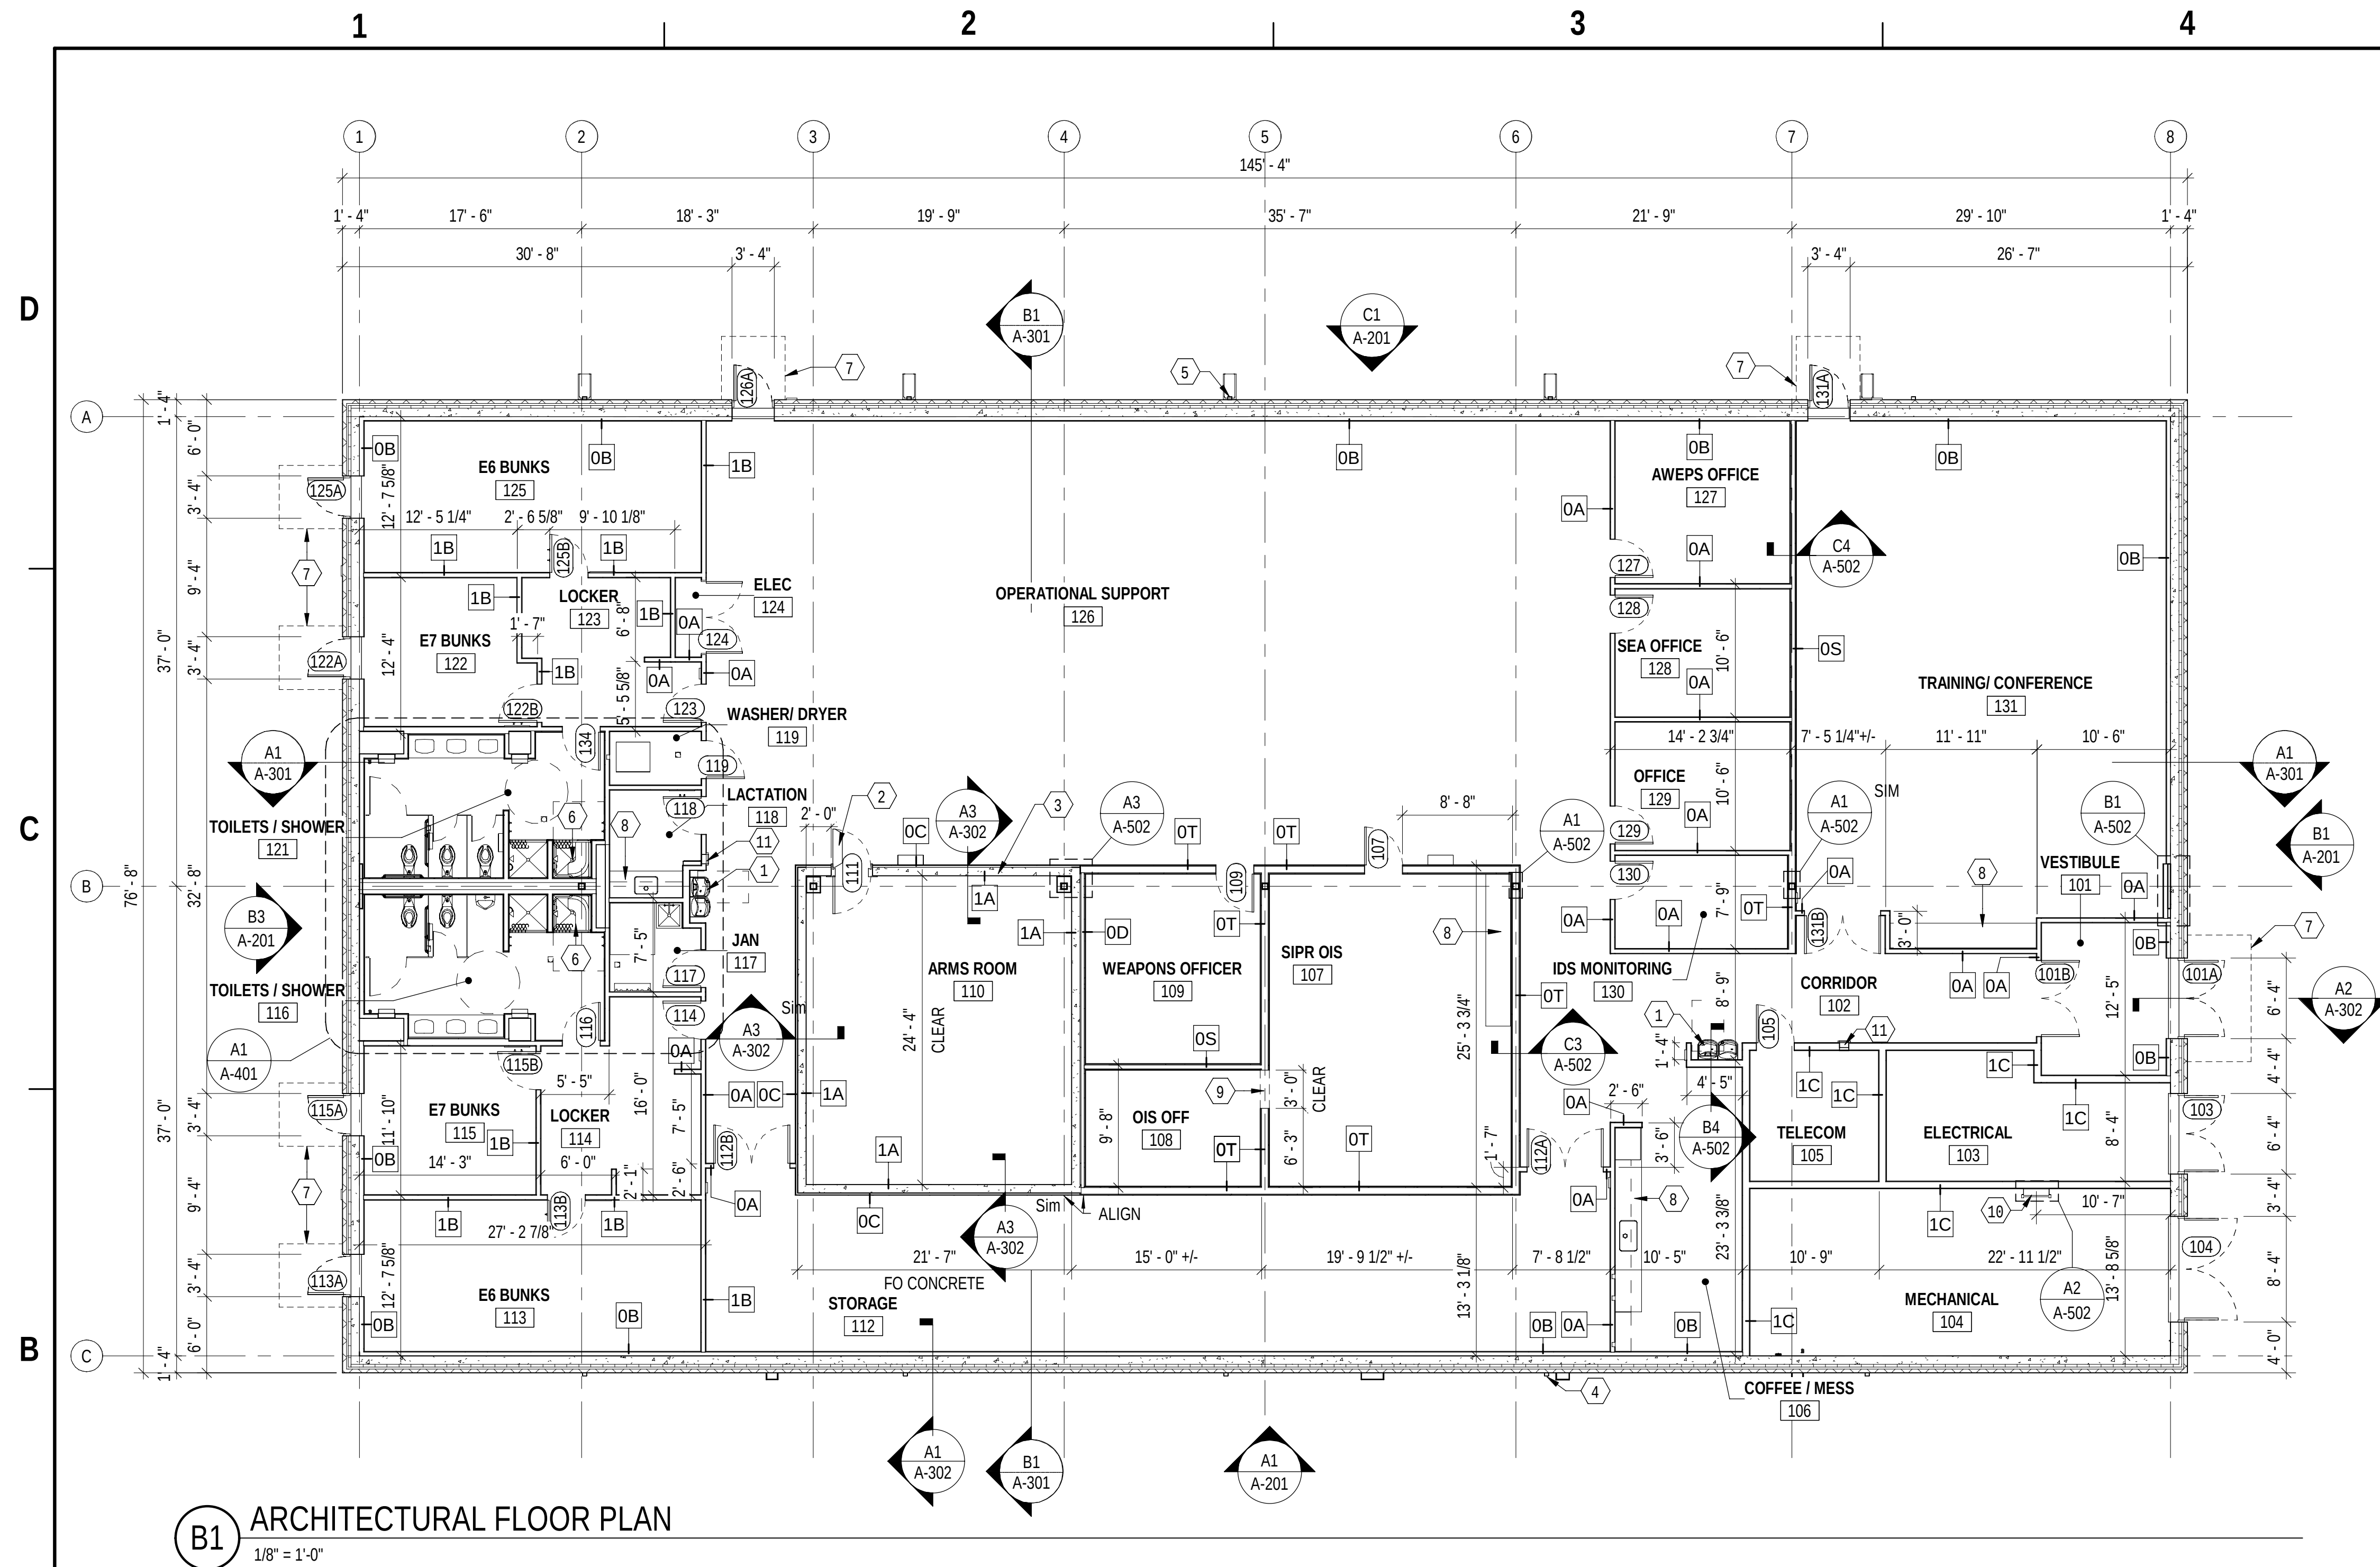

GENERAL SHEET NOTES

- A. LOCATE EDGE OF DOOR JAMBS 6" OFF THE FINISHED FACE OF ADJACENT GYPSUM BOARD PARTITION UNLESS OTHERWISE NOTED.
- B. EXTERIOR DIMENSIONS ARE FROM CONCRETE AND ROUGH OPENINGS. DIMENSION STRINGS ON ENDS OF BUILDING ARE TO OUTSIDE FINISH MATERIAL.
- C. INTERIOR DIMENSIONS ARE FROM METAL STUD TO METAL STUD, OR CONCRETE UNLESS NOTED OTHERWISE.
- D. DIFFERENT FLOOR FINISH MATERIALS MUST MEET UNDER THE CENTERLINES OF DOORS UNLESS OTHERWISE NOTED.
- E. PARTITION / WALL MOUNTED EQUIPMENT NOT INDICATED ON THE DRAWINGS MUST BE COORDINATED WITH THE COR PRIOR TO INSTALLATION.
- F. INSTALLED FLOOR FINISHES MUST BE PROTECTED FROM DIRECT CONTACT BY MEANS OF COVERING FOR DURATION OF CONSTRUCTION.
- G. CORRIDORS, BREAK, OPERATIONAL SUPPORT, AND TRAINING/ CONFERENCE ROOMS MUST HAVE ABUSE RESISTANT GYPSUM BOARD REFER TO ENLARGED PLANS FOR PARTITION TYPES WITHIN TOILET/ SHOWER ROOMS
- I. PROVIDE WALL MARKING AND IDENTIFICATION FOR FIRE AND SMOKE BARRIERS IN ACCORDANCE WITH NFPA 101

SHEET KEYNOTES

- 1 ABA COMPLIANT HIGH/ LOW DRINKING FOUNTAINS W/ BOTTLE FILLING
STATION
- 2 GSA CLASS 5 VAULT W/ DAY GATE
- 3 8" CAST-IN-PLACE CONCRETE WALL
- 4 DOWNSPOUT (MTL-3), TYP
- 5 DOWNSPOUT (MTL-3) W/ CONCRETE SPLASHBLOCK, TYP
- 6 ABA COMPLIANT SHOWER W/ GRAB BARS AND BENCH
- 7 DELEGATED DESIGN, PRE-MANUFACTURED, PREFINISHED METAL CANOPY
(ABOVE)
- 8 CASEWORK, REFER TO INTERIORS
- 9 3' X 7' GYPSUM BOARD OPENING
- 10 OSHA COMPLIANT ROOF ACCESS LADDER
- 11 SEMI-RECESSED FIRE EXTINGUISHER CABINET



Jacobs

1100 NORTH GLEBE ROAD
SUITE 500
ARLINGTON, VIRGINIA 22201
571.218.1000
FAX: 571.218.1600

APPROVED _____

FOR COMMANDER NAVFAC

ACTIVITY
APPROVED BY LCDR ELIZABETH
OLOKODE NAVFAC NLON FEAD
DIRECTOR NEW LONDON, GROTON.

SATISFACTORY TO DATE 05/27/2025

DES	PS	DRW	PS	CHK	W
-----	----	-----	----	-----	---

PM/DM SMS/

BRANCH MANAGER

CHIEF ENG/ARCH

CHIEF ENGINEER

FIRE PROTECTION			
1	2	3	4

AND	VA	UT	Y
-----	----	----	---

MMF	IC	DLK ₁	TIC	IT ₁
-----	----	------------------	-----	-----------------

COM
NTI
RFO
ECT
CIL

ANSWER
LINE
AC

ITEM	TITLE	NO.	DATE	FA
------	-------	-----	------	----

15

Case	Age	Sex	Site	Pathologic	Immunohistochemical	Immunofluorescent	Electron Microscopic	Immunoelectron Microscopic	Immunoblot	Genetic	Other
1	50	M	Small intestine	Adenocarcinoma	+	+	+	+	+	+	
2	60	M	Small intestine	Adenocarcinoma	+	+	+	+	+	+	
3	60	M	Small intestine	Adenocarcinoma	+	+	+	+	+	+	
45	60</										

PRINTED BY MESSRS. J. & J. L. S. DODD & CO. LTD. LONDON

DEED -	RC	AT
--------	----	----


GINI	NA	G	ER
------	----	---	----

PE

ES	MR	O	N
----	----	---	---

CE

ACIL	NC	
SC		

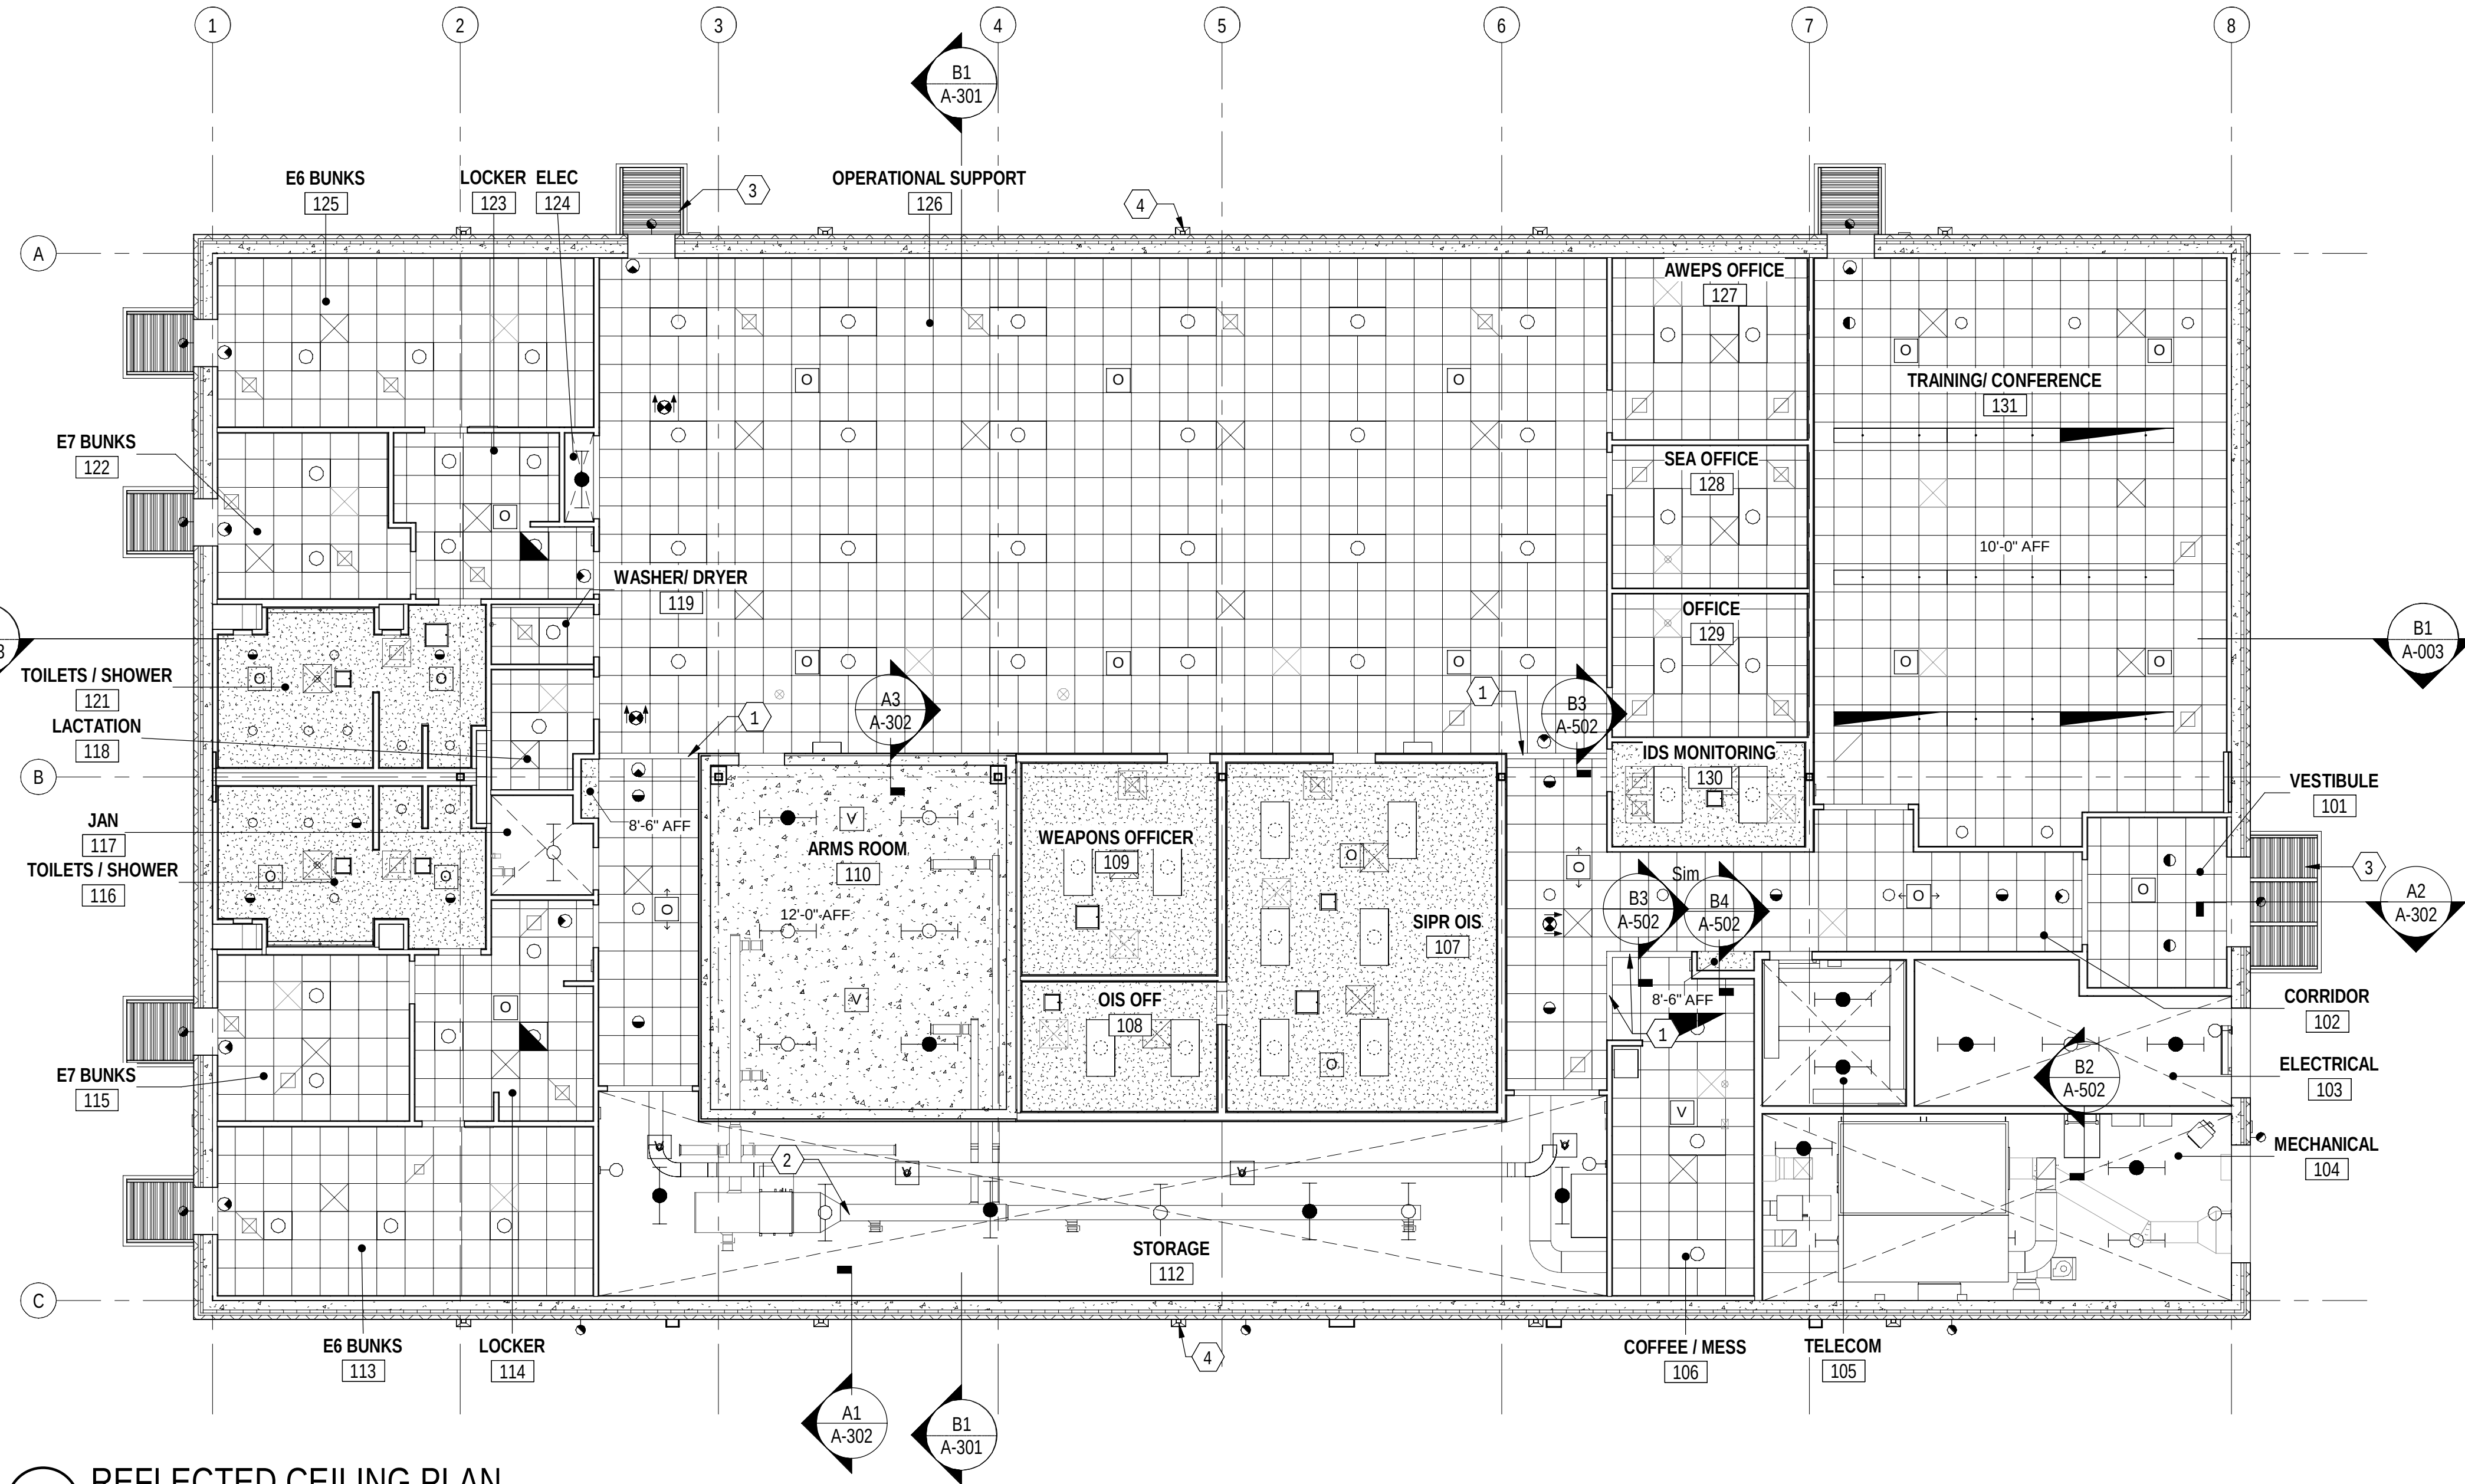

B1 REFLECTED CEILING PLAN
1/8" = 1'-0"

GENERAL SHEET NOTES

- REFER TO PLUMBING, MECHANICAL, ELECTRICAL, FIRE SUPPRESSION, FIRE ALARM AND TELECOMMUNICATION DRAWINGS FOR VENTS, SPRINKLER HEADS, GRILLES, REGISTERS, DIFFUSERS, DUCTS, LIGHTS, DETECTORS, ETC AND COORDINATE BETWEEN DISCIPLINES.
- CEILING HEIGHTS AT 9'-0" AFF, UON.
- CENTER CEILING MOUNTED FIXTURES (SPRINKLER HEADS, SMOKE AND HEAT DETECTORS, OCCUPANCY SENSORS, ETC.) UON.
- GYPSUM BOARD BULKHEADS AT 8'-6" AFF, UON.
- PROVIDE MOISTURE RESISTANT GYPSUM BOARD AT WET LOCATIONS
- REFER TO ARCHITECTURAL REFLECTED CEILING PLANS FOR THE GENERAL INTENDED LAYOUTS OF MECHANICAL AND ELECTRICAL AS THEY OCCUR WITHIN THE FINISH CEILING SYSTEM.

SHEET KEYNOTES

- GYPSUM BOARD BULKHEAD
- MECHANICAL EQUIPMENT, TYP. REFER TO MECHANICAL
- DELEGATED DESIGN, PRE-MANUFACTURED, PREFINISHED METAL CANOPY (MTL-2), TYP
- DOWNSPOUT (MTL-3), TYP


REFLECTED CEILING PLAN LEGEND

SYMBOL	DESCRIPTION
	AREA NOT IN CONTRACT
	CONCRETE CEILING (ARMORY AREAS ONLY)
	WIRE MESH CEILING (STORAGE AREA)
	NO CEILING - EXPOSED TO ROOF DECK ABOVE
	2' - 0" X 2' - 0" ACOUSTICAL CEILING TILE
	GYPSUM BOARD CEILING.
(X'-X")	FINISHED CEILING HEIGHT ABOVE FINISHED FLOOR
	LIGHT FIXTURE - REFER TO ELECTRICAL DRAWINGS
	EMERGENCY LIGHT FIXTURE - REFER TO ELECTRICAL DRAWINGS
	EXIT SIGN - REFER TO ELECTRICAL DRAWINGS
	OCCUPANCY/ VACANCY SENSOR. REFER TO ELECTRICAL DRAWINGS.
	CEILING SUPPLY DIFFUSER. REFER TO MECHANICAL DRAWINGS.
	CEILING RETURN OR EXHAUST. REFER TO MECHANICAL DRAWINGS.
	ACCESS PANELS - 12" X 12", 18" X 18". COORDINATE LOCATION WITH MECHANICAL EQUIPMENT. SHOWN FOR REFERENCE

0 4' 8' 16' 24'
1/8" = 1'-0"



SYMBOL	DESCRIPTION	DATE	APPROVED

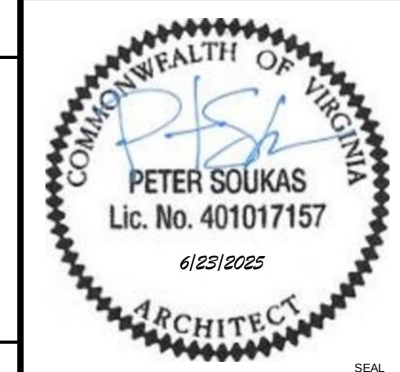

Jacobs
1100 NORTH GLEBE ROAD
SUITE 500
ARLINGTON, VIRGINIA 22201
571.218.1000
FAX: 571.218.1600

APPROVED

FOR COMMANDER NAVFAC

ACTIVITY APPROVED BY LCDR ELIZABETH
CLOKODE NAVFAC NLON HEAD
DIRECTOR NEW LONDON, GROTON, CT

SATISFACTORY TO DATE 05/27/2025

DES PS DRW PS CHK WS

PMOM SMS/ CWJ

BRANCH MANAGER DJD

CHIEF ENGINEER JWJ

FIRE PROTECTION HPN

NAVAL FACILITIES ENGINEERING SYSTEMS COMMAND - MID-ATLANTIC

NAVAL STATION - NORFOLK, VA

NAVAL FACILITIES ENGINEERING SYSTEMS COMMAND - MID-ATLANTIC

NAVAL SUBMARINE BASE NEW LONDON

GROTON, CONNECTICUT

P-1102 WEAPONS MAGAZINE & ORDNANCE OPERATIONS FACILITY

OPERATIONS

ARCHITECTURAL REFLECTED CEILING PLAN

A

B

C

D

APPROVED

PROJECT NO.: 1667770


CONSTR. CONTR. NO.

NAVFAC DRAWING NO. 12893976

SHEET 26 OF 140

A-102

6/20/2025 10:32:31 AM A-103
\\b0119501\\b0119501\\FDZEL628\\AFCHBLDG-1667770-A-BIM.rvt

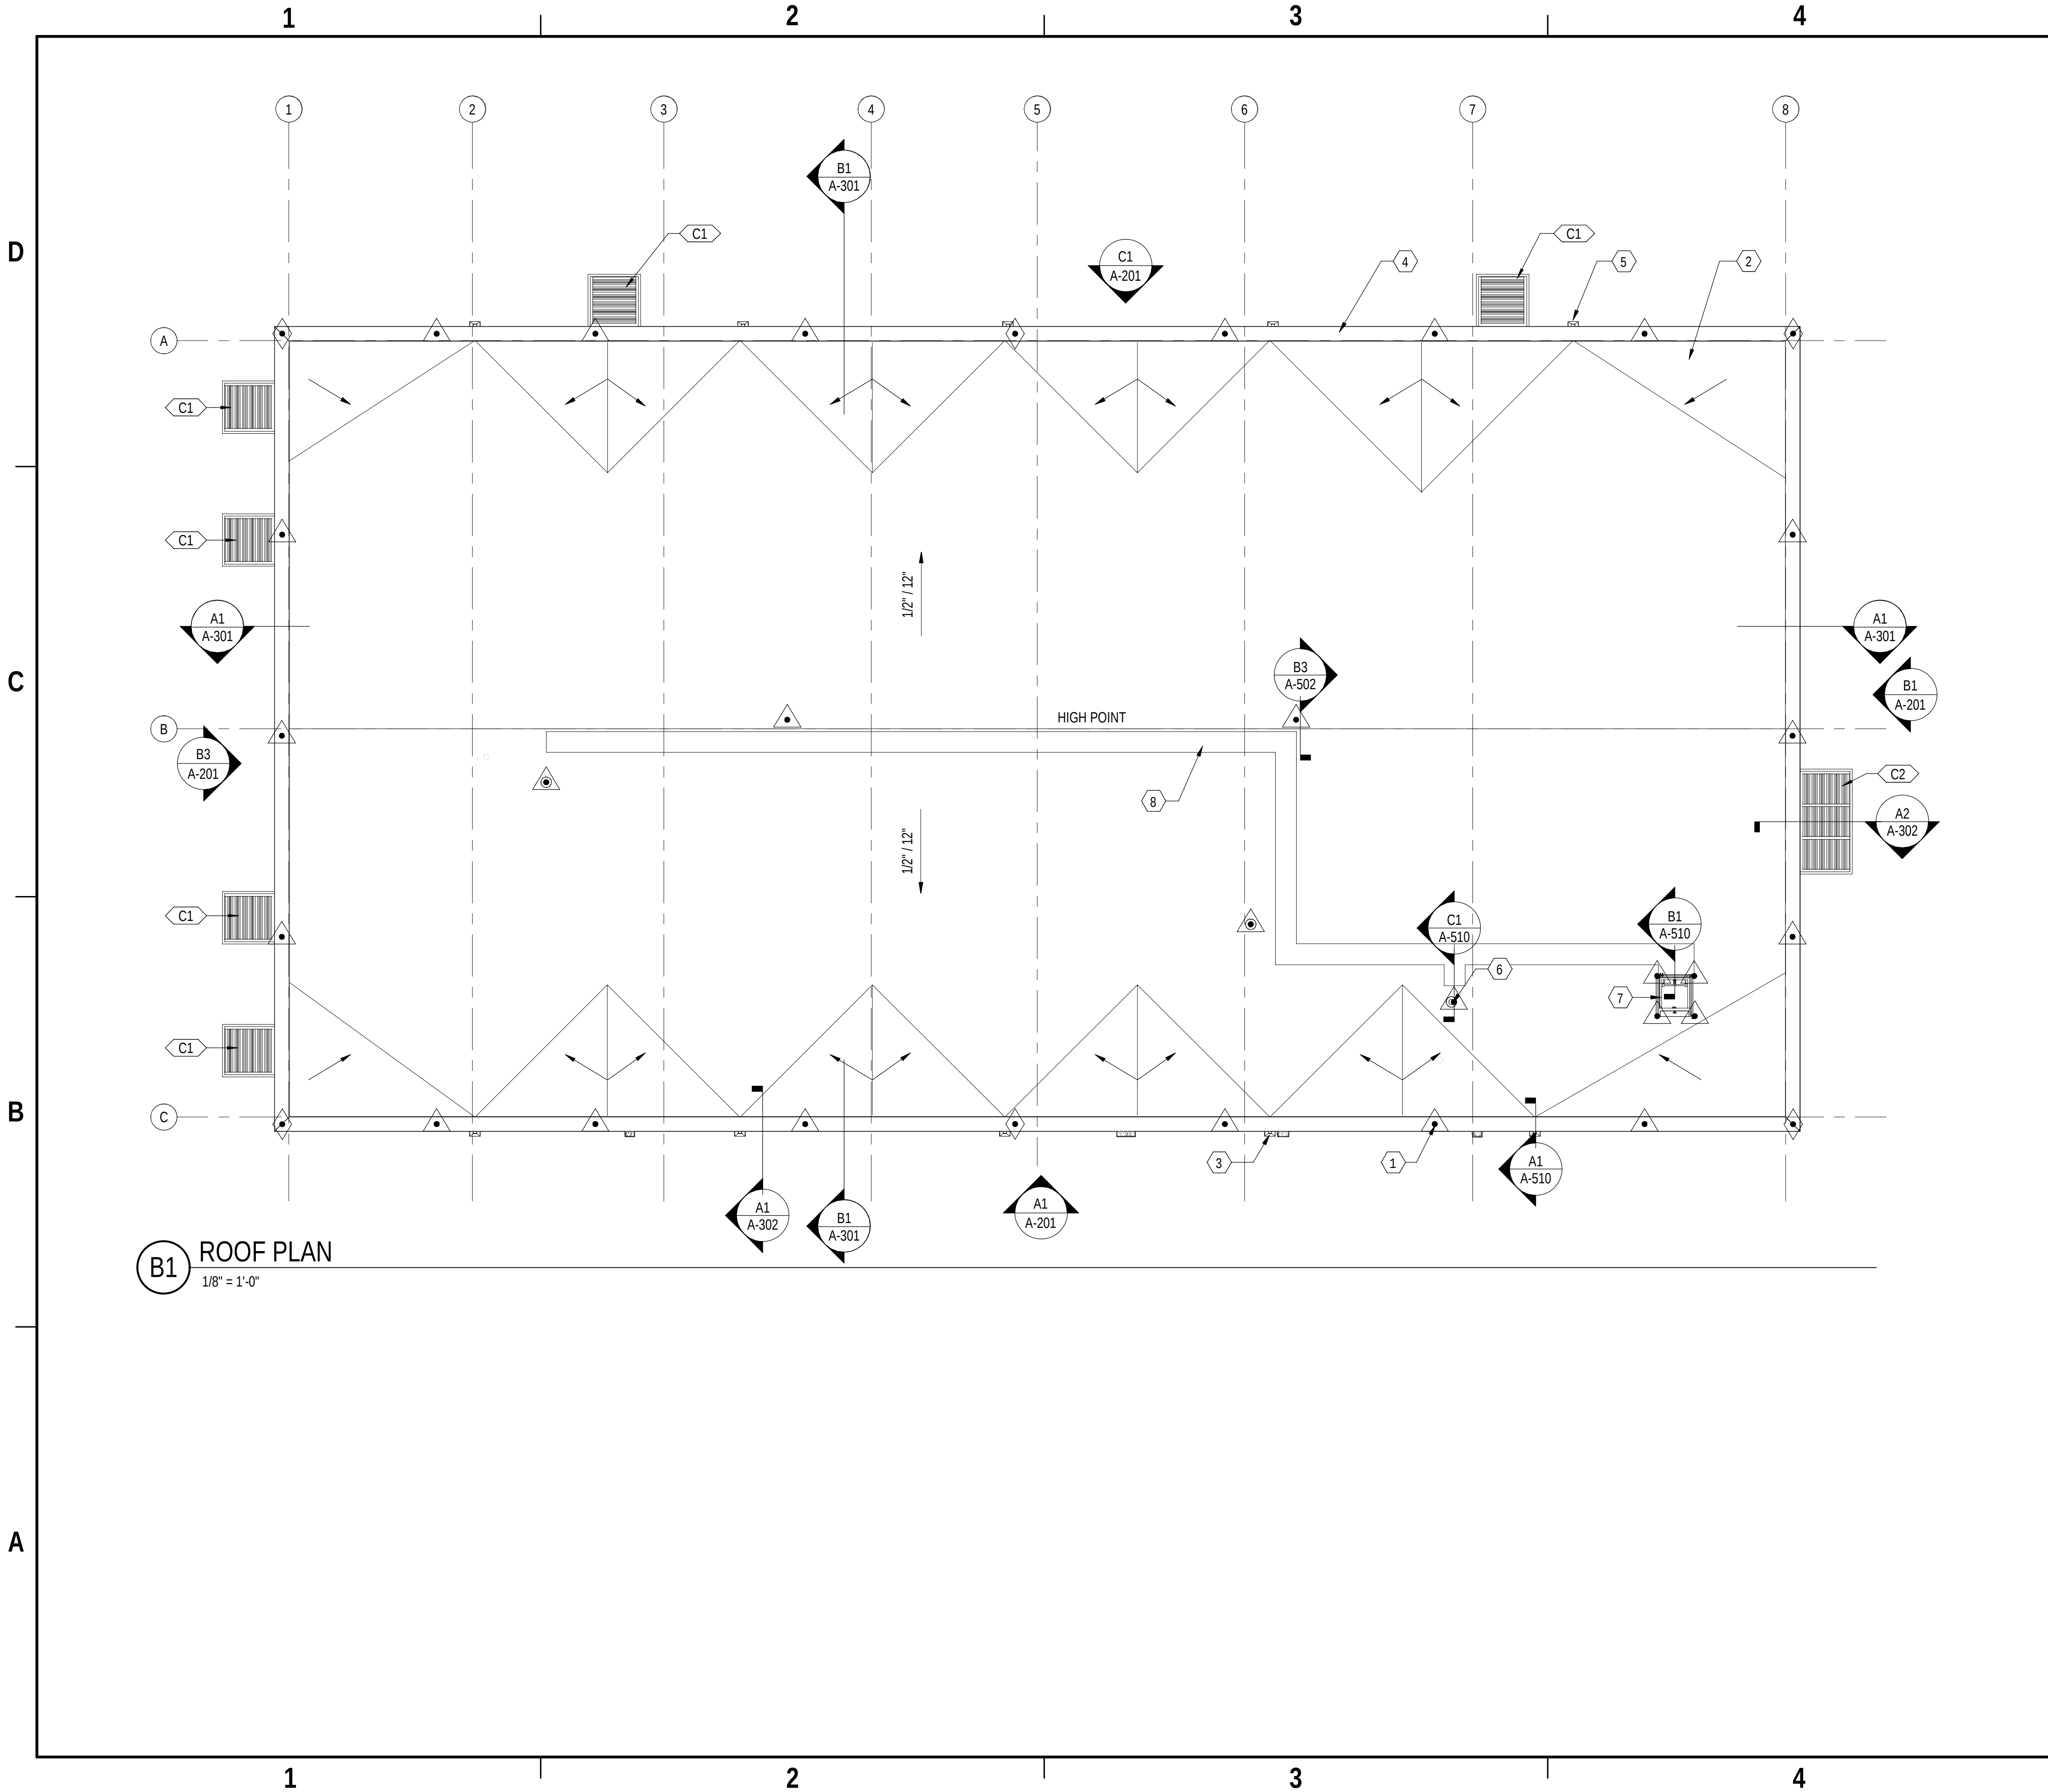


GENERAL SHEET NOTES

- A. ROOF IS A FULLY ADHERED TPO ROOFING SYSTEM.
B. ROOF SYSTEMS MUST BE FURNISHED AND INSTALLED PER ROOF MANUFACTURER'S INSTRUCTIONS AND STANDARDS.
C. STAGGER ROOF INSULATION JOINTS. INSULATION JOINTS GREATER THAN 1/4" MUST BE FILLED WITH INSULATION STRIPS.
D. ROOF MUST HAVE A CONTINUOUS MINIMUM VALUE OF R-35 INSULATION.
E. CRICKET SLOPE MUST BE 1" PER 1'-0".

SHEET KEYNOTES

- 1 LIGHTNING PROTECTION, TYP. REFER TO ELECTRICAL
2 ROOF CRICKET, TYP
3 DOWNSPOUT (MTL-3), TYP
4 PREFINISHED SLOPED METAL COPING (MTL-1)
5 THROUGH WALL SCUPPER W/ CONDUCTOR HEAD, TYP
6 PIPE PENETRATION, TYP
7 OSHA COMPLIANT 30" X 37" SINGLE-LEAF ROOF HATCH W/ SAFETY RAILS AND GATE
8 NON-SLIP WALKWAY PAD PER ROOFING MFR

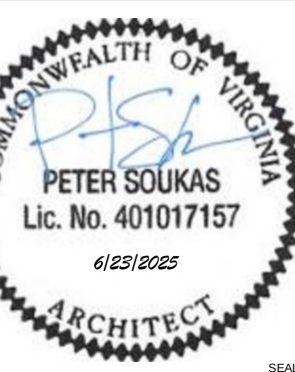

Jacobs

1100 NORTH GLEBE ROAD
SUITE 500
ARLINGTON, VIRGINIA 22201
571.218.1000
FAX: 571.218.1600

APPROVED

FOR COMMANDER NAVFAC

ACTIVITY APPROVED BY LCDR ELIZABETH
CLOKODE NAVFAC NLON FEAD
DIRECTOR NEW LONDON, GROTON, CT

SATISFACTORY TO DATE 05/27/2025

DES	PS	DRW	PS	CHK	WS

PMOM SMS/ CWJ

BRANCH MANAGER DJD

CHIEF ENGINEER JWJ

FIRE PROTECTION HPN

NAVAL FACILITIES ENGINEERING SYSTEMS COMMAND - MID-ATLANTIC

NAVAL STATION - NORFOLK, VA

NAVAL SUBMARINE BASE NEW LONDON

GROTON, CONNECTICUT

P-1102 WEAPONS MAGAZINE & ORDNANCE OPERATIONS FACILITY

OPERATIONS

ARCHITECTURAL ROOF PLAN

SCALE: AS NOTED

PROJECT NO.: 1667770

CONSTR. CONTR. NO.


NAVFAC DRAWING NO. 12893977

SHEET 27 OF 140

A-103

6/20/2025 10:32:40 AM
\\bcl1v901\liefm\p\FDZ\1628\AFCH\BLDG-1667770-A-BIM.rvt

A-201

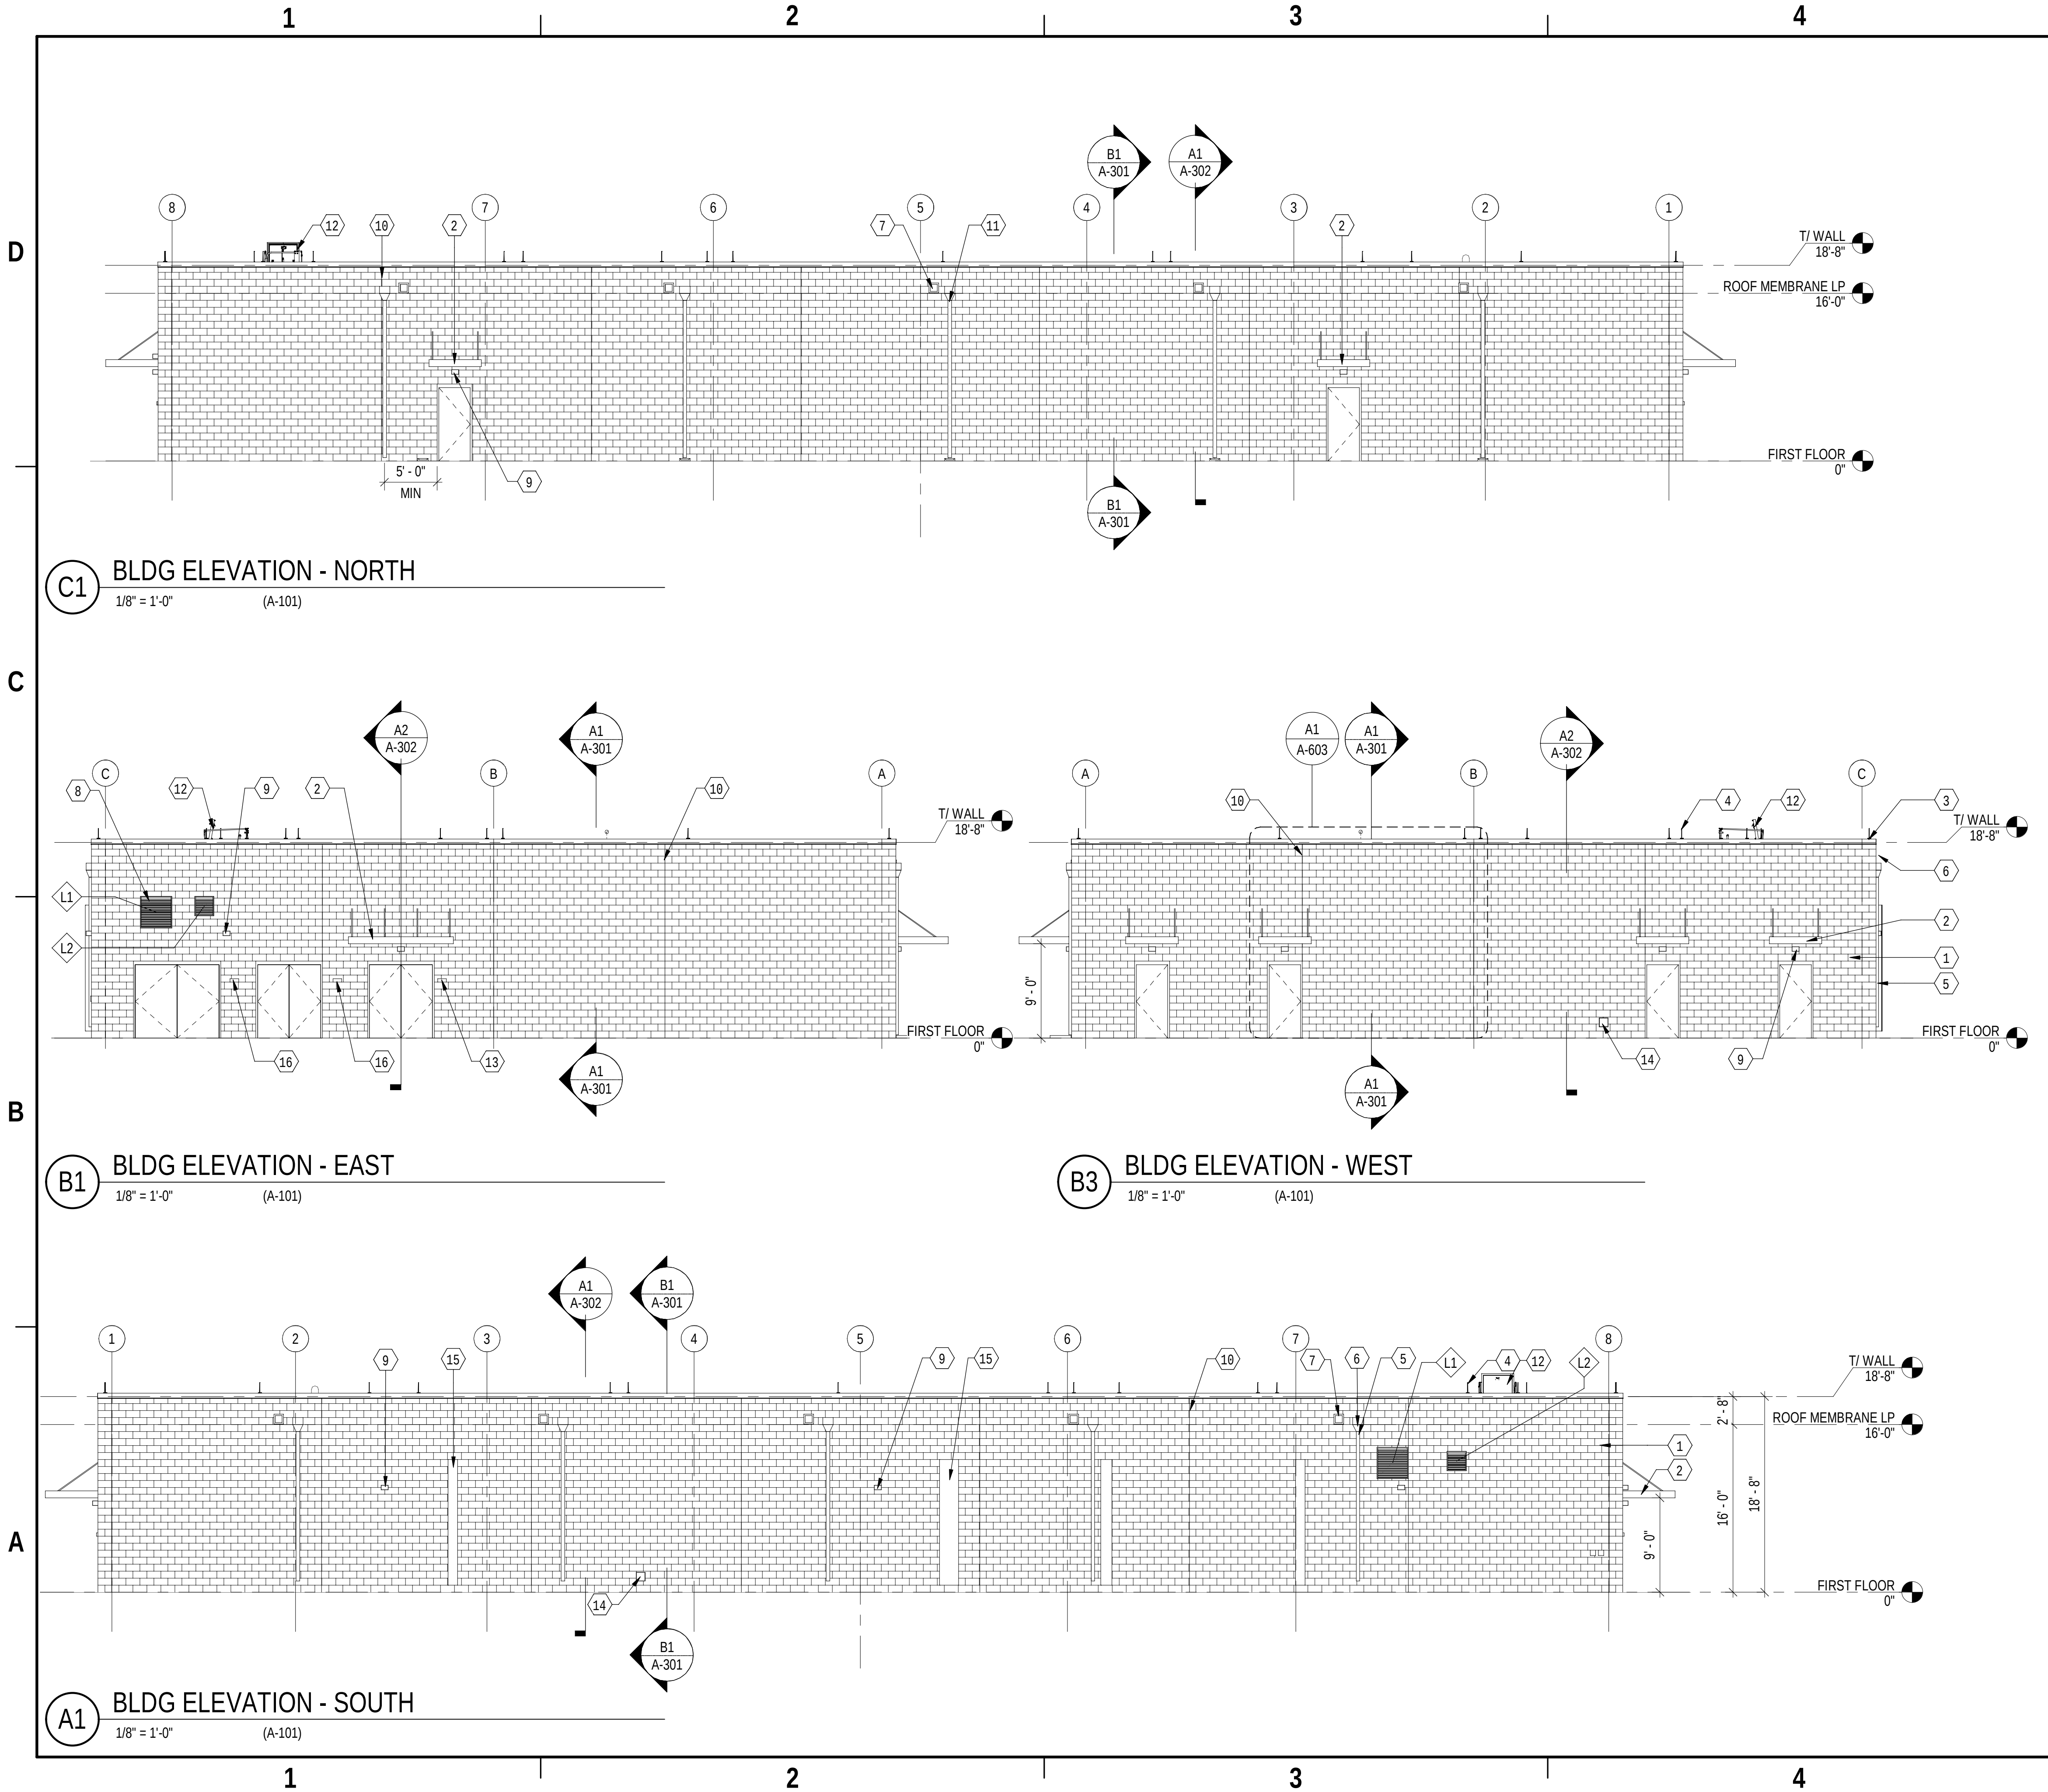

GENERAL SHEET NOTES

- DOWNSPOUT DISCHARGE - NORTH ELEVATION TO DISCHARGE ONTO CONCRETE SPLASHBLOCK, SOUTH ELEVATION TO CONNECTED TO UNDERGROUND PIPING
- REFER TO SHEET A-603 FOR EXTERIOR FINISHES AND ARCHITECTURAL CMU PATTERN, FINISH, AND COLOR
- REFER TO SHEET A-601 FOR LOUVER SCHEDULE AND DETAILS

SHEET KEYNOTES

- ARCHITECTURAL CMU
- DELEGATED DESIGN, PRE-MANUFACTURED, PREFINISHED METAL CANOPY (MTL-2), TYP
- PREFINISHED SLOPED METAL COPING (MTL-1)
- LIGHTNING PROTECTION, TYP. REFER TO ELECTRICAL
- DOWNSPOUT (MTL-3), TYP
- CONDUCTOR HEAD, TYP
- OVERFLOW SCUPPER. LOCATE 2" ABOVE ROOF SURFACE, TYP
- 36" X 36" LOUVER
- EXTERIOR LIGHTING, TYP
- CONTROL JOINT, TYP
- DOWNSPOUT (MTL-3) W/ CONCRETE SPLASHBLOCK, TYP
- OSHA COMPLIANT 30" X 37" SINGLE-LEAF ROOF HATCH W/ SAFETY RAILS AND GATE (HATCH IN OPEN POSITION)
- EXTERIOR BUILDING SIGNAGE
- HOSE BIB CENTERED ON SINGULAR ARCHITECTURAL BLOCK, TYP, REFER TO PLUMBING.
- GALVANIZED STEEL COVER AROUND REFRIGERANT PIPING, TYP. REFER TO MECHANICAL. FINISH TO MATCH METAL COPING
- EXTERIOR ROOM NAME SIGNAGE



Jacobs
1100 NORTH GLEBE ROAD
SUITE 500
ARLINGTON, VIRGINIA 22201
571.218.1000
FAX: 571.218.1600

APPROVED

FOR COMMANDER NAVFAC

ACTIVITY
APPROVED BY LCDR ELIZABETH
CLOKODE NAVFAC NLON FEAD
DIRECTOR NEW LONDON, GROTON, CT

SATISFACTORY TO DATE 05/27/2025

DES PS DRW PS CHK WS

PMOM SMS/ CWJ

BRANCH MANAGER DJD

CHIEF ENGINEER JWJ

FIRE PROTECTION HPN

DEPARTMENT OF THE NAVY

NAVAL FACILITIES ENGINEERING SYSTEMS COMMAND

NAVAL FACILITIES ENGINEERING SYSTEMS COMMAND - MID-ATLANTIC

MID-ATLANTIC

NAVAL SUBMARINE BASE NEW LONDON

GROTON, CONNECTICUT

P-1102 WEAPONS MAGAZINE & ORDNANCE OPERATIONS FACILITY

OPERATIONS

ARCHITECTURAL BUILDING ELEVATIONS

A

B

C

D

APPR

DATE

SYM

DESCRIPTION

1667770

CONSTR. CONTR. NO.

NAVFAC DRAWING NO.

12893978

SHEET 28 OF 140

A-201



1

2

3

4

5

GENERAL SHEET NOTES

A. REFER TO OTHER DISCIPLINES FOR ADDITIONAL INFORMATION

SHEET KEYNOTES

- 1 CONCRETE SLAB, REFER STRUCTURAL
- 2 CONCRETE FOOTING, REFER TO STRUCTURAL
- 3 STRUCTURAL STEEL FRAMING, REFER TO STRUCTURAL
- 4 GRAVEL
- 5 PREFINISHED SLOPED METAL COPING (MTL-1)
- 6 DELEGATED DESIGN, PRE-MANUFACTURED, PREFINISHED METAL CANOPY (MTL-2), TYP
- 7 SCHEDULED CEILING
- 8 OSHA COMPLIANT 30" X 37" SINGLE-LEAF ROOF HATCH W/ SAFETY RAILS AND GATE




Jacobs
1100 NORTH GLEBE ROAD
SUITE 500
ARLINGTON, VIRGINIA 22201
571.218.1000
FAX: 571.218.1600

APPROVED					
FOR COMMANDER NAVFAC					
ACTIVITY: APPROVED BY LCDR ELIZABETH OLOKODE NAVFAC NLON FEAD DIRECTOR NEW LONDON, GROTON, CT					
SATISFACTORY TO DATE: 05/27/2025					
DES	PS	DRW	PS	CHK	WS
PWDM				SMSI/CWJ	
BRANCH MANAGER				DJJ	
CHIEF ENGINEER				JWJ	
FIRE PROTECTION				HPN	


DEPARTMENT OF THE NAVY
NAVAL FACILITIES ENGINEERING SYSTEMS COMMAND - MID-ATLANTIC
NAVAL STATION - NORFOLK, VA
NAVAL SUBMARINE BASE NEW LONDON
GROTON, CONNECTICUT
P-1102 WEAPONS MAGAZINE & ORDNANCE OPERATIONS FACILITY
OPERATIONS
ARCHITECTURAL BUILDING SECTIONS

SCALE: AS NOTED	
PROJECT NO.: 1667770	
CONSTR. CONTR. NO.	
NAVFAC DRAWING NO. 12893979	
SHEET 29	OF 140

A-301

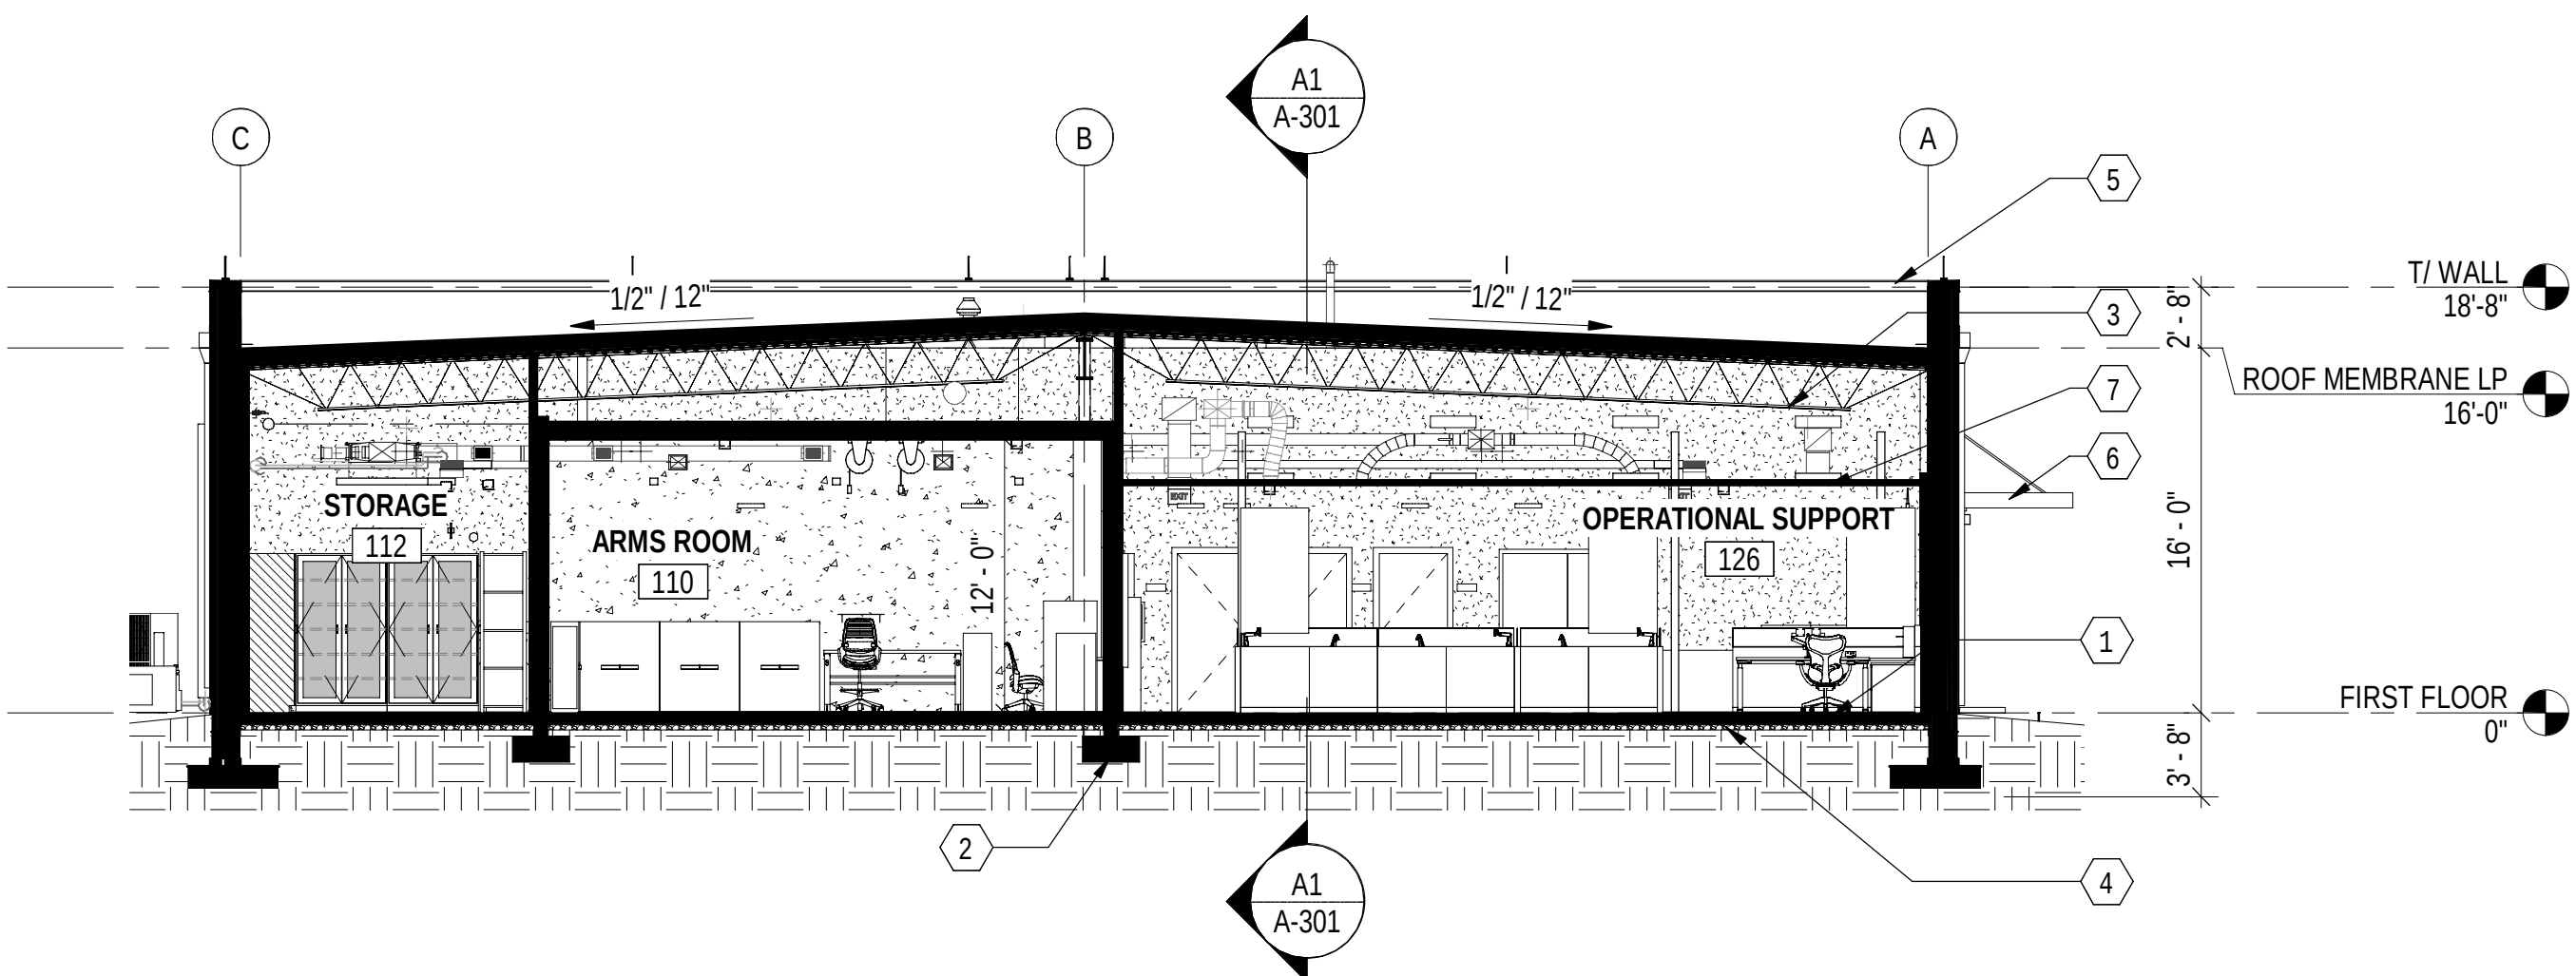


B1 NORTH-SOUTH BUILDING SECTION
1/8" = 1'-0" (A-101)

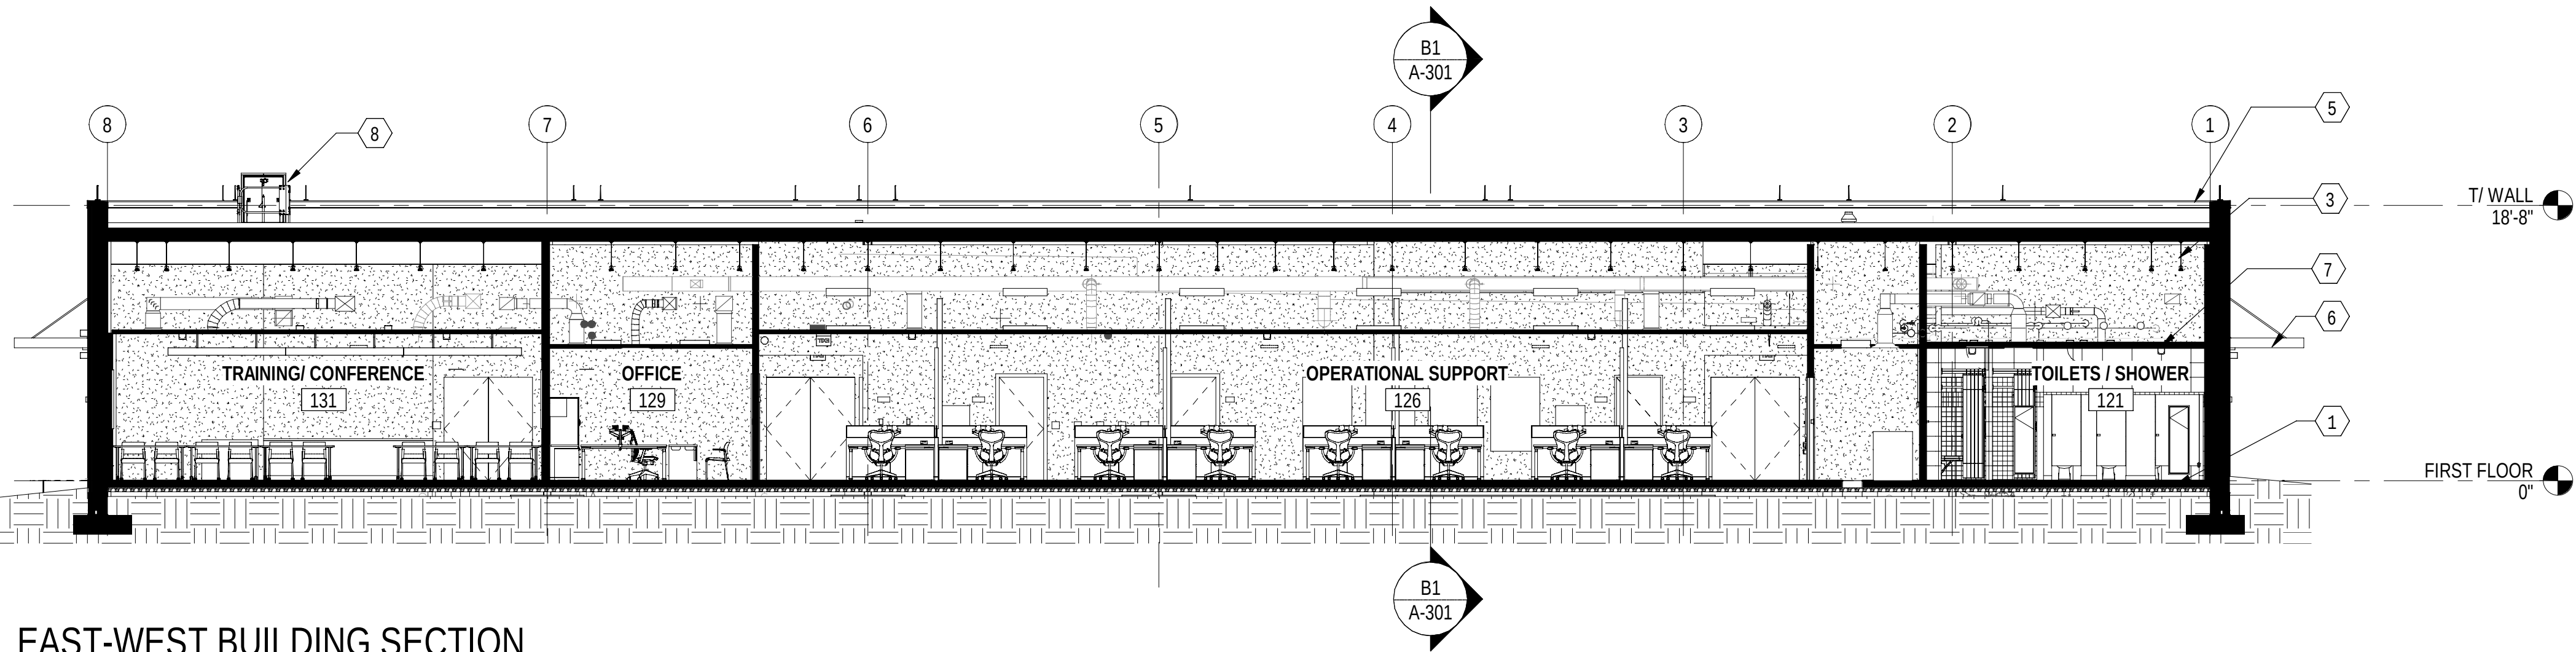

A1 EAST-WEST BUILDING SECTION
1/8" = 1'-0" (A-101)



6/20/2025 10:32:55 AM A-302
\\06119501\\06119501\\FD\\E1628\\AFCH\\BLOG-1667770-A-BIM.rvt

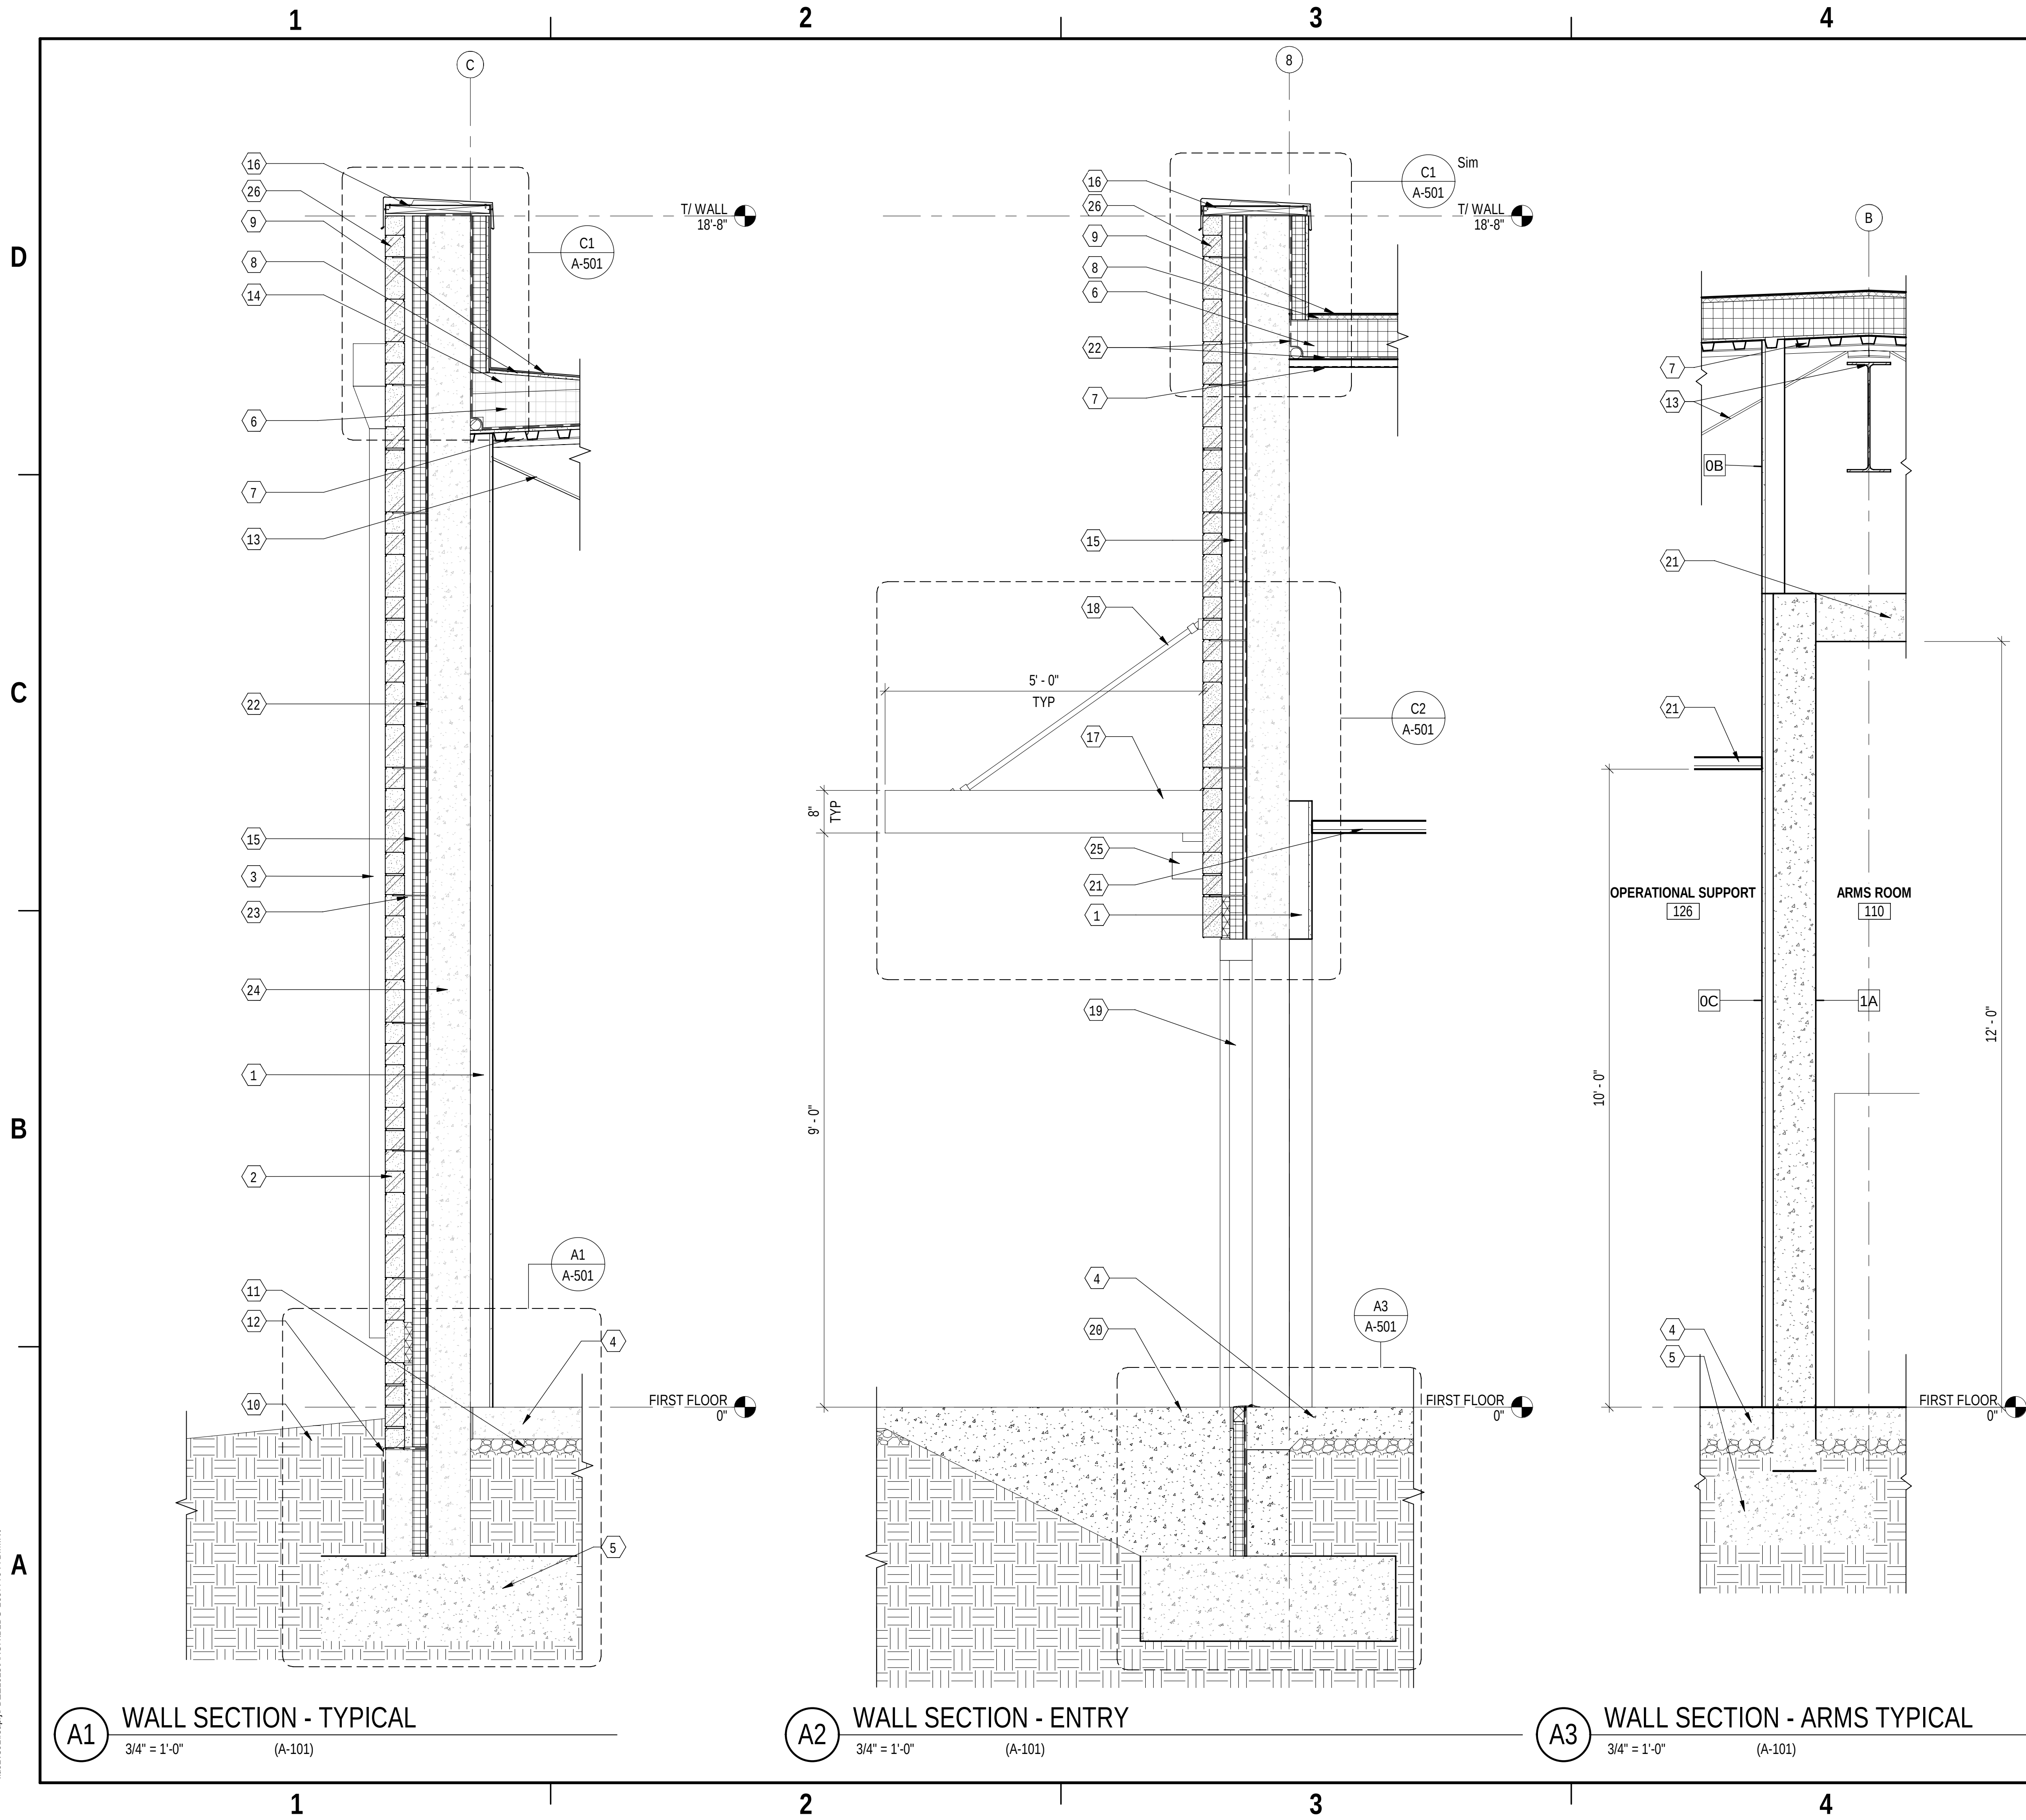


GENERAL SHEET NOTES


- A. PER IBC 2603.5.5 THE EXTERIOR WALL ASSEMBLY IS EXEMPT FROM BEING TESTED IN ACCORDANCE WITH AND COMPLY WITH THE ACCEPTANCE CRITERIA OF NFPA 285. THE ORDANANCE BUILDING IS A ONE STORY BUILDING COMPLYING WITH IBC SECTION 2603.4.1.4.
- B. REFER TO STRUCTURAL FOR ADDITIONAL INFORMATION.

SHEET KEYNOTES

- 1 SCHEDULED PARTITION
- 2 ARCHITECTURAL CMU
- 3 DOWNSPOUT (BEYOND)
- 4 CONCRETE SLAB, REFER STRUCTURAL
- 5 CONCRETE FOOTING, REFER TO STRUCTURAL
- 6 R-35 CONT RIGID INSULATION
- 7 METAL ROOF DECK, REFER TO STRUCTURAL
- 8 5/8" COVER BOARD
- 9 FULLY ADHERED TPO MEMBRANE
- 10 GRADE, REFER TO CIVIL
- 11 COMPACTED GRAVEL SUB-BASE, REFER TO STRUCTURAL
- 12 DAMPPROOFING
- 13 STRUCTURAL STEEL FRAMING, REFER TO STRUCTURAL
- 14 TAPERED INSULATION BOARD AT CRICKET LOCATIONS
- 15 R-13.3 FOIL-FACED CONT RIGID INSULATION
- 16 PREFINISHED SLOPED METAL COPING (MTL-1)
- 17 DELEGATED DESIGN, PRE-MANUFACTURED, PREFINISHED METAL CANOPY (MTL-2), TYP
- 18 1" HANGAR PIPE ASSEMBLY W/ THREADED ADJUSTED ROD
- 19 HOLLOW METAL DOOR
- 20 CONCRETE SIDEWALK (SLOPE AWAY FROM BUILDING), REFER TO CIVIL
- 21 SCHEDULED CEILING
- 22 AIR BARRIER/ VAPOR RETARDER
- 23 THERMALLY BROKEN VENEER ANCHOR, TYP
- 24 CAST-IN-PLACE 8" CONCRETE
- 25 EXTERIOR LIGHTING, TYP
- 26 WEEP VENT INSERTS AT 24" OC

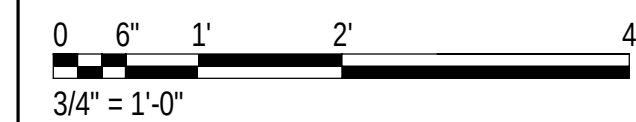

SYM	DESCRIPTION	DATE	APPR

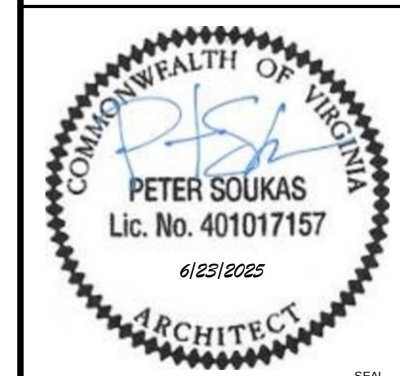


Jacobs
1100 NORTH GLEBE ROAD
SUITE 500
ARLINGTON, VIRGINIA 22201
571.218.1000
FAX: 571.218.1600


APPROVED					
FOR COMMANDER NAVFAC					
ACTIVITY APPROVED BY LCDR ELIZABETH CLOKODE NAVFAC NLON FEAD DIRECTOR NEW LONDON, GROTON, CT					
SATISFACTORY TO DATE 05/27/2025					
DES	PS	DRW	PS	CHK	WS
PM/DI				SMS/ CWJ	
BRANCH MANAGER				DJD	
CHIEF ENGINEER				JWJ	
FIRE PROTECTION				HPN	

DEPARTMENT OF THE NAVY
NAVAL FACILITIES ENGINEERING SYSTEMS COMMAND - MID-ATLANTIC
NAVAL STATION - NORFOLK, VA
NAVAL FACILITIES ENGINEERING SYSTEMS COMMAND - MID-ATLANTIC
NAVAL SUBMARINE BASE NEW LONDON
GROTON, CONNECTICUT
P-1102 WEAPONS MAGAZINE & ORDNANCE OPERATIONS FACILITY
OPERATIONS
ARCHITECTURAL WALL SECTIONS


SCALE: AS NOTED	
EPROJECT NO.: 1667770	
CONSTR. CONTR. NO.	
NAVFAC DRAWING NO. 12893980	
SHEET 30	OF 140
A-302	

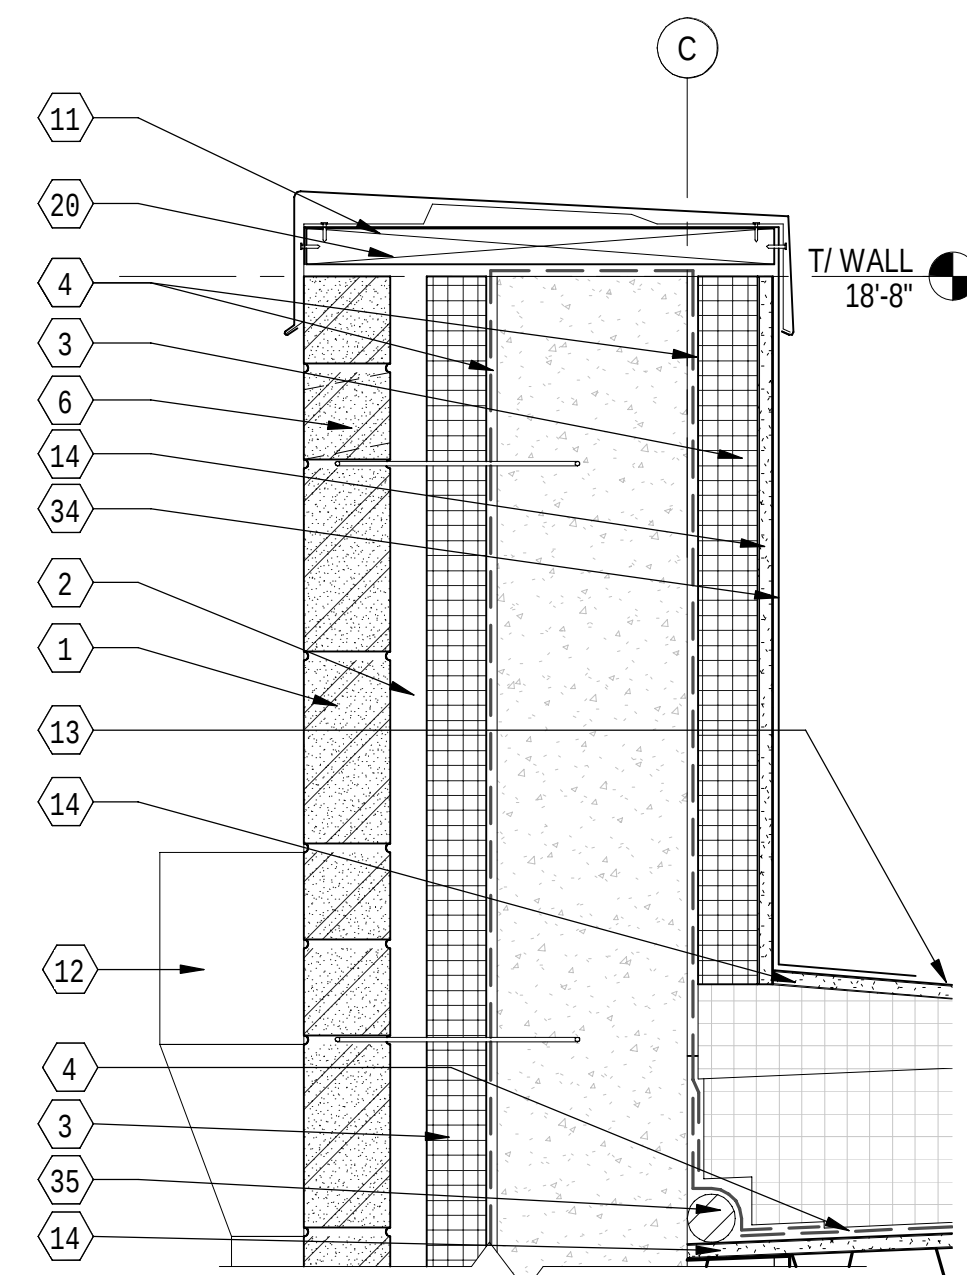


C1 COPING DETAIL
1 1/2" = 1'-0" (A-30)

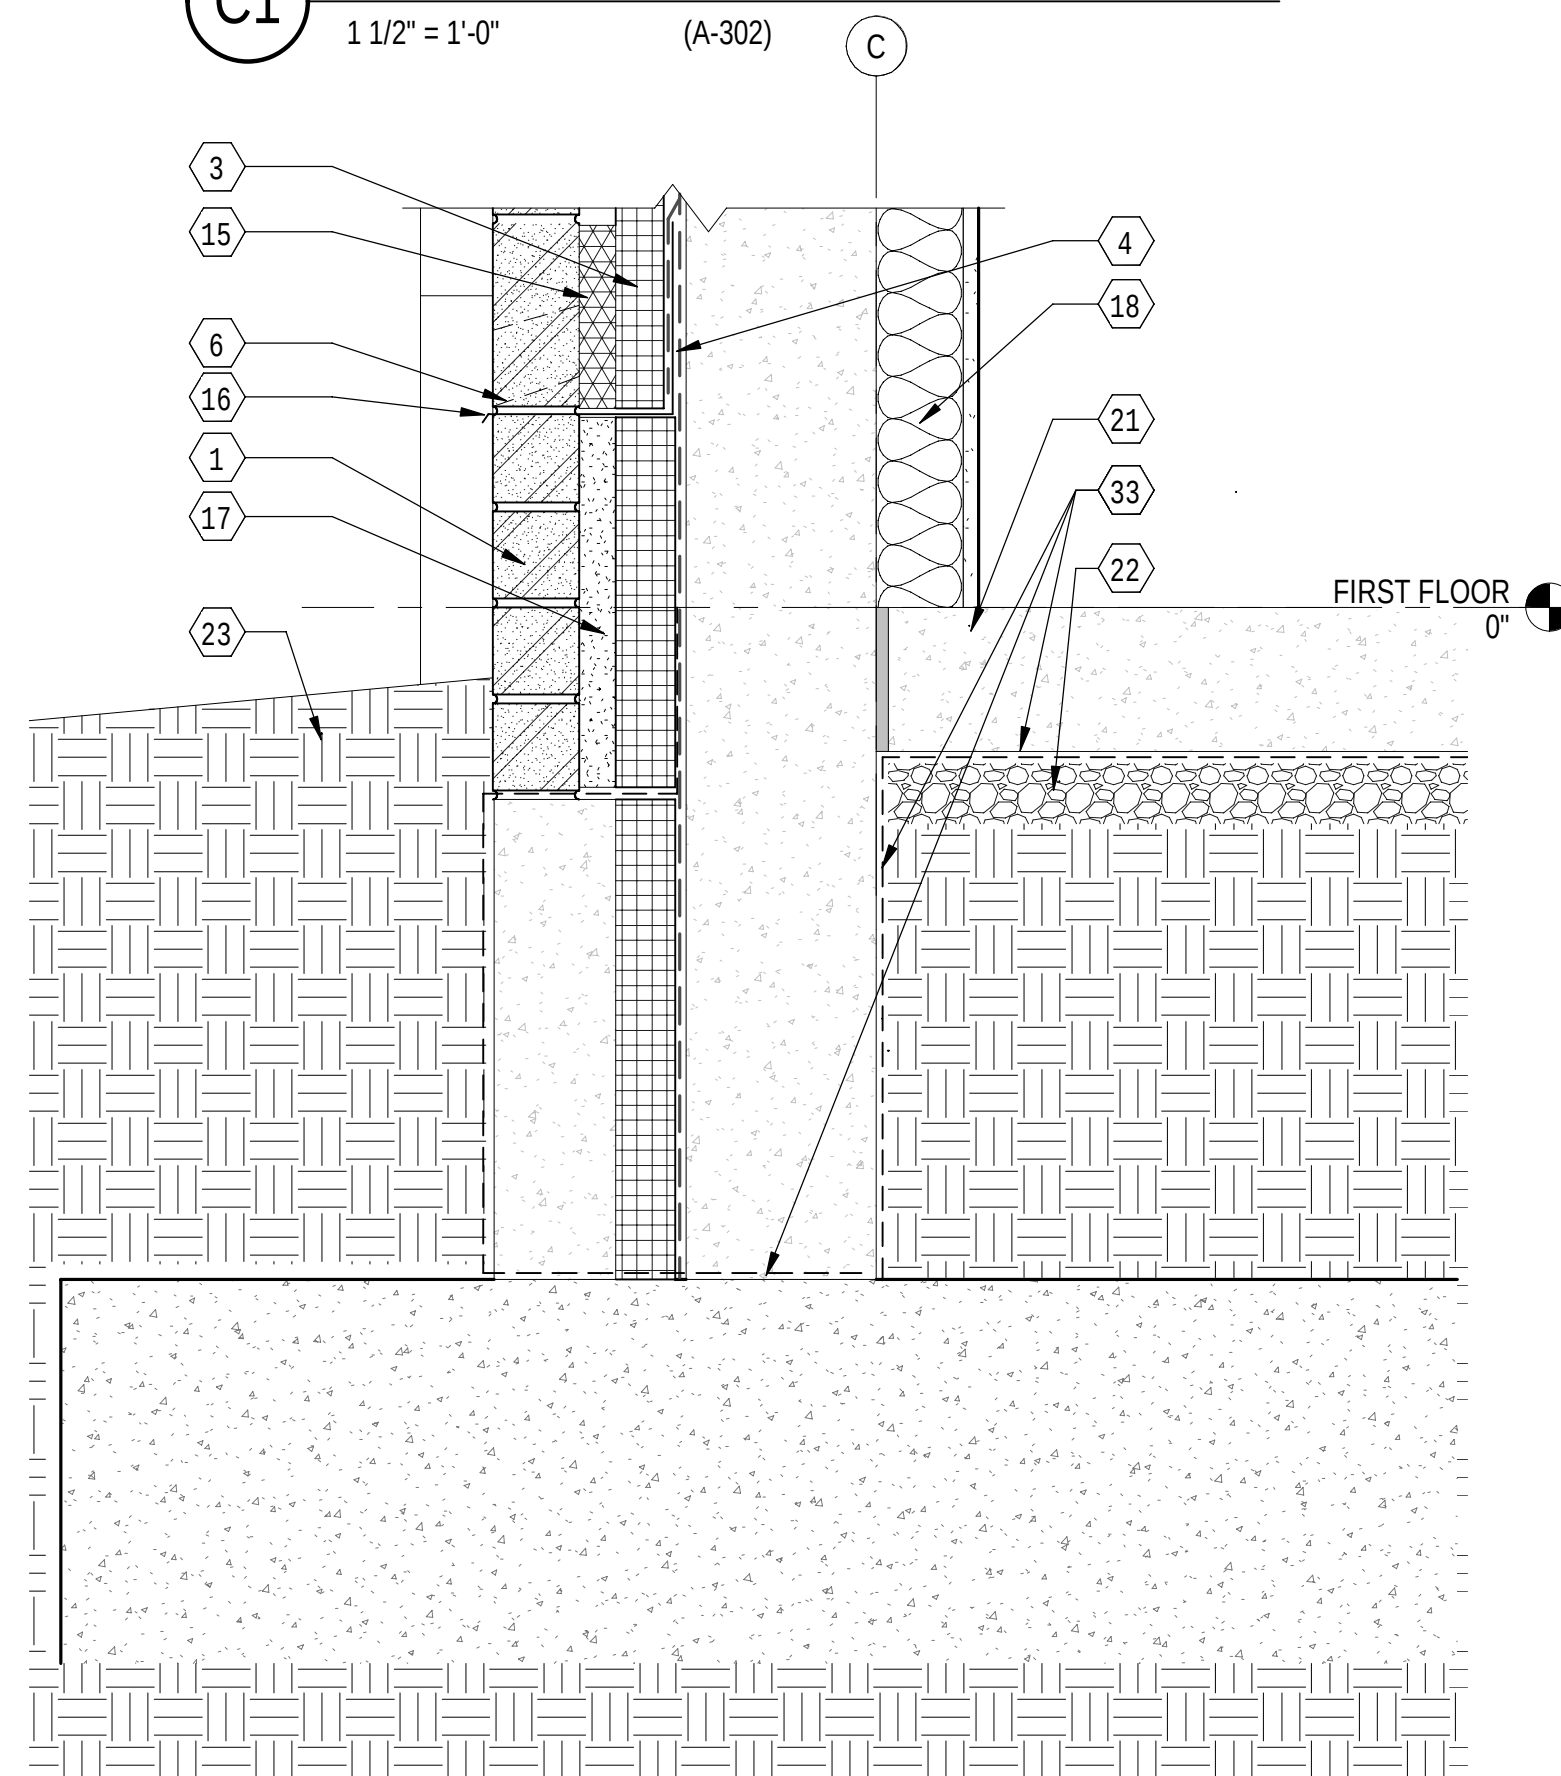

A1 FOUNDATION DETAIL
1 1/2" = 1'-0" (A-302)

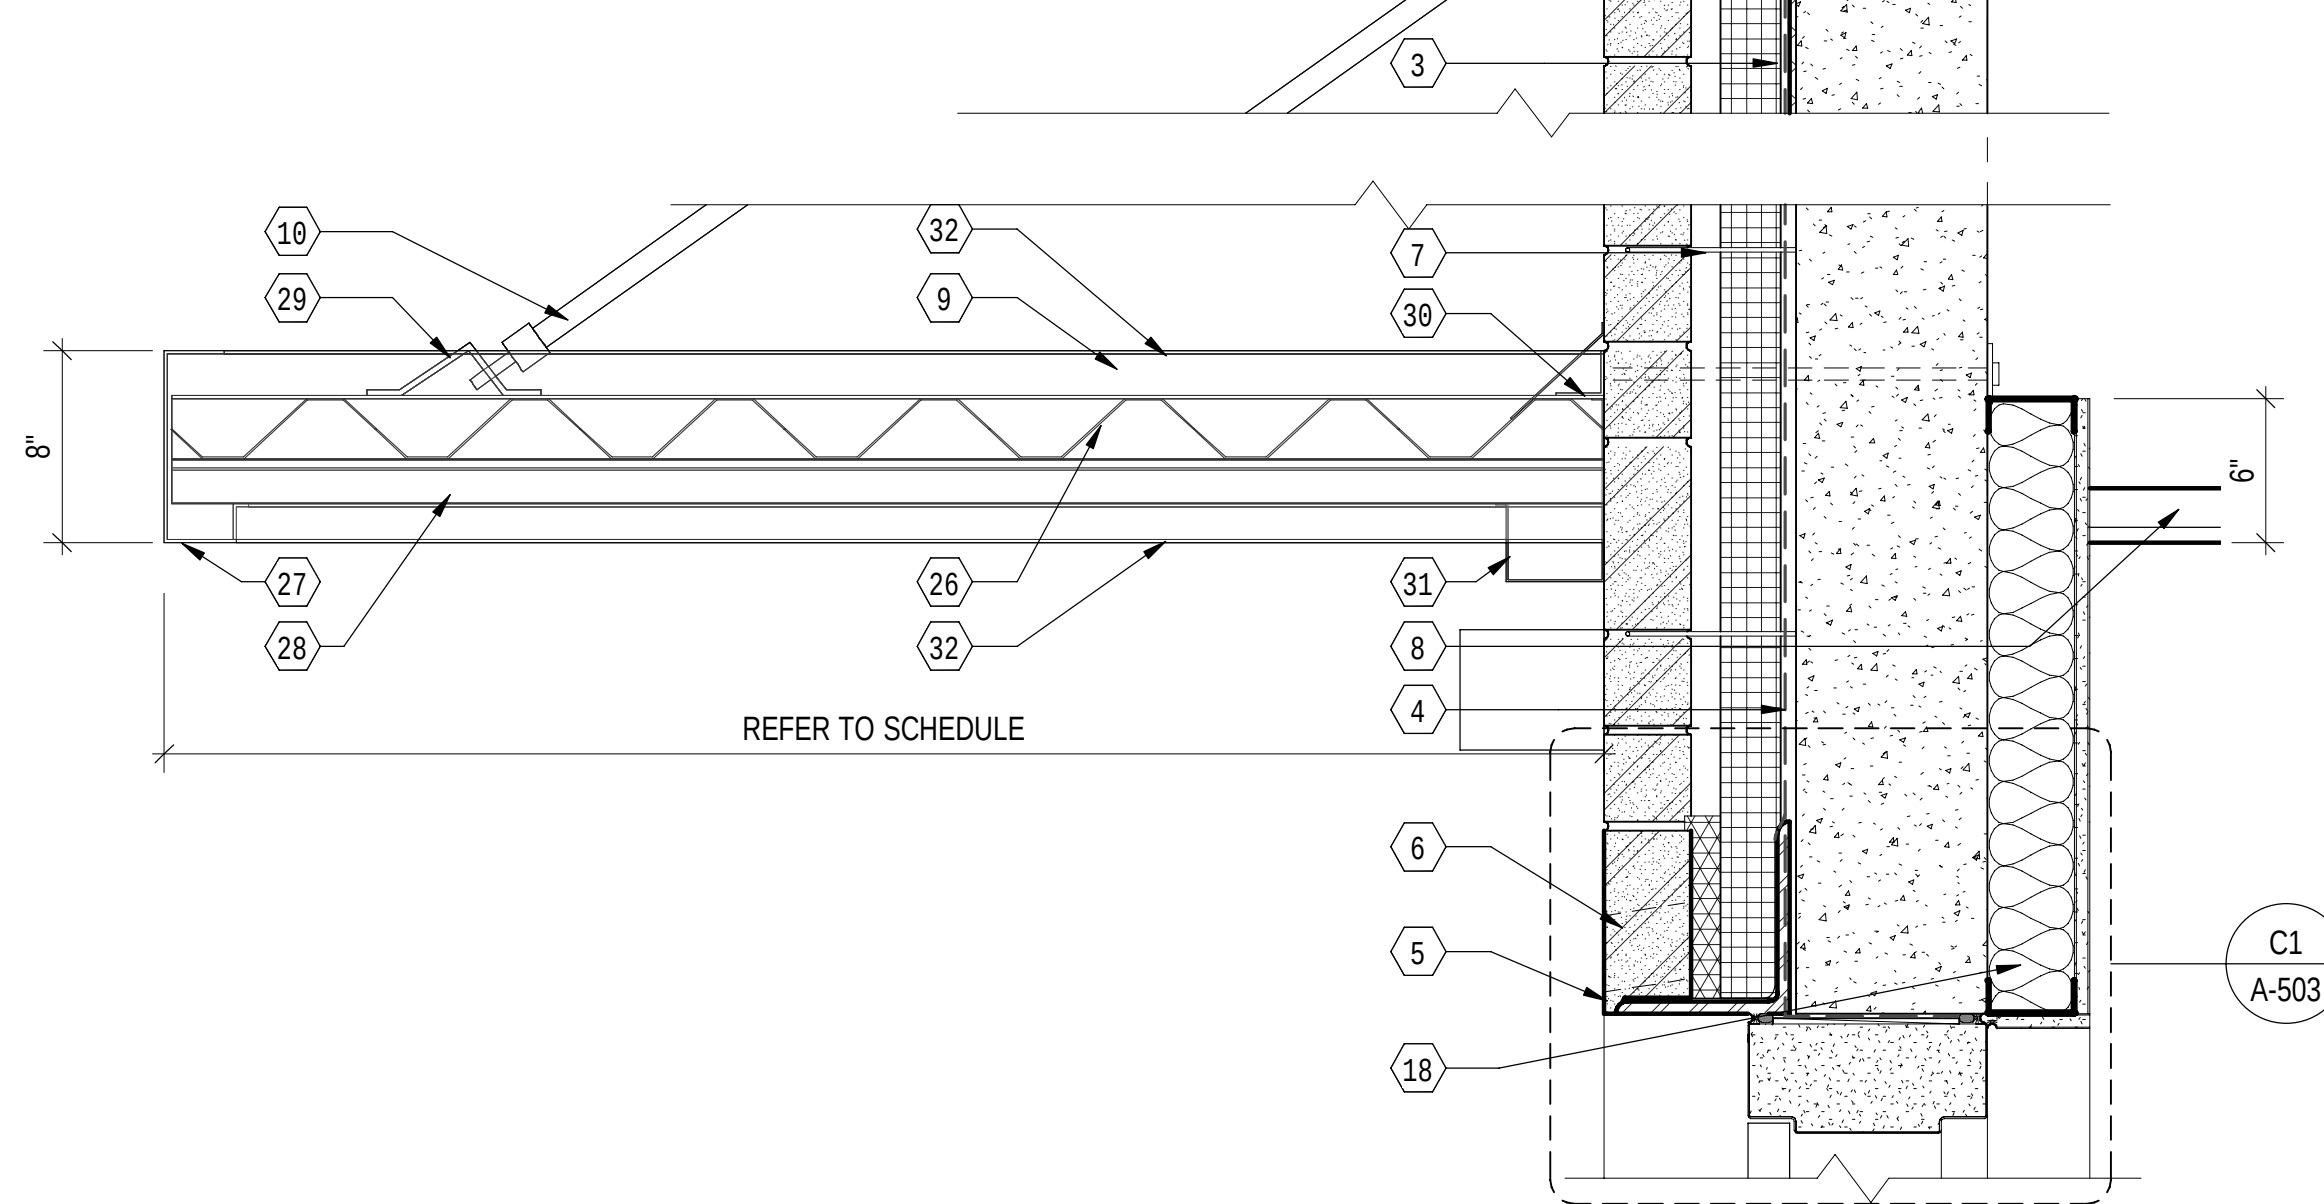


C2 CANOPY/ WALL DETAIL
1 1/2" = 1'-0" (A-302)

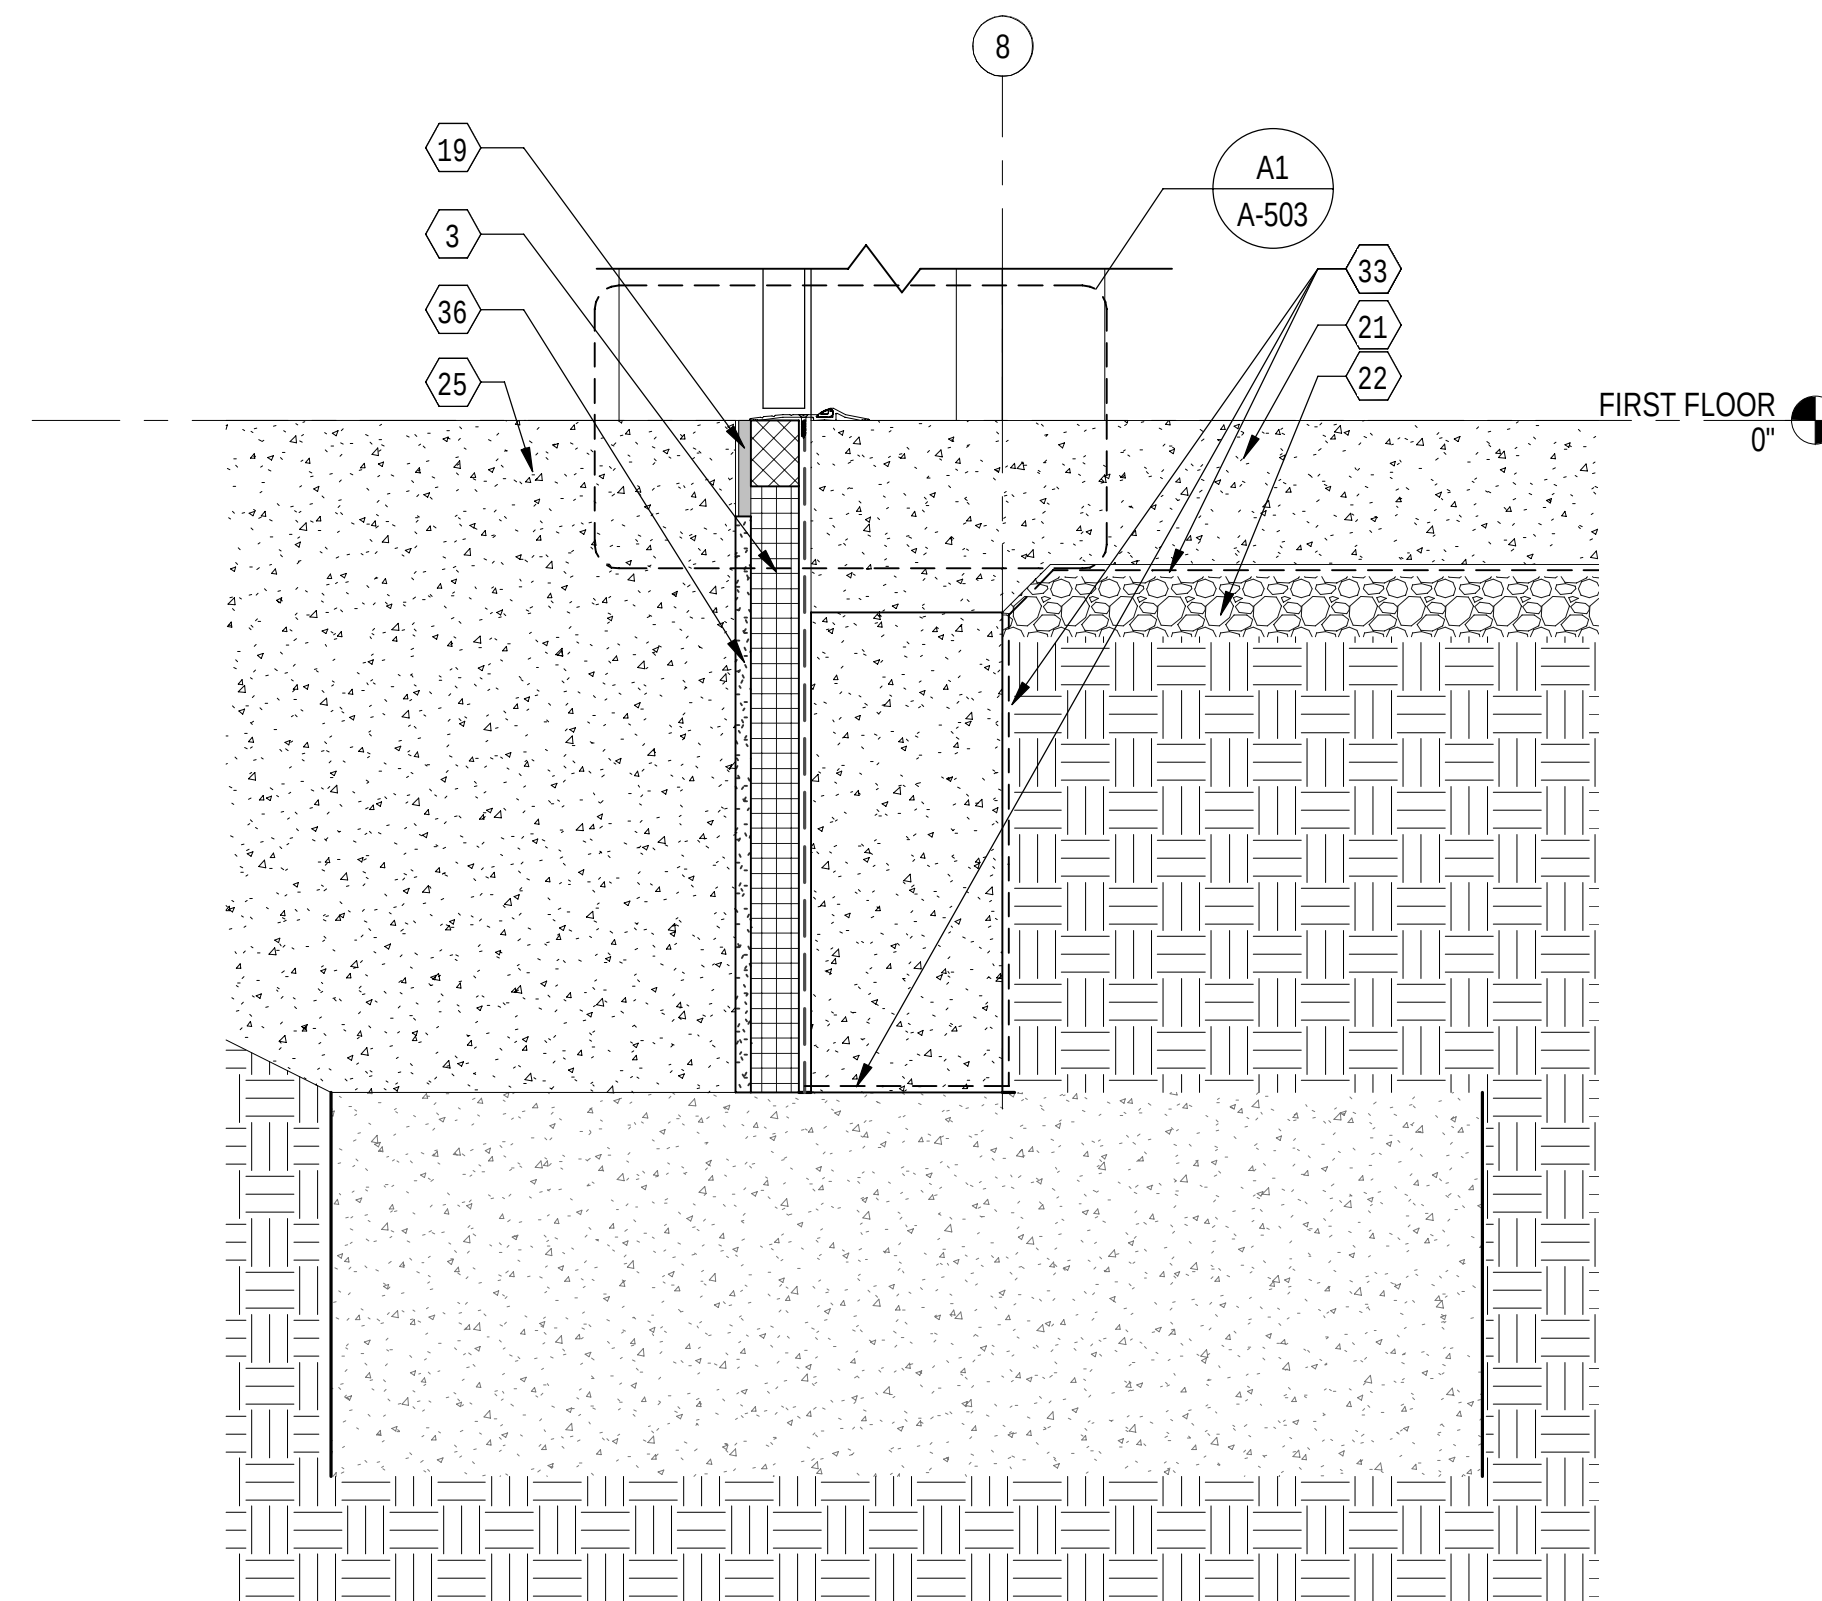

A3 ENTRY/ FOUNDATION DETAIL
1 1/2" = 1'-0" (A-302)

SHEET KEYNOTES

- 1 ARCHITECTURAL CMU
- 2 AIRSPACE
- 3 R-13.3 FOIL-FACED CONT RIGID INSULATION
- 4 AIR BARRIER/ VAPOR RETARDER
- 5 LIPPED ARCHITECTURAL CMU
- 6 WEEP VENT INSERTS AT 24" OC
- 7 THERMALLY BROKEN VENEER ANCHOR, TYP
- 8 SCHEDULED CEILING
- 9 DELEGATED DESIGN, PRE-MANUFACTURED, PREFINISHED METAL CANOPY (MTL-2), TYP
- 10 1" HANGAR PIPE ASSEMBLY W/ THREADED ADJUSTED ROD
- 11 PREFINISHED SLOPED METAL COPING (MTL-1)
- 12 CONDUCTOR HEAD, TYP
- 13 FULLY ADHERED TPO MEMBRANE
- 14 5/8" COVER BOARD
- 15 MORTAR MESH
- 16 CONTINUOUS HEMMED THRU WALL FLASHING
- 17 GROUT CAVITY
- 18 SCHEDULED PARTITION
- 19 1/2" JOINT FILLER
- 20 EXTERIOR GRADE NAILER
- 21 CONCRETE SLAB, REFER STRUCTURAL
- 22 COMPACTED GRAVEL SUB-BASE, REFER TO STRUCTURAL
- 23 GRADE, REFER TO CIVIL
- 24 CANOPY THRU-WALL FASTENER WITH COMPRESSION SPACER AS REQUIRED BY MFR, REFER TO STRUCTURAL FOR CONCRETE REQUIREMENTS AT FASTENER LOCATIONS
- 25 CONCRETE SIDEWALK (SLOPE AWAY FROM BUILDING), REFER TO CIVIL
- 26 2-1/2" X 12" ALUMINUM DECKING
- 27 EXTRUDED ALUMINUM FASCIA
- 28 INTERMEDIATE ALUMINUM TROUGH
- 29 CARRIAGE BOLT ASSEMBLY
- 30 ALUMINUM REAR CLIP ANGLE, W/ COUNTER FLASHING AND SEALANT
- 31 CANOPY GUTTER BY MFR
- 32 EXTRUDED ALUMINUM FASCIA (BEYOND)
- 33 VAPOR RETARDER
- 34 TPO MEMBRANE ADHERED TO WALL. EXTEND UP AND OVER COPING BLOCKING AND TERMINATE ON FACE OF COPING BLOCKING
- 35 AIR BARRIER TRANSITION MEMBRANE OVER 2" CONT FOAM
- 36 PROTECTION BOARD

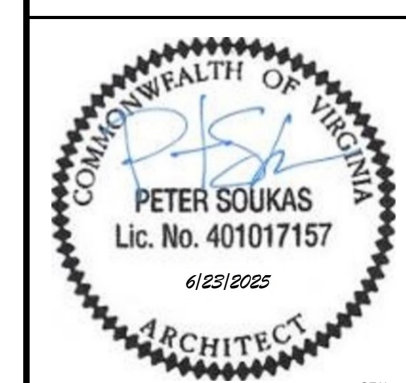[illegible]

Jacobs
1100 NORTH GLEBE ROAD
SUITE 500
ARLINGTON, VIRGINIA 22201
571.218.1000
FAX: 571.218.1600

	AE INFO
APPROVED	

FOR COMMANDER NAVFAC

ACTIVITY
APPROVED BY LCDR ELIZABETH
OLOKODE NAVFAC NLON FEAD
DIRECTOR NEW LONDON, GROTON, CT

SATISFACTORY TO DATE 05/27/2025

DES	PS	DRW	PS	CHK	WS
-----	----	-----	----	-----	----

PM/DM	SMS/ CWJ
-------	----------

BRANCH MANAGER	DJD
----------------	-----

CHIEF ENGINEER	JWJ
----------------	-----

FIRE PROTECTION HPN

ENGINEERING SYSTEMS COMMAND
ND - MID-ATLANTIC
NAVAL STATION - NORFOLK, VA
GROTON, CONNECTICUT
OPERATIONS FACILITY

SCALE: AS NOTED

EPROJECT NO.:	1667770
---------------	---------

CONSTR. CONTR. NO.



NAVJAG DRAWING NO.

A-501

6/20/2025 10:33:11 AM A-503
\\b1c1v9d1\\dgm\\FDZE1628\\ARCH\\BLOGS-1667770-A-BIM.rvt


A

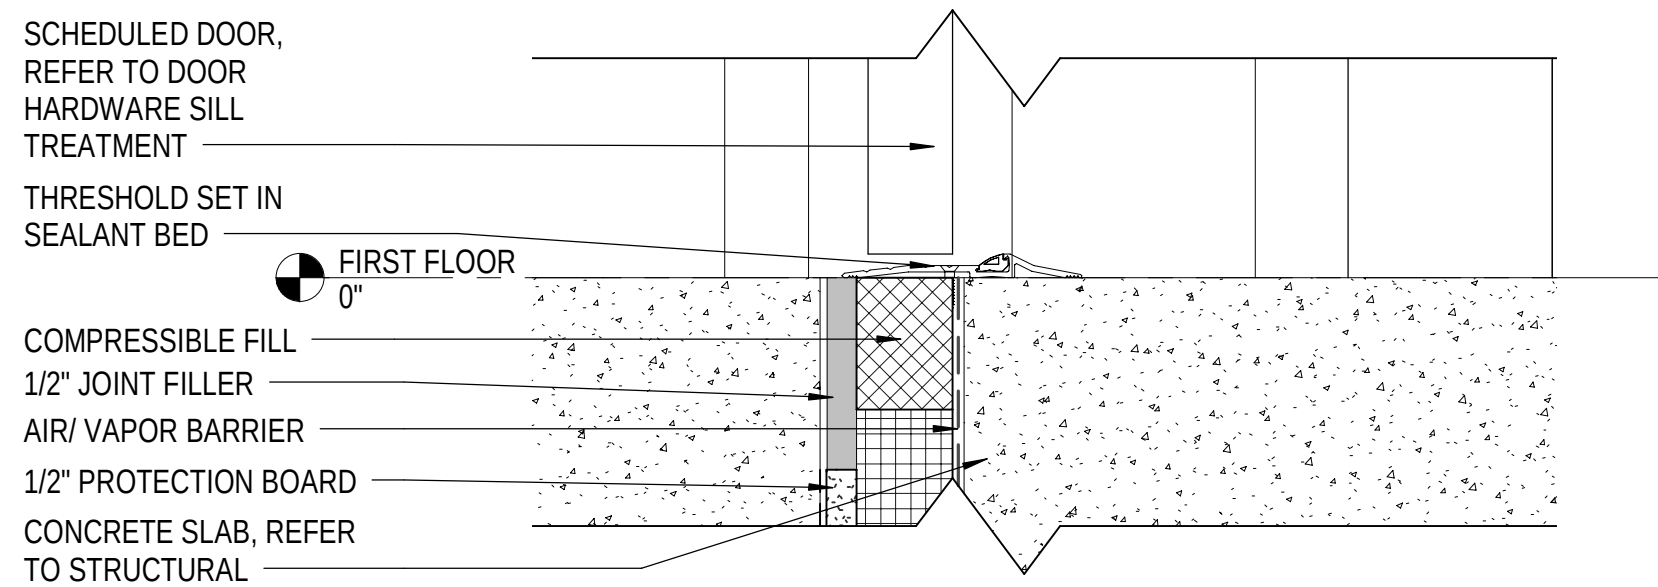

A1 EXT DOOR SILL DETAIL
3" = 1'-0" (A-501)


B

B1 EXT DOOR JAMB DETAIL
3" = 1'-0"

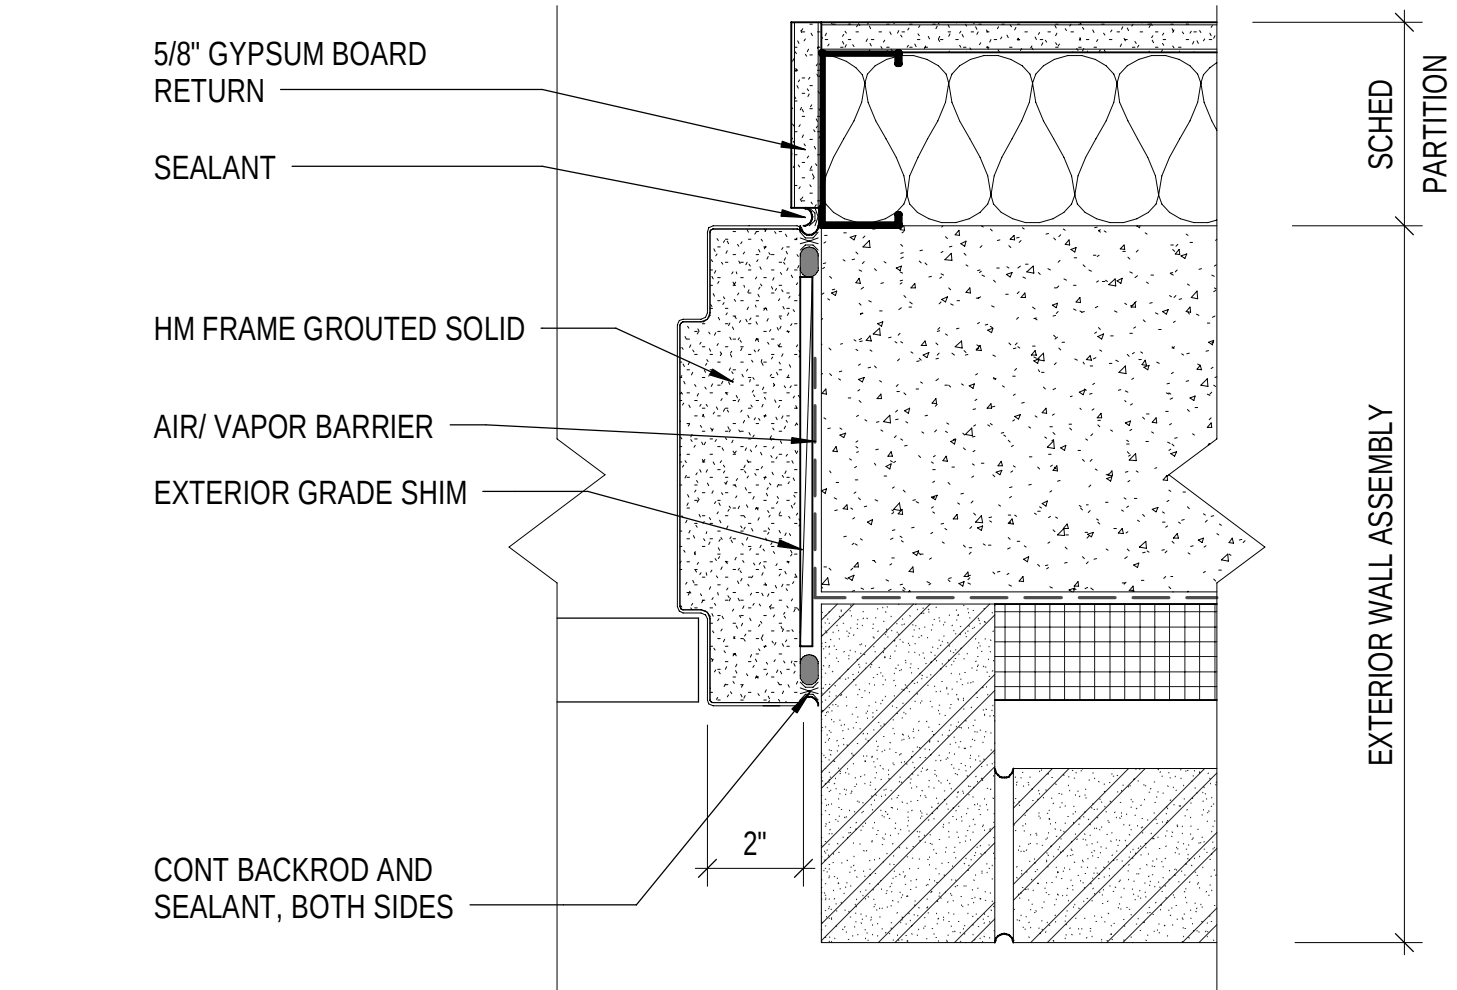

C


C1 EXT HM DOOR HEAD DETAIL
3" = 1'-0" (A-501)

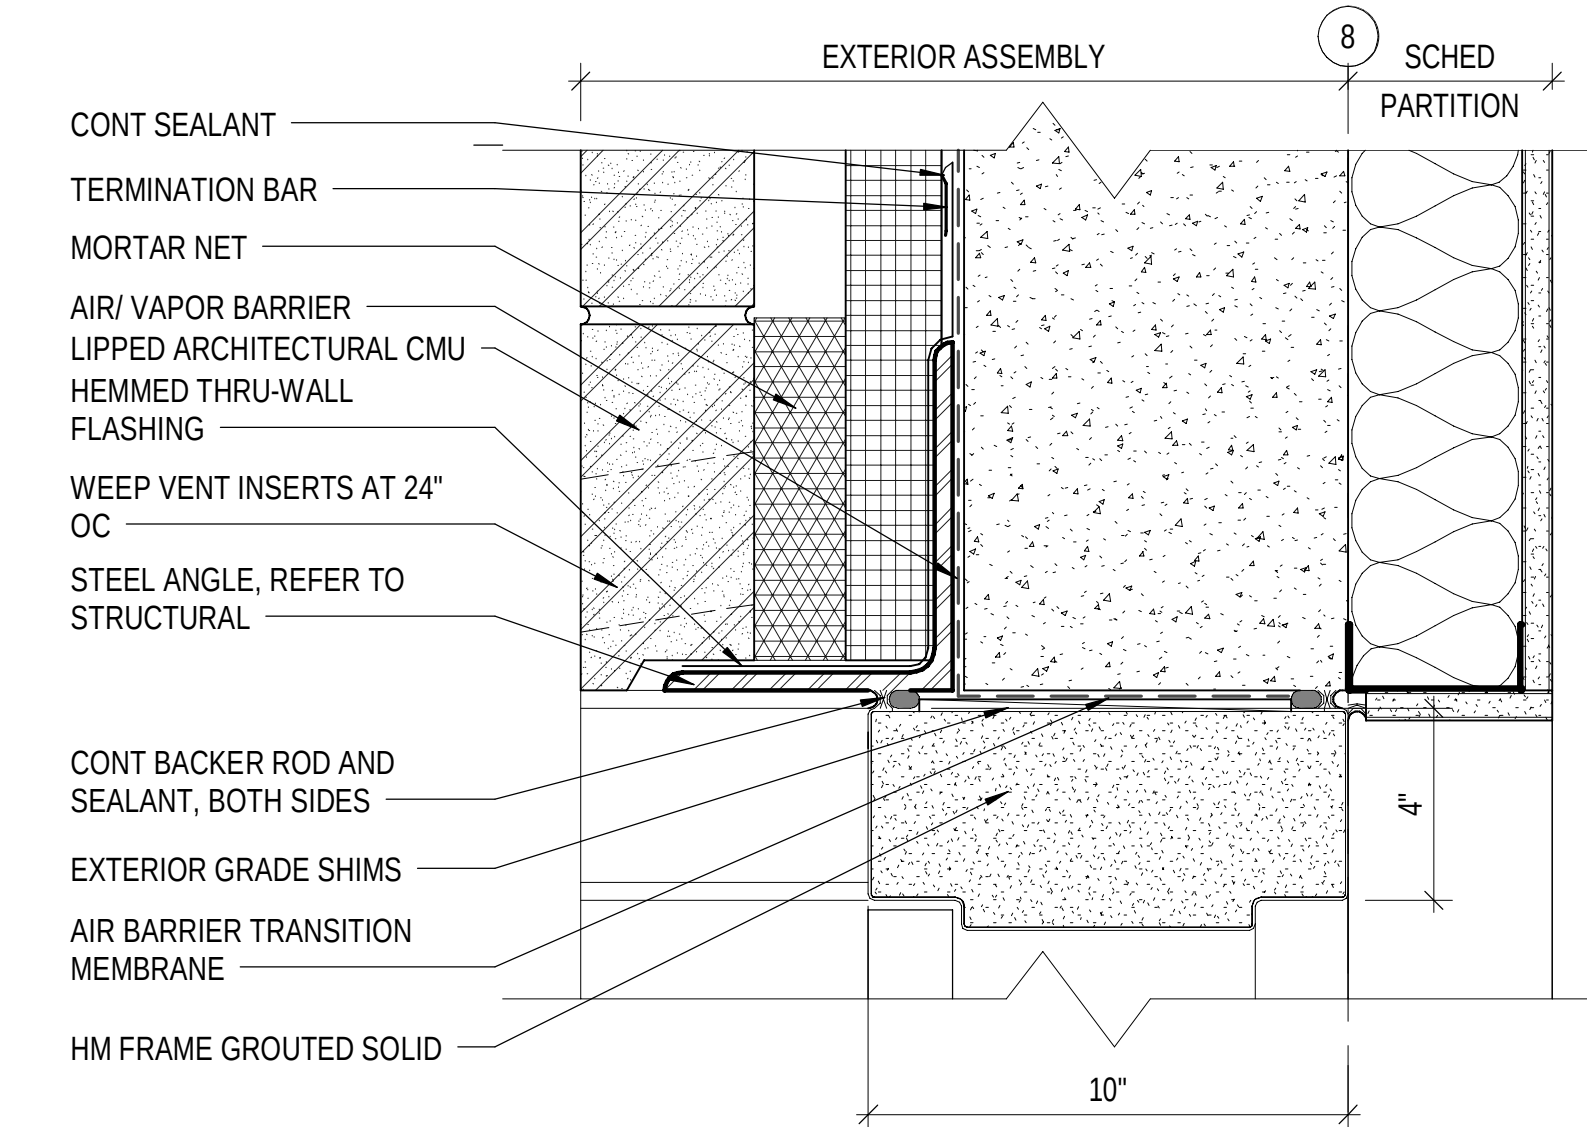


D

2


A2 ARMORY DOOR SILL DETAIL
3" = 1'-0"

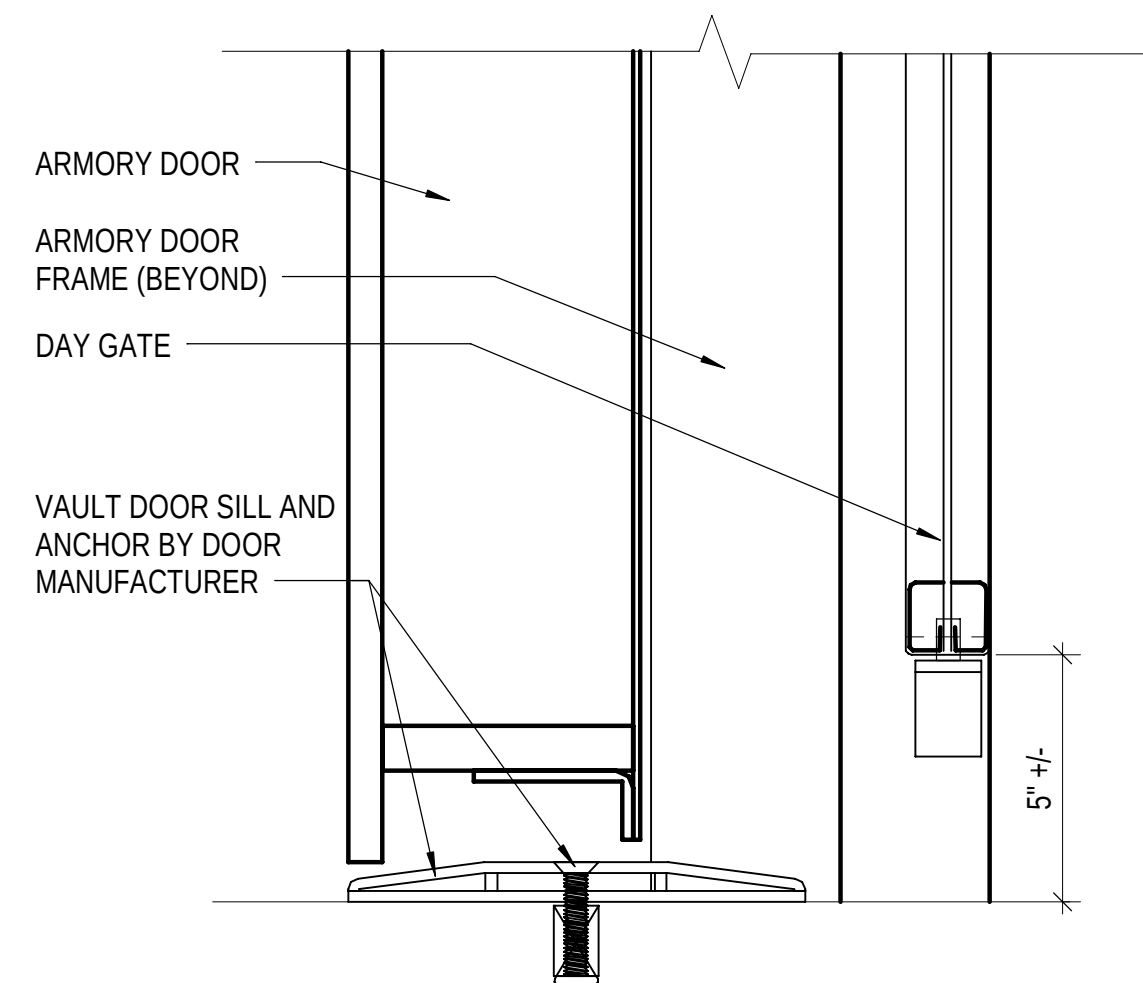

B2 ARMORY DOOR JAMB DETAIL
3" = 1'-0"

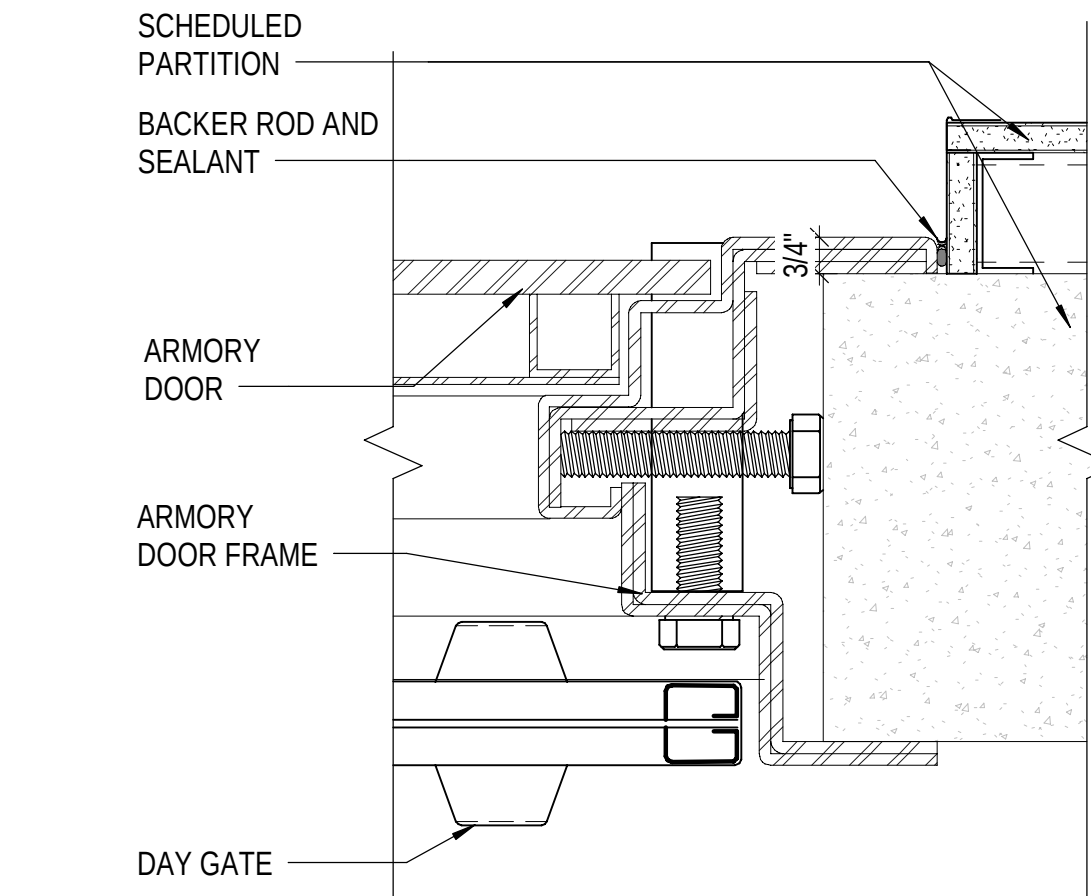


C2 ARMORY DOOR HEAD DETAIL
3" = 1'-0"

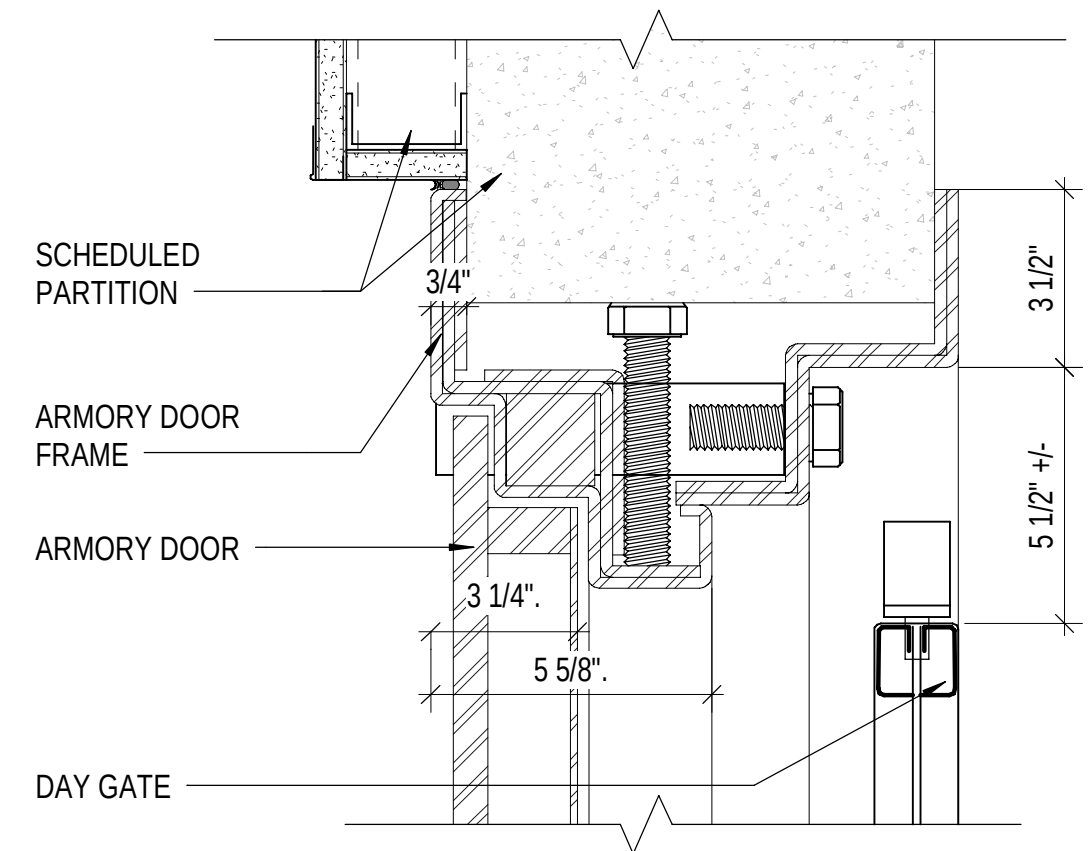


3


A3 EXT LOUVER SILL DETAIL
3" = 1'-0"

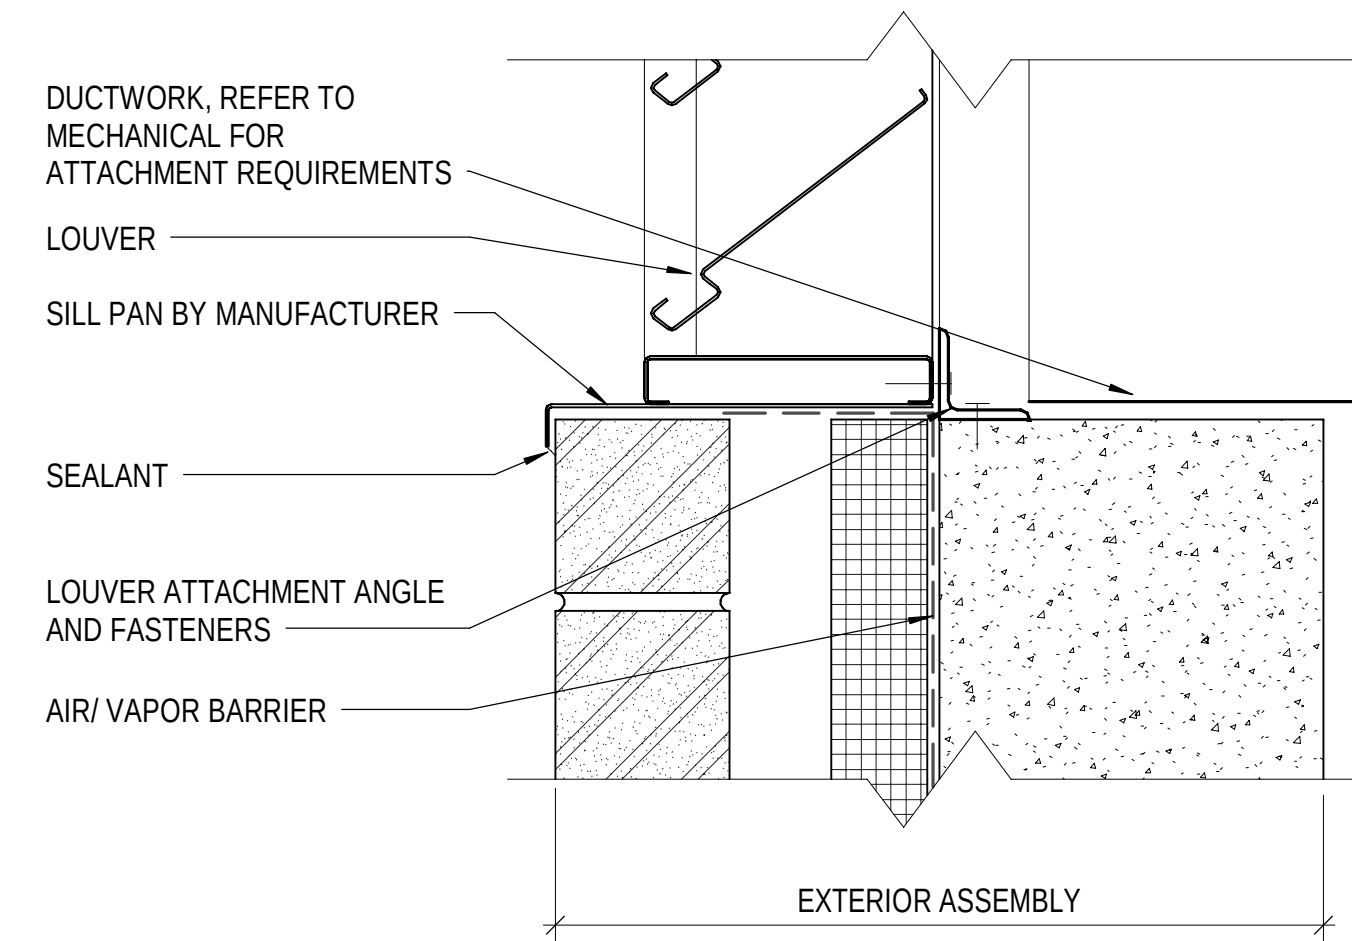

B3 EXT LOUVER JAMB DETAIL
3" = 1'-0"

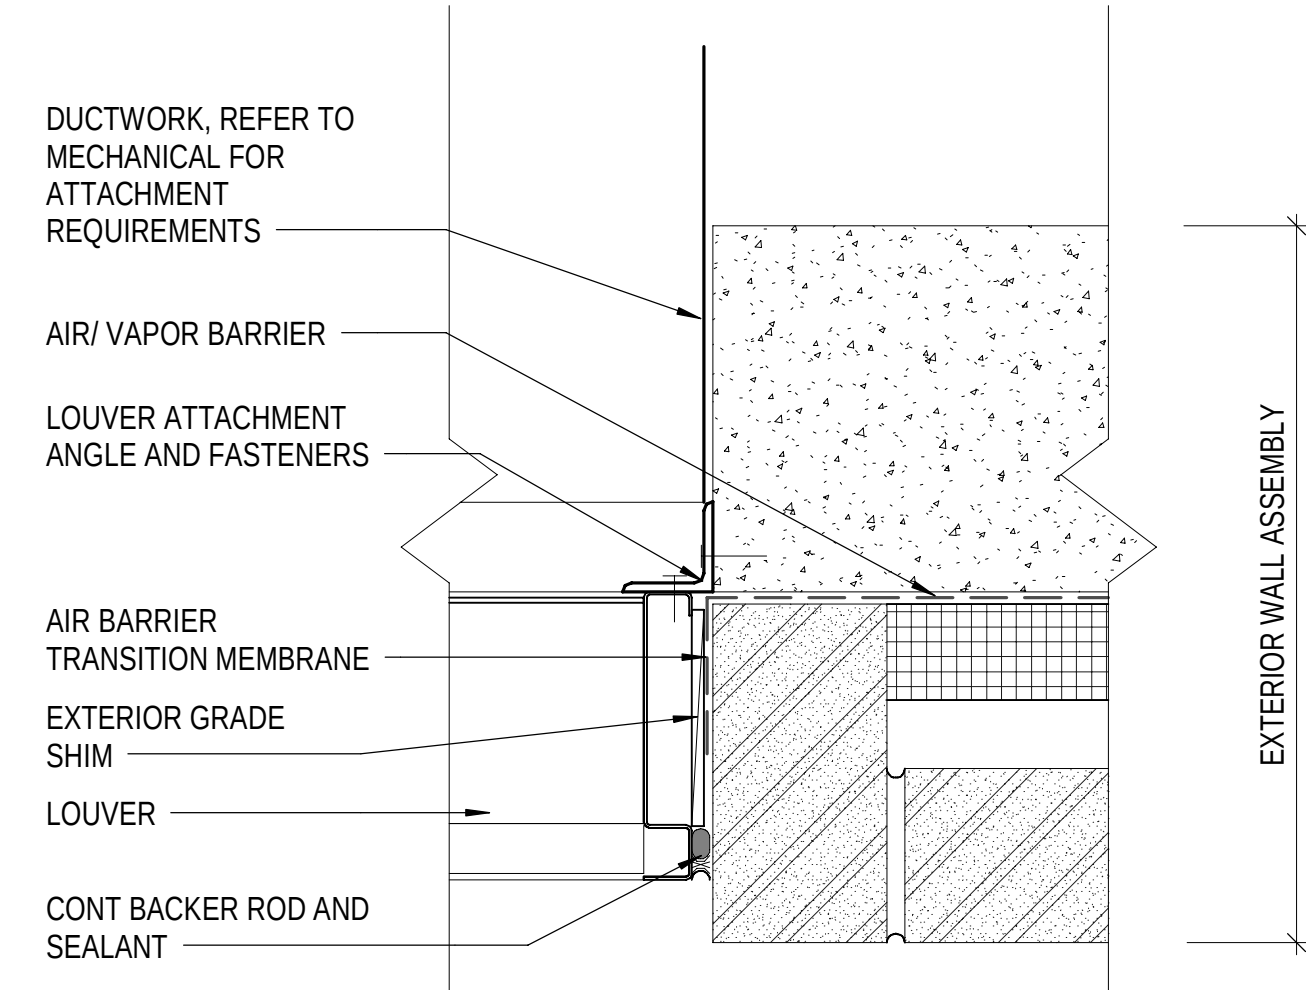


C3 EXT LOUVER HEAD DETAIL
3" = 1'-0"

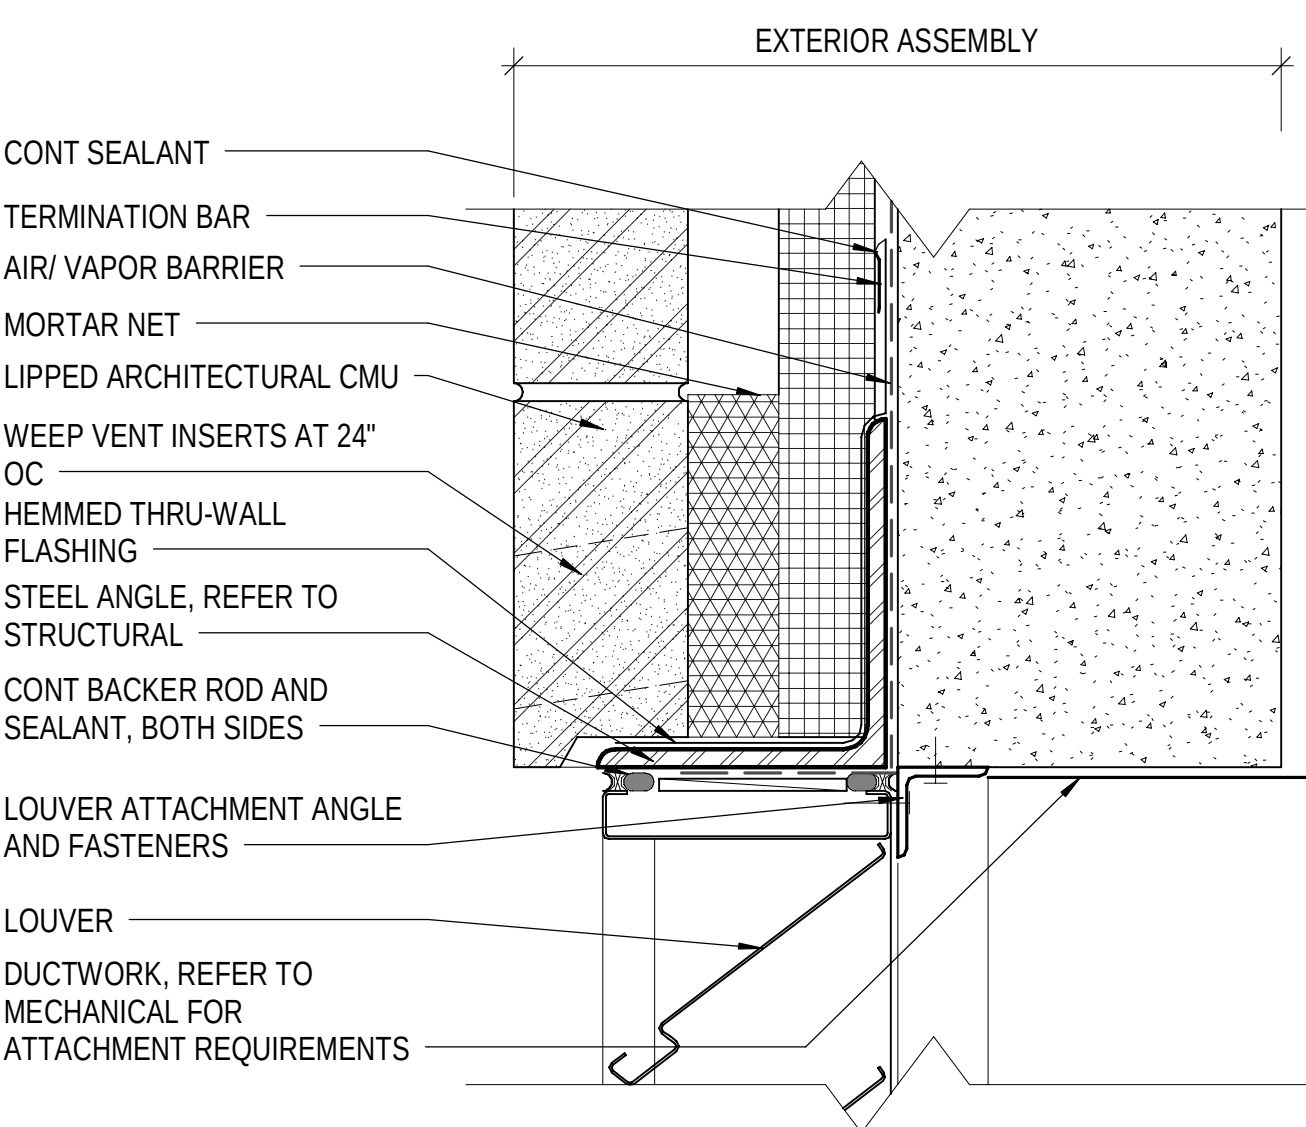


5


A4 INT. DOOR HEAD/ JAMB DETAIL
3" = 1'-0"

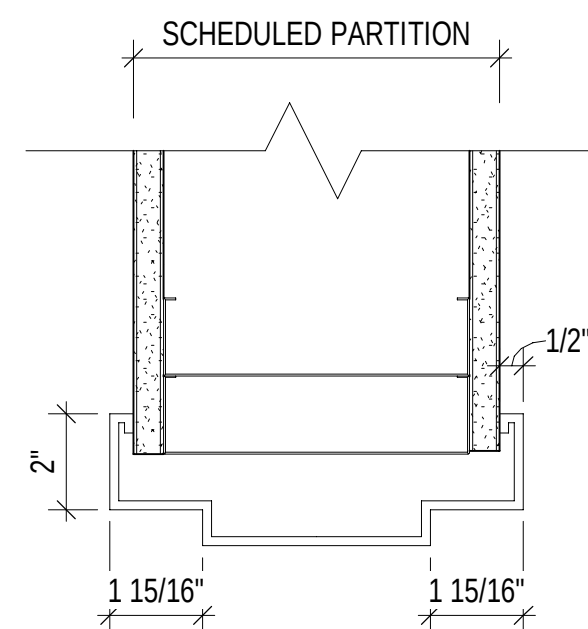

B4 AIR BARRIER AT CONTROL JOINT
3" = 1'-0"

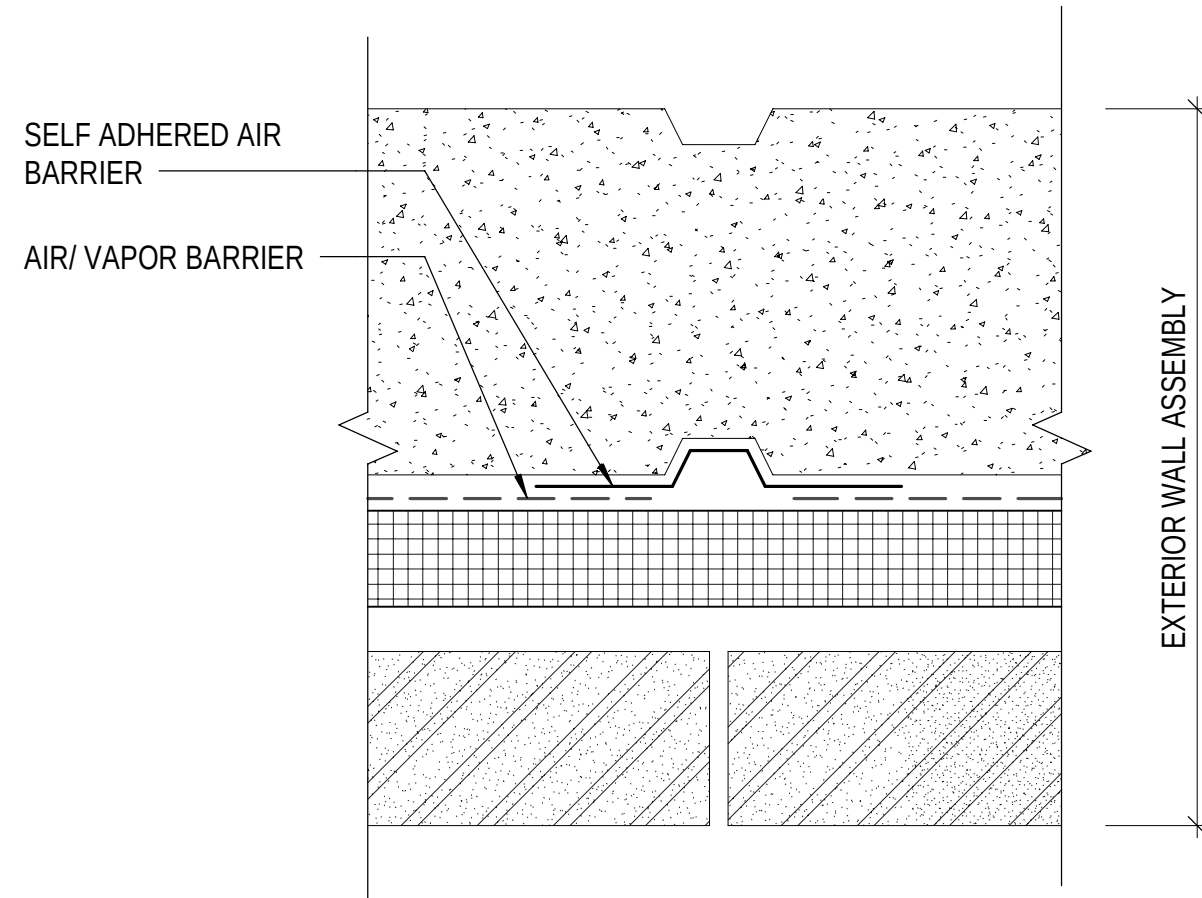

C4 TYPICAL PENETRATION AT AIR BARRIER
3" = 1'-0"

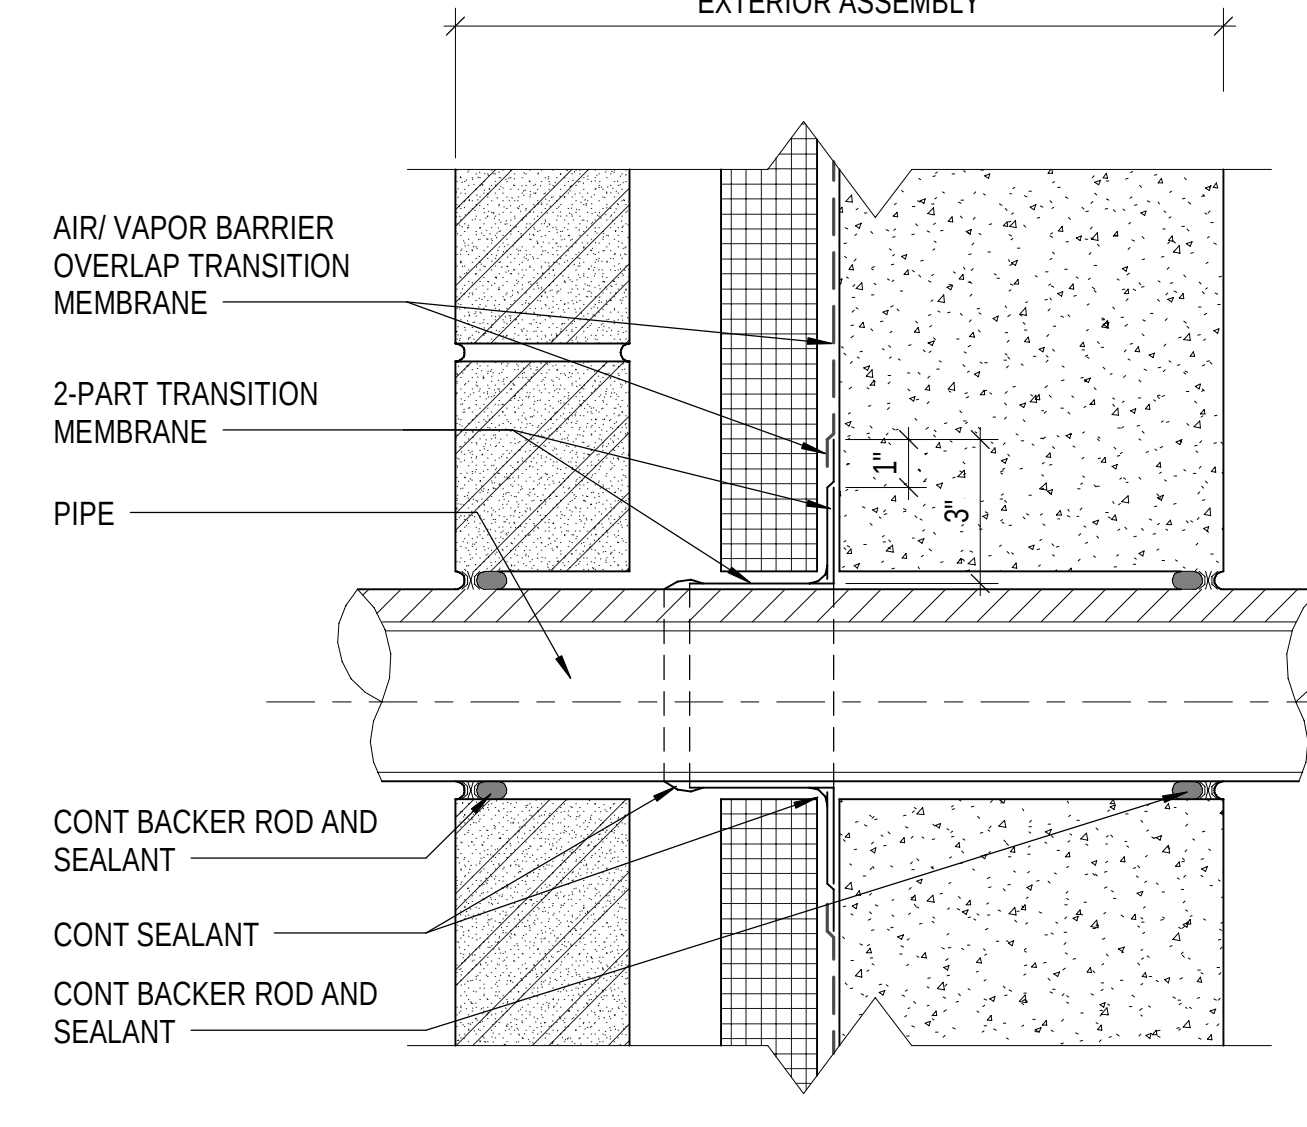

A

OPENING DETAILS

B

AE INFO

DEPARTMENT OF THE NAVY
NAVAL FACILITIES ENGINEERING SYSTEMS COMMAND - MID-ATLANTIC
NAVAL STATION - NORFOLK, VA
NAVAL FACILITIES ENGINEERING SYSTEMS COMMAND - MID-ATLANTIC
NAVAL SUBMARINE BASE NEW LONDON
P-1102 WEAPONS MAGAZINE & ORDNANCE OPERATIONS FACILITY
GROTON, CONNECTICUT
OPERATIONS

FOR COMMANDER NAVFAC
ACTIVITY APPROVED BY LCDR ELIZABETH CLOKODE NAVFAC NLON HEAD DIRECTOR NEW LONDON, GROTON, CT
SATISFACTORY TO DATE 05/27/2025
DES PS DRW PS CHK WS
BRANCH MANAGER SMS/ CWJ
CHIEF ENGINEER DJD
CHIEF ARCHITECT JMJ
FIRE PROTECTION HPN

APPROVED

Jacobs
1100 NORTH GLEBE ROAD
SUITE 500
ARLINGTON, VIRGINIA 22201
571.218.1000
FAX: 571.218.1600

COMMONWEALTH OF VIRGINIA
PETER SOUKAS
Lic. No. 401017157
6/23/2025
ARCHITECT



D

SYM DESCRIPTION DATE APPR


6/20/2025 10:33:13 AM A-510
\\ac119501\\dwg\\p\\FDZEL628\\AFCHBLDG-1667770-A-BIM.rvt

D

C


B

A

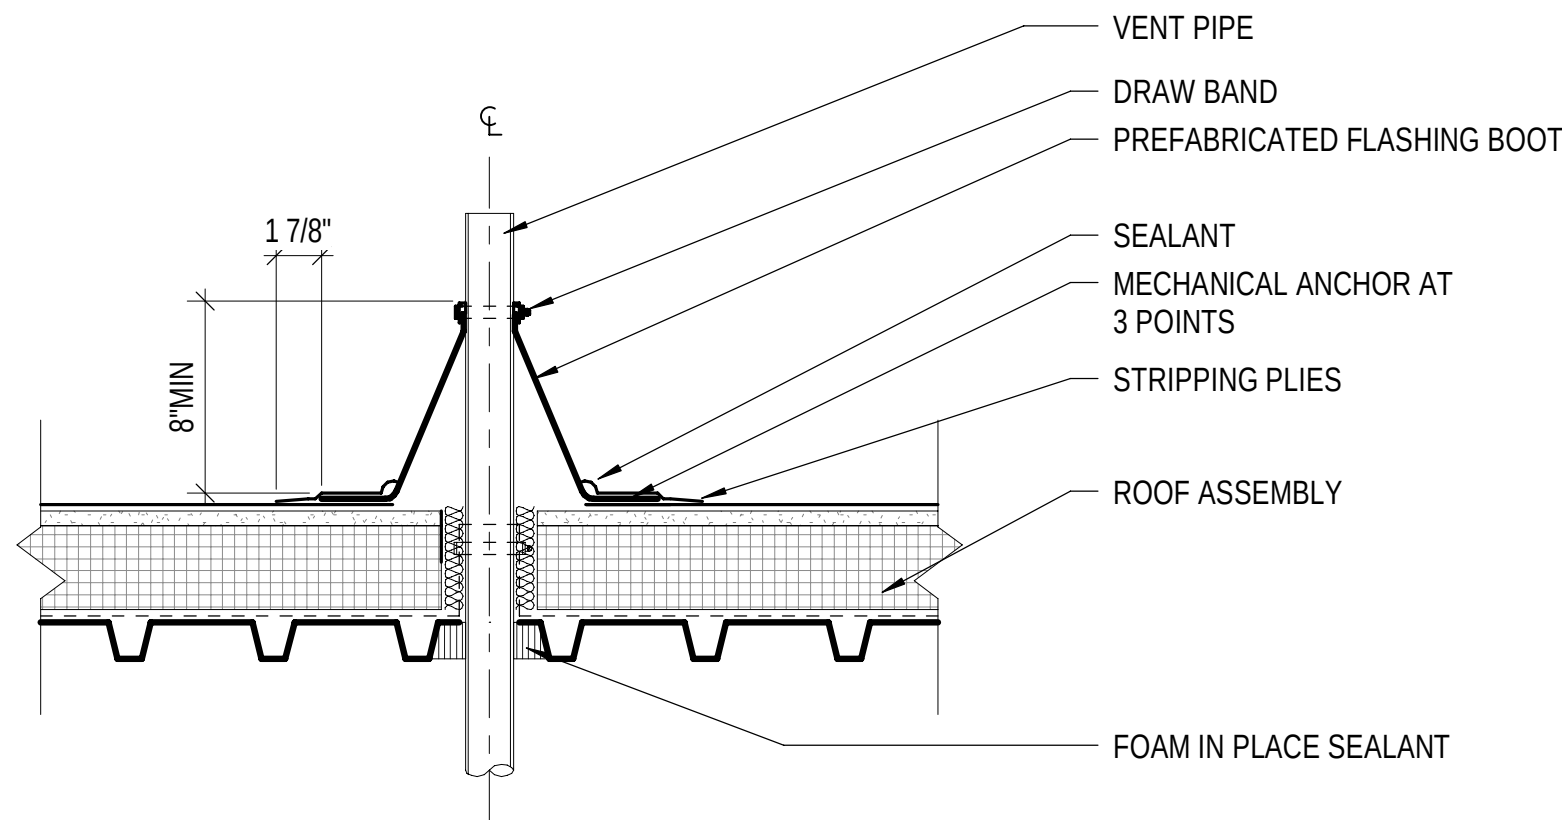


C1 TYPICAL PIPE PENETRATION

1 1/2" = 1'-0" (A-103)

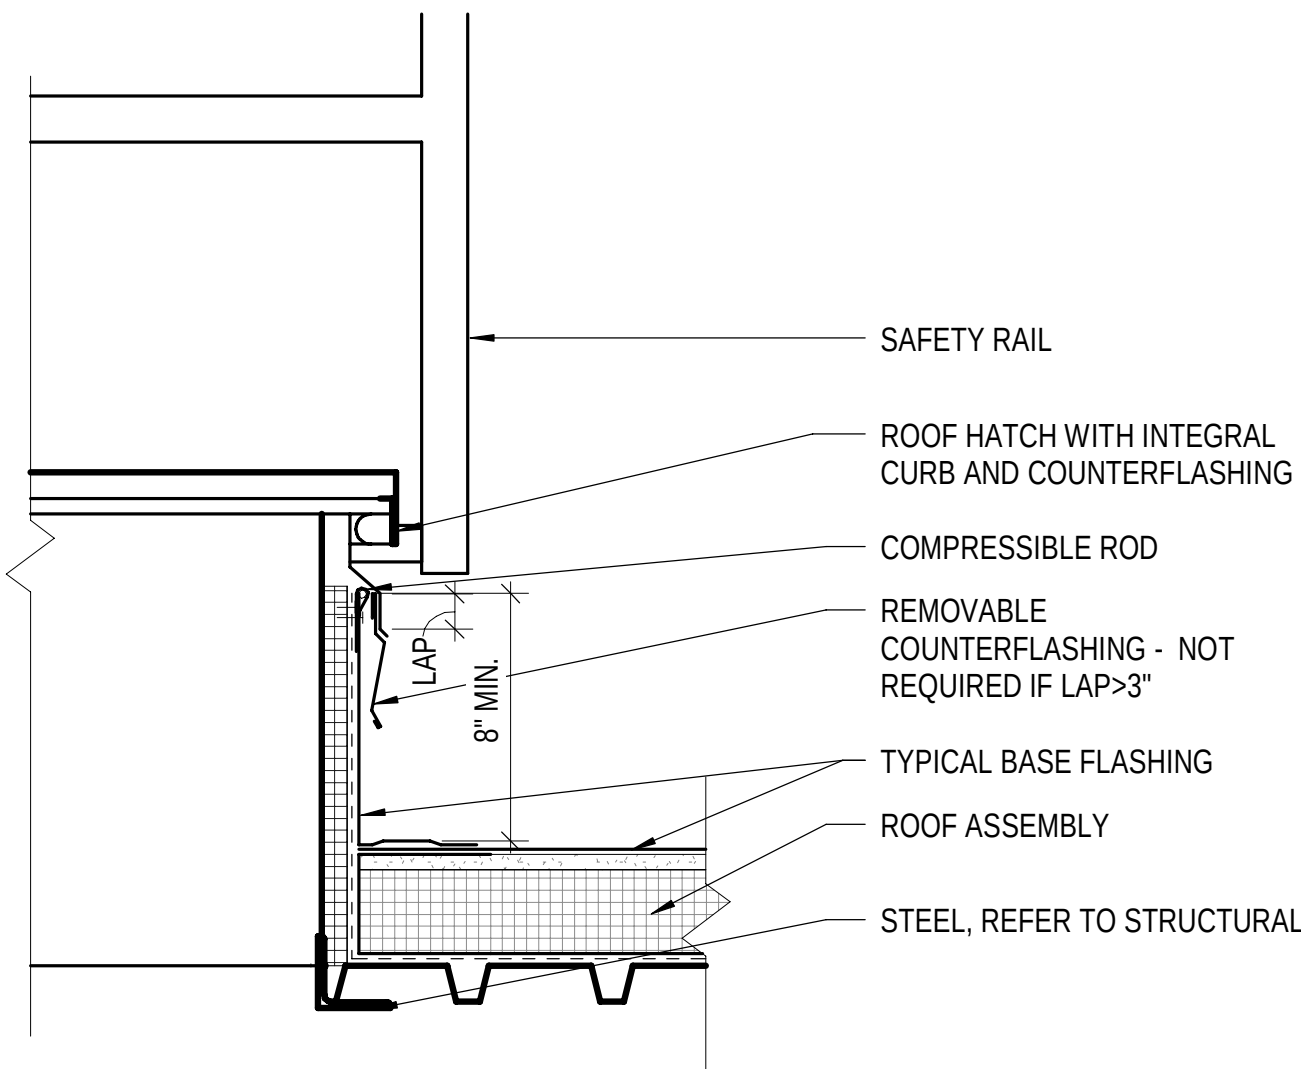

B1 ROOF HATCH DETAIL

1 1/2" = 1'-0" (A-103)

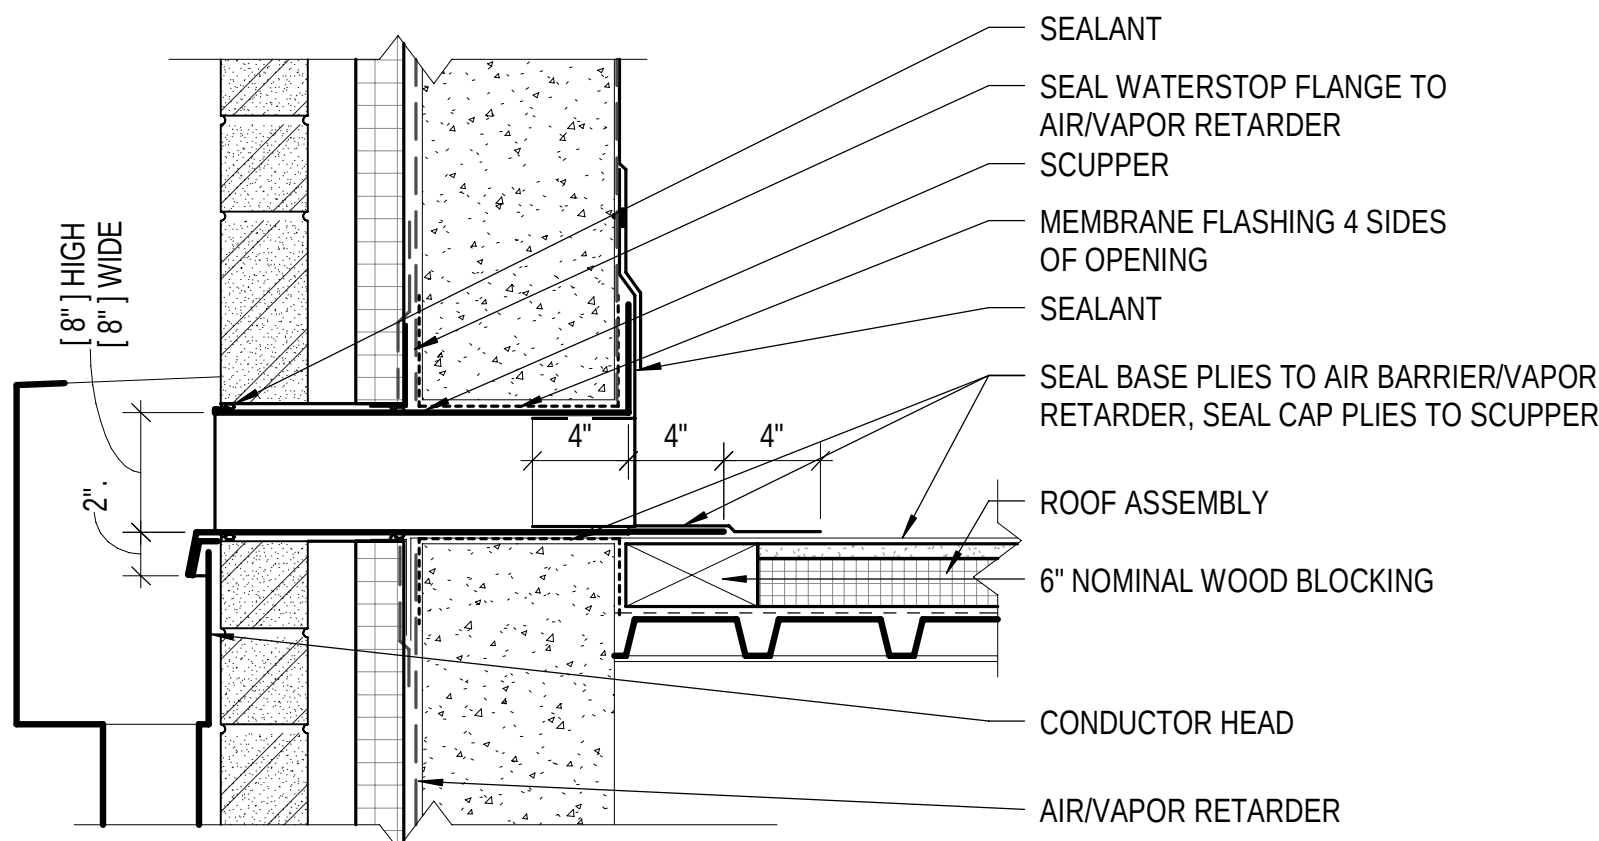

A1 TYPICAL SCUPPER/ CONDUCTOR HEAD DETAIL

1 1/2" = 1'-0" (A-103)

GENERAL SHEET NOTES

- A. TYPICAL DETAILS DO NOT GRAPHICALLY PORTRAY ROOF AND WALL ASSEMBLIES. REFER TO WALL SECTIONS FOR ASSEMBLIES.



Jacobs
1100 NORTH GLEBE ROAD
SUITE 500
ARLINGTON, VIRGINIA 22201
571.218.1600
FAX: 571.218.1600

APPROVED
AE INFO

FOR COMMANDER NAVFAC

ACTIVITY APPROVED BY LCDR ELIZABETH
CLOKODE NAVFAC NLON FEAD
DIRECTOR NEW LONDON, GROTON, CT

SATISFACTORY TO DATE 05/27/2025

DES	PS	DRW	PS	CHK	WS
-----	----	-----	----	-----	----

PM/DM SMSI/ CWJ

BRANCH MANAGER DJD

CHIEF ENGINEER JWJ


FIRE PROTECTION HPN

DEPARTMENT OF THE NAVY
NAVAL FACILITIES ENGINEERING SYSTEMS COMMAND
NAVAL FACILITIES ENGINEERING SYSTEMS COMMAND - MID-ATLANTIC
NAVAL STATION - NORFOLK, VA
NAVAL SUBMARINE BASE NEW LONDON
GROTON, CONNECTICUT
P-1102 WEAPONS MAGAZINE & ORDNANCE OPERATIONS FACILITY
OPERATIONS

TYPICAL ROOF DETAILS

SCALE: AS NOTED
EPROJECT NO.: 1667770
CONSTR. CONTR. NO.
NAVFAC DRAWING NO. 12893985
SHEET 35 OF 140


A-510

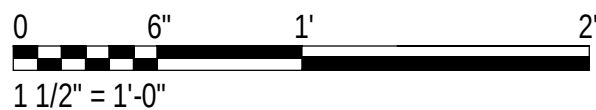


6/20/2025 10:33:16 AM
\\ac11901\lief\p\FDZ\EL628\AFCH\BLOG-166770-A-BIM.rvt

A-601

A

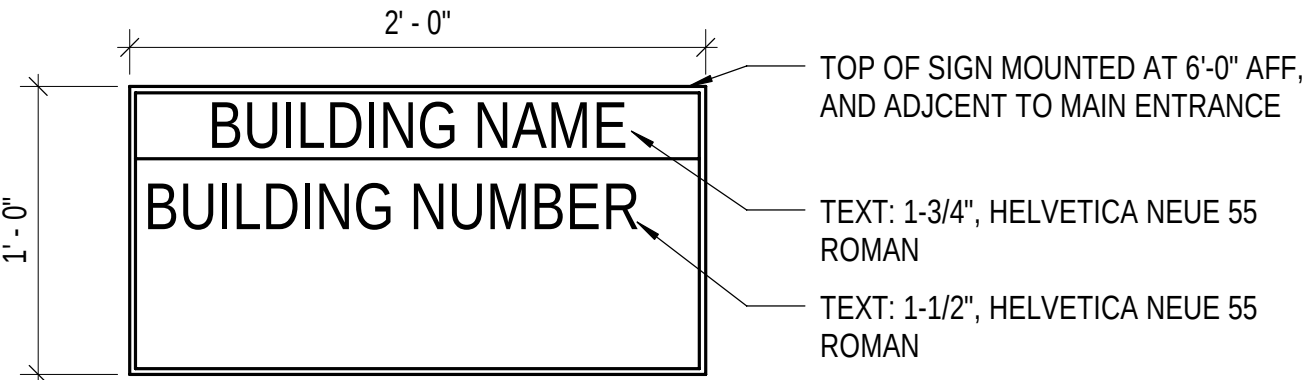


A1 BUILDING SIGNAGE
1 1/2" = 1'-0"

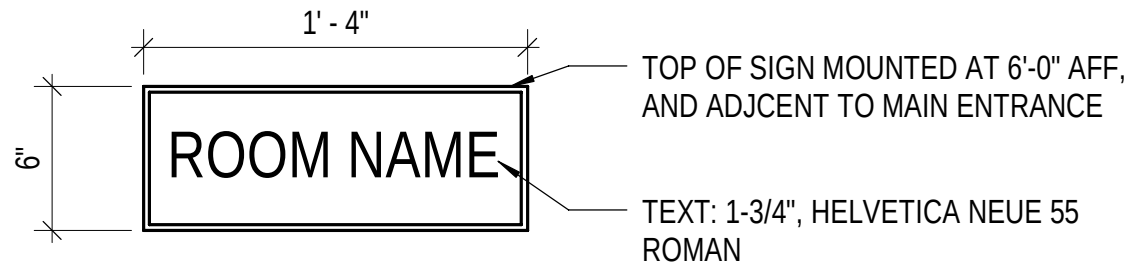


A2 ROOM SIGNAGE
1 1/2" = 1'-0"


B

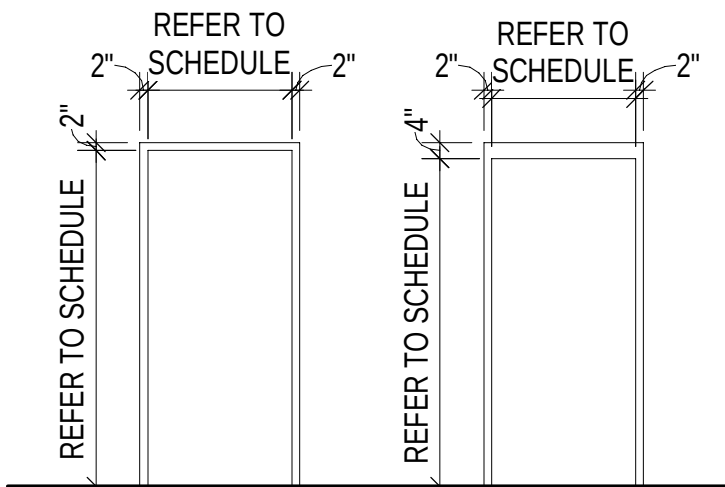

TYPE: F1 F2

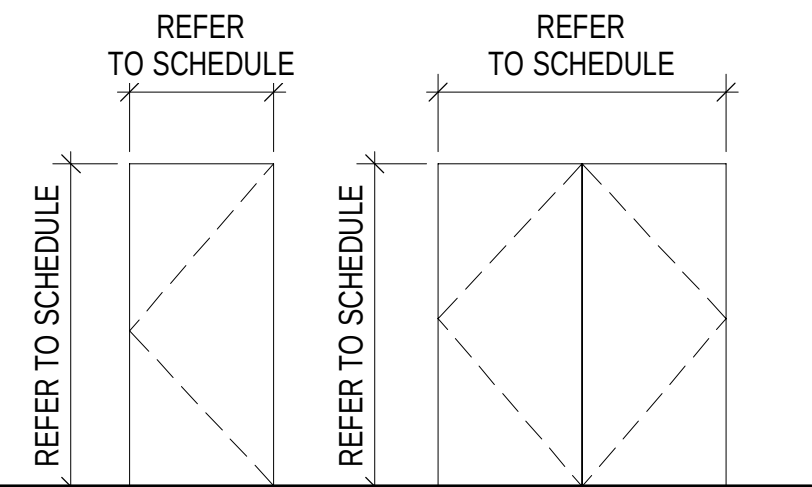


TYPE: A B

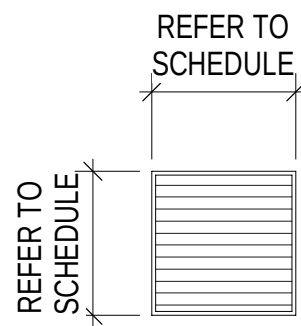

TYPE: L(#)

LOUVER TYPES
1/4" = 1'-0"

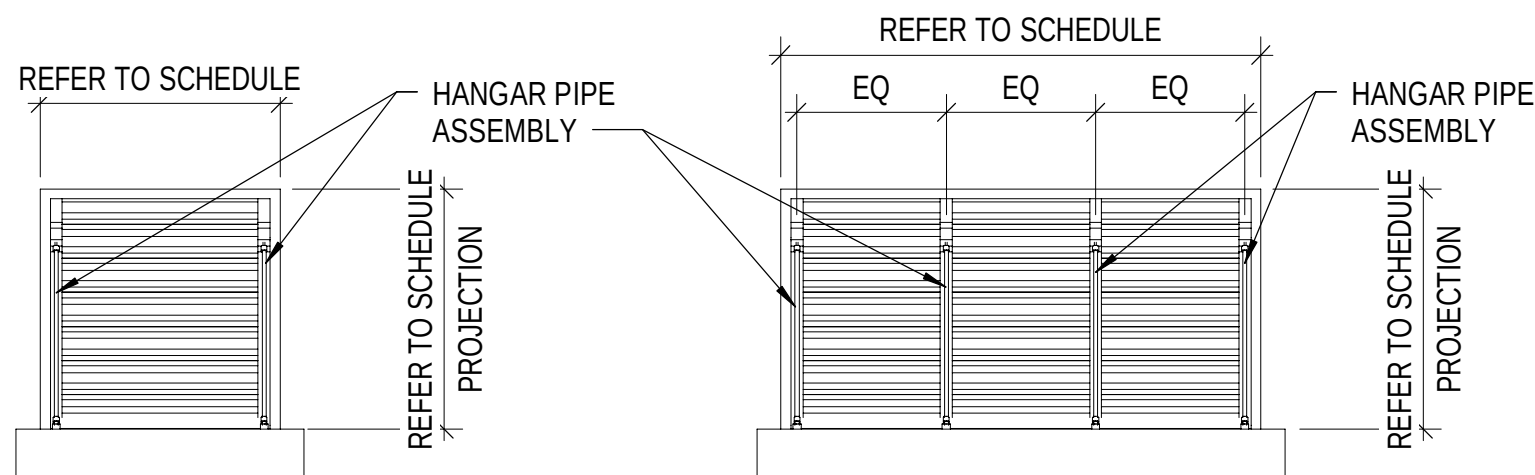


TYPE: C1 C2

CANOPY TYPES
1/4" = 1'-0"

GENERAL SHEET NOTES

A. REFER TO SPECIFICATION 08 71 00 FOR DOOR HARDWARE SETS.

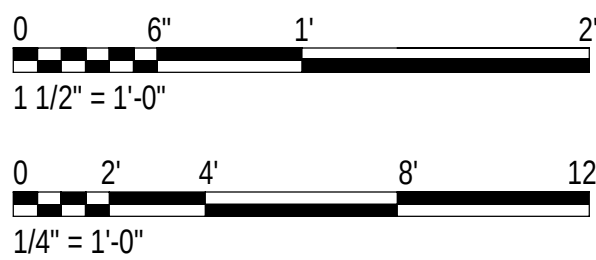

DEPARTMENT OF THE NAVY
NAVAL FACILITIES ENGINEERING SYSTEMS COMMAND - MID-ATLANTIC
MID-ATLANTIC
NAVAL SUBMARINE BASE NEW LONDON
P-1102 WEAPONS MAGAZINE & ORDNANCE OPERATIONS FACILITY
GROTON, CONNECTICUT
ARCHITECTURAL SCHEDULES

SCALE: AS NOTED
EPROJECT NO.: 1667770
CONSTR. CONTR. NO.
NAVFAC DRAWING NO. 12893986
SHEET 36 OF 140

A-601

A

B

B

AE INFO

Jacobs
1100 NORTH GLEBE ROAD
SUITE 500
ARLINGTON, VIRGINIA 22201
571.218.1000
FAX: 571.218.1600



C

D

DATE
SYN DESCRIPTION
APPR

D

C

B

A

1

2

3

4

5

1

2

3

4

5



SCALE: AS NOTED		
EPROJECT NO.:		1667770
CONSTR. CONTR. NO.		
NAVFAC DRAWING NO.		
12893987		
SHEET	37	OF 140
A-602		

B

GOVERNMENT FURNISHED / GOVERNMENT INSTALLED (GFGI) EQUIPMENT

A


6/20/2025 10:30:13 AM I-103 \\ac1v9d\\l\\e\\p\\FDZ\\E1628\\AFCH\\BLDG-1667770-A-BLM.rvt


D

C


B

A

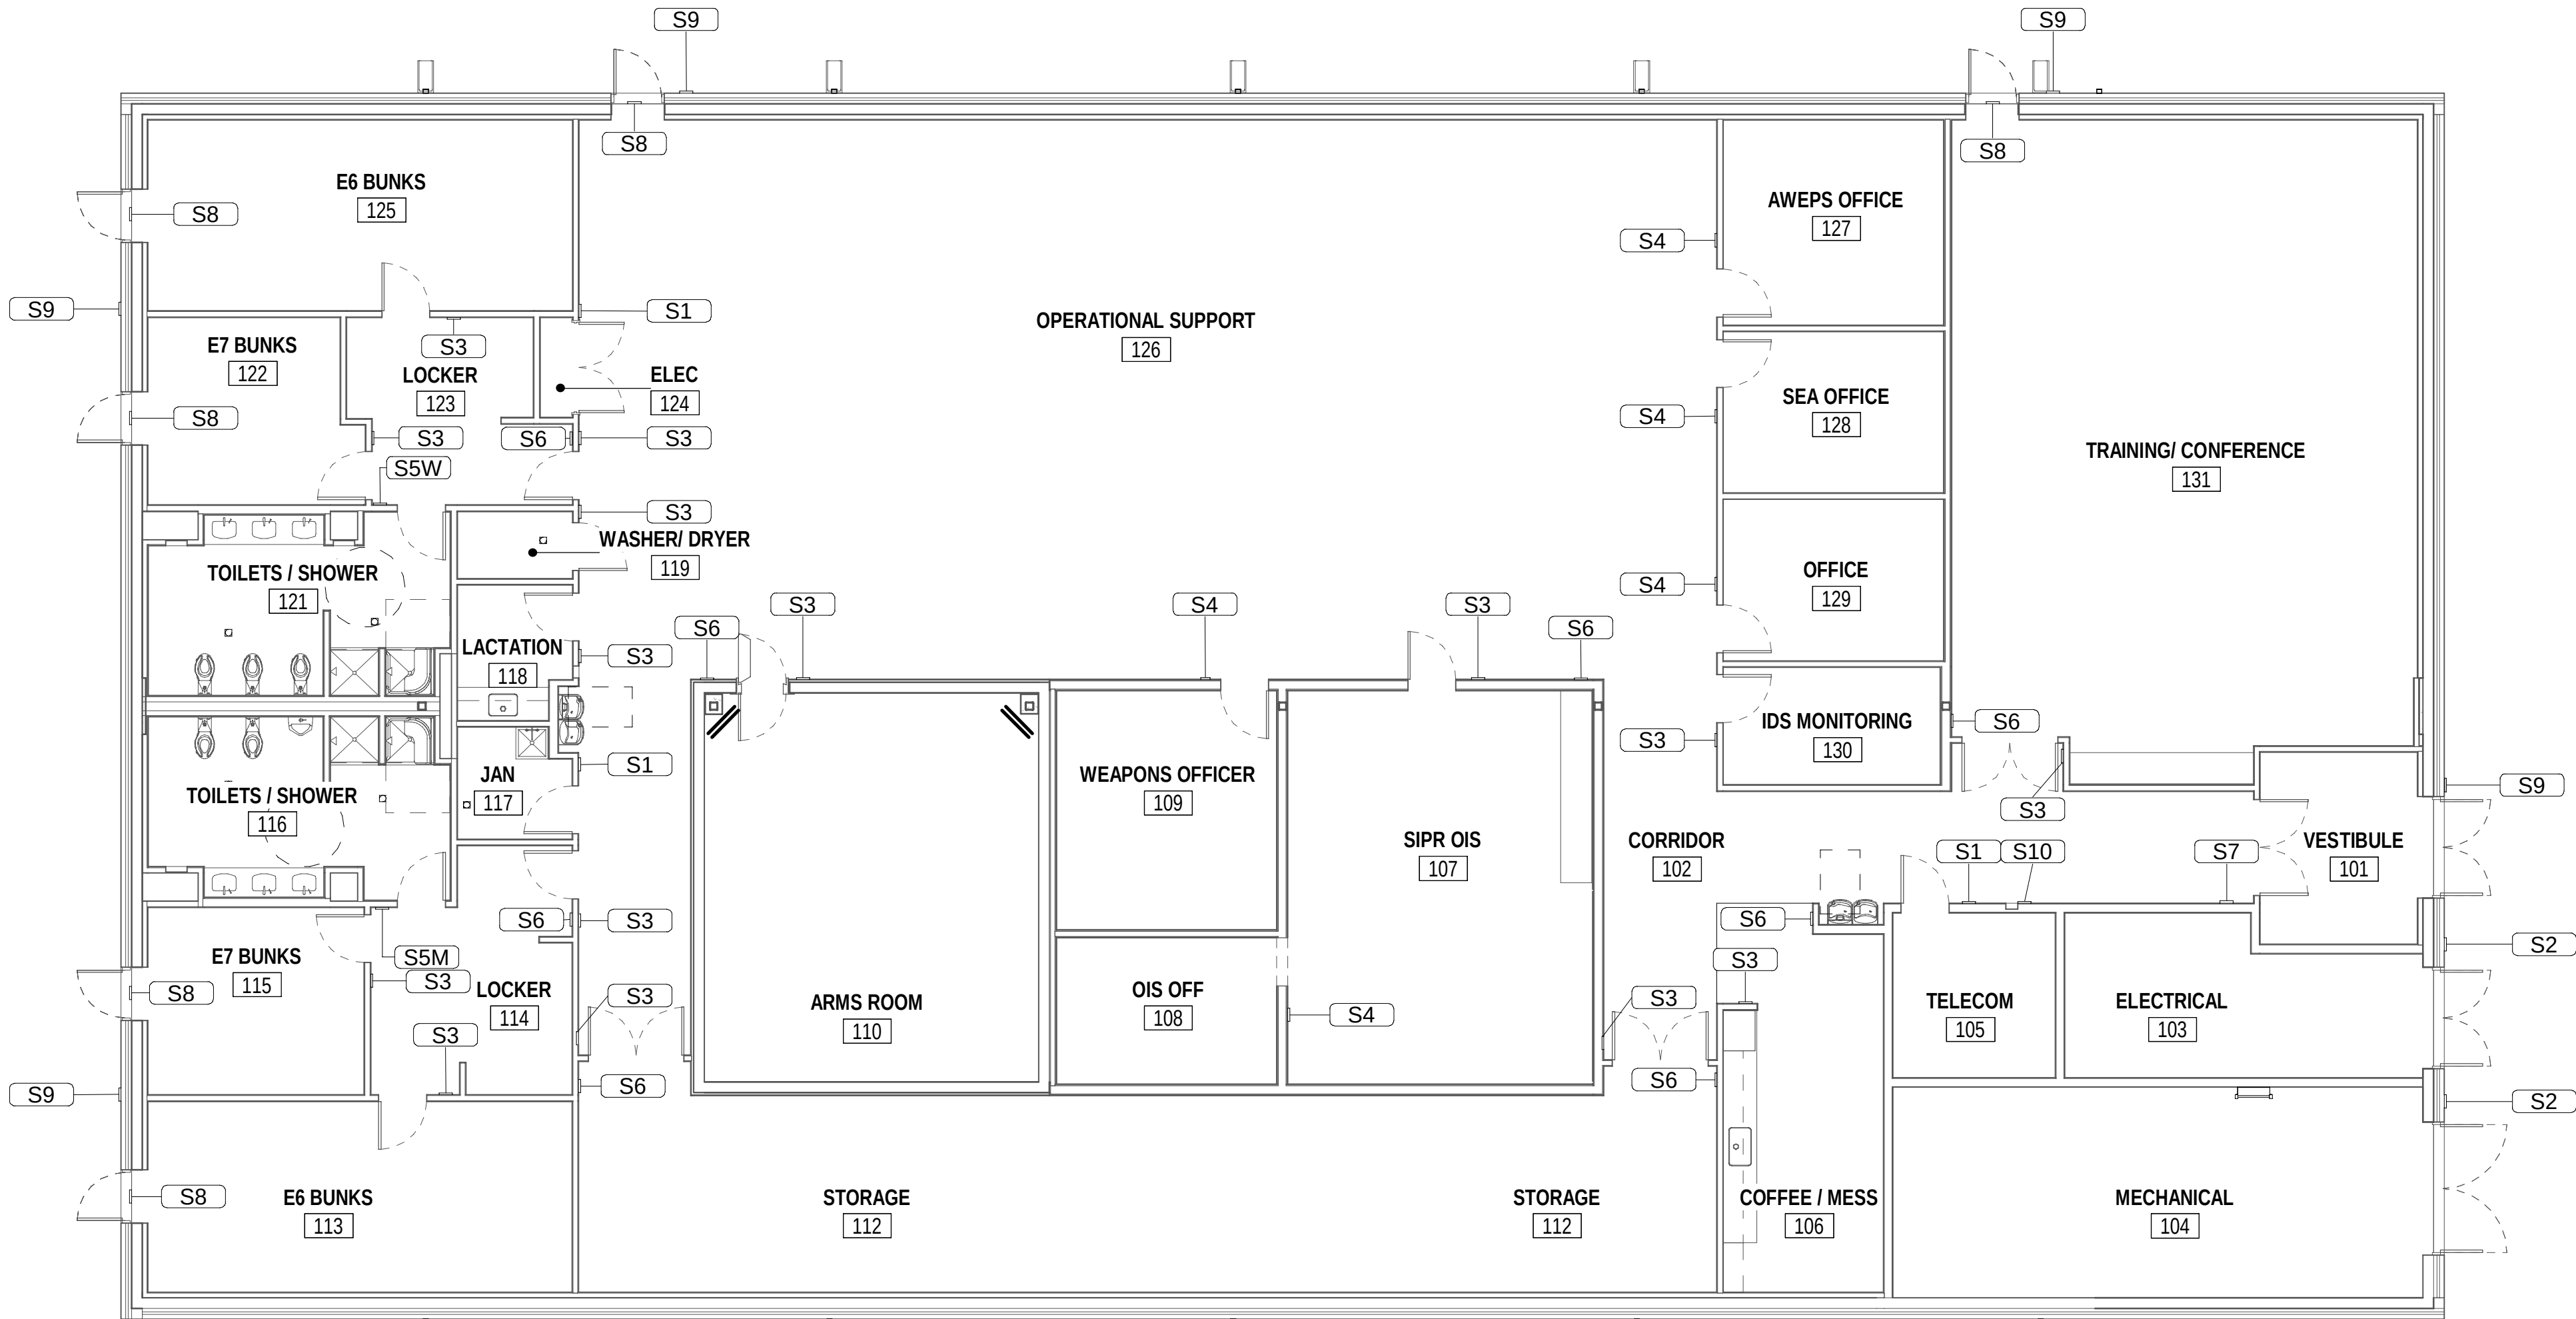


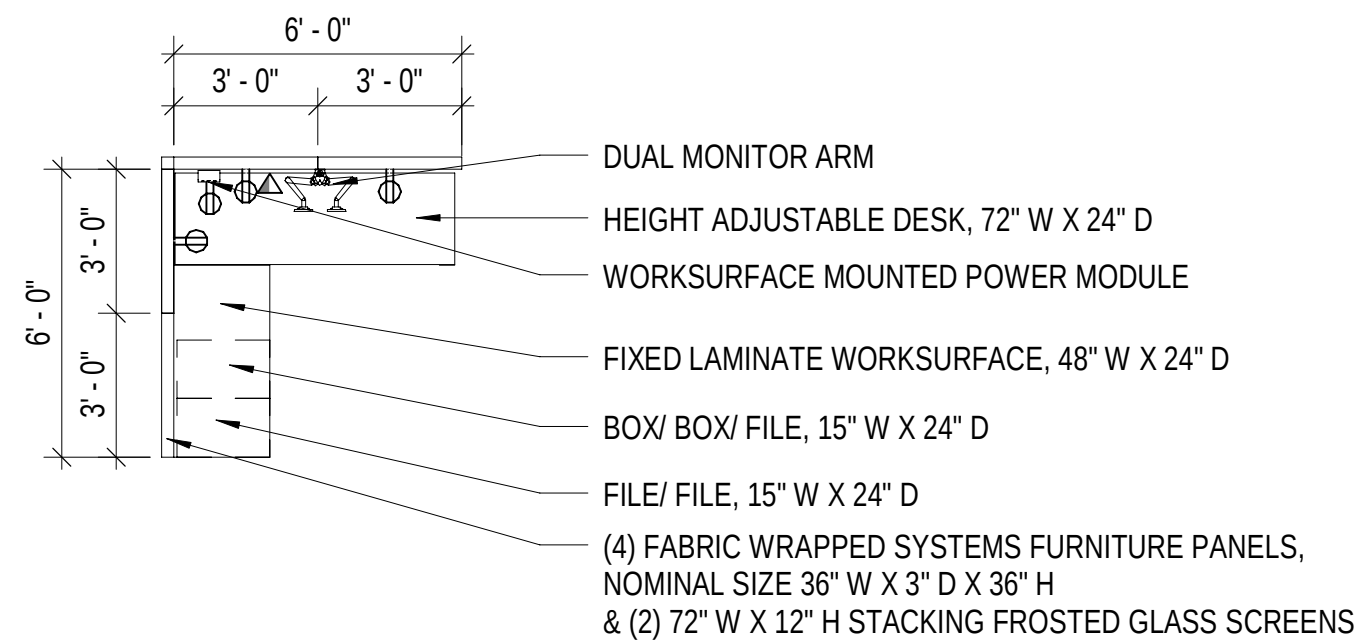


D1 WS01 WORKSTATION PLAN
1/4" = 1'-0"

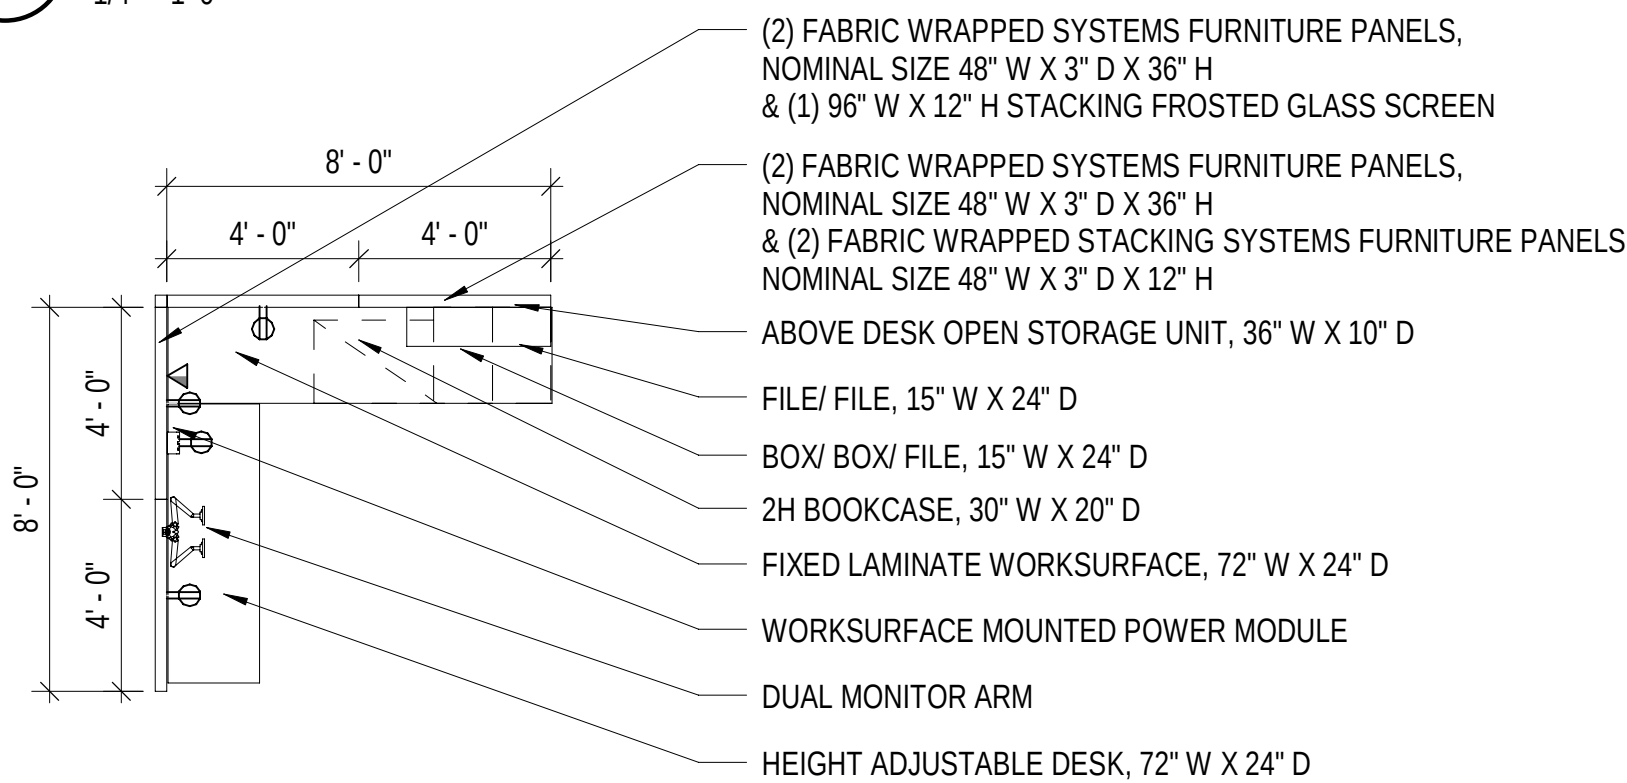


C1 WS02 WORKSTATION PLAN
1/4" = 1'-0"

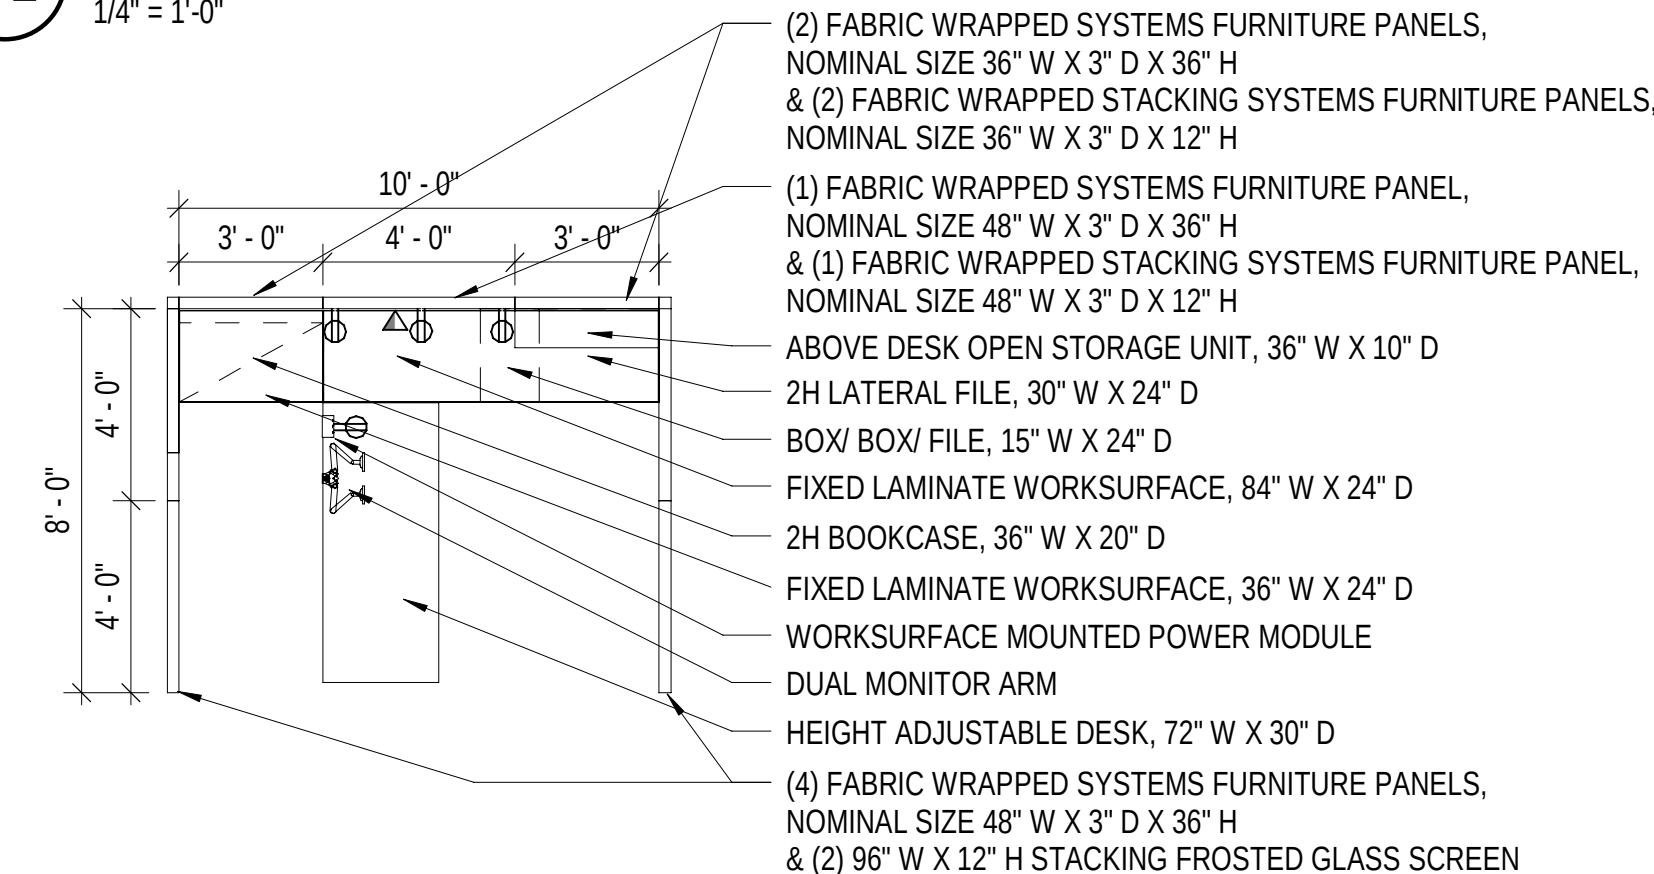


B1 WS03 WORKSTATION PLAN
1/4" = 1'-0"

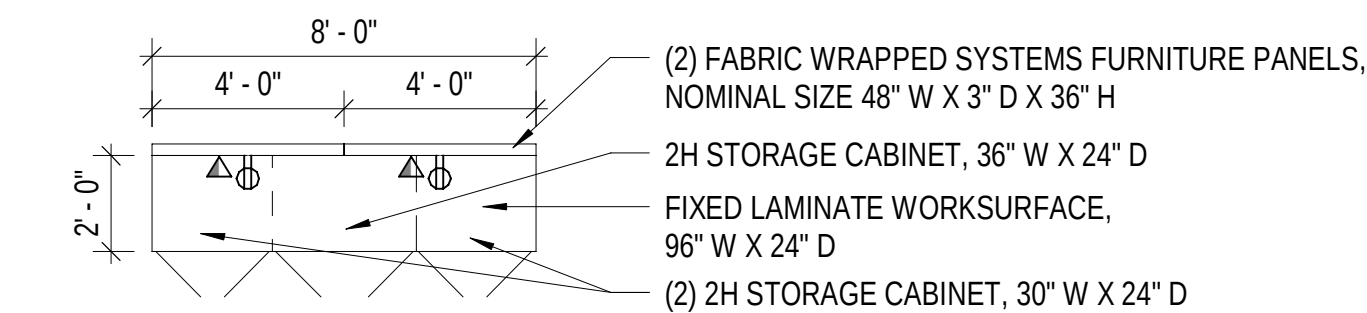


A1 ST05 PRINT & EQUIPMENT STATION PLAN
1/4" = 1'-0"

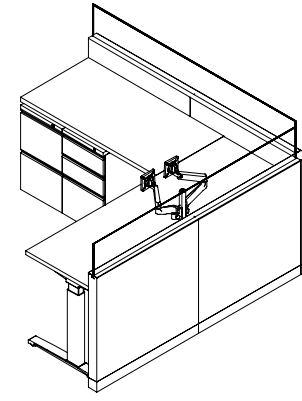


D2 WS01 WORKSTATION 3D ISOMETRIC VIEW
NTS

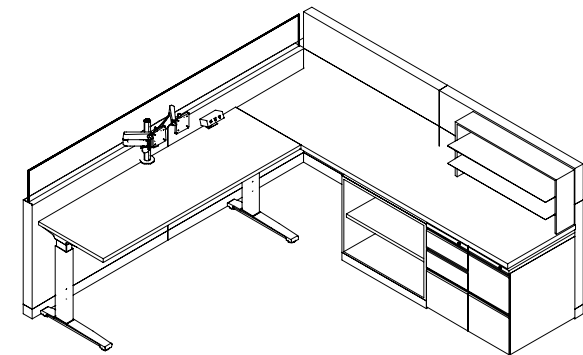


C2 WS02 WORKSTATION 3D ISOMETRIC VIEW
NTS

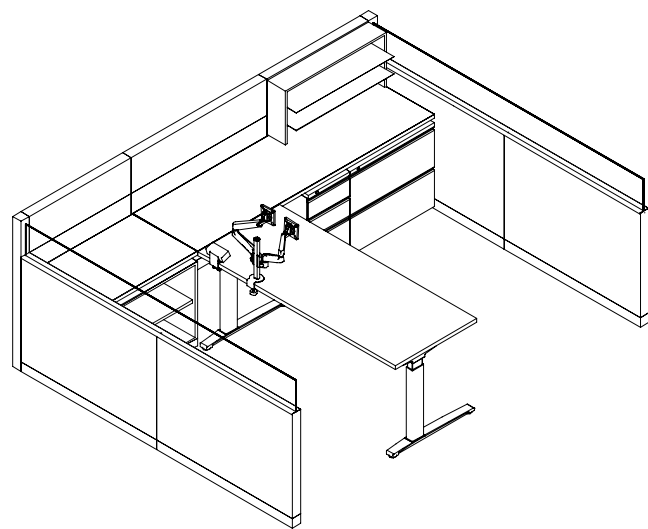


B2 WS03 WORKSTATION 3D ISOMETRIC VIEW
NTS

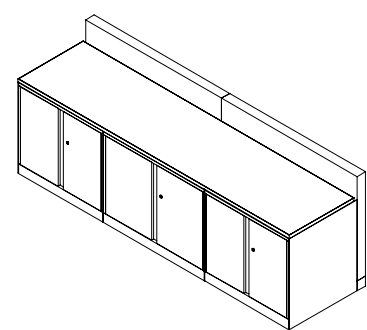

A2 ST05 PRINT STATION 3D ISOMETRIC VIEW

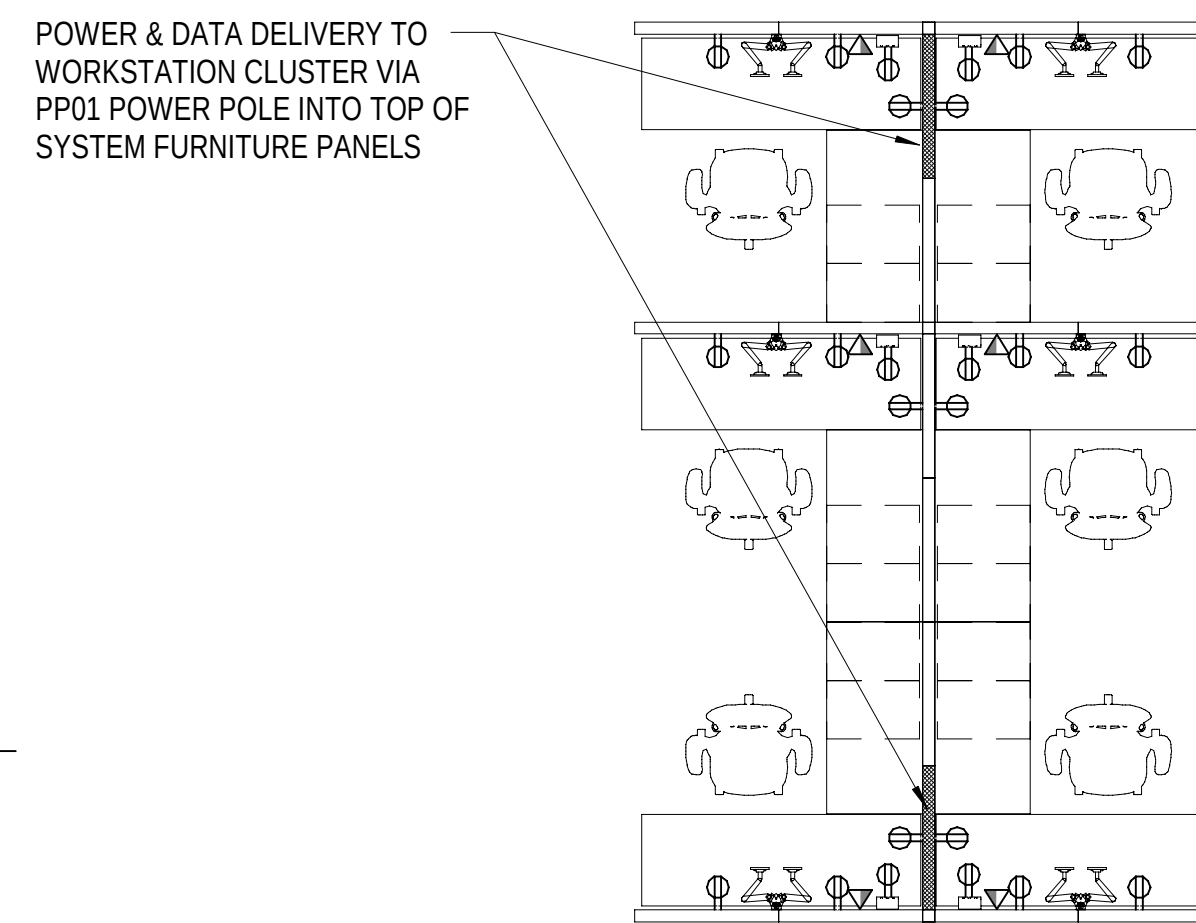

D4 WS01 WORKSTATION CLUSTER PLAN
1/4" = 1'-0"

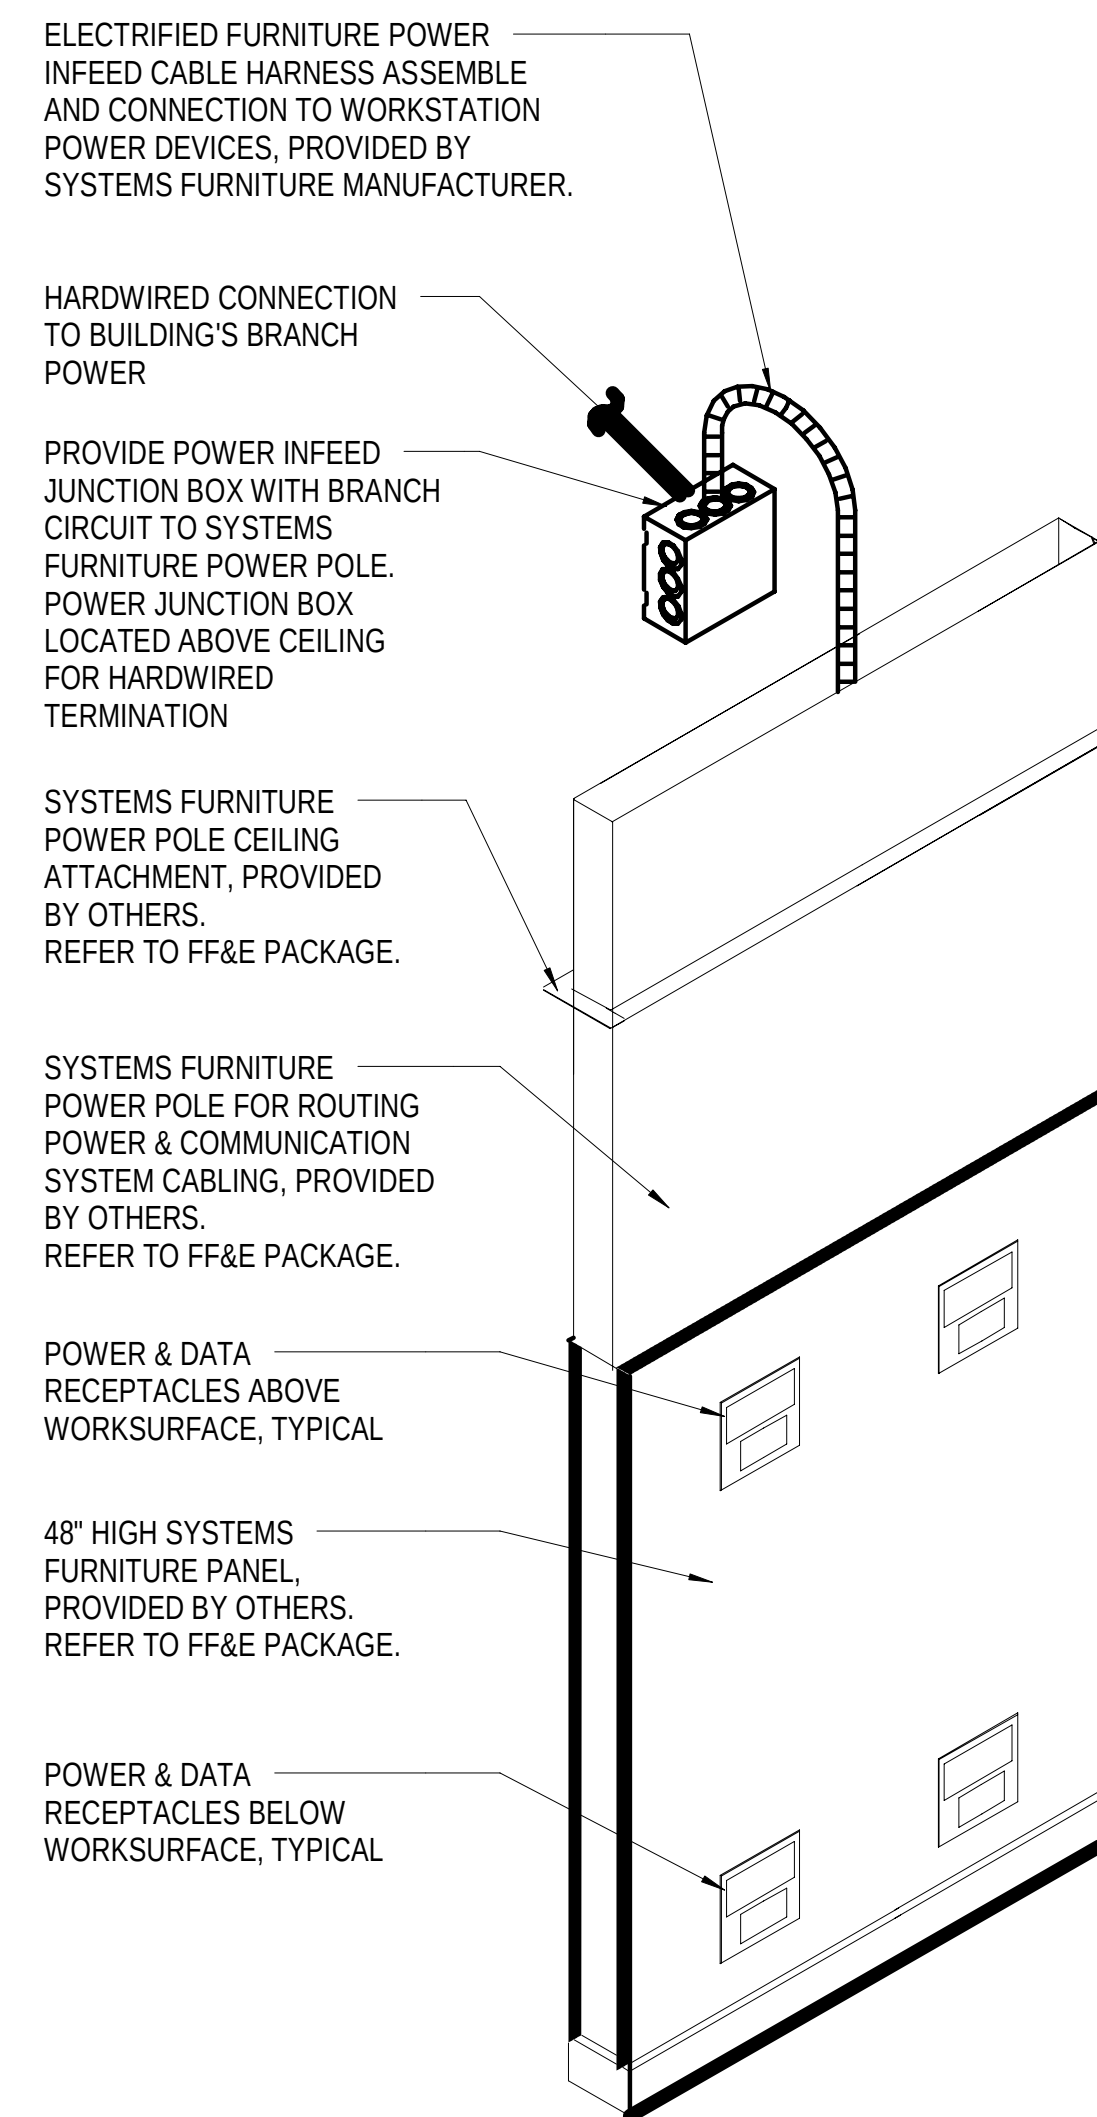

A3 SYSTEMS FURNITURE POWER POLE DETAIL

GENERAL SHEET NOTES

A. REFER TO I-601 FOR FURNITURE, FIXTURES, AND EQUIPMENT (FF&E) SCHEDULE FOR TAG DESCRIPTIONS AND QUANTITIES.

B. FURNITURE, FIXTURES, AND EQUIPMENT (FF&E) INDICATED IS PROVIDED FOR COORDINATION PURPOSES ONLY.

C. FF&E IS NOT PART OF THE CONSTRUCTION BASE BID CONTRACT. THE FF&E PACKAGE WILL BE CONTRACTOR FURNISHED/CONTRACTOR PROVIDED (CFCI) AND WILL BE FUNDED SEPARATELY THROUGH A PLANNED MODIFICATION TO THE CONSTRUCTION CONTRACT. REFER TO THE FF&E PACKAGE FOR FURTHER INFORMATION.

D. PROVIDE MINIMAL HEIGHT MODESTY PANELS WHERE PANELS ARE ADJACENT TO WALLS TO ALLOW EASY ACCESS TO WALL OUTLETS.

E. PROVIDE GROMMETS AT EACH FIXED WORKSURFACE.

F. PROVIDE WIRE MANAGEMENT, WORKSURFACE MOUNTED ELECTRICAL RECEPTACLE, CRASH LIMITER/SENSOR, AND 250 LB WEIGHT CAPACITY AT EACH HEIGHT ADJUSTABLE WORKSURFACE.

G. ALL STORAGE COMPONENTS KEYED ALIKE FOR EACH OFFICE OR WORKSTATION.

H. POWER, DATA AND VOICE OUTLETS ARE ILLUSTRATED ON OFFICE AND WORKSTATION TYPICALS FOR DESIGN INTENT & SYSTEMS FURNITURE COMPONENT COORDINATION WITH INFRASTRUCTURE. REFER TO ELECTRICAL AND TELECOM DRAWINGS FOR POWER AND DATA LOCATIONS.

I. OFFICE AND WORKSTATION SYSTEMS FURNITURE COMPONENTS ARE NOT TO OBSTRUCT POWER AND DATA WALL CONNECTIONS.

J. COORDINATE FINAL LOCATIONS OF OUTLETS WITH FF&E MANUFACTURER'S REQUIREMENTS.

K. PROVIDE JUNCTION BOX FOR POWER IN-FEED CONNECTION TO PANEL-BASED SYSTEMS FURNITURE WITH FLEXIBLE CONDUIT "POWER WHIP". COORDINATE POWER REQUIREMENTS WITH AWARDED MANUFACTURER PRIOR TO COMMENCING WITH WORK.




6/20/2025 10:30:26 AM I-403
\\n0c1v9d\\l\\e\\p\\FD\\E\\1628\\AF\\CH\\B\\DG-166770-A\\B\\M.rvt

D

C


B

A

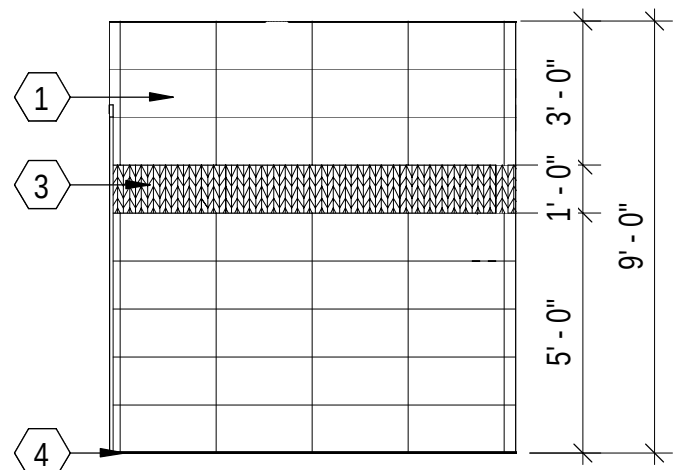


RESTROOM WALLS TO USE THE TILE
PATTERN ABOVE UON.


C1 TYPICAL WALL TILE ELEVATION
1/4" = 1'-0" (A-401)

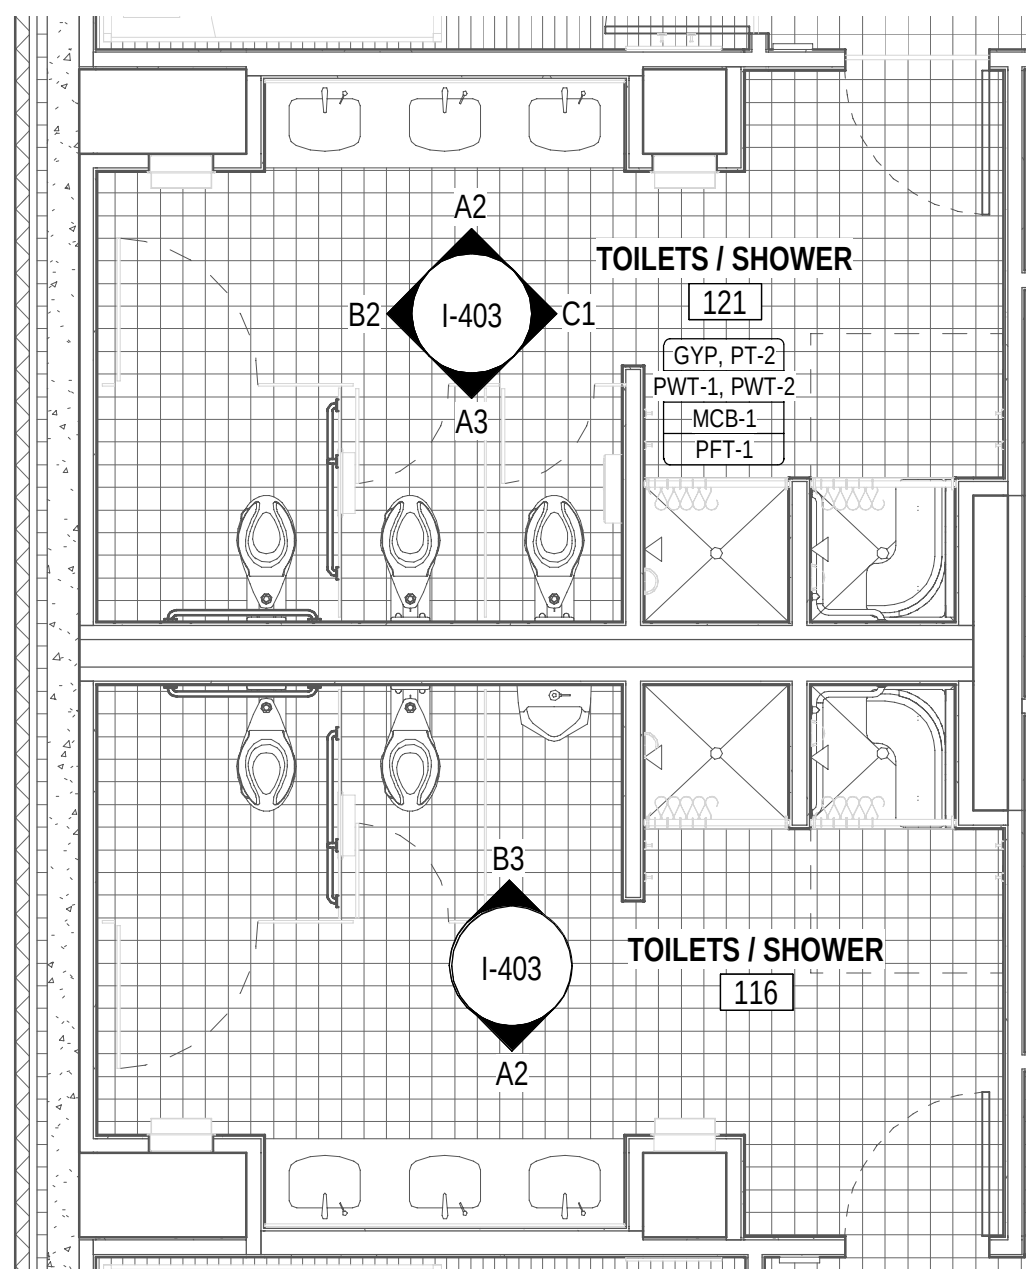


A1 ENLARGED RESTROOMS PLAN
1/4" = 1'-0" (I-102)

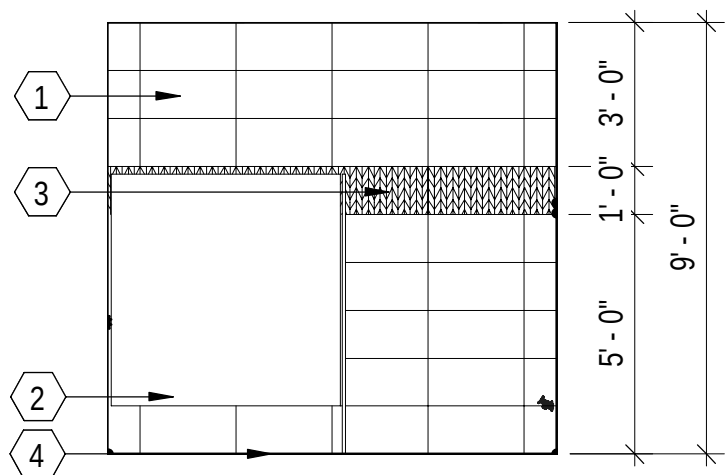


B2 RESTROOM STALL TILE TYPICAL ELEVATION
1/4" = 1'-0"

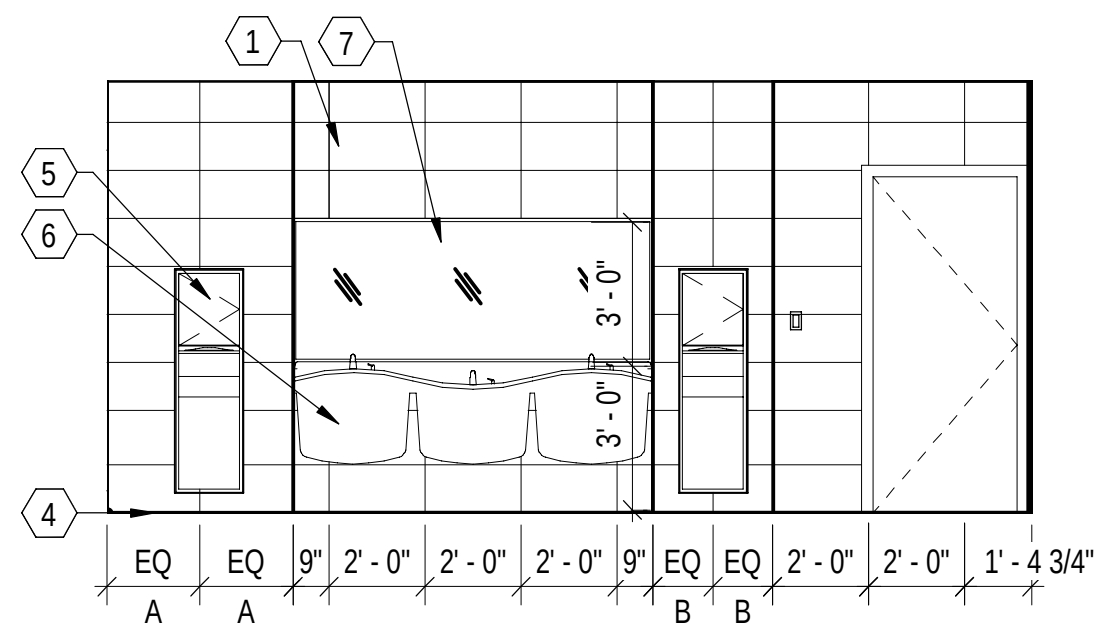

A2 RESTROOM SINK TILE TYPICAL ELEVATION
1/4" = 1'-0" (A-401)

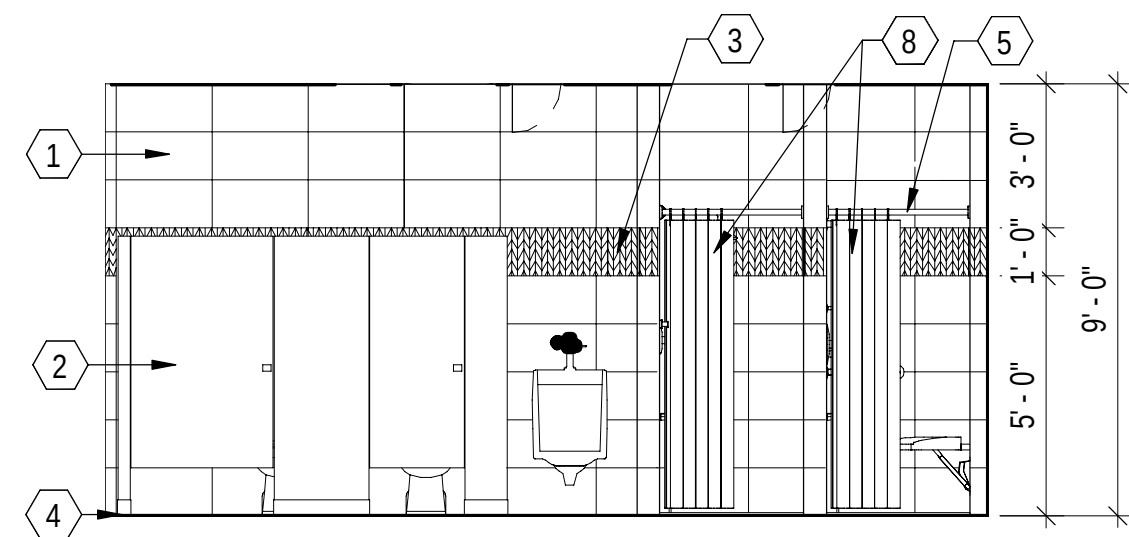

B3 MEN'S TOILETS/ SHOWER ROOM 116 ELEVATION
1/4" = 1'-0" (A-401)

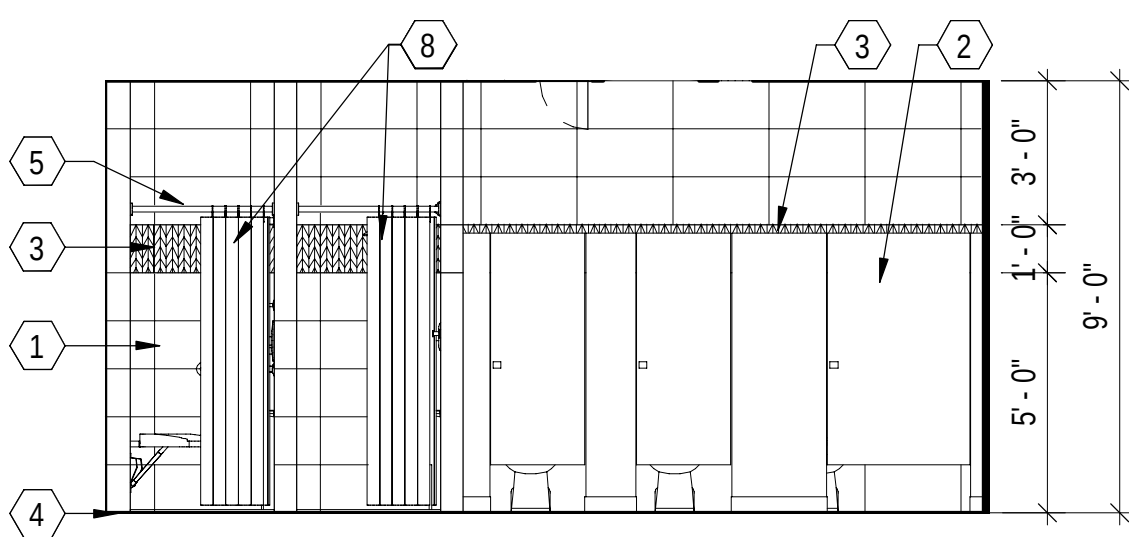

A3 WOMEN'S TOILETS/ SHOWER ROOM 121 ELEVATION
1/4" = 1'-0" (A-401)

GENERAL SHEET NOTES

- A. REFER TO ARCHITECTURE (A) SHEETS FOR DOOR NUMBERS, ADDITIONAL DIMENSIONS, AND PARTITION TYPE DESIGNATIONS, IF NOT INDICATED ON ENLARGED PLAN.
- B. REFER TO I-102 FOR INTERIORS FINISH PLAN & AND ROOM FINISH SCHEDULE.
- C. REFER TO I-601 FOR INTERIOR MATERIAL FINISH SCHEDULE
- D. REFER TO I-501 FOR INTERIORS MILLWORK DETAILS.
- E. FF&E IS NOT IN CONTRACT AND SHOWN FOR COORDINATION ONLY. REFER TO I-101 FOR FF&E SCHEDULE. REFER TO FF&E PACKAGE SUBMITTED UNDER SEPARATE COVER FOR FF&E REQUIREMENTS.
- F. REFER TO ARCHITECTURE (A) SHEET A-401 FOR TOILET / BATH ACCESSORIES (TBA) INFORMATION.
- G. REFER TO AV (TA) PLAN AND ELEVATIONS AV EQUIPMENT TYPES AND LOCATIONS. COORDINATE AV FLATSCREEN MONITOR MOUNTING HEIGHT WITH ELECTRICAL AND DATA CONNECTIONS.
- H. REFER TO PLUMBING (P) SHEETS FOR PLUMBING FIXTURES AND DETAILS.
- I. FIELD VERIFY DIMENSIONS PRIOR TO ORDERING MATERIALS AND FINISHES.
- J. WHERE WALL TILE IS PROVIDED, PROVIDE ANODIZED ALUMINUM TRIM PIECE AT OUTSIDE CORNERS.


SHEET KEYNOTES

- PORCELAIN WALL TILE, PWT-1.
- TOILET PARTITION, TBA-02. REFER TO ARCHITECTURE FOR TOILET ACCESSORIES SCHEDULE.
- PORCELAIN MOSAIC WALL TILE, PWT-2.
- METAL COVE BASE, MCB-1.
- REFER TO ARCHITECTURE FOR TOILET ACCESSORIES SCHEDULE, TYP.
- ABA COMPLIANT (3) STATION LAVATORY. REFER TO ARCHITECTURE AND PLUMBING DRAWINGS FOR PLUMBING FIXTURE AND TOILET ACCESSORY INFORMATION.
- 3'-0" HIGH, FULL-WIDTH MIRROR. REFER TO ARCHITECTURE FOR TOILET ACCESSORIES SCHEDULE.
- SHOWER CURTAIN & SHOWER CURTAIN HOOKS, EQ03. REFER TO FF&E PACKAGE. BOTTOM OF SHOWER CURTAIN TO HANG APPROX 1" ABOVE FINISHED FLOOR. COORDINATE SHOWER CURTAIN & HOOK HEIGHT.

0 2' 4' 8' 12'
1/4" = 1'-0"



SYN	DESCRIPTION	DATE	APPR

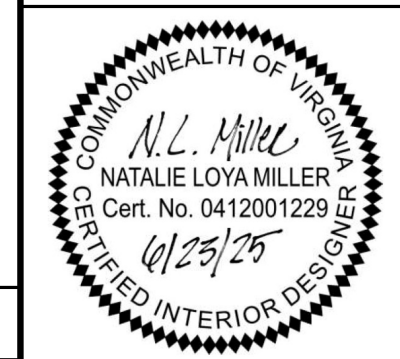

Jacobs
1100 NORTH GLEBE ROAD
SUITE 500
ARLINGTON, VIRGINIA 22201
571.218.1000
FAX: 571.218.1600

APPROVED
AE INFO

FOR COMMANDER NAVFAC
ACTIVITY
APPROVED BY LCDR ELIZABETH
CLOKODE NAVFAC NLON FEAD
DIRECTOR NEW LONDON, GROTON, CT

SATISFACTORY TO DATE 05/27/2025

DES NM DRW AW CHK AB

PMOM SMSI/CWJ

BRANCH MANAGER DJD

CHIEF ENGINEER JWC

FIRE PROTECTION HPN

DEPARTMENT OF THE NAVY

NAVAL FACILITIES ENGINEERING SYSTEMS COMMAND

NAVAL FACILITIES ENGINEERING SYSTEMS COMMAND - MID-ATLANTIC

NAVAL STATION - NORFOLK, VA

MID-ATLANTIC

NAVAL SUBMARINE BASE NEW LONDON

GROTON, CONNECTICUT

P-1102 WEAPONS MAGAZINE & ORDNANCE OPERATIONS FACILITY

OPERATIONS

INTERIOR ENLARGED PLANS & ELEVATIONS

SCALE: AS NOTED

PROJECT NO.: 1667770

CONSTR. CONTR. NO.

NAVFAC DRAWING NO. 12893994


SHEET 44 OF 140

I-403


6/20/2025 10:30:31 AM
\\ac119501\lief\p\FD\21628\AFCH\B\DG-1667770-A-BIM.rvt

I-404


A

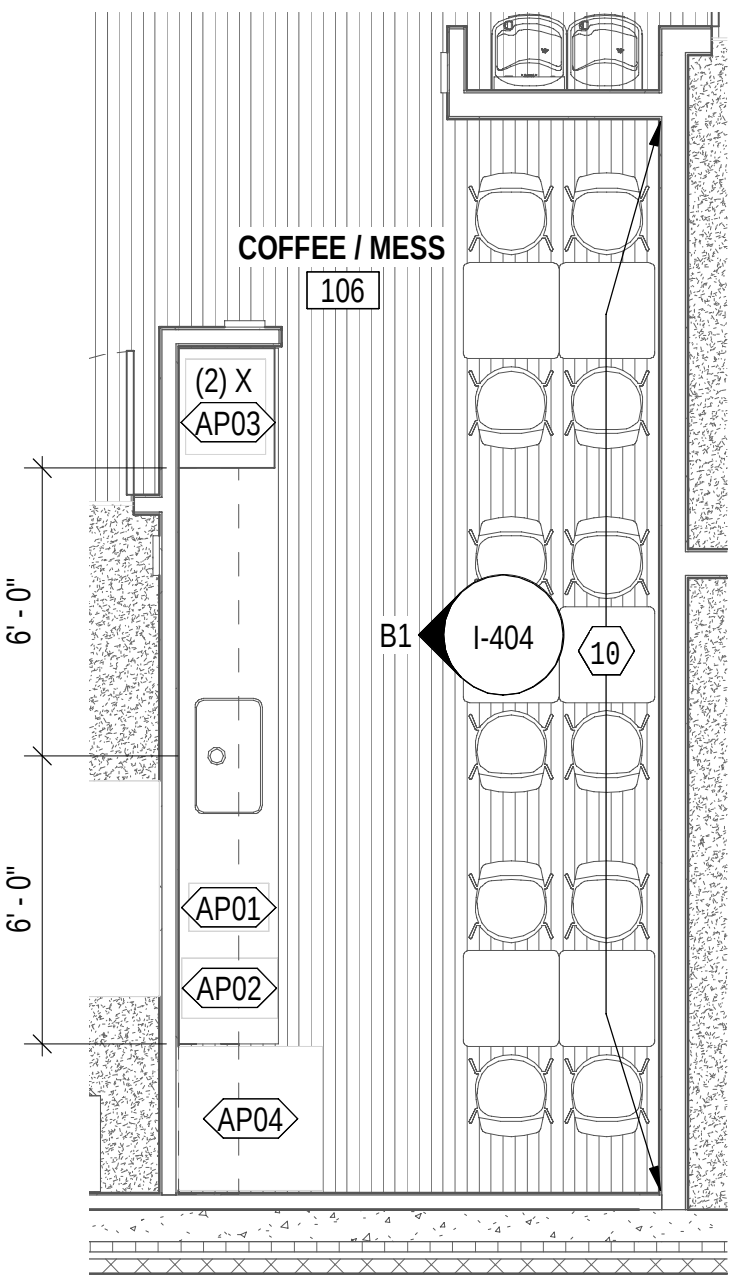

A1 COFFEE/MISC 106 ENLARGED PLAN
1/4" = 1'-0" (I-102)

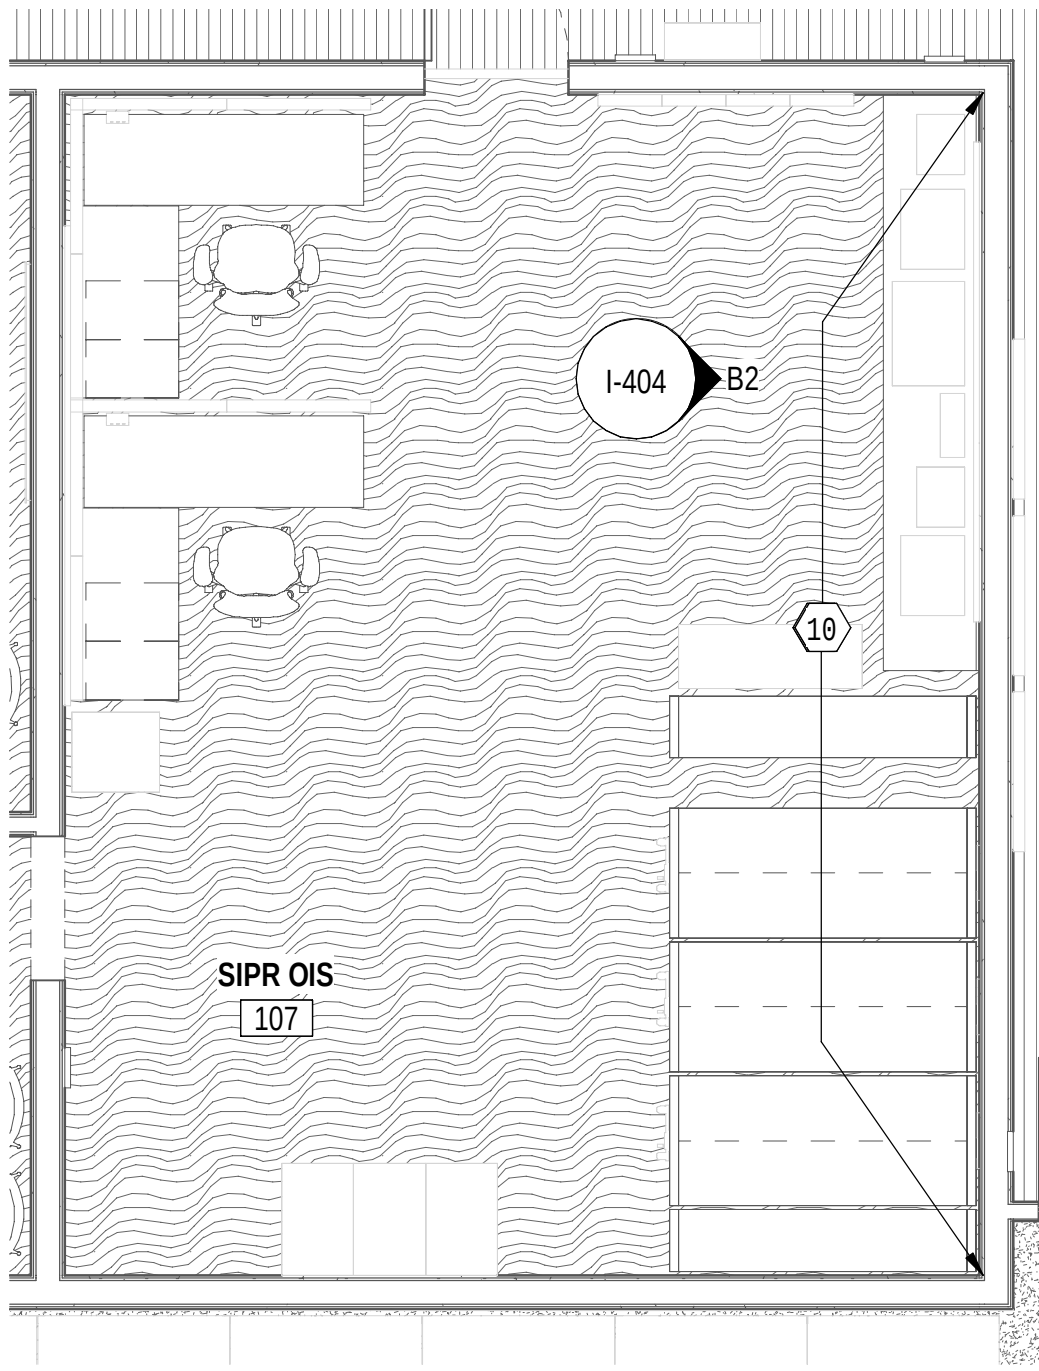


A2 SIPR OIS 107 ENLARGED PLAN
1/4" = 1'-0" (I-102)

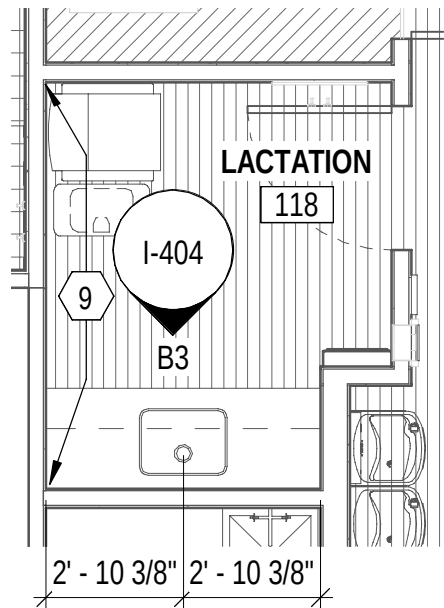


A3 LACTATION 118 ENLARGED PLAN
1/4" = 1'-0" (I-102)

D


C

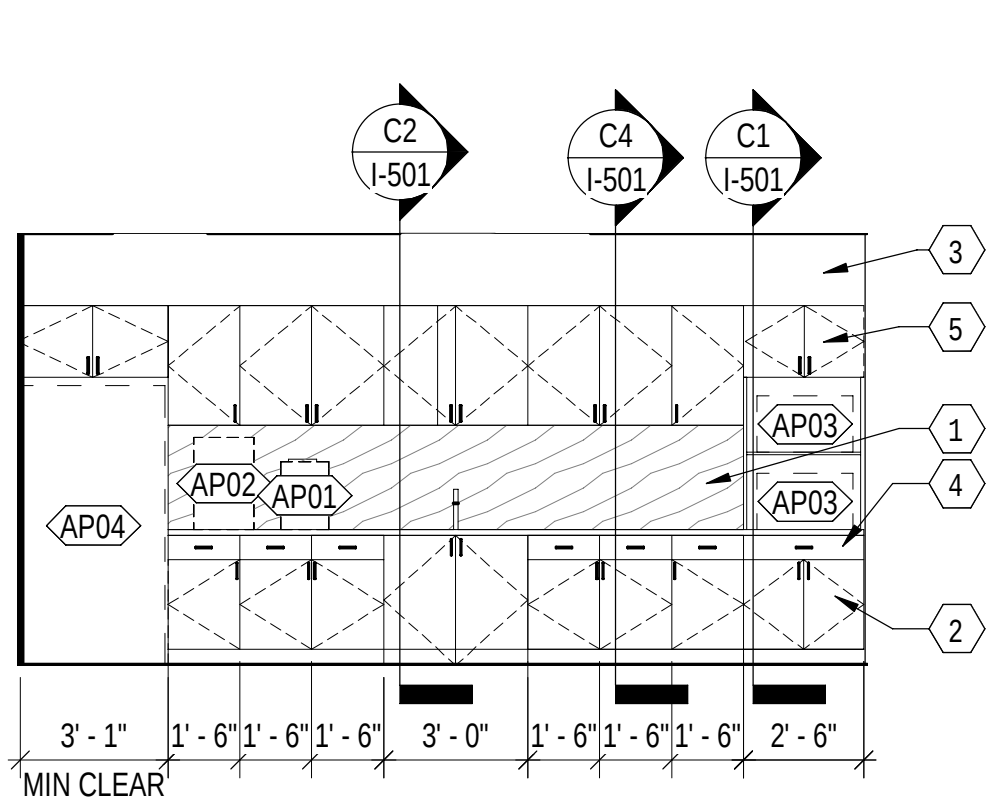

B1 COFFEE/MISC 106 WEST ELEVATION
1/4" = 1'-0" (I-404)

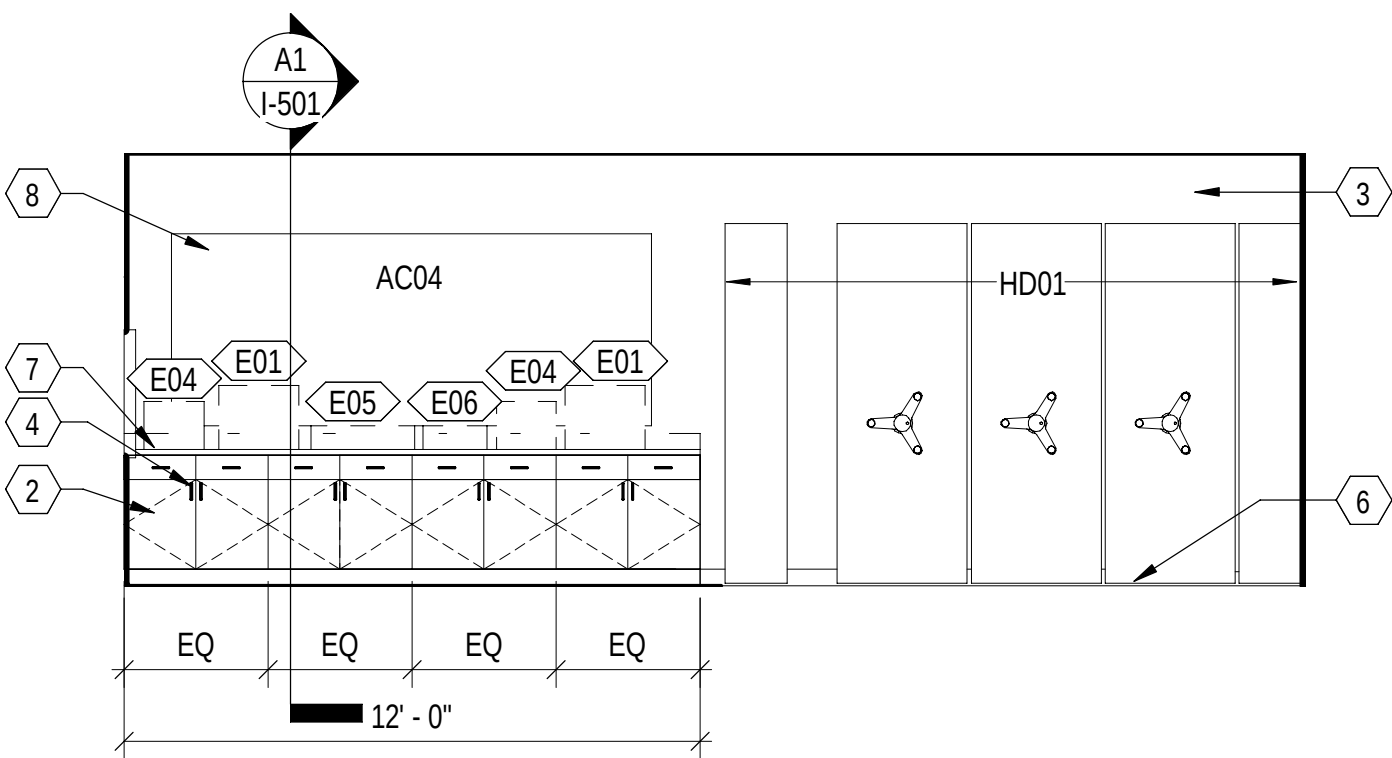

B2 SIPR OIS 107 EAST ELEVATION
1/4" = 1'-0" (I-404)

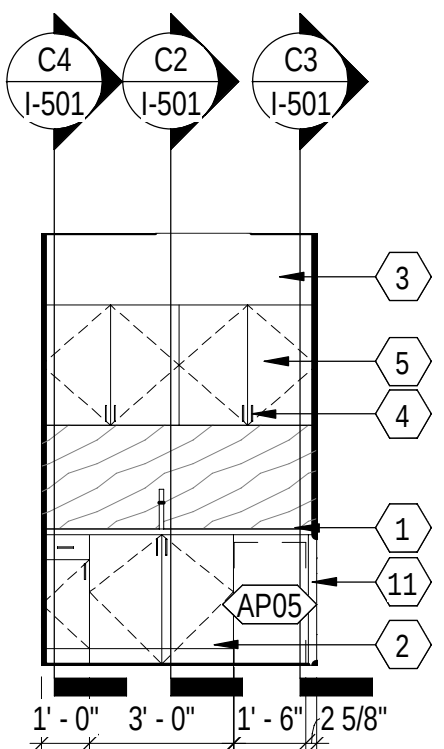

B3 LACTATION 118 SOUTH ELEVATION
1/4" = 1'-0" (A-401)

GENERAL SHEET NOTES

- A. REFER TO ARCHITECTURE (A) SHEETS FOR DOOR NUMBERS, ADDITIONAL DIMENSIONS, AND PARTITION TYPE DESIGNATIONS, IF NOT INDICATED ON ENLARGED PLAN.
- B. REFER TO I-102 FOR INTERIORS FINISH PLAN & AND ROOM FINISH SCHEDULE.
- C. REFER TO I-601 FOR INTERIOR MATERIAL FINISH SCHEDULE
- D. REFER TO I-501 FOR INTERIORS MILLWORK DETAILS.
- E. FF&E IS NOT IN CONTRACT AND SHOWN FOR COORDINATION ONLY. REFER TO I-101 FOR FF&E SCHEDULE. REFER TO FF&E PACKAGE SUBMITTED UNDER SEPARATE COVER FOR FF&E REQUIREMENTS.
- F. REFER TO ARCHITECTURE (A) SHEET A-401 FOR TOILET / BATH ACCESSORIES (TBA) INFORMATION.
- G. REFER TO AV (TA) PLAN AND ELEVATIONS AV EQUIPMENT TYPES AND LOCATIONS. COORDINATE AV FLATSCREEN MONITOR MOUNTING HEIGHT WITH ELECTRICAL AND DATA CONNECTIONS.
- H. REFER TO PLUMBING (P) SHEETS FOR PLUMBING FIXTURES AND DETAILS.
- I. FIELD VERIFY DIMENSIONS PRIOR TO ORDERING MATERIALS AND FINISHES.
- J. WHERE WALL TILE IS PROVIDED, PROVIDE ANODIZED ALUMINUM TRIM PIECE AT OUTSIDE CORNERS.

SHEET KEYNOTES

- SOLID SURFACE COUNTERTOP WITH FULL-HEIGHT BACKSPLASH TO UNDERSIDE OF CABINET ABOVE, SS-1.
- PLASTIC LAMINATE, PL-1.
- PAIN AS SCHEDULED.
- 4" BAR PULL, BRUSHED STAINLESS STEEL FINISH.
- PLASTIC LAMINATE, PL-2.
- REFER TO STRUCTURAL DRAWINGS FOR HIGH DENSITY FILING SLAB DEPRESSION.
- SOLID SURFACE COUNTERTOP WITH 4" HIGH BACKSPLASH, SS-1.
- MOUNT MARKERBOARD ABOVE FURNITURE/MILLWORK.
- ACCENT PAINT, PT-6.
- ACCENT PAINT, PT-5.
- PLASTIC LAMINATE FILLER STRIP, PL-1.

0 2' 4' 8' 12'
1/4" = 1'-0"



SYN	DESCRIPTION	DATE	APPR



Jacobs
1100 NORTH GLEBE ROAD
SUITE 500
ARLINGTON, VIRGINIA 22201
571.218.1000
FAX: 571.218.1600

APPROVED

FOR COMMANDER NAVFAC

ACTIVITY APPROVED BY LCDR ELIZABETH
CLOKODE NAVFAC NLON FEAD
DIRECTOR NEW LONDON, GROTON, CT

SATISFACTORY TO DATE 05/27/2025

DES NM DRW AW CHK AB

PMIDM SMSI CWJ

BRANCH MANAGER DJD

CHIEF ENGINEER JWJ

FIRE PROTECTION HPN

NAVAL FACILITIES ENGINEERING SYSTEMS COMMAND

NAVAL FACILITIES ENGINEERING SYSTEMS COMMAND - MID-ATLANTIC

NAVAL STATION - NORFOLK, VA

NAVAL FACILITIES ENGINEERING SYSTEMS COMMAND - MID-ATLANTIC

A1 TRAINING/CONFERENCE 131 ENLARGED PLAN
1/4" = 1'-0" (I-102)



J. WHERE WALL TILE IS PROVIDED, PROVIDE ANODIZED ALUMINUM TRIM PIECE AT OUTSIDE CORNERS.

1 PAINT AS SCHEDULED.
2 PLASTIC LAMINATE, PL-1.
3 SOLID SURFACE COUNTERTOP WITH 4" HIGH BACKSPLASH, SS-1.
4 4" BAR PULL, BRUSHED STAINLESS STEEL FINISH.
5 ACCENT PAINT, PT-6.
6 RESILIENT WALL BASE AS SCHEDULED.
7 PAINT DOOR AND TRIM, PT-3 AS SCHEDULED.
8 AUDIO VISUAL EQUIPMENT; REFER TO AV PLAN AND ELEVATIONS
OR AV EQUIPMENT TYPES, LOCATIONS AND MOUNTING HEIGHTS

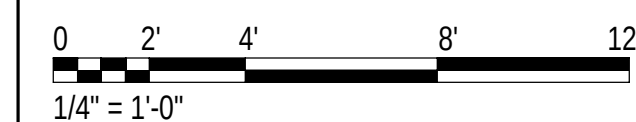

Jacobs
1100 NORTH GLEBE ROAD
SUITE 500
ARLINGTON, VIRGINIA 22201
571.218.1000
FAX: 571.218.1600


APPROVED				ACTIVITY	
FOR COMMANDER NAVFAC					
APPROVED BY LCDR ELIZABETH OLOKODE NAVFAC NLON FEAD DIRECTOR NEW LONDON, GROTON, CT					
SATISFACTORY TO DATE				05/27/2025	
DES	NM	DRW	AW	CHK	AB
PM/DM				SMS/ CWJ	
BRANCH MANAGER				DJD	
CHIEF ENGARCH				JWJ	
FIRE PROTECTION				HPN	

DEPARTMENT OF THE NAVY
NAVAL FACILITIES ENGINEERING SYSTEMS COMMAND - MID-ATLANTIC
NAVAL SUBMARINE BASE NEW LONDON
GROTON, CONNECTICUT
NAVAL STATION - NORFOLK, VA


SCALE:	AS NOTED		
EPROJECT NO.:	1667770		
CONSTR. CONTR. NO.			
NAVFAC DRAWING NO.	12893996		
SHEET	46	OF	140

I-405


INTERIOR ENLARGED PLANS & ELEVATIONS

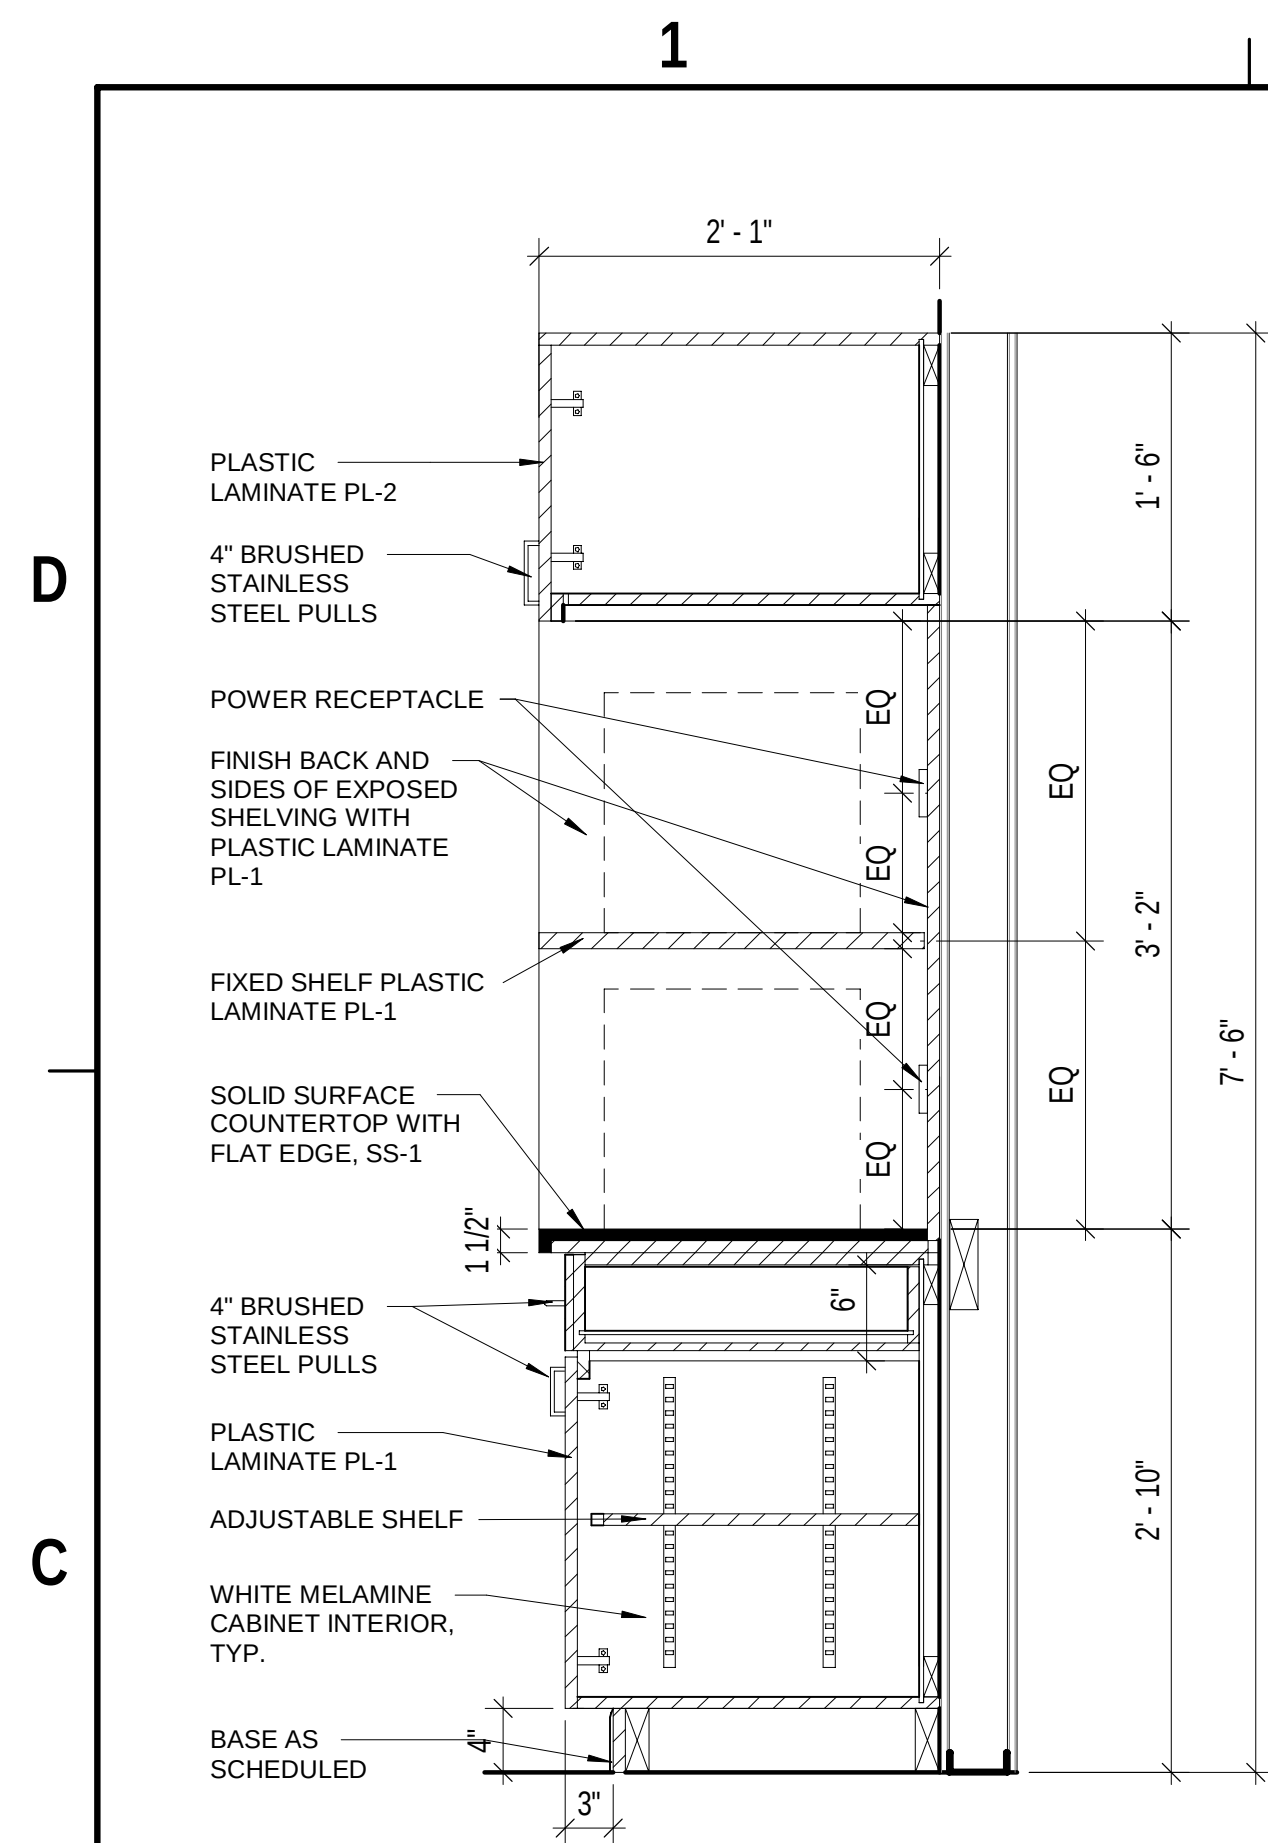


(C1) MILLWORK SECTION - MICROWAVE TOWER
1" = 1'-0"

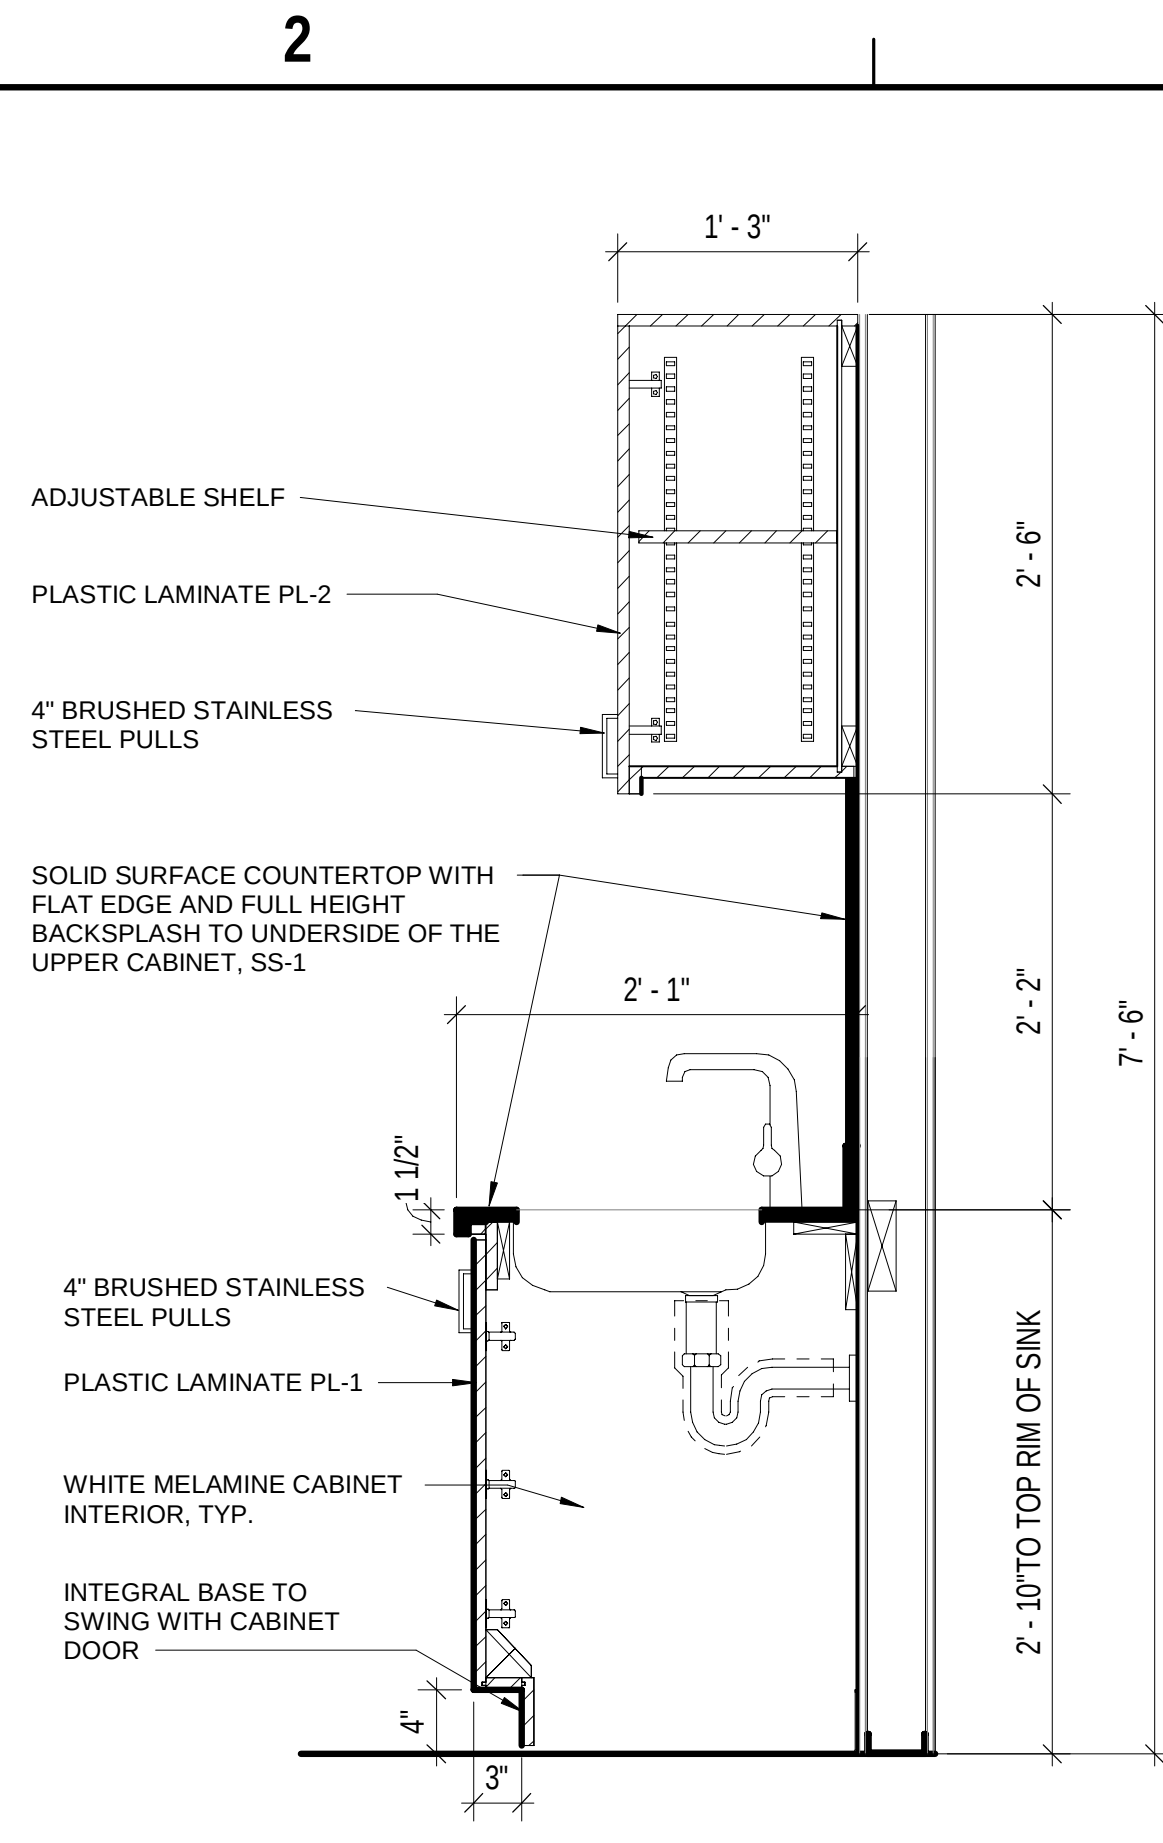


C2 MILLWORK SECTION - CABINET AT SINK
1" = 1'-0"

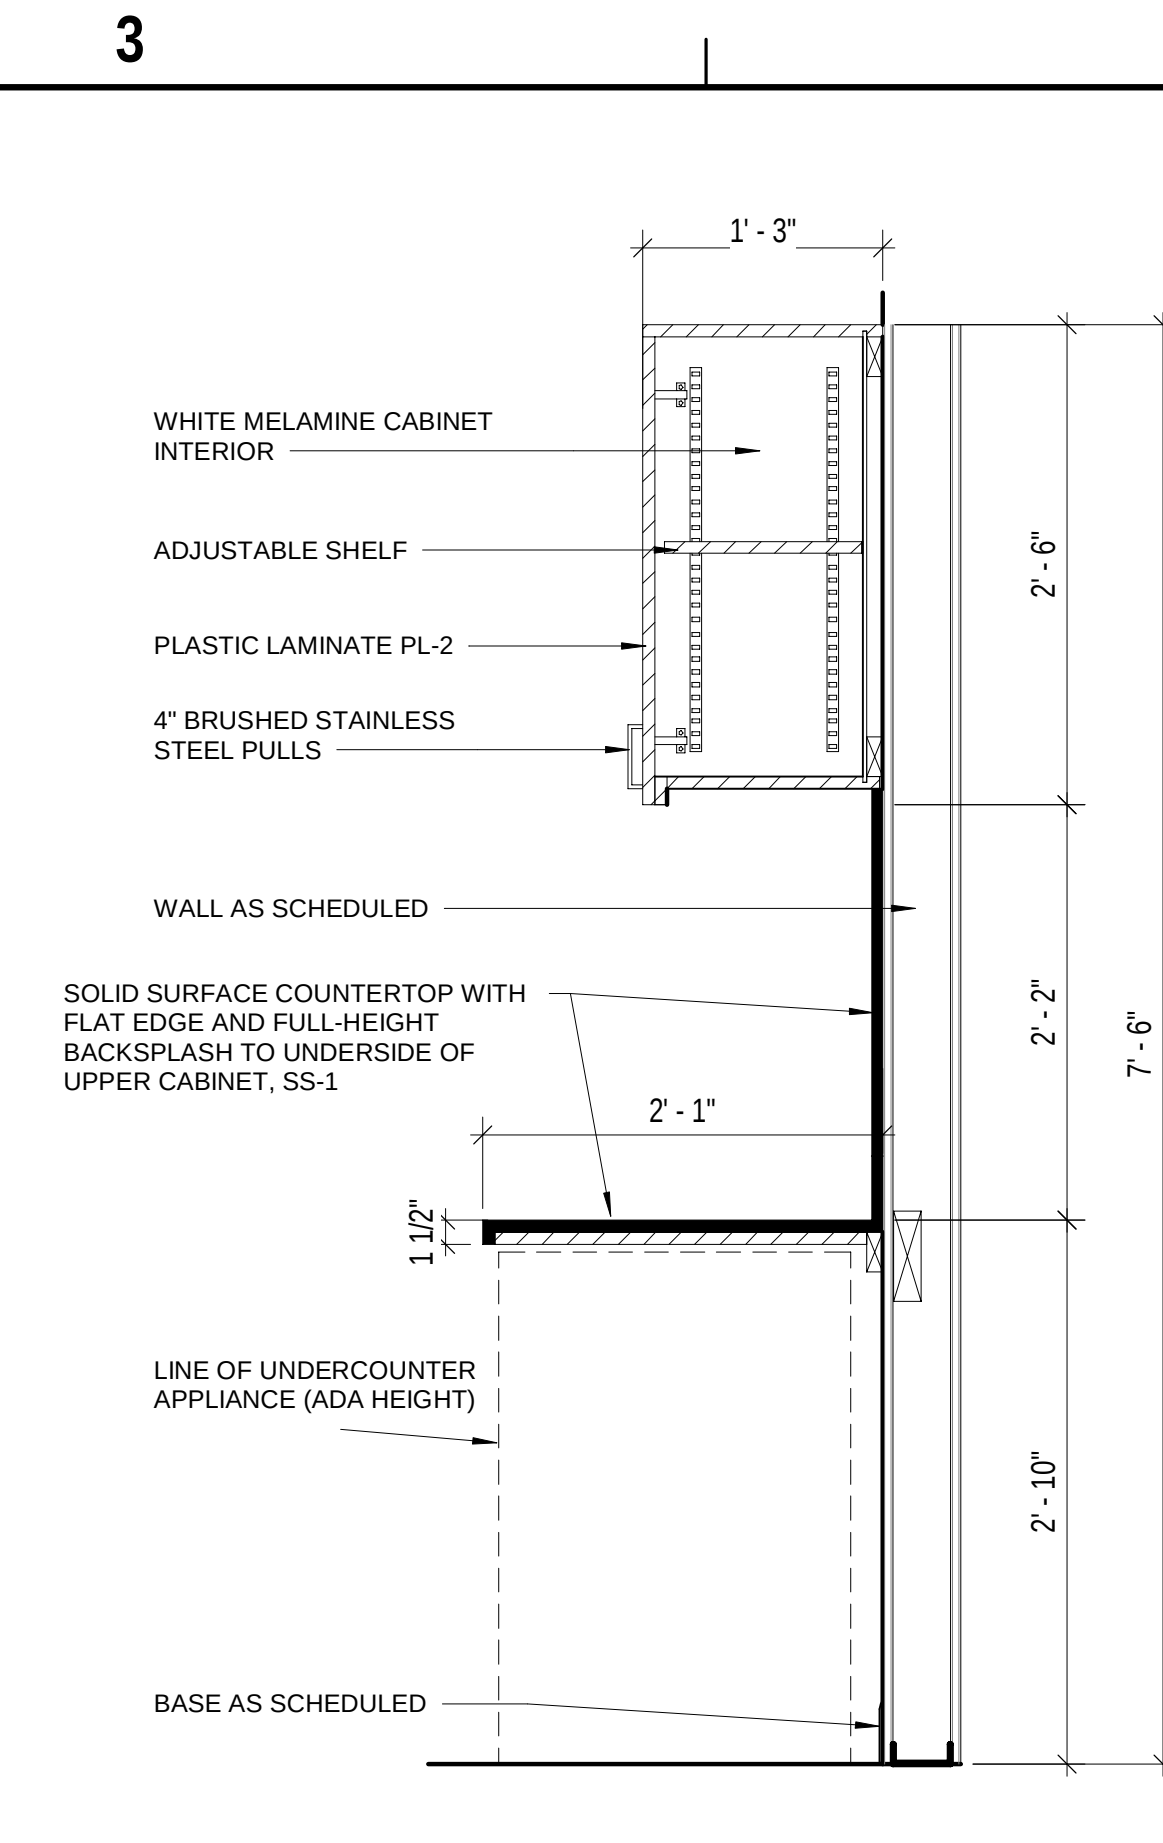


C3 MILLWORK SECTION - UNDERCOUNTER APPLIANCE
1" = 1'-0"

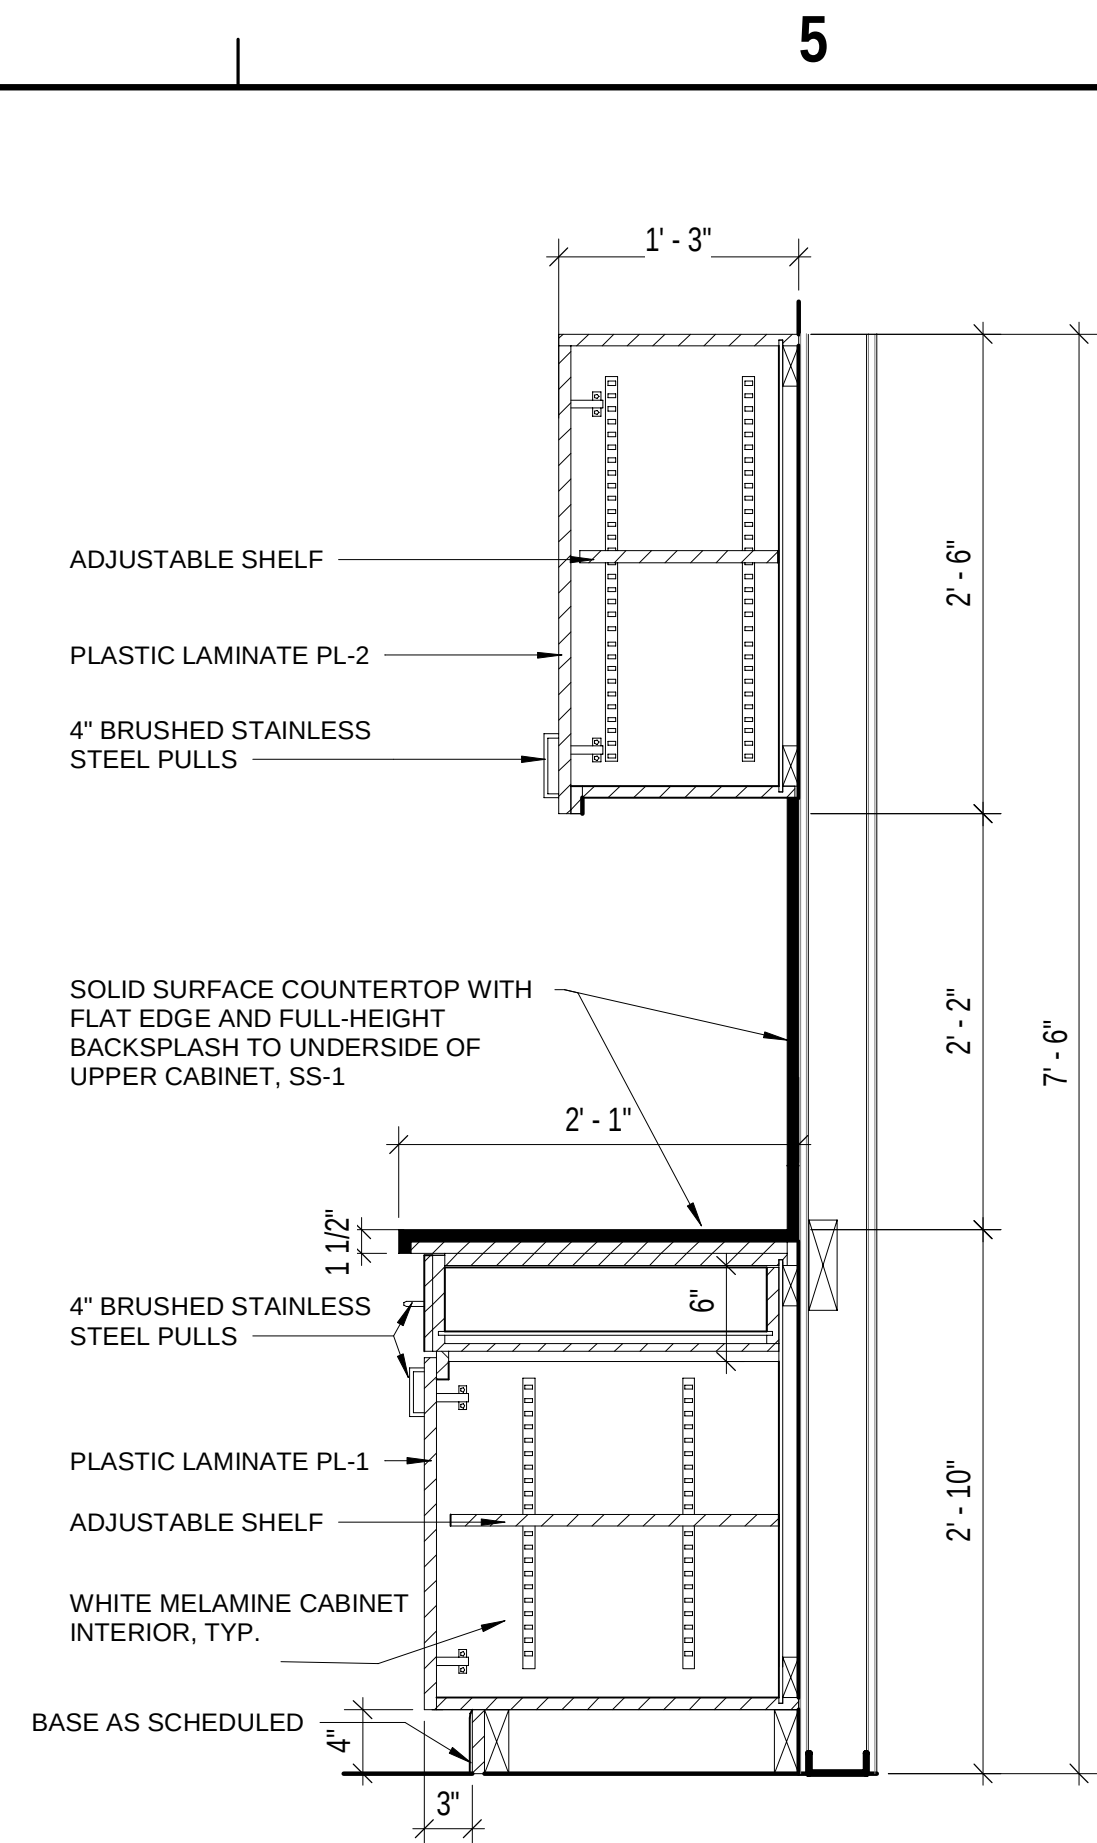


C4 MILLWORK SECTION - UPPER & BASE CABINET
1" = 1'-0"

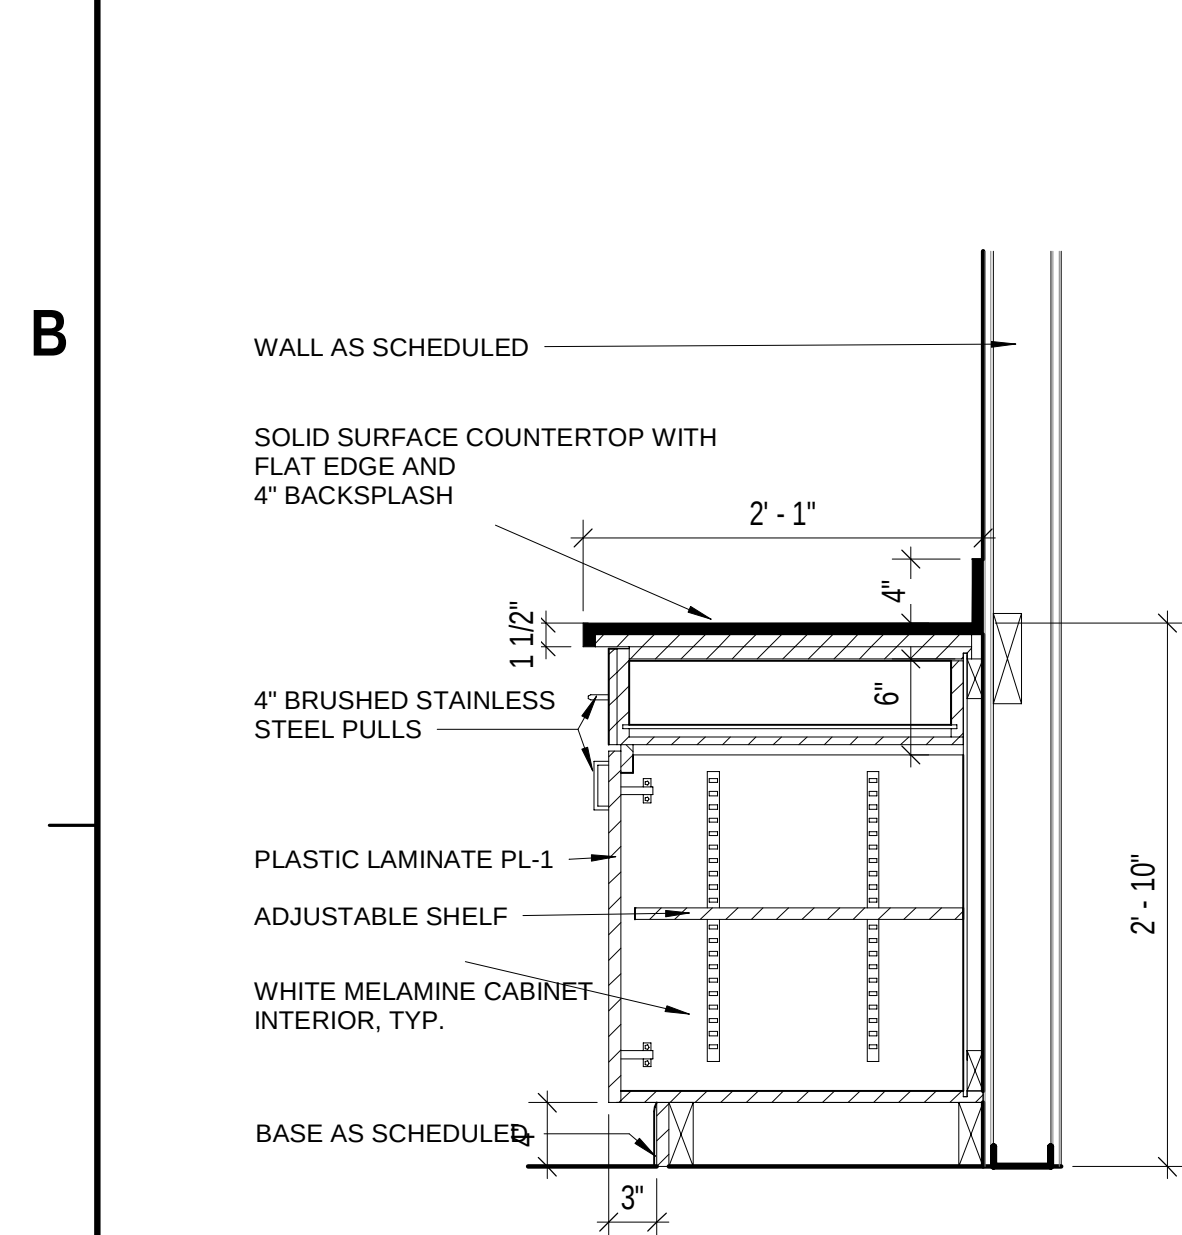


A1 MILLWORK SECTION - BASE CABINET
1" = 1'-0"

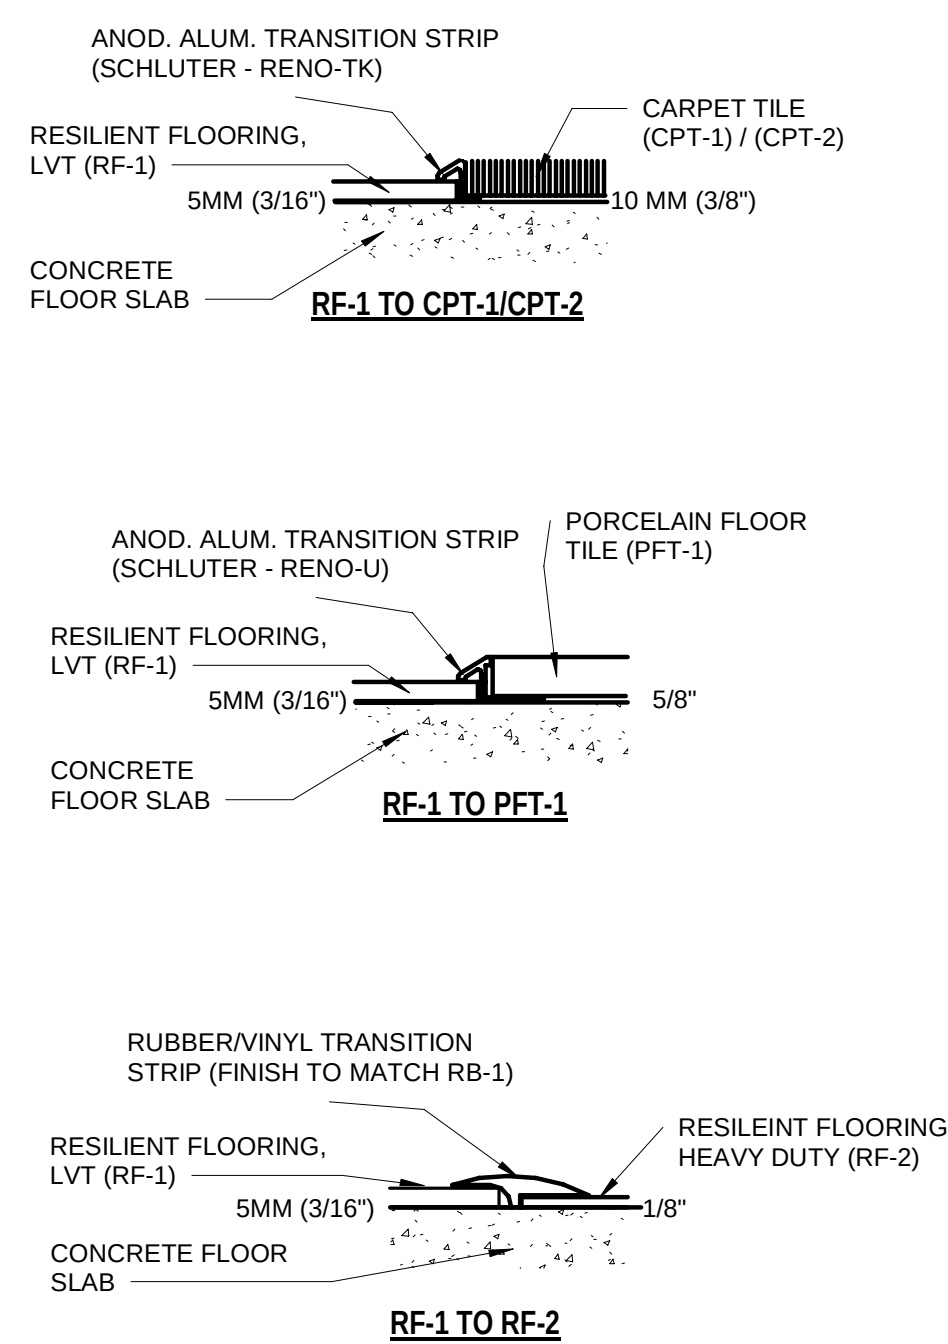


A2 FLOORING TRANSITION DETAILS
6" = 1'-0"

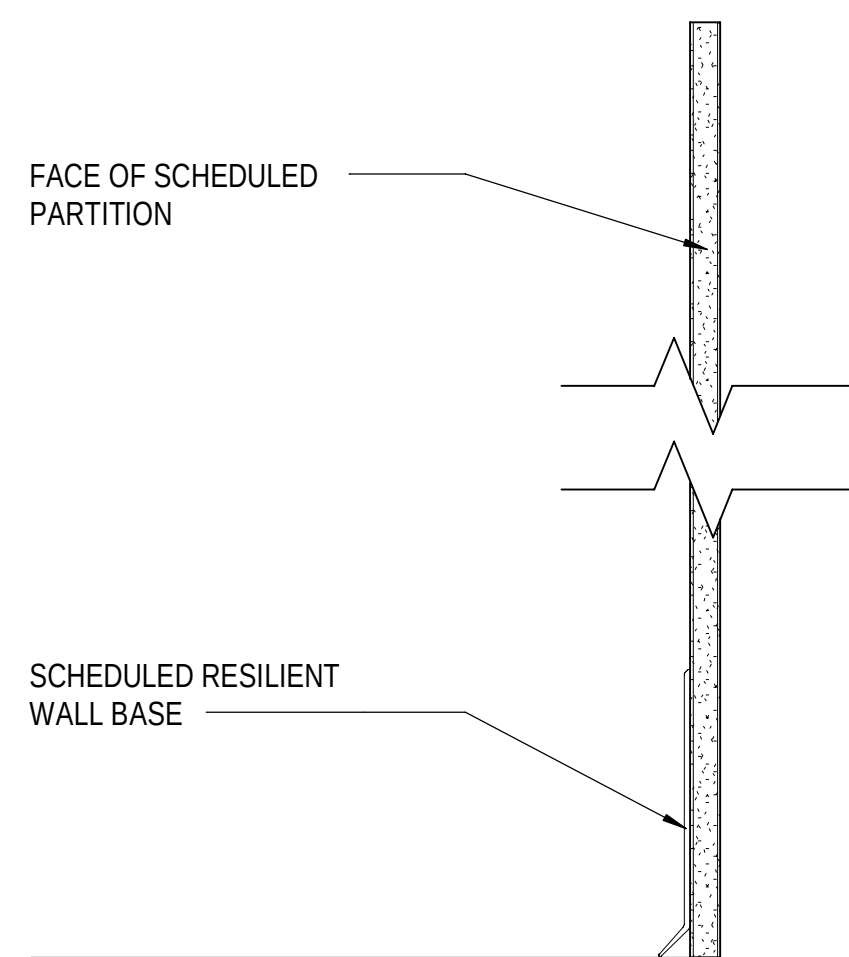



A3 RESILIENT WALL BASE DETAIL
3" = 1'-0"

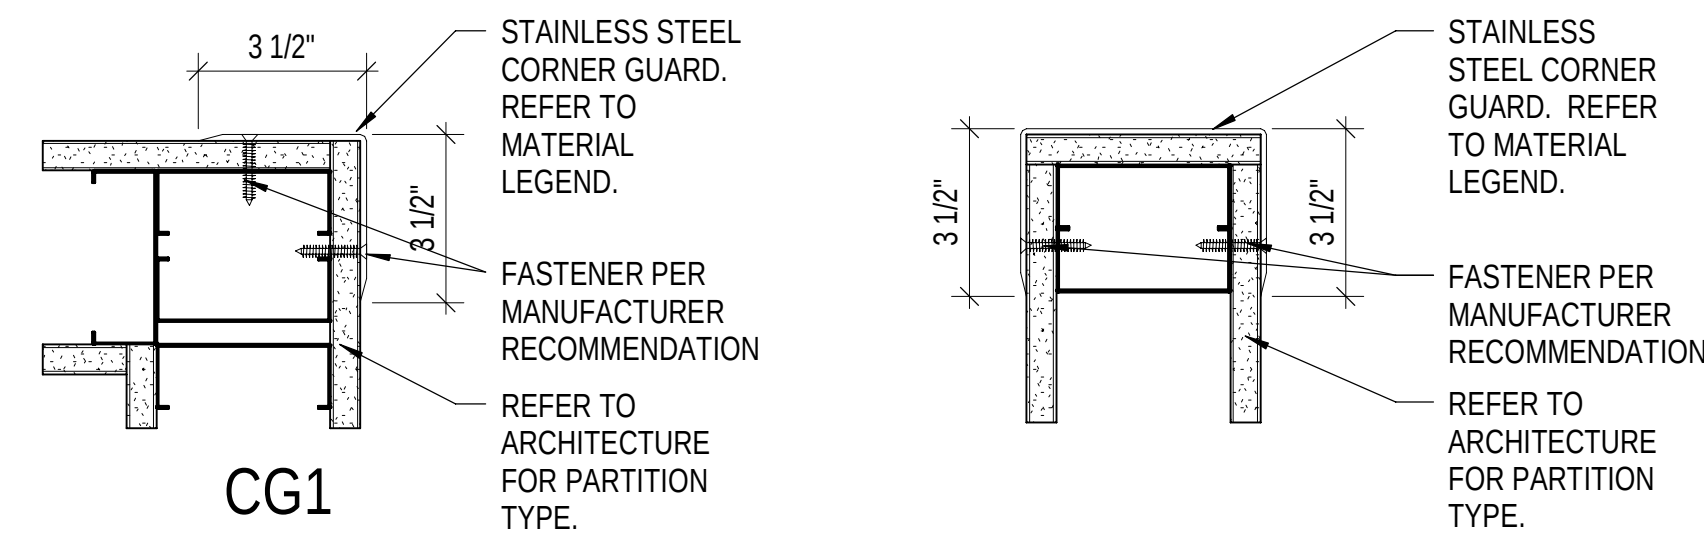

B4 CORNER GUARDS DETAIL
3" = 1'-0"

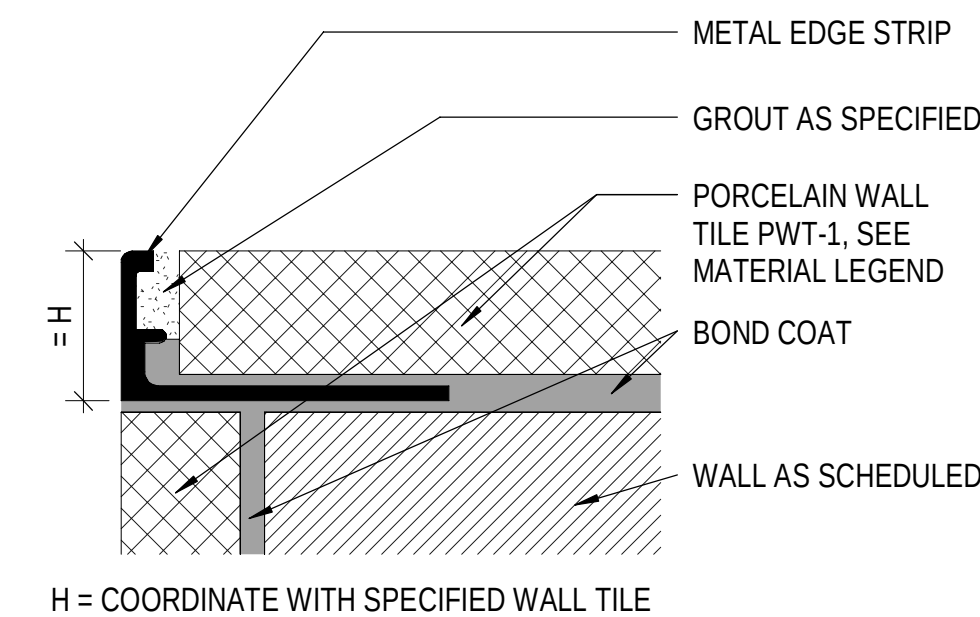

A4 METAL EDGE STRIP DETAIL
12" = 1'-0"

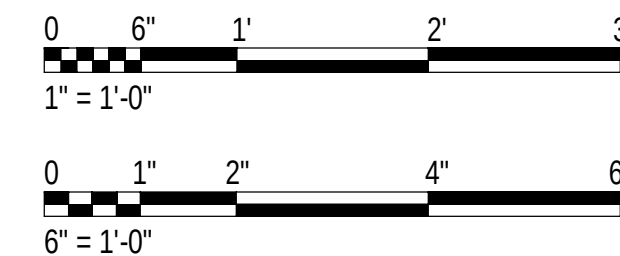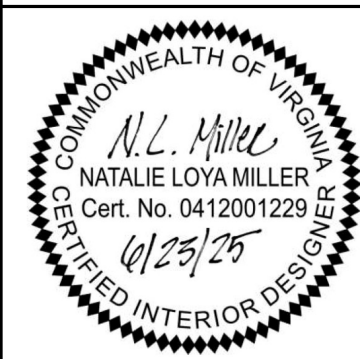[illegible]

Jacobs
1100 NORTH GLEBE ROAD
SUITE 500
ARLINGTON, VIRGINIA 22201
571.218.1000
FAX: 571.218.1600

					AE INFO	
APPROVED						
FOR COMMANDER NAVFAC						
ACTIVITY						
APPROVED BY LCDR ELIZABETH CLOKODE NAVFAC NLON FEAD						
DIRECTOR NEW LONDON, GROTON, CT						
SATISFACTORY TO DATE					05/27/2025	
DES	NM	DRW	AW	CHK	AB	
PM/MD					SMS/ CWJ	
BRANCH MANAGER					DJD	
CHIEF ENGLISH					JWJ	
CHIEF PRODUCTION					LDM	

	DEPARTMENT OF THE NAVY	NAVAL FACILITIES ENGINEERING SYSTEMS COMMAND NAVAL FACILITIES ENGINEERING SYSTEMS COMMAND - MID-ATLANTIC MID-ATLANTIC	THE PROJECT	NAVAL STATION - NORFOLK, VA
		NAVAL SUBMARINE BASE NEW LONDON	GROTON, CONNECTICUT	
		P-1102 WEAPONS MAGAZINE & ORDNANCE OPERATIONS FACILITY OPERATIONS		
		INTERIOR DETAILS		

SCALE: AS NOTED		
EPROJECT NO.:		1667770
CONSTR. CONTR. NO.		
NAVFAC DRAWING NO.		
12893997		
SHEET	47	OF 140
I-501		

[illegible]