

[illegible]

- A**


- B**

- C**

- D



- E

- F**

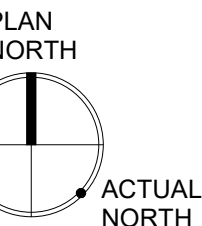[illegible]

GENERAL NOTES

- DEMOLISH EXISTING SPRINKLERS AND PIPING TO ACCOMMODATE NEW ARCHITECTURAL LAYOUT WITHIN THE AREA OF WORK UNLESS NOTED OTHERWISE. COORDINATE WITH VA OUTAGE REQUIREMENTS AND THE COR.
- EXISTING SPRINKLER MAIN PIPING AND ZONING IS SHOWN IN APPROXIMATE LOCATIONS. CONTRACTOR SHALL VERIFY EXACT LOCATIONS AND SIZE OF PIPING AND EQUIPMENT PRIOR TO CONSTRUCTION. EXISTING CONDITIONS DETERMINED FROM LIMITED SITE INVESTIGATION AND RECORD DOCUMENTS.
- EXISTING SMOKE ZONE BOUNDARIES SHOWN ARE BASED ON RECORD DOCUMENTATION AND GENERAL INFORMATION DRAWINGS. CONTRACTOR SHALL COORDINATE WITH THE COR AND VA PERSONNEL IF ANY DISCREPANCIES ARE DISCOVERED IN THE FIELD.
- MAINTAIN ALL FIRE SUPPRESSION SYSTEMS CONTINUITY AND NFPA 13 COMPLIANCE (E.G. SPACING, DISTANCE TO CEILING, OBSTRUCTION REQUIREMENTS, ETC.) DURING RENOVATION. THE FIRE DEPARTMENT AND THE VA COR SHALL BE NOTIFIED IMMEDIATELY IF THE FIRE SUPPRESSION SYSTEM IS OUT OF SERVICE AND AN APPROVED FIRE WATCH SHALL BE PROVIDED FOR ALL OCCUPANTS LEFT UNPROTECTED BY THE SHUTDOWN UNTIL THE FIRE SUPPRESSION SYSTEM HAS BEEN RETURNED TO SERVICE.
- SPRINKLER SYSTEM IS TO REMAIN IN SERVICE THROUGHOUT PROJECT. TEMPORARILY REPLACE EXISTING PENDENT SPRINKLERS WITH UPRIGHT SPRINKLERS AND PIPING IN AREAS THAT HAVE CEILINGS REMOVED PER NFPA 241 AND NFPA 13.
- SPRINKLER SYSTEM SHALL COMPLY WITH NFPA 13 AT THE COMPLETION OF EACH PHASE. IF NEW DEFICIENCIES IN SPRINKLER SYSTEM SPACING IN AREAS OUTSIDE OF THE CONSTRUCTION AREA ARE CREATED DUE TO DEMOLITION AND CONSTRUCTION ACTIVITIES (E.G. WHEN TEMPORARY BARRIERS ARE INSTALLED, WHEN EXISTING WALLS ARE DEMOLISHED, AND/OR WHEN NEW PERMANENT WALLS ARE INSTALLED), THE CONTRACTOR SHALL MODIFY THE EXISTING SPRINKLERS TO MAINTAIN NFPA 13 COMPLIANCE.
- EXISTING SPRINKLER SYSTEMS OUTSIDE OF THE WORK AREA SHALL STAY ACTIVE THROUGHOUT THE PROJECT. SHUTDOWNS FOR WORK ON THE SYSTEM WITHIN THE AREA OF WORK THAT IMPACT SPRINKLER SYSTEMS OUTSIDE OF THE WORK AREA SHALL BE SCHEDULED WITH THE VA TWO WEEKS IN ADVANCE AND PROVISIONS SET IN PLACE PER NFPA 241. RESTORE SYSTEMS TO SERVICE AT THE END OF EACH WORKDAY.
- CONTRACTOR SHALL COORDINATE WITH THE COR AND VA PERSONNEL PRIOR TO ANY WORK ON THE EXISTING SPRINKLER SYSTEM.
- REFER TO GENERAL INFORMATION DRAWINGS FOR CONSTRUCTION PHASING INFORMATION.

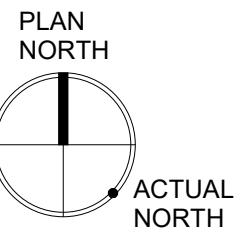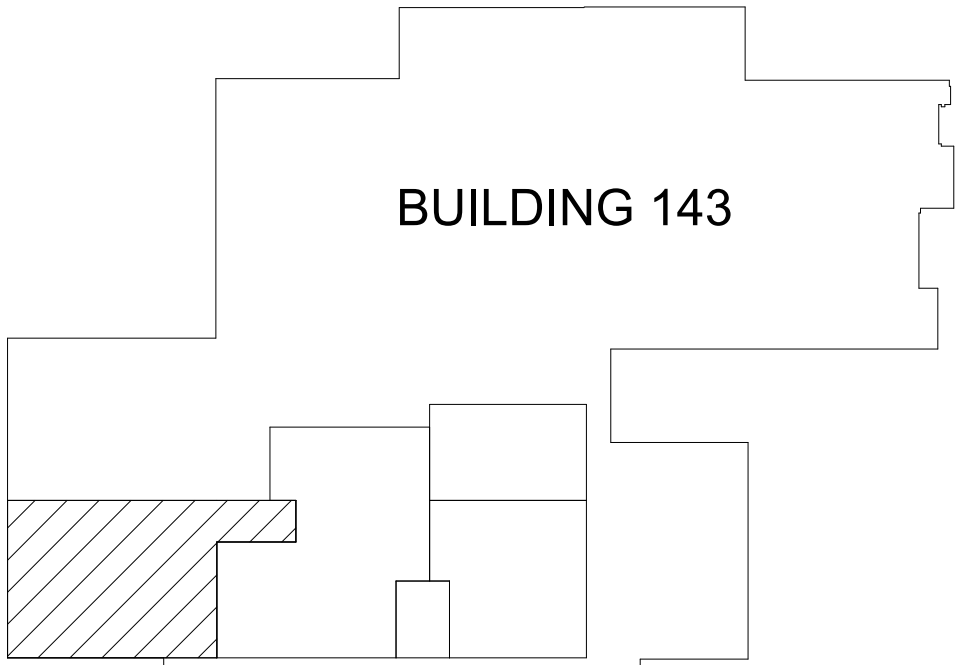

BUILDING 143

KEYPLAN

FIRST FLOOR FIRE SUPPRESSION
DEMOLITION PLAN - PHASE 1

F1

1/8" = 1'-0"

PRINTS OF THIS DRAWING SHALL NOT BE USED FOR ANY PURPOSE WHATSOEVER WITHOUT THE SEAL AND SIGNATURE OF THE PROFESSIONAL ENGINEER

CONSULTANT

Architecture: PF&A DESIGN, P.C. Civil Engineering: LABELLA ASSOCIATES Fire & Life Safety: STANTON ENGINEERING SERVICES, LLC

ENGINEER OF RECORD



(856) 429-4000 Miller-Remick.com

STANTON ENGINEERING SERVICES
PROFESSIONAL ENGINEER



Office of
Construction
and Facilities
Management

VA U.S. Department
of Veterans Affairs

Drawing Title
FIRE SUPPRESSION
DEMOLITION PLAN
FIRST FLOOR PHASE 1

Approved by:
Jon Manninen, COR

Phase

BID DOCUMENTS

FULLY SPRINKLERED

Project Title
RENOVATE SURGICAL SUITE
PHASE II
Project Number 658-19-103

Location
SALEM VA MEDICAL CENTER

Issue Date 2025-12-30 Checked PJ Drawn CA

VA Drawing Number
2617
Building Number
143

Drawing Number
P1-FK101

FIRST FLOOR FIRE SUPPRESSION PLAN -
PHASE 1

(F1) PHA
1/8" = 1'-0"

$$1/8'' = 1'-0''$$

PRINTS OF THIS DRAWING SHALL NOT BE USED FOR ANY PURPOSE WHATSOEVER WITHOUT THE SEAL AND SIGNATURE OF THE PROFESSIONAL ENGINEER	
Revisions:	Date:

CONSULTANT		
Architecture: PF&A DESIGN, P.C.	Civil Engineering: LABELLA ASSOCIATES	Fire & Life Safety: STANTON ENGINEERING SERVICES, LLC

ENGINEER OF RECORD



A Service-Disabled Veteran-Owned Small Business

(856) 429-6000 • [Miller-Remick.com](http://www.Miller-Remick.com)

PROFESSIONAL ENGINEERING

STANTON ENGINEERING SERVICES
PROFESSIONAL ENGINEER



12-95-0005

Office of
Construction
and Facilities
Management

VA | U.S. Department
of Veterans Affairs


Drawing Title	FIRE SUPPRESSION NEW WORK PLAN FIRST FLOOR PHASE 1
Approved by:	Jon Manninen, COR

Phase	BID DOCUMENTS
	FULLY SPRINKLERED


Project Title				VA Drawing Number	
RENOVATE SURGICAL SUITE PHASE II				2617	
Project Number				Building Number	
658-19-103				143	
Location				Drawing Number	
SALEM VA MEDICAL CENTER				P1-FX101	
Issue Date		Checked	Drawn		P1-FX101
2025-12-30		PJ	CA		

GENERAL NOTES

1. ALL AREAS ARE LIGHT HAZARD UNLESS OTHERWISE INDICATED BY HATCHING. REFER TO LEGEND BELOW FOR HAZARD CLASSIFICATION HATCHING.
2. FOR AREAS SUBJECT TO ELEVATED AMBIENT TEMPERATURES, SPRINKLER HEAD TEMPERATURE RATINGS SHALL BE IN ACCORDANCE WITH NFPA 13.
3. PROVIDE AUXILIARY DRAINS AS NECESSARY IN ACCORDANCE WITH NFPA 13.
4. PROVIDE ALL EQUIPMENT, MATERIAL, LABOR, SUPERVISION, COSTS AND SERVICES REQUIRED TO INSTALL COMPLETE AND WORKING SYSTEMS INCLUDING ALL ITEMS AND ADJUSTANCES NECESSARY, REASONABLY INCIDENTAL OR CUSTOMARILY INCLUDED, EVEN THOUGH EACH AND EVERY ITEM IS NOT SPECIFIED OR SHOWN.
5. PENETRATIONS OF WALLS OR FLOORS FOR SPRINKLER PIPING AND/OR EQUIPMENT SHALL BE PROPERLY SEALED AFTER INSTALLATIONS. FIELD VERIFY EXISTING WALL PENETRATIONS AND SEAL AS REQUIRED TO MAINTAIN WALL OR FLOOR RATING.
6. EACH TRADE SHALL COORDINATE THE ROUTING AND INSTALLATION OF THEIR WORK WITH THAT OF ALL OTHER TRADES THROUGH THE GENERAL CONTRACTOR. IN ANY INSTANCES OF CONFLICT, SYSTEMS REQUIRING "GRADE" OR "SLOPE" FOR DRAINAGE (SANITARY SEWER, SANITARY VENT, EQUIPMENT/CONDENSATE DRAINS, ETC.) SHALL HAVE PRIORITY.
7. CONTRACTOR TO COORDINATE ROUTING OF SPRINKLER PIPING WITH DUCTWORK, PIPING, AND STRUCTURE.
8. REFER TO MANUFACTURER'S LITERATURE AND INSTALLATION RECOMMENDATIONS/INSTRUCTIONS FOR EXACT SIZES AND LOCATIONS OF CONNECTIONS AND REQUIREMENTS OF OWNER FURNISHED EQUIPMENT.
9. DO NOT ROUTE SPRINKLER PIPING OVER OR THROUGH ELECTRICAL OR COMMUNICATION ROOMS UNLESS THE PIPING DIRECTLY SERVES EQUIPMENT IN THE ROOM.
10. DO NOT ROUTE PIPE ABOVE ELECTRICAL EQUIPMENT AS REQUIRED BY NFPA 13 AND NFPA 70, WHERE PIPING IS INSTALLED ABOVE THE DEDICATED ELECTRICAL SPACE, PROVIDE DRIP PANS BELOW AND ENSURE THERE ARE NO FITTINGS WITHIN THE DEDICATED ELECTRICAL SPACE.
11. CONTRACTOR SHALL COORDINATE WITH THE COR AND VA PERSONNEL PRIOR TO ANY WORK ON THE EXISTING SPRINKLER SYSTEM.
12. THE NEW SPRINKLER ZONES BOUNDARIES SHOWN SHALL MATCH THE NEW SMOKE COMPARTMENTS SHOWN IN THE GENERAL INFORMATION DRAWINGS. IF EXISTING SPRINKLERS SERVING AREAS OUTSIDE THE SCOPE OF WORK ARE FOUND TO BE AFFECTED BY THE NEW ZONING, PROVISIONS SHALL BE MADE TO PROVIDE A CONNECTION TO ITS APPROPRIATE ZONE. ALL WORK SHALL BE COORDINATED WITH THE COR AND VA PERSONNEL.
13. REFER TO GENERAL INFORMATION DRAWINGS FOR CONSTRUCTION PHASING INFORMATION.

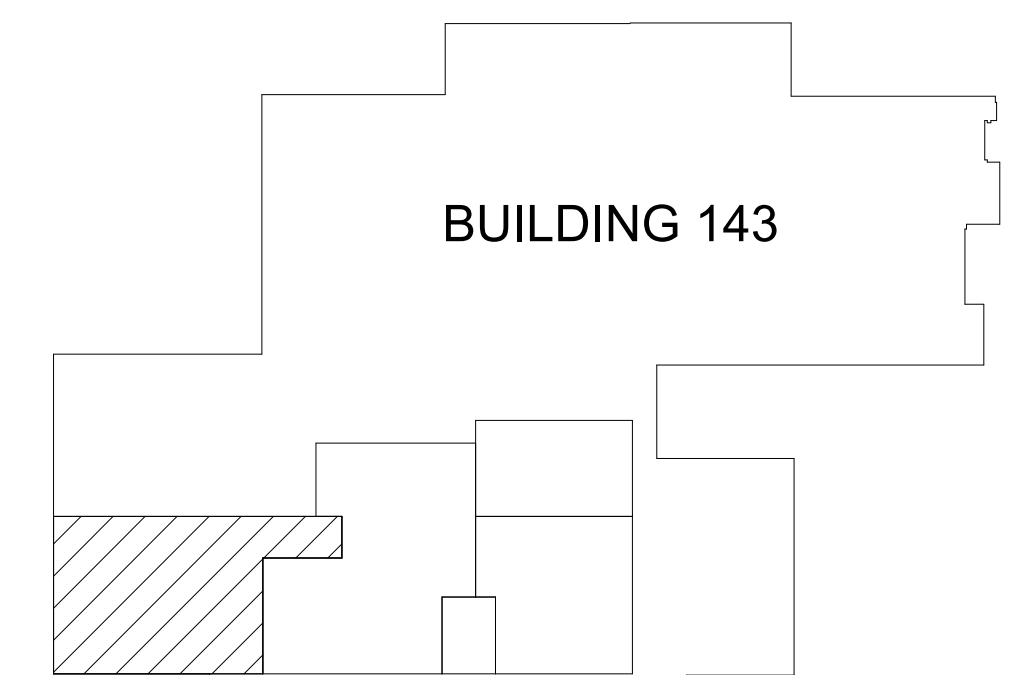

KEYPLAN

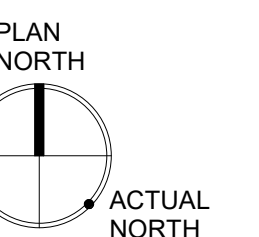



1. DEMOLISH EXISTING SPRINKLERS AND PIPING TO ACCOMMODATE NEW ARCHITECTURAL LAYOUT WITHIN THE AREA OF WORK UNLESS NOTED OTHERWISE. COORDINATE WITH VA OUTAGE REQUIREMENTS AND THE COR.
2. EXISTING SPRINKLER MAIN PIPING AND ZONING IS SHOWN IN APPROXIMATE LOCATIONS. PER RECORD DOCUMENTS, THE ZONE CD SPRINKLER MAINS ARE CONNECTED BY BRANCHLINES. CONTRACTOR SHALL VERIFY EXACT LOCATIONS AND SIZE OF PIPING AND EQUIPMENT PRIOR TO CONSTRUCTION. EXISTING CONDITIONS DETERMINED FROM LIMITED SITE INVESTIGATION AND RECORD DOCUMENTS.
3. EXISTING SMOKE ZONE BOUNDARIES SHOWN ARE BASED ON RECORD DOCUMENTATION AND GENERAL INFORMATION DRAWINGS. CONTRACTOR SHALL COORDINATE WITH THE COR AND VA PERSONNEL IF ANY DISCREPANCIES ARE DISCOVERED IN THE FIELD.
4. MAINTAIN ALL FIRE SUPPRESSION SYSTEMS CONTINUITY AND NFPA 13 COMPLIANCE (E.G. SPACING, DISTANCE TO CEILING, OBSTRUCTION REQUIREMENTS, ETC.) DURING RENOVATION. THE FIRE DEPARTMENT AND THE VA COR SHALL BE NOTIFIED IMMEDIATELY IF THE FIRE SUPPRESSION SYSTEM IS OUT OF SERVICE AND AN APPROVED FIRE WATCH SHALL BE PROVIDED FOR ALL OCCUPANTS LEFT UNPROTECTED BY THE SHUTDOWN UNTIL THE FIRE SUPPRESSION SYSTEM HAS BEEN RETURNED TO SERVICE.
5. SPRINKLER SYSTEM IS TO REMAIN IN SERVICE THROUGHOUT PROJECT. TEMPORARILY REPLACE EXISTING PENDENT SPRINKLERS WITH UPRIGHT SPRINKLERS AND PIPING IN AREAS THAT HAVE CEILINGS REMOVED PER NFPA 241 AND NFPA 13.
6. SPRINKLER SYSTEM SHALL COMPLY WITH NFPA 13 AT THE COMPLETION OF EACH PHASE. IF NEW DEFICIENCIES IN SPRINKLER SYSTEM SPACING IN AREAS OUTSIDE OF THE CONSTRUCTION AREA ARE CREATED DUE TO DEMOLITION AND CONSTRUCTION ACTIVITIES (E.G. WHEN TEMPORARY BARRIERS ARE INSTALLED, WHEN EXISTING WALLS ARE DEMOLISHED, AND/OR WHEN NEW PERMANENT WALLS ARE INSTALLED), THE CONTRACTOR SHALL MODIFY THE EXISTING SPRINKLERS TO MAINTAIN NFPA 13 COMPLIANCE.
7. EXISTING SPRINKLER SYSTEMS OUTSIDE OF THE WORK AREA SHALL STAY ACTIVE THROUGHOUT THE PROJECT. SHUTDOWNS FOR WORK ON THE SYSTEM WITHIN THE AREA OF WORK THAT IMPACT SPRINKLER SYSTEMS OUTSIDE OF THE WORK AREA SHALL BE SCHEDULED WITH THE VA TWO WEEKS IN ADVANCE AND PROVISIONS SET IN PLACE PER NFPA 241. RESTORE SYSTEMS TO SERVICE AT THE END OF EACH WORKDAY.
8. CONTRACTOR SHALL COORDINATE WITH THE COR AND VA PERSONNEL PRIOR TO ANY WORK ON THE EXISTING SPRINKLER SYSTEM.
9. REFER TO GENERAL INFORMATION DRAWINGS FOR CONSTRUCTION PHASING INFORMATION.



F1

PRINTS OF THIS DRAWING SHALL NOT BE USED FOR ANY PURPOSE WHATSOEVER WITHOUT THE SEAL AND SIGNATURE OF THE PROFESSIONAL ENGINEER	
Revisions:	Date:

Architecture: PF&A DESIGN, P.C.	Civil Engineering: LABELLA ASSOCIATES	Fire & Life Safety: STANTON ENGINEERING SERVICES, LLC

A Service-Disabled Veteran-Owned Small Business
(856) 429-4000 • MillerRemick.com
13200 Old Forge Road, Suite 200, Newark, NJ 07102


VA U.S. Department
of Veterans Affairs

Approved by:
Jon Manninen, COR


FULLY SPRINKLERED

Location	SALEM VA MEDICAL CENTER
----------	-------------------------

Drawing Number
2617
Building Number
143
Drawing Number
P2-FK101

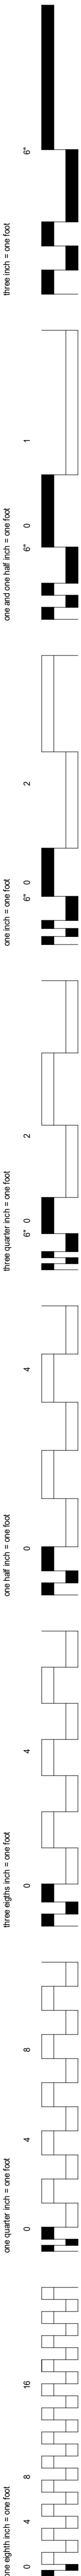

1. ALL AREAS ARE LIGHT HAZARD UNLESS OTHERWISE INDICATED BY HATCHING. REFER TO LEGEND BELOW FOR HAZARD CLASSIFICATION HATCHING.
2. FOR AREAS SUBJECT TO ELEVATED AMBIENT TEMPERATURES, SPRINKLER HEAD TEMPERATURE RATINGS SHALL BE IN ACCORDANCE WITH NFPA 13.
3. PROVIDE AUXILIARY DRAINS AS NECESSARY IN ACCORDANCE WITH NFPA 13.
4. PROVIDE ALL EQUIPMENT, MATERIAL, LABOR, SUPERVISION, COSTS AND SERVICES REQUIRED TO INSTALL COMPLETE AND WORKING SYSTEMS INCLUDING ALL ITEMS AND APPURTENANCES NECESSARY, REASONABLY INCIDENTAL, OR CUSTOMARILY INCLUDED, EVEN THOUGH EACH AND EVERY ITEM IS NOT SPECIFIED OR SHOWN.
5. PENETRATIONS OF WALLS OR FLOORS FOR SPRINKLER PIPING AND/OR EQUIPMENT SHALL BE PROPERLY SEALED AFTER INSTALLATIONS. FIELD VERIFY EXISTING WALL PENETRATIONS AND SEAL AS REQUIRED TO MAINTAIN WALL OR FLOOR RATING.
6. EACH TRADE SHALL COORDINATE THE ROUTING AND INSTALLATION OF THEIR WORK WITH THAT OF ALL OTHER TRADES THROUGH THE GENERAL CONTRACTOR. IN ANY INSTANCES OF CONFLICT, SYSTEMS REQUIRING "GRADE" OR "SLOPE" FOR DRAINAGE (SANITARY SEWER, SANITARY VENT, EQUIPMENT/CONDENSATE DRAINS, ETC.) SHALL HAVE PRIORITY.
7. CONTRACTOR TO COORDINATE ROUTING OF SPRINKLER PIPING WITH DUCTWORK, PIPING, AND STRUCTURE.
8. REFER TO MANUFACTURER'S LITERATURE AND INSTALLATION RECOMMENDATION INSTRUCTIONS FOR EXACT SIZES AND LOCATIONS OF CONNECTIONS AND REQUIREMENTS OF OWNER FURNISHED EQUIPMENT.
9. DO NOT ROUTE SPRINKLER PIPING OVER OR THROUGH ELECTRICAL OR COMMUNICATION ROOMS UNLESS THE PIPING DIRECTLY SERVES EQUIPMENT IN THE ROOM.
10. DO NOT ROUTE PIPE ABOVE ELECTRICAL EQUIPMENT AS REQUIRED BY NFPA 13 AND NFPA 70. WHERE PIPING IS INSTALLED ABOVE THE DEDICATED ELECTRICAL SPACE, PROVIDE DRIP PANS BELOW AND ENSURE THERE ARE NO FITTINGS WITHIN THE DEDICATED ELECTRICAL SPACE.
11. CONTRACTOR SHALL COORDINATE WITH THE COR AND VA PERSONNEL PRIOR TO ANY WORK ON THE EXISTING SPRINKLER SYSTEM.
12. THE NEW SPRINKLER ZONES BOUNDARIES SHOWN SHALL MATCH THE NEW SMOKE COMPARTMENTS SHOWN IN THE GENERAL INFORMATION DRAWINGS. IF EXISTING SPRINKLERS SERVING AREAS OUTSIDE THE SCOPE OF WORK ARE FOUND TO BE AFFECTED BY THE NEW ZONING, PROVISIONS SHALL BE MADE TO PROVIDE A CONNECTION TO ITS APPROPRIATE ZONE. ALL WORK SHALL BE COORDINATED WITH THE COR AND VA PERSONNEL.
13. REFER TO GENERAL INFORMATION DRAWINGS FOR CONSTRUCTION PHASING INFORMATION.

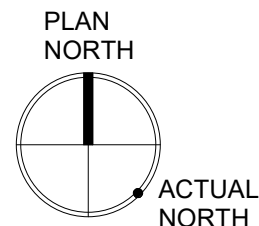

KEYPLAN

F1

PRINTS OF THIS DRAWING SHALL NOT BE USED FOR ANY PURPOSE WHATSOEVER WITHOUT THE SEAL AND SIGNATURE OF THE PROFESSIONAL ENGINEER

Revisions:	Date:

Architecture: PF&A DESIGN, P.C.	Civil Engineering: LABELLA ASSOCIATES	Fire & Life Safety: STANTON ENGINEERING SERVICES, LLC

A Service-Disabled Veteran-Owned Small Business
(856) 429-4000 ★ Miller-Remick.com

VA U.S. Department
of Veterans Affairs

Approved by:
Jon Manninen, COR


FULLY SPRINKLERED

Location		
SALEM VA MEDICAL CENTER		
Issue Date	Checked	Drawn
2025-12-30	PJ	

Drawing Number	2617
Building Number	143
Drawing Number	P2-FX101


GENERAL NOTES

- ALL AREAS ARE LIGHT HAZARD UNLESS OTHERWISE INDICATED BY HATCHING. REFER TO LEGEND BELOW FOR HAZARD CLASSIFICATION HATCHING.
- FOR AREAS SUBJECT TO ELEVATED AMBIENT TEMPERATURES, SPRINKLER HEAD TEMPERATURE RATINGS SHALL BE IN ACCORDANCE WITH NFPA 13.
- PROVIDE AUXILIARY DRAINS AS NECESSARY IN ACCORDANCE WITH NFPA 13.
- PROVIDE ALL EQUIPMENT, MATERIAL, LABOR, SUPERVISION, COSTS AND SERVICES REQUIRED TO INSTALL COMPLETE AND WORKING SYSTEMS INCLUDING ALL ITEMS AND APPURTENANCES NECESSARY, REASONABLY INCIDENTAL, OR CUSTOMARILY INCLUDED, EVEN THOUGH EACH AND EVERY ITEM IS NOT SPECIFIED OR SHOWN.
- PENETRATIONS OF WALLS OR FLOORS FOR SPRINKLER PIPING AND/OR EQUIPMENT SHALL BE PROPERLY SEALED AFTER INSTALLATIONS. FIELD VERIFY EXISTING WALL PENETRATIONS AND SEAL AS REQUIRED TO MAINTAIN WALL OR FLOOR RATING.
- EACH TRADE SHALL COORDINATE THE ROUTING AND INSTALLATION OF THEIR WORK WITH THAT OF ALL OTHER TRADES THROUGH THE GENERAL CONTRACTOR. IN ANY INSTANCES OF CONFLICT, SYSTEMS REQUIRING "GRADE" OR "SLOPE" FOR DRAINAGE (SANITARY SEWER, SANITARY VENT, EQUIPMENT/CONDENSATE DRAINS, ETC.) SHALL HAVE PRIORITY.
- CONTRACTOR TO COORDINATE ROUTING OF SPRINKLER PIPING WITH DUCTWORK, PIPING, AND STRUCTURE.
- REFER TO MANUFACTURER'S LITERATURE AND INSTALLATION RECOMMENDATIONS/INSTRUCTIONS FOR EXACT SIZES AND LOCATIONS OF CONNECTIONS AND REQUIREMENTS OF OWNER FURNISHED EQUIPMENT.
- DO NOT ROUTE SPRINKLER PIPING OVER OR THROUGH ELECTRICAL OR COMMUNICATION ROOMS UNLESS THE PIPING DIRECTLY SERVES EQUIPMENT IN THE ROOM.
- DO NOT ROUTE PIPE ABOVE ELECTRICAL EQUIPMENT AS REQUIRED BY NFPA 13 AND NFPA 70. WHERE PIPING IS INSTALLED ABOVE THE DEDICATED ELECTRICAL SPACE, PROVIDE DRIP PANS BELOW AND ENSURE THERE ARE NO FITTINGS WITHIN THE DEDICATED ELECTRICAL SPACE.
- CONTRACTOR SHALL COORDINATE WITH THE COR AND VA PERSONNEL PRIOR TO ANY WORK ON THE EXISTING SPRINKLER SYSTEM.
- THE NEW SPRINKLER ZONES BOUNDARIES SHOWN SHALL MATCH THE NEW SMOKE COMPARTMENTS SHOWN IN THE GENERAL INFORMATION DRAWINGS. IF EXISTING SPRINKLERS SERVING AREAS OUTSIDE THE SCOPE OF WORK ARE FOUND TO BE AFFECTED BY THE NEW ZONING, PROVISIONS SHALL BE MADE TO PROVIDE A CONNECTION TO ITS APPROPRIATE ZONE. ALL WORK SHALL BE COORDINATED WITH THE COR AND VA PERSONNEL.
- REFER TO GENERAL INFORMATION DRAWINGS FOR CONSTRUCTION PHASING INFORMATION.

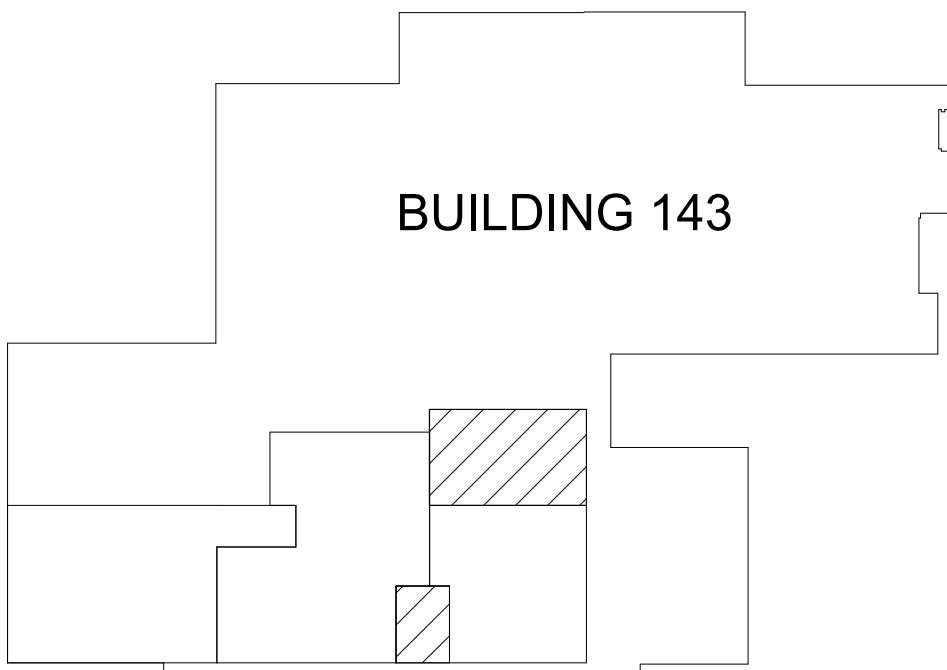

BUILDING 143

KEYPLAN

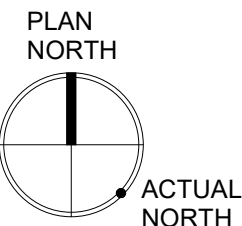

FIRST FLOOR FIRE SUPPRESSION PLAN -
PHASE 3 - PREP/RECOVERY

F1

1/8" = 1'-0"

PRINTS OF THIS DRAWING SHALL NOT BE USED FOR ANY PURPOSE WHATSOEVER WITHOUT THE SEAL AND SIGNATURE OF THE PROFESSIONAL ENGINEER

CONSULTANT

Architecture: PF&A DESIGN, P.C. Civil Engineering: LABELLA ASSOCIATES Fire & Life Safety: STANTON ENGINEERING SERVICES, LLC

ENGINEER OF RECORD



(856) 429-4000 • Miller-Remick.com

STANTON ENGINEERING SERVICES
PROFESSIONAL ENGINEER



Office of
Construction
and Facilities
Management

VA U.S. Department
of Veterans Affairs

Drawing Title
FIRE SUPPRESSION
NEW WORK PLAN
FIRST FLOOR PHASE 3

Approved by:
Jon Manninen, COR

Phase

BID DOCUMENTS

FULLY SPRINKLERED

Project Title
RENOVATE SURGICAL SUITE
PHASE II

Project Number 658-19-103

Location
SALEM VA MEDICAL CENTER

Issue Date 2025-12-30 Checked PJ Drawn CA

VA Drawing Number

2617


Building Number 143

Drawing Number

P3-FX101


GENERAL NOTES

- DEMOLISH EXISTING SPRINKLERS AND PIPING TO ACCOMMODATE NEW ARCHITECTURAL LAYOUT WITHIN THE AREA OF WORK UNLESS NOTED OTHERWISE. COORDINATE WITH VA OUTAGE REQUIREMENTS AND THE COR.
- EXISTING SPRINKLER MAIN PIPING AND ZONING IS SHOWN IN APPROXIMATE LOCATIONS. PER RECORD DOCUMENTS, THE ZONE CD SPRINKLER MAINS ARE CONNECTED BY BRANCHLINES. CONTRACTOR SHALL VERIFY EXACT LOCATIONS AND SIZE OF PIPING AND EQUIPMENT PRIOR TO CONSTRUCTION. EXISTING CONDITIONS DETERMINED FROM LIMITED SITE INVESTIGATION AND RECORD DOCUMENTS.
- EXISTING SMOKE ZONE BOUNDARIES SHOWN ARE BASED ON RECORD DOCUMENTATION AND GENERAL INFORMATION DRAWINGS. CONTRACTOR SHALL COORDINATE WITH THE COR AND VA PERSONNEL IF ANY DISCREPANCIES ARE DISCOVERED IN THE FIELD.
- MAINTAIN ALL FIRE SUPPRESSION SYSTEMS CONTINUITY AND NFPA 13 COMPLIANCE (E.G. SPACING, DISTANCE TO CEILING, OBSTRUCTION REQUIREMENTS, ETC.) DURING RENOVATION. THE FIRE DEPARTMENT AND THE VA COR SHALL BE NOTIFIED IMMEDIATELY IF THE FIRE SUPPRESSION SYSTEM IS OUT OF SERVICE AND AN APPROVED FIRE WATCH SHALL BE PROVIDED FOR ALL OCCUPANTS LEFT UNPROTECTED BY THE SHUTDOWN UNTIL THE FIRE SUPPRESSION SYSTEM HAS BEEN RETURNED TO SERVICE.
- SPRINKLER SYSTEM IS TO REMAIN IN SERVICE THROUGHOUT PROJECT. TEMPORARILY REPLACE EXISTING PENDENT SPRINKLERS WITH UPRIGHT SPRINKLERS AND PIPING IN AREAS THAT HAVE CEILINGS REMOVED PER NFPA 241 AND NFPA 13.
- SPRINKLER SYSTEM SHALL COMPLY WITH NFPA 13 AT THE COMPLETION OF EACH PHASE. IF NEW DEFICIENCIES IN SPRINKLER SYSTEM SPACING IN AREAS OUTSIDE OF THE CONSTRUCTION AREA ARE CREATED DUE TO DEMOLITION AND CONSTRUCTION ACTIVITIES (E.G. WHEN TEMPORARY BARRIERS ARE INSTALLED, WHEN EXISTING WALLS ARE DEMOLISHED, AND/OR WHEN NEW PERMANENT WALLS ARE INSTALLED), THE CONTRACTOR SHALL MODIFY THE EXISTING SPRINKLERS TO MAINTAIN NFPA 13 COMPLIANCE.
- EXISTING SPRINKLER SYSTEMS OUTSIDE OF THE WORK AREA SHALL STAY ACTIVE THROUGHOUT THE PROJECT. SHUTDOWNS FOR WORK ON THE SYSTEM WITHIN THE AREA OF WORK THAT IMPACT SPRINKLER SYSTEMS OUTSIDE OF THE WORK AREA SHALL BE SCHEDULED WITH THE VA TWO WEEKS IN ADVANCE AND PROVISIONS SET IN PLACE PER NFPA 241. RESTORE SYSTEMS TO SERVICE AT THE END OF EACH WORKDAY.
- CONTRACTOR SHALL COORDINATE WITH THE COR AND VA PERSONNEL PRIOR TO ANY WORK ON THE EXISTING SPRINKLER SYSTEM.
- REFER TO GENERAL INFORMATION DRAWINGS FOR CONSTRUCTION PHASING INFORMATION.

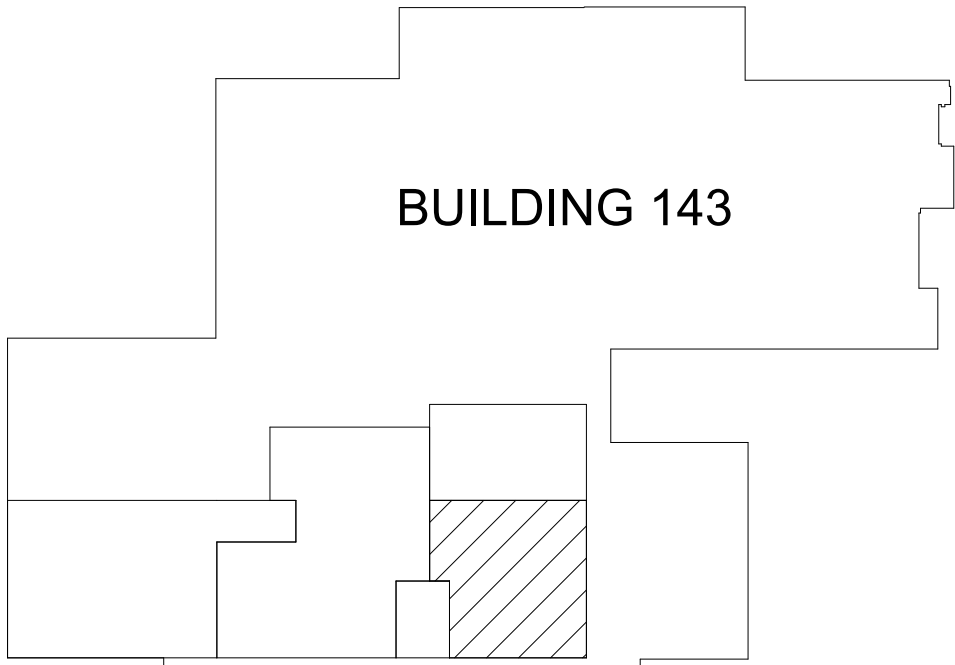

BUILDING 143

KEYPLAN

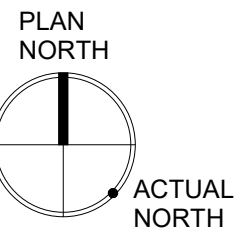

FIRST FLOOR FIRE SUPPRESSION
DEMOLITION PLAN - PHASE 4

1/8" = 1'-0"

PRINTS OF THIS DRAWING SHALL NOT BE USED FOR ANY PURPOSE WHATSOEVER WITHOUT THE SEAL AND SIGNATURE OF THE PROFESSIONAL ENGINEER

CONSULTANT

Architecture: PF&A DESIGN, P.C. Civil Engineering: LABELLA ASSOCIATES Fire & Life Safety: STANTON ENGINEERING SERVICES, LLC

ENGINEER OF RECORD



Miller-Remick.com

STANTON ENGINEERING SERVICES
PROFESSIONAL ENGINEER



Office of
Construction
and Facilities
Management



U.S. Department
of Veterans Affairs

Drawing Title
FIRE SUPPRESSION
DEMOLITION PLAN
FIRST FLOOR PHASE 4

Approved by:
Jon Manninen, COR

Phase

BID DOCUMENTS

FULLY SPRINKLERED

Project Title
RENOVATE SURGICAL SUITE
PHASE II

Project Number 658-19-103

Location
SALEM VA MEDICAL CENTER

Issue Date
2025-12-30

Checked
PJ

Drawn
CA

VA Drawing Number

2617

Building Number


143

Drawing Number

P4-FK101



1. ALL AREAS ARE LIGHT HAZARD UNLESS OTHERWISE INDICATED BY HATCHING. REFER TO LEGEND BELOW FOR HAZARD CLASSIFICATION HATCHING.
2. FOR AREAS SUBJECT TO ELEVATED AMBIENT TEMPERATURES, SPRINKLER HEAD TEMPERATURE RATINGS SHALL BE IN ACCORDANCE WITH NFPA 13.
3. PROVIDE AUXILIARY DRAINS AS NECESSARY IN ACCORDANCE WITH NFPA 13.
4. PROVIDE ALL EQUIPMENT, MATERIAL, LABOR, SUPERVISION, COSTS AND SERVICES REQUIRED TO INSTALL COMPLETE AND WORKING SYSTEMS INCLUDING ALL ITEMS AND APPURTENANCES NECESSARY. REASONABLY INCIDENTAL, OR CUSTOMARILY INCURRED, EVEN THOUGH EACH AND EVERY ITEM IS NOT SPECIFIED OR SHOWN.
5. PENETRATIONS OF WALLS OR FLOORS FOR SPRINKLER PIPING AND/OR EQUIPMENT SHALL BE PROPERLY SEALED AFTER INSTALLATIONS. FIELD VERIFYING EXISTING WALL PENETRATIONS AND SEAL AS REQUIRED TO MAINTAIN WALL OR FLOOR RATING.
6. EACH TRADE SHALL COORDINATE THE ROUTING AND INSTALLATION OF THEIR WORK WITH THAT OF ALL OTHER TRADES THROUGH THE GENERAL CONTRACTOR. IN ANY INSTANCES OF CONFLICT, SYSTEMS REQUIRING "GRADE" OR "SLOPE" FOR DRAINAGE (SAFETY SEWER, SLOTTED VENT, EQUIPMENT/CONDENSATE DRAINS, ETC.) SHALL HAVE PRIORITY.
7. CONTRACTOR TO COORDINATE ROUTING OF SPRINKLER PIPING WITH DUCTWORK, PIPING, AND STRUCTURE.
8. REFER TO MANUFACTURER'S LITERATURE AND INSTALLATION RECOMMENDATIONS FOR EXACT SIZES AND LOCATIONS OF CONNECTIONS AND REQUIREMENTS OF OWNER FURNISHED EQUIPMENT.
9. DO NOT ROUTE SPRINKLER PIPING OVER OR THROUGH ELECTRICAL OR COMMUNICATION ROOMS UNLESS THE PIPING DIRECTLY SERVES EQUIPMENT IN THE ROOM.
10. DO NOT ROUTE PIPE ABOVE ELECTRICAL EQUIPMENT AS REQUIRED BY NFPA 13 AND NFPA 70, WHERE PIPING IS INSTALLED ABOVE THE DEDICATED ELECTRICAL SPACE, PROVIDE DRIP PANS BELOW AND ENSURE THERE ARE NO FITTINGS WITHIN THE DEDICATED ELECTRICAL SPACE.
11. CONTRACTOR SHALL COORDINATE WITH THE COR AND VA PERSONNEL PRIOR TO ANY WORK ON THE EXISTING SPRINKLER SYSTEM.
12. THE NEW SPRINKLER ZONES BOUNDARIES SHOWN SHALL MATCH THE NEW SMOKE COMPARTMENTS SHOWN IN THE GENERAL INFORMATION DRAWINGS. IF EXISTING SPRINKLERS SERVING AREAS OUTSIDE THE SCOPE OF WORK ARE FOUND TO BE AFFECTED BY THE NEW ZONING, PROVISIONS SHALL BE MADE TO PROVIDE A CONNECTION TO ITS APPROPRIATE ZONE. ALL WORK SHALL BE COORDINATED WITH THE COR AND VA PERSONNEL.
13. REFER TO GENERAL INFORMATION DRAWINGS FOR CONSTRUCTION PHASING INFORMATION.

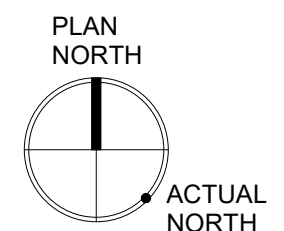

KEYPLAN

F1

PRINTS OF THIS DRAWING SHALL NOT BE USED FOR ANY PURPOSE WHATSOEVER WITHOUT THE SEAL AND SIGNATURE OF THE PROFESSIONAL ENGINEER	
Revisions:	Date:

Architecture: PF&A DESIGN, P.C.	Civil Engineering: LABELLA ASSOCIATES	Fire & Life Safety: STANTON ENGINEERING SERVICES, LLC

A Service-Disabled Veteran-Owned Small Business

(856) 429-4000 • Miller-Remick.com

OUR PROJECT NO: 0480156

VA | U.S. Department
of Veterans Affairs


Approved by:
Jon Manninen, COR

FULLY SPRINKLERED


Location	SALEM VA MEDICAL CENTER
----------	-------------------------

P4-FX101


0 1 2 

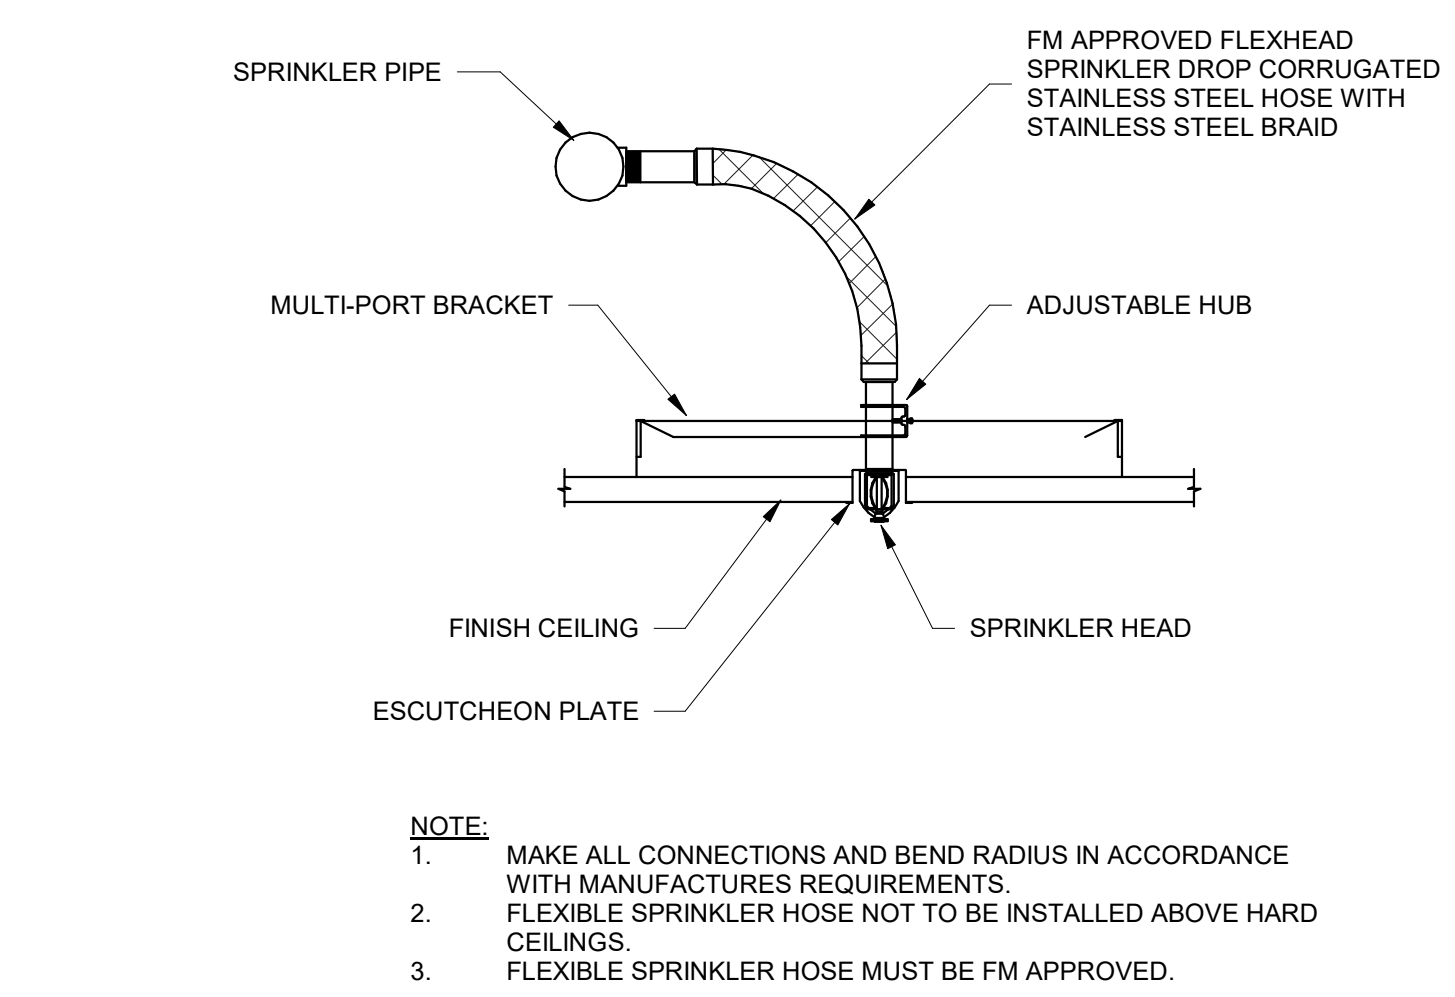


TYPICAL FLEXIBLE SPRINKLER HOSE DETAIL
B6
NTS

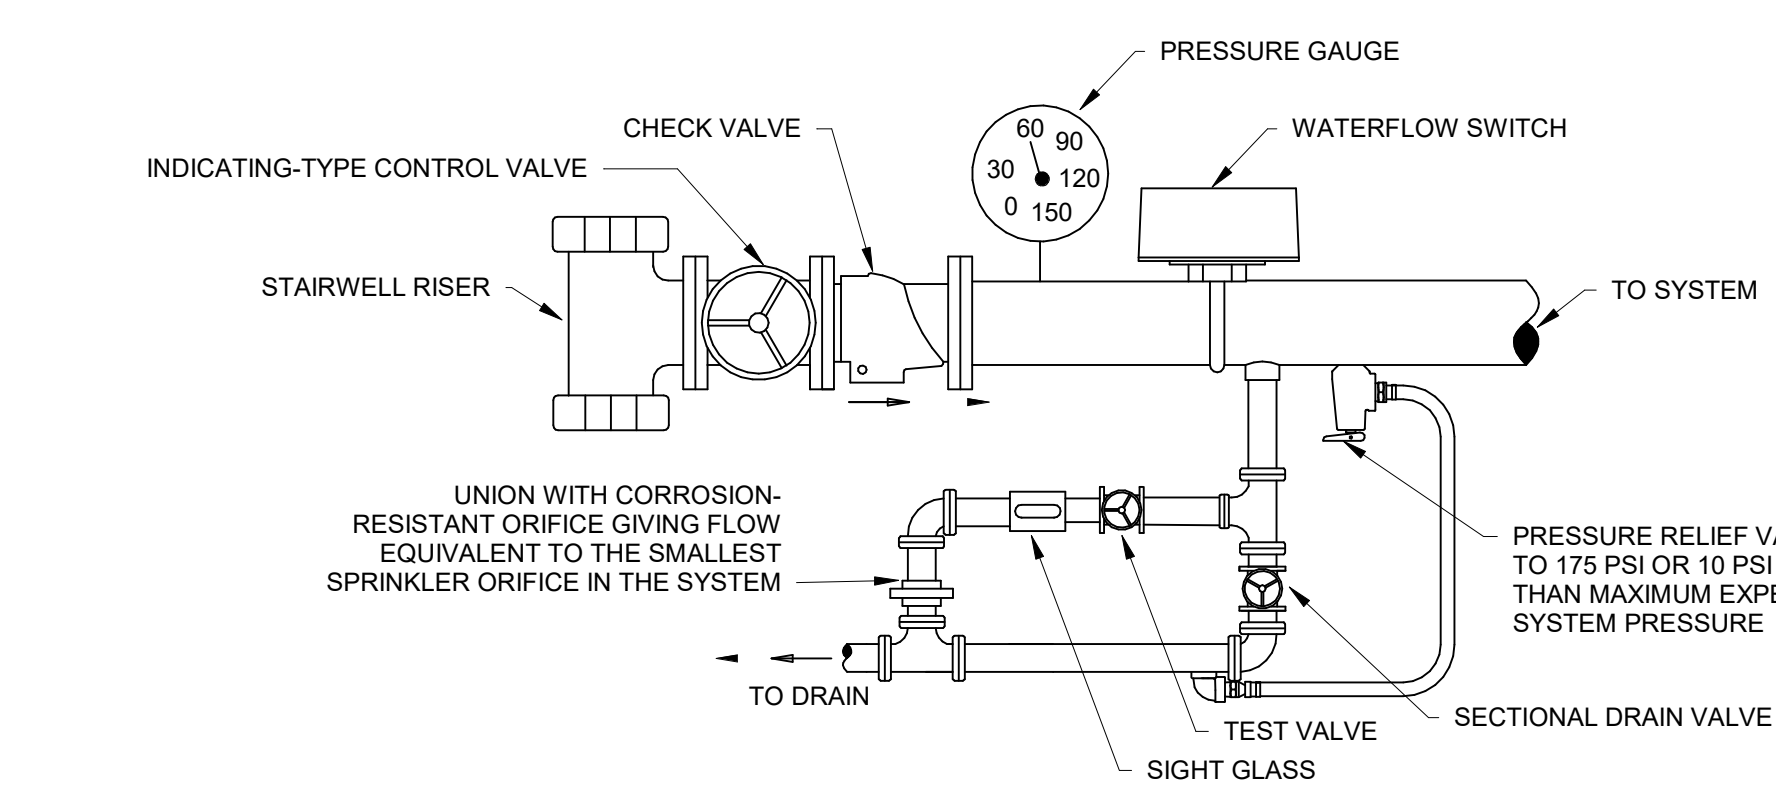


TYPICAL ZONE CONTROL ASSEMBLY (PRESSURE GAUGE)
D6
NTS

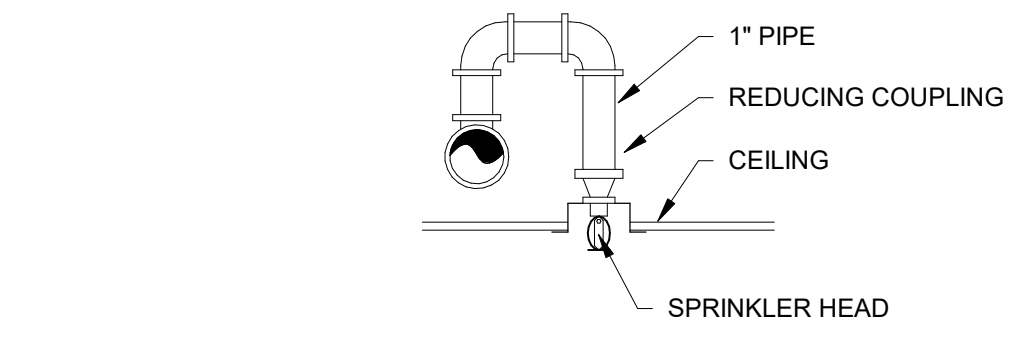

SEMI-RECESSED SPRINKLER HEAD DETAIL
D8
NTS

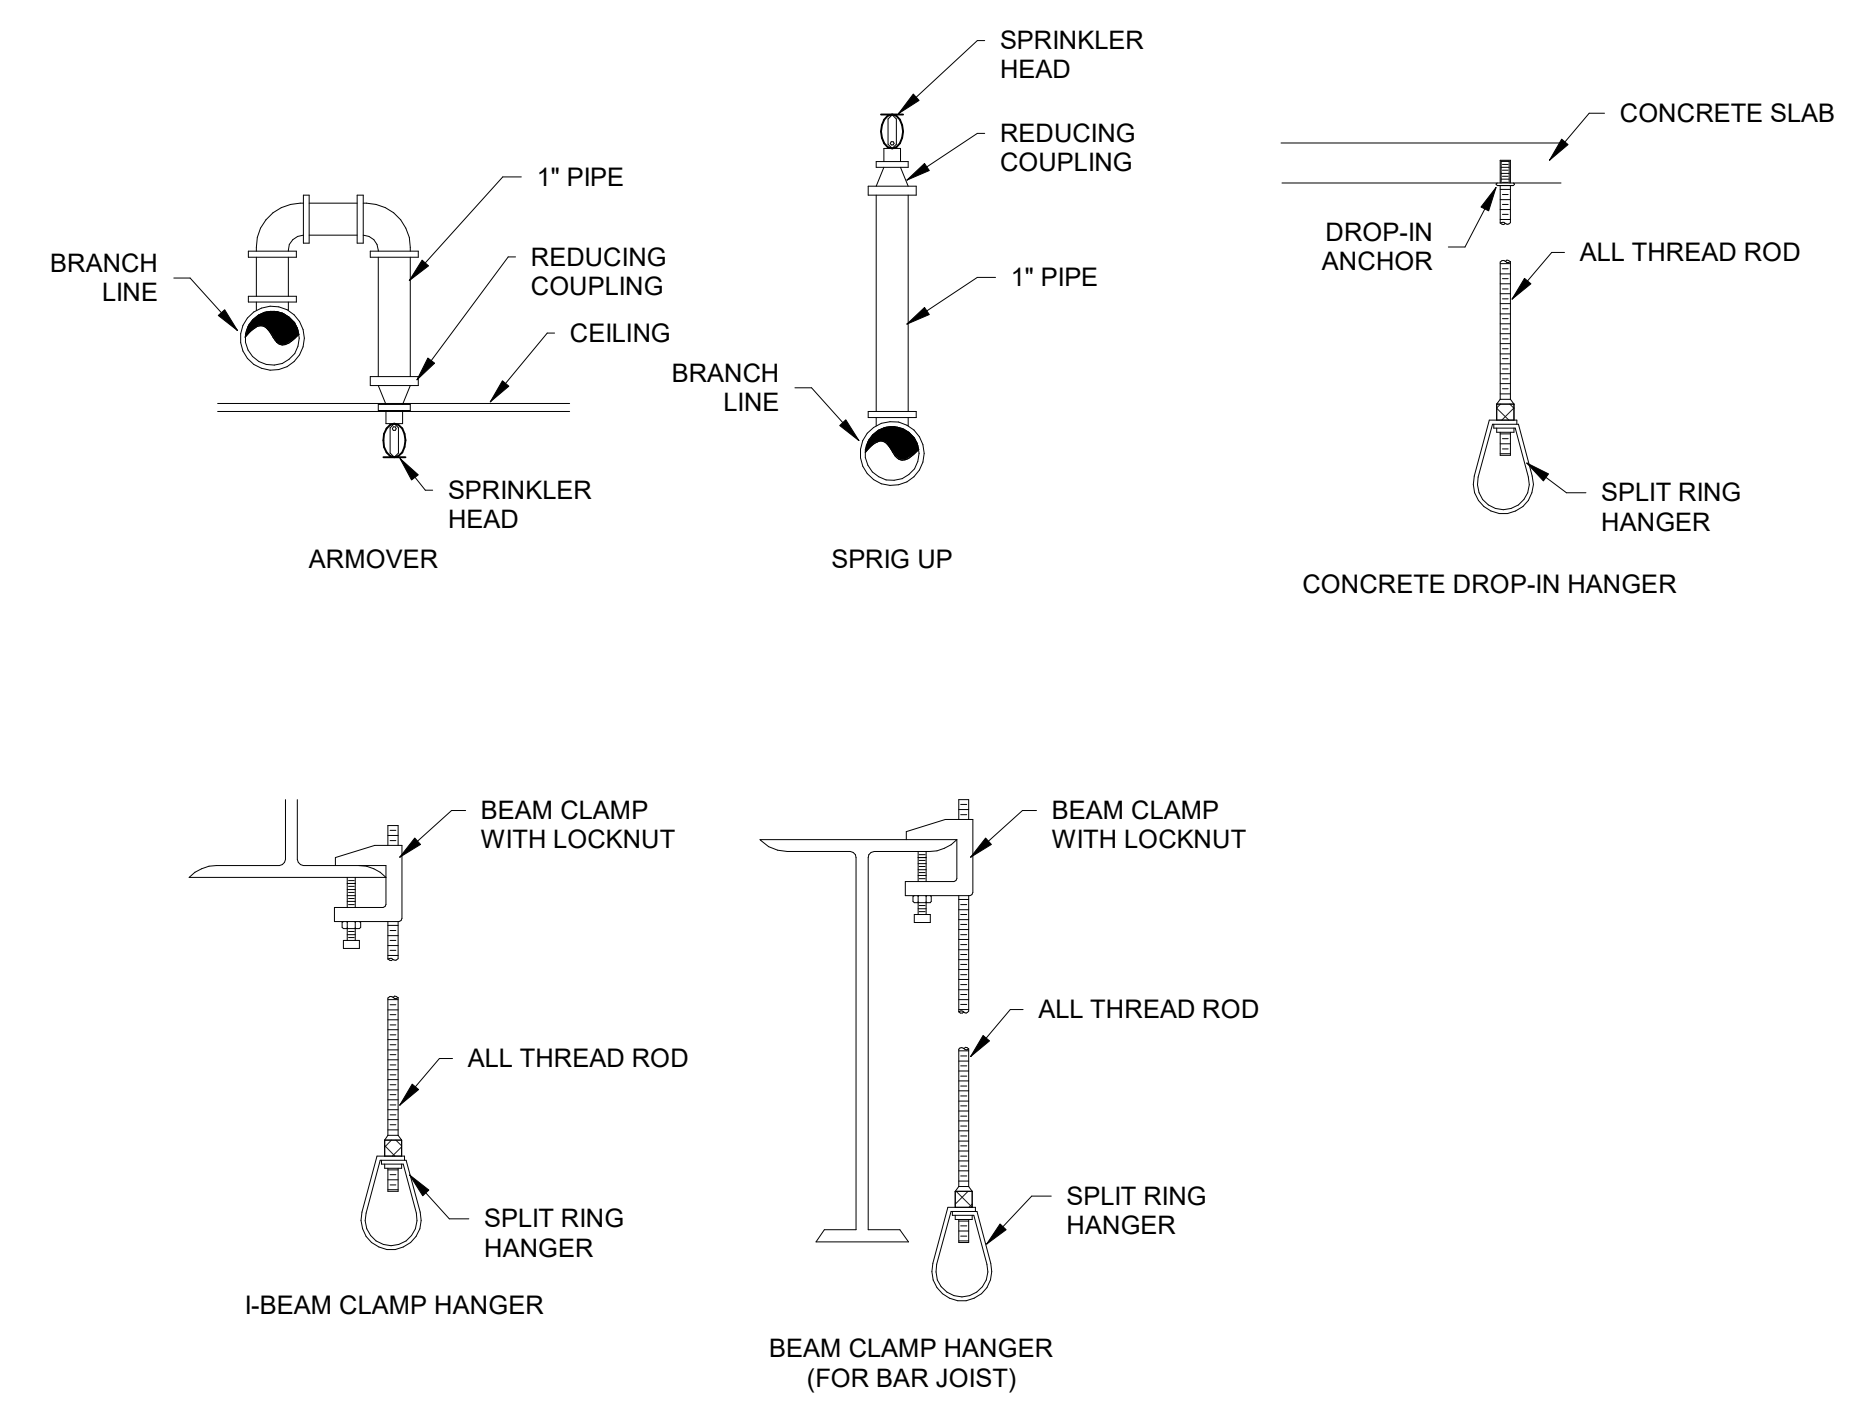


SPRINKLER ARMOVER, SPRIG, AND HANGER DETAILS
F6
NTS

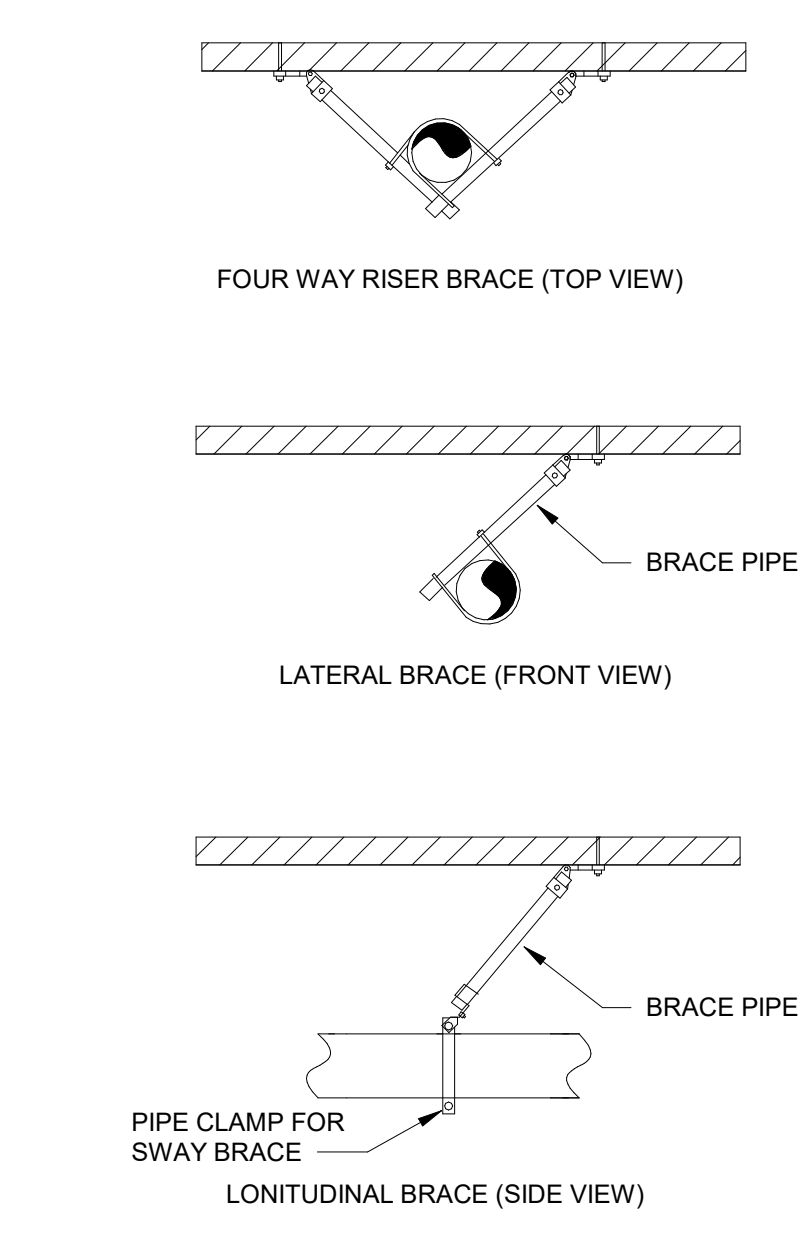

SEISMIC/EARTHQUAKE
F8
NTS


PRINTS OF THIS DRAWING SHALL NOT BE USED FOR ANY PURPOSE WHATSOEVER WITHOUT THE SEAL AND SIGNATURE OF THE PROFESSIONAL ENGINEER		CONSULTANT			ENGINEER OF RECORD		STANTON ENGINEERING SERVICES PROFESSIONAL ENGINEER		Office of Construction and Facilities Management VA U.S. Department of Veterans Affairs		Drawing Title FIRE SUPPRESSION DETAILS	Phase BID DOCUMENTS	Project Title RENOVATE SURGICAL SUITE PHASE II Project Number 658-19-103	VA Drawing Number 2617 Building Number 143
Revisions:		Architecture: PF&A DESIGN, P.C.	Civil Engineering: LABELLA ASSOCIATES	Fire & Life Safety: STANTON ENGINEERING SERVICES, LLC	MILLER-REMICK A Service-Disabled Veteran-Owned Small Business (856) 429-4000 • Miller-Remick.com		PAUL KENNETH JORDAN PROFESSIONAL ENGINEER 12-30-2025		Approved by: Jon Manninen, COR		FULLY SPRINKLERED		Location SALEM VA MEDICAL CENTER	Drawing Number FX501
Date:													Issue Date 2025-12-30	Checked PJ
													Drawn CA	

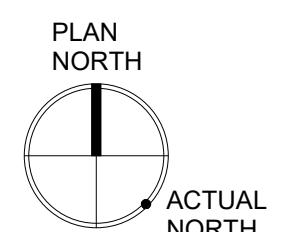


PRINTS OF THIS DRAWING SHALL NOT BE USED FOR ANY PURPOSE WHATSOEVER WITHOUT THE SEAL AND SIGNATURE OF THE PROFESSIONAL ENGINEER		CONSULTANT Architecture: PF&A DESIGN, P.C. Civil Engineering: LABELLA ASSOCIATES Fire Protection: STANTON ENGINEERING SERVICES, LLC			ENGINEER OF RECORD MILLER-REMICK LLC PROFESSIONAL ENGINEER ANTHONY DANIEL PACABO, II Lic. No. 402055079 PROFESSIONAL ENGINEER A Service-Disabled Veteran-Owned Small Business (856) 429-4000 • Miller-Remick.com 4000 DOWNTOWN BLVD., SUITE 200 NEWTON, NJ 07854		Drawing Title PLUMBING NEW WORK PLAN 1ST FLOOR, PHASE 1 Approved by: Jon Manninen, COR		Phase BID DOCUMENTS FULLY SPRINKLERED		Project Title RENOVATE SURGICAL SUITE PHASE II Project Number 658-19-103 Location SALEM VA MEDICAL CENTER Issue Date 2025-12-30 Checked GM Drawn SP			VA Drawing Number 2617 Building Number 143 Drawing Number P1-P-112	
Revisions:		Date:													

GENERAL SHEET NOTES:

1. REFER TO DRAWING P-001 FOR PLUMBING ABBREVIATIONS, GENERAL NOTES & SYMBOLS.
2. REFER TO DRAWING SERIES P-500 FOR PLUMBING DETAILS
3. REFER TO DRAWING SERIES P-600 FOR PLUMBING RISER DIAGRAMS
4. REFER TO DRAWING P-701 FOR PLUMBING SCHEDULES

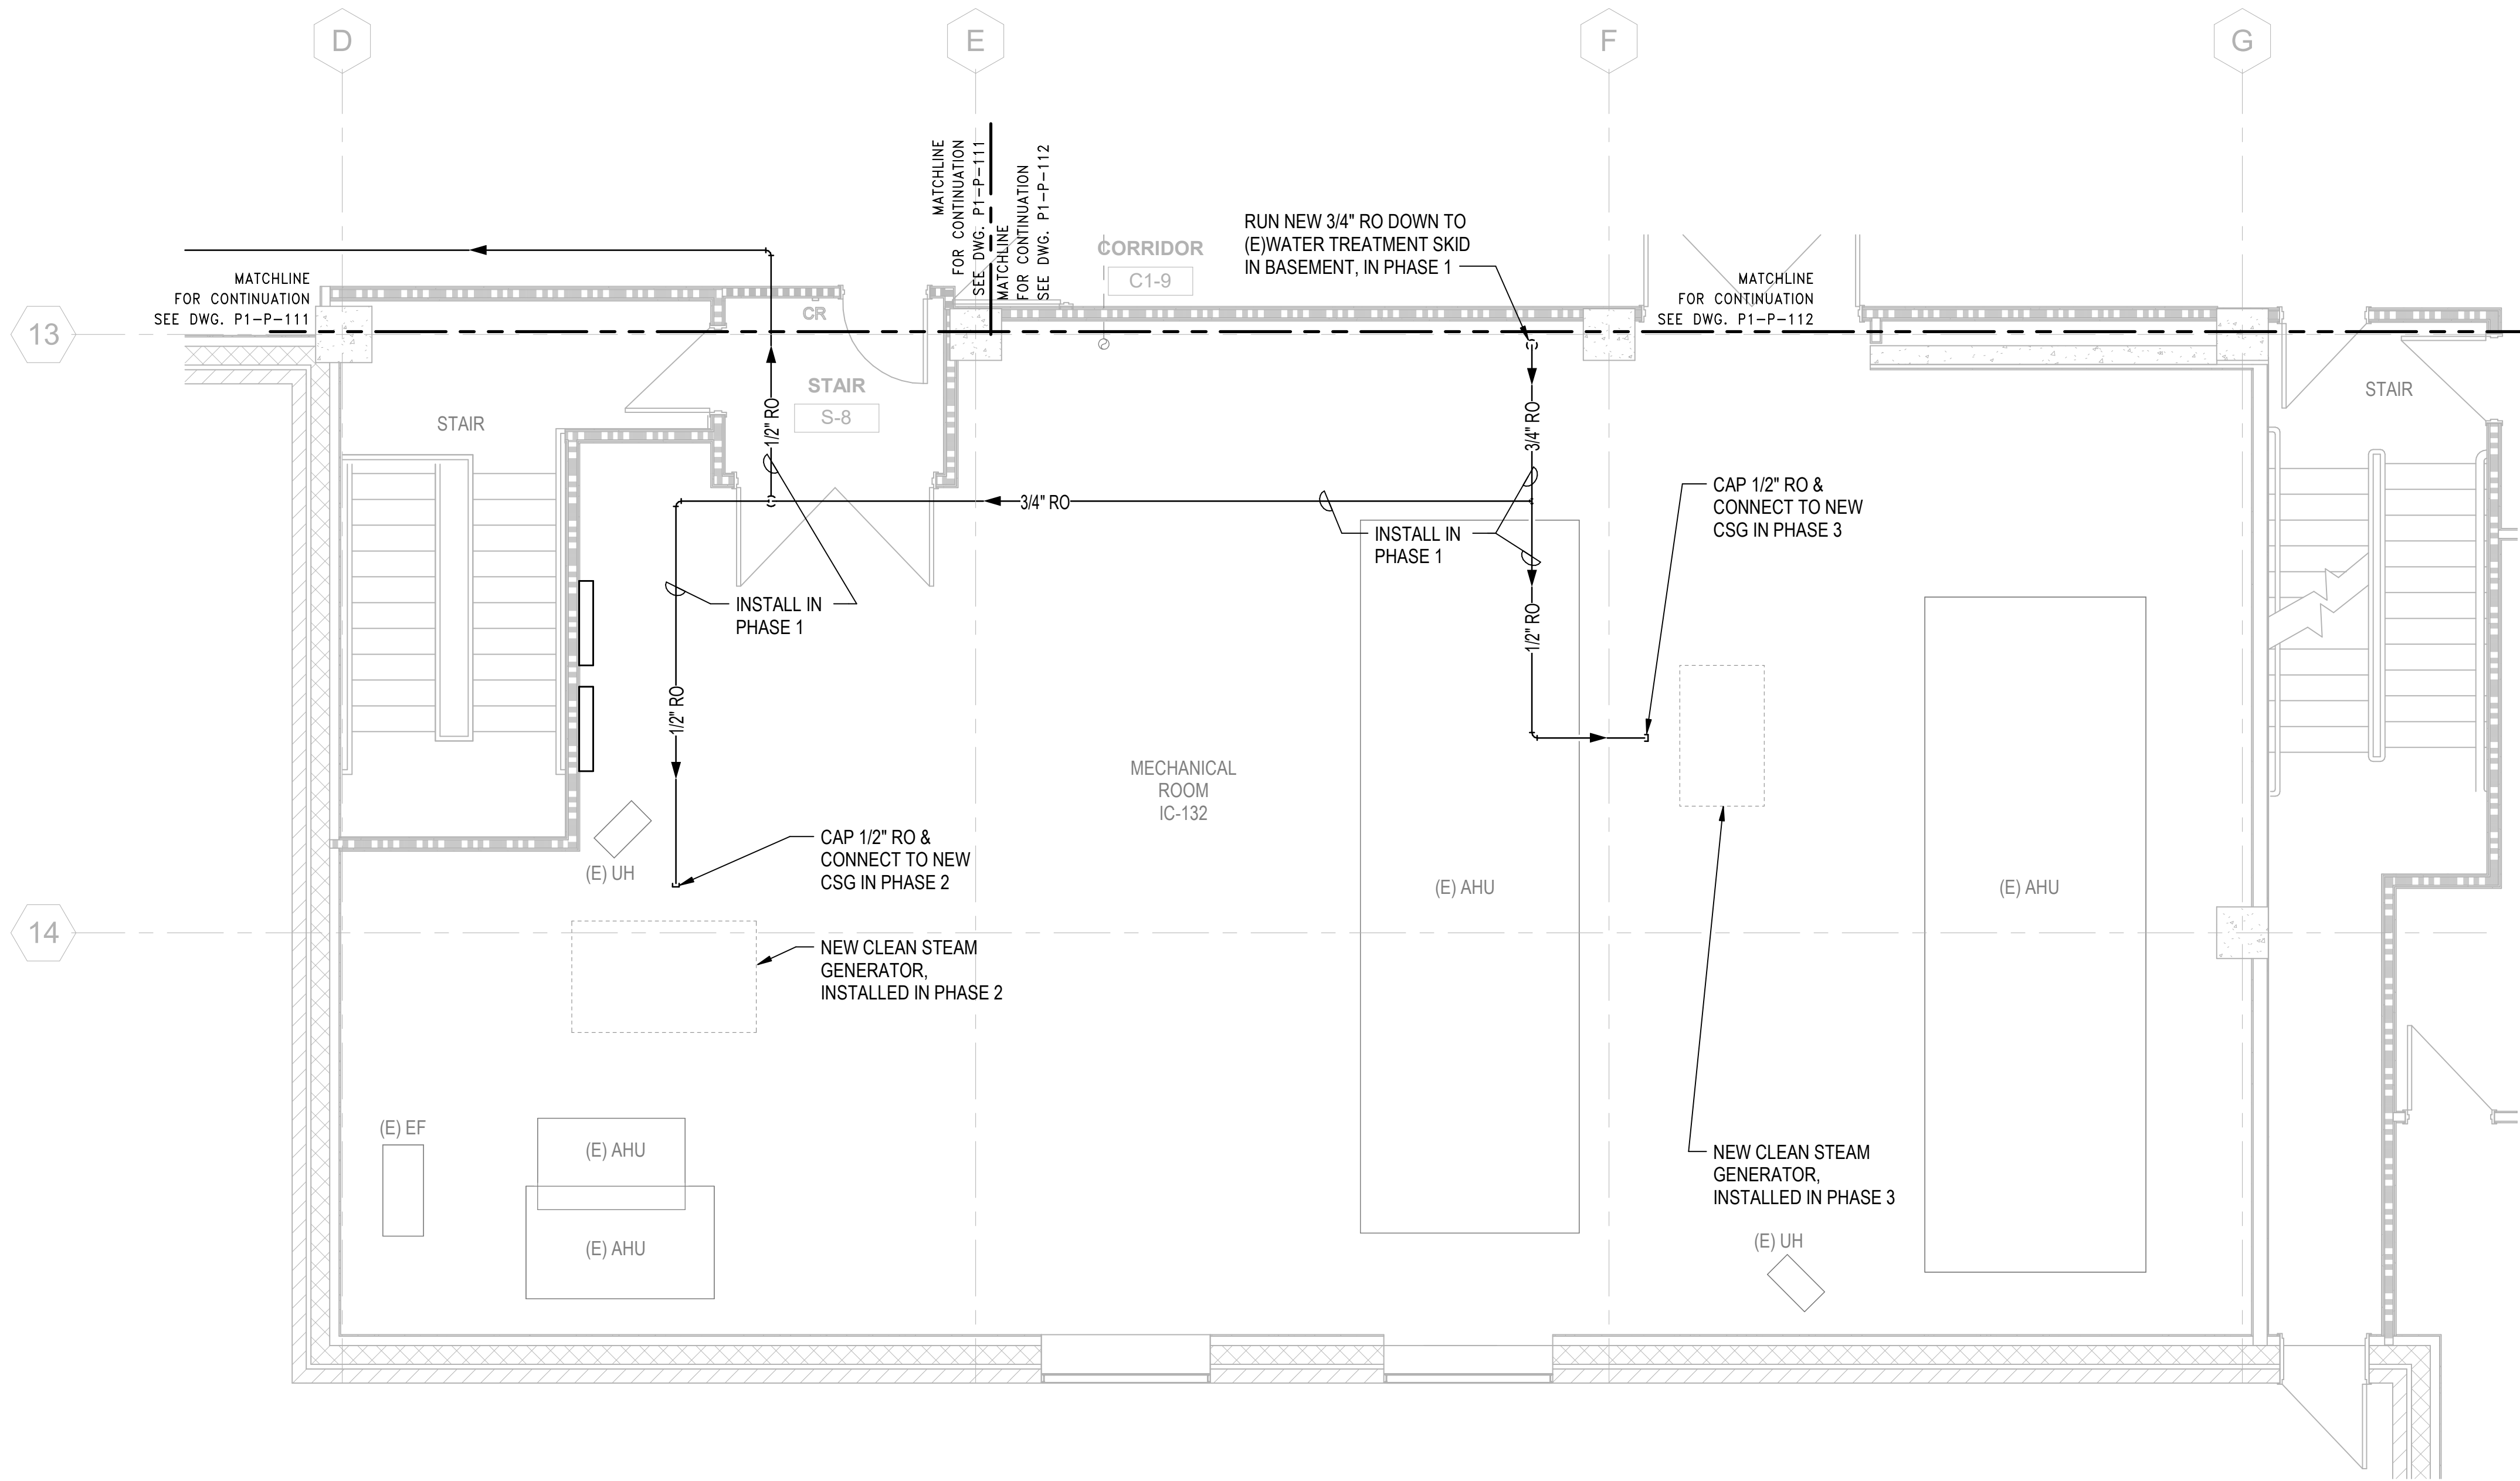


1 FLOOR PLAN - MECHANICAL ROOM
SCALE: 1/4" = 1'-0"

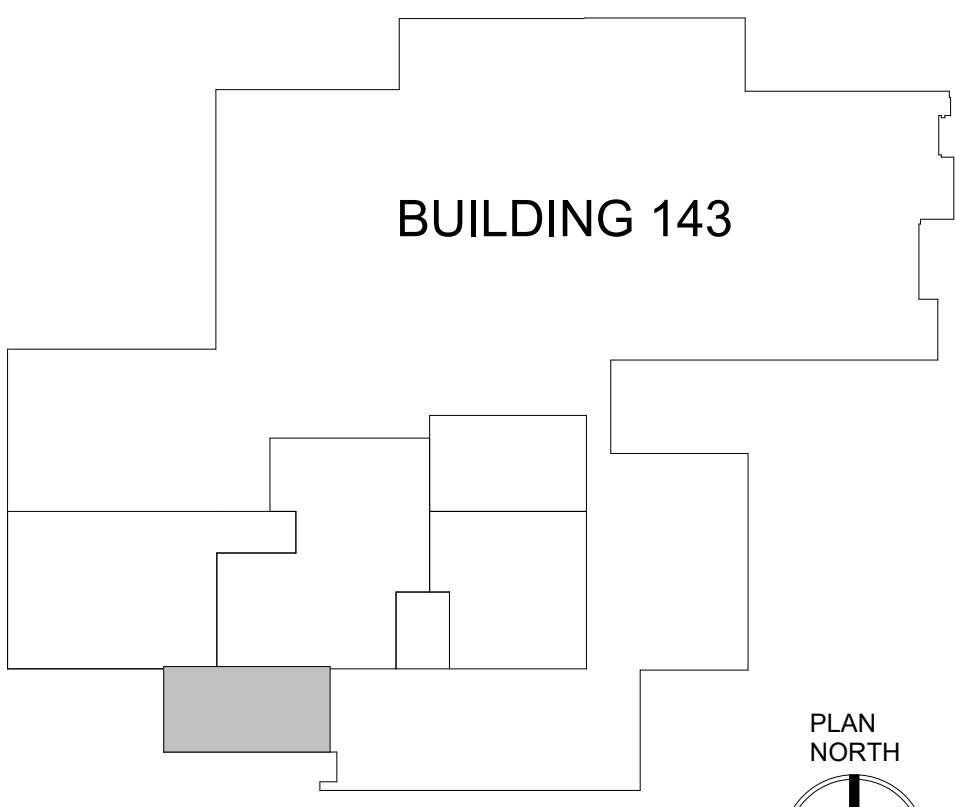



PRINTS OF THIS DRAWING SHALL NOT BE USED FOR ANY PURPOSE WHATSOEVER WITHOUT THE SEAL AND SIGNATURE OF THE PROFESSIONAL ENGINEER		CONSULTANT			ENGINEER OF RECORD		Drawing Title		Phase		Project Title		VA Drawing Number	
		Architecture:	Civil Engineering:	Fire Protection:			PLUMBING		BID DOCUMENTS		RENOVATE SURGICAL SUITE		2617	
		PF&A DESIGN, P.C.	LABELLA ASSOCIATES	STANTON ENGINEERING SERVICES, LLC			NEW WORK PLAN				PHASE II		Building Number	
							MECHANICAL ROOM, PHASE 1		FULLY SPRINKLERED		Project Number 658-19-103		143	
							Approved by:				Location		Drawing Number	
							Jon Manninen, COR				SALEM VA MEDICAL CENTER		P1-P-113	
											Issue Date	Checked	Drawn	
											2025-12-30	CS	SP	

1. REFER TO DRAWING P-001 FOR PLUMBING ABBREVIATIONS, GENERAL NOTES & SYMBOLS.
2. REFER TO DRAWING SERIES P-500 FOR PLUMBING DETAILS
3. REFER TO DRAWING SERIES P-600 FOR PLUMBING RISER DIAGRAMS
4. REFER TO DRAWING P-701 FOR PLUMBING SCHEDULES
5. SANITARY PIPING SHOWN ON THIS PLAN IS BELOW FLOOR.

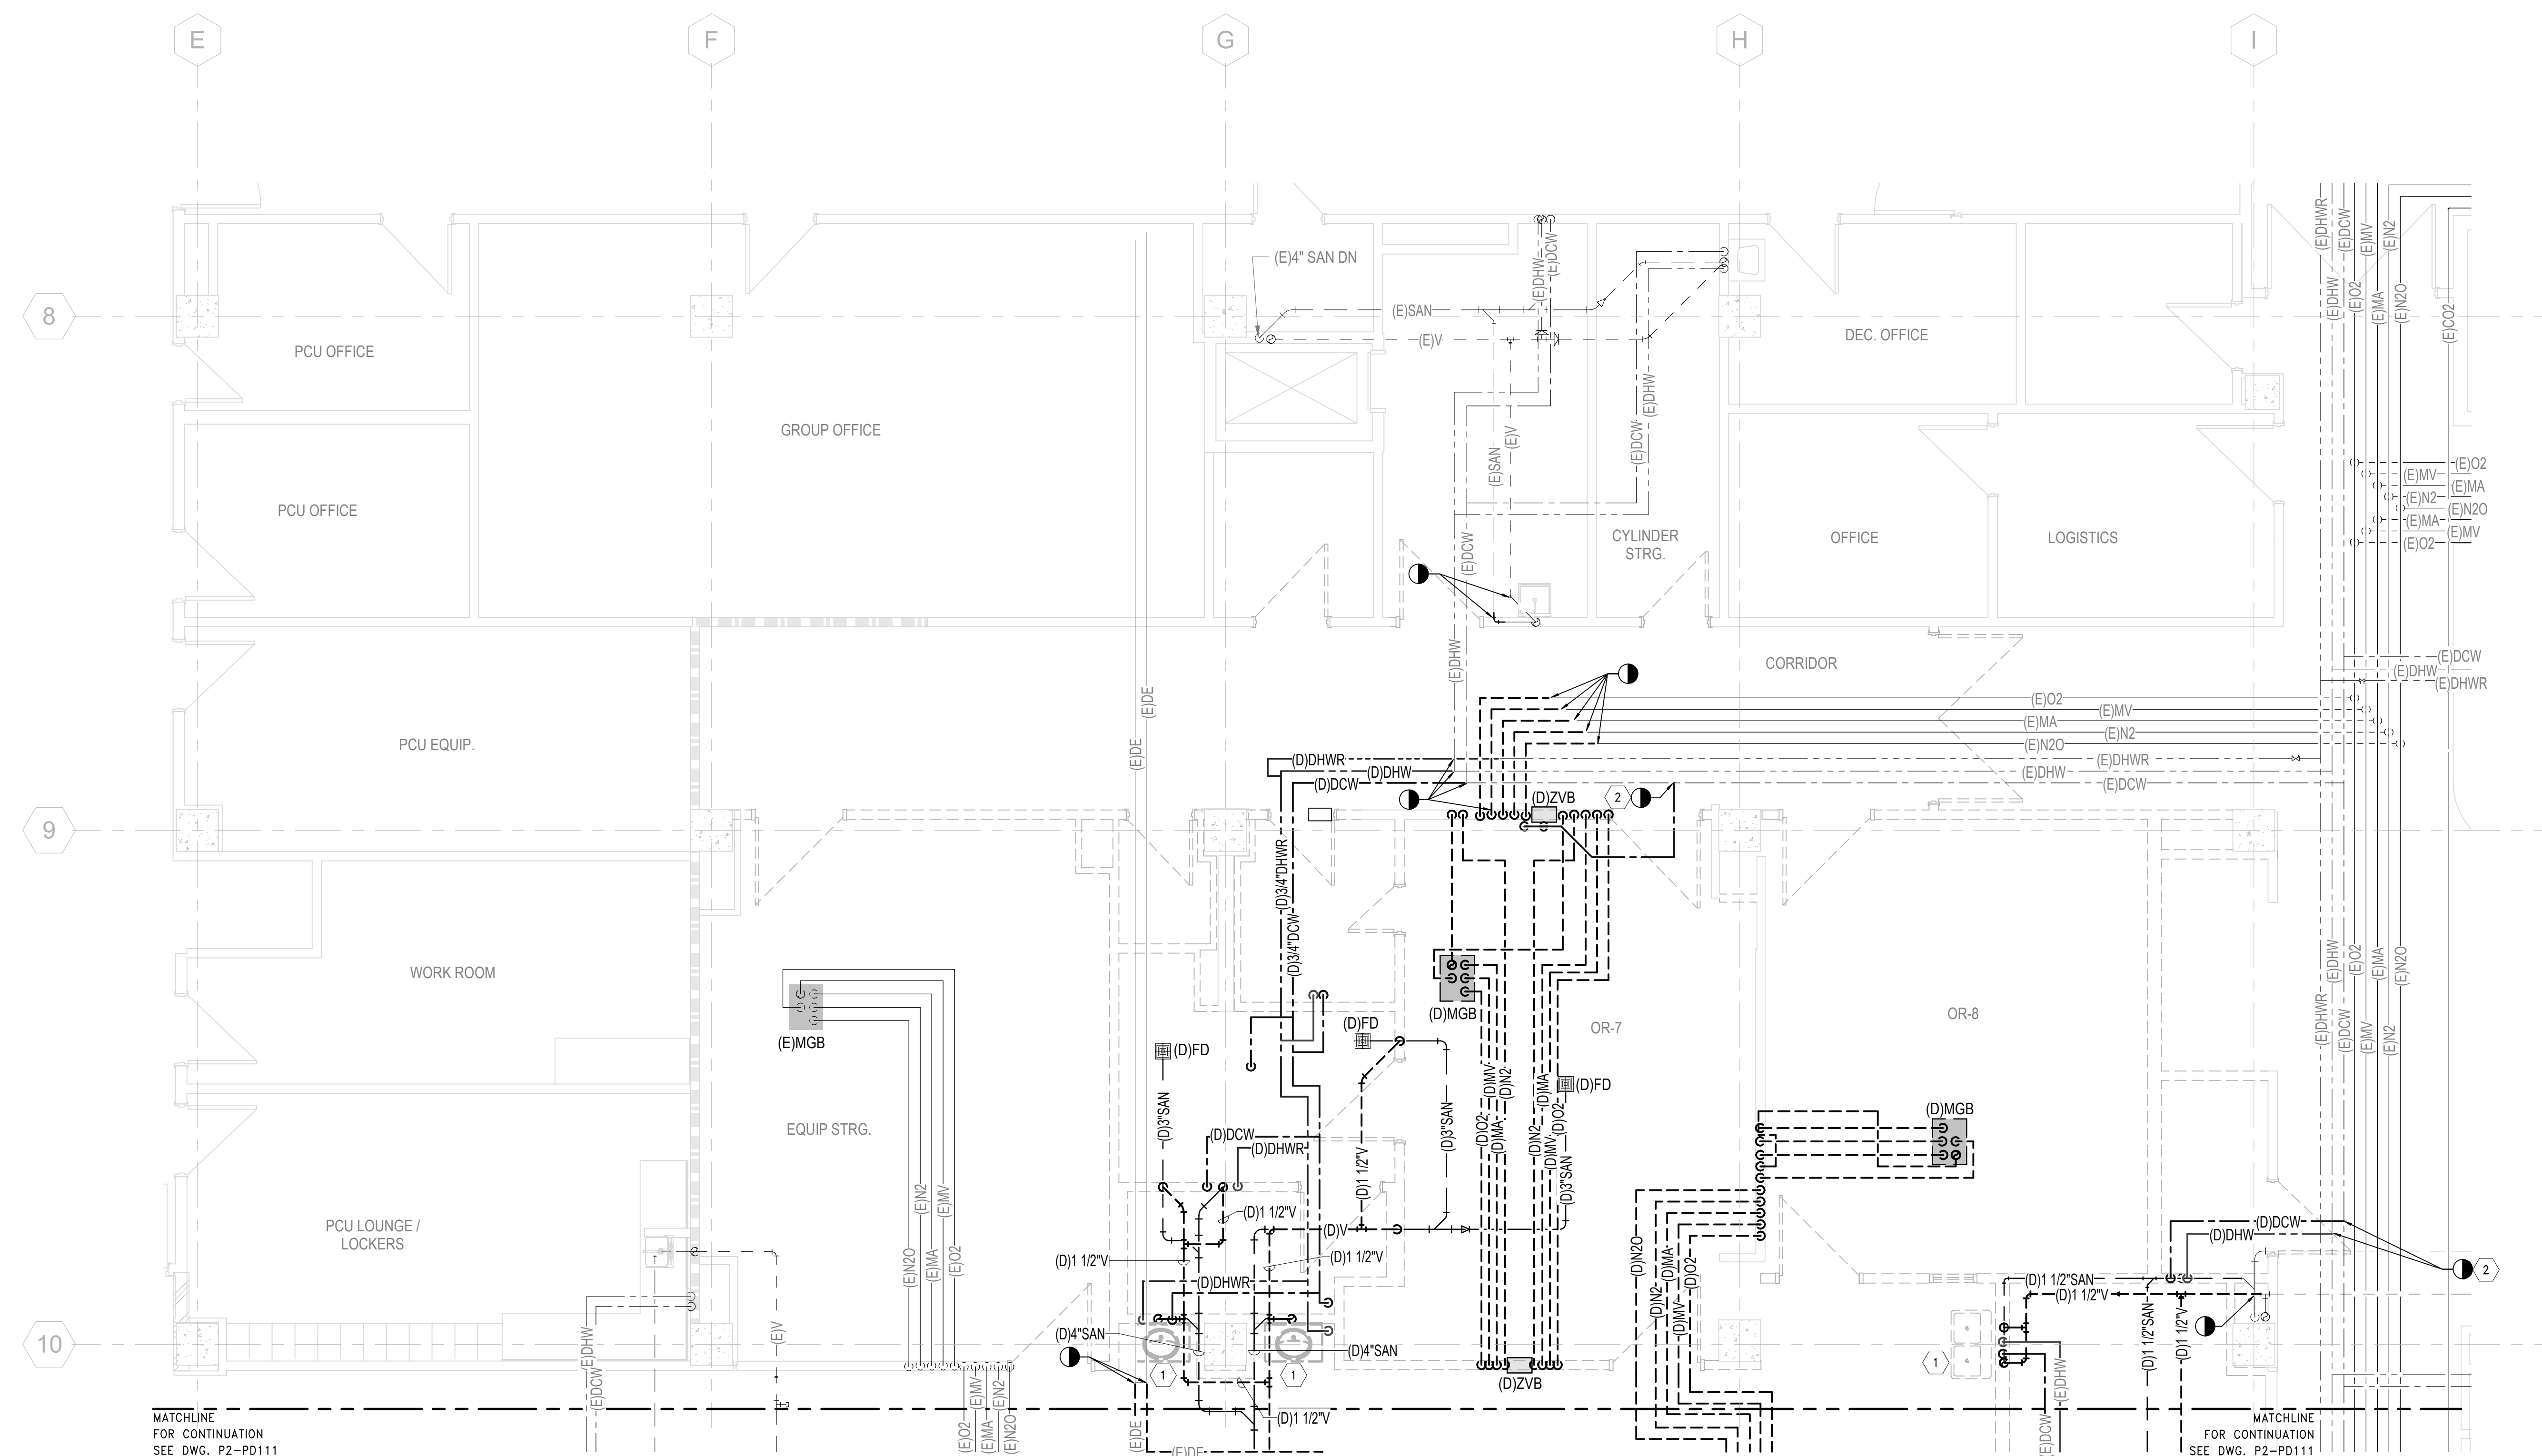

1 PLUMBING DEMOLITION PLAN - 1ST FLOOR, PHASE 2 (NORTH)
SCALE: 1/4" = 1'-0"

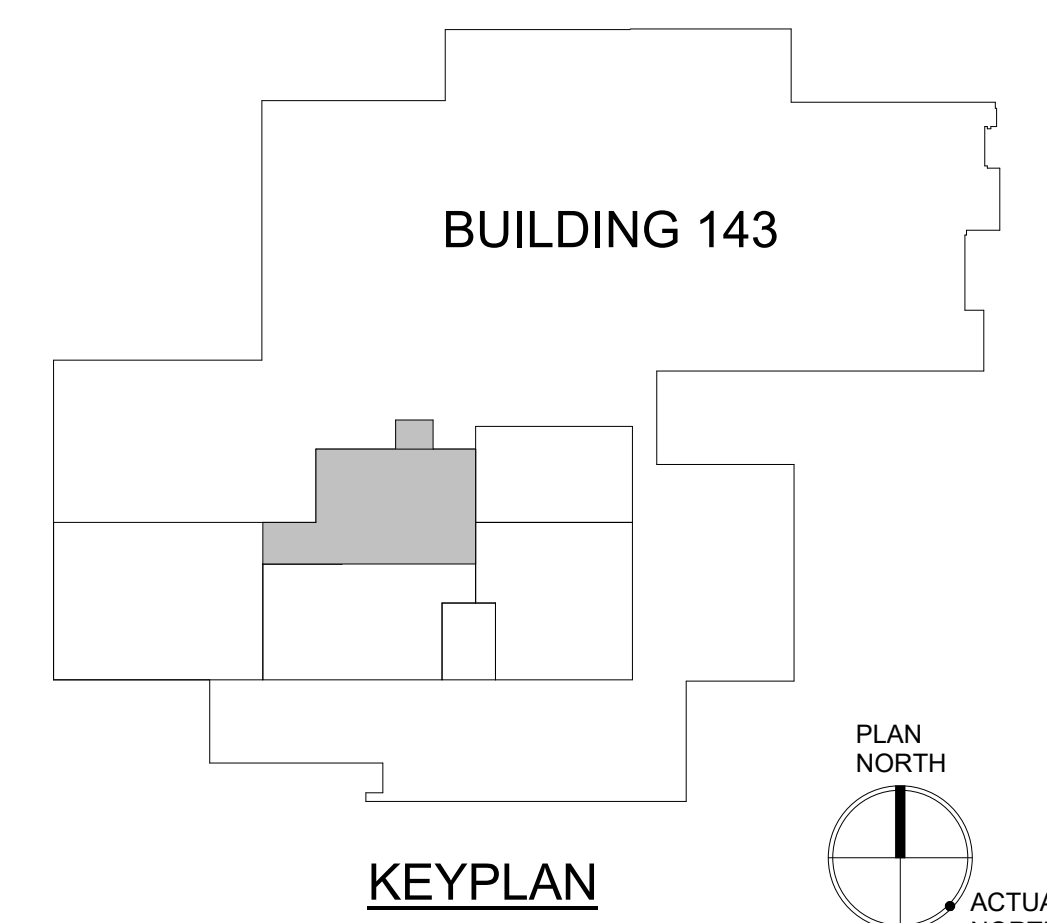


 PRINTS OF THIS DRAWING SHALL NOT BE USED FOR ANY PURPOSE WHATSOEVER WITHOUT THE SEAL AND SIGNATURE OF THE PROFESSIONAL ENGINEER		CONSULTANT			ENGINEER OF RECORD		MILLER-REMIK LLC PROFESSIONAL ENGINEER		Office of Construction and Facilities Management		Drawing Title PLUMBING DEMOLITION PLAN 1ST FLOOR, PHASE 2 (NORTH)		Phase BID DOCUMENTS		Project Title RENOVATE SURGICAL SUITE PHASE II Project Number 658-19-103			VA Drawing Number 2617	
		Architecture: PF&A DESIGN, P.C.		Civil Engineering: LABELLA ASSOCIATES	Fire Protection: STANTON ENGINEERING SERVICES, LLC					 U.S. Department of Veterans Affairs		Approved by: Jon Manninen, COR		FULLY SPRINKLERED		Location SALEM VA MEDICAL CENTER		Building Number 143	
																Drawing Number P2-PD112			
																			
																			
																			
Revisions:																			
Date:																			


1. REFER TO DRAWING P-001 FOR PLUMBING ABBREVIATIONS, GENERAL NOTES & SYMBOLS
2. REFER TO DRAWING SERIES P-500 FOR PLUMBING DETAILS
3. REFER TO DRAWING SERIES P-600 FOR PLUMBING RISER DIAGRAMS
4. REFER TO DRAWING P-701 FOR PLUMBING SCHEDULES
5. SANITARY PIPING SHOWN ON THIS PLAN IS BELOW FLOOR.
6. PROVIDE LOCKABLE HANDLES FOR ALL MEDICAL GAS VALVES LOCATED ABOVE CEILING.
7. ALL DHW/DWC LINES TO FIXTURES TO BE 1/2"Ø UNLESS OTHERWISE NOTED.

⬡ SHEET KEYNOTES:

- 1 ZONE VALVE BOX. PROVIDE THE FOLLOWING MEDICAL GAS LINES TO / FROM ZVB - 1/2" MA, 3/4" MV, 1/2" O2, 1/2" N2O, 1/2" N2, 1/2" CO2 & 3/4" WAGD.

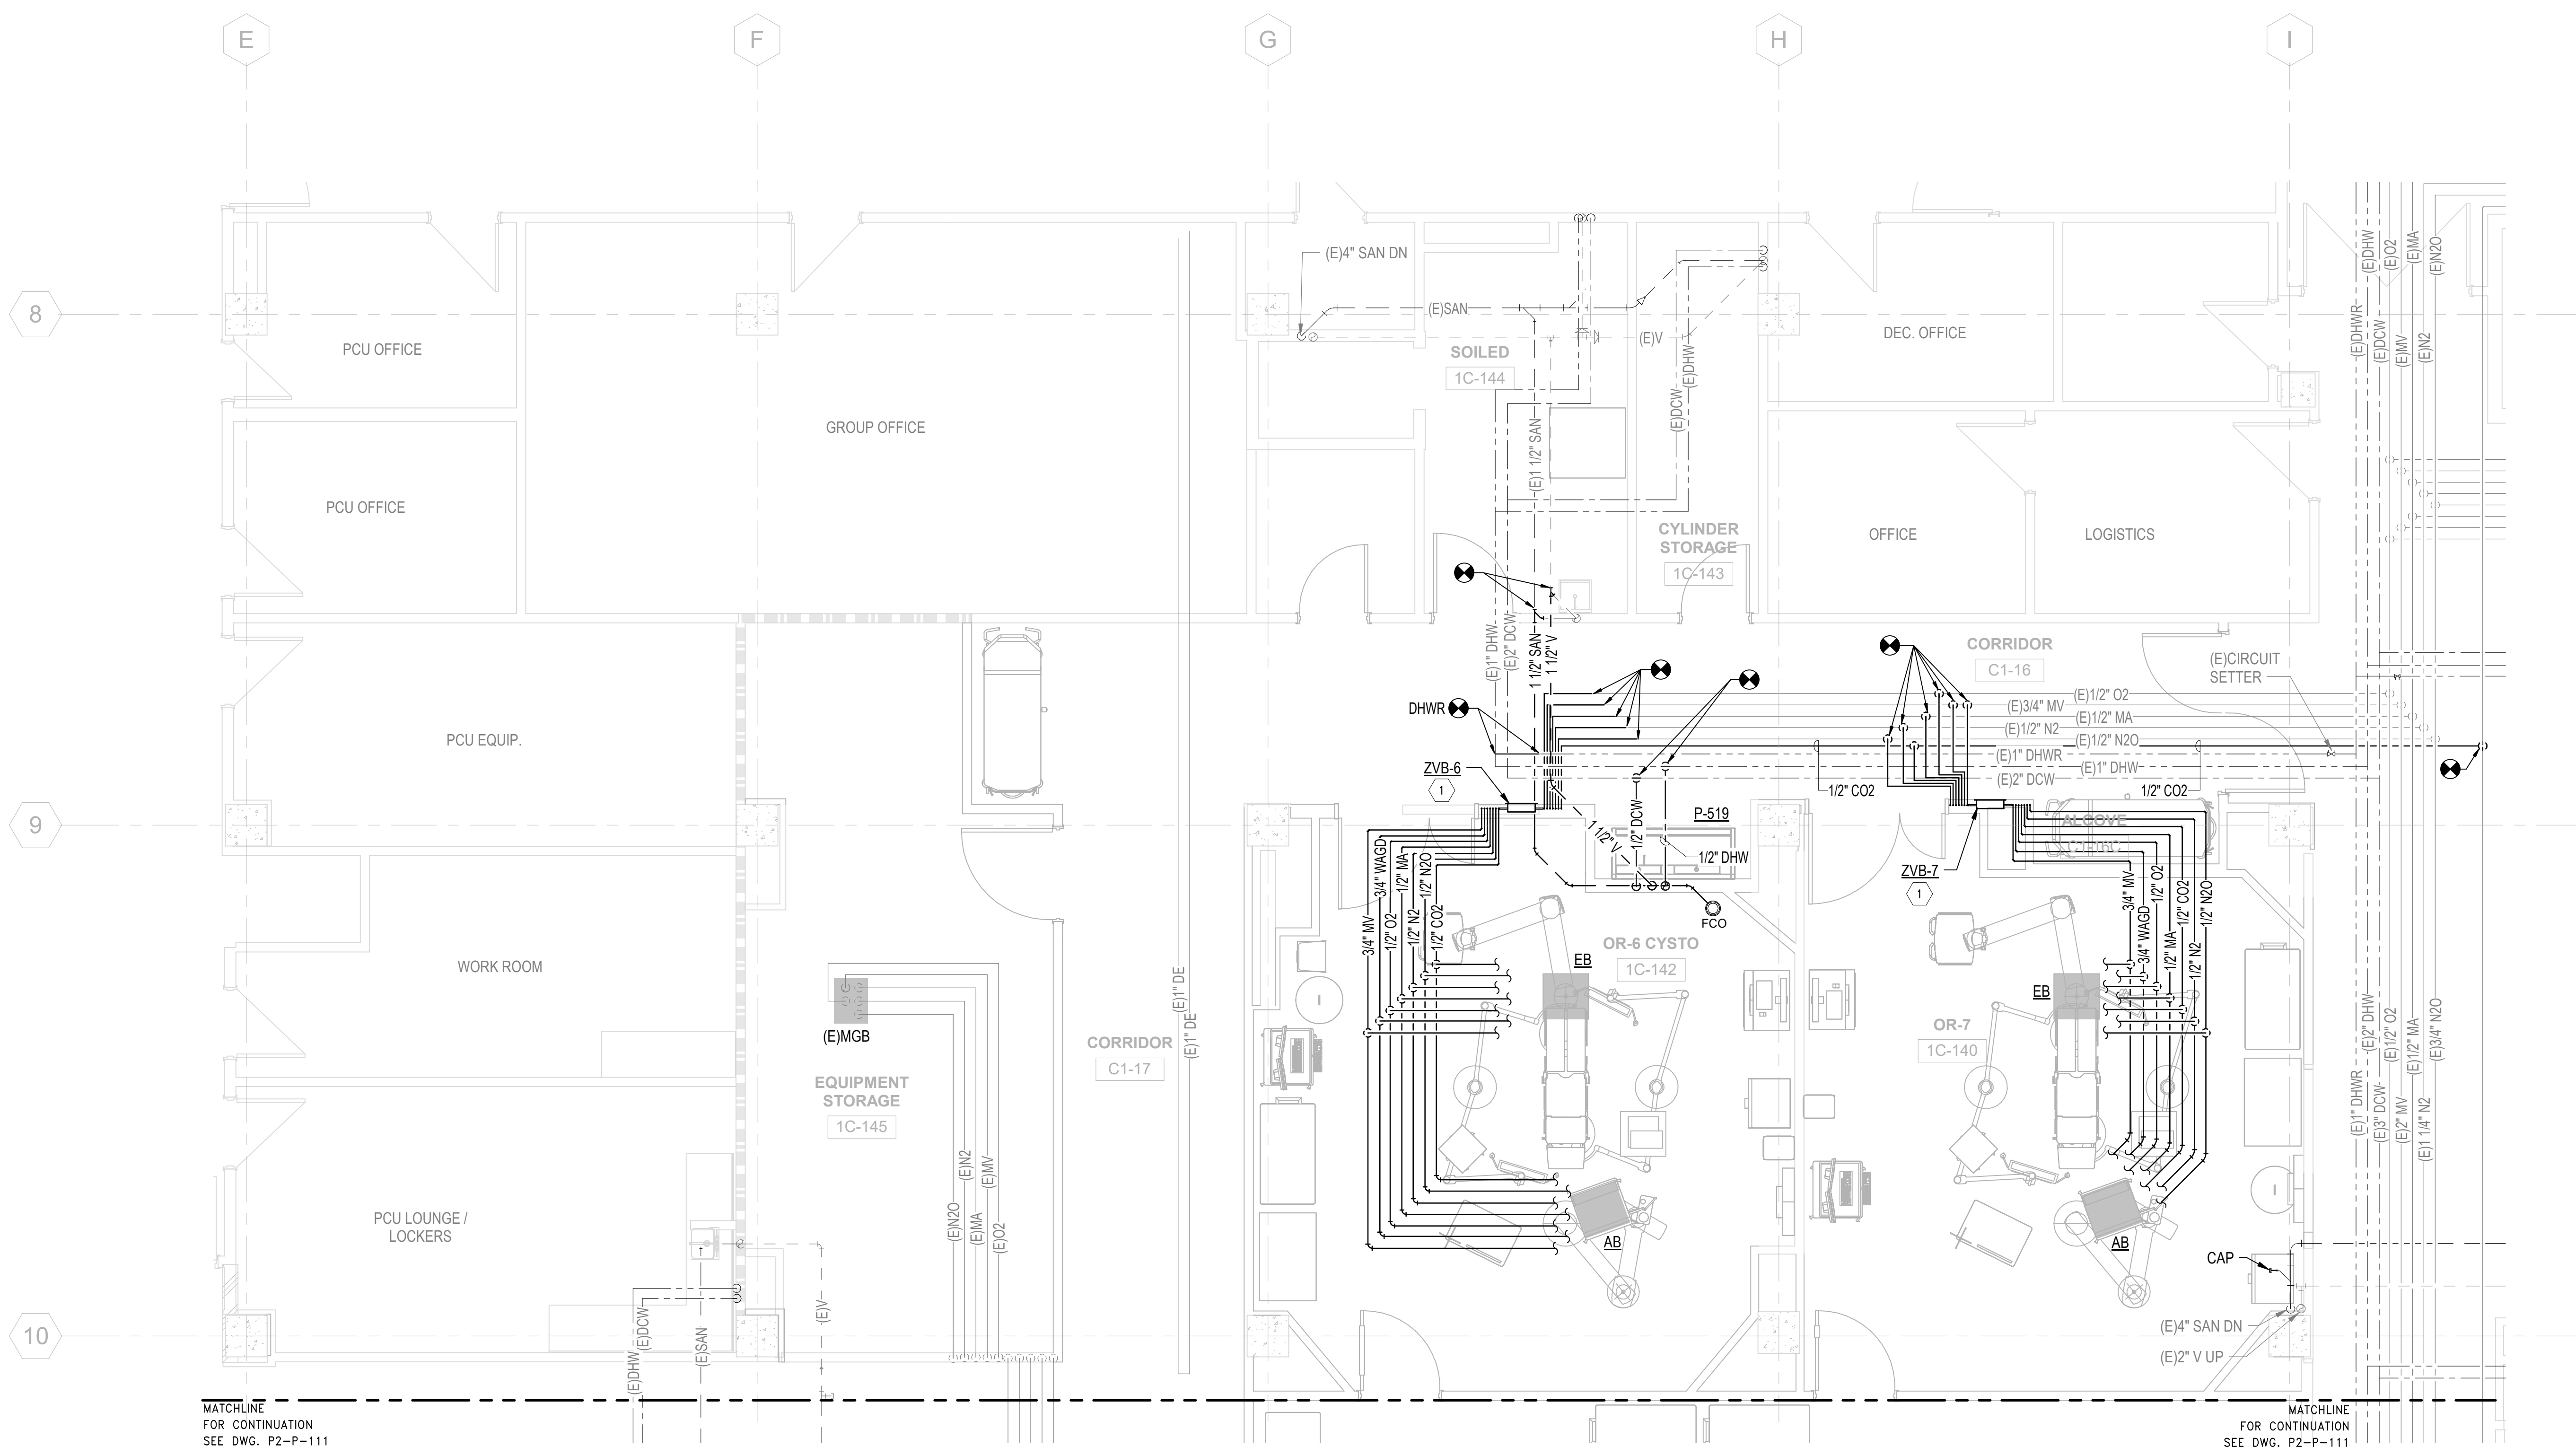

1 PLUMBING PLAN - 1ST FLOOR, PHASE 2 (NORTH)
SCALE: 1/4" = 1'-0"

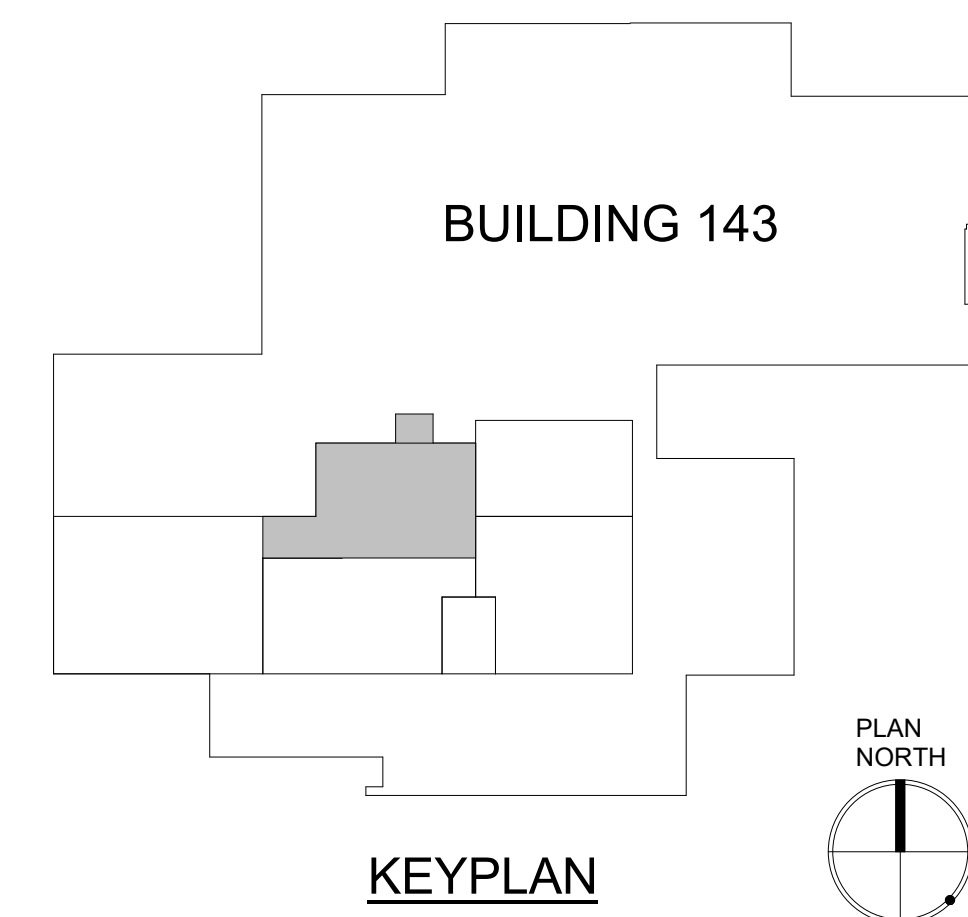[illegible]

GENERAL SHEET NOTES:


1. REFER TO DRAWING P-001 FOR PLUMBING ABBREVIATIONS, GENERAL NOTES & SYMBOLS.
2. REFER TO DRAWING SERIES P-500 FOR PLUMBING DETAILS
3. REFER TO DRAWING SERIES P-600 FOR PLUMBING RISER DIAGRAMS
4. REFER TO DRAWING P-701 FOR PLUMBING SCHEDULES
5. SANITARY PIPING SHOWN ON THIS PLAN IS BELOW FLOOR.

SHEET KEYNOTES:

- 1 DEMOLISH EXISTING PLUMBING FIXTURES AND ASSOCIATED PIPING.
- 2 REMOVE DEAD LEGS FROM HOT AND COLD WATER PIPES AND INSTALL SPOOL PIECE. WHERE IT IS NOT POSSIBLE, LIMIT DEAD LEG TO 1.5 x PIPE DIAMETER.

1 DEMOLITION PLAN - 1ST FLOOR, PHASE 3 (NORTH)
SCALE: 1/4" = 1'-0"

2 DEMOLITION PLAN - 1ST FLOOR, PHASE 3 (SOUTH)
SCALE: 1/4" = 1'-0"

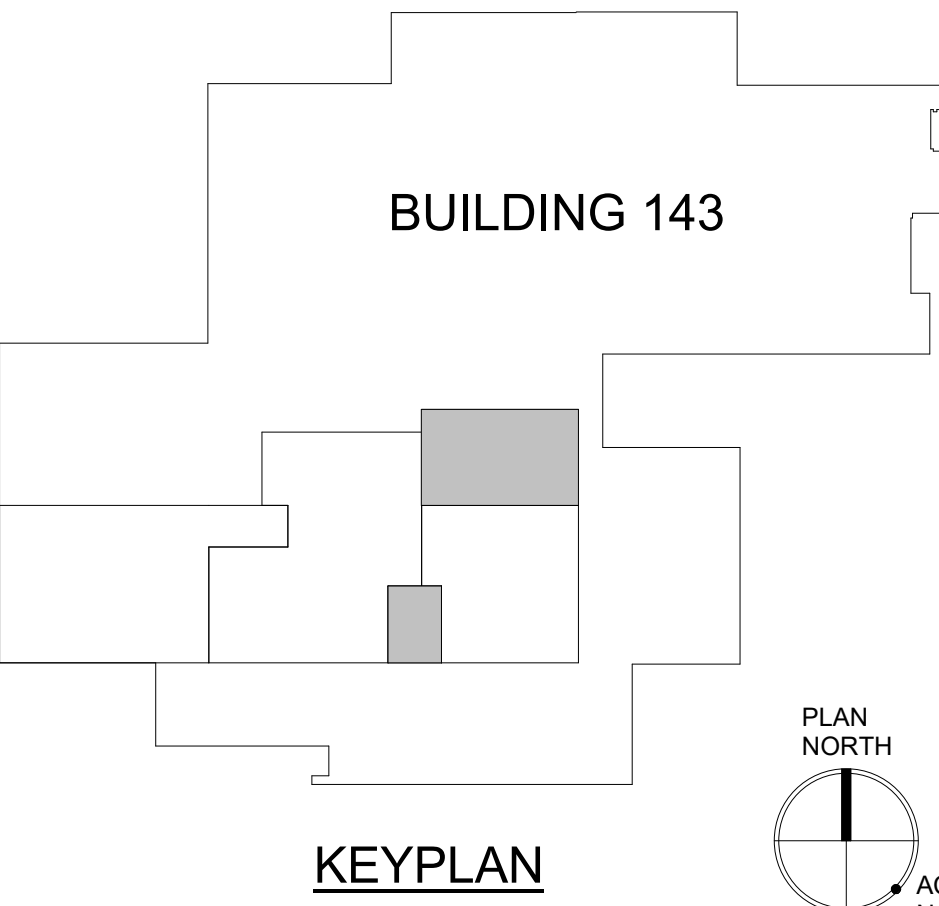

PRINTS OF THIS DRAWING SHALL NOT BE USED FOR ANY PURPOSE WHATSOEVER WITHOUT THE SEAL AND SIGNATURE OF THE PROFESSIONAL ENGINEER		CONSULTANT		ENGINEER OF RECORD		Office of Construction and Facilities Management		Drawing Title PLUMBING DEMOLITION PLAN 1ST FLOOR, PHASE 3		Phase BID DOCUMENTS		Project Title RENOVATE SURGICAL SUITE PHASE II		VA Drawing Number 2617	
Architecture: PF&A DESIGN, P.C.		Civil Engineering: LABELLA ASSOCIATES		Fire Protection: STANTON ENGINEERING SERVICES, LLC		Miller-Remick LLC PROFESSIONAL ENGINEER		Approved by: Jon Manninen, COR		FULLY SPRINKLERED		Project Number 658-19-103		Building Number 143	
Revisions:		Date:				Commonwealth of Virginia Professional Engineer Seal Anthony Daniel Pacardo Jr. Lic. No. 402055076						Location SALEM VA MEDICAL CENTER		Drawing Number P3-PD111	
Issue Date 2025-12-30		Checked GM		Drawn SP											

GENERAL SHEET NOTES:


1. REFER TO DRAWING P-001 FOR PLUMBING ABBREVIATIONS, GENERAL NOTES & SYMBOLS.
2. REFER TO DRAWING SERIES P-500 FOR PLUMBING DETAILS
3. REFER TO DRAWING SERIES P-600 FOR PLUMBING RISER DIAGRAMS
4. REFER TO DRAWING P-701 FOR PLUMBING SCHEDULES
5. SANITARY PIPING SHOWN ON THIS PLAN IS BELOW FLOOR.
6. PROVIDE LOCKABLE HANDLES FOR ALL MEDICAL GAS VALVES LOCATED ABOVE CEILING.
7. ALL DHW/DCW LINES TO FIXTURES TO BE 1/2"Ø UNLESS OTHERWISE NOTED.

SHEET KEYNOTES:

1. MEDICAL GAS HEADWALL. PROVIDE THE FOLLOWING MEDICAL GAS LINES FOR EACH PATIENT BED - 3/4" MV, 1/2" MA & 1/2" O2. REFER TO DETAIL 3 / P-501.
2. ZONE VALVE BOX. PROVIDE THE FOLLOWING MEDICAL GAS LINES TO / FROM ZVB - 3/4" MV, 1/2" MA & 1/2" O2.


1 PLUMBING PLAN - 1ST FLOOR, PHASE 4

SCALE: 1/4" = 1'-0"

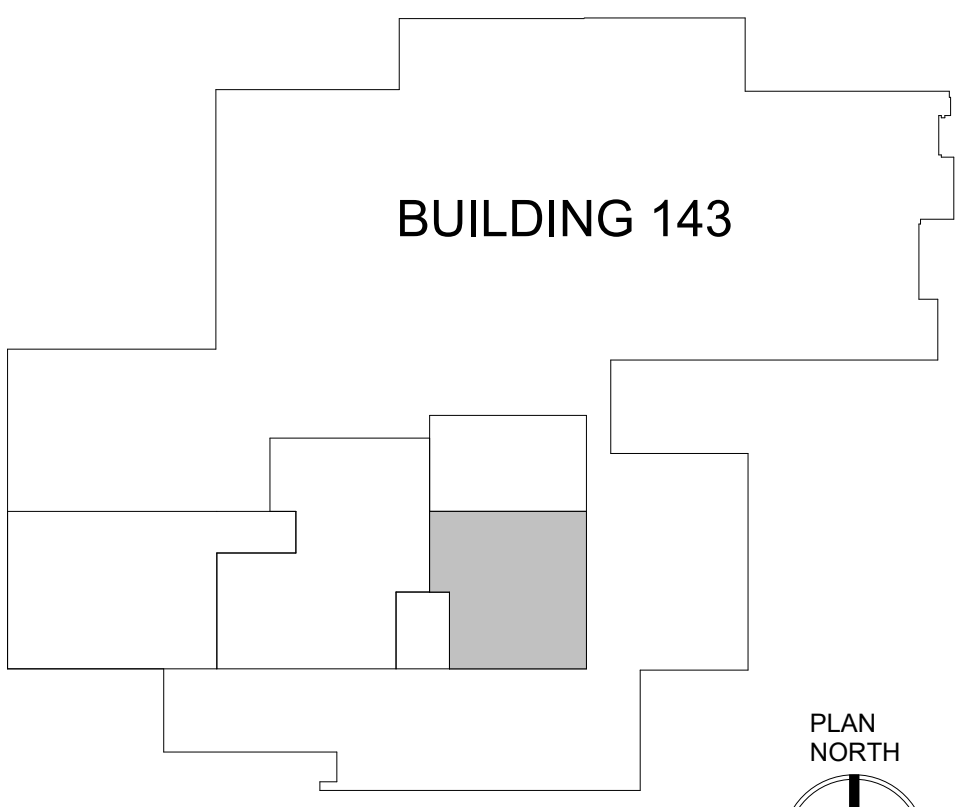


KEYPLAN


PRINTS OF THIS DRAWING SHALL NOT BE USED FOR ANY PURPOSE WHATSOEVER WITHOUT THE SEAL AND SIGNATURE OF THE PROFESSIONAL ENGINEER			CONSULTANT			ENGINEER OF RECORD			Drawing Title PLUMBING NEW WORK PLAN 1ST FLOOR, PHASE 4			Phase BID DOCUMENTS			Project Title RENOVATE SURGICAL SUITE PHASE II Project Number 658-19-103			VA Drawing Number 2617 Building Number 143		
Revisions:			Architecture: PF&A DESIGN, P.C.			Civil Engineering: LABELLA ASSOCIATES			Approved by: Jon Manninen, COR			FULLY SPRINKLERED			Location SALEM VA MEDICAL CENTER			Drawing Number P4-P-111		
Date:			Fire Protection: STANTON ENGINEERING SERVICES, LLC			MILLER-REMICK LLC PROFESSIONAL ENGINEER			Office of Construction and Facilities Management						Issue Date 2025-12-30			Checked GM		
12/29/2025 10:52:24 AM						MILLER-REMICK A Service-Disabled Veteran-Owned Small Business (856) 429-4000 • Miller-Remick.com			U.S. Department of Veterans Affairs						Drawn SP					

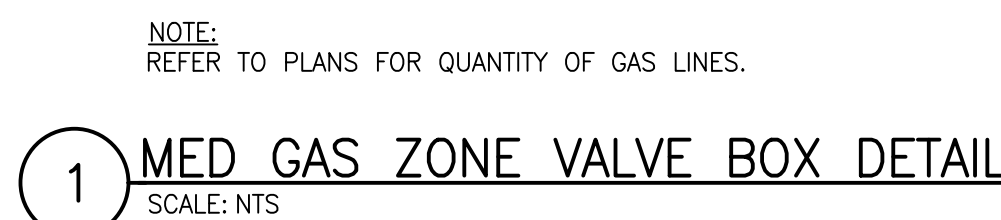

VA Drawing Number
2617
Building Number
143
Drawing Number
P-501

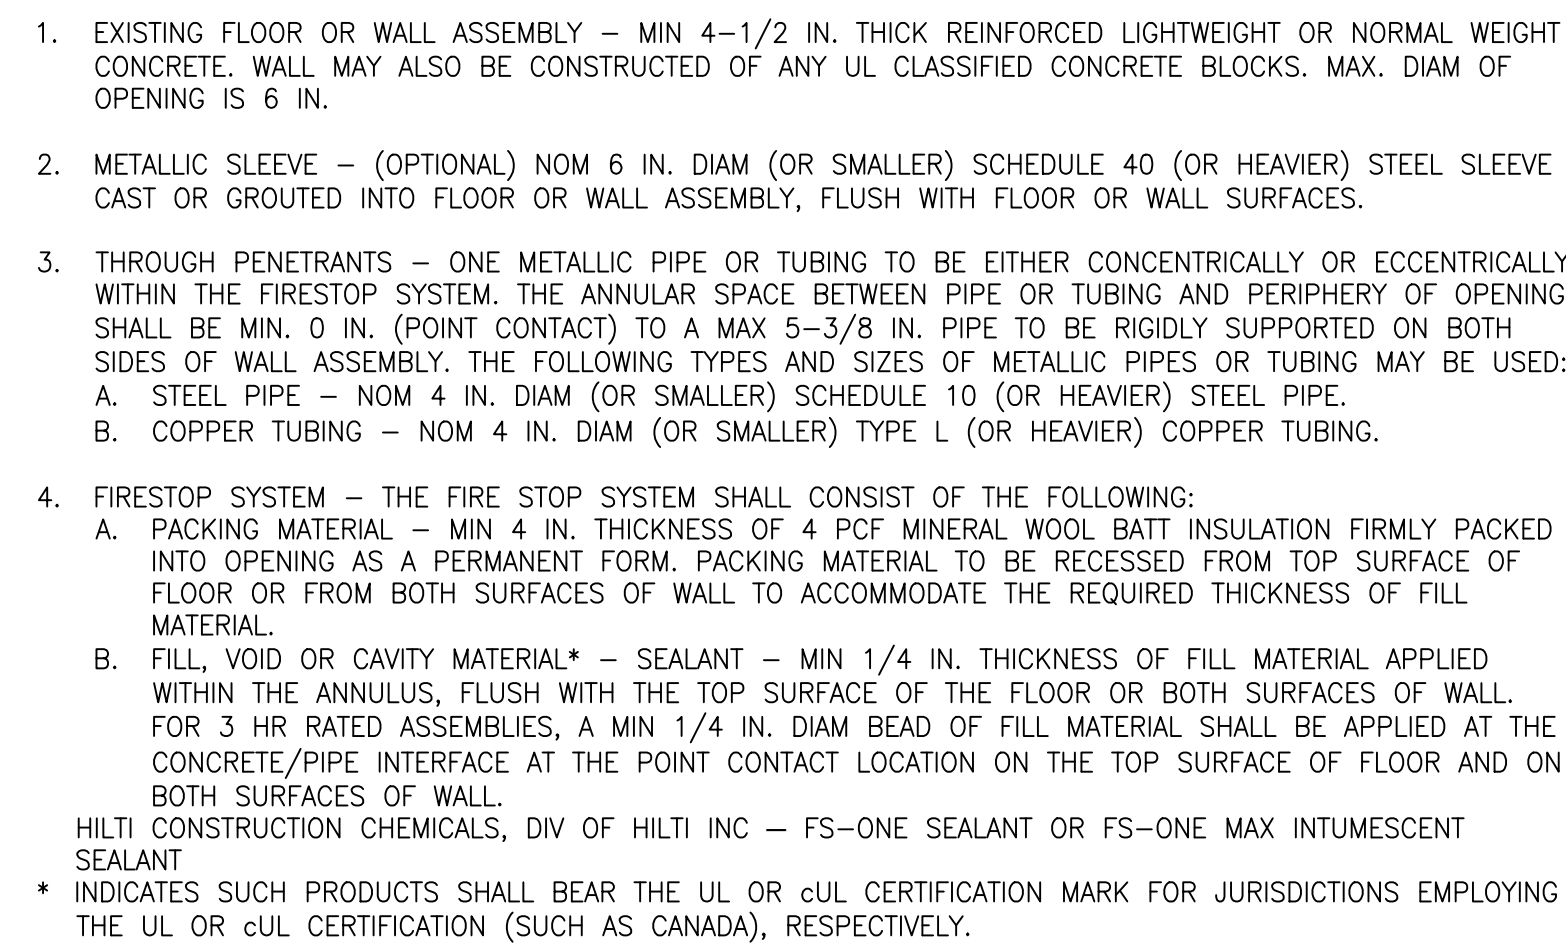

2 TYPICAL CONCRETE OR MASONRY
PIPE PENETRATION
SCALE: NTS

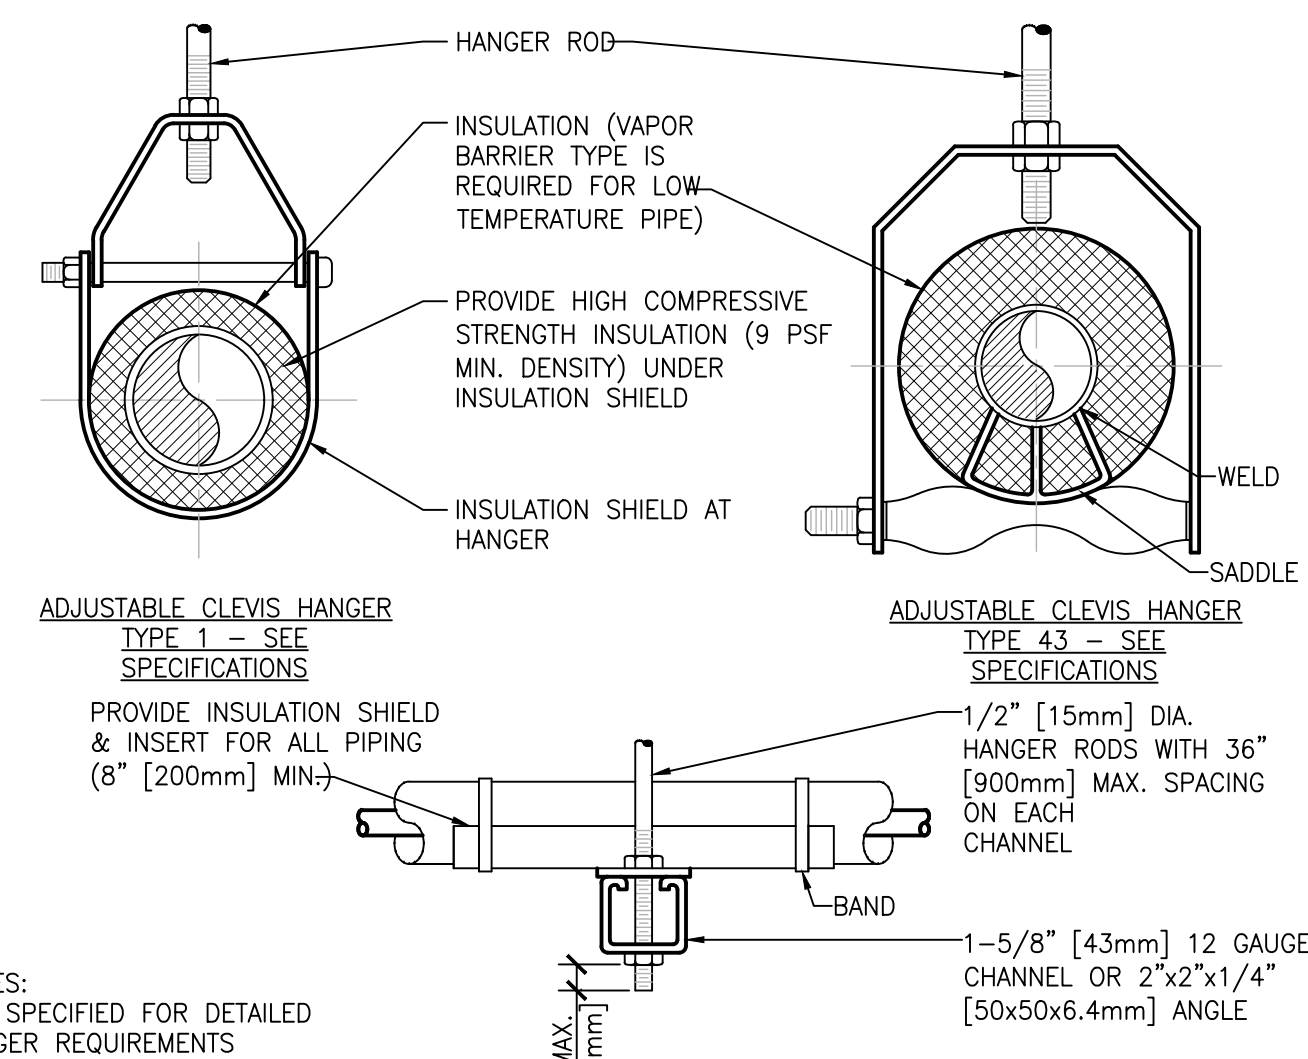

SIDE VIEW TRAPEZE HANGER FOR UP TO
1000 LB. [453KG] UNIFORM LOAD

MAXIMUM PIPE/TUBING SUPPORT SPACING														
NOM. SIZE	IN. [mm]	THRU [20]	3/4 [25]	1 [25]	1 1/4 [30]	1 1/2 [40]	2 [50]	2 1/2 [63]	3 [75]	4 [100]	5 [125]	6 [150]	8 [200]	10 [250]
PIPE	ft. [mm]	[2100]	2100	2100	2100	2700	3000	3400	3700	4100	4900	5200	5800	6700
TUBING	ft. [mm]	5 FT [1500]	6	7	8	8	9	8	9	10	12	13	14	16
		[1500]	[1800]	[2100]	[2400]	[2400]	[2700]	[3000]	[3700]	[4000]	[4100]	[4900]		-
NOTE: FOR TRAPEZE HANGER TAIL SPACING OF SMALLEST SIZE ON TRAPEZE.														

4 PIPE HANGER DETAIL
SCALE: NTS

PRINTS OF THIS DRAWING SHALL NOT BE USED FOR ANY PURPOSE WHATSOEVER WITHOUT THE SEAL AND SIGNATURE OF THE PROFESSIONAL ENGINEER.		
CONSULTANTS		
Architecture: PF&A DESIGN, P.C.	Civil Engineering: LABELLA ASSOCIATES	Fire & Life Safety: STANTON ENGINEERING SERVICES, LLC
NO.	DESCRIPTION	DATE



A Service-Disabled Veteran-Owned Small Business
(856) 429-4000 • Miller-Remick.com

ENGINEER OF RECORD



 ANTHONY JAMES FALCATO, P.E.
 License No. 40205507
 PROFESSIONAL ENGINEER

Office of Construction and Facilities Management

 U.S. Department of Veterans Affairs

Drawing Title	Phase	Project Title	VA Drawing Number
PLUMBING DETAILS	BID DOCUMENTS	RENOVATE SURGICAL SUITE PHASE II	2617
		Project Number 658-19-103	Building Number 143
Approved by: Jon Manninen, COR	Location	Drawing Number	
	FULLY SPRINKLERED	SALEM VA MEDICAL CENTER	P-502
		Issue Date: 2025-12-30	
		Checked: BH	
		Drawn: pd	

- GENERAL SHEET NOTES:
1. REFER TO DRAWING P-001 FOR PLUMBING ABBREVIATIONS, GENERAL NOTES & SYMBOLS.
 2. REFER TO DRAWING SERIES P-500 FOR PLUMBING DETAILS
 3. REFER TO DRAWING SERIES P-600 FOR PLUMBING RISER DIAGRAMS
 4. REFER TO DRAWING P-701 FOR PLUMBING SCHEDULES
 5. ALL DHW/DCW LINES TO FIXTURES TO BE 1/2"Ø UNLESS OTHERWISE NOTED.

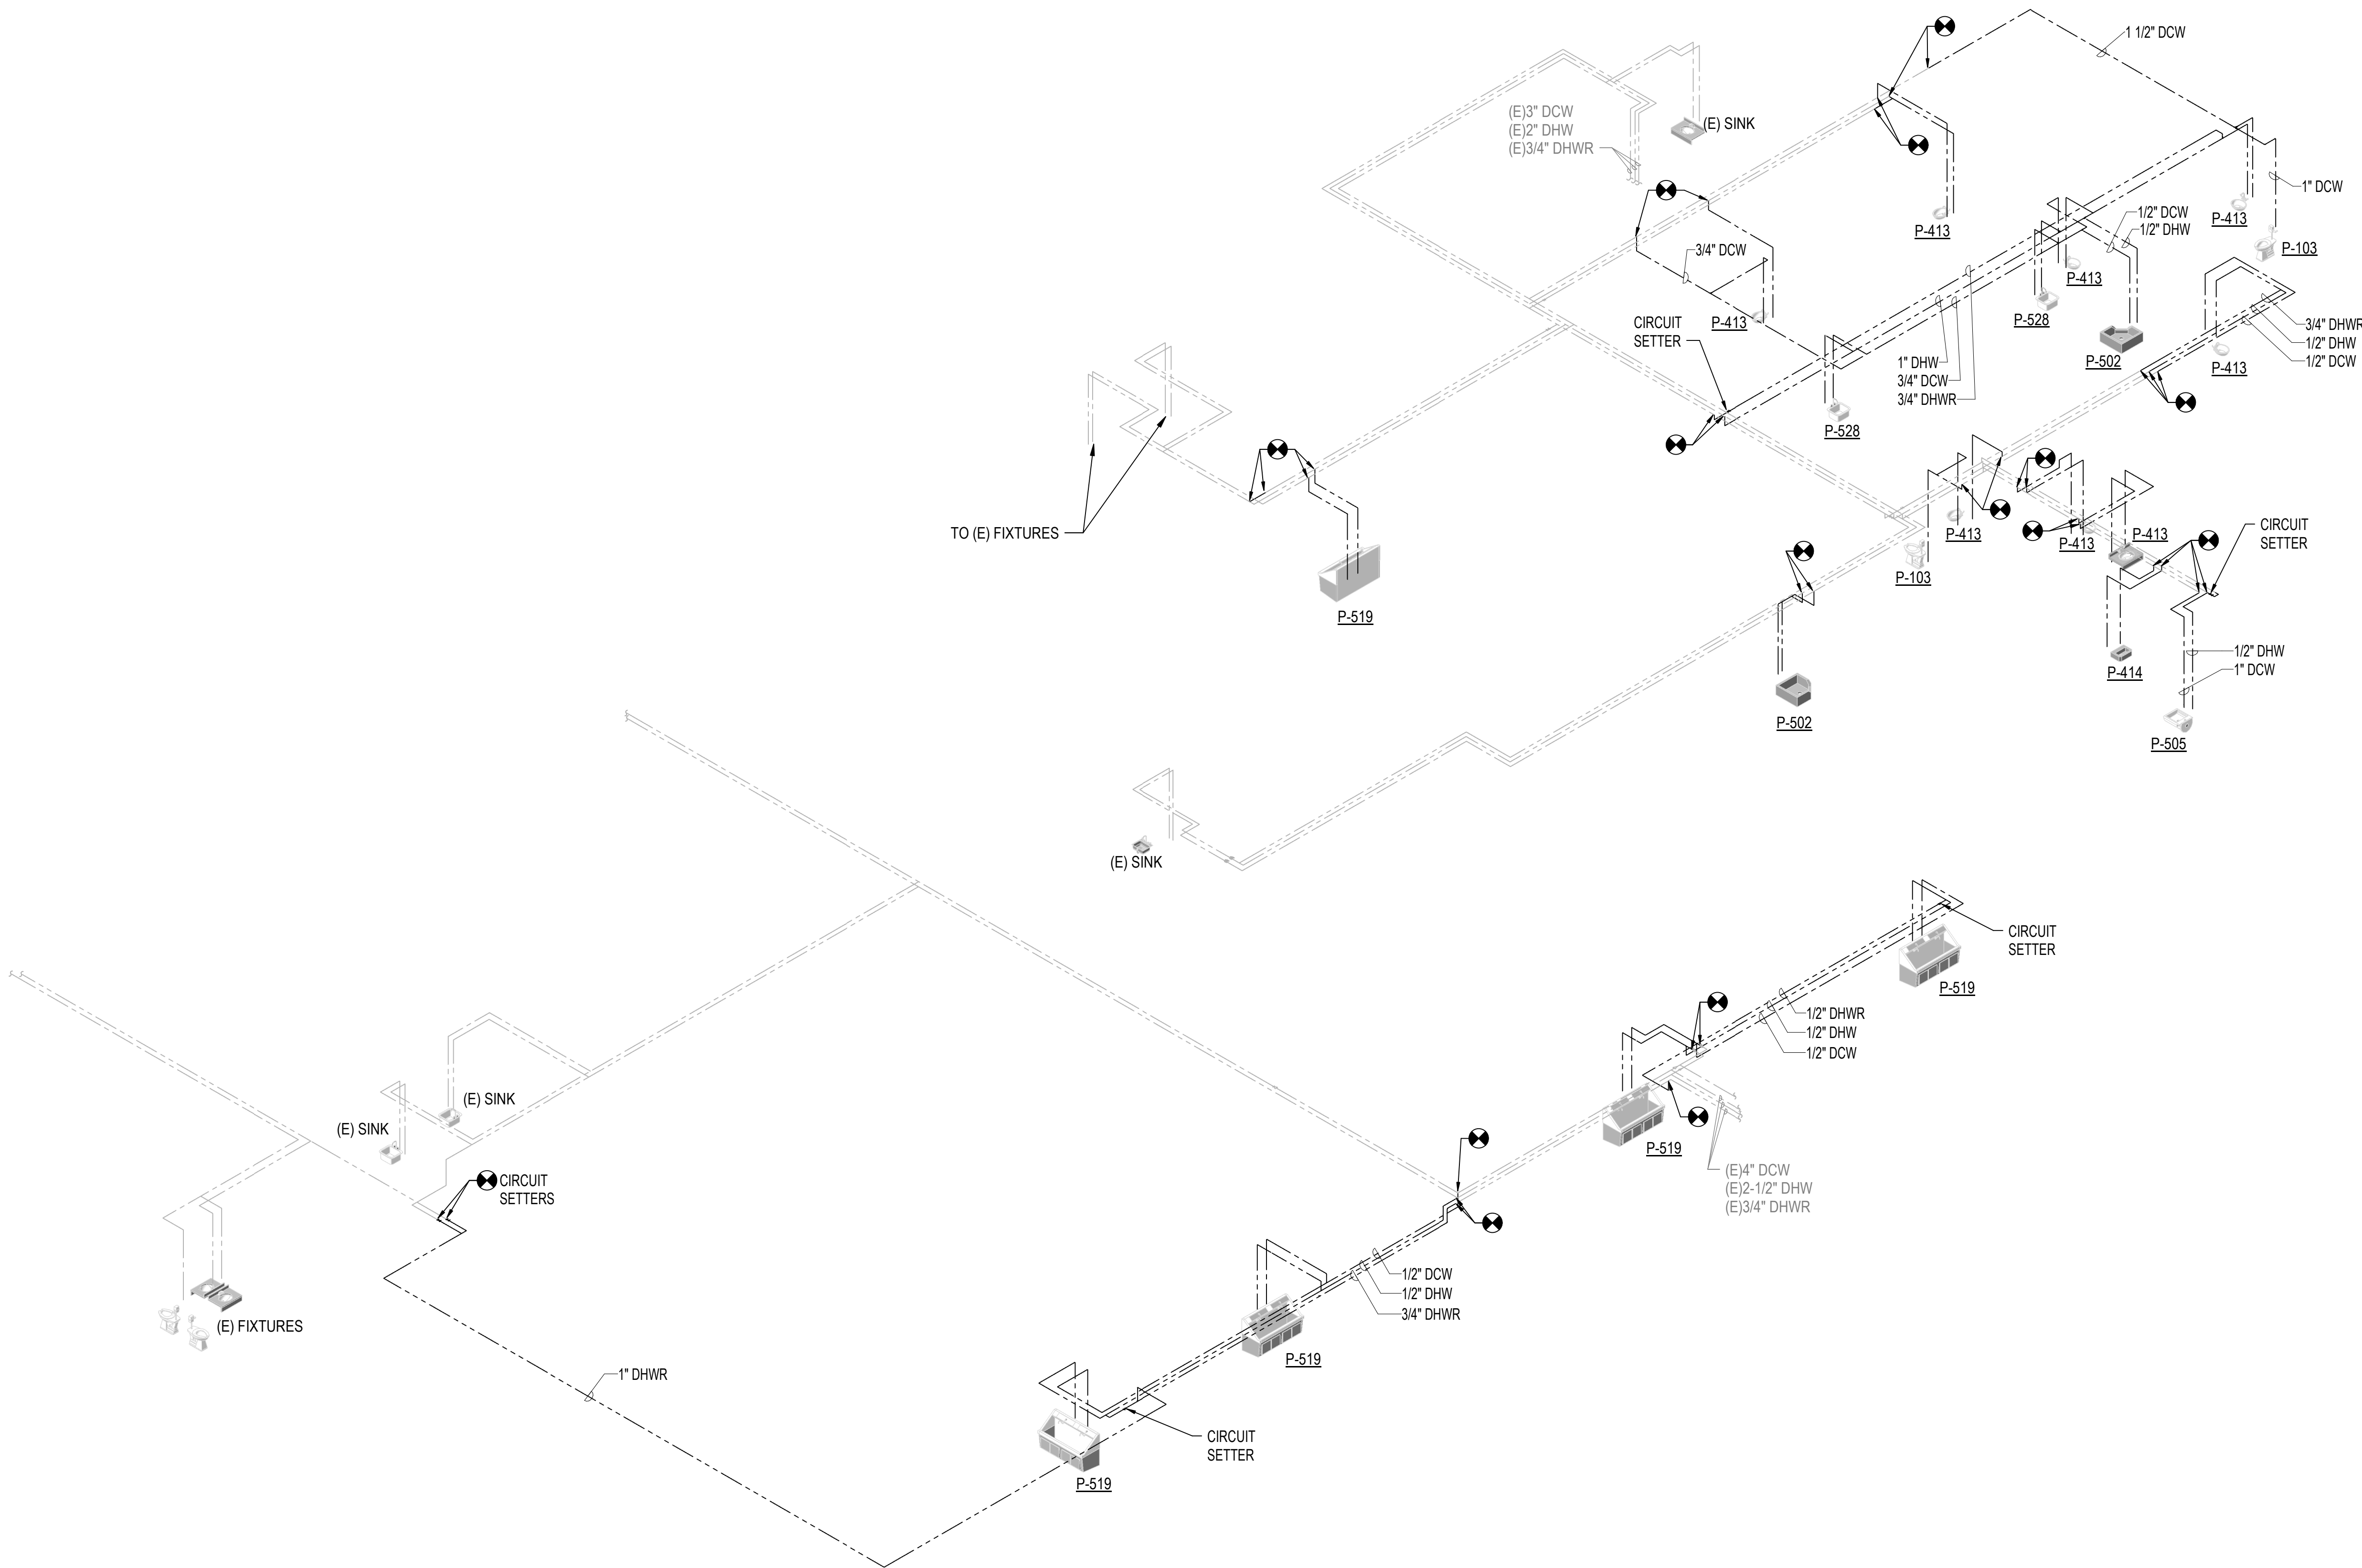

1 ISOMETRIC DIAGRAM DOMESTIC WATER
SCALE: NTS

PRINTS OF THIS DRAWING SHALL NOT BE USED FOR ANY PURPOSE WHATSOEVER WITHOUT THE SEAL AND SIGNATURE OF THE PROFESSIONAL ENGINEER		CONSULTANT			ENGINEER OF RECORD		Drawing Title		Phase		Project Title		VA Drawing Number	
		Architecture:	Civil Engineering:	Fire Protection:			PLUMBING ISOMETRIC DIAGRAM DOMESTIC WATER		BID DOCUMENTS		RENOVATE SURGICAL SUITE PHASE II		2617	
		PF&A DESIGN, P.C.	LABELLA ASSOCIATES	STANTON ENGINEERING SERVICES, LLC							Project Number 658-19-103		Building Number 143	
							Approved by:		FULLY SPRINKLERED		Location SALEM VA MEDICAL CENTER		Drawing Number	
							Jon Manninen, COR				Issue Date		2025-12-30	
											Checked		JS	
											Drawn		SP	
													P-602	

MEDICAL GAS ALARM PANEL SCHEDULE											
MARK	LOCATION	TYPE OF PANEL	GAGES	TEST BUTTON	ABNORMAL SERVICE PRESSURE INDICATOR LIGHTS						
					CARBON DIOXIDE	MEDICAL AIR	MED VACUUM	WAGD	NITROGEN	NITROUS OXIDE	OXYGEN
MGA-1	OR	AREA ALARM	YES	YES	NO	YES	YES	YES	YES	YES	YES
MGA-2	PRE-OP	AREA ALARM	YES	YES	NO	YES	YES	YES	NO	NO	YES
MGA-3	PACU	AREA ALARM	YES	YES	NO	YES	YES	YES	NO	NO	YES

Office of Construction and Facilities Management  U.S. Department of Veterans Affairs	Drawing Title PLUMBING SCHEDULES	Phase BID DOCUMENTS	Project Title RENOVATE SURGICAL SUITE PHASE II Project Number 658-19-103			VA Drawing Number 2617
	Approved by: Jon Manninen, COR	FULLY SPRINKLERED	Location SALEM VA MEDICAL CENTER			Building Number 143
			Issue Date 2025-12-30	Checked BH	Drawn pd	Drawing Number P-701