



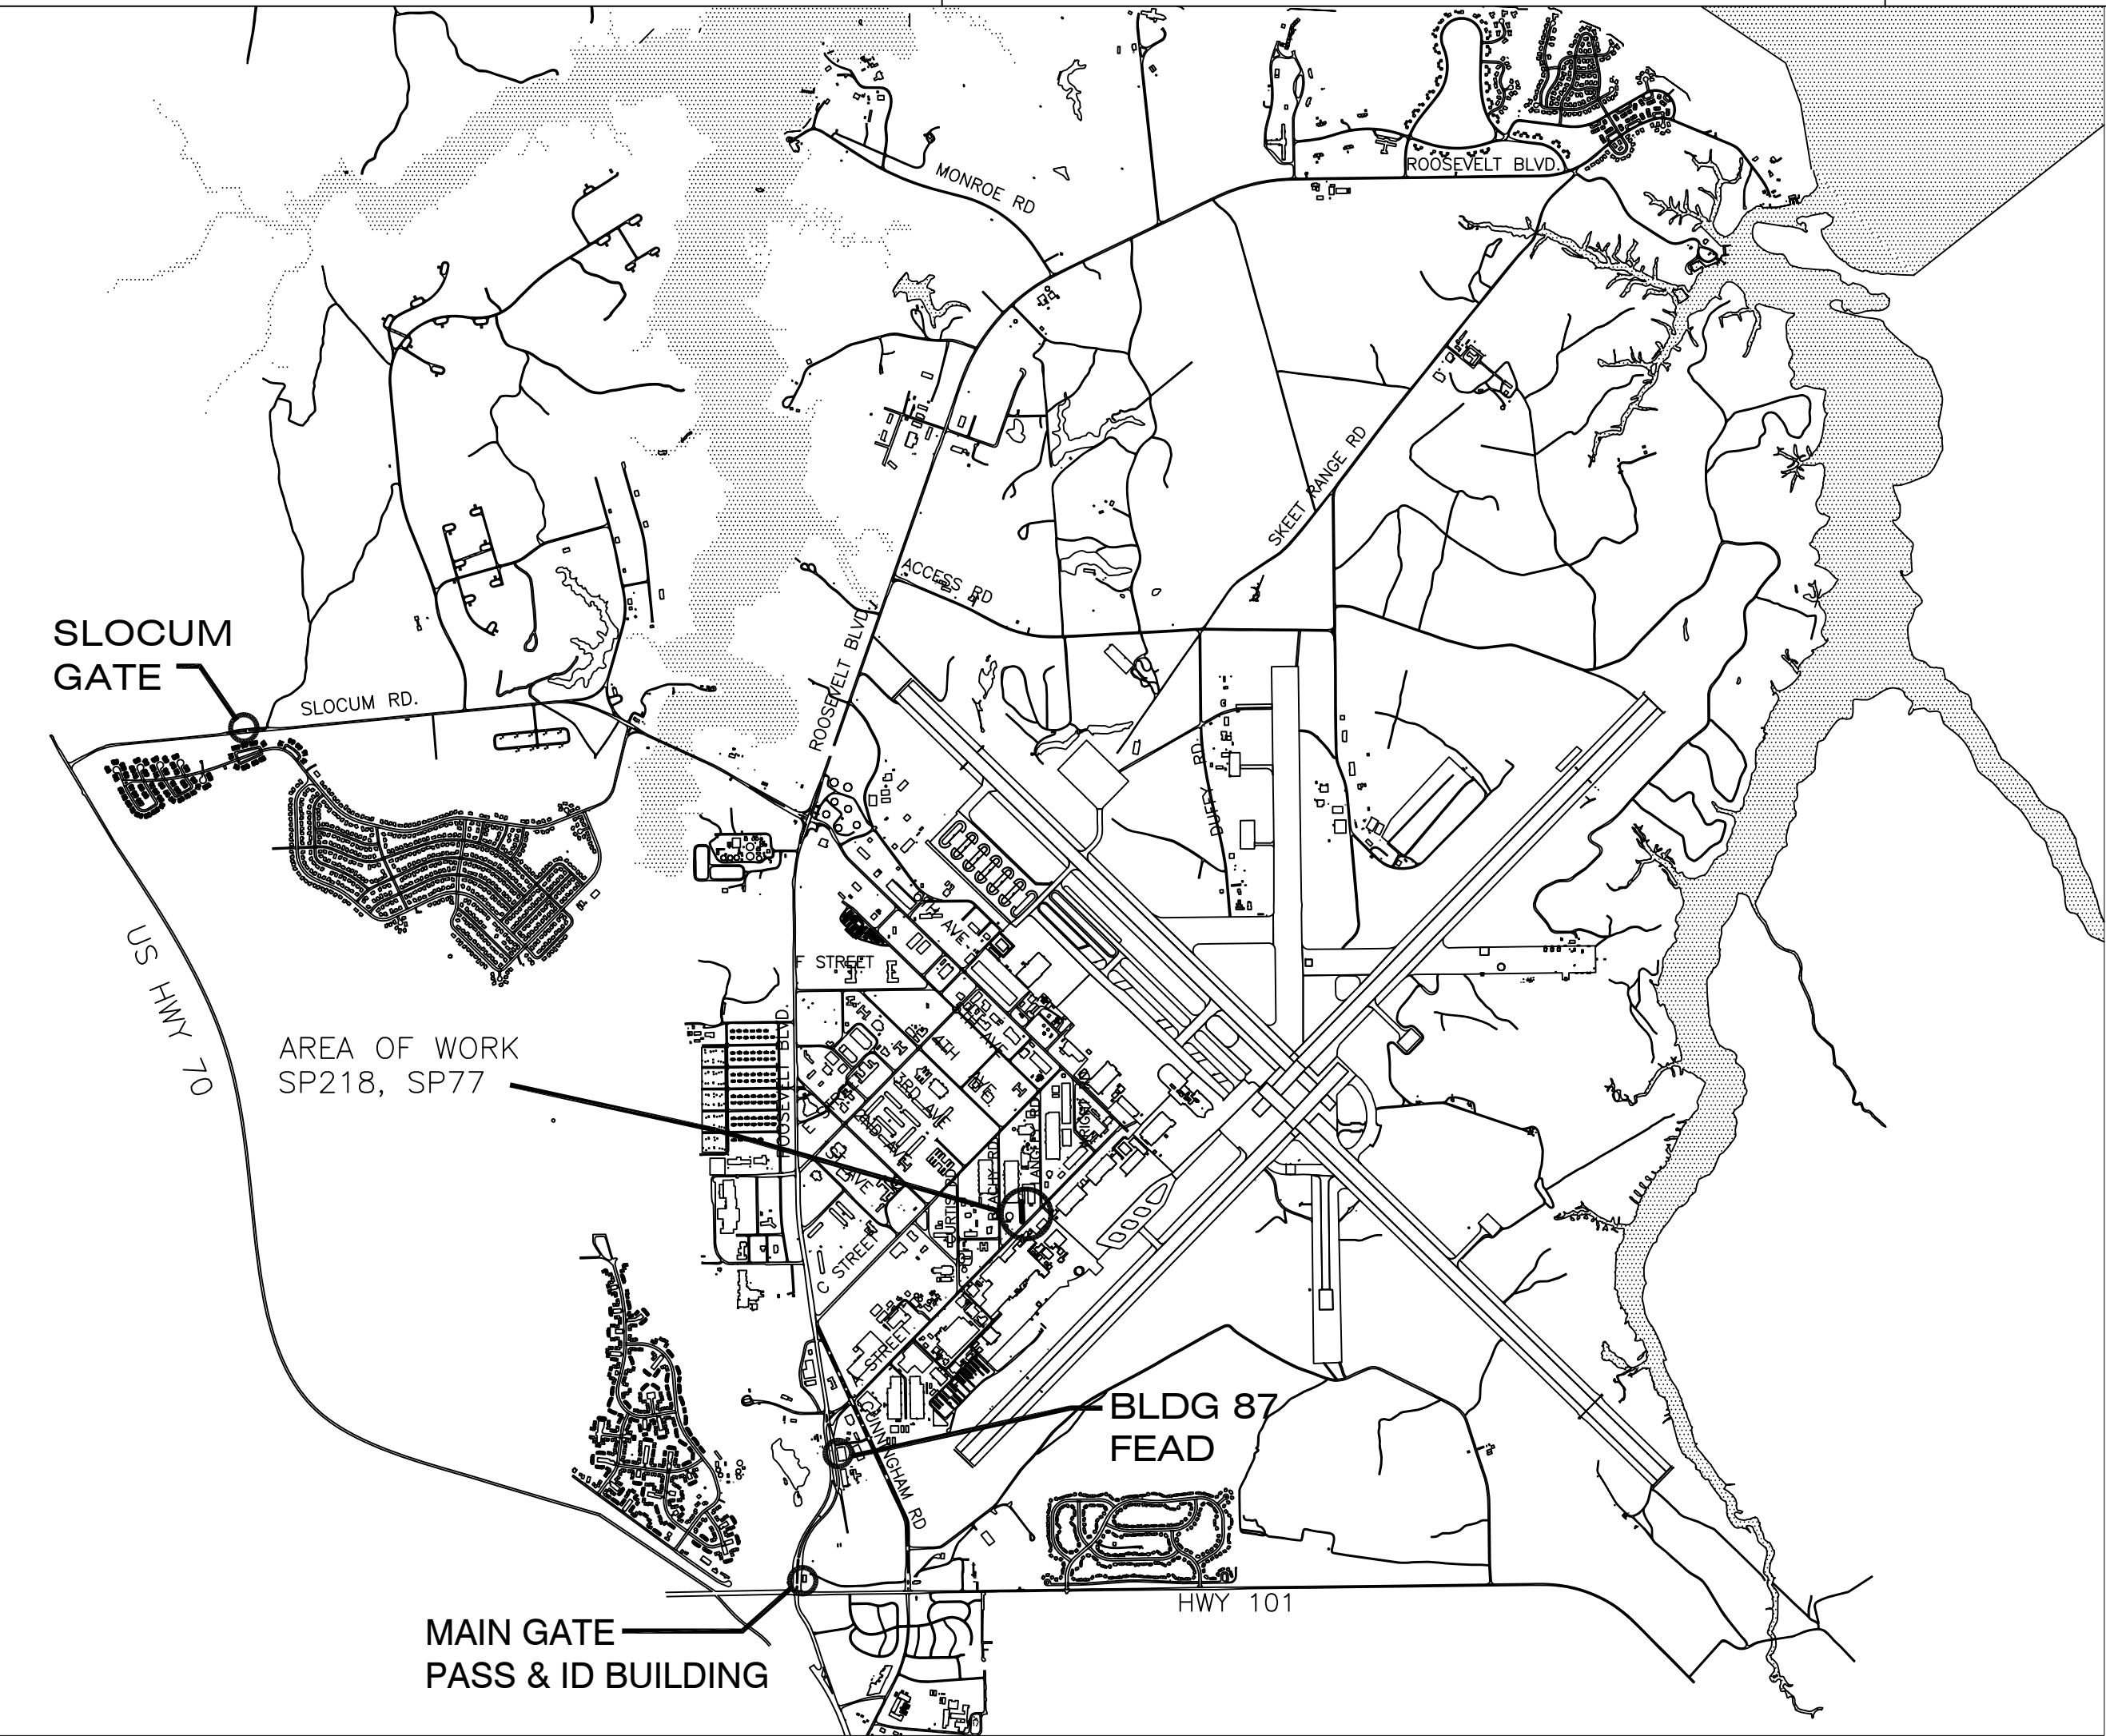

LOCATION MAP

NOT TO SCALE

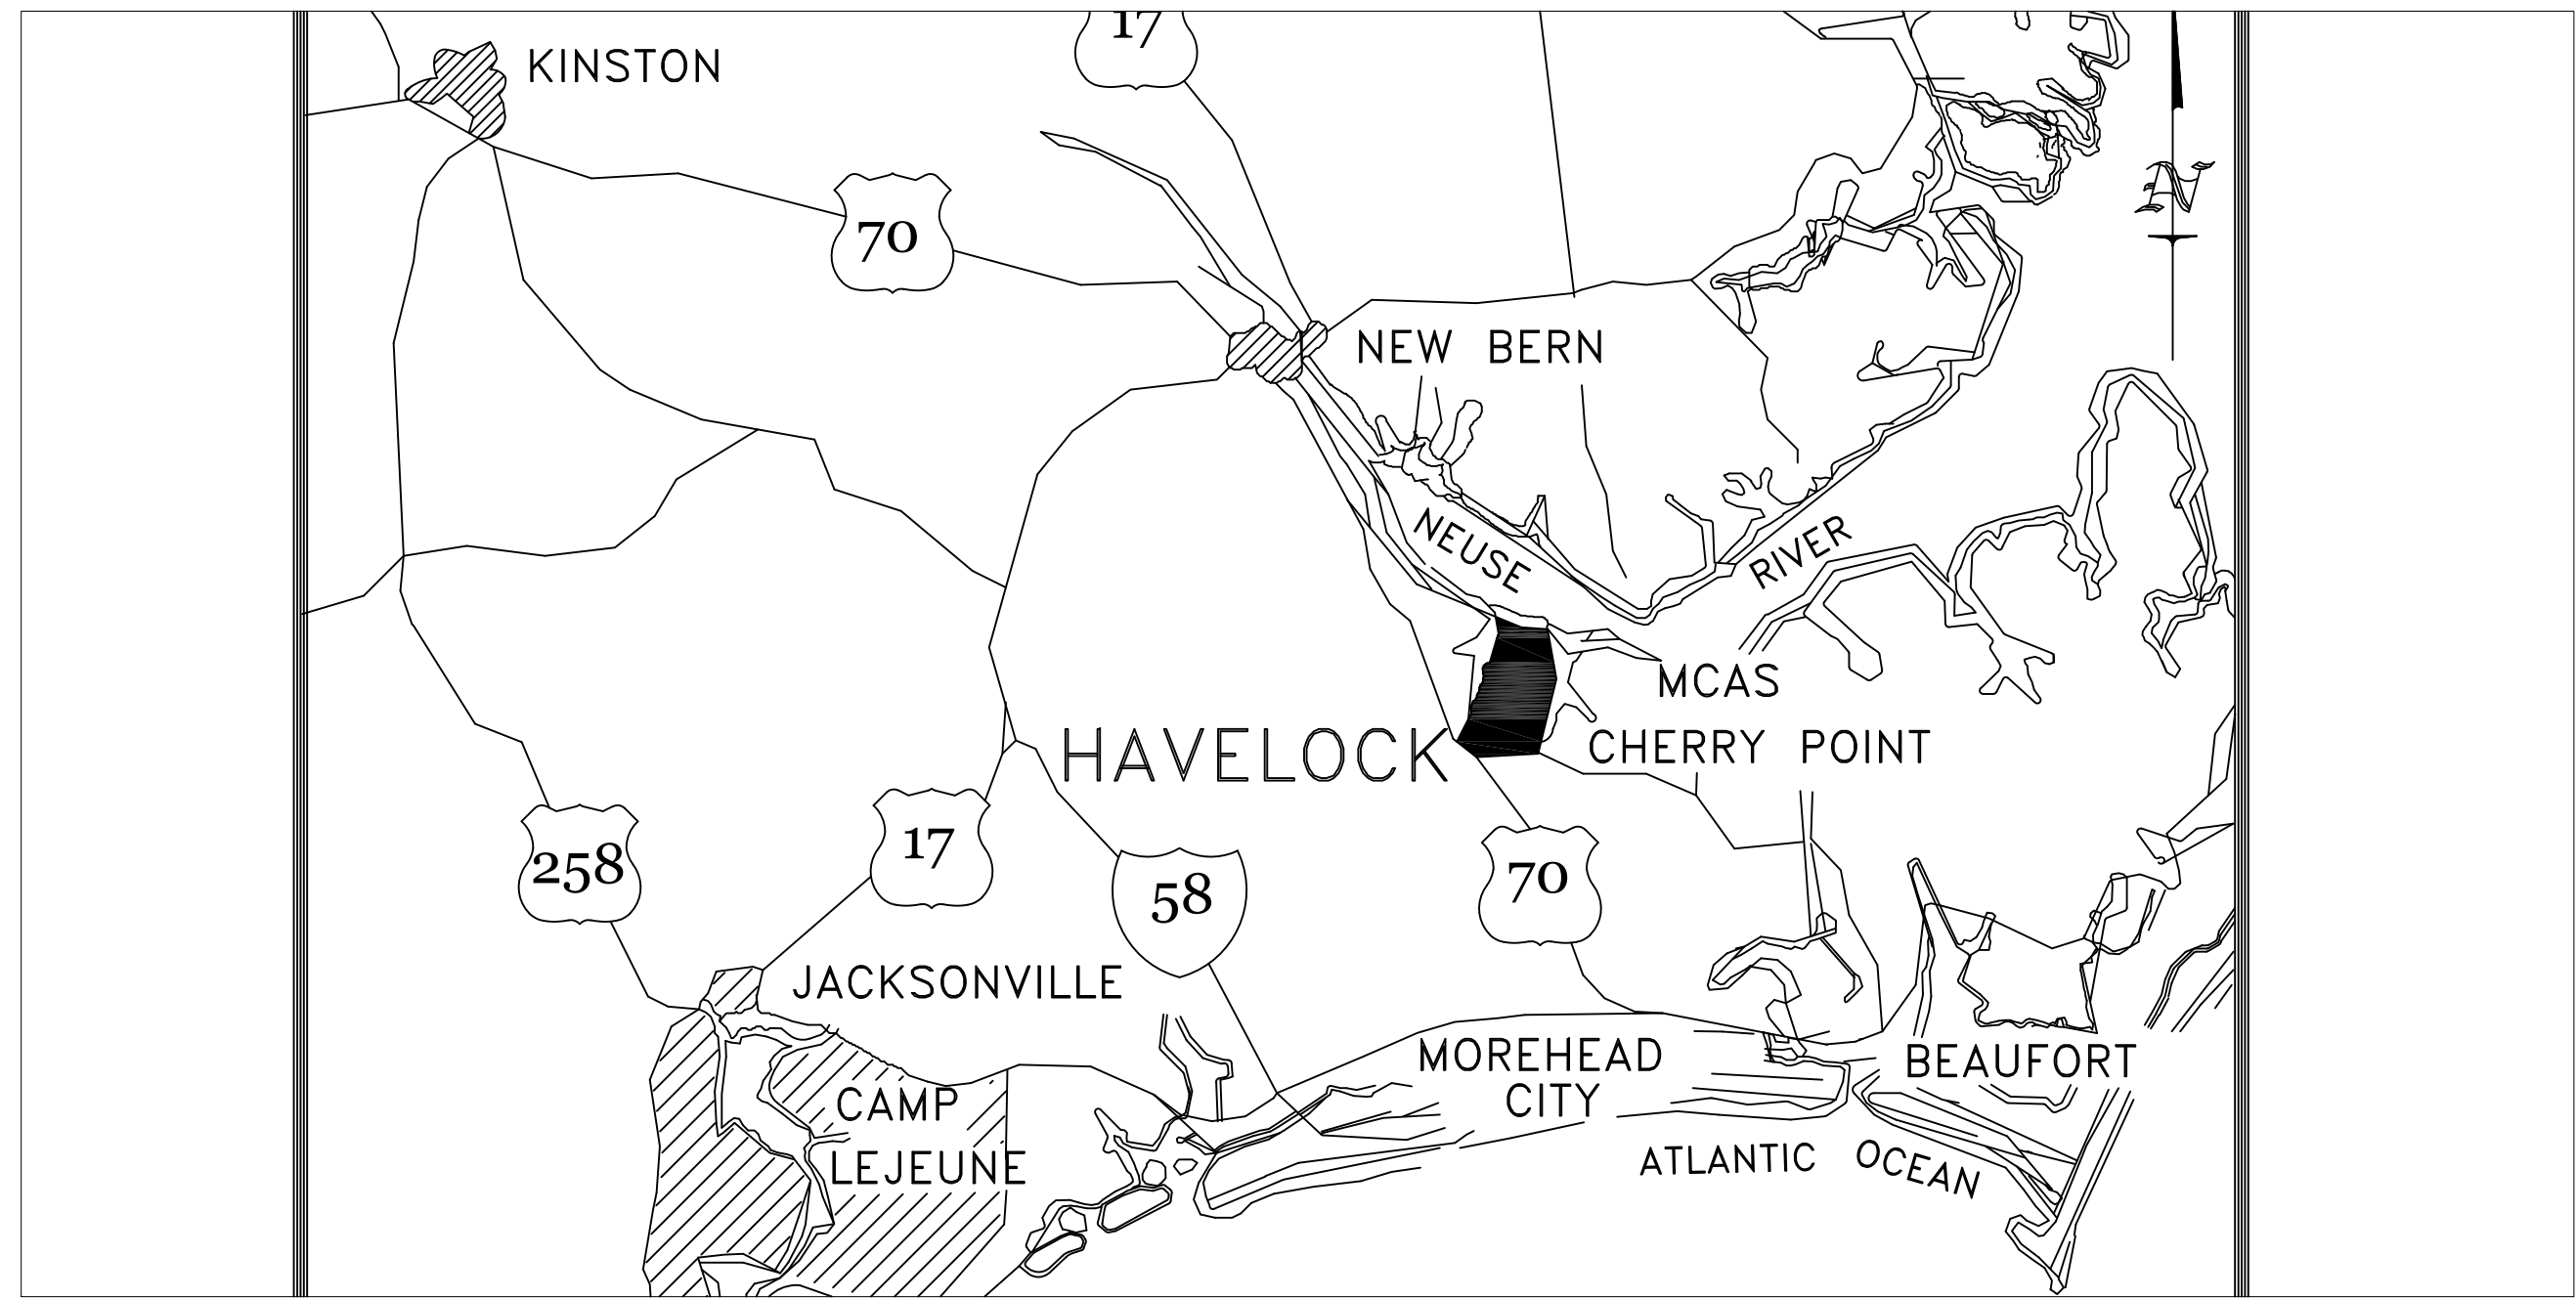

VICINITY MAP

NOT TO SCALE


REPLACE CONDENSATE PIPE BETWEEN SP218 AND SP77

MARINE CORPS AIR STATION
CHERRY POINT, NORTH CAROLINA

WO# 7417111

INDEX OF DRAWINGS

NAVFAC NO.	DWG NO.	TITLE
12926190	G-001	TITLE SHEET
12926191	CD101	CIVIL DEMOLITION SITE PLAN
12926192	CS101	CIVIL NEW WORK SITE PLAN
12926193	CS501	CIVIL DETAILS
12908483	MD101	MECHANICAL DEMOLITION SITE PLAN
12908484	MS101	MECHANICAL NEW WORK SITE PLAN
12908485	MD401	MECHANICAL DEMOLITION STEAM PIT DETAILS
12908486	MS401	MECHANICAL NEW WORK STEAM PIT DETAILS

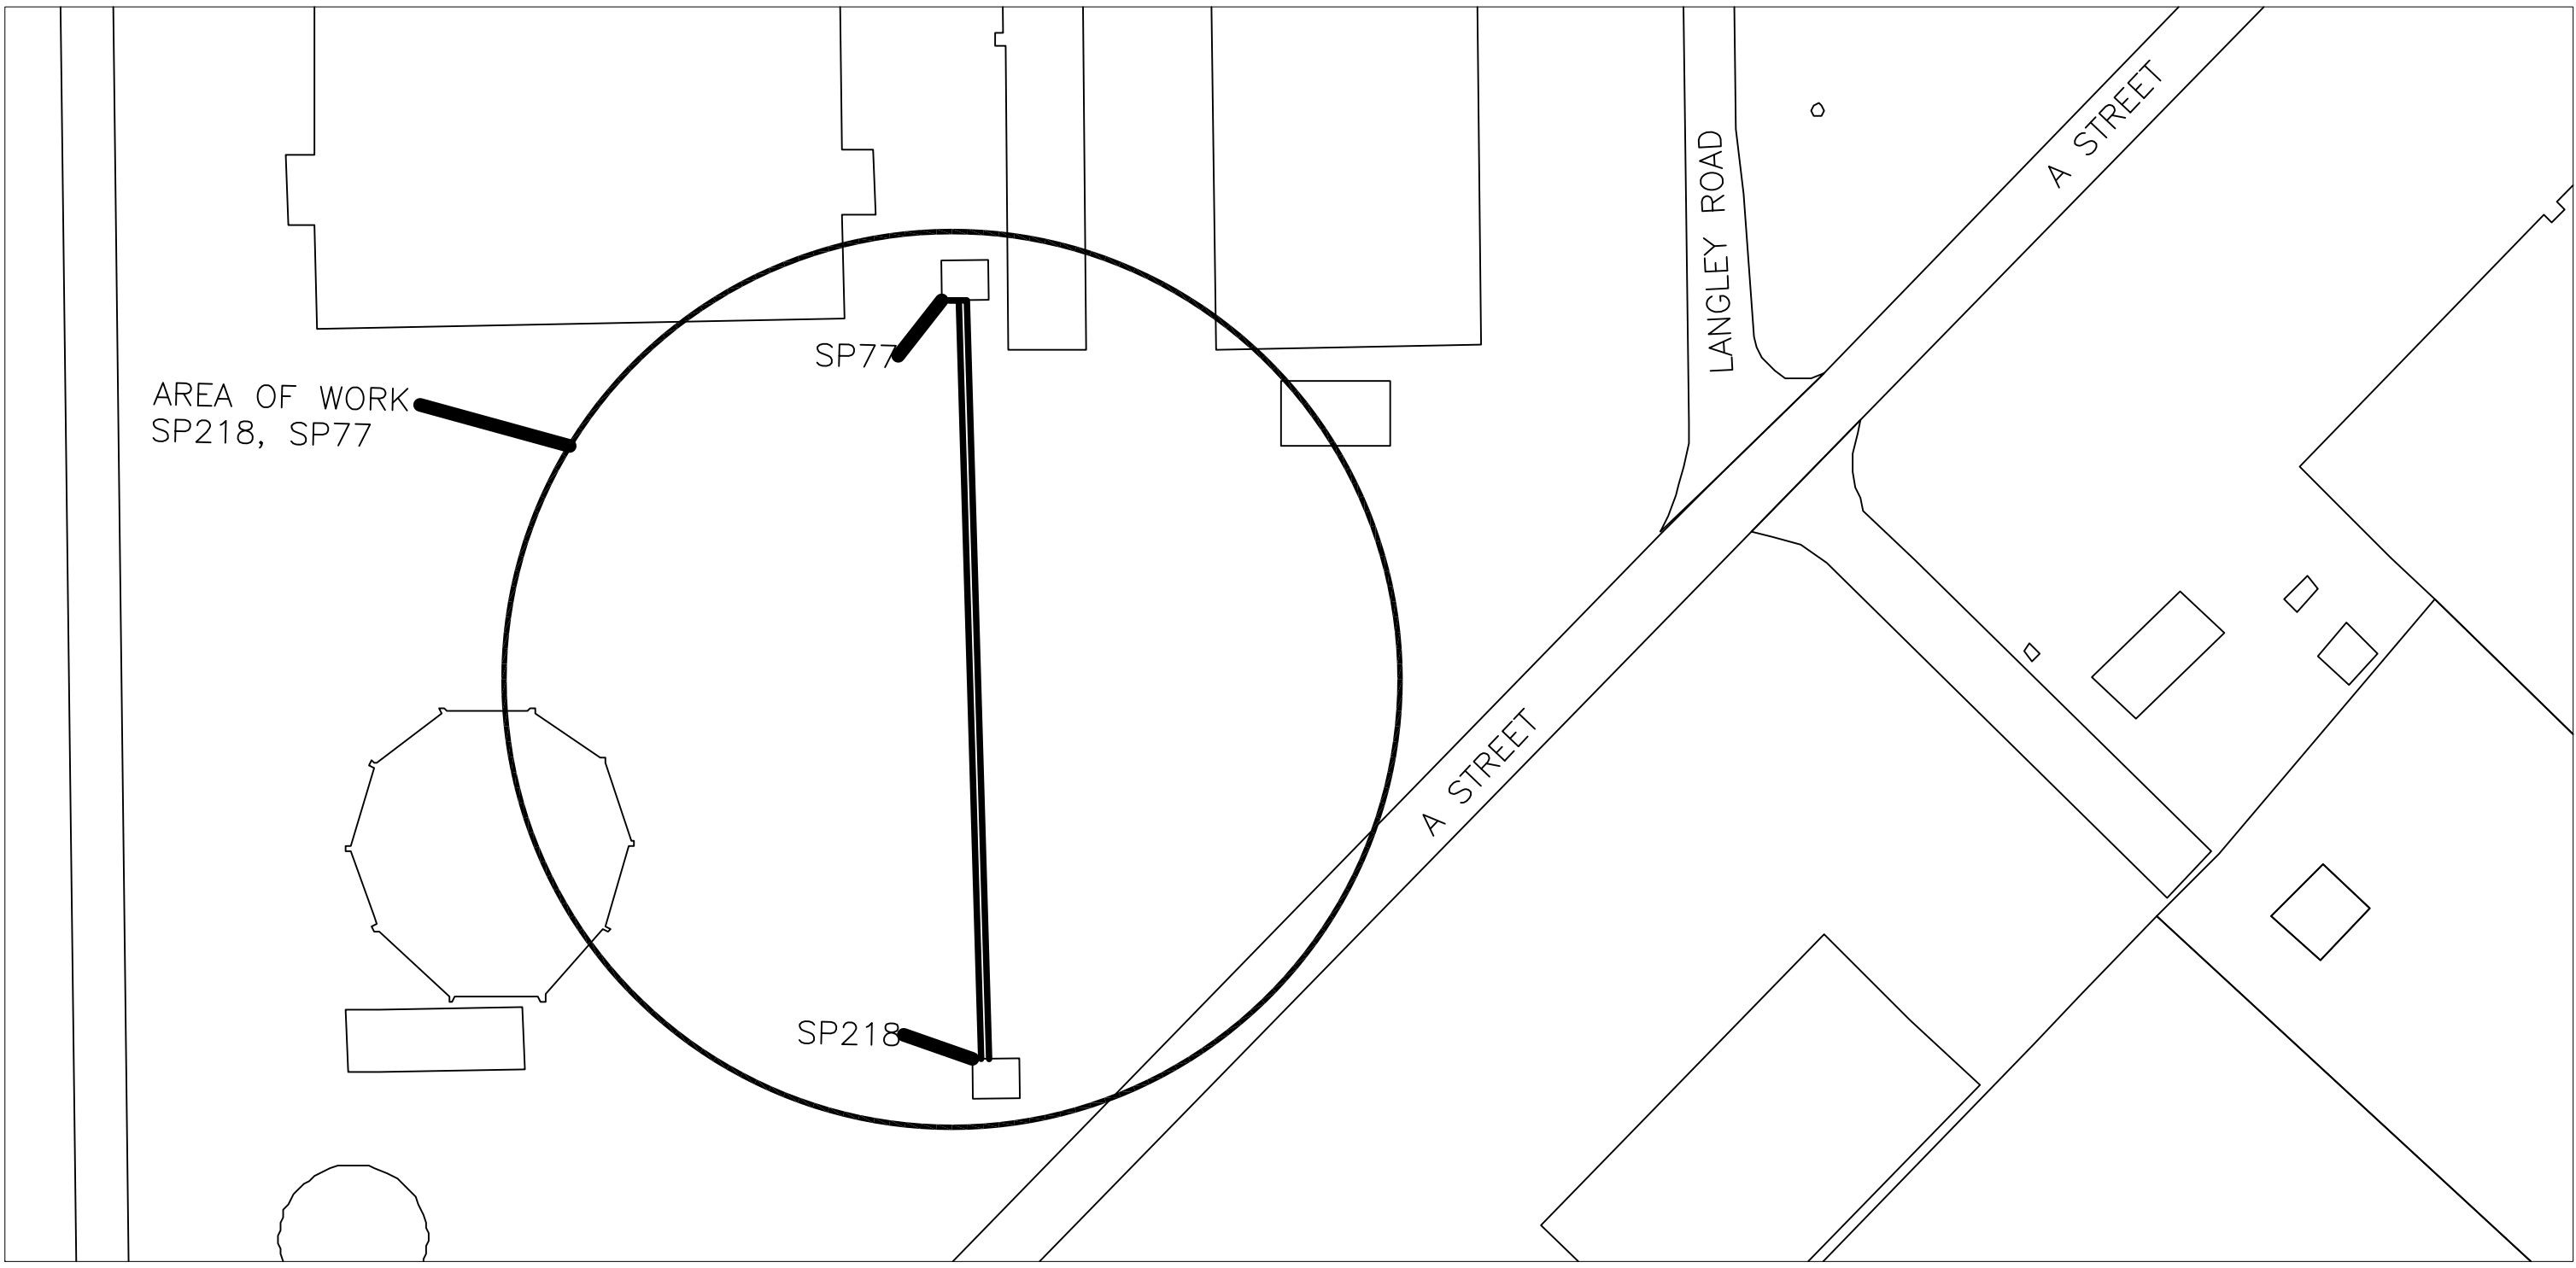


PROJECT SITE STEAM PITS 218 AND 77

NOT TO SCALE


DATE	APPR
DESCRIPTION	SYN
DESIGNED & ENGINEERED BY: FACILITIES ENGINEERING MECHANICAL	
	
A/E'S USE THIS SPACE FOR YOUR ADDRESS INFO	
FINAL	
3/6/2026	
SEAL	
APPROVED	
Michelle Sazynski, PC	
ACTIVITY - SATISFACTORY TO	
03/25/2026	
DATE	
APPROVED	
FOR EFD FOR COMMANDER NAVFAC	
DATE	
A/E	
DESIGN JRM	
DRAWN JRM	
REVIEW NAH	
QC	
CHIEF ARCH/ ENR	
PROJECT MANAGER	
FIRE PROTECTION	
BRANCH MANAGER NAH	
DESIGN DIRECTOR LPF	
NAVFAC DRAWING NO. 12926190	
SHEET 1 OF 8	
G-001	
DRAWING REVISION JULY 2003	

[illegible]

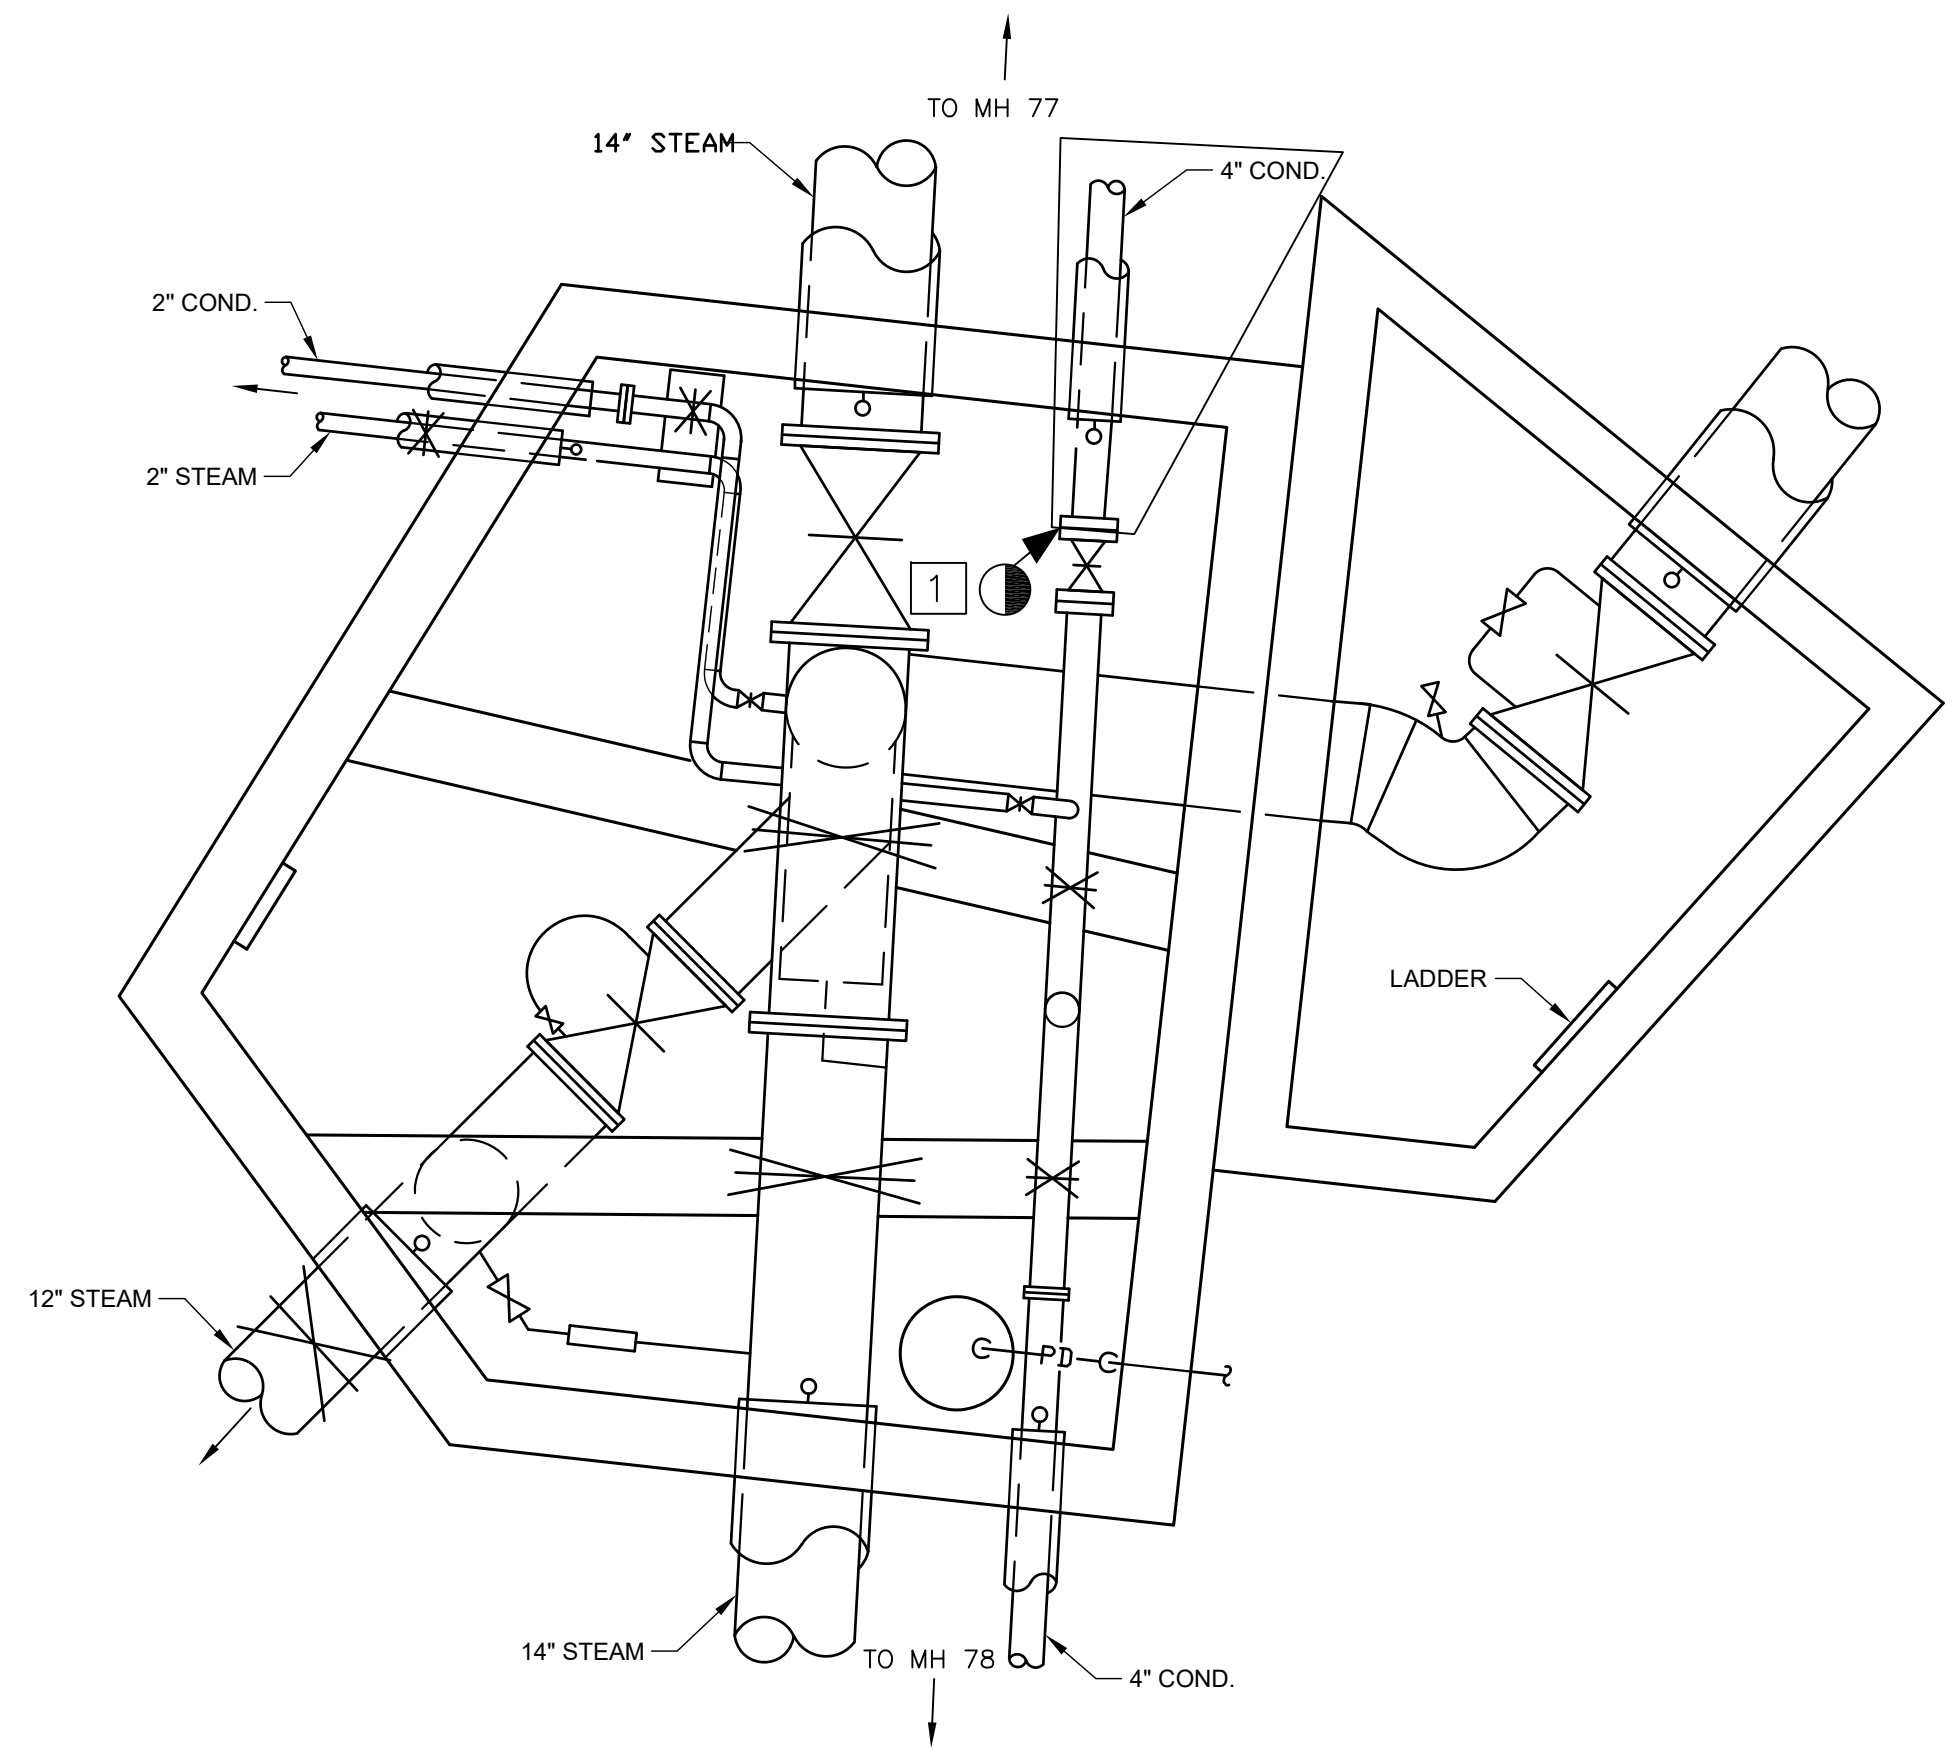

- LEGEND
- CHECK VALVE
 - DRIP STATION
 - END CAPPED
 - FLANGED UNION
 - GATE VALVE
 - GATE VALVE
 - GATE VALVE IN RISER
 - GATE VALVE IN RISER
 - PIPE ANCHOR
 - PIPE DOWN
 - PIPE UP
 - PRESSURE GAUGE
 - PUMPED DISCHARGE
 - RECEIVER
 - VENT
 - STEAM TRAP

1 DEMOLITION - STEAM PIT 218 DETAIL
SCALE: 1/2"=1'

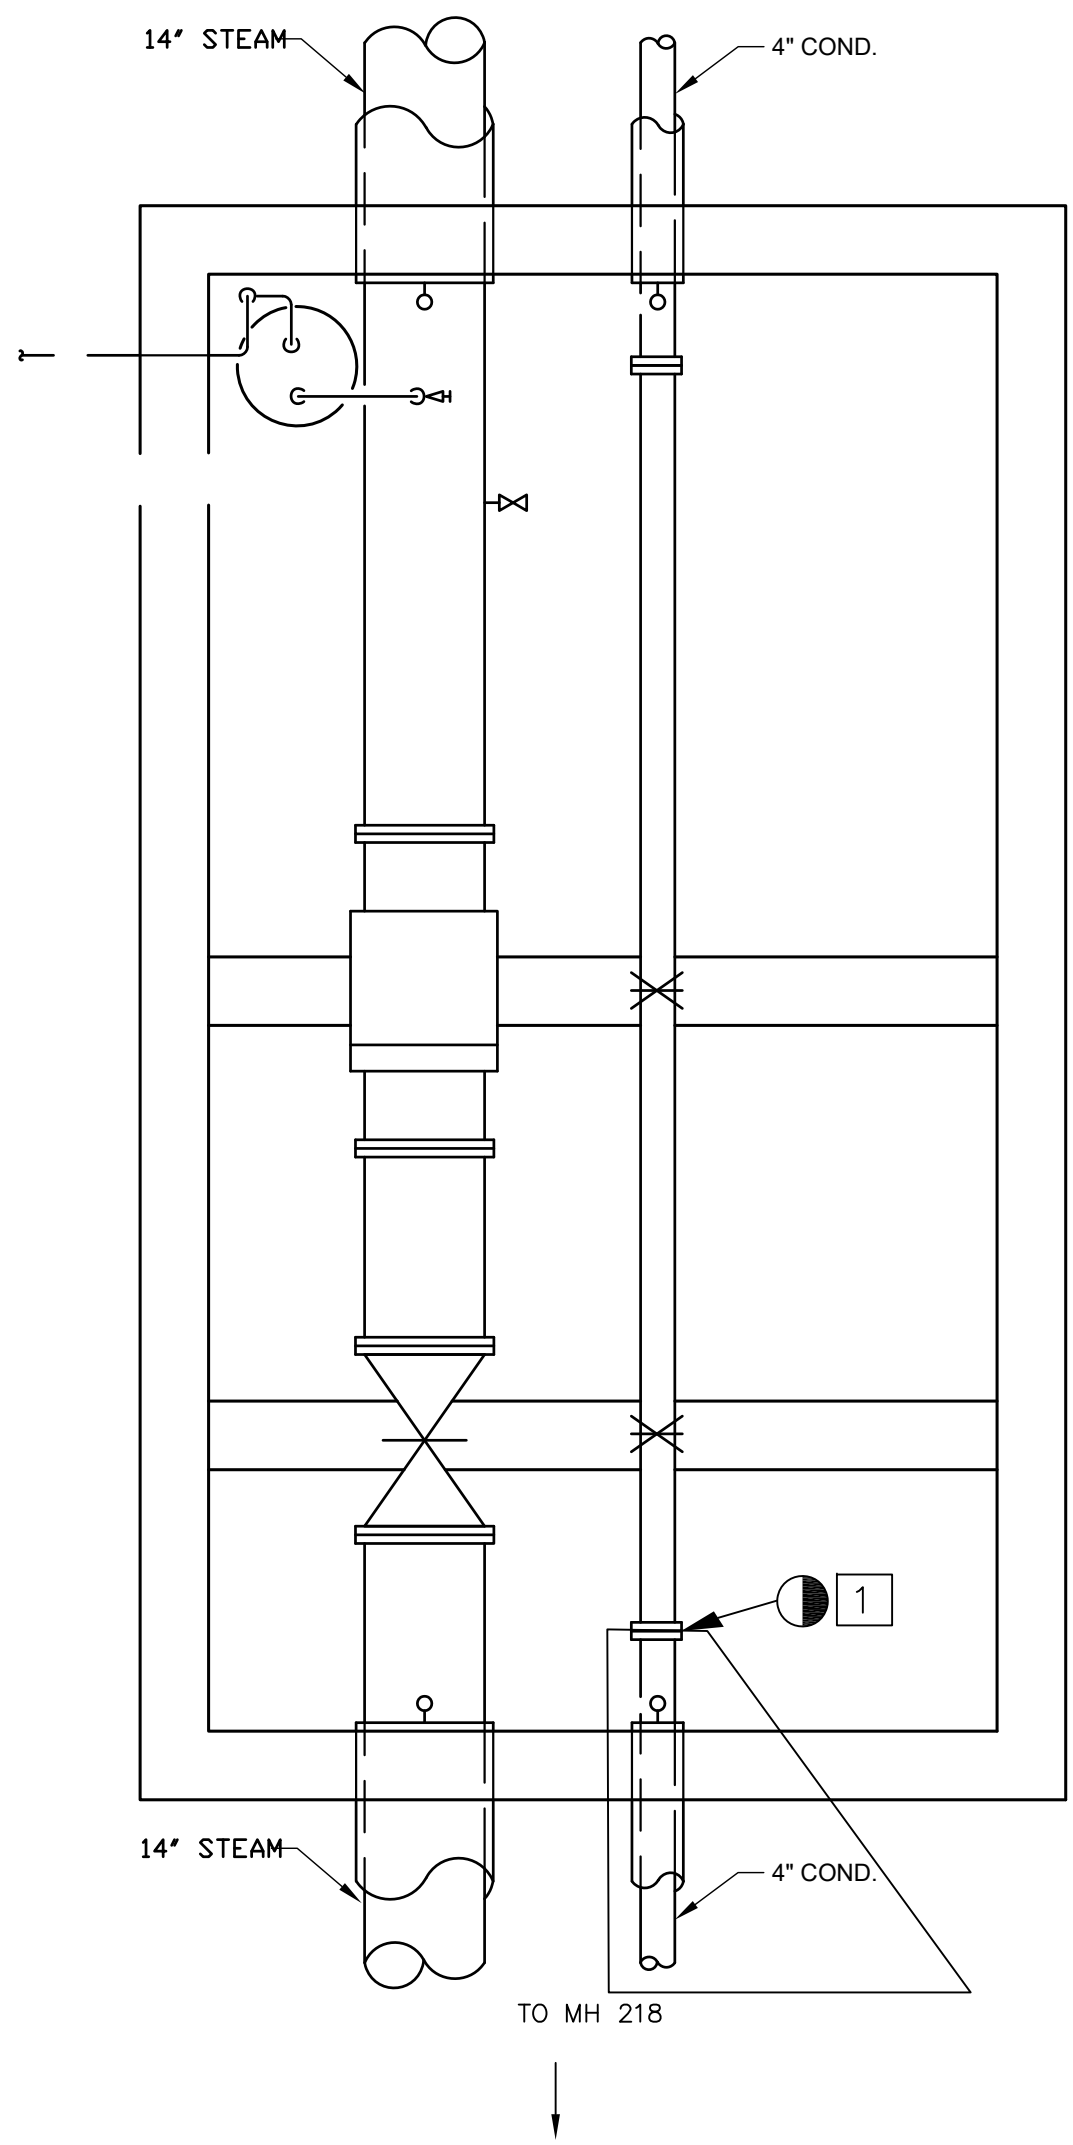

- LEGEND
- CHECK VALVE
 - DRIP STATION
 - END CAPPED
 - FLANGED UNION
 - GATE VALVE
 - GATE VALVE
 - GATE VALVE IN RISER
 - GATE VALVE IN RISER
 - PIPE ANCHOR
 - PIPE DOWN
 - PIPE UP
 - PRESSURE GAUGE
 - PUMPED DISCHARGE
 - RECEIVER
 - VENT
 - STEAM TRAP

2 DEMOLITION - STEAM PIT 77 DETAIL
SCALE: 1/2"=1'



DEMOLITION NOTES:

1 REMOVE PIPING, INSULATION, AND SUPPORTS DISCONNECT FROM FLANGE.

1/2" = 1'-0"



DESIGNED & ENGINEERED BY: FACILITIES ENGINEERING MECHANICAL		DATE	APPR
A/E'S USE THIS SPACE FOR YOUR ADDRESS INFO.		SYN	
			
FINAL			
3/6/2026			
SEAL			
APPROVED			
ACTIVITY - SATISFACTORY TO			
DATE			
APPROVED			
FOR EFD FOR COMMANDER NAVFAC			
DATE			
A/E		EFD	
DESIGN		JRM	
DRAWN		JRM	
REVIEW		NAH	
QC			
CHIEF		ARCH./ ENGR.	
PROJECT MANAGER			
FIRE PROTECTION			
BRANCH MANAGER			
DESIGN DIRECTOR			
NAH LPF			
NAVAL FACILITIES ENGINEERING COMMAND			
MARINE CORPS AIR STATION, CHERRY POINT, N.C.			
REPLACE CONDENSATE PIPE BETWEEN SP218 AND SP77			
MECHANICAL DEMOLITION STEAM PIT DETAILS			
DEPARTMENT OF THE NAVY			
CODE ID. NO.	80091	SIZE	D
SCALE: AS SHOWN			
FED. NO.			
STA. PROJ. NO. 7417111			
SPEC. NO.			
CONSTR. CONTR. NO.			
NAVFAC DRAWING NO. 12908484			
SHEET 6 OF 8			
MD401			
DRAWING REVISION JULY 2003			

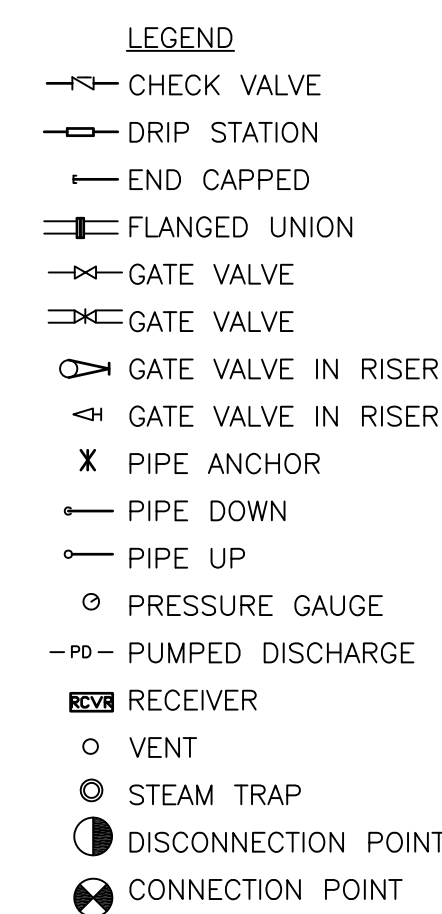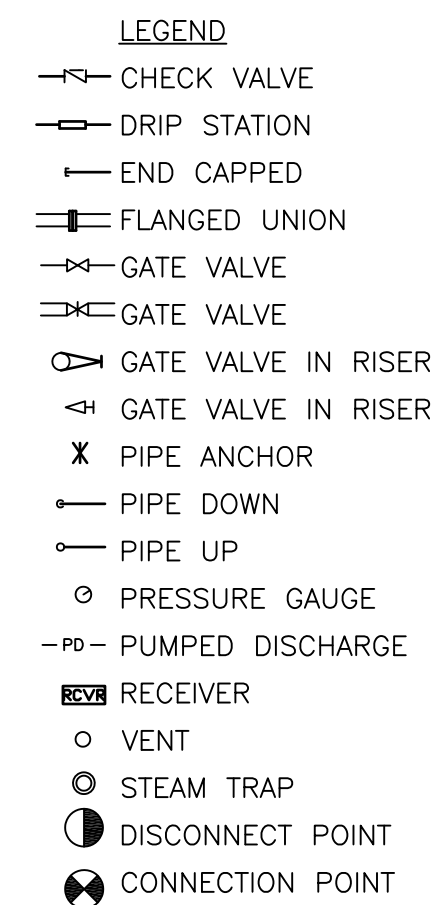

NEW WORK – STEAM PIT 218 DETAIL
SCALE: 1/2"=1'

1 INSTALL PIPING, INSULATION, JACKETING, AND RECONNECT TO THE FLANGE.

NEW WORK - STEAM PIT 77 DETAIL
SCALE: 1/2"=1'

$$1/2'' = 1'-0''$$
[illegible]