

8

7

6

5

4

3

2

1

REV

PC#

QTY

UNIT

MFR PART NO / NSN

DESCRIPTION

MATERIAL

0

1

AR

—

—

PLATE, 7.65#

STEEL

0

2

AR

—

—

PLATE, 10.2#

STEEL

0

3

AR

—

—

PLATE, 12.75#

STEEL

0

4

AR

—

—

PLATE, 20.4#

STEEL

0

5

AR

—

—

TEE, MT 3x2.2#

STEEL

0

6

AR

—

—

TEE, WT 8x10#

STEEL

0

7

AR

—

—

TEE, WT 6x7#

STEEL

0

8

AR

—

—

TEE, WT 5x6#

STEEL

0

9

AR

—

—

TEE, WT 7x11#

STEEL

0

10

AR

—

—

TEE, MT 4x3.25#

STEEL

GENERAL NOTES

1. THE PURPOSE OF THIS DRAWING IS TO PROVIDE CONSTRUCTION INFORMATION AND MATERIAL NECESSARY FOR THE STRUCTURAL BULKHEADS AND DECK PLATING AND FRAMING OF THE USCG HSCL.

2. STRUCTURE SHOWN IS PRELIMINARY AND NOT FOR PRODUCTION.

3. SCANTLINGS REFLECT ABS MVR PART 3 AND ARE ABS GRADE H36 STEEL UNLESS OTHERWISE NOTED.

4. UNITS AND SIZES ARE US CUSTOMARY, DIMENSIONS ARE IN INCHES UNLESS OTHERWISE NOTED.

5. ALL SECTIONS ARE DRAWN LOOKING AFT UNLESS OTHERWISE NOTED.

REV

SH

ZONE

ITEM

DESCRIPTION

DATE

APPL SIG & ORG

0

—

—

—

PRELIMINARY RELEASE FOR DRAFT RFP

02/24/26

1

—

—

NO.

TITLE

DRAWING NO.

REFERENCE PLANS

SPECIAL NOTATIONS

PRELIMINARY DRAWING ISSUED TO SUPPORT DRAFT RFP. DRAWING IS UNDER DEVELOPMENT, AND NOT APPROVED.

RESERVATIONS:

A. ENGINE FOUNDATION IS PRELIMINARY AND SUBJECT TO FURTHER DEVELOPMENT.

B. CRANE FOUNDATION IS PRELIMINARY AND SUBJECT TO FURTHER DEVELOPMENT.

STINFO DESIGNATION

DISTRIBUTION STATEMENT D: DISTRIBUTION AUTHORIZED TO DHS/CG/DOD AND THEIR CONTRACTORS FOR ADMINISTRATIVE AND OPERATIONAL PURPOSES; 02/24/2026. OTHER REQUESTS SHALL BE REFERRED TO CG-SEA-AB.
DESTRUCTION NOTICE: FOR UNCLASSIFIED, LIMITED DOCUMENTS, DESTROY BY ANY METHOD THAT WILL PREVENT DISCLOSURE OF CONTENTS OR RECONSTRUCTION OF THE DOCUMENT.

UNITED STATES COAST GUARD

WASHINGTON, D.C. 20593

69 FT

HSCL

HOMELAND SECURITY CUTTER LIGHT

DECKS & BULKHEADS

TITLE SHEET & MATERIALS LIST

DESIGNED: DSGN SIG /s/ MM/DD/YY

DRAWN: DRWN SIG /s/ MM/DD/YY

CHECKED: CHKD SIG /s/ MM/DD/YY

APPROVED: APVD SIG /s/ MM/DD/YY

USCG APPROVAL MM/DD/YY

APPL SIG /s/

SELECTED RECORD DRAWING

UPDATE REQUIRED FOR ALL AUTHORIZED CONFIGURATION CHANGES.

H

81340

USCG DRAWING NO.

69-HSCL-101-002

REV

0

SCALE: NONE

SHEET: 1 OF 7

69-HSCL

ALL BOATS

ASSET CLASS

HULLS

APPLICABILITY

7

0

ELEVATIONS & DETAILS

6

0

1ST PLATFORM

5

0

SECTION VIEW OF BULKHEADS 43 & 49

4

0

SECTION VIEW OF BULKHEADS 4, 13, 26 & 33

3

0

WORKING DECK

2

0

MAIN DECK

1

0

TITLE SHEET & MATERIALS LIST

SH

REV

SHEET SUBTITLE

SHEET REVISION STATUS AND SUBTITLE INDEX

8

7

6

5

4

3

2

1

A

B

C

D

E

F

G

H

8

7

6

5

4


3

2


1


69-HSCL_101_002_0 Decks & Bulkheads.dwg


ELECTRONIC FILE NAME:

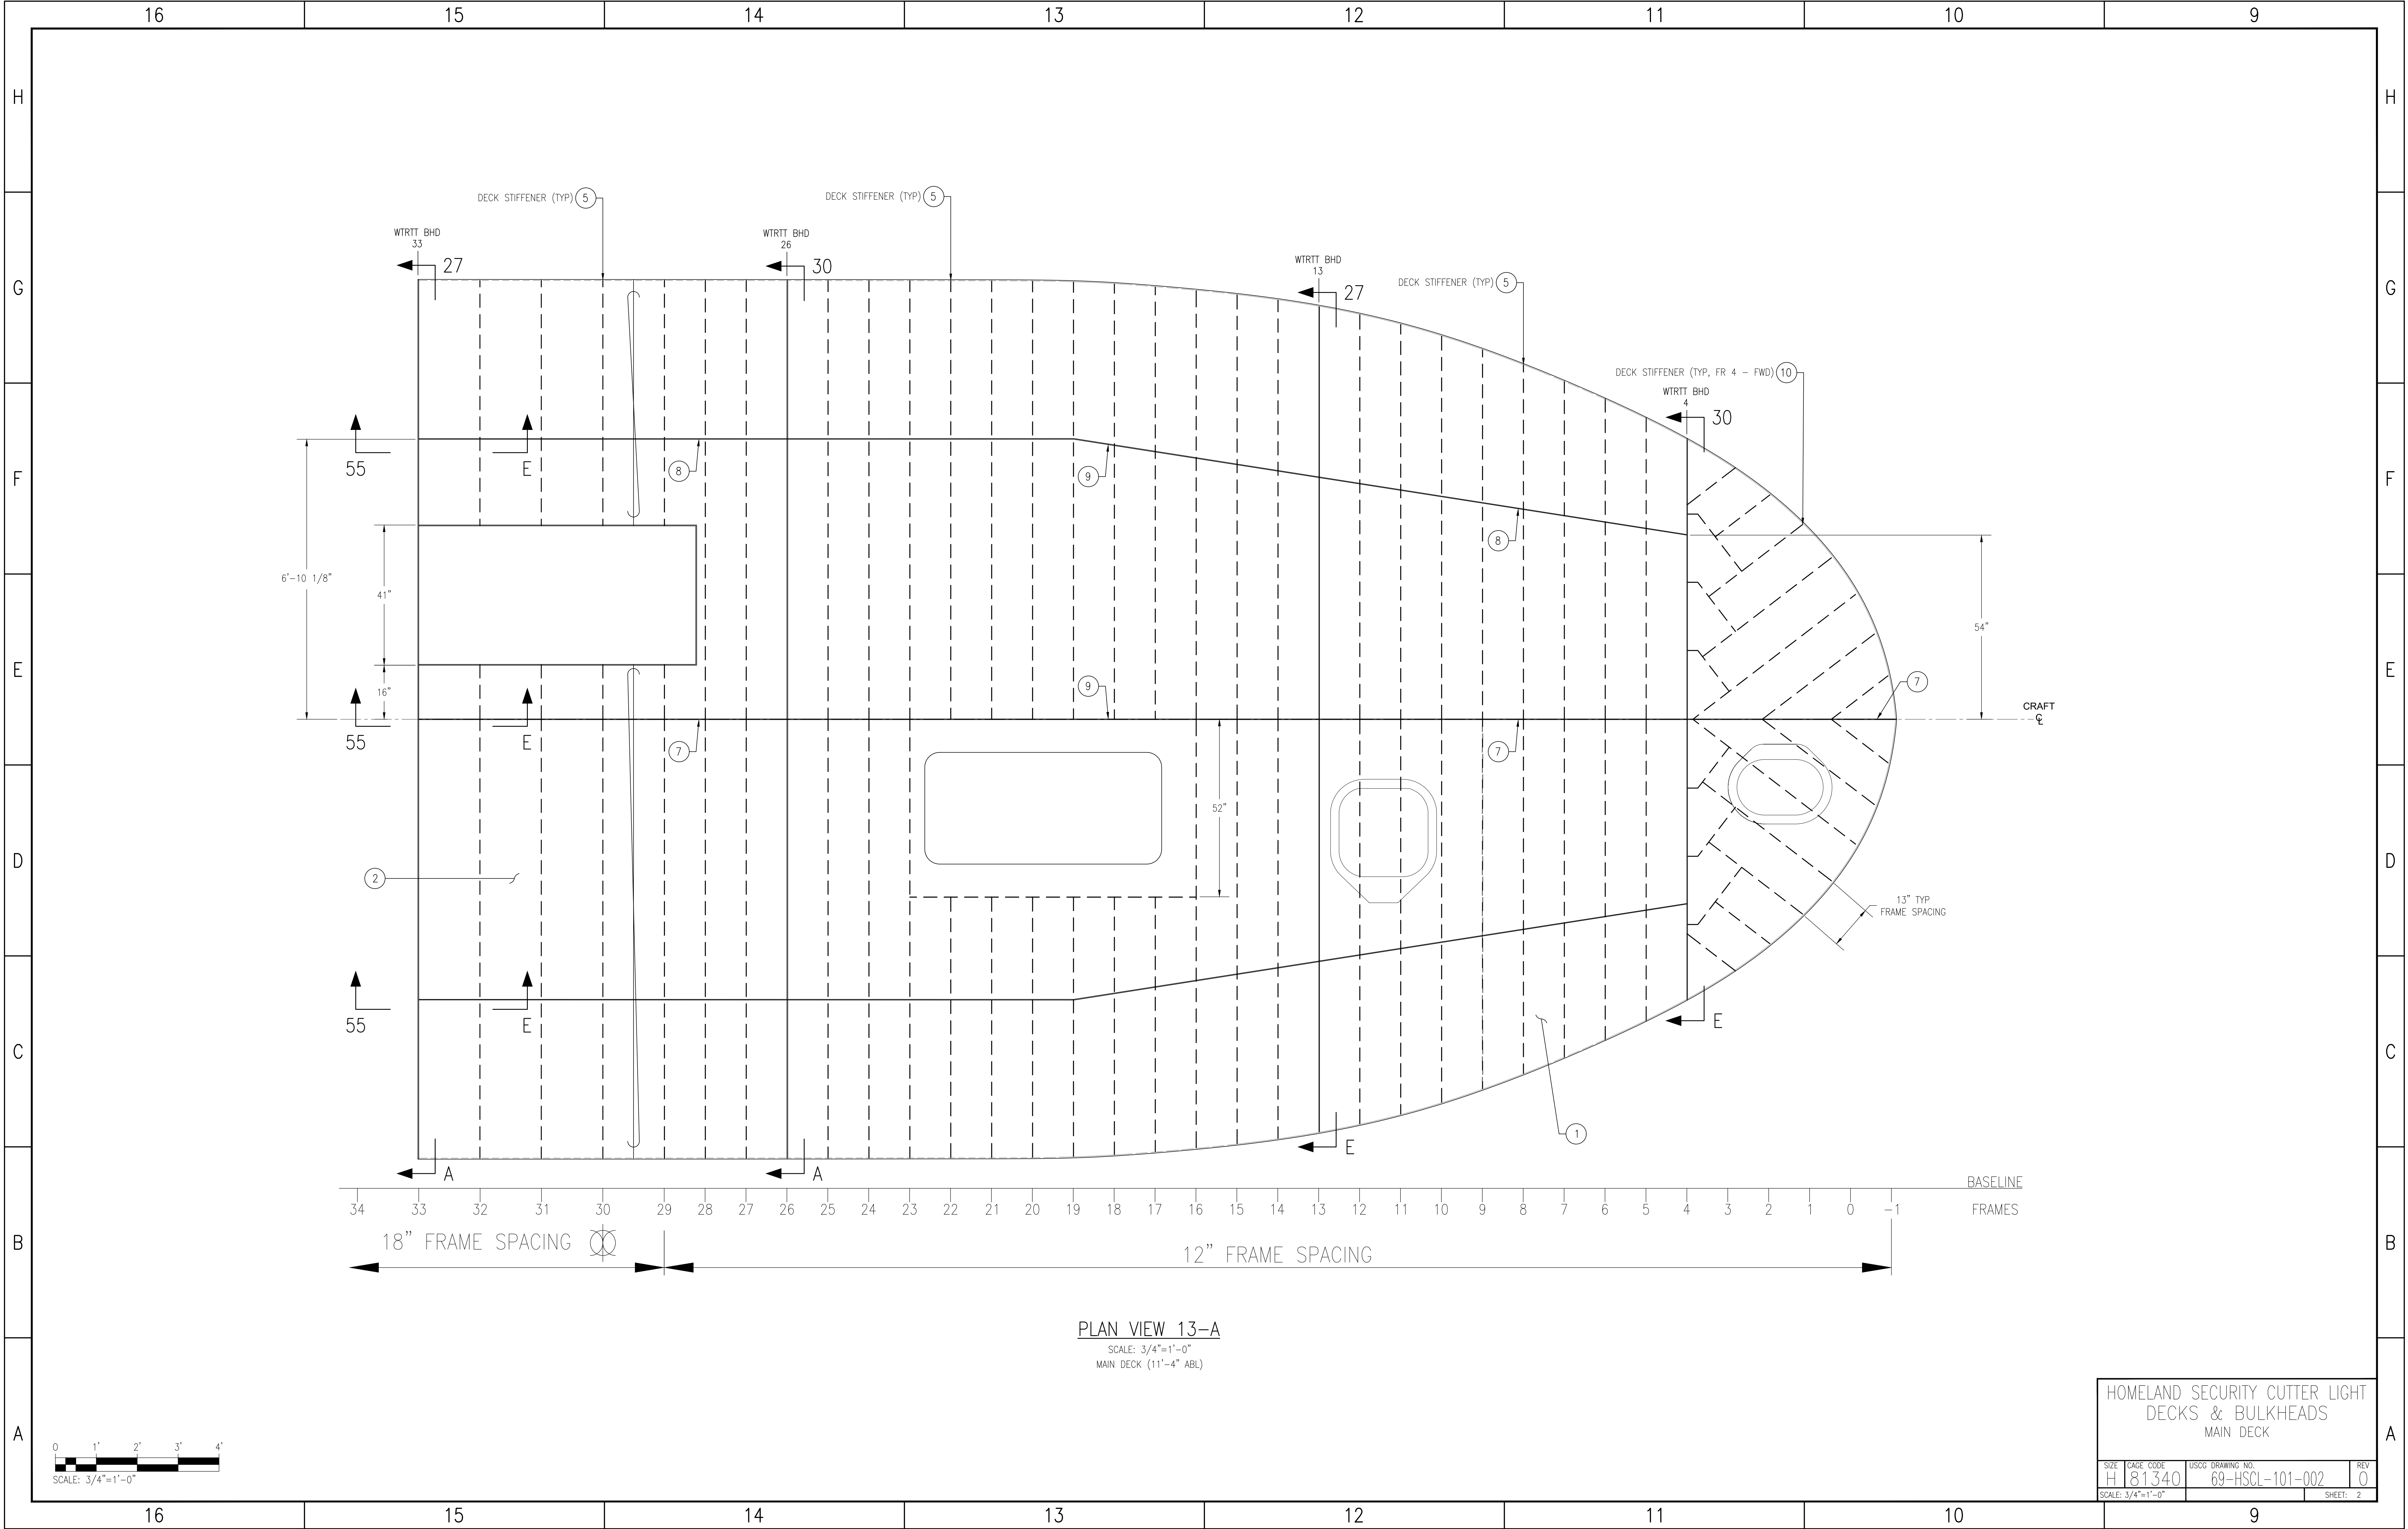


HOMELAND SECURITY CUTTER LIGHT DECKS & BULKHEADS MAIN DECK			
SIZE H 181340	CAGE CODE	USCG DRAWING NO. 69-HSCL-101-002	REV 0
SCALE: 3/4"=1'-0"		SHEET: 2	

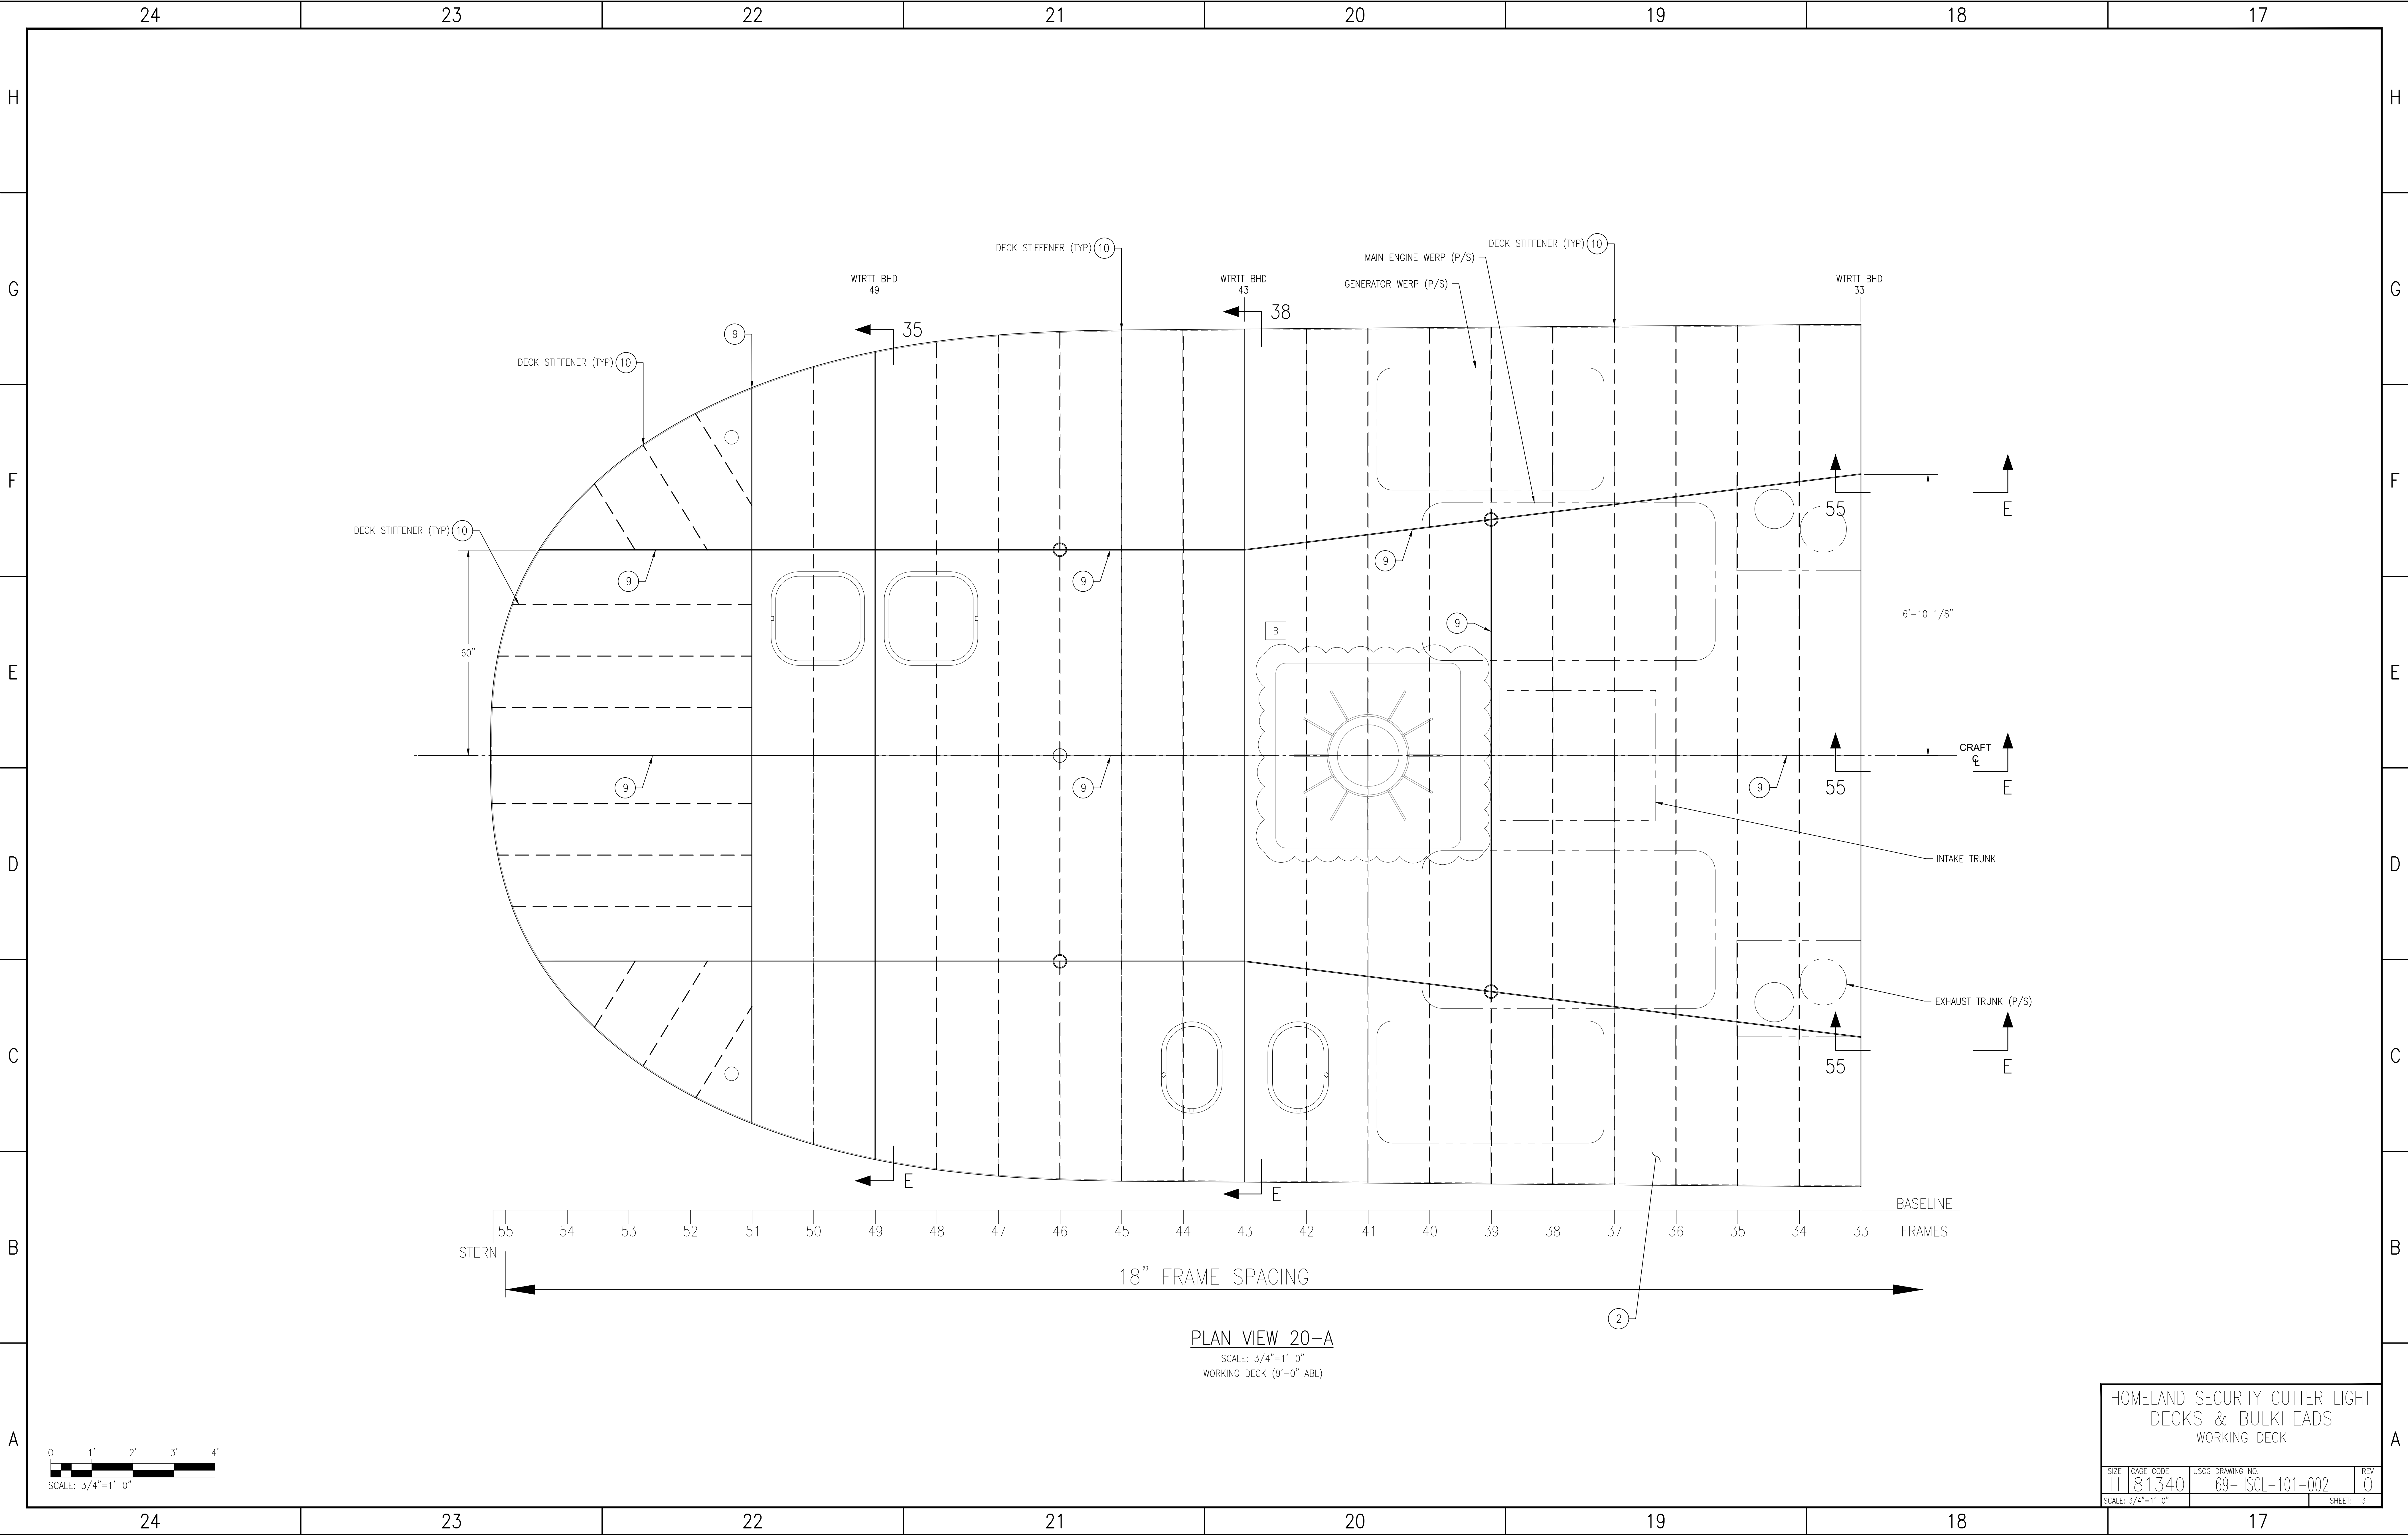



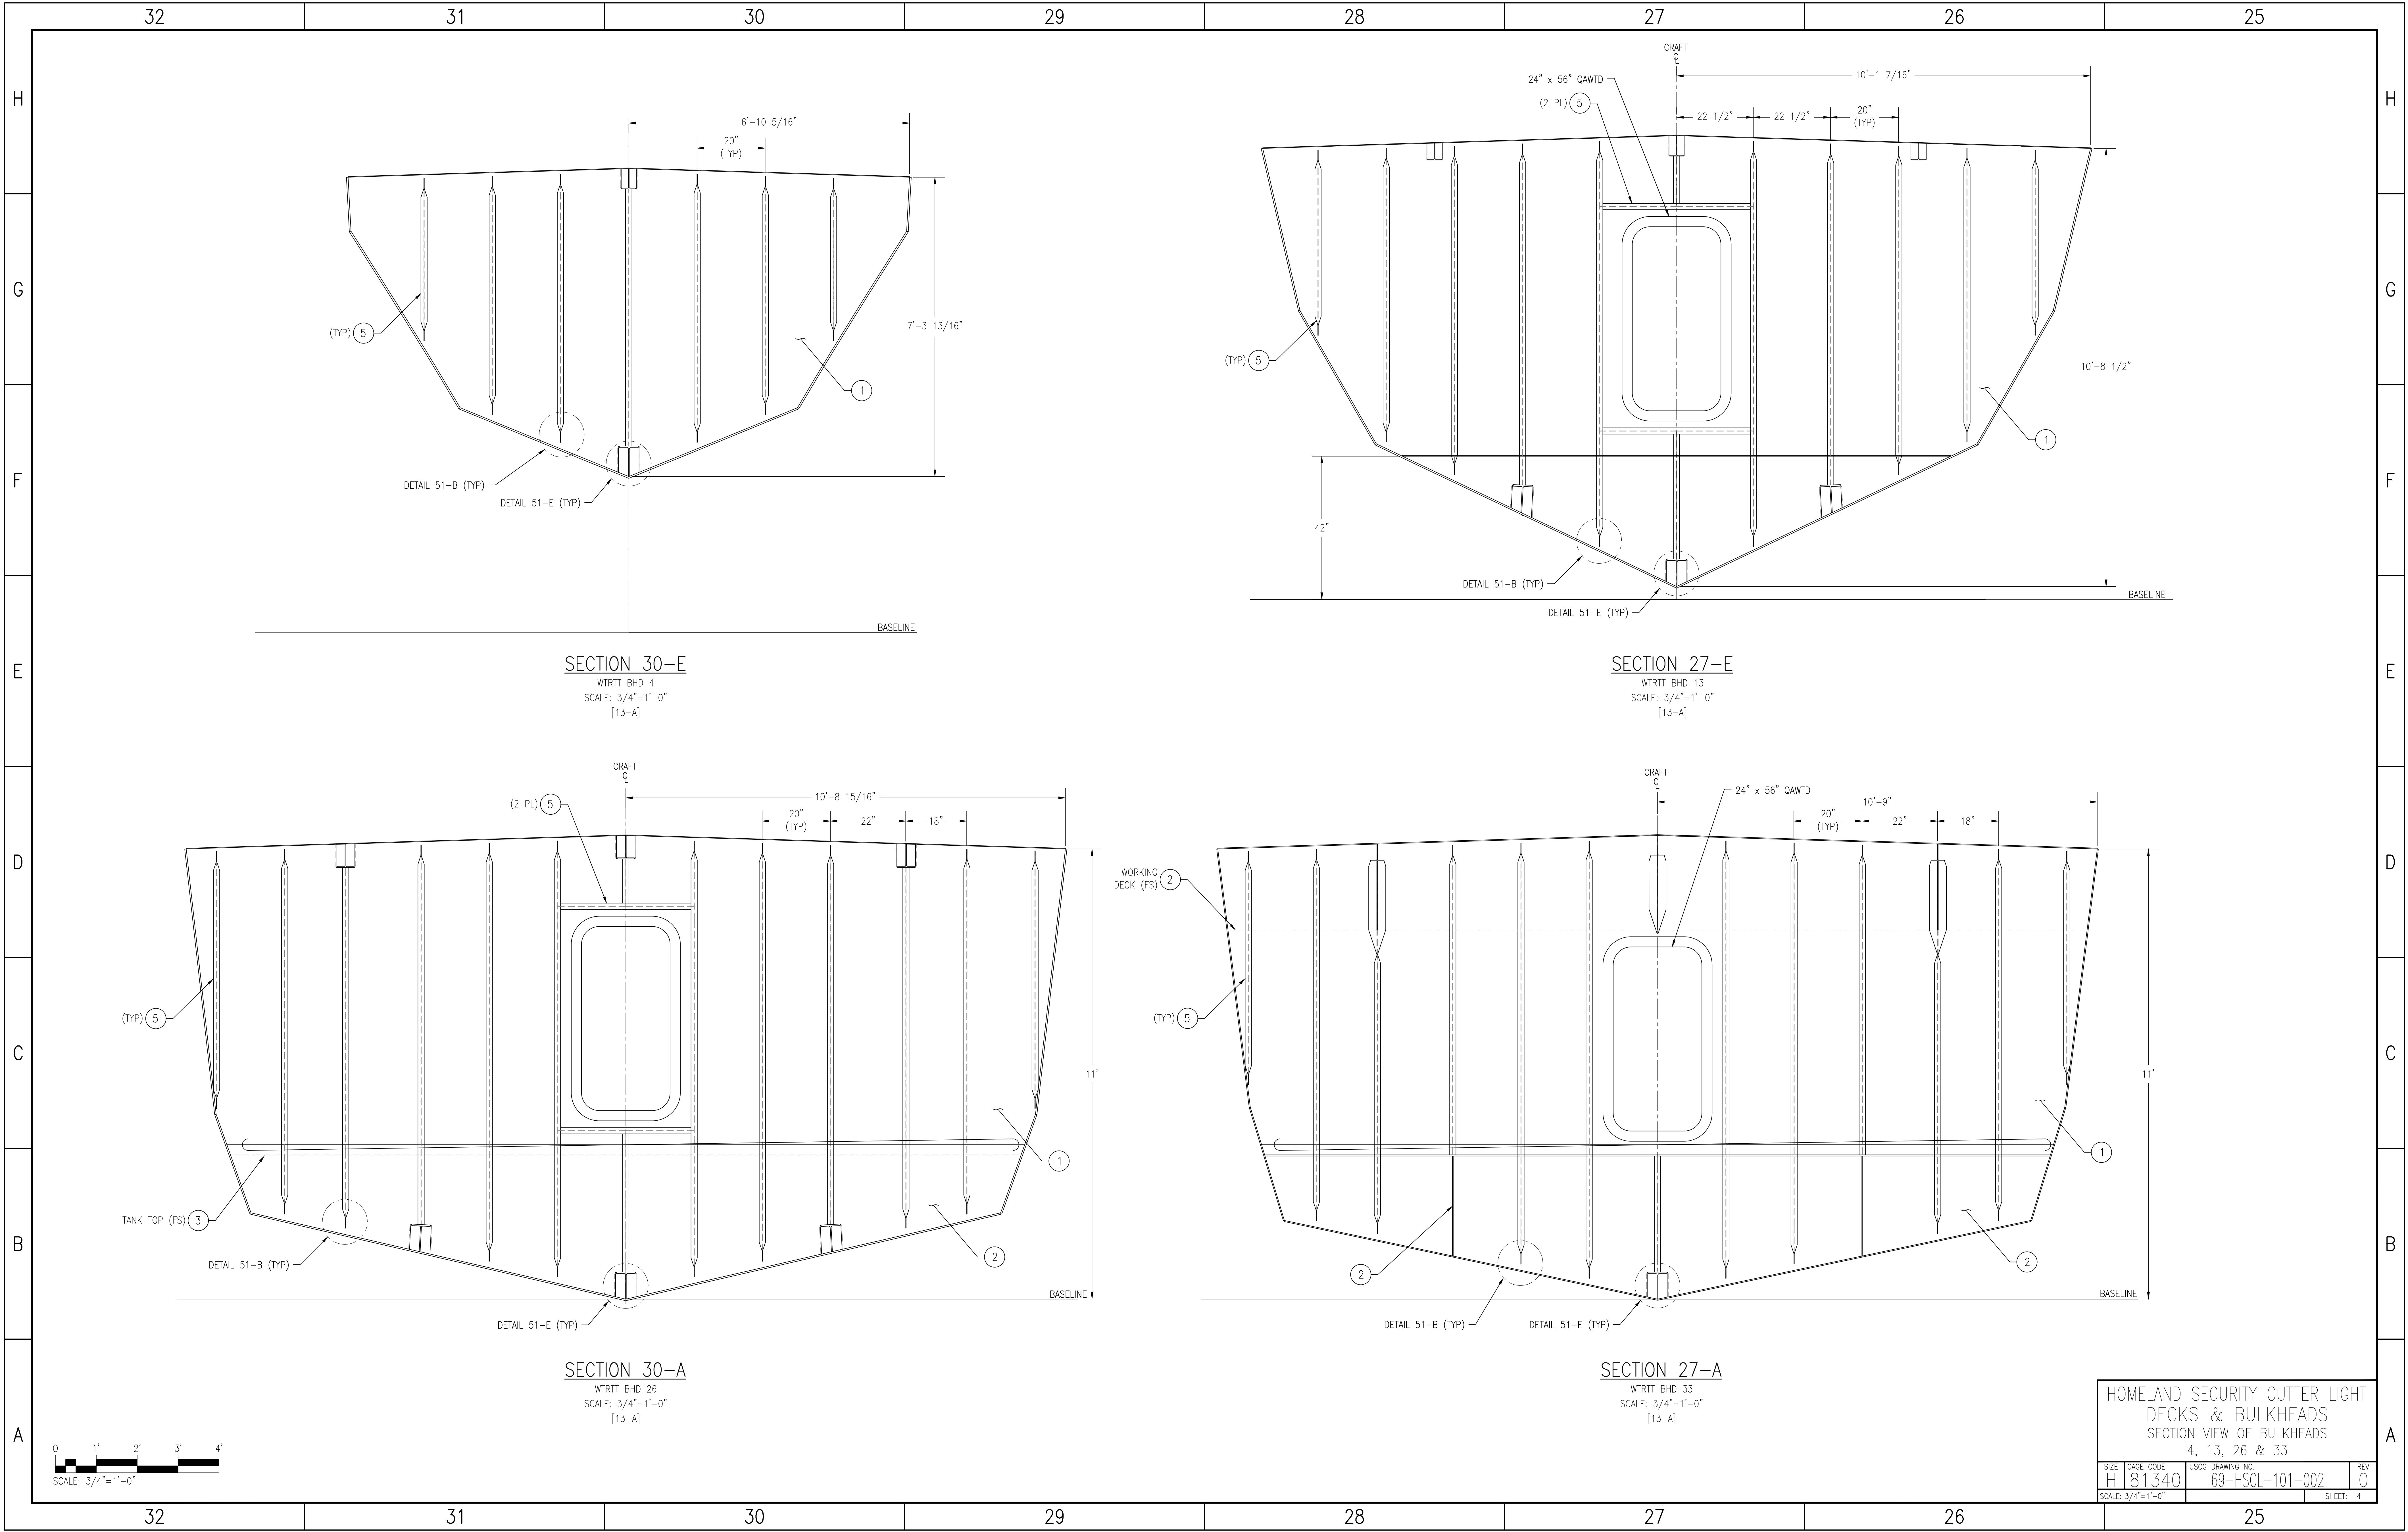


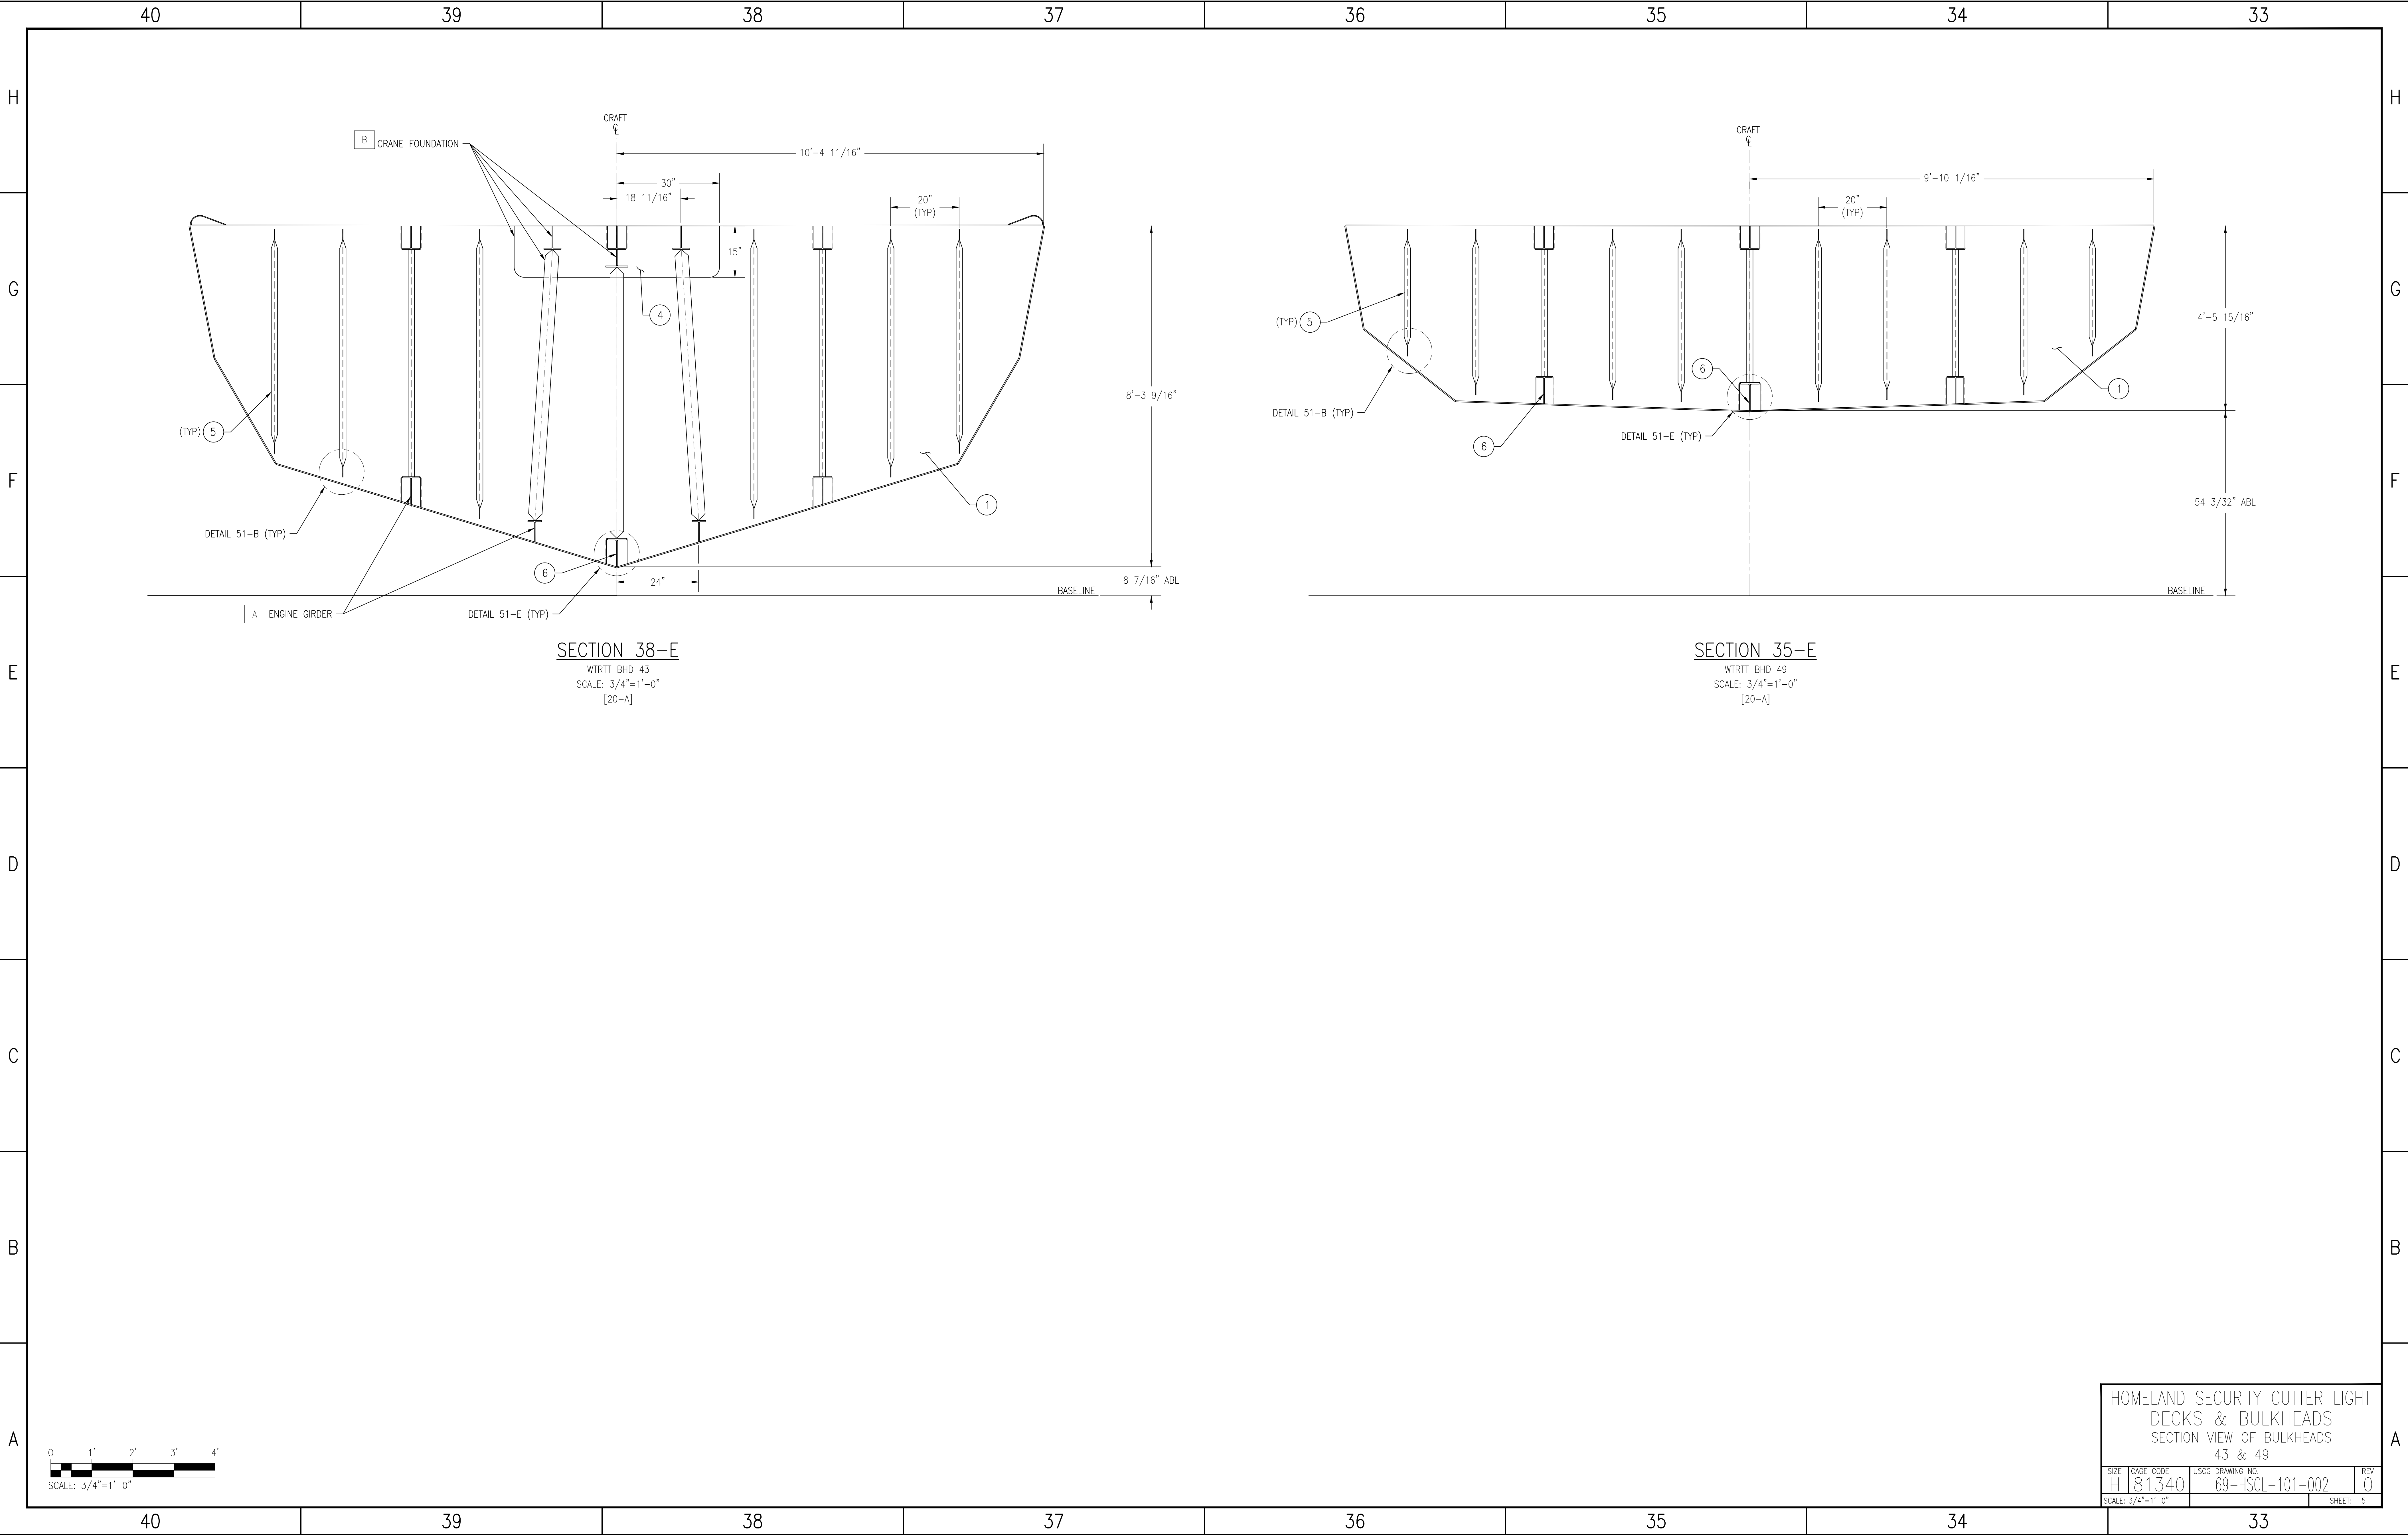

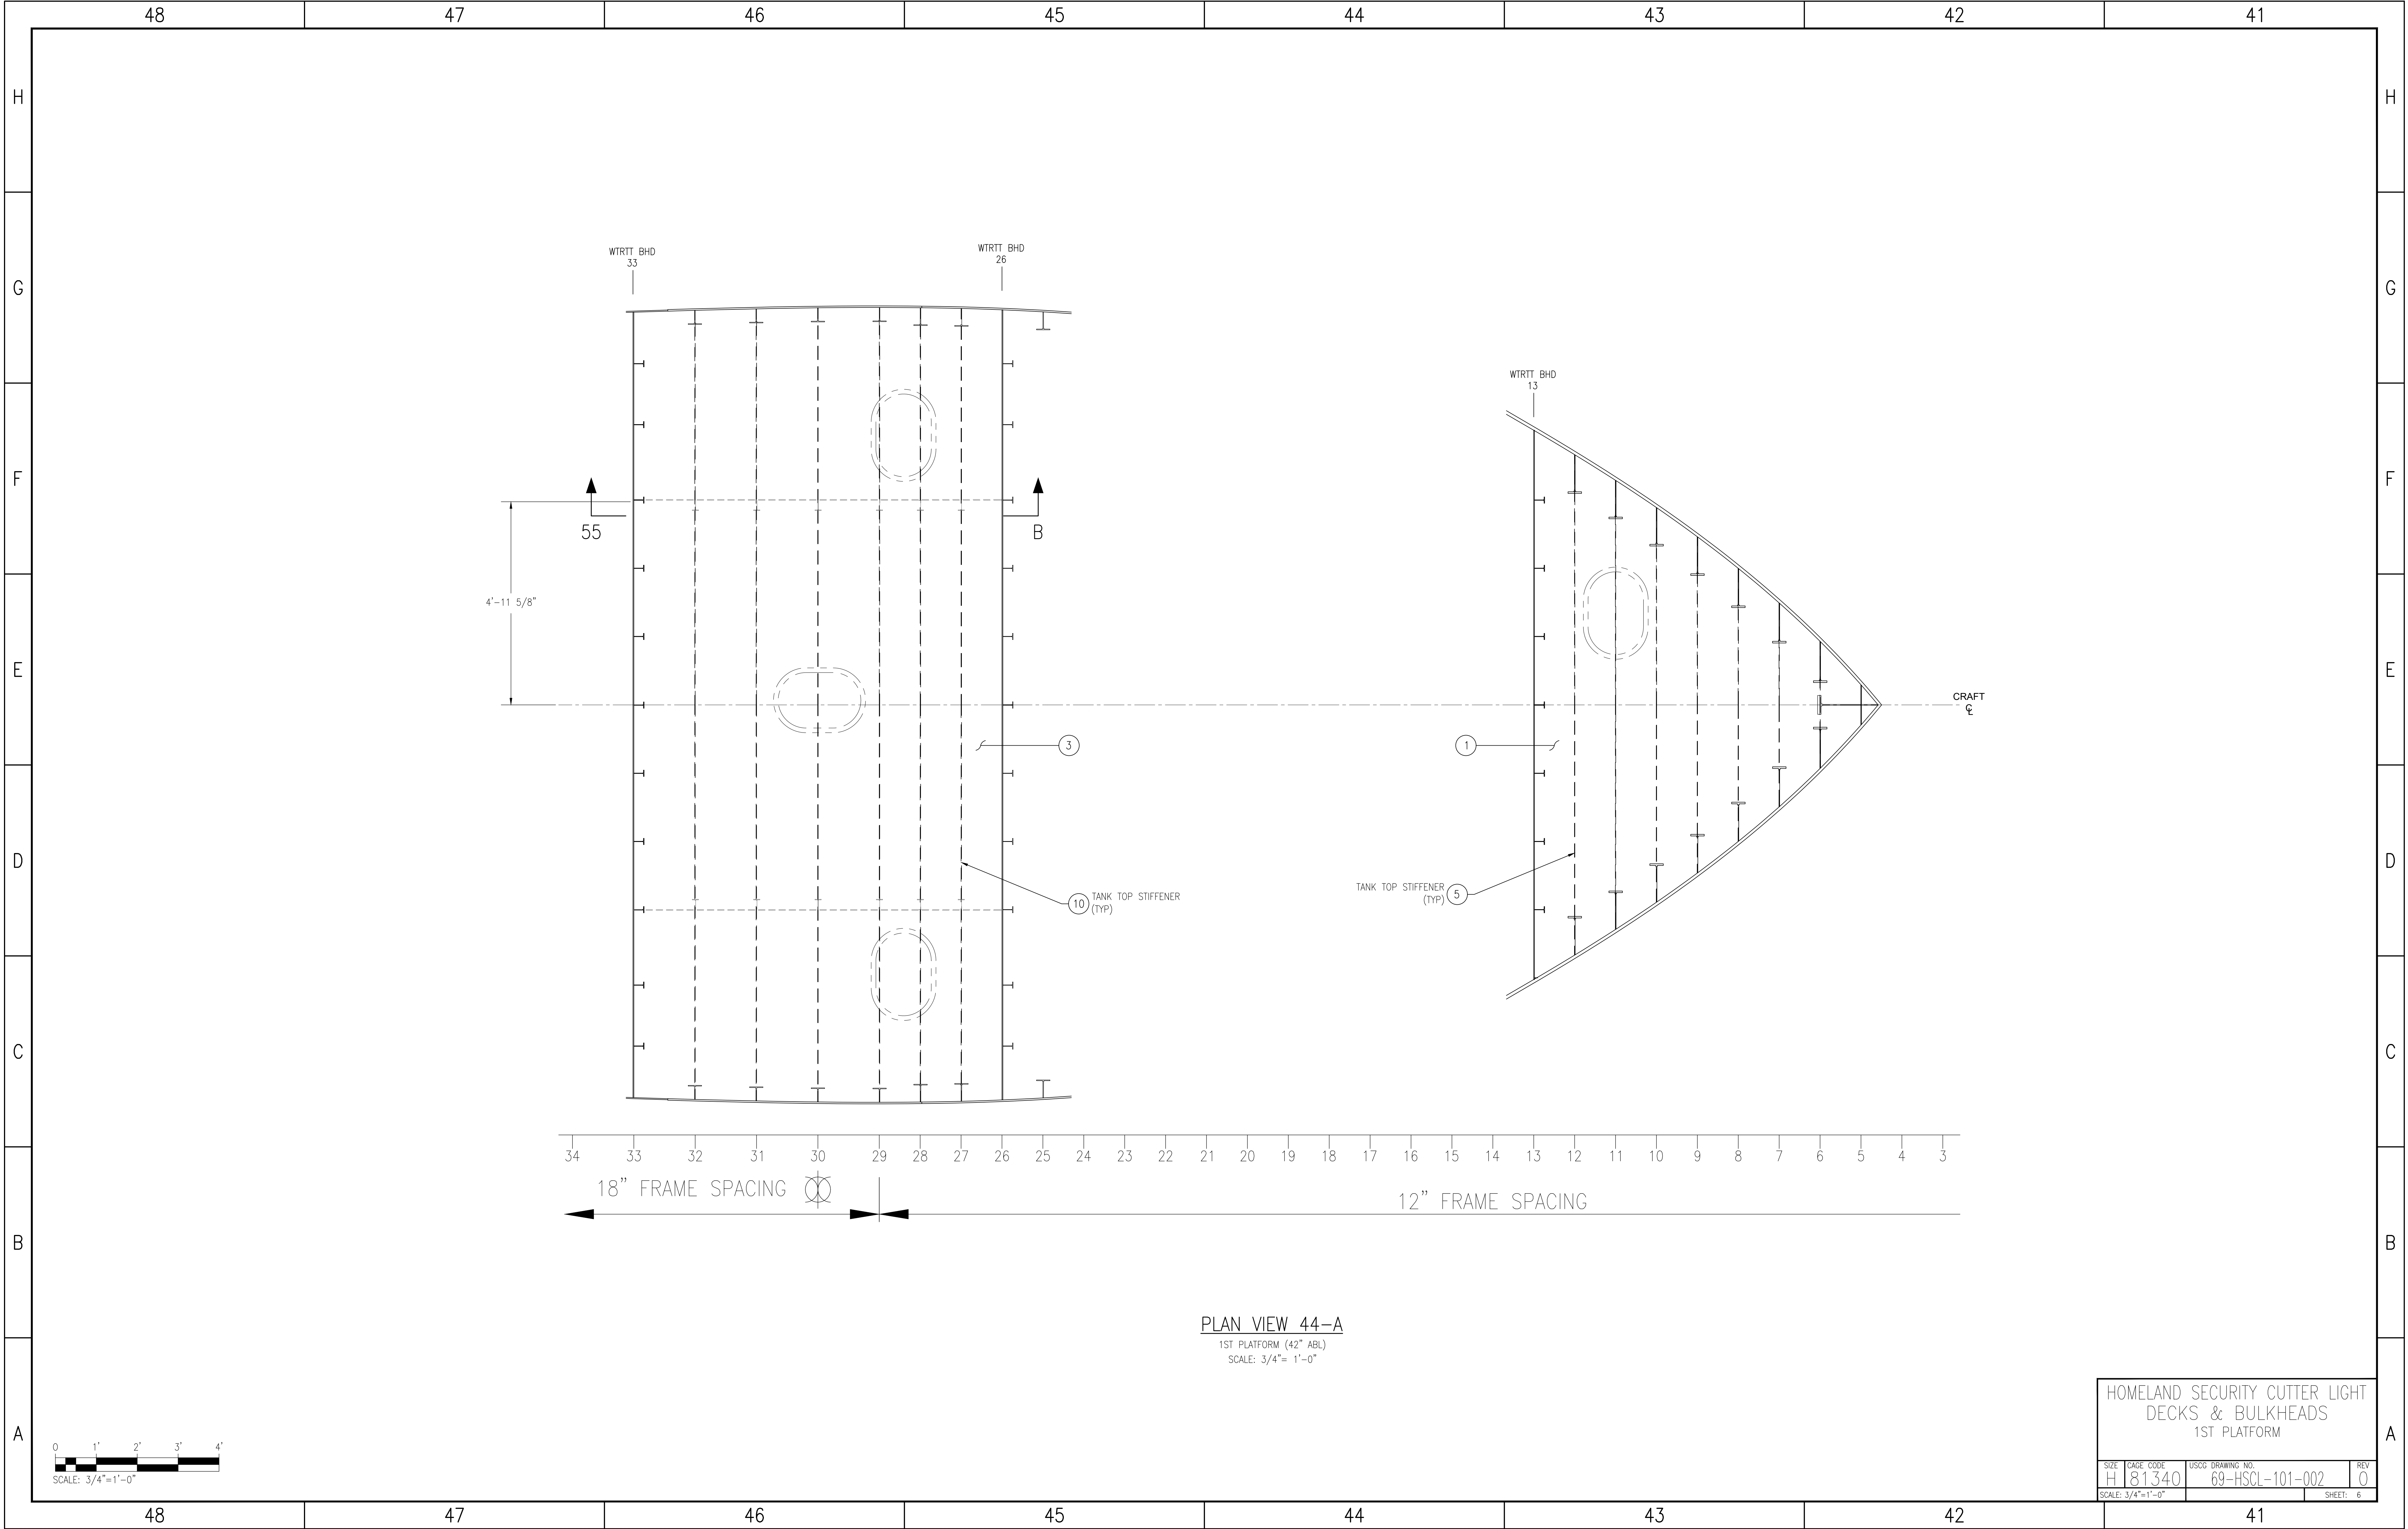

HOMELAND SECURITY CUTTER LIGHT
DECKS & BULKHEADS
1ST PLATFORM

SIZE	CAGE CODE	USCG DRAWING NO.	REV
H	81340	69-HSCL-101-002	0
SCALE: 3/4"=1'-0"			SHEET: 6

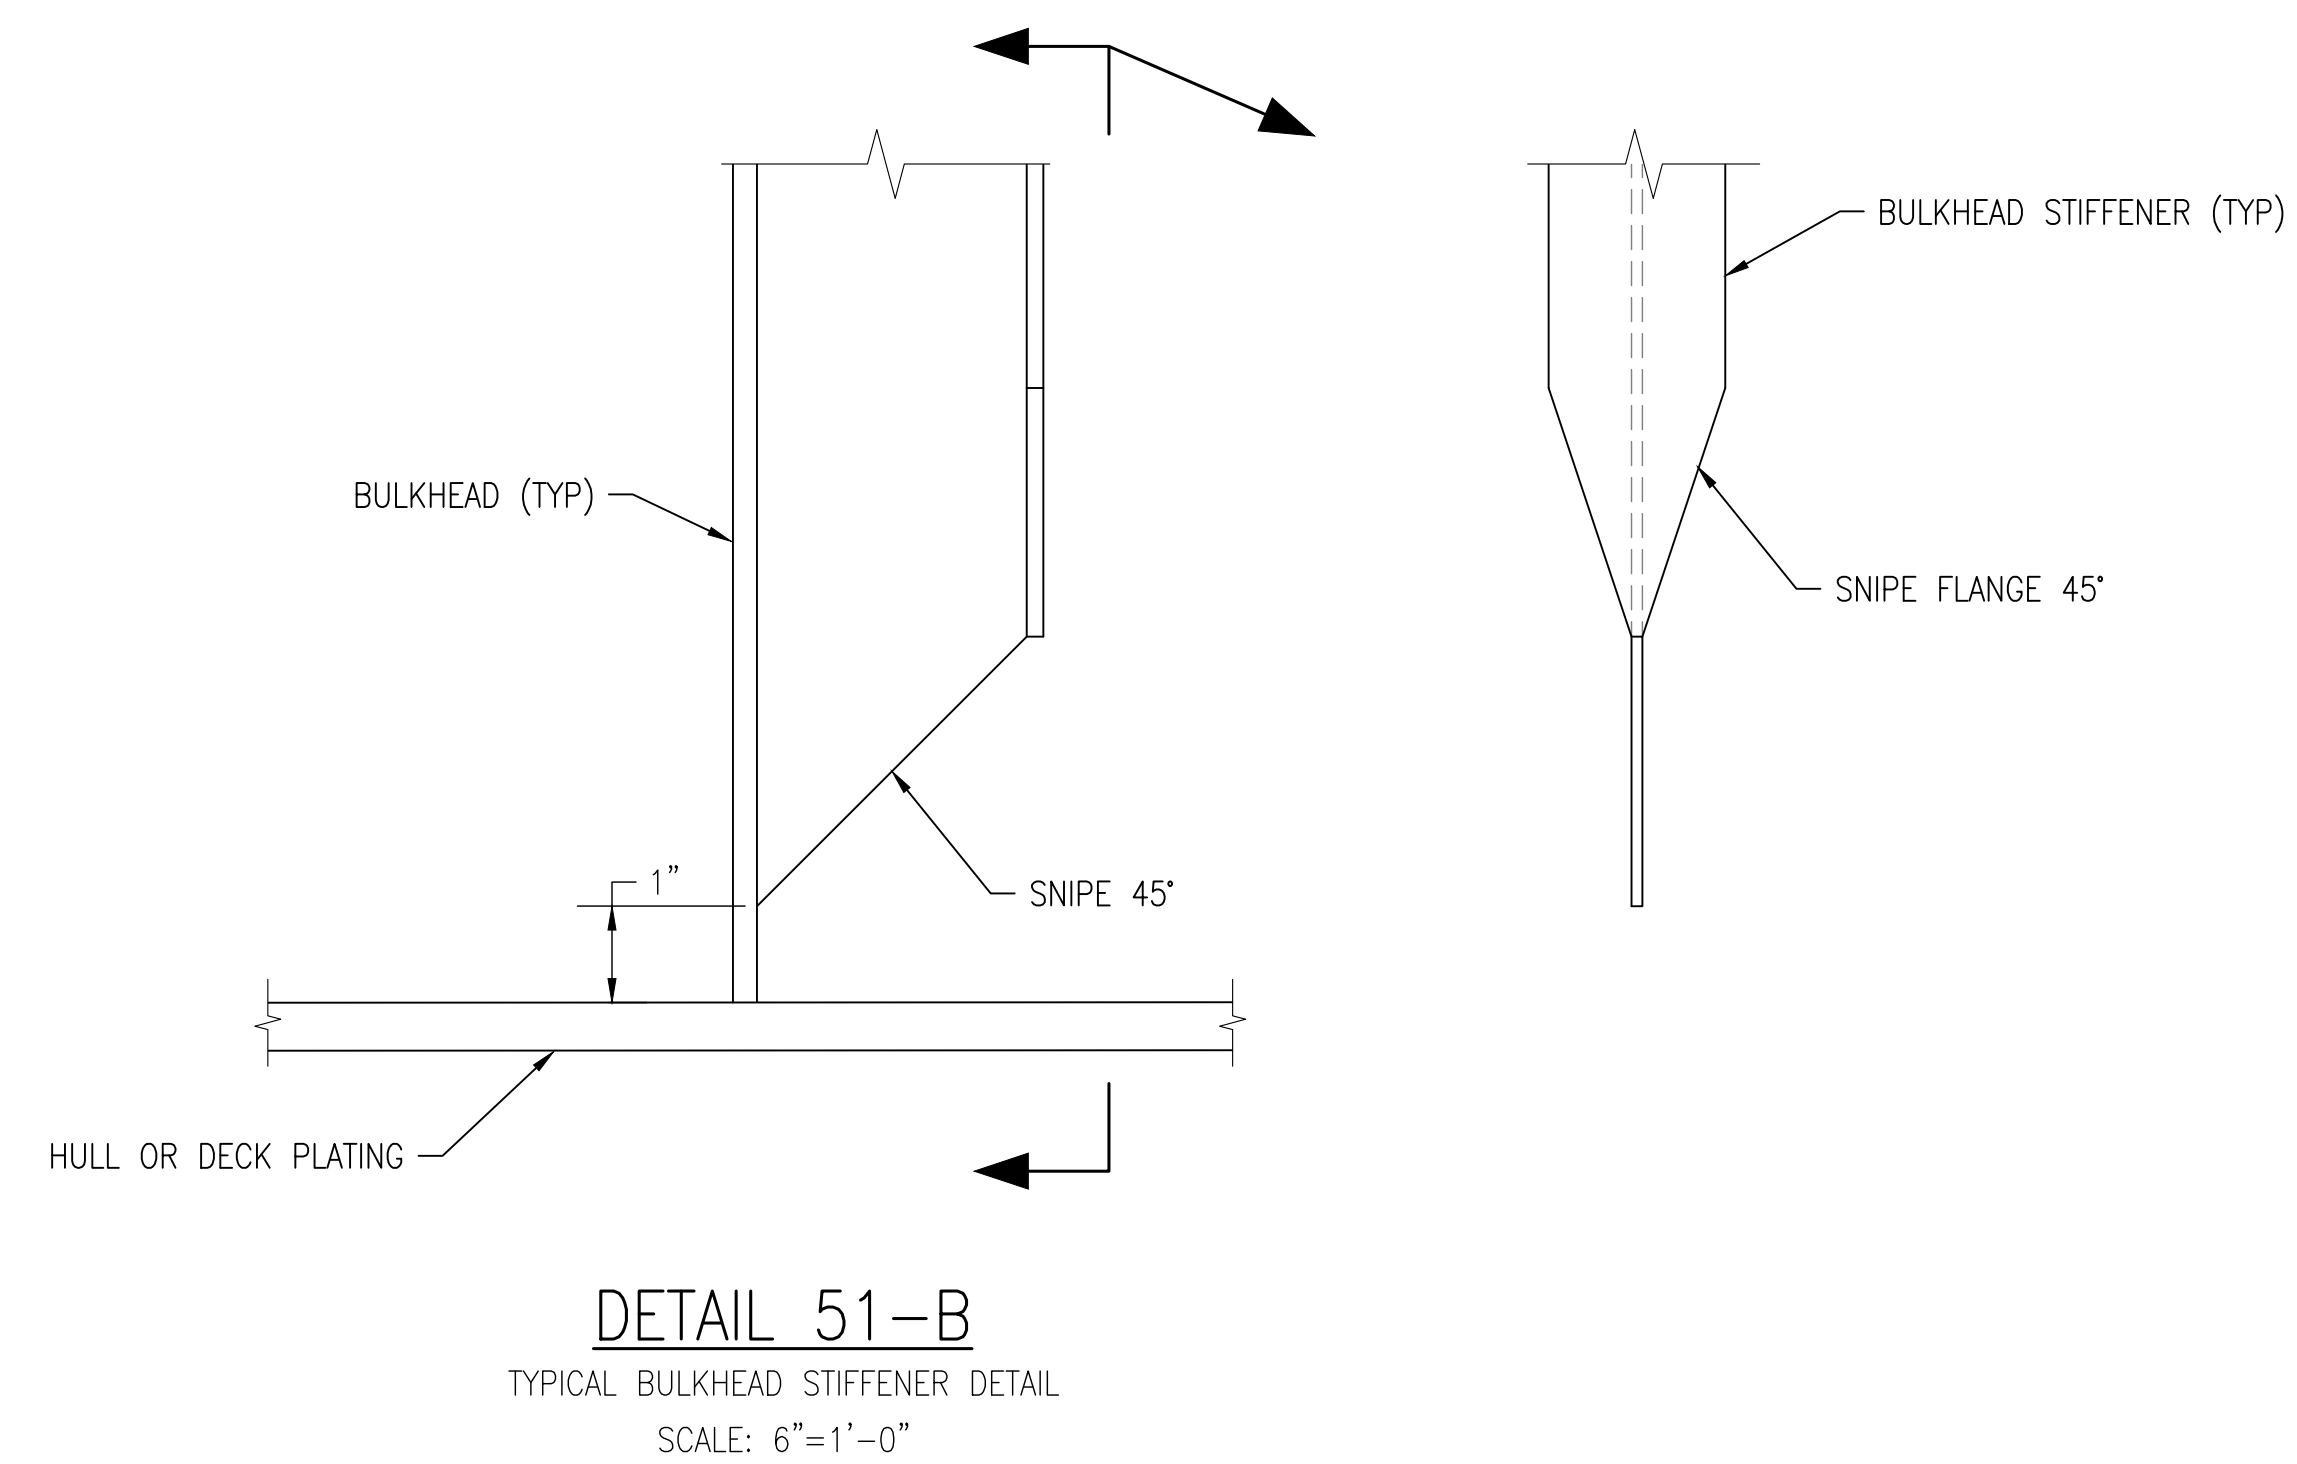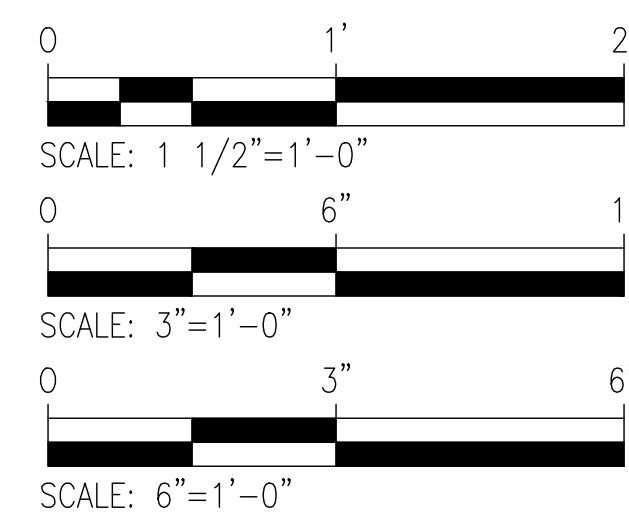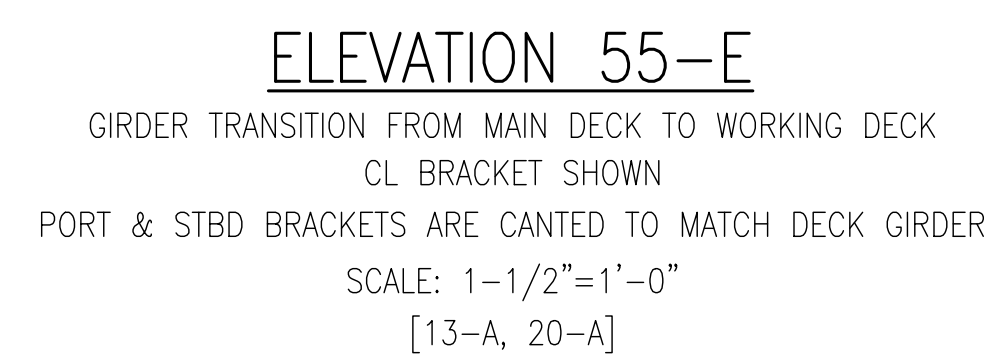

HOMELAND SECURITY CUTTER LIGHT DECKS & BULKHEADS ELEVATIONS & DETAILS				A
SIZE H	CAGE CODE 81340	USCG DRAWING NO. 69-HSC-101-002	REV 0	
SCALE: AS NOTED			SHEET: 7	