



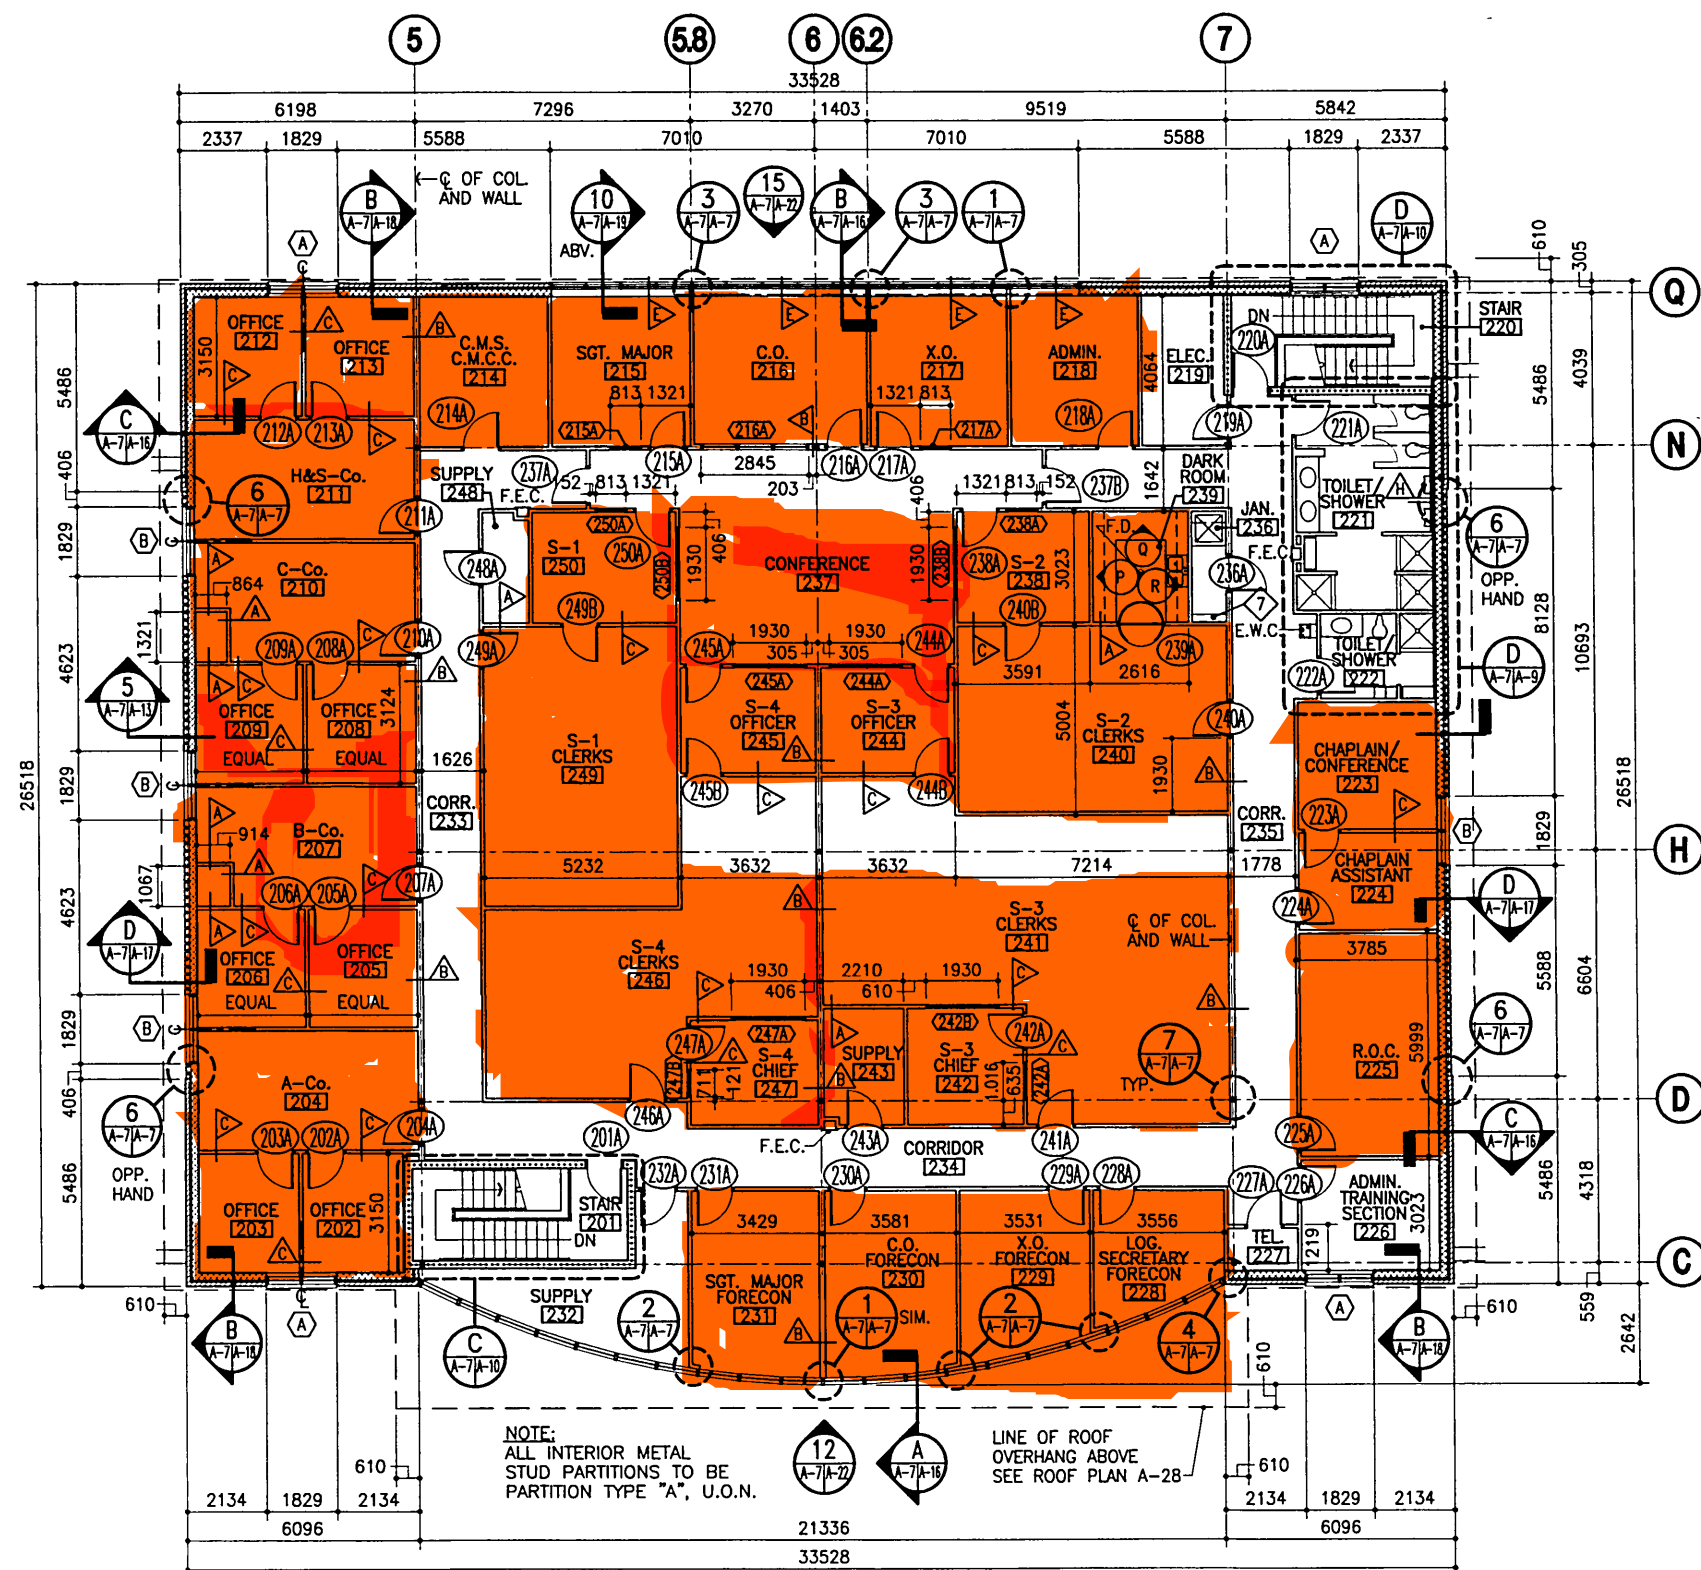

SECOND FLOOR PLAN - OPERATIONS BUILDING


1:100

NOTE: SEE SHEET A-30 FOR CASEWORK ELEVATIONS MARKED THUS

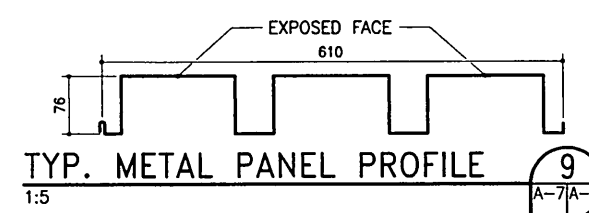


TYP. METAL PANEL PROFILE

1:5

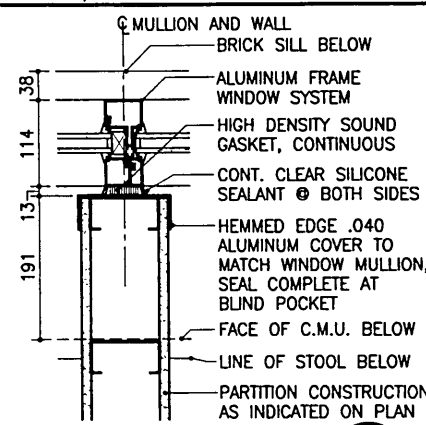


MULLION DETAIL 1

1:5

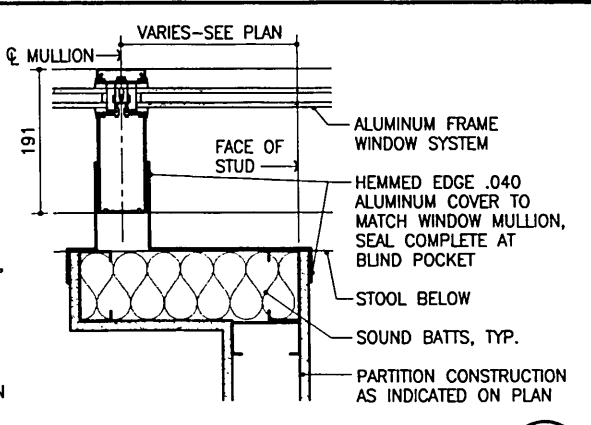


MULLION DETAIL 2

1:5

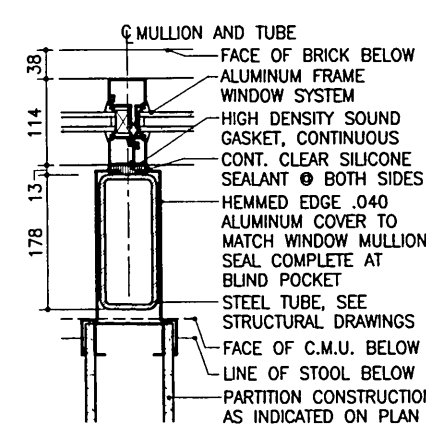


MULLION DETAIL 3

1:5

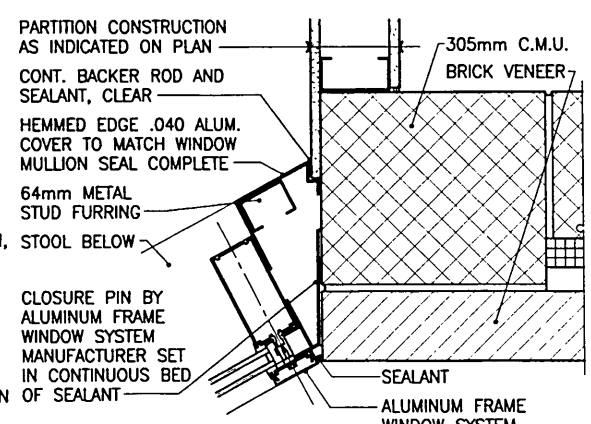


MULLION/JAMB DETAIL 4

1:5

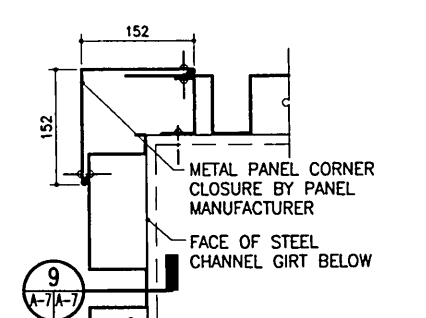


PANEL DETAIL TYP 5

1:5

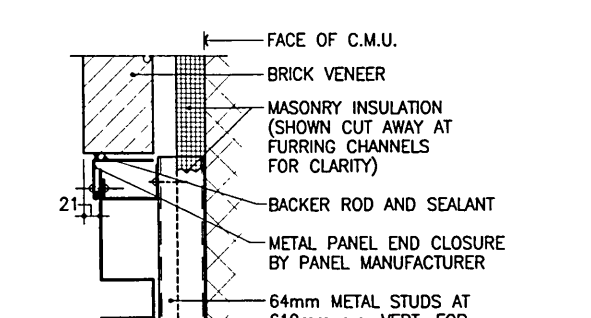


PANEL DETAIL 6

1:5

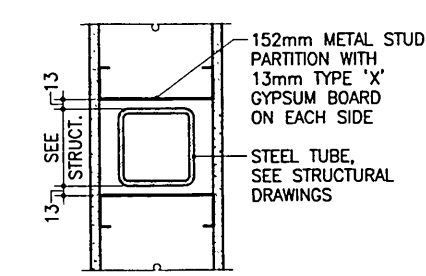

COLUMN DETAIL 7

1:5

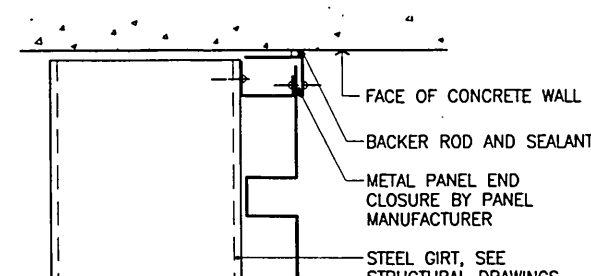

PANEL DETAIL 8

1:5



*ALL DIMENSIONS ARE MILLIMETERS (mm) UNLESS OTHERWISE NOTED

HARGROVE, BROCKWELL AND ASSOCIATES 207 BUSINESS PARK DRIVE SUITE 200 VIRGINIA BEACH, VIRGINIA 23462-5609 V.E. CONTRACT NO. 05-98-8024		WILLIAM H. HARGROVE, III REGISTERED ARCHITECT 03610 VIRGINIA BEACH, VIRGINIA	
NAVAL FACILITIES ENGINEERING COMMAND ATLANTIC DIVISION NAVAL STATION COURTHOUSE BAY, U.S. MARINE CORPS BASE CAMP LEJEUNE, NORTH CAROLINA		MAINTENANCE AND OPERATION FACILITY 2nd MARINE DIVISION RECON BATTALION OPERATIONS BUILDING SECOND FLOOR PLAN AND DETAILS	
CODE NO. 80091 SCALE: GRAPHIC STD. NO. 509666 STA. PROJ. NO. P-568 SPEC. NO. 05-98-8024 CONSTR. CONTR. NO. N62470-98-R-8024 NAVFAC DRAWING NO. 4409666	SHEET 53 OF 164 A-7	REVISIONS NO. DESCRIPTION DATE APPROVED 1 11-11-99 12/16/99	