

Amendment Purpose

1. Drawings and specifications revised in response to Pre-Proposal Inquiries.

Drawing Revisions

The following drawings are revised as of 4/10/2026 and accompany this Amendment.

DRAWING NO.	REVISION NO.	NAVFAC DWG NO.	TITLE
G-002	1	12940906	ABBREVIATIONS AND DRAWING INDEX
CD100	1	12940913	DEMO PLAN NORTH
CD101	1	12940914	DEMO PLAN SOUTH
EC100	1	12940915	EPSC PLAN NORTH
EC101	1	12940916	EPSC PLAN SOUTH
CS100	1	12940918	SITE PLAN NORTH
CS101	1	12940919	SITE PLAN SOUTH
C-500	1	12940921	CHAIN LINK FENCE AND DETAIL
C-501	1	12940922	TYPICAL PERSONNEL GATE AND BOLLARD DETAIL
C-502	1	12940923	TYPICAL CABLE REINFORCED CHAIN-LINK FENCE GATE, CABLE REINFORCING AND JOINT SEALANT DETAILS

On NAVFAC Dwg. No. 12940906 (G-002)

G-002: Title changes to Drawing Index.

On NAVFAC Dwg. No. 12940913 (CD100)

CD100: Deleted new work fence layer from demolition plan.

On NAVFAC Dwg. No. 12940914 (CD101)

CD101: Deleted new work fence layer from demolition plan.

On NAVFAC Dwg. No. 12940915 (EC100)

EC100: Revised construction entrance location. Added 12' double leaf swing gate. Added (2) stockpile areas. Shifted drawing viewport.

On NAVFAC Dwg. No. 12940916 (EC101)

EC101: Shifted drawing viewport. No other revisions.

On NAVFAC Dwg. No. 12940918 (CS100)

CS-100: Revised construction entrance location. Added detail call out B1/C-501.

Keynote #1:

Removed keynote #1 from sheet and renumbered subsequent keynotes.

On NAVFAC Dwg. No. 12940919 (CS101)

Keynote #1:

Deleted keynote #1 from sheet and renumbered subsequent keynotes.

On NAVFAC Dwg. No. 12940921 (C-500)

D1/C-100:

Revised notes on detail D1/C-500. Added double swing gate detail C1/C-500

On NAVFAC Dwg. No. 12940922 (C-501)

B1/C-501

Revised detail B1/C-501 to show flowable grout location. Revised berm slope on C1/C-501.

On NAVFAC Dwg. No. 12940923 (C-502)

C-502 Addition of details.

Specification Revisions

The following specifications have been revised as of 4/10/2026.

01 14 00 – Work Restrictions

1.3. Special Scheduling Requirements subpart a – ADD - “The contractor will have full access to the site. Government fueling operations are not anticipated to impede construction work at the Berm.”

01 32 17.00 20 – Cost-Loaded Network Analysis Schedules (NAS)

1.9. Designated Project Scheduler: ADD – “The Project Manager may also serve as the Designated Project Scheduler as long as the Project Manager meets the qualification requirements stated subpart 1.9.1.”

01 50 00 – Temporary Construction Facilities and Controls

2.3 Fencing: DELETE Section 2.3 Fencing

01 57 19 – Temporary Environmental Controls

1.3 Submittals: DELETE – “Stormwater Pollution Prevention Plan (SWPPP); G”

1.5.1.1.5.3.1: Contractor Site Custodian: **ADD** – “The QC/SSHO manager or superintendent may serve as the site custodian and must meet the requirements stated in 1.5.1.1.5.3.1.b.”

1.5.1.1.3. Virginia Stormwater Management: **DELETE** Sections, 1.5.1.1.3 Virginia Stormwater Management , 1.5.1.1.3.1 Stormwater General Permit for Construction Activities Registration Statement, and 1.5.1.1.3.2 Stormwater General Permit Inspection Reports in their entirety.

1.6.4 Environmental Manager: **ADD** – “The QC/SSHO manager or superintendent may serve as Environmental Manager.”

1.7.9.1 Haul Route: **ADD** – “The haul route must be kept clean of dirt and debris at all times. At a minimum, any tracked sediment on public roads must be cleaned by the end of each workday.”

Specification Deletions

The following specifications have been deleted as of 4/10/2026 per this Amendment.

01 32 16.00 20 – Small Project Construction Progress Schedule

-- End of Amendment --

FILE NAME: P:\Projects\2024\21297-24020 NAVFAC Midant LP-38 Berm Recert\510-COU\510-Arch\WD\A-DWG\1766586-G-002.dwg PLOTTED: Thursday, April 09, 2026 - 10:02am USER: emore

D

C

B

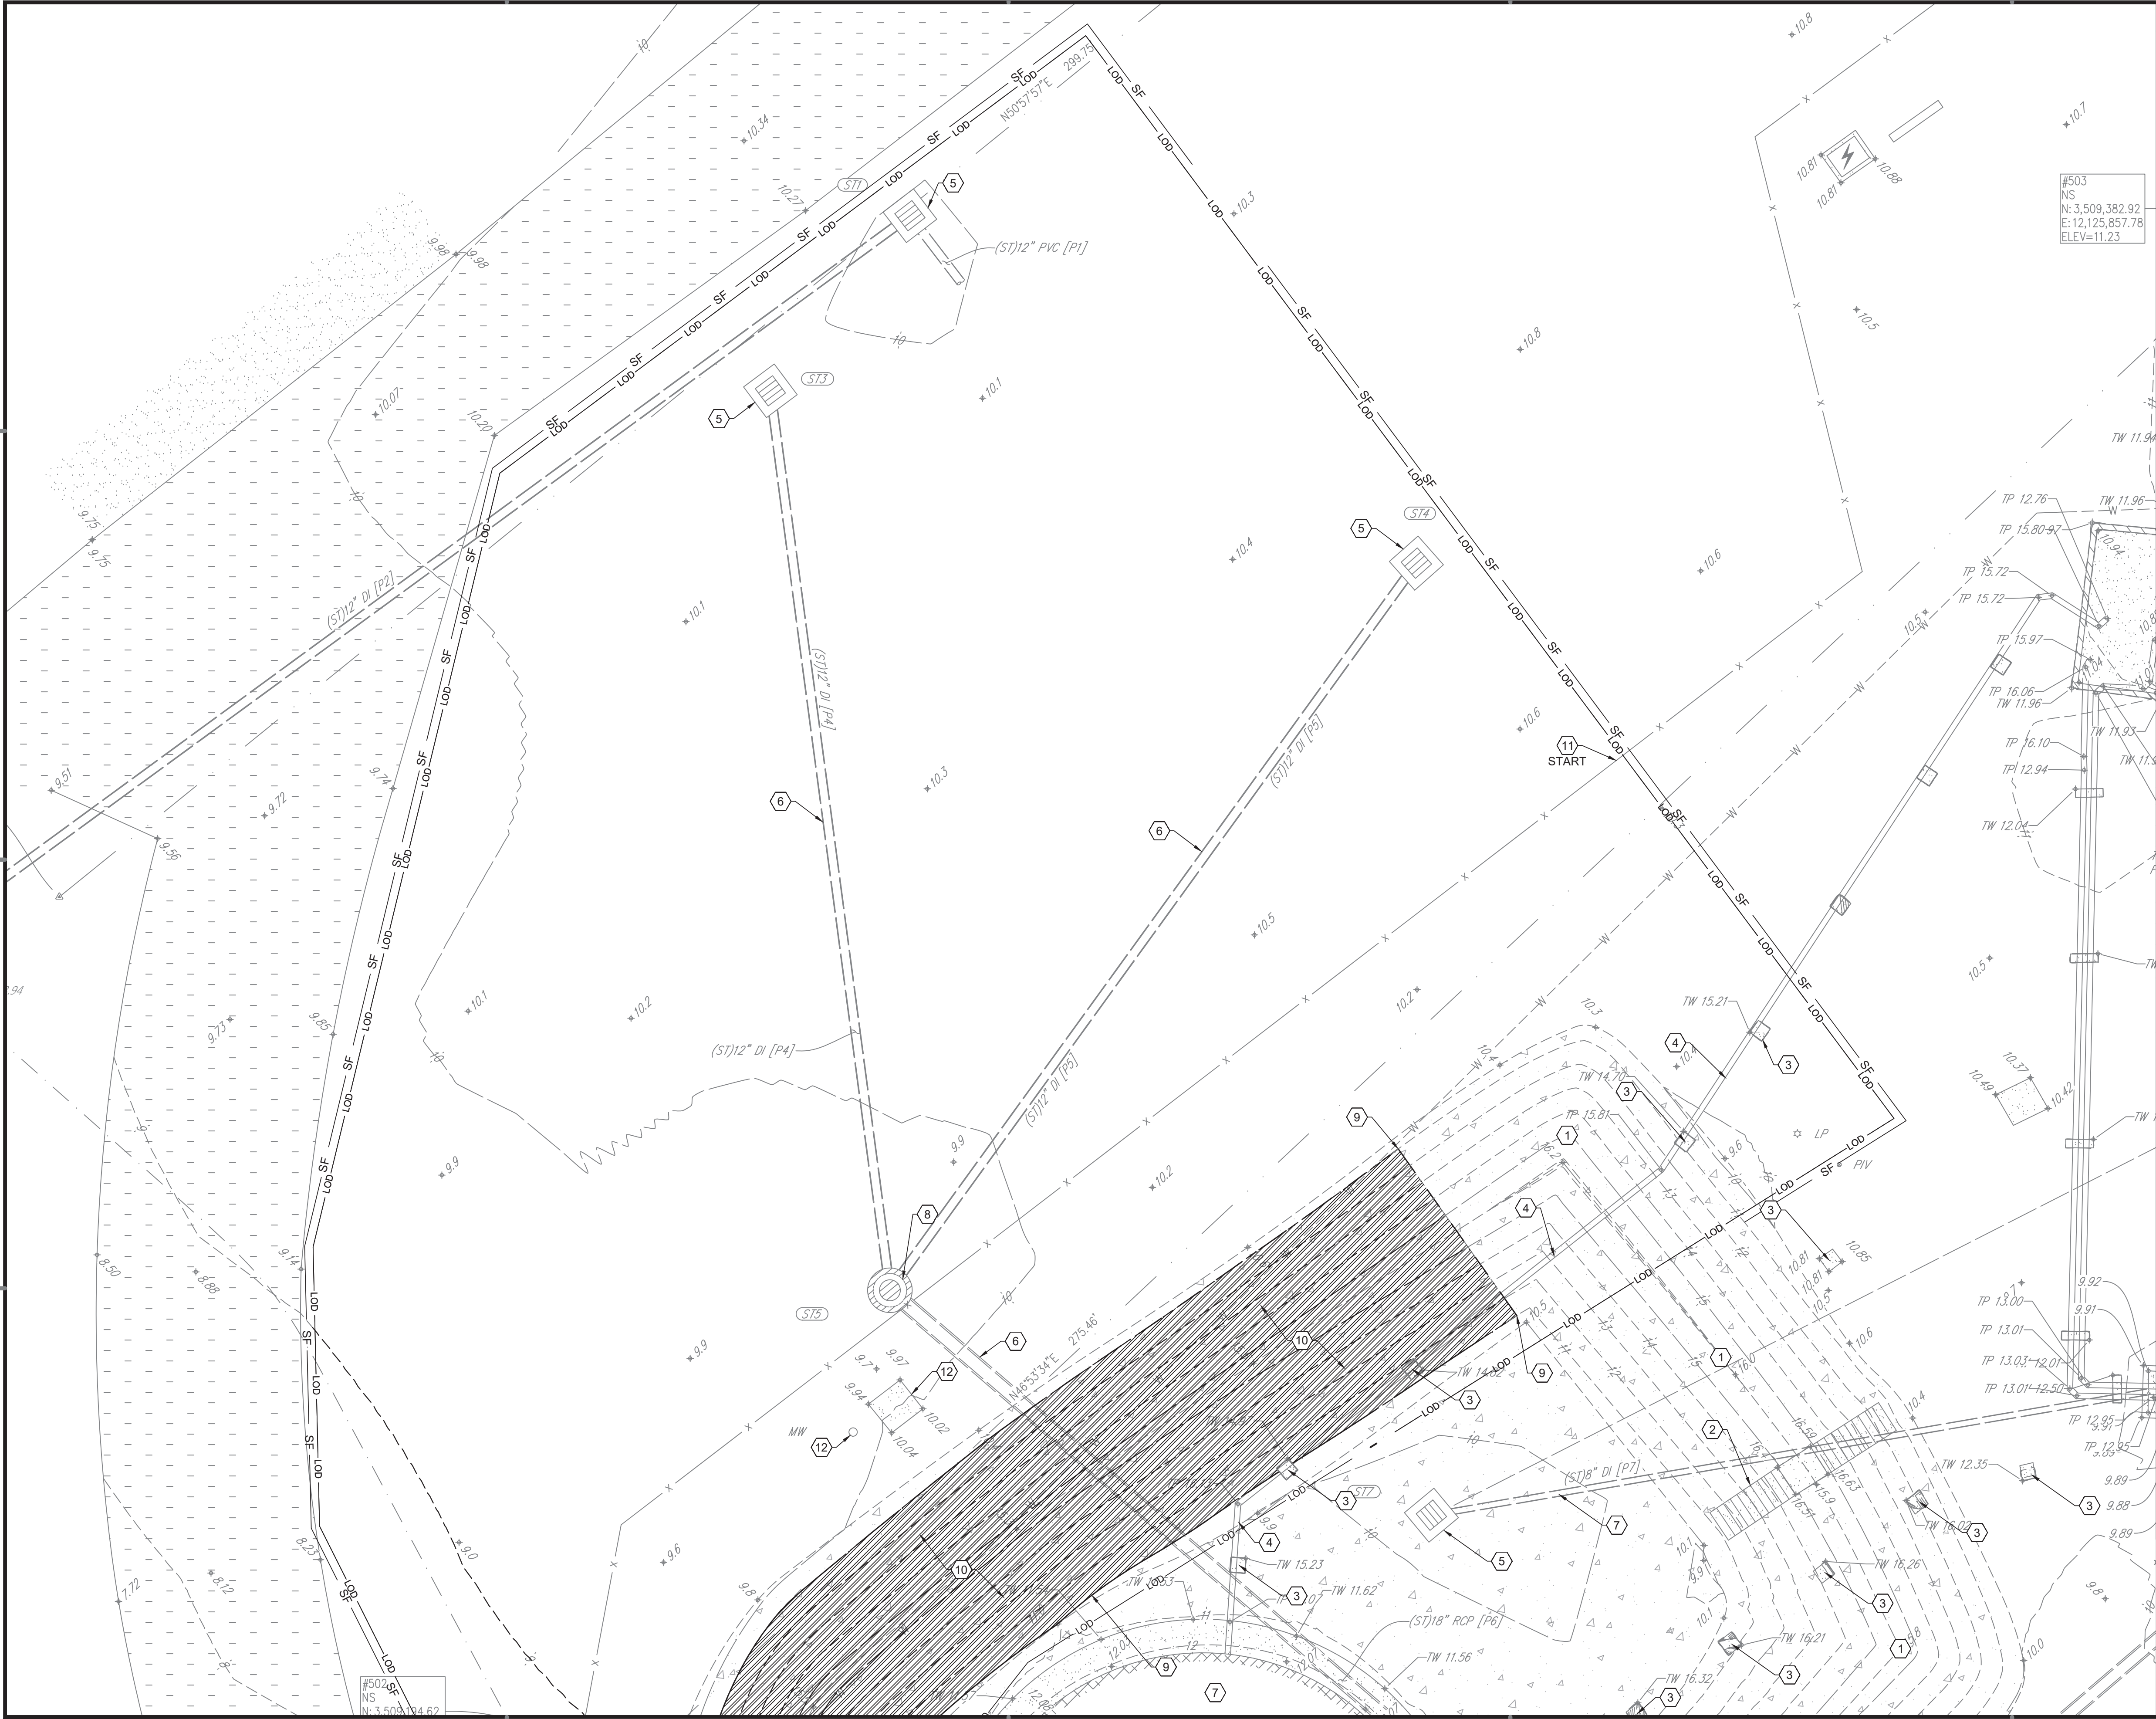
A

ABBREVIATIONS

L	ANGLE	CS	CAST STONE	FR	FRAME	LPL	LIGHTPROOF LOUVER
A/C	AIR CONDITIONING	CSK	COUNTERSUNK	FRG	FORGED	LPT	LOW POINT
AB	ANCHOR BOLT	CSMT	CASEMENT	FRMG	FRAMING	LR	LIVING ROOM
ABV	ABOVE	CT	CERAMIC TILE	FRT	FIRE-RETARDANT	LS	LAWN SPRINKLER
AC	ALTERNATING CURRENT	CT	CURRENT TRANSFORMER	FST	FULL SIZE	LT	LIGHT
ACC	ACCESSIBLE	CTO	CENTER TO CENTER	FSTNR	FASTEN(ER)	LT WT	LIGHTWEIGHT
ACI	AMERICAN CONCRETE INSTITUTE	CTR	CENTER	FT	FEET	LTG	LIGHTING
ACR	ACRYLIC PLASTIC	CU	CONDENSING UNIT	FTG	FOOTING	LTNG	LIGHTNING
ACS DR	ACCESS DOOR	Cu	COPPER	FURG	FURRING	LVR	LOUVER
ACS PNL	ACCESS PANEL	CU FT	CUBIC FEET	FUT	FUTURE	LWC	LIGHTWEIGHT CONCRETE
ACSR	ALUMINUM CABLE STEEL REINFORCED	CUH	CUBIC YARD	FW	FIRE WATER	LWT	LEAVING WATER TEMPERATURE
ACST	ACOUSTIC	CU YD	CUBIC YARDS	FWC	FABRIC WALL COVERING	M	METER(S)
ACT	ACOUSTICAL CEILING TILE	CV	CEILING VENT	G	NATURAL GAS	M&B	MATCHED AND BEADED
ADDM	ADDENDUM	CVH	CONDUCTIVE VINYL HOMOGENEOUS	GA	GAGE	MACH	MACHINE
ADH	ADHESIVE	DBL	DOUBLE	GAL	GALLON(S)	MAS	MASONRY
ADJ	ADJACENT, ADJOINING, ADJUSTABLE	CW	CYLINDER	GALV	GALVANIZED	MATL	MATERIAL(S)
ADO	AUTOMATIC DOOR OPERATOR	CYL	PENNY (AS IN NAIL - 100)	GALV STL	GALVANIZED STEEL	MAX	MAXIMUM
AF	ABOVE FINISHED FLOOR	GB	GENERAL	MB	MACHINE BOLTS	MB	MEMBER
AGGR	AGGREGATE	DAT	DATUM	MC	MEDICINE CABINET	MBR	MASONRY CONTROL JOINT
AHR	AIR HANDLING UNIT	DB	DOUBLE	MCJ	MASONRY CONTROL JOINT	MCD	METAL-CASED OPENING
AHU	AREA INLET	DBL ACT DR	DOUBLE ACTING DOOR	GFCI	GROUND FAULT CIRCUIT INTERRUPTER	MDS	METAL DIVIDER STRIP
AIC	AMPERE INTERRUPTING CAPACITY	DCJ	DUMMIED CONTROL JOINT	GFE	GOVERNMENT-FURNISHED EQUIPMENT	MECH	MECHANICAL
AISC	AMERICAN INSTITUTE OF STEEL CONSTRUCTION	DCJT	DUMMIED CONTROL JOINT	GFE/CI	GOVERNMENT-FURNISHED EQUIPMENT	MECH RM	MECHANICAL ROOM
A/L	ACTIVE LEAF	DEG	DEGREE	GI	CONTRACTOR INSTALLED	MED	MEDIUM
ALT	ALTERNATE	DEMO	DEMOLITION	GIP	GALVANIZED IRON PIPE	MEM	MEMBRANE
ALU	ALUMINUM	DEPT	DEPARTMENT	GKT	GASKET(ED)	MES	METAL EDGE STRIP
AMB	AMBIENT	DET	DETAIL	GL	GLASS	MFD	METAL FLOOR DECKING
AMP	AMPERE	DF	DRINKING FOUNTAIN	GL BLK	GLASS BLOCK	MFG	MANUFACTURING
ANOD	ANODIZE	DGA	DENSE GRADED AGGREGATE	GLF	GLASS FIBER	MFR	MANUFACTURER
ANSI	AMERICAN NATIONAL STANDARDS INSTITUTE	DH	DOUBLE HUNG	GLZ	GLAZED	MGT	MOTOR GENERATOR
APRPTD	APPROVED	DH	DUCT HEATER	GLZ CMU	GLAZED CONCRETE MASONRY UNITS	MH	MANHOLE
APPROX	APPROXIMATE	DIA	DIAMETER	G	GROUND	MI	MALLEABLE IRON
ARCH	ARCHITECT	DIAG	DIAGONAL	GOVT	GOVERNMENT	MIN	MINIMUM
ARI	AMERICAN REFRIGERATION INSTITUTE	DIM	DIMENSION	GPM	GALLONS PER MINUTE	MISC	MISCELLANEOUS
ASB	ASBESTOS	DIM	DIMENSION	GPT	GYP(SUM) TILE	ML	METAL LATH
ASBR	ASBESTOS SUSPENDED CEILING	DISP	DISCONNECT	GRAN	GRANITE	MLD	MOLDING
ASPH	ASPHALT	DISTR PNL	DISTRIBUTION PANEL	GR	GRADE	MLWK	MILLWORK
ATC	ACOUSTICAL TILE CEILING	DIV	DIVISION	GR LN	GRADE LINE	MN	MATERIAL NOT IN CONTRACT
AUTO	AUTOMATIC	DL	DEAD LOAD	GRTG	GRATING	MOD	MODIFIED
AVG	AVERAGE	DMPF	DAMP PROOFING	GST	GLAZED STRUCTURAL TILE	MOT	MOTOR
AWT	ACOUSTICAL WALL TREATMENT	DMPR	DAMP	GT	GLAZED STRUCTURAL UNITS	MR	MOP RECEPTOR
BB	BULLETIN BOARD	DMT	DEMOUNTABLE	GWT	GLAZED WALL TILE	MRO	MARBLE BASE
BC	BOOKCASE	DN	DOWN	HDW	HEAD JOINT	MS	MACHINE SCREWS
BD	BOARD	DOOR	DOOR	HDR	HEADER	MT	MOUNT
BDRY	BOUNDARY	DR	DRAIN	HDW	HARDWARE	MTD	MOUNTED
BEJ	BRICK EXPANSION JOINT	DRB	DRAINBOARD	HDWD	HARDWOOD	MTR	METAL THRESHOLD
BEV	BEVEL	DR CL	DOOR CLOSER	HES	HIGH EARLY-STRENGTH CEMENT	MTL	METAL
BITUM	BITUMINOUS	DS	DOUBLE STRENGTH (GLASS)	HEX	HEXAGON	MVBL	MOVABLE
BJT	BED JOINT	DVTL	DOWNSPOUT	HCH	HANDICAPPED	MULL	MULLION
BL	BUILDING LINE	DT	DOWNSPOUT	HCP	HANDICAPPED	N	NORTH
BLDG	BUILDING	DVTL	DOWNSPOUT	HD	HEAD	NAT	NATURAL
BLW	BELOW	DWGL	DRAWING	HDO	HEAD DUTY	NC	NORMALLY CLOSED
BM	BENCHMARK	DWLS	DOWELS	HDBD	HARDBOARD	NEC	NATIONAL ELECTRICAL CODE
BO	BOTTOM OF	DWR	DRAWER	HDJT	HEAD JOINT	NEMA	NATIONAL ELECTRICAL MANUFACTURERS
BOT	BOTTOM	DWTR	DUMBWATER	HDR	HEADER	ASSOCIATION	ASSOCIATION
BP	BACK PLASTER(ED)	DX	DIRECT EXPANSION	HDW	HARDWARE	FFPA	FIRE PROTECTION ASSOCIATION
BRCG	BRACING	E	EAST	HDX	HARDWOOD	N	NICKEL
BRDG	BRIDGING	EA	EACH	HES	HIGH EARLY-STRENGTH CEMENT	NC	NORMALLY CLOSED
BRQ	BEARING	EAT	ENTERING AIR TEMPERATURE	HEX	HEXAGON	NEC	NATIONAL ELECTRICAL CODE
BRG PL	BEARING PLATE	EF	EACH FACE	HH	HANDHOLE	NEMA	NATIONAL ELECTRICAL MANUFACTURERS
BRK	BRICK	EJ	EXPANSION JOINT	HK	HOCKS	ASSOCIATION	ASSOCIATION
BRKT	BRACKET	EL	ELEVATION - GRADE OR BUILDING	HNDRL	HANDRAIL	FFPA	FIRE PROTECTION ASSOCIATION
BRZ	BRONZE	ELEC	ELECTRIC	HORIZ	HORIZONTAL	N	NICKEL
BS	BOTH SIDES	EMD	EXPANDED METAL	HP	HIGH PRESSURE	NC	NORMALLY CLOSED
BSMT	BASEMENT	EM	ESTIMATED MAXIMUM DEMAND	HP	HIGH PRESSURE	NEC	NATIONAL ELECTRICAL CODE
Bu	BRITISH THERMAL UNIT	EMER	EMERGENCY	HPT	HIGH POINT	NEMA	NATIONAL ELECTRICAL MANUFACTURERS
BuH	BTU PER HOUR	ENCL	ENCLOSURE	HR	HOUR	ASSOCIATION	ASSOCIATION
BTWN	BETWEEN	ENR	ENTRANCE, ENTERING	HS	HIGH STRENGTH	FFPA	FIRE PROTECTION ASSOCIATION
BUR	BUILT-UP ROOFING	EP	ELECTRICAL PANELBOARD	HSGYP	HIGH-STRENGTH GYPSUM PLASTER	N	NICKEL
BW	BOTH WAYS	EPRF	EXPLOSION PROOF	HSKPG	HOUSEKEEPING	NL	NAILE
CAB	CABINET	EQ	EPOXY COATING	HT	HEIGHT	NL	NEOPRENE LATEX
CAP	CAPACITY	EQ	EQUAL	HTG	HEATING	NM	NONMETALLIC
CB	CATCH BASIN	EQUIP	EQUIPMENT	HTR	HEATER	RWC	RUBBER WATER CONDUCTOR
CCT	CUBICLE CURTAIN TRACK	ESCAL	ESCALATOR	HVAC	HEATING, VENTILATING AND AIR	S	SOUTH
CCTV	CLOSED CIRCUIT TELEVISION	EST	ESTIMATE(D)	CONDITIONING	CONDITIONING	SA	SUPPLY AIR
CE	COVER ELEVATION	EWG	ELECTRIC WATER COOLER	HYDR	HYDRAULIC	SB	SPLASH BLOCK
CEM	CEMENT	EWI	ENTERING WATER TEMPERATURE	IC	INTERCOM	SC	SECURITY BARS
CEM PLAS	CEMENT PLASTER	EXC	EXCAVATE	INTS	INTERCOM	SCHD	SCHEDULE
CER	CERAMIC	EXH	EXHAUST	ID	INSIDE DIAMETER	SCRN	SCREEN
CFI	CONDUCTIVE FLOORING	EXH A	EXHAUST AIR	IESNA	ILLUMINATING ENGINEERING SOCIETY OF	SCT	STRUCTURAL CLAY TILE
CFLG	COUNTERFLASHING	EXST	EXPOSED	INCH	INCH	SD	STORM DRAIN
CF	CUBIC FEET PER MINUTE	EXP	EXPANSION	ILK	INTERLOCK	SDI	STEEL DOOR INSTITUTE
CG	CORNER GUARD	EXP	EXPOSED	INCL	INCINERATOR	SEQ	SEQUENCE
CH BD	CHALKBOARD	EXP BT	EXPANSION BOLT	INCL	INCINERATOR	SFGL	SAFETY GLASS
CHFR	CHAMFER	EXT	EXTERIOR	INCL	INCLUDED	SFTU	STRUCTURAL FACING TILE UNIT
CHIM	CHIMNEY	FA	FAHRENHEIT	INCL	INCLUDED	SFTU	STRUCTURAL FACING UNIT
CHK	CHECK	FA	FIRE ALARM	INCL	INCLUDED	SG	SHOULDER
CHR PL	CHROME PLATED	FAC	FIRE APPARATUS CLOSET	INT	INTERIOR	SHDR	SHOULDER
CI	CAST IRON	FAC	FIRE APPARATUS CLOSET	INTM	INTERMEDIATE	SHT	SHEET
CJ	CURB INLET	FAC	FIRE APPARATUS CLOSET	INTM	INTERMEDIATE	SHTG	SHEATHING
CP	CAST-IN-PLACE	FBI	FIRE BRICK	IP	INVERT	SHV	SHELVING
CIRC	CIRCULAR	FBI	FIRE BRICK	IP	INVERT	SHV	SHELVING
CJ	CONTROL JOINT	FBI	FIRE BRICK	IP	INVERT	SHV	SHELVING
CJ	CONSTRUCTION JOINT	FBI	FIRE BRICK	IP	INVERT	SHV	SHELVING
CKT	CIRCUIT	FBI	FIRE BRICK	IP	INVERT	SHV	SHELVING
CKT BRKR	CIRCUIT BREAKER	FBI	FIRE BRICK	IP	INVERT	SHV	SHELVING
CL	CENTER LINE	FBI	FIRE BRICK	IP	INVERT	SHV	SHELVING
CLG	CEILING	FBI	FIRE BRICK	IP	INVERT	SHV	SHELVING
CLG HT	CEILING HEIGHT	FBI	FIRE BRICK	IP	INVERT	SHV	SHELVING
CLGL	CLEAR GLASS	FBI	FIRE BRICK	IP	INVERT	SHV	SHELVING
CLL	CONTRACT LIMIT LINE	FBI	FIRE BRICK	IP	INVERT	SHV	SHELVING
CLOS	CLOSURE	FBI	FIRE BRICK	IP	INVERT	SHV	SHELVING
CLR	CLEAR(ANCE)	FBI	FIRE BRICK	IP	INVERT	SHV	SHELVING
CLWG	CLEAR WIRED GLASS	FBI	FIRE BRICK	IP	INVERT	SHV	SHELVING
cm	CENTIMETER(S)	FBI	FIRE BRICK	IP	INVERT	SHV	SHELVING
CMF	CORRUGATED METAL PIPE	FBI	FIRE BRICK	IP	INVERT	SHV	SHELVING
CMPT	COMPOSITE	FBI	FIRE BRICK	IP	INVERT	SHV	SHELVING
CMU	CONCRETE MASONRY UNIT	FBI	FIRE BRICK	IP	INVERT	SHV	SHELVING
CND	CONDUIT	FBI	FIRE BRICK	IP	INVERT	SHV	SHELVING
CNL	CONDUCTIVE NEOPRENE LATEX	FBI	FIRE BRICK	IP	INVERT	SHV	SHELVING
CNR	CORNER	FBI	FIRE BRICK	IP	INVERT	SHV	SHELVING
CNTR	COUNTER	FBI	FIRE BRICK	IP	INVERT	SHV	SHELVING
CO	CLEANOUT	FBI	FIRE BRICK	IP	INVERT	SHV	SHELVING
CO2	CARBON DIOXIDE	FBI	FIRE BRICK	IP	INVERT	SHV	SHELVING
COL	COLUMN	FBI	FIRE BRICK	IP	INVERT	SHV	SHELVING
COM	COMMON	FBI	FIRE BRICK	IP	INVERT	SHV	SHELVING
COMB	COMBUSTION	FBI	FIRE BRICK	IP	INVERT	SHV	SHELVING
COMPT	COMPARTMENT	FBI	FIRE BRICK	IP	INVERT	SHV	SHELVING
CONC	CONCRETE	FBI	FIRE BRICK	IP	INVERT	SHV	SHELVING
CONN	CONNECT	FBI	FIRE BRICK	IP	INVERT	SHV	SHELVING
CONSTR	CONSTRUCTION	FBI	FIRE BRICK	IP	INVERT	SHV	SHELVING
CONTR	CONTRACTOR	FBI	FIRE BRICK	IP	INVERT	SHV	SHELVING
CORR	CORRIDOR	FBI	FIRE BRICK	IP	INVERT	SHV	SHELVING
COV	COVER	FBI	FIRE BRICK	IP	INVERT	SHV	SHELVING
CPRS	COMPRESSIBLE	FBI	FIRE BRICK	IP	INVERT	SHV	SHELVING
CPT	CARPET	FBI	FIRE BRICK	IP	INVERT	SHV	SHELVING
CRCMF	CIRCUMFERENCE	FBI	FIRE BRICK	IP	INVERT	SHV	SHELVING
CRES	CORROSIVE RESISTANT STEEL	FBI	FIRE BRICK	IP	INVERT	SHV	SHELVING
CRG	CROSS GRAIN	FBI	FIRE BRICK	IP	INVERT	SHV	SHELVING
CRS	COURSE(S)	FBI	FIRE BRICK	IP	INVERT	SHV	SHELVING

FRAME	
FORGED	
FRAMING	
FIRE-RETARDANT	
FULL SIZE	
FASTEN(ER)	
FEET	
FOOTING	
FURRING	
FUTURE	
FIRE WATER	
FABRIC WALL COVERING	
NATURAL GAS	
GAGE	
GALLON(S)	
GALVANIZED	
GALVANIZED STEEL	
GRAB BAR	
GENERAL CONTRACTOR	
GENERAL	
GROUND FAULT CIRCUIT INTERRUPTER	
GOVERNMENT-FURNISHED EQUIPMENT	
GOVERNMENT-FURNISHED EQUIPMENT	
LED	
GALVANIZED IRON	
GALVANIZED IRON PIPE	
GASKET(ED)	
GLASS	
GLASS BLOCK	
GLASS FIBER	
GLAZING	
GLAZED CONCRETE MASONRY UNITS	
GROUND	
GOVERNMENT	
GALLONS PER MINUTE	
GYP(SUM) TILE	
GRANITE	
GRADE LINE	
GRATING	
GLAZED STRUCTURAL TILE	
GLAZED STRUCTURAL UNITS	
GROUT	
GLAZED WALL TILE	
GYPSUM	
GYPSUM BOARD	
GYPSUM PLASTER	
HOSE BIBB	
HOLLOW CORE	
HALON CONTAINMENT DAMPER	
HANDICAPPED	
HEAD	
HEAVY DUTY	
HARDBOARD	
HEAD JOINT	
HEADER	
HARDWARE	
HARDWOOD	
HIGH EARLY-STRENGTH CEMENT	
HEXAGON	
HANDHOLE	
HOCKS	
HOLLOW METAL	
HANDRAIL	
HORIZONTAL	
HIGH PRESSURE	
HORSEPOWER	
HIGH POINT	
HOUR	
HIGH STRENGTH	
HIGH-STRENGTH GYPSUM PLASTER	
HOUSEKEEPING	
HEIGHT	
HEATING	
HEATER	
HEATING, VENTILATING AND AIR	
CONDITIONING	
HYDRAULIC	
HERTZ	
INTERCOM	
INSIDE DIAMETER	
ILLUMINATING ENGINEERING SOCIETY OF AMERICA	
INTERLOCK	
INCH	
INCINERATOR	
INCLUDED	
INSULATING FILL	
INSULATION	
INTERIOR	
INTERMEDIATE	
INVERT	
IRON PIPE	
IRON PIPE SIZE	
INSIDE PIPE SIZE	
JANITOR'S CLOSET	
JUNCTION BOX	
JUNCTION	
JOIST	
JOINT	
KILFOUND (1000 POUNDS)	
KITCHEN	
KNOCKOUT PANEL	
KICKPLATE	
KILOVOLTS	
KILOVOLT AMPERES	
KILOVOLT AMPERES REACTIVE	
KILOWATT	
KEYWAY	
LABORATORY	
LADDER	
LAMINATE	
LEAVING AIR TEMPERATURE	
LAUNDRY	
LAVATORY	
LAG BOLT	
FOUND	
LABEL	
LUMBER	
LIGHT CONTROL	
LOADING	
LENGTH	
LEFT HAND(ED)	
LINEAR	
LOCKER	
LIVE LOAD	
LEAD-LINED DOOR	
LUMEN	
LIMESTONE	
LINTEL	
LONGITUDINAL	
LIGHTPROOF	
LIGHTPROOF DOOR	






FILE NAME: P:\Projects\2024\21297-24020 NAVFAC Midlant LP-38 Berm Recert\500-500\591-Civil\231848 DEMO AND EXISTING CONDITIONS PLAN.dwg LAYOUT NAME: CD-100-DEMO PLAN PLOTTED: Thursday, April 09, 2026 - 6:27am USER: cmoore



- NOTE: NOT ALL KEYNOTES APPLY TO EACH SHEET
1. EXISTING BERM FOR TANK CONTAINMENT.
2. EXISTING ACCESS STAIR TO REMAIN AND BE PROTECTED DURING CONSTRUCTION.
3. EXISTING CONCRETE PIPE SUPPORTS TO REMAIN, AND BE PROTECTED DURING CONSTRUCTION.
4. EXISTING TANK PIPING TO REMAIN AND BE PROTECTED DURING CONSTRUCTION.
5. EXISTING STORM INLET TO REMAIN AND BE PROTECTED DURING CONSTRUCTION.
6. EXISTING STORM LINE THAT WAS IDENTIFIED AS ABANDONED IN ORIGINAL CONSTRUCTION DRAWINGS FOR TANK AND BERM CONSTRUCTION. CONTRACTOR TO FIELD VERIFY IF LINE IS ACTIVE OR NOT. PROTECT IN PLACE DURING CONSTRUCTION.
7. EXISTING TANK TO REMAIN AND BE PROTECTED DURING CONSTRUCTION.
8. EXISTING STORM SEWER INLET STRUCTURE TO BE REMOVED, AND REPLACED WITH WATERTIGHT MANHOLE (MIN. 72" DIA.), EXCAVATION BACKFILLED.
9. EXISTING BERM LINER TO BE CUT AND PREPPED FOR NEW LINER ATTACHMENT BASE ON NEW LINER MANUFACTURE SPECIFICATIONS.
10. EXISTING BERM AND LINER SECTION TO BE REMOVED FOR EXPANSION SECTION.
11. EXISTING SECURITY FENCE TO BE REMOVED, NEW SECURITY FENCE TO BE PLACED BEFORE EXISTING FENCE DEMOLITION BEGINS TO MAINTAIN SECURE AREA, CONTRACTOR TO SUBMIT A PHASING SCHEDULE AND COORDINATE WITH BASE.
12. CONTRACTOR TO COORDINATE CAPPING/REMOVAL OF MONITORING WELL AND VALVE BOX WITH CONTRACTING OFFICER.

SYMBOL/ABBREVIATION - DESCRIPTION


○ <i>WM</i> - WATER METER	○ <i>FH</i> - FIRE HYDRANT
○ <i>FDC</i> - FIRE DEPARTMENT CONNECTION	○ <i>WELL</i> - WELL
○ <i>MWELL</i> - MONITOR WELL	○ <i>WMH</i> - WATER MANHOLE
○ <i>WV</i> - WATER VALVE	○ <i>SPICOT</i> - SPIGOT
○ <i>SSMH</i> - SANITARY MANHOLE	○ <i>SCD</i> - SANITARY CLOSURE
○ <i>SV</i> - SANITARY VALVE	○ <i>FMV</i> - FORCE MAIN VALVE
○ <i>LP</i> - LIGHT POLE	○ <i>GLIGHT</i> - GROUND LIGHT
○ <i>GU</i> - GUY WIRE	○ <i>TR</i> - TRANSFORMER
○ <i>EM</i> - ELECTRIC METER	○ <i>PP</i> - POWER POLE
○ <i>EBOX</i> - ELECTRIC BOX	
□ <i>COMM BOX</i> - COMMUNICATIONS BOX	
○ <i>TPED</i> - TELEPHONE PEDESTAL	○ <i>TMH</i> - TELEPHONE MANHOLE
○ <i>CPED</i> - CABLE TV PEDESTAL	○ <i>CTV BOX</i> - CABLE TV BOX
○ <i>GM</i> - GAS METER	○ <i>GV</i> - GAS VALVE
○ <i>FC</i> - FILLER CAP	
○ <i>DI1</i> - DROP INLET 1	○ <i>DI2</i> - DROP INLET 2
○ <i>DI3</i> - DROP INLET 3	○ <i>CB</i> - CATCH BASIN
○ <i>RD</i> - ROOF DRAIN	○ <i>STCLO</i> - STORM CLEANOUT
○ <i>SMH</i> - SANITARY MANHOLE	○ <i>YD</i> - YARD DROP INLET
○ <i>FES</i> - FARED-END SECTION	○ <i>PIPE END (CONTINUES)</i>
○ <i>AC</i> - AC UNIT	○ <i>MH</i> - MANHOLE
○ <i>POST</i> - POST	
○ <i>BOL</i> - BOLLARD	○ <i>WITPOST</i> - WITNESS POST
○ <i>BORING</i> - BORING	○ <i>SIGN</i>
○ <i>MB</i> - MAIL BOX	
EVERGREEN - 	 - BUSH/HEDGE
○ <i>TREES</i> - DECIDUOUS	- WOODS LINE/ WOODED

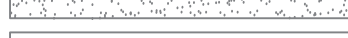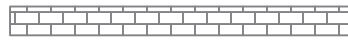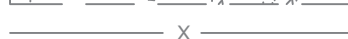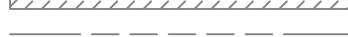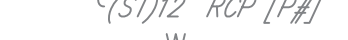	CURB AND GUTTER
	CONCRETE
	PAVEMENT
	BRICK
	GRAVEL
	FENCE
	GUARDRAIL
	PROPERTY LINE
	RIGHT-OF-WAY LINE
	BUILDINGS
	TOP OF BANK
	TOP OF SLOPE
	¢ OF DITCH
	¢ OF SWALE
	WATER/HYDROGRAPHIC FEATURE
	STORM SEWER
	PIPE LABEL (SIZE, TYPE, ID)
	WATER LINE
	SANITARY SEWER
	PIPE LABEL (SIZE, TYPE, ID)
	UNDERGROUND CABLE
	OVERHEAD CABLE
	OVERHEAD TELEPHONE
	UNDERGROUND FIBER OPTIC
	UNDERGROUND TELEPHONE
	UNDERGROUND GAS
	OVERHEAD ELECTRIC
	UNDERGROUND ELECTRIC
	FIRE MAIN
	STEAM LINE
	UNDERGROUND UNKNOWN UTILITIES
	UNDERGROUND TRAFFIC CONTROL
	LIMITS OF DISTURBANCE
	SILT FENCE



1:10'

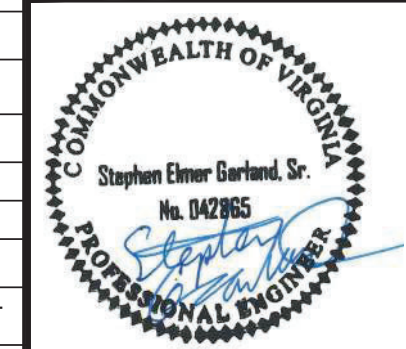0 10 20 FEET

[illegible]

APPROVED

FOR COMMANDER NAVFAC 4-10-86
ACTIVITY :BILL BOUNDS, DLA

SATISFACTORY TO DATE:14 JAN. 2026		
SG	PAE	RB
PM/DM :W. WITHAM, P.E.		
BRANCH MANAGER :W. WITHAM, P.E.		
CHIEF ENG/ARCH :J. MILLER, P.E.		

DEPARTMENT OF THE NAVY	NAVAL FACILITIES ENGINEERING SYSTEMS COMMAND	NAVAL FACILITIES ENGINEERING SYSTEMS COMMAND
NAVAL FACILITIES ENGINEERING SYSTEMS COMMAND - MID-ATLANTIC	NAVAL FACILITIES ENGINEERING SYSTEMS COMMAND - MID-ATLANTIC	NAVAL FACILITIES ENGINEERING SYSTEMS COMMAND - MID-ATLANTIC
MID-ATLANTIC DC CORE	NAVAL STATION - NORFOLK, VA	NAVAL STATION - NORFOLK, VA
NAVAL STATION SHIPYARD	NORFOLK, VIRGINIA	NORFOLK, VIRGINIA
LP-38 BERM RECERTIFICATION REPAIR		
DEMO PLAN SOUTH		

SCALE:	
EPROJECT NO.:	1766588
CONSTR. CONTR. NO.	N40085-22-D-0039
NAVFAC DRAWING NO.	12940914
SHEET 10	OF 19
CD101	

FILE NAME: P:\Projects\2024\21297-24020 NAVFAC Midant LP-38 Berm Recert\500-500\591-Civil\231848_EPSC PLAN.dwg LAYOUT NAME: EC-100 PLOTTED: Thursday, April 09, 2026 - 6:33am USER: amore



- # EPSC KEY NOTES:
- NOTE: NOT ALL KEYNOTES APPLY TO EACH SHEET
1. PROPOSED CONSTRUCTION SITE GATE (12' SWING).
 2. CONSTRUCTION FENCE TO TIE INTO AND CONTINUE FROM EXTENTS OF EXISTING SECURITY FENCE DEMO. CONTRACTOR TO PLACE CONSTRUCTION FENCE IN SUCH A MANNER THAT WILL NOT DAMAGE OR IMPACT THE EXISTING SECURITY FENCE THAT COULD COMPROMISE THE SECURE AREA. REF. DRAWING C-500.
 3. MAINTAIN STORM INLET PROTECTION FOR STORM WATER INLET UNTIL CONSTRUCTION ON STRUCTURE AND PIPE IS COMPLETE (REFER TO VDEQ DETAIL C-SCM-04-3) SEE B3/C-501.

EPSC GENERAL NOTES:

THE CONTRACTOR IS REQUIRED TO FURNISH A MINIMUM OF 6" TOPSOIL IN ANY LANDSCAPE / LAWN / AREAS DISTURBED BY CONSTRUCTION. IT IS THE CONTRACTOR'S RESPONSIBILITY TO DETERMINE THE AMOUNT OF TOPSOIL REQUIRED AND INCLUDE IT IN THE BID. TOPSOIL MUST BE INCIDENTAL TO CONTRACT.

SITE BMP PLAN

THE PHASES LISTED BELOW AND CONTROLS SHOWN ON PLANS ARE A GENERAL OVERVIEW AND MAY BE ADJUSTED IN THE FIELD DUE TO CONSTRUCTION ACTIVITIES AND CONSTRUCTION MEANS AND METHODS.

PHASE I - BMP PLAN (CLEARING & GRUBBING; DEMOLITION). ERECT EROSION CONTROL MEASURE (SILT FENCE) ALONG THE DOWN SLOPE SIDE OF THE PROJECT PERIMETER. INSTALL INLET PROTECTION AT DOWN SLOPE STORM SEWER STRUCTURES (WHERE APPLICABLE). CONTRACTOR MAY MARKUP NEW LOCATION AND DATE THE CHANGE ON A PAPER COPY OF THE BMP PLAN ONSITE. MAINTAIN THE SILT FENCE ALONG THE DOWN SLOPE PROJECT PERIMETER.

PHASE II - BMP PLAN (EARTHWORK). DURING THIS PHASE OF CONSTRUCTION ACTIVITIES, SILT FENCE MUST BE REMOVED, RELOCATED, AND/OR ADDED AS CONSTRUCTION PROGRESSES. CONTRACTOR MAY MARKUP NEW LOCATION AND DATE THE CHANGE ON A PAPER COPY OF THE BMP PLAN ONSITE. MAINTAIN THE SILT FENCE ALONG THE DOWN SLOPE PROJECT PERIMETER.

PHASE III - BMP PLAN (SUBSTANTIAL SITE CONSTRUCTION COMPLETION). MAINTAIN THE SILT FENCE ALONG THE DOWN SLOPE PROJECT PERIMETER. WHERE NORMAL SEED AND MULCH COVER METHODS ARE INEFFECTIVE, OR ON SLOPES 3:1 OR STEEPER, INSTALL EROSION CONTROL MATTING, 6 MONTH LONGEVITY. MAINTAIN INLET PROTECTION. CONTRACTOR MAY MARKUP NEW LOCATION AND DATE THE CHANGE ON A PAPER COPY OF THE BMP PLAN ONSITE. FINISH CONSTRUCTION AND SEED AND MULCH COVER A 10' BUFFER AROUND NEW WORK AFTER CONCRETE HAS BEEN INSTALLED.

PHASE IV - BMP PLAN (FINAL CONSTRUCTION). REMOVE SILT FENCE AND OTHER CONTROLS THAT ARE INHIBITING FINAL CONSTRUCTION AND ARE NO LONGER NEEDED. CONTRACTOR MAY MARKUP NEW LOCATION (AND/OR AREAS OF BMPs REMOVED) AND DATE THE CHANGE ON A PAPER COPY OF THE BMP PLAN ONSITE. FINALLY, REMOVE ANY REMAINING EROSION CONTROL MEASURES AND PROTECT ANY REMAINING DISTURBED AREAS WITH SEED AND MULCH COVER.

ALL ESC/BMP DETAILS MUST REFER TO VDEQ DETAILS.

NPDES NOI INFORMATION

AREA OF SITE: 0.80 ACRES

AREA OF DISTURBANCE: 0.45 ACRES

SHEET LEGEND	
GRAPHIC	DESCRIPTION
SF	SILT FENCE REFER TO VDOT 113.07
LOD	LIMITS OF DISTURBANCE
	CONSTRUCTION LIMIT
	INLET PROTECTION
	6" CHAIN LINK CONSTRUCTION FENCE
	CONSTRUCTION ENTRANCE
	LINER
TS	TEMPORARY SLOPE STABILIZATION: REFER TO VDOT DETAIL 113.02
PS	PERMANENT SLOPE STABILIZATION: REFER TO VDOT DETAIL 113.05
IP	INLET PROTECTION: REFER TO VDOT DETAIL 113.10

N



A1

1:10'

0 10 20 FEET

EPSC PLAN NORTH

MISC. REVISIONS	FINAL SET	DATE
		4/10/26
		1/28/26
		DATE

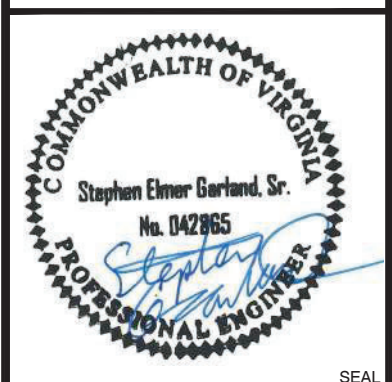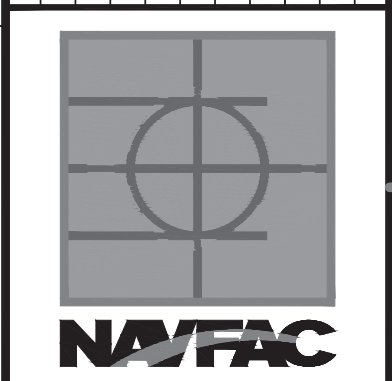

APPROVED

FOR COMMANDER NAVFAC

ACTIVITY: BILL BOUNDS, OLA

SATISFACTORY TO DATE: 14 JAN 2026

SG PAE RB

PM/DM W. WITHAM, P.E.

BRANCH MANAGER W. WITHAM, P.E.

CHIEF ENG/ARCH J. MILLER, P.E.

FIRE PROTECTION N/A

NAVFACILITIES ENGINEERING SYSTEMS COMMAND

NAVAL STATION - NORFOLK


NORFOLK, VIRGINIA

LP-38 BERM RECERTIFICATION REPAIR

EPSC PLAN NORTH

SCALE:	1766588
PROJECT NO.:	N40085-22-D-0039
CONSTR. CONTR. NO.:	12940915
NAVAC DRAWING NO.:	EC-100
SHEET 11 OF 19	

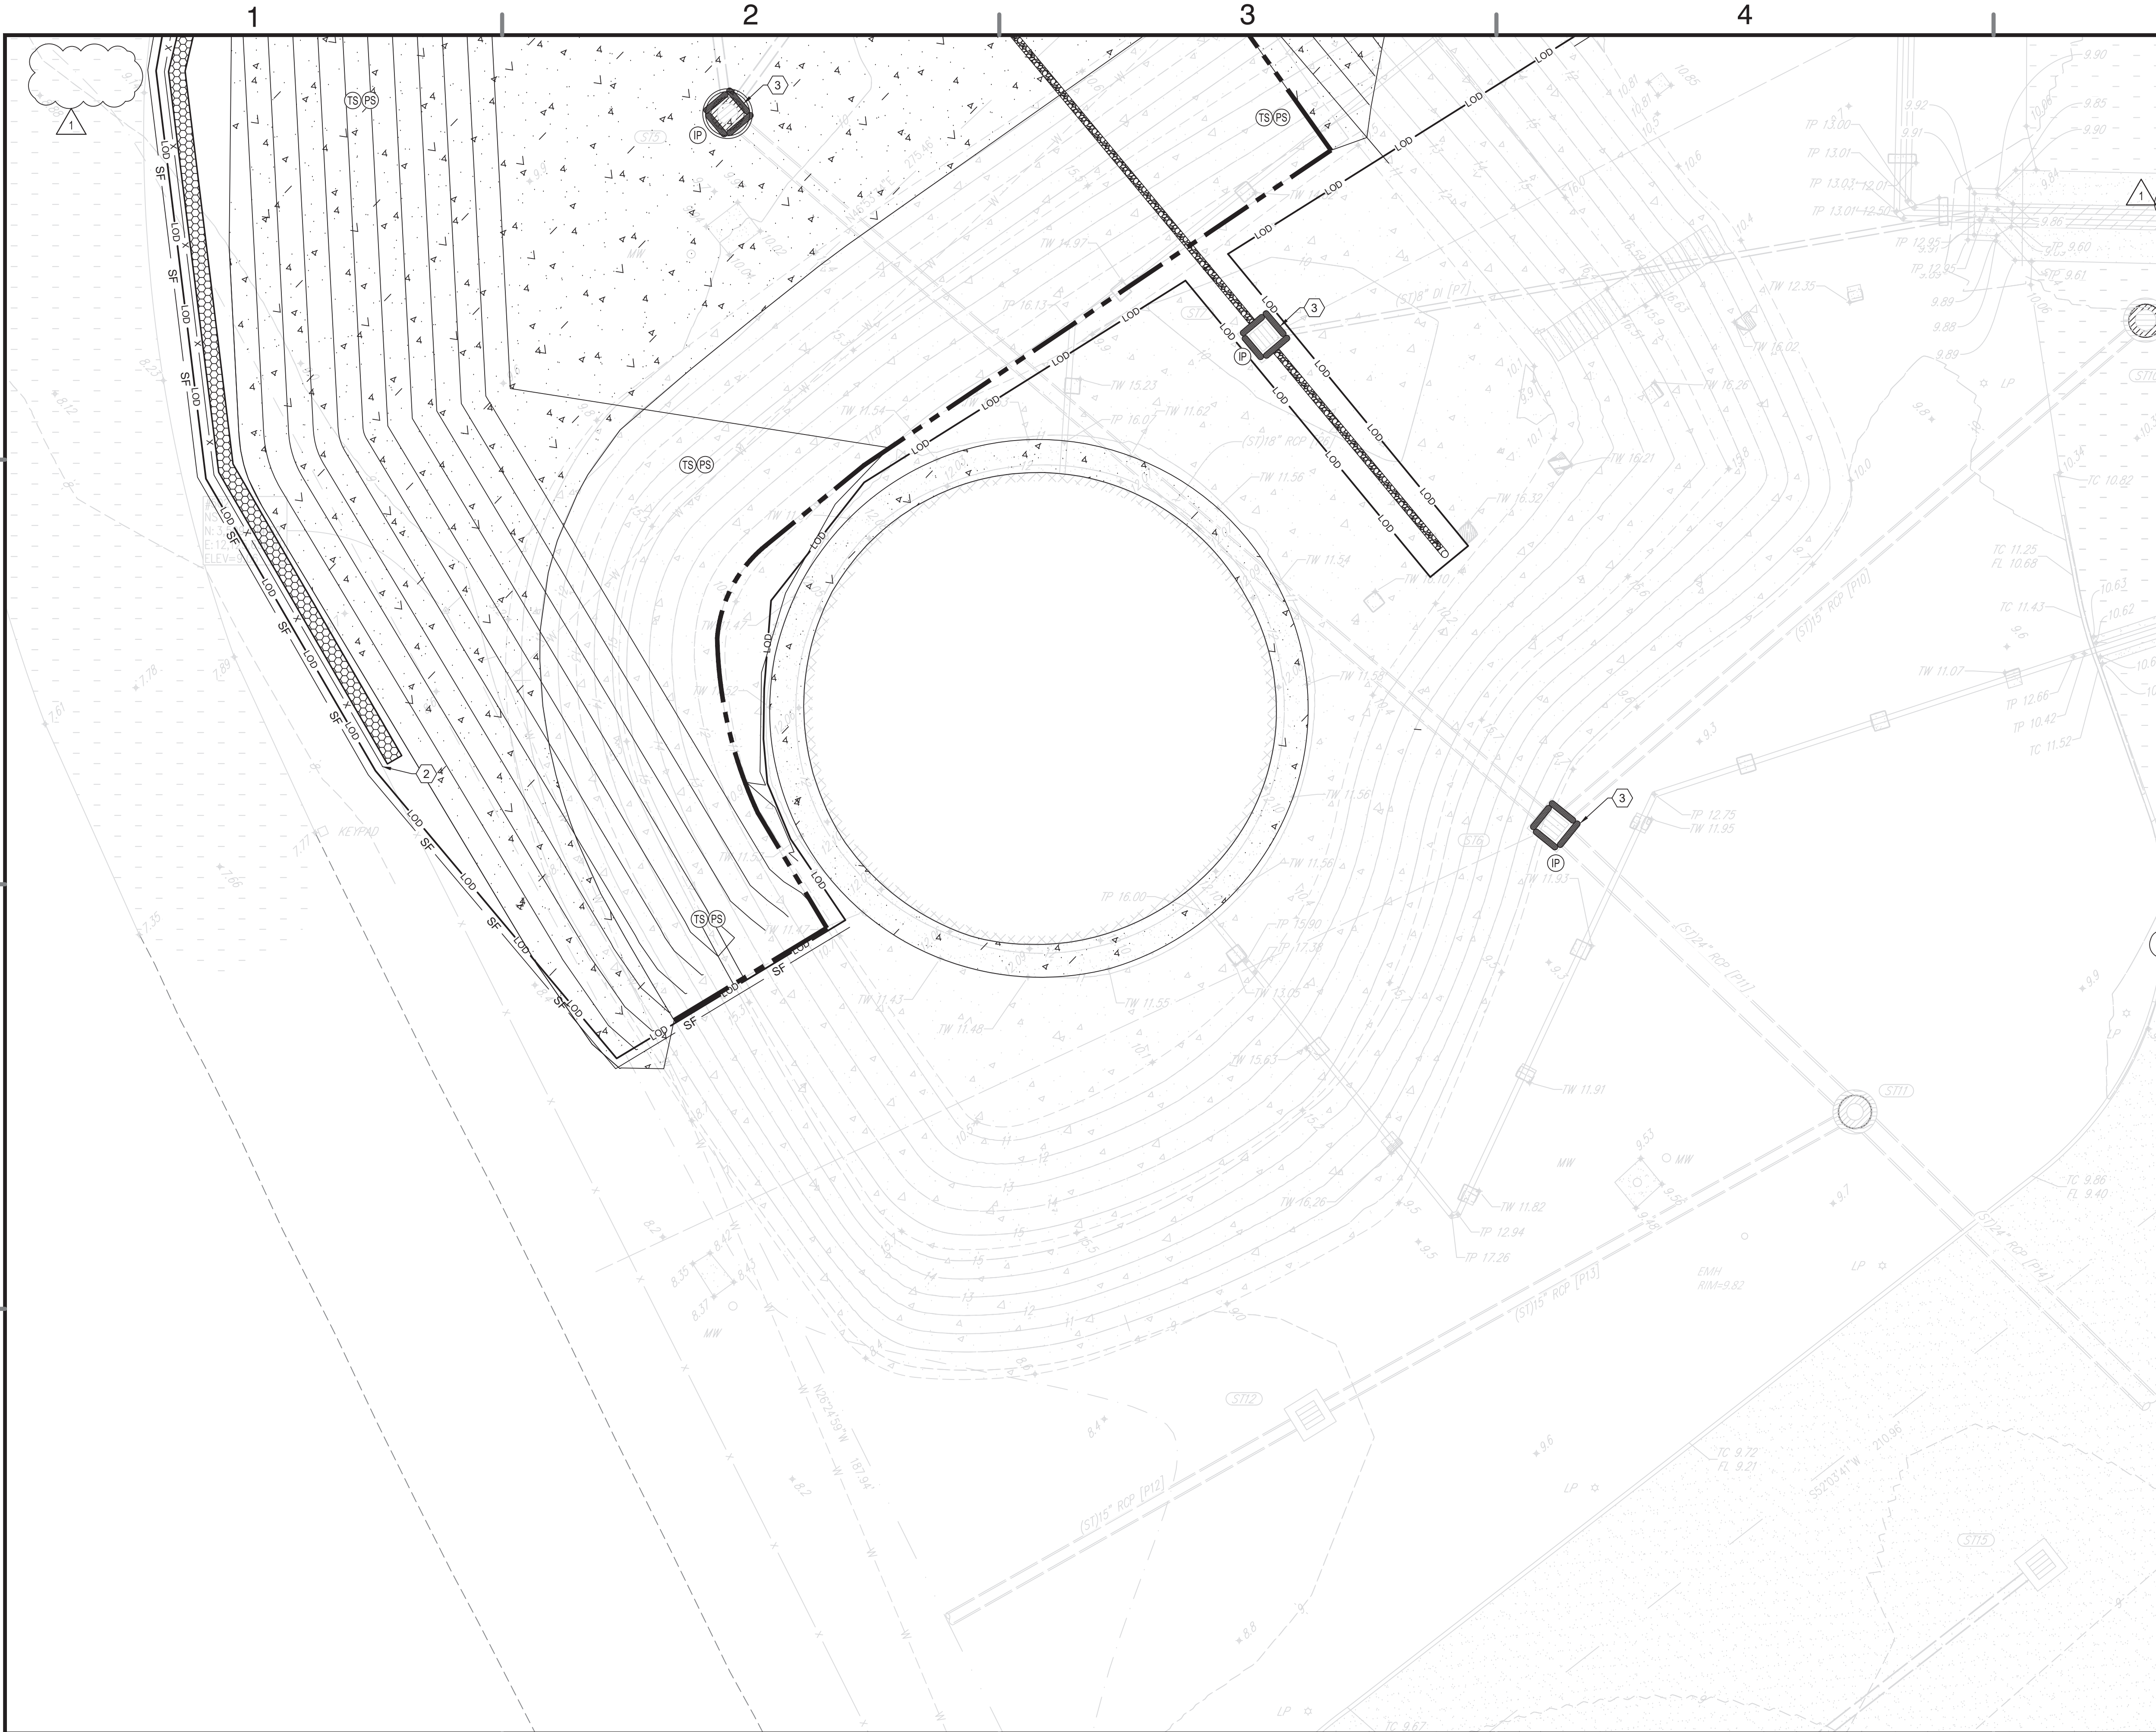FILE NAME: P:\Projects\2024\21297-24020 NAVFAC Midant LP-38 Berm Recert\500-500\591-Civil\231848_EPSC PLAN.dwg LAYOUT NAME: EC-101 PLOTTED: Thursday, April 09, 2026 - 7:20am USER: cmoreno



#

EPSC KEY NOTES:

NOTE: NOT ALL KEYNOTES APPLY TO EACH SHEET

1. PROPOSED CONSTRUCTION SITE GATE (12' SWING).

2. CONSTRUCTION FENCE TO TIE INTO AND CONTINUE FROM EXTENTS OF EXISTING SECURITY FENCE DEMO. CONTRACTOR TO PLACE CONSTRUCTION FENCE IN SUCH A MANNER THAT WILL NOT DAMAGE OR IMPACT THE EXISTING SECURITY FENCE THAT COULD COMPROMISE THE SECURE AREA. REF. DRAWING C-500.

3. MAINTAIN STORM INLET PROTECTION FOR STORM WATER INLET UNTIL CONSTRUCTION ON STRUCTURE AND PIPE IS COMPLETE (REFER TO VDEQ DETAIL C-SCM-04-3) SEE B3/C-501.

EPSC GENERAL NOTES:

THE CONTRACTOR IS REQUIRED TO FURNISH A MINIMUM OF 6" TOPSOIL IN ANY LANDSCAPE / LAWN / AREAS DISTURBED BY CONSTRUCTION. IT IS THE CONTRACTOR'S RESPONSIBILITY TO DETERMINE THE AMOUNT OF TOPSOIL REQUIRED AND INCLUDE IT IN THE BID. TOPSOIL MUST BE INCIDENTAL TO CONTRACT.

SITE BMP PLAN

THE PHASES LISTED BELOW AND CONTROLS SHOWN ON PLANS ARE A GENERAL OVERVIEW AND MAY BE ADJUSTED IN THE FIELD DUE TO CONSTRUCTION ACTIVITIES AND CONSTRUCTION MEANS AND METHODS.

PHASE I - BMP PLAN (CLEARING & GRUBBING; DEMOLITION). ERECT EROSION CONTROL MEASURE (SILT FENCE) ALONG THE DOWN SLOPE SIDE OF THE PROJECT PERIMETER. INSTALL INLET PROTECTION AT DOWN SLOPE STORM SEWER STRUCTURES (WHERE APPLICABLE). CONTRACTOR MAY MARKUP NEW LOCATION AND DATE THE CHANGE ON A PAPER COPY OF THE BMP PLAN ONSITE.

PHASE II - BMP PLAN (EARTHWORK). DURING THIS PHASE OF CONSTRUCTION ACTIVITIES, SILT FENCE MUST BE REMOVED, RELOCATED, AND OR ADDED AS CONSTRUCTION PROGRESSES. CONTRACTOR MAY MARKUP NEW LOCATION AND DATE THE CHANGE ON A PAPER COPY OF THE BMP PLAN ONSITE. MAINTAIN THE SILT FENCE ALONG THE DOWN SLOPE PROJECT PERIMETER.

PHASE III - BMP PLAN (SUBSTANTIAL SITE CONSTRUCTION COMPLETION). MAINTAIN THE SILT FENCE ALONG THE DOWN SLOPE PROJECT PERIMETER. WHERE NORMAL SEED AND MULCH COVER METHODS ARE INEFFECTIVE, OR ON SLOPES 3:1 OR STEEPER, INSTALL EROSION CONTROL MATTING, 6 MONTH LONGEVITY. MAINTAIN INLET PROTECTION. CONTRACTOR MAY MARKUP NEW LOCATION AND DATE THE CHANGE ON A PAPER COPY OF THE BMP PLAN ONSITE. FINISH CONSTRUCTION AND SEED AND MULCH COVER A 10' BUFFER AROUND NEW WORK AFTER CONCRETE HAS BEEN INSTALLED.

PHASE IV - BMP PLAN (FINAL CONSTRUCTION). REMOVE SILT FENCE AND OTHER CONTROLS THAT ARE INHIBITING FINAL CONSTRUCTION AND ARE NO LONGER NEEDED. CONTRACTOR MAY MARKUP NEW LOCATION (AND/OR AREAS OF BMPS REMOVED) AND DATE THE CHANGE ON A PAPER COPY OF THE BMP PLAN ONSITE. FINALLY, REMOVE ANY REMAINING EROSION CONTROL MEASURES AND PROTECT ANY REMAINING DISTURBED AREAS WITH SEED AND MULCH COVER.

ALL ESC/BMP DETAILS MUST REFER TO VDEQ DETAILS.

NPDES NOI INFORMATION

AREA OF SITE: 0.80 ACRES

AREA OF DISTURBANCE: 0.45 ACRES

SHEET LEGEND

GRAPHIC	DESCRIPTION
SF	SILT FENCE REFER TO VDOT 113.07
LOD	LIMITS OF DISTURBANCE
	CONSTRUCTION LIMIT
	INLET PROTECTION
	6" CHAIN LINK CONSTRUCTION FENCE
	CONSTRUCTION ENTRANCE
	LINER
TS	TEMPORARY SLOPE STABILIZATION: REFER TO VDOT DETAIL 113.02
PS	PERMANENT SLOPE STABILIZATION: REFER TO VDOT DETAIL 113.05
IP	INLET PROTECTION: REFER TO VDOT DETAIL 113.10

N

A1

1:10'

0 10 20

FEET

EPSC PLAN NORTH

NAVFAC

COMMONWEALTH OF VIRGINIA

Stephen Elmer Garland, Sr.
No. 042865

Schmidt PRIME, Inc.

911 West Garden Street
Pensacola, Florida 32502
P: 850-438-0050
schmidtconsultinggroup.com

APPROVED

Car M. Miller

FOR COMMANDER NAVFAC

ACTIVITY: BILL BOUNDS, OLA

SATISFACTORY TO DATE: 14 JAN. 2026

SG	PAE	RB
----	-----	----

PM/DM: W. WITHAM, P.E.
BRANCH MANAGER: W. WITHAM, P.E.
CHIEF ENG/ARCH: J. MILLER, P.E.
FIRE PROTECTION: N/A

NAVFACILITIES ENGINEERING SYSTEMS COMMAND
NAVAL STATION - NORFOLK
NORFOLK, VIRGINIA

LP-38 BERM RECERTIFICATION REPAIR

EPSC PLAN SOUTH

SCALE:

PROJECT NO.: 1766588

CONSTR. CONTR. NO.: N40085-22-D-0039

NAVFAC DRAWING NO.: 12940919

SHEET 12 OF 19

EC-101

DRAWFORM REVISION: 14 SEP 2023



5

- 1:10'
- 0 10 20
- FEET

A

PLAN VIEW (GATE CLOSED)



NOT TO SCALE

NOT TO SCALE



SG	PAE	RB
PM/DM :W, WITHAM, P.E.		

MAND	C	VA	NIA
------	---	----	-----

LE

SEEKING
MID-AT
TION
FOLK
PA
TE, C
S

MANITOWOC

IS C
CA
LINK
EALP

SYS	RT	CHA OIN
-----	----	------------

PEER
RE
ORC
G AN

SHIPY,
ER
E RE
FOR

U.S. NAVY
FACILITIES
CORE
ATION
2-38
AL C
R

DEPARTMENT	AVAILABILITY	TYPE
------------	--------------	------

SCALE:	
EPROJECT NO.:	1766588

NAVFAC DRAWING NO.
12940923

C-502