

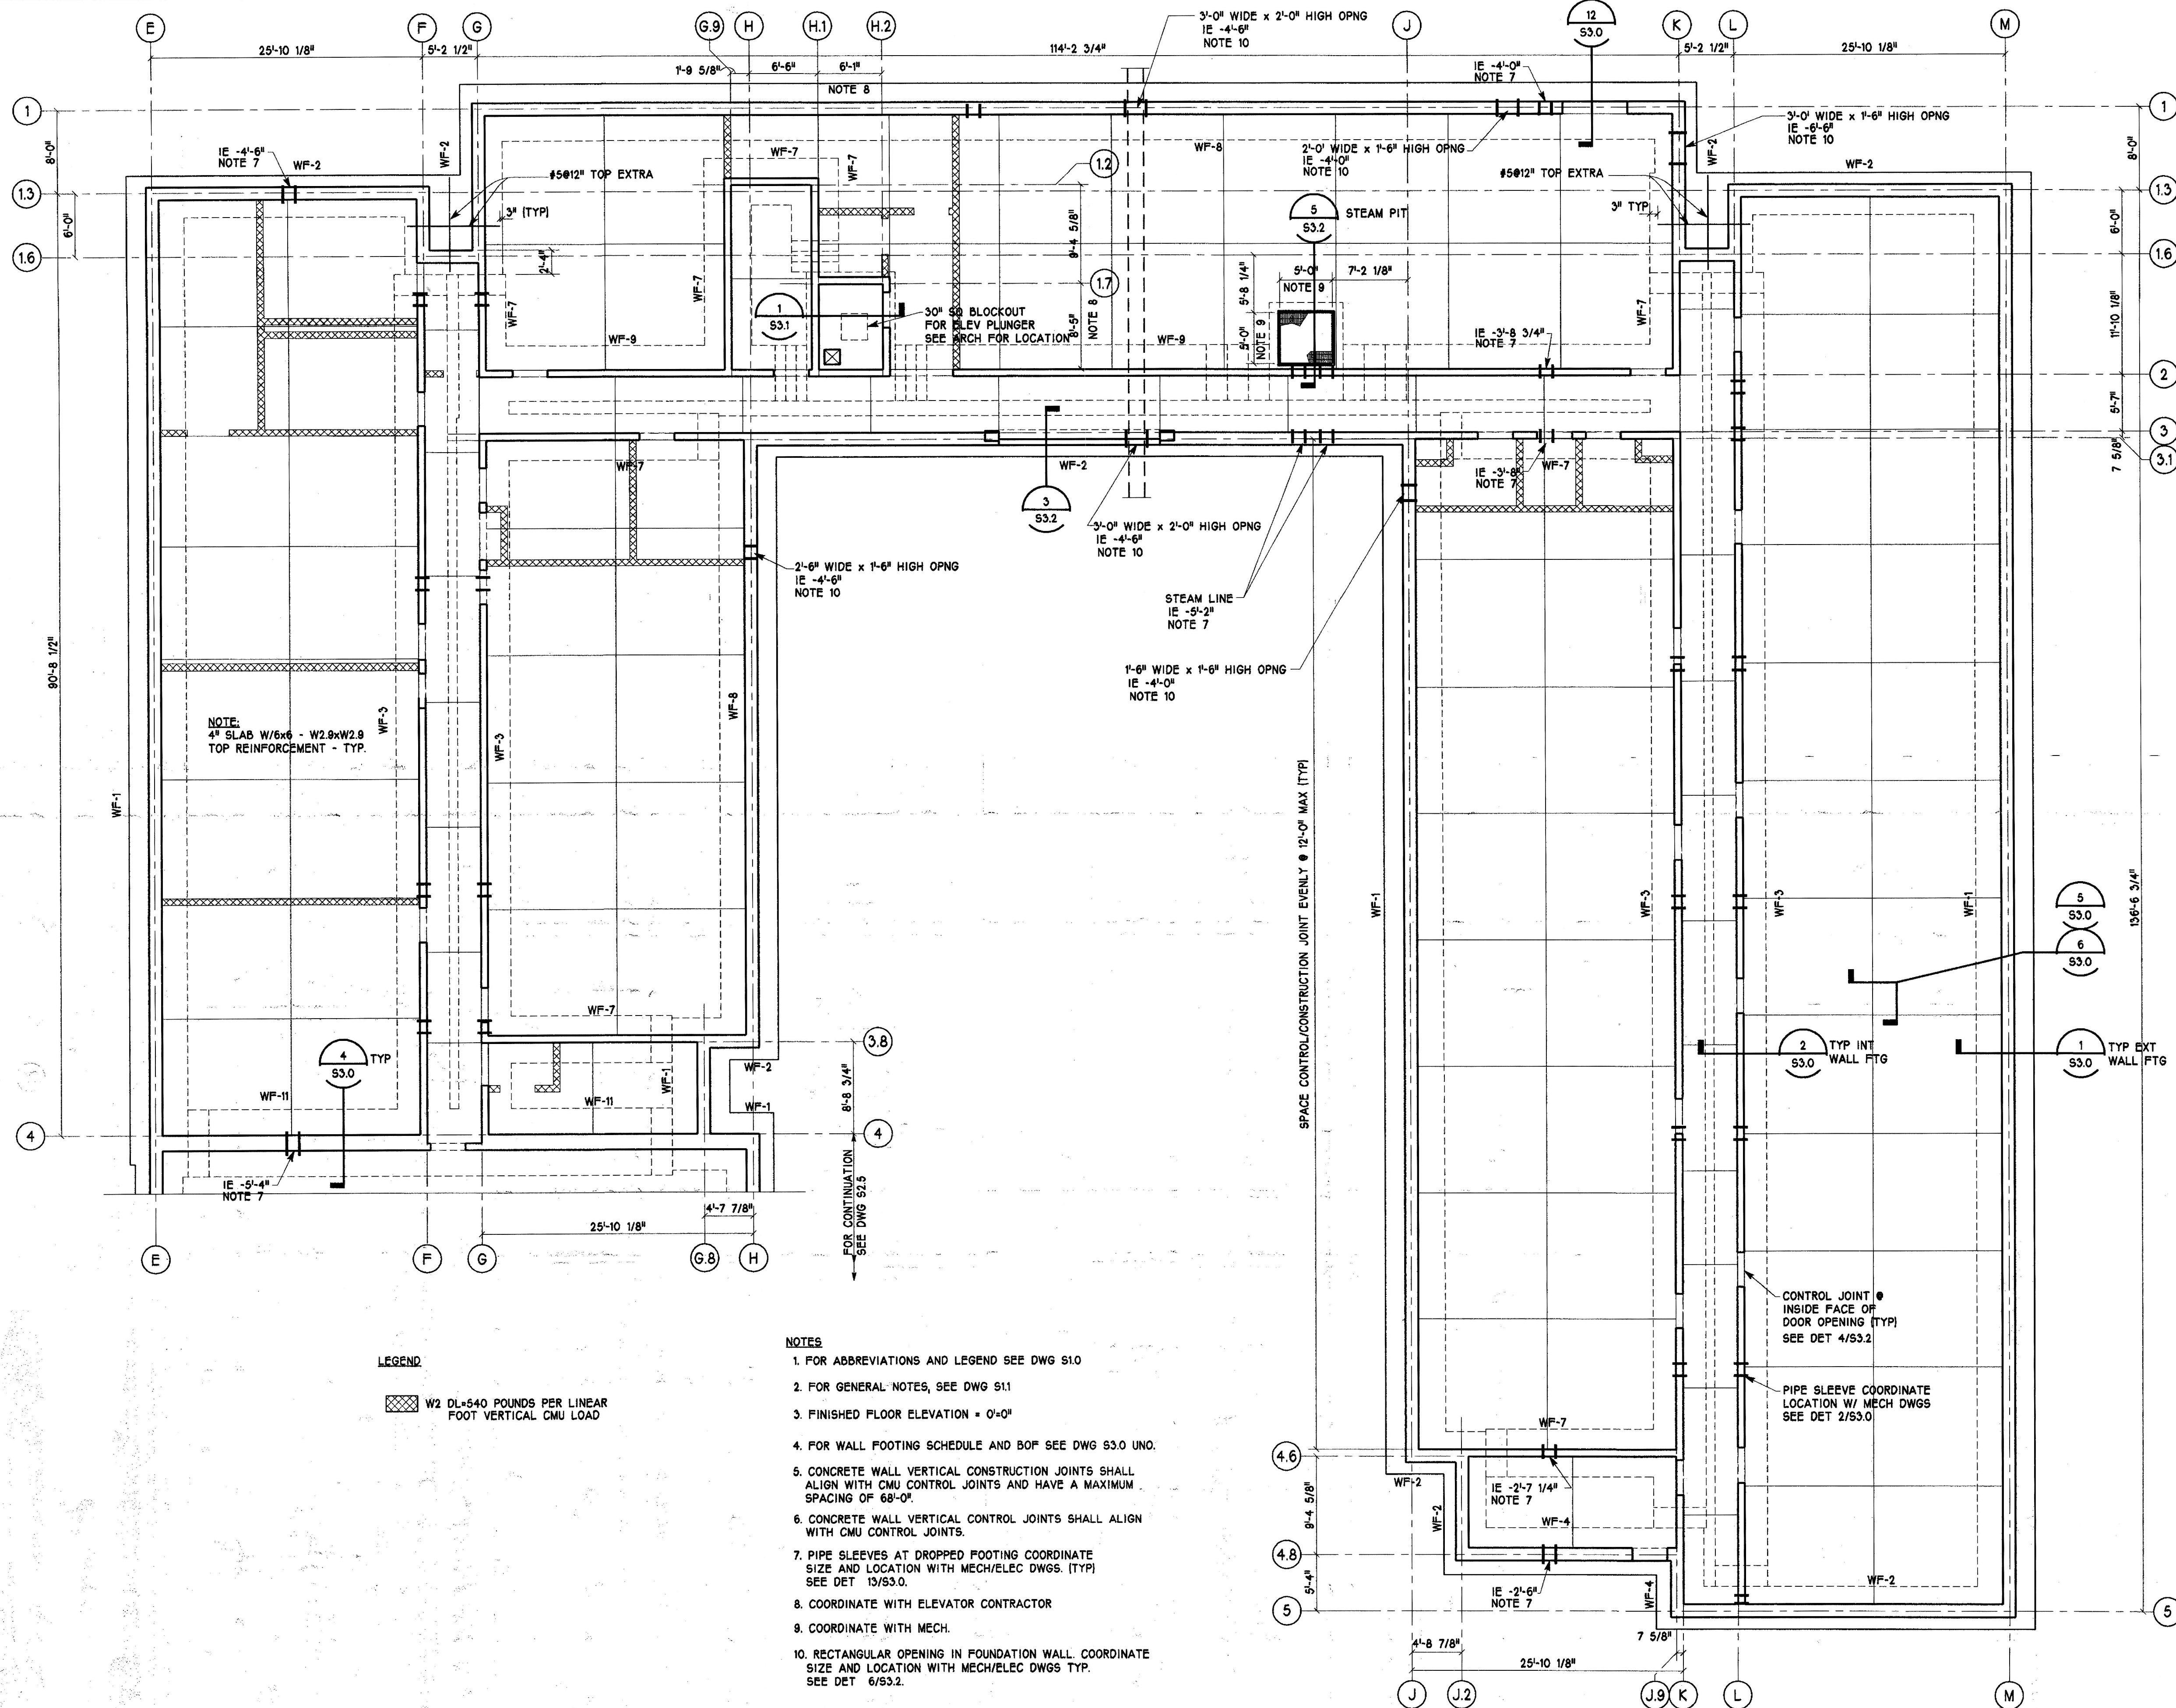


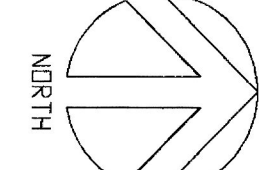

- NOTES
1. FOR ABBREVIATIONS AND LEGEND SEE DWG S1.0
  2. FOR GENERAL NOTES, SEE DWG S1.1
  3. FINISHED FLOOR ELEVATION = 0'-0"
  4. FOR WALL FOOTING SCHEDULE AND BOF SEE DWG S3.0 UNO.
  5. CONCRETE WALL VERTICAL CONSTRUCTION JOINTS SHALL ALIGN WITH CMU CONTROL JOINTS AND HAVE A MAXIMUM SPACING OF 68'-0".
  6. CONCRETE WALL VERTICAL CONTROL JOINTS SHALL ALIGN WITH CMU CONTROL JOINTS.
  7. PIPE SLEEVES AT DROPPED FOOTING COORDINATE SIZE AND LOCATION WITH MECH/ELEC DWGS. (TYP) SEE DET 13/S3.0.
  8. COORDINATE WITH ELEVATOR CONTRACTOR
  9. COORDINATE WITH MECH.
  10. RECTANGULAR OPENING IN FOUNDATION WALL. COORDINATE SIZE AND LOCATION WITH MECH/ELEC DWGS TYP. SEE DET 6/S3.2.

LEGEND

W2 DL-540 POUNDS PER LINEAR FOOT VERTICAL CMU LOAD

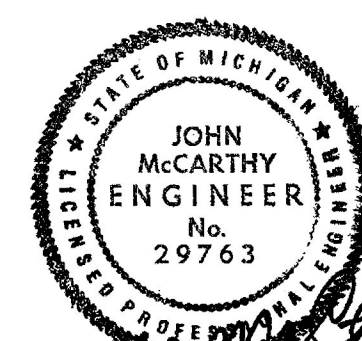

SCALE: 1/8" = 1'-0"

|                        |                           |                                             |                                      |                  |                |                            |                                           |          |
|------------------------|---------------------------|---------------------------------------------|--------------------------------------|------------------|----------------|----------------------------|-------------------------------------------|----------|
| DESIGNED BY: P. TANDOC | PREP BY: DATE: 23 JULY 98 | REV. DESCRIPTION: 1 ISSUED FOR CONSTRUCTION | NAVAL FACILITIES ENGINEERING COMMAND | E. F. A. MIDWEST | NAVAL HOSPITAL | BACHELOR ENLISTED QUARTERS | BUILDING P641 FOUNDATION/FIRST FLOOR PLAN | APPROVED |
| CHECKED BY: R. SKOMRON |                           |                                             | GREAT LAKES, IL                      | GREAT LAKES, IL  | NAVAL HOSPITAL | BACHELOR ENLISTED QUARTERS | BUILDING P641 FOUNDATION/FIRST FLOOR PLAN |          |
| BRANCH HEAD:           |                           |                                             |                                      |                  |                |                            |                                           |          |
| P.E.:                  |                           |                                             |                                      |                  |                |                            |                                           |          |
| PROJ. ENG.:            |                           |                                             |                                      |                  |                |                            |                                           |          |
| DIV. DIR.:             |                           |                                             |                                      |                  |                |                            |                                           |          |

McHUGH

WIGHT

Steinberg/SHG

|                     |                  |
|---------------------|------------------|
| RECORD DRAWING DATE |                  |
| CODE I.D. NO.       | 80091            |
| DRAWING SIZE:       | D                |
| SPEC. NO. 06-       |                  |
| CONSTR. CONTR. NO.  | N62467-96-C-0757 |
| NAVFAC DRAWING NO.  |                  |
| SHEET OF            | S2.0             |