



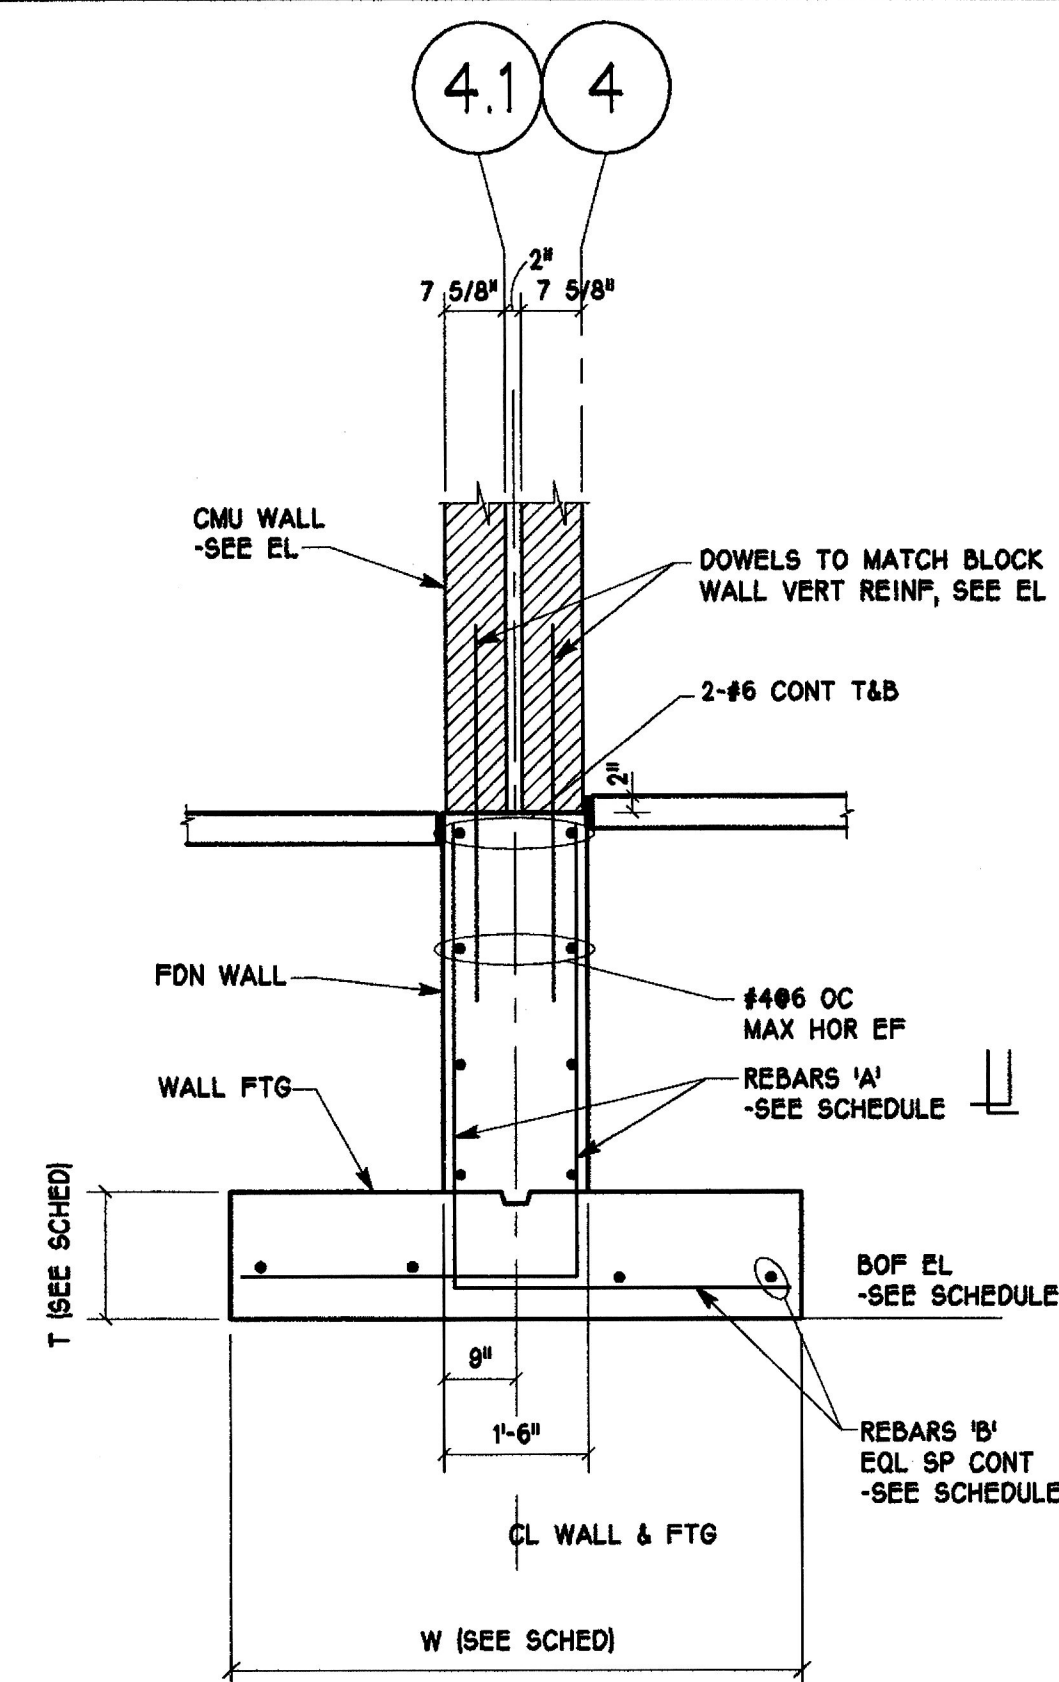


WALL FOOTING TYPE - 3
TYPICAL INTERIOR WALL FOOTING
@ EXPANSION JOINT

4
S2.0
1/2" = 1'-0"

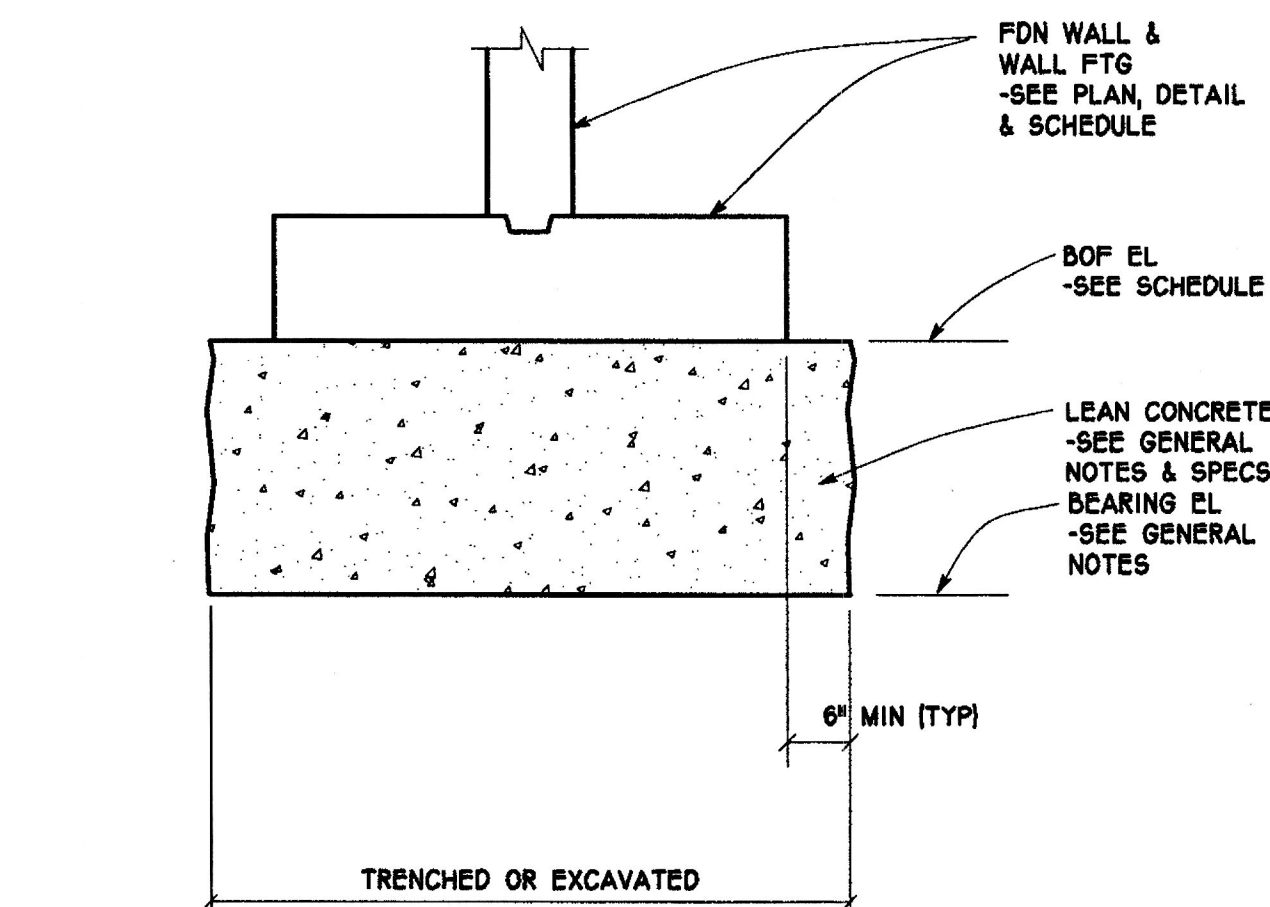


3
TYP
1/2" = 1'-0"

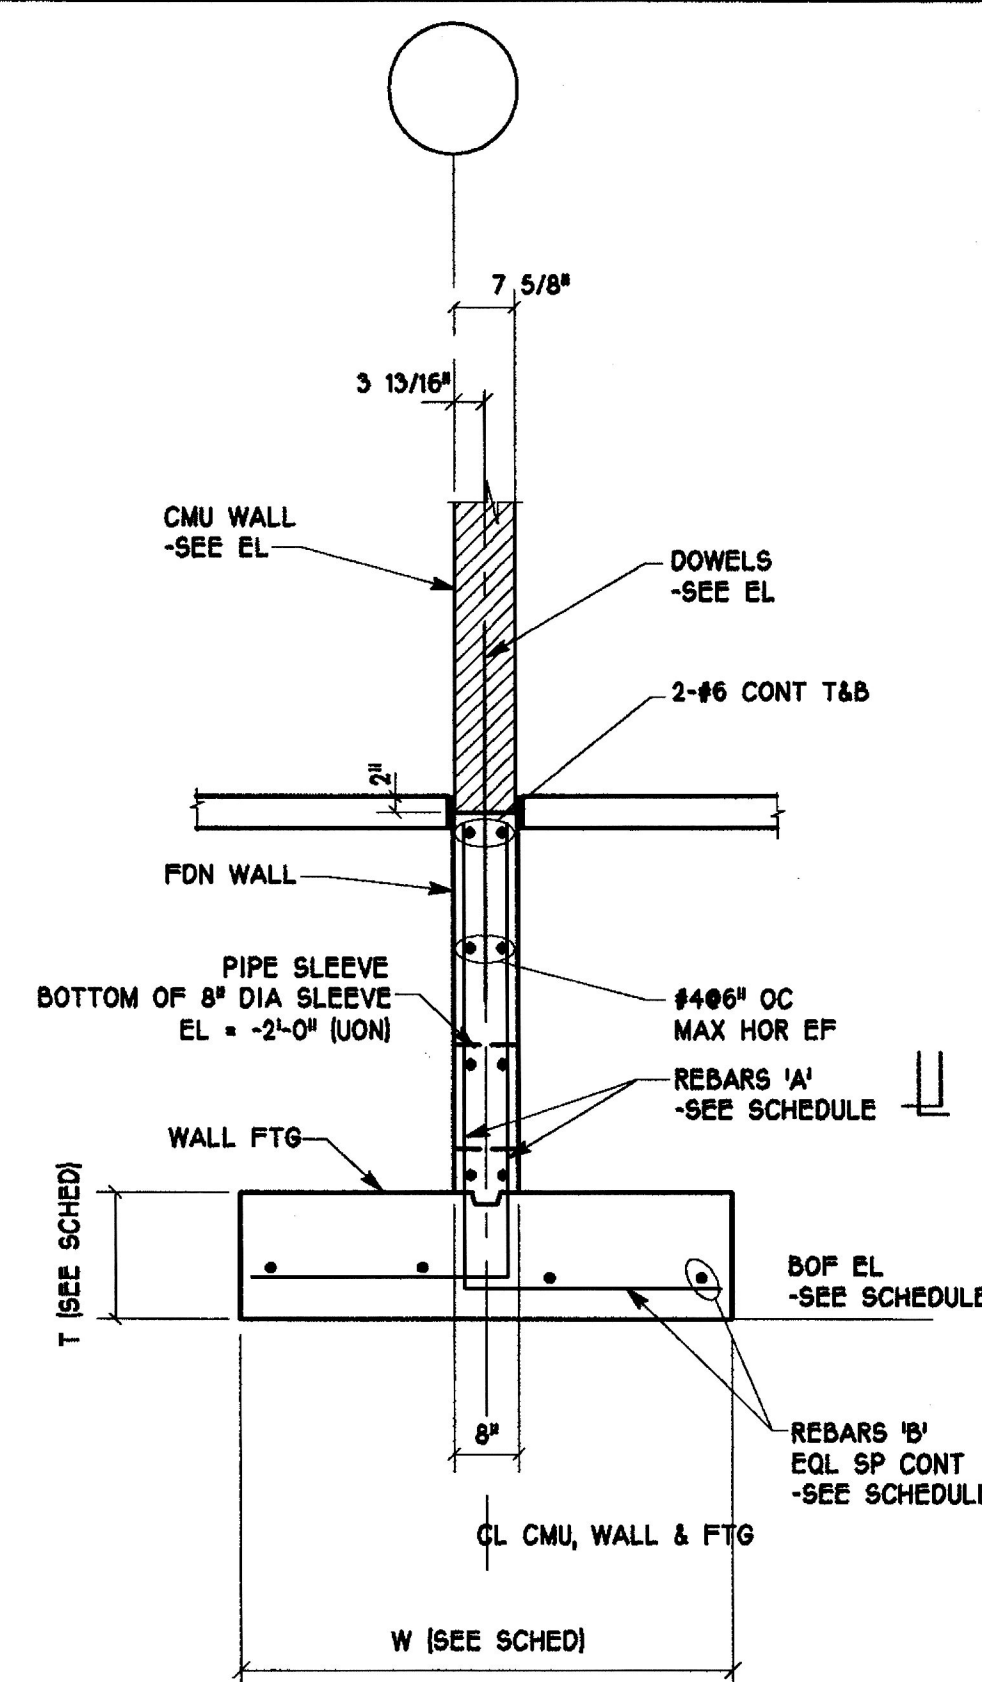


WALL FOOTING TYPE - 2
TYPICAL INTERIOR WALL FOOTING DETAIL

2
TYP
1/2" = 1'-0"

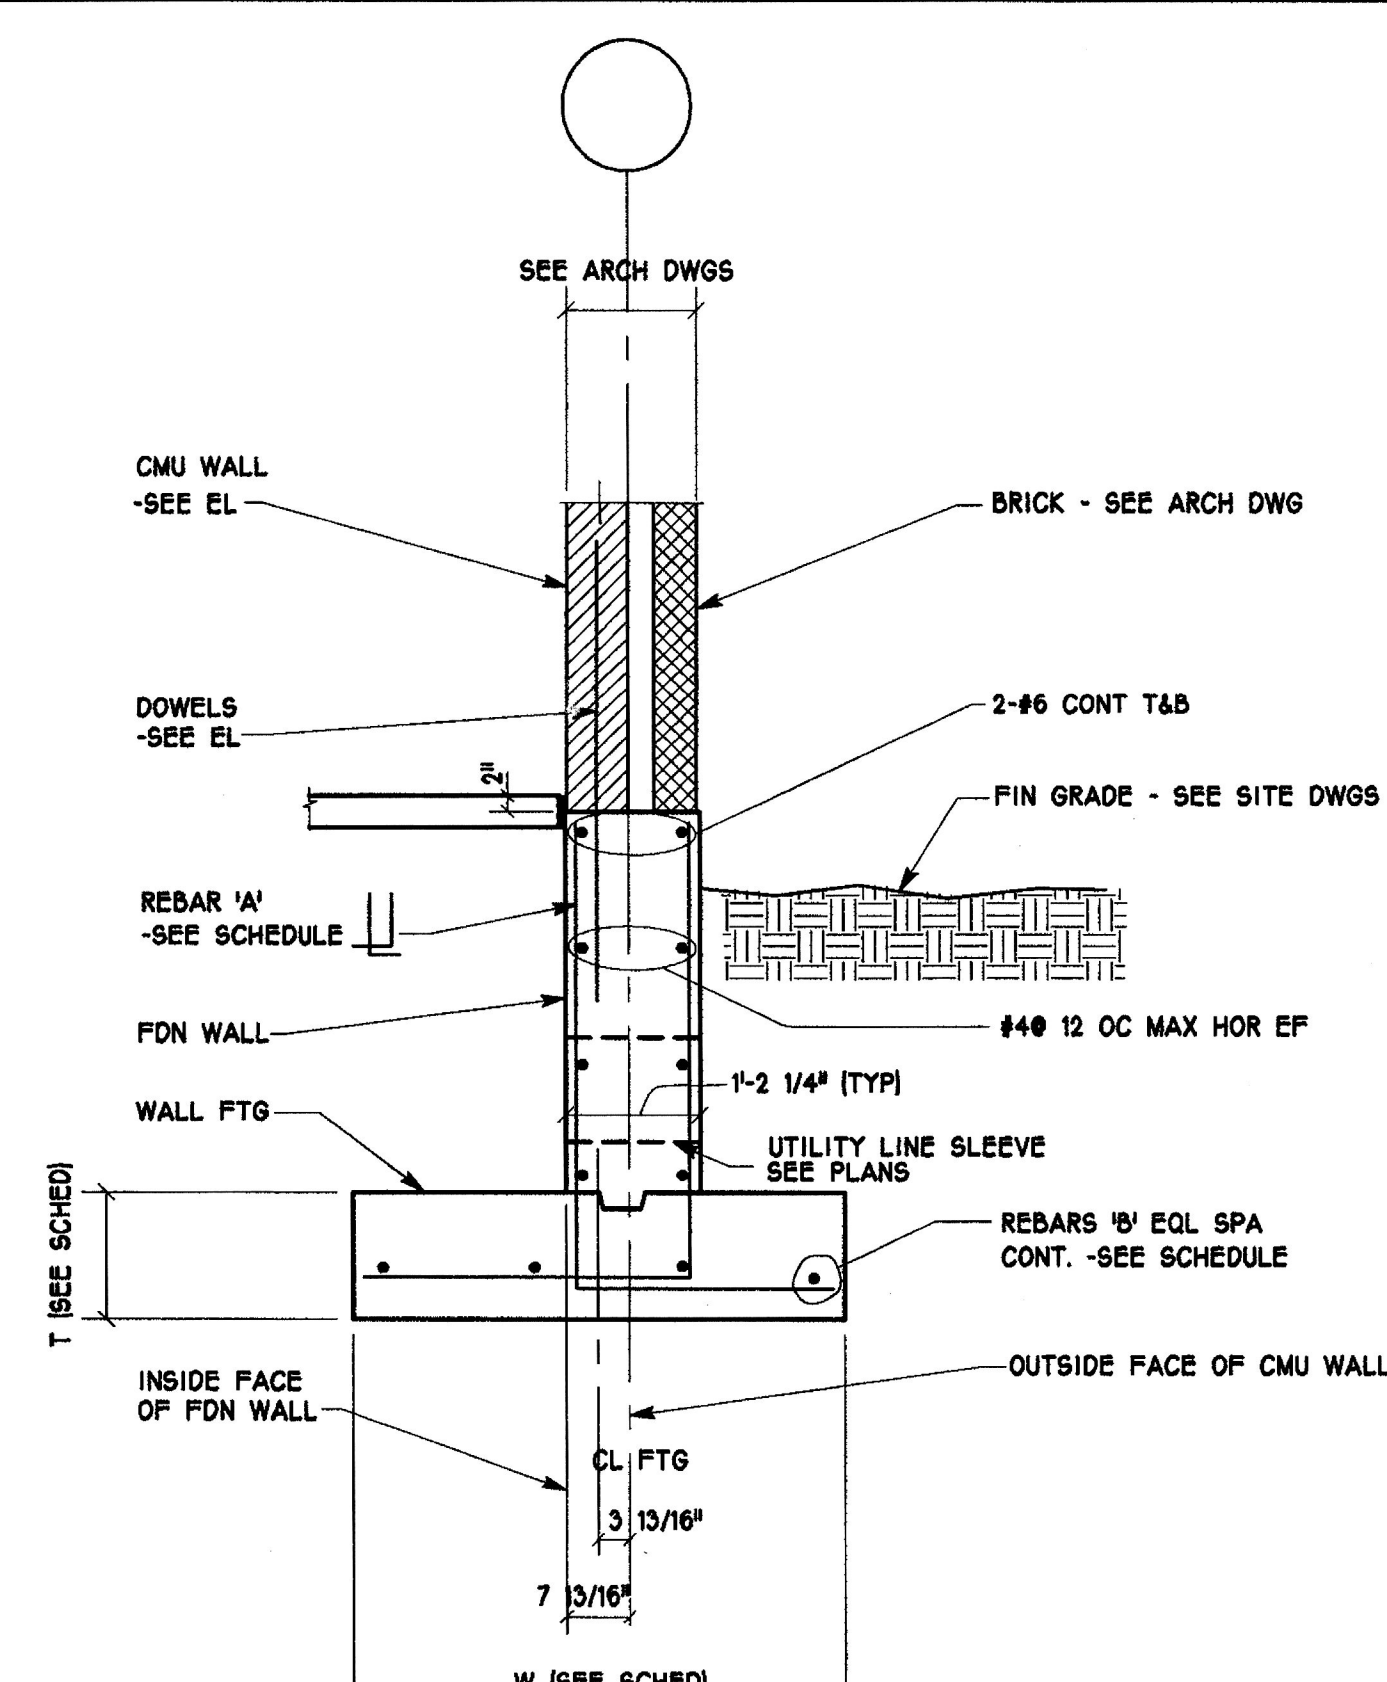


WALL FOOTING TYPE - 1
TYPICAL EXTERIOR WALL FOOTING DETAIL


1
TYP
1/2" = 1'-0"

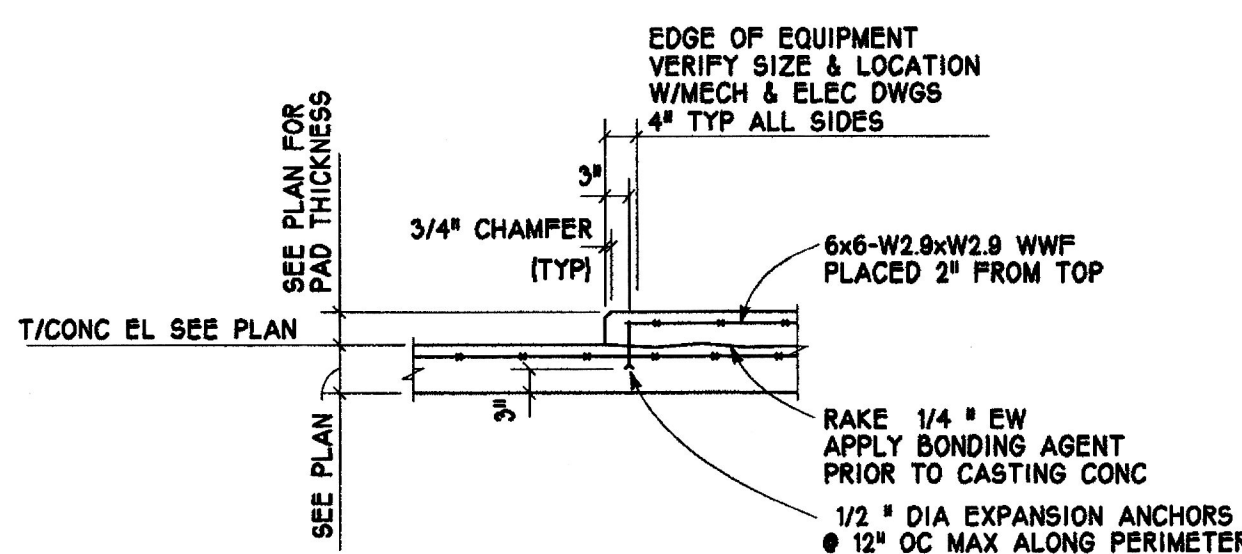


8
TYP
NTS

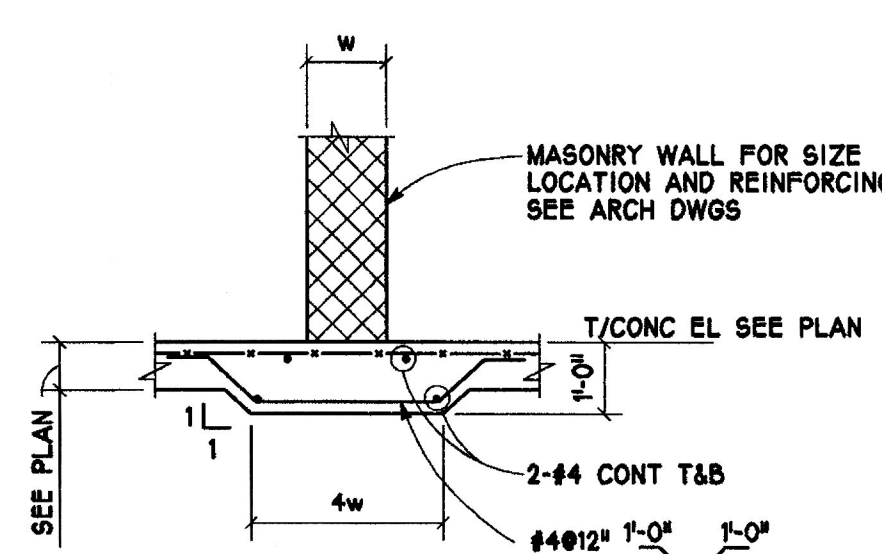

7
TYP
NTS

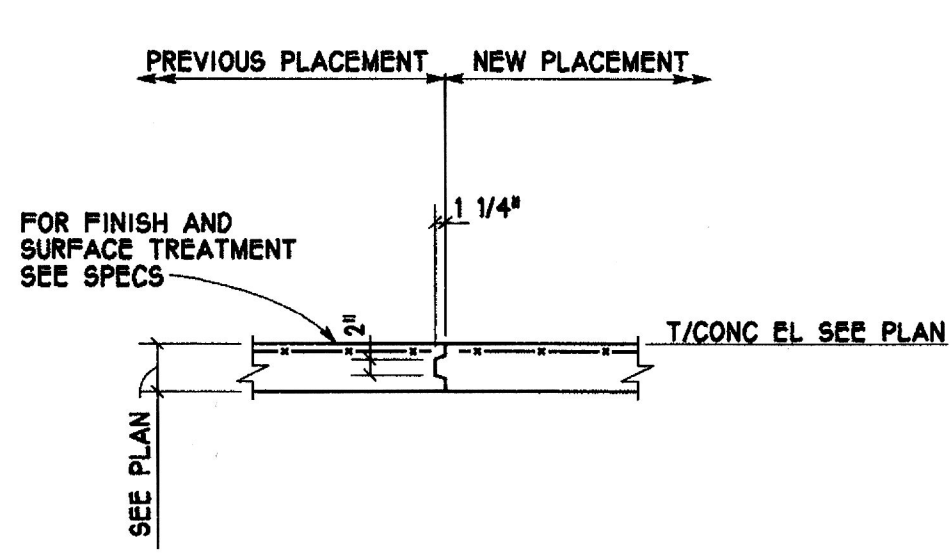


6
TYP
NTS

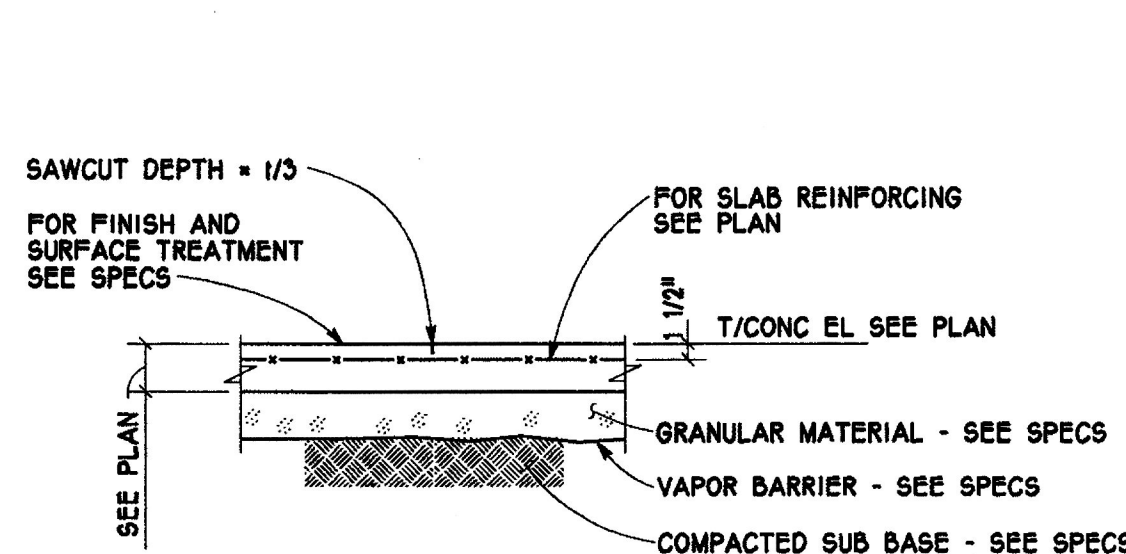


5
TYP
NTS

WALL FOOTING SCHEDULE						
MARK	TYPE	W	T	A	B	BOF EL
WF-1	1	5'-6"	1'-0"	#5@12	6'-4"	-4'-2"
WF-2	1	4'-0"	1'-0"	#4@12	4'-4"	-4'-2"
WF-3	2	5'-0"	1'-0"	#5@12	6'-4"	-3'-2"
WF-4	1	4'-6"	1'-0"	#5@12	5'-4"	-4'-2"
WF-5	1	4'-0"	1'-0"	#4@12	4'-4"	-4'-2"
WF-6	2	3'-6"	1'-0"	#4@12	4'-4"	-3'-2"
WF-7	2	4'-6"	1'-0"	#5@12	5'-4"	-3'-2"
WF-8	1	5'-6"	1'-0"	#6@12	6'-4"	-4'-2"
WF-9	2	5'-6"	1'-0"	#6@12	6'-4"	-3'-2"
WF-10	2	4'-0"	1'-0"	#4@12	4'-4"	-3'-2"
WF-11	3	6'-6"	1'-0"	#6@12	8'-4"	-3'-2"


NOTE:
1. BOTTOM OF FOOTING ELEVATIONS SHOWN ARE REFERRED TO TOP OF FLOOR SLAB EL 0'-0". FOR ACTUAL DATUM ELEVATIONS, SEE SITE DRAWINGS

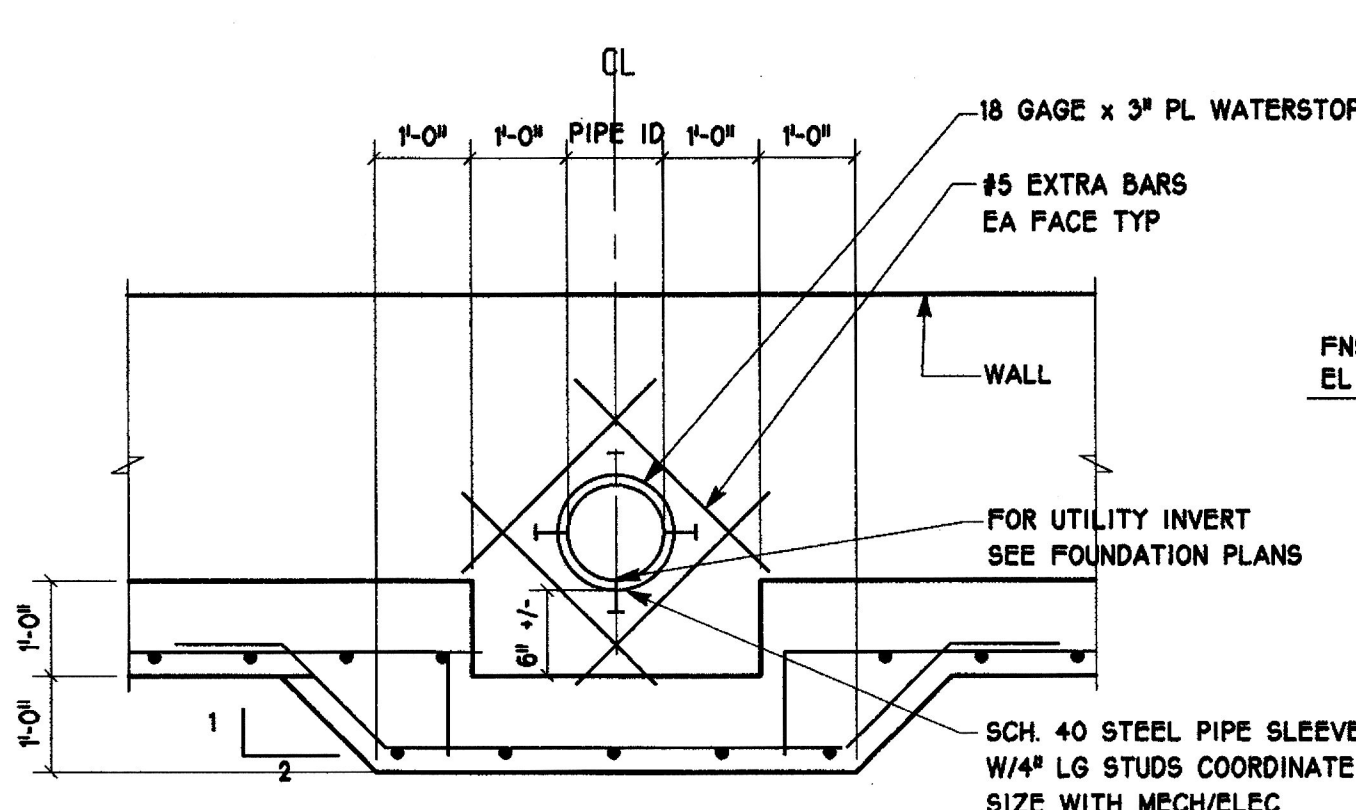


13
TYP
NTS

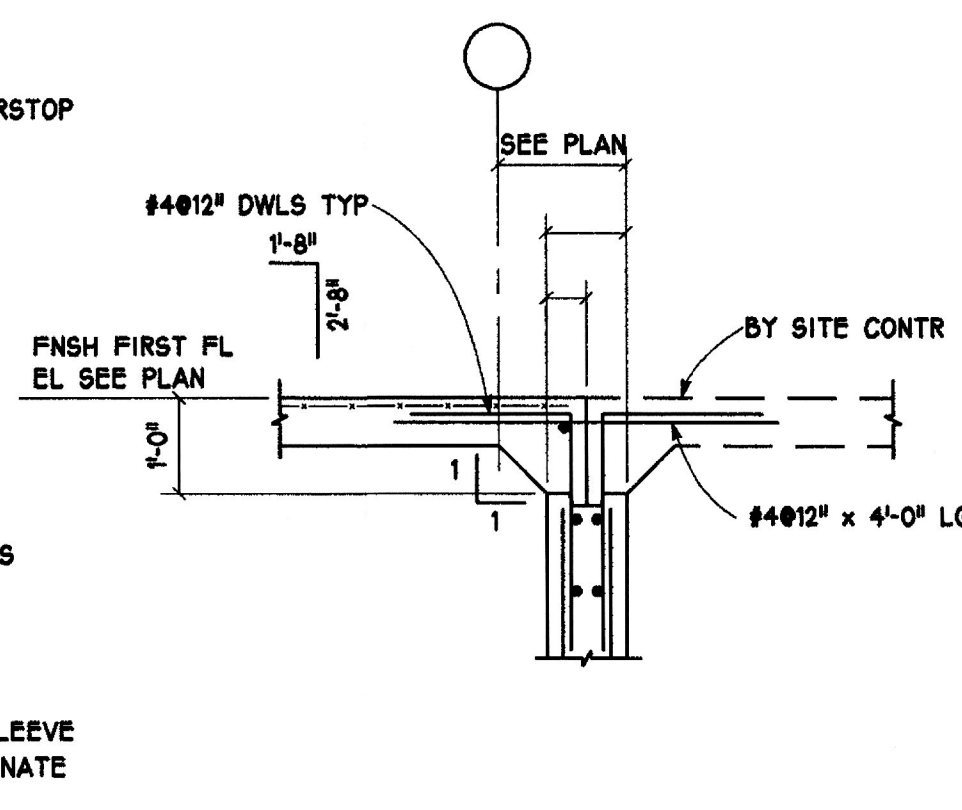


12
TYP
NTS

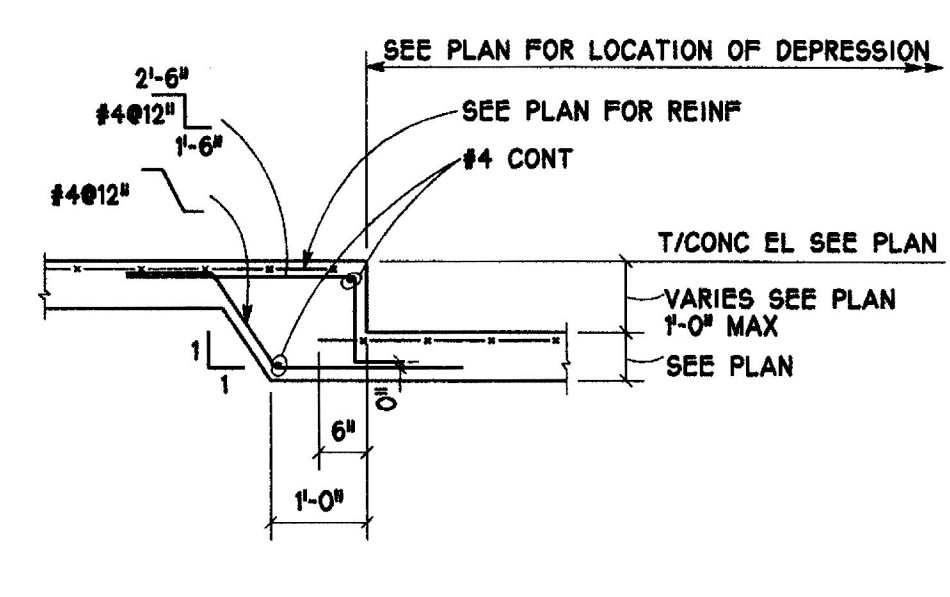


11
TYP
NTS

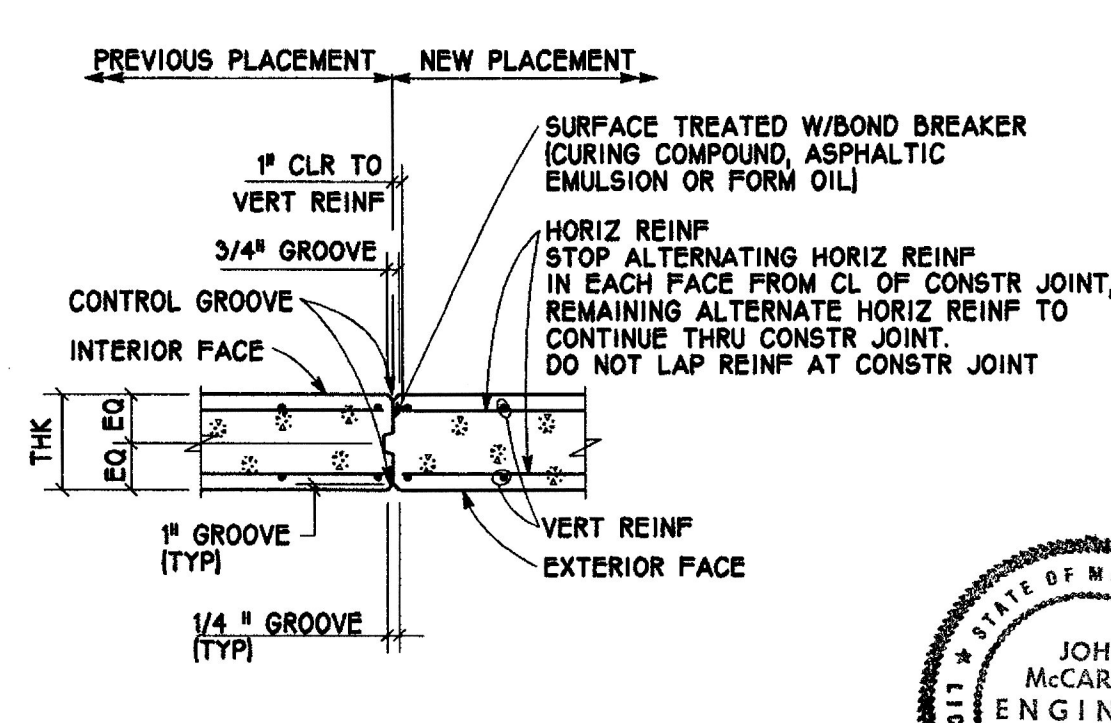

10
TYP
NTS

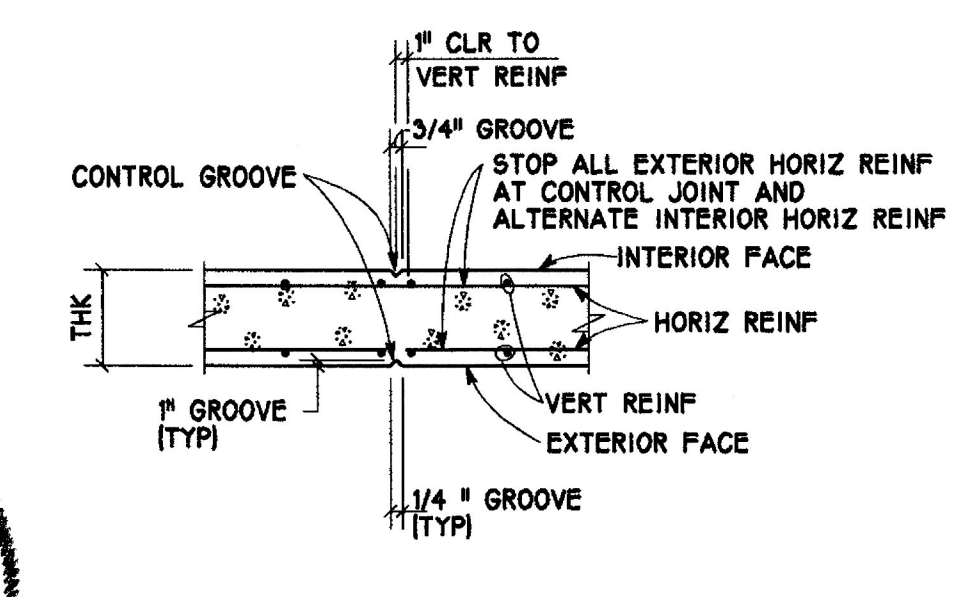

9
TYP
NTS

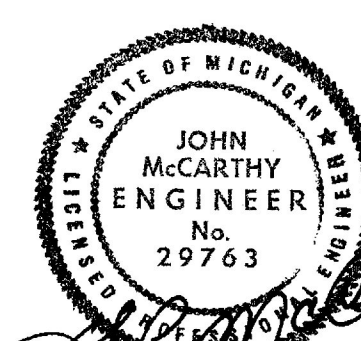

DESIGNED BY: P. TANDOC
DRAWN BY: R. SKORON
CHECKED BY:
BRANCH HEAD:
P.E.:
PROJ. ENG.:
DW. DIR.:
REV. DESCRIPTION PREP BY DATE APPRO
1 ISSUED FOR CONSTRUCTION 23 JULY 98
NAVAL FACILITIES ENGINEERING COMMAND
E F A MIDWEST
GREAT LAKES, IL
NAVAL HOSPITAL
GREAT LAKES
BACHELOR ENLISTED QUARTERS
BUILDING P641 & P641A SPREAD FOOTING SCHEDULE & DETAILS
EFD FOR COMMANDER, NAVFAC
APPROVED
DATE
RECORD DRAWING DATE
CODE I.D. NO. 80091
DRAWING SIZE: D
SPEC. NO. 06-
CONSTR. CONTR. NO. N62467-96-C-0757
NAVFAC DRAWING NO.
SHEET OF
S3.0