

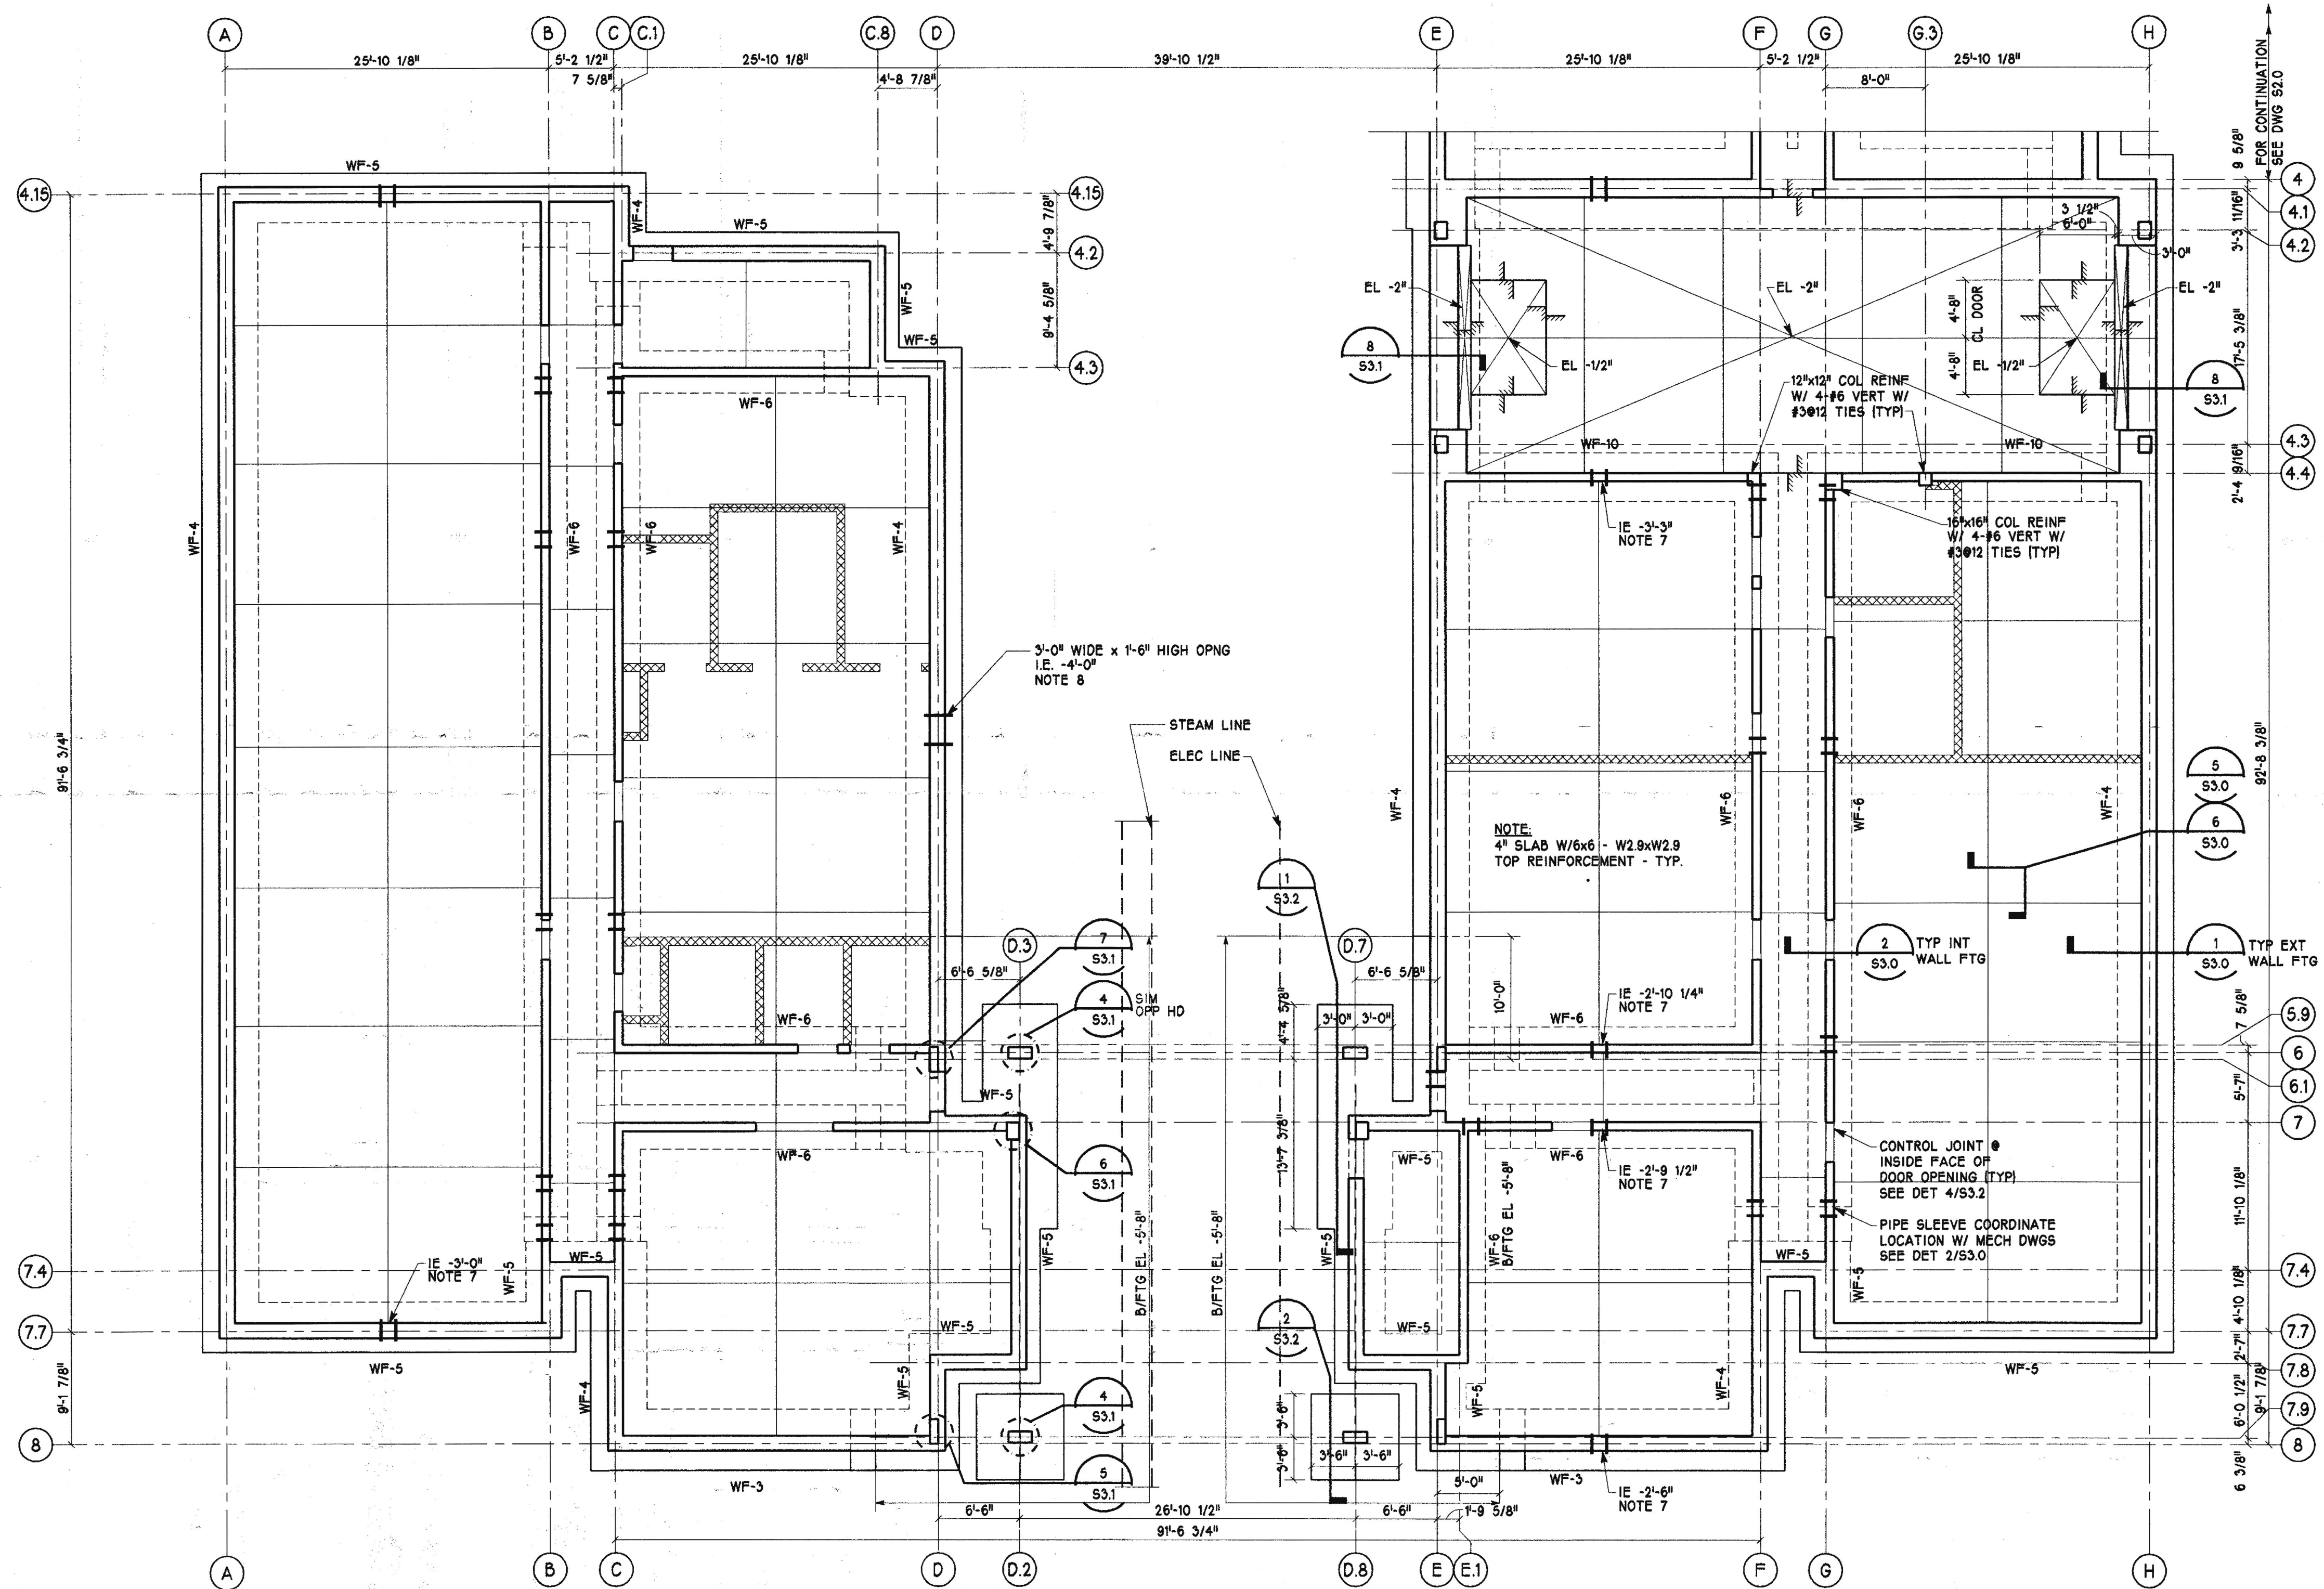


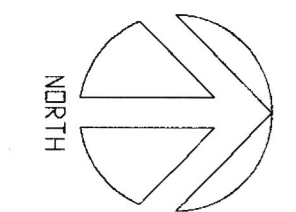

- NOTES**
1. FOR ABBREVIATIONS AND LEGEND SEE DWG S1.0
  2. FOR GENERAL NOTES, SEE DWG S1.01
  3. FINISHED FLOOR ELEVATION = 0'-0"
  4. FOR WALL FOOTING SCHEDULE & BOF SEE DWG S3.0 UON.
  5. CONCRETE WALL VERTICAL CONSTRUCTION JOINTS SHALL ALIGN WITH CMU CONTROL JOINTS AND HAVE A MAXIMUM SPACING OF 68'-0".
  6. CONCRETE WALL VERTICAL CONTROL JOINTS SHALL ALIGN WITH CMU CONTROL JOINTS.
  7. PIPE SLEEVES AT EXTERIOR DROPPED FOOTING COORDINATE SIZE AND LOCATION WITH MECH/ELEC DWGS. (TYP) SEE DET 13/S3.0.
  8. RECTANGULAR OPENING IN FOUNDATION WALL. COORDINATE SIZE AND LOCATION WITH MECH/ELEC DWGS TYP. SEE DET 6/S3.2.

**LEGEND**

W2 DL=540 POUNDS PER LINEAR FOOT VERTICAL CMU LOAD

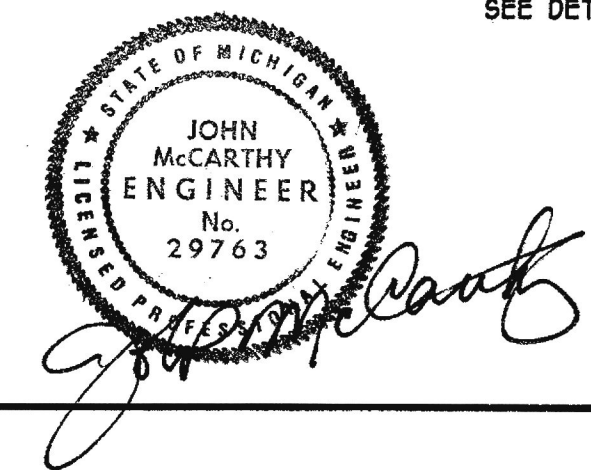

SCALE: 1/8" = 1'-0"

|                        |                                      |               |                 |                                                                          |
|------------------------|--------------------------------------|---------------|-----------------|--------------------------------------------------------------------------|
| DESIGNED BY: P. TANDOC | REV. DESCRIPTION                     | PREP BY       | DATE            | APPROV                                                                   |
| DRAWN BY: R. SKOMRON   | 1 ISSUED FOR CONSTRUCTION            |               | 23 JULY 98      |                                                                          |
| CHECKED BY:            |                                      |               |                 |                                                                          |
| BRANCH HEAD:           |                                      |               |                 |                                                                          |
| P.E.I.                 |                                      |               |                 |                                                                          |
| PROJ. ENG.             |                                      |               |                 |                                                                          |
| DIV. DIR.              |                                      |               |                 |                                                                          |
| DEPARTMENT OF THE NAVY | NAVAL FACILITIES ENGINEERING COMMAND | E F A MIDWEST | GREAT LAKES, IL | BACHELOR ENLISTED QUARTERS<br>BUILDING P641A FOUNDATION/FIRST FLOOR PLAN |
| NAVAL HOSPITAL         |                                      |               |                 |                                                                          |
| RECORD DRAWING DATE    |                                      |               |                 |                                                                          |
| CODE I.D. NO.          |                                      |               |                 | 80091                                                                    |
| DRAWING SIZE:          |                                      |               |                 | D                                                                        |
| SPEC. NO. 06-          |                                      |               |                 |                                                                          |
| CONSTR. CONTR. NO.     |                                      |               |                 | N62467-96-C-0757                                                         |
| NAVFAC DRAWING NO.     |                                      |               |                 |                                                                          |
| SHEET                  |                                      |               |                 | OF                                                                       |
|                        |                                      |               |                 | S2.5                                                                     |