
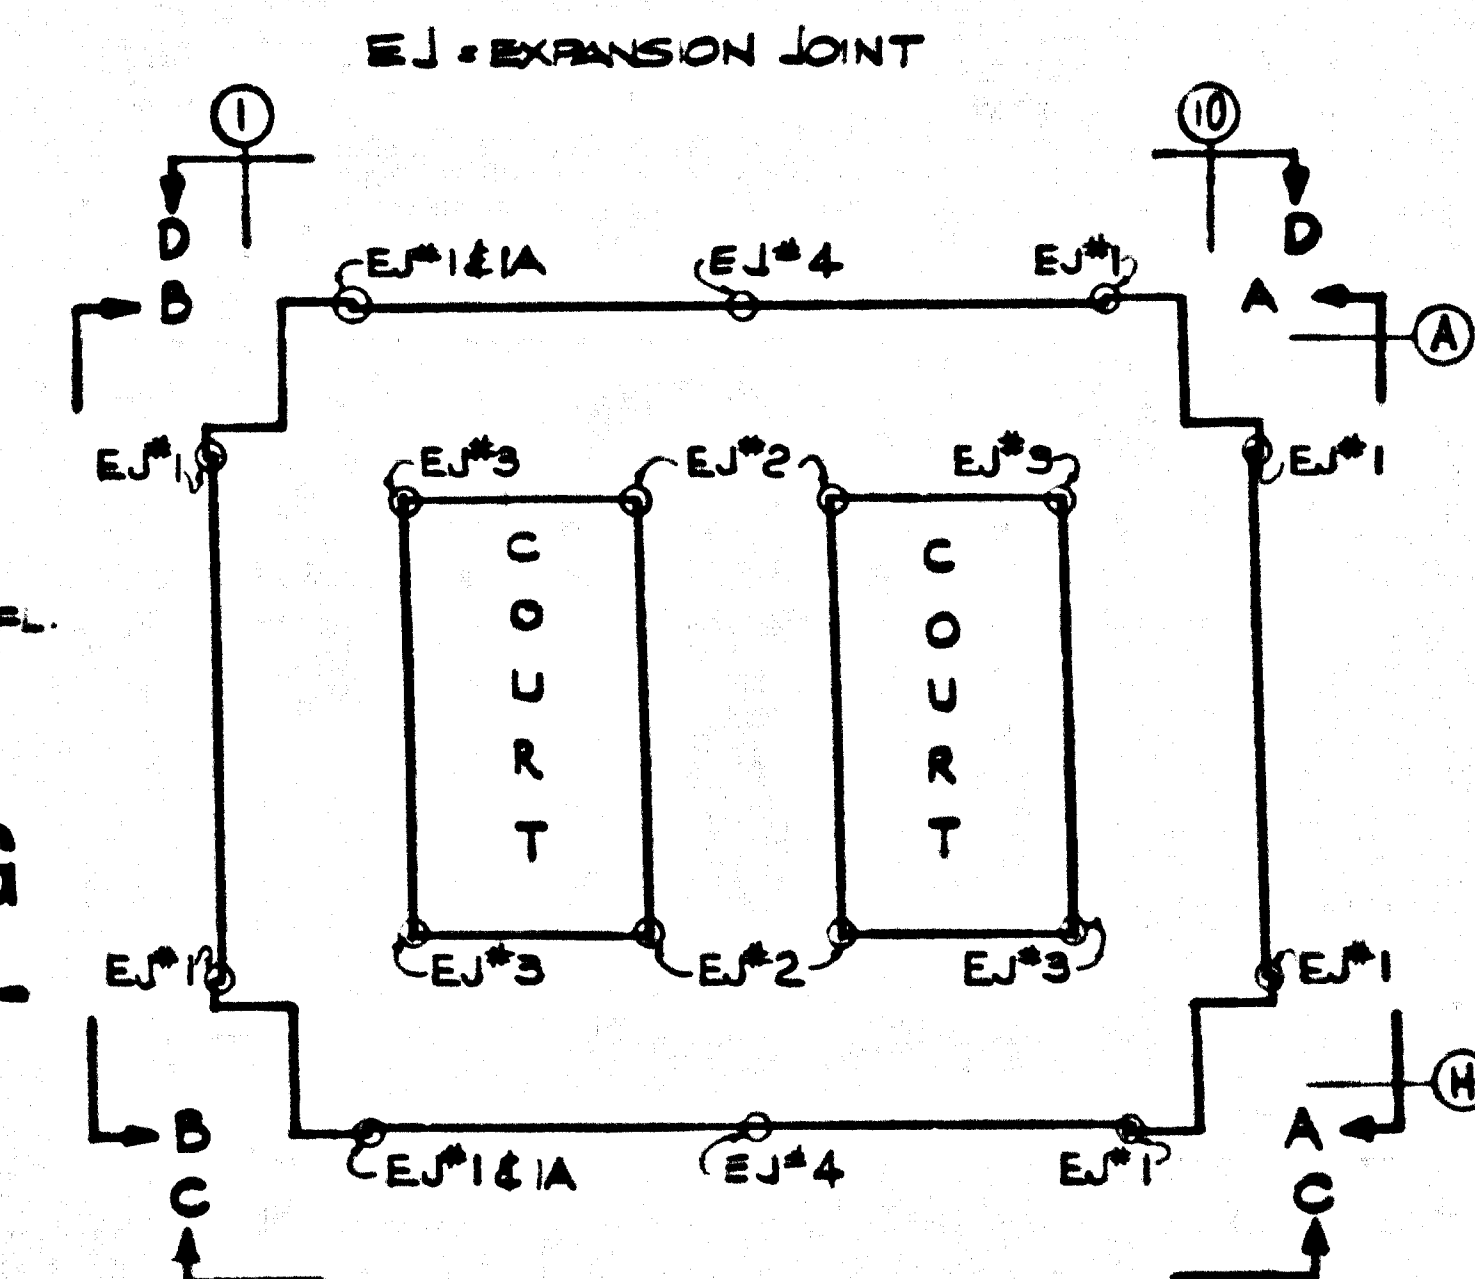
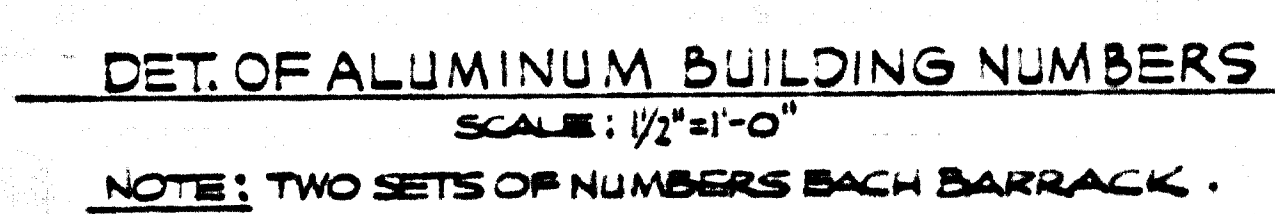
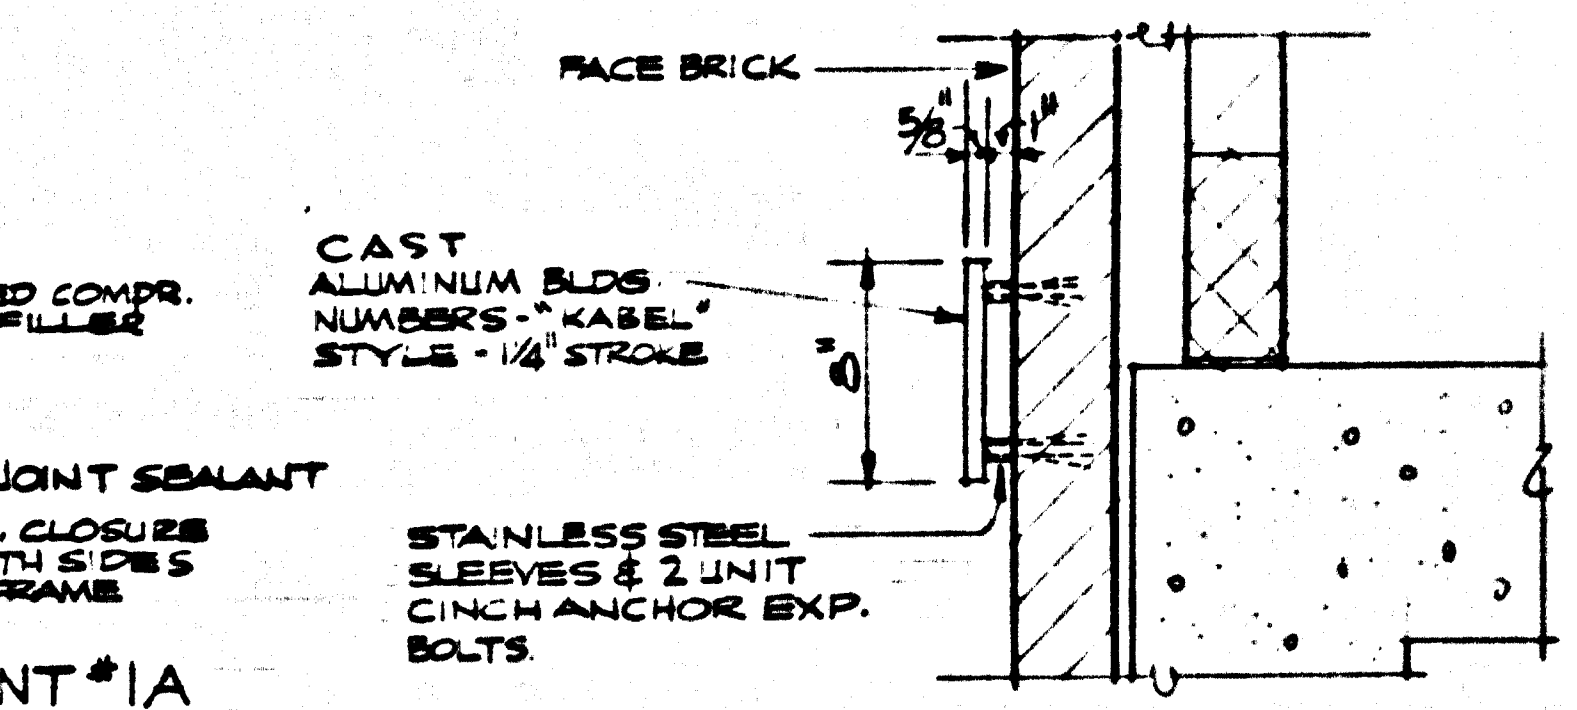


REVISIONS				
SYMBOL	DESCRIPTION	BY	DATE	APPROVAL
A	AM NO 1 INCORPORATED CHANGES BY APPENDIX NO 1	AM	7-20	✓
B	AM NO 3 ADDED ENFNS BY LINE 12 - BARRACKS	CP	---	✓
C	TRAINING CORRECTIONS	WE	---	

AWARDED ON BID ITEM No 4- BLOG 533 DELETED.

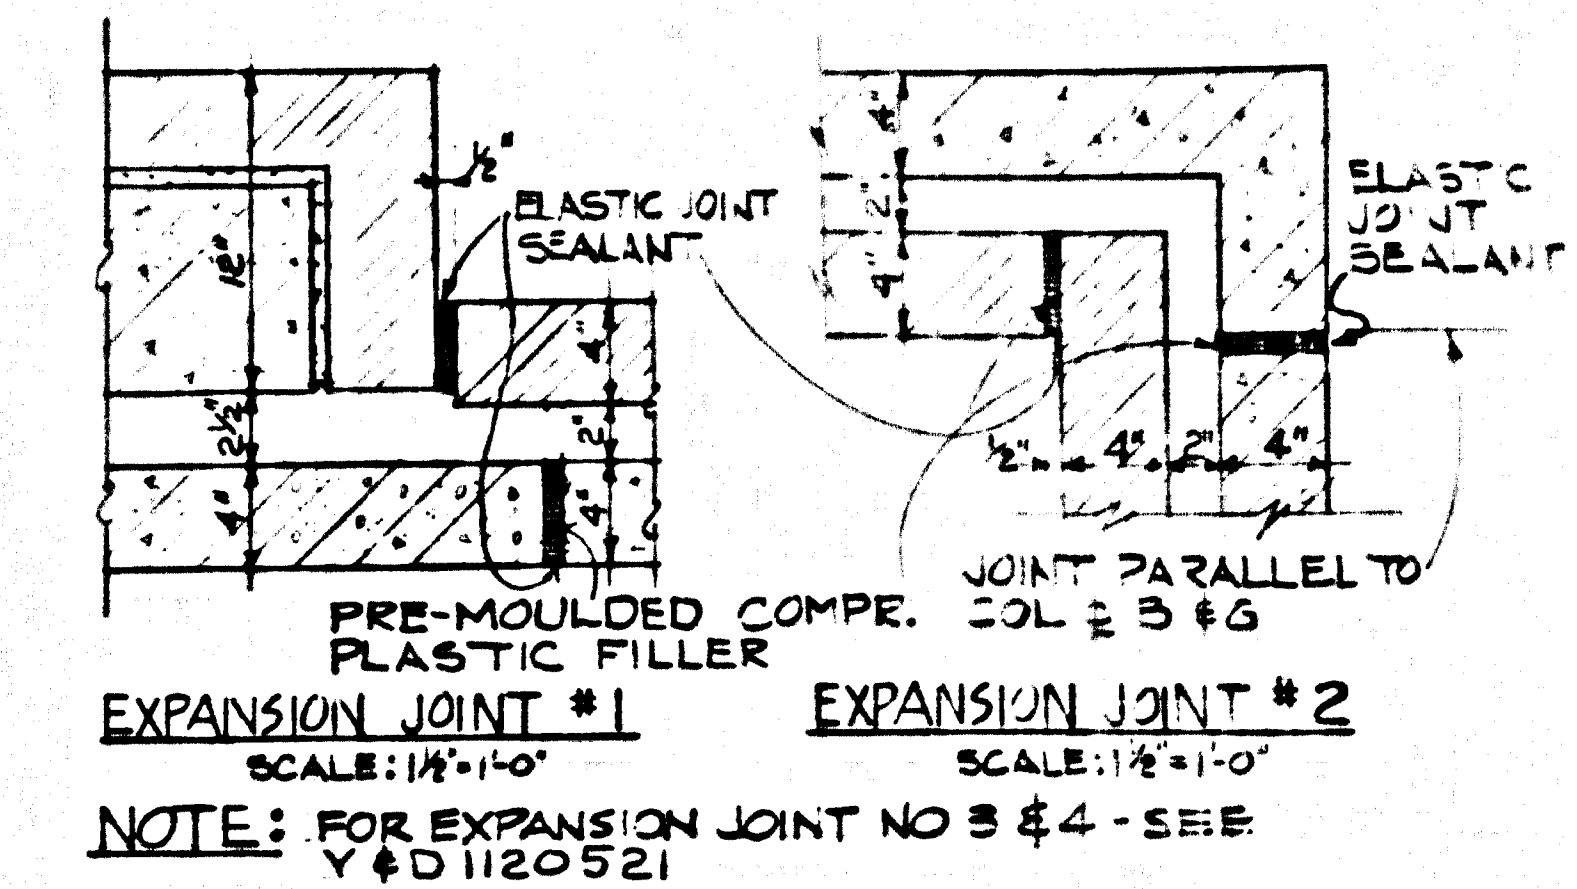

KEY PLAN
NO SCALE
BARRACKS NO. 533

WITH BARRACKS NO. 33 EXCEPT ORIENTATION.

CHILD & SMITH, INCORPORATED
ARCHITECTURE - ENGINEERING
100 N. WADSWORTH DR.
CHICAGO, ILL.

DATE 10/23/68 CHG. 10/23

SUPPLY 10/23/68 10/23

SUBMITTED BY 10/23/68 DATE 10/23/68

FILE 10/23/68 10/23/68

PREPARED BY 10/23/68

APPROVED BY 10/23/68 DATE 10/23/68

FORWARDED BY 10/23/68 DATE 10/23/68

RECEIVED BY 10/23/68 DATE 10/23/68

MAIL ROOM TO/FROM CHIEF MAIL ROOM

DEPARTMENT OF THE NAVY
MIDWEST DIVISION
GREAT LAKES, ILLINOIS

U.S. NAVAL TRAINING CENTER ILLINOIS

GREAT LAKES

SERVICE SCHOOL BARRACKS AND MESS HALL
(MOO BLOCK)
BKS 532-EXTERIOR ELEVATIONS
ARCHITECTURAL

SIZE CODE IDENT NO. V & S DRAWING NO.

FIG. # 80091 1120520

SCALE 1/4" = 1'-0" SPEC. 051-002-00 N. 051-000 SHEET 20 OF 128

