 
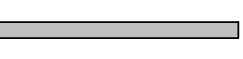


LEGEND:

 EXISTING WALL ASSEMBLY TO REMAIN


 DOOR - SEE DOOR SCHEDULE

 NEW CMU WALLS
(SEE WALL TYPE PLAN)


 NEW METAL FRAMING WALLS
(SEE WALL TYPE PLAN)


 NEW CONCRETE FLOOR SLAB. INSTALL
NEW SLAB ON TOP OF VAPOR BARRIER
(SEE 03 3000) OVER 6" OF CRUSHED
AGGREGATE BASE COMPACTED TO
100% MODIFIED DENSITY - REFER TO
STRUCTURAL FOR REINFORCING AND
OTHER REQUIREMENTS


 STC 50 RATED WALL
CONSTRUCTION. WALLS TO
EXTEND AND BE SEALED TIGHT TO
SECOND FLOOR SLAB ABOVE.
PATCH AND FILL ALL OPENINGS IN
EXISTING MASONRY WALLS
SCHEDULED TO REMAIN.

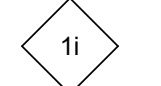 WINDOW / STOREFRONT

 DOOR TAG - SEE
DOOR SCHEDULE

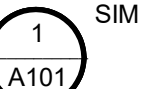 DETAIL SECTION

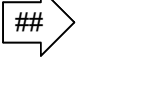 SPECIFIC NOTE TAG

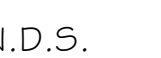 NEW DOWNSPOUT

SPECIFIC NOTES:

- 1

SOLID 6" WIDE PAINTED RED LINE. COORDINATE EXACT LOCATION WITH CONTRACTING OFFICER REPRESENTATIVE ON SITE.
- 2

DASHED 6" WIDE PAINTED RED LINE. COORDINATE EXACT LOCATION WITH CONTRACTING OFFICER REPRESENTATIVE ON SITE.
- 3

NEW DOWNSPOUT. MATCH EXISTING SIZE PROFILE AND CONNECT TO EXISTING GUTTER.
- 4



PATCH AND PAINT CMU IN THIS LOCATION. PROVIDE NEW 4" CMU TO INFILL VOID AT ELECTRICAL PANEL SCHEDULED TO BE REMOVED.
- 5

6" WIDE SOLID YELLOW PAINTED LINE - COORDINATE EXACT LOCATION/EXTENTS WITH CONTRACTING OFFICER REPRESENTATIVE ON SITE
- 6



PAINTED YELLOW STOP BAR. 36" X 12". COORDINATE EXACT LOCATION WITH CONTRACTING OFFICER REPRESENTATIVE ON SITE.
- 7

PAINTED GREEN BOX. 6" WIDE LINE, 24" X 24" SQUARE CENTERED ON EMERGENCY FIXTURE

KEY PLAN

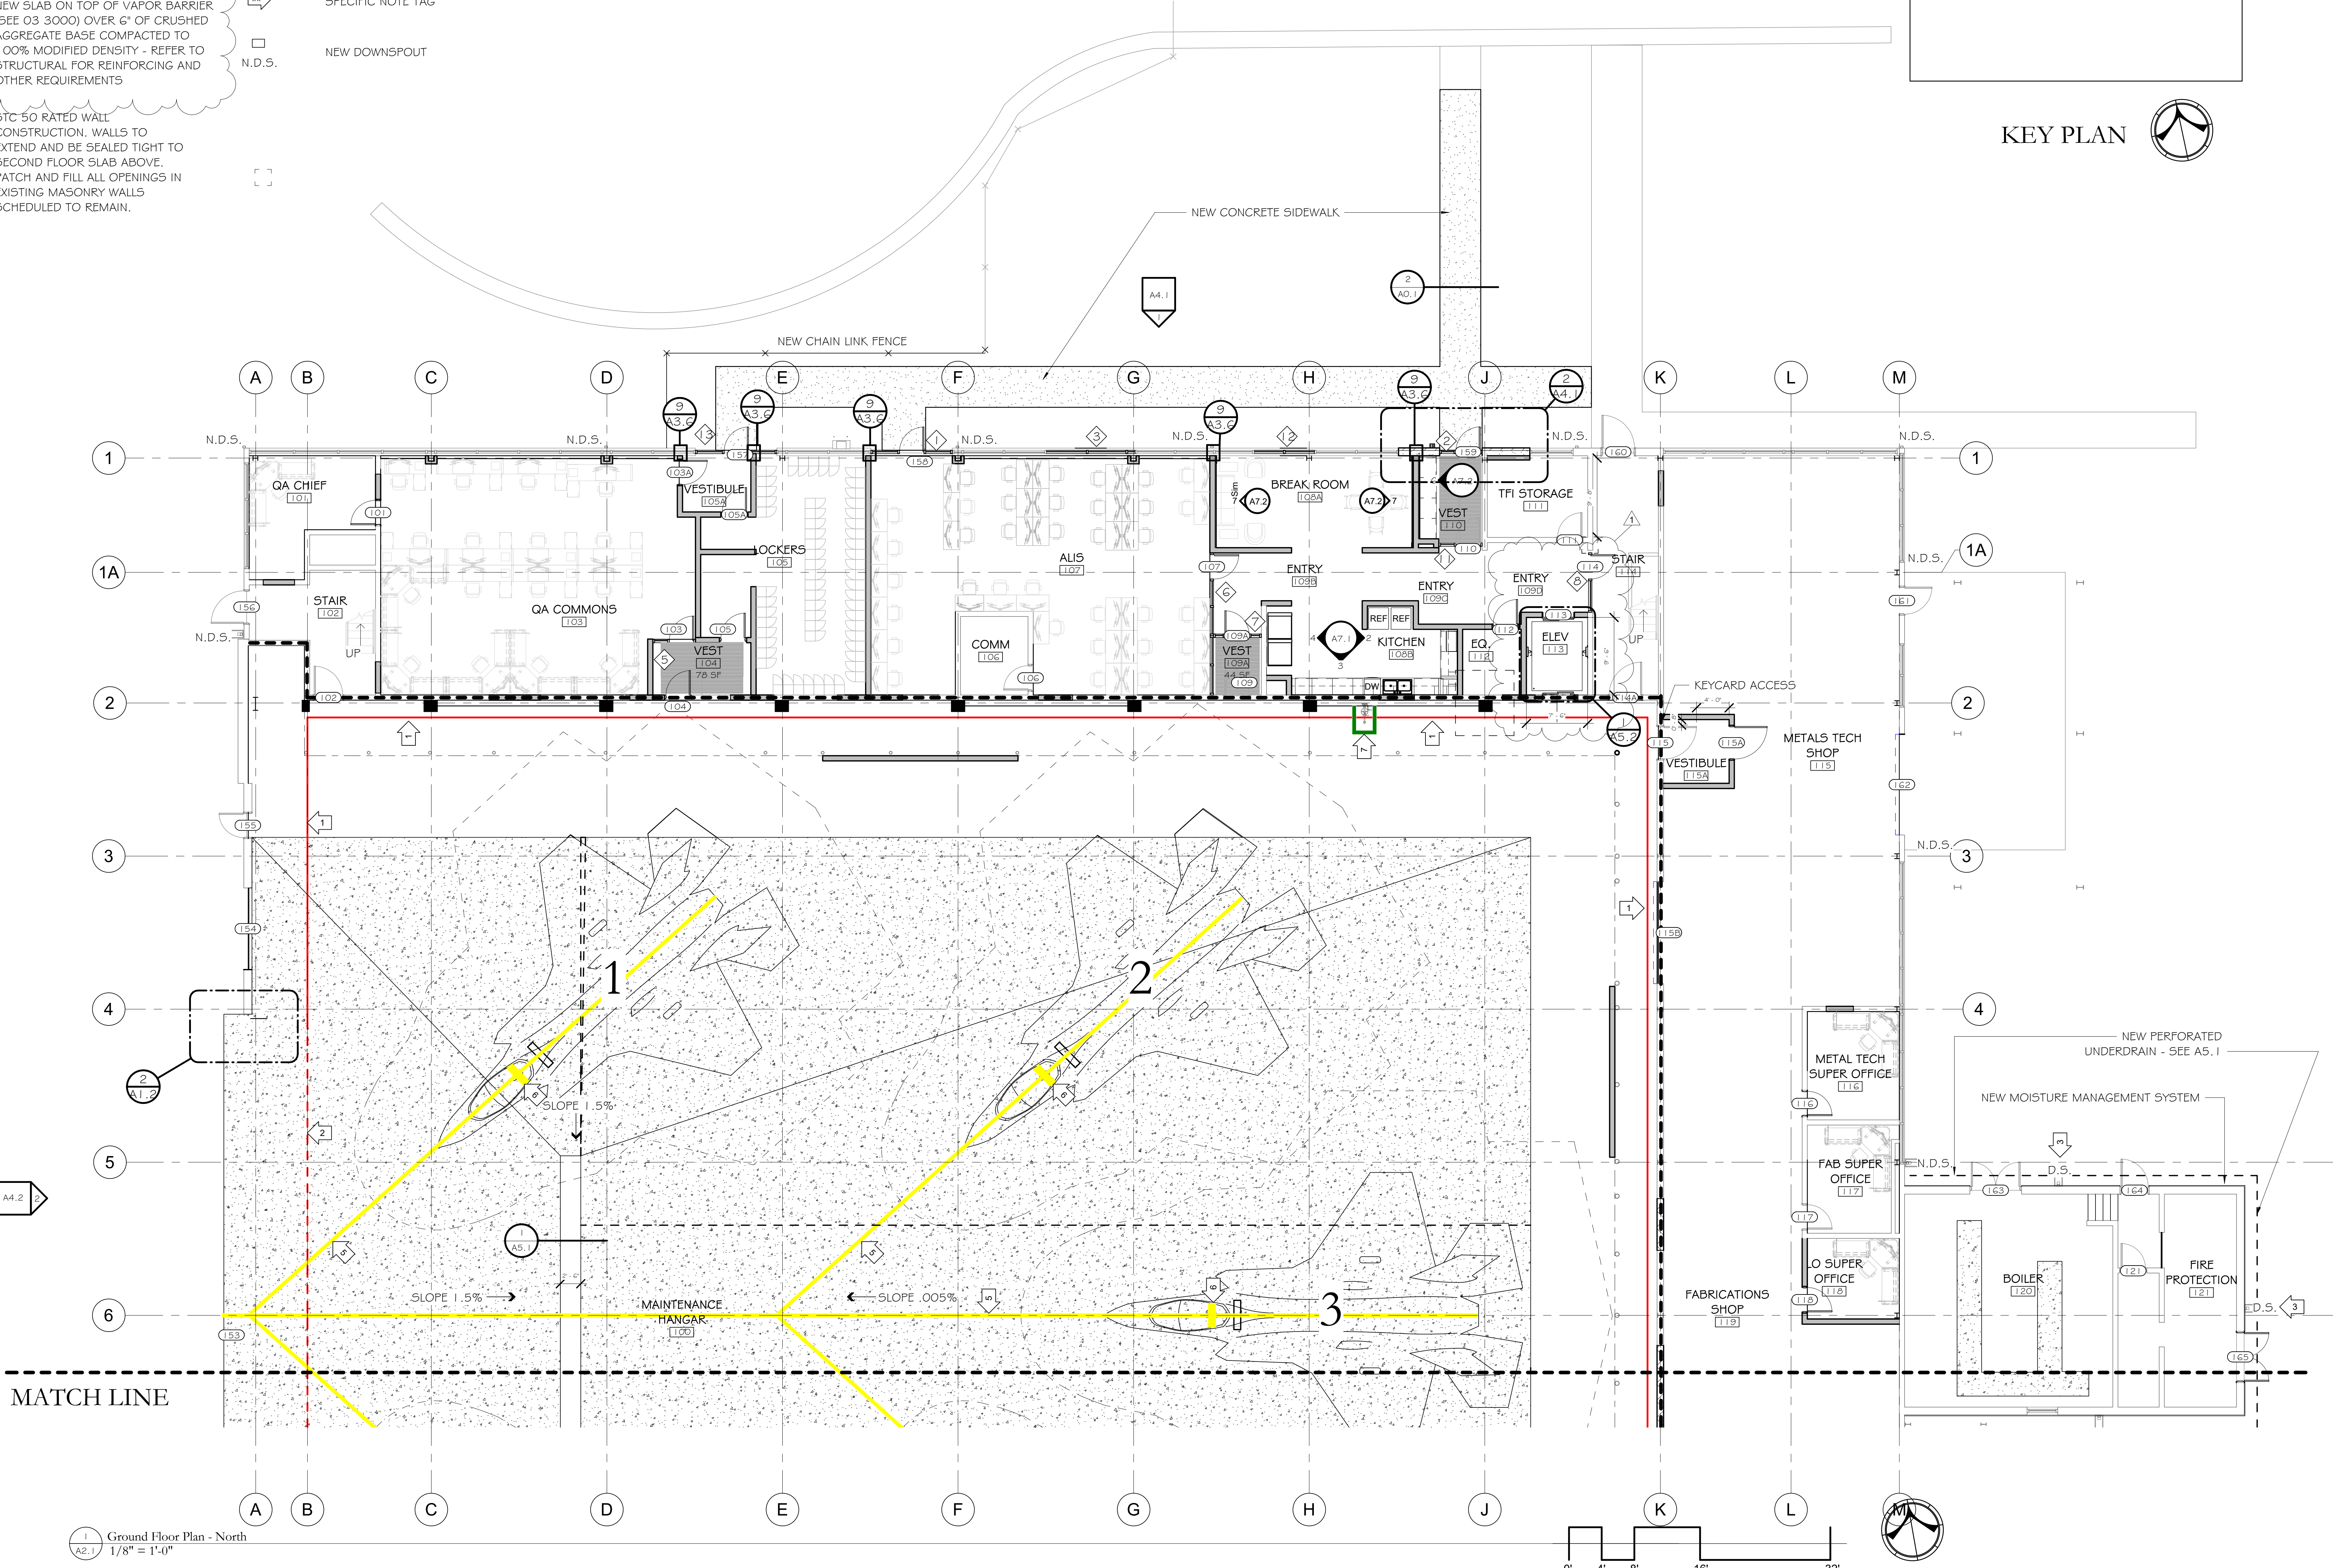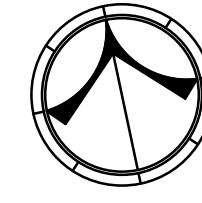

1 Ground Floor Plan - North
A2.1 1/8" = 1'-0"

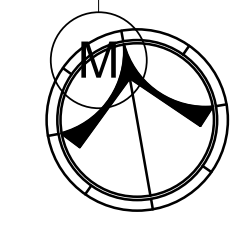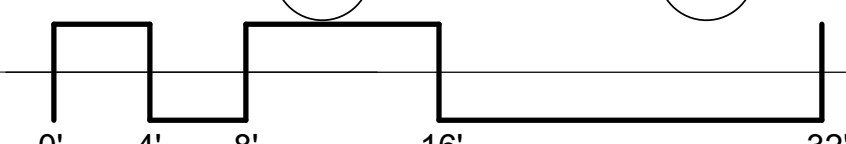


BLDG 1201
187TH FW, DANNELLY
FIELD, MONTGOMERY, AL

Sheet Title
FIRST FLOOR PLAN
NORTH

Sheet Number

A2.1

LEGEND:

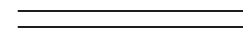


EXISTING WALL ASSEMBLY TO REMAIN



DOOR - SEE DOOR SCHEDULE



NEW CMU WALLS
(SEE WALL TYPE PLAN)

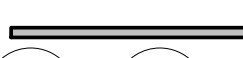


NEW METAL FRAMING WALLS
(SEE WALL TYPE PLAN)



NEW CONCRETE FLOOR SLAB. INSTALL NEW SLAB ON TOP OF VAPOR BARRIER (SEE 03 3000) OVER 6" OF CRUSHED AGGREGATE BASE COMPACTED TO 100% MODIFIED DENSITY - REFER TO STRUCTURAL FOR REINFORCING AND OTHER REQUIREMENTS




STC 50 RATED WALL CONSTRUCTION. WALLS TO EXTEND AND BE SEALED TIGHT TO SECOND FLOOR SLAB ABOVE. PATCH AND FILL ALL OPENINGS IN EXISTING MASONRY WALLS SCHEDULED TO REMAIN.

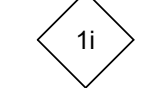


WINDOW / STOREFRONT



DOOR TAG - SEE DOOR SCHEDULE

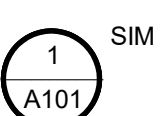

DETAIL SECTION

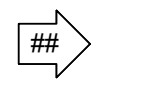

SPECIFIC NOTE TAG



N.D.S. NEW DOWNSPOUT

SPECIFIC NOTES:

- 1

SOLID 6" WIDE PAINTED RED LINE. COORDINATE EXACT LOCATION WITH CONTRACTING OFFICER REPRESENTATIVE ON SITE.
- 2

DASHED 6" WIDE PAINTED RED LINE. COORDINATE EXACT LOCATION WITH CONTRACTING OFFICER REPRESENTATIVE ON SITE.
- 3

NEW DOWNSPOUT. MATCH EXISTING SIZE PROFILE AND CONNECT TO EXISTING GUTTER.
- 4

PATCH AND PAINT CMU IN THIS LOCATION. PROVIDE NEW 4" CMU TO INFILL VOID AT ELECTRICAL PANEL SCHEDULED TO BE REMOVED.
- 5

6" WIDE SOLID YELLOW PAINTED LINE - COORDINATE EXACT LOCATION/EXTENTS WITH CONTRACTING OFFICER REPRESENTATIVE ON SITE
- 6

PAINTED YELLOW STOP BAR. 36" X 12". COORDINATE EXACT LOCATION WITH CONTRACTING OFFICER REPRESENTATIVE ON SITE.
- 7

PAINTED GREEN BOX . 6" WIDE LINE, 24" X 24" SQUARE CENTERED ON EMERGENCY FIXTURE

