




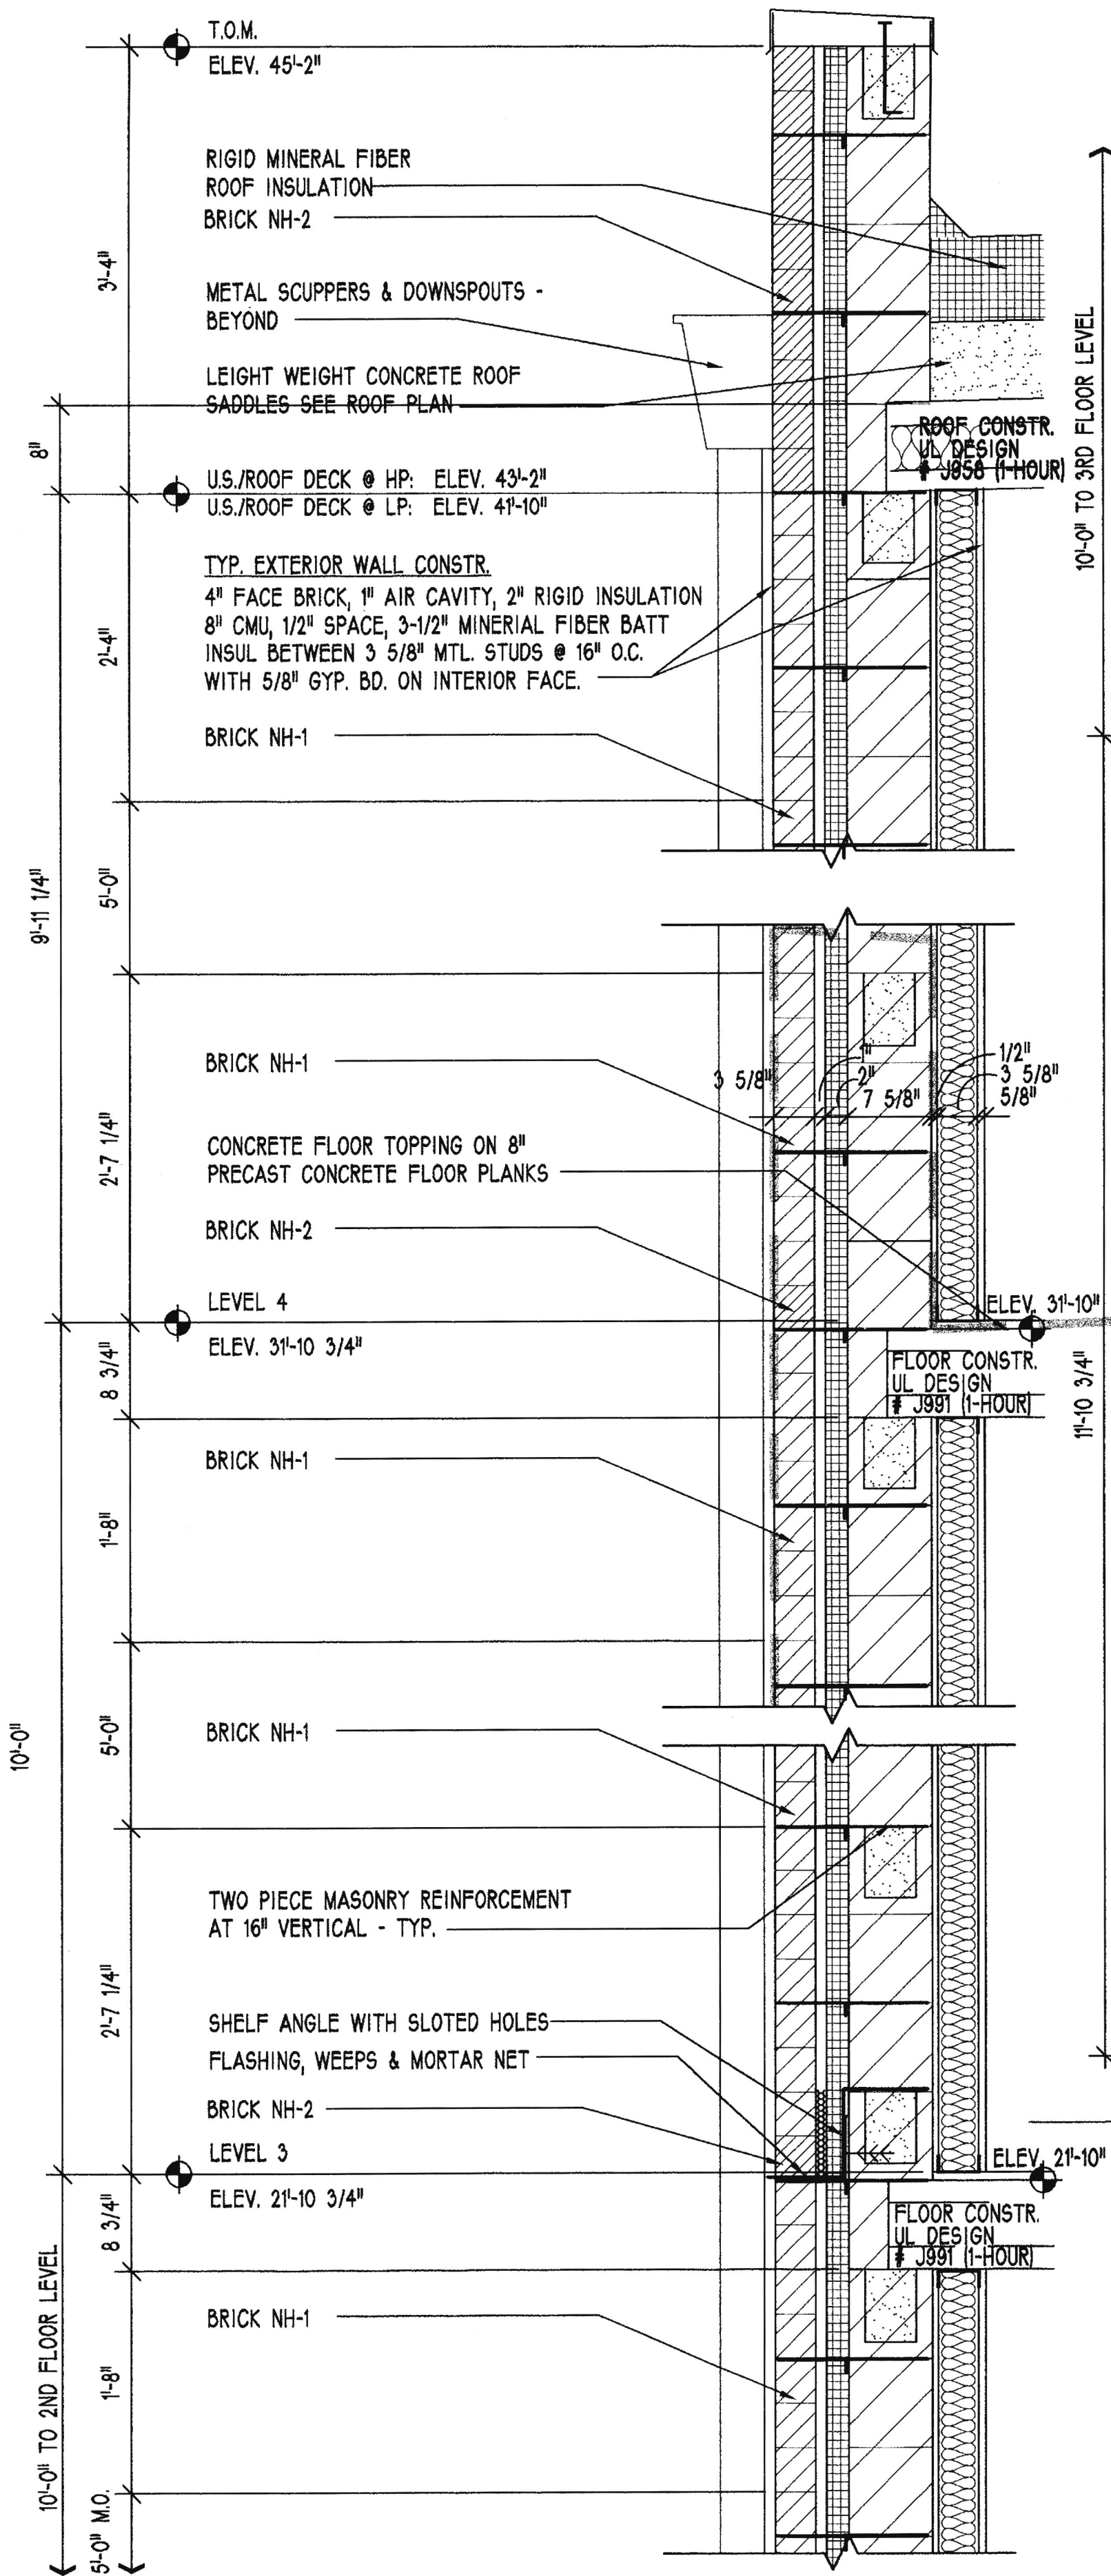


4
A6.1
TYPICAL WALL SECTION
1" = 1'

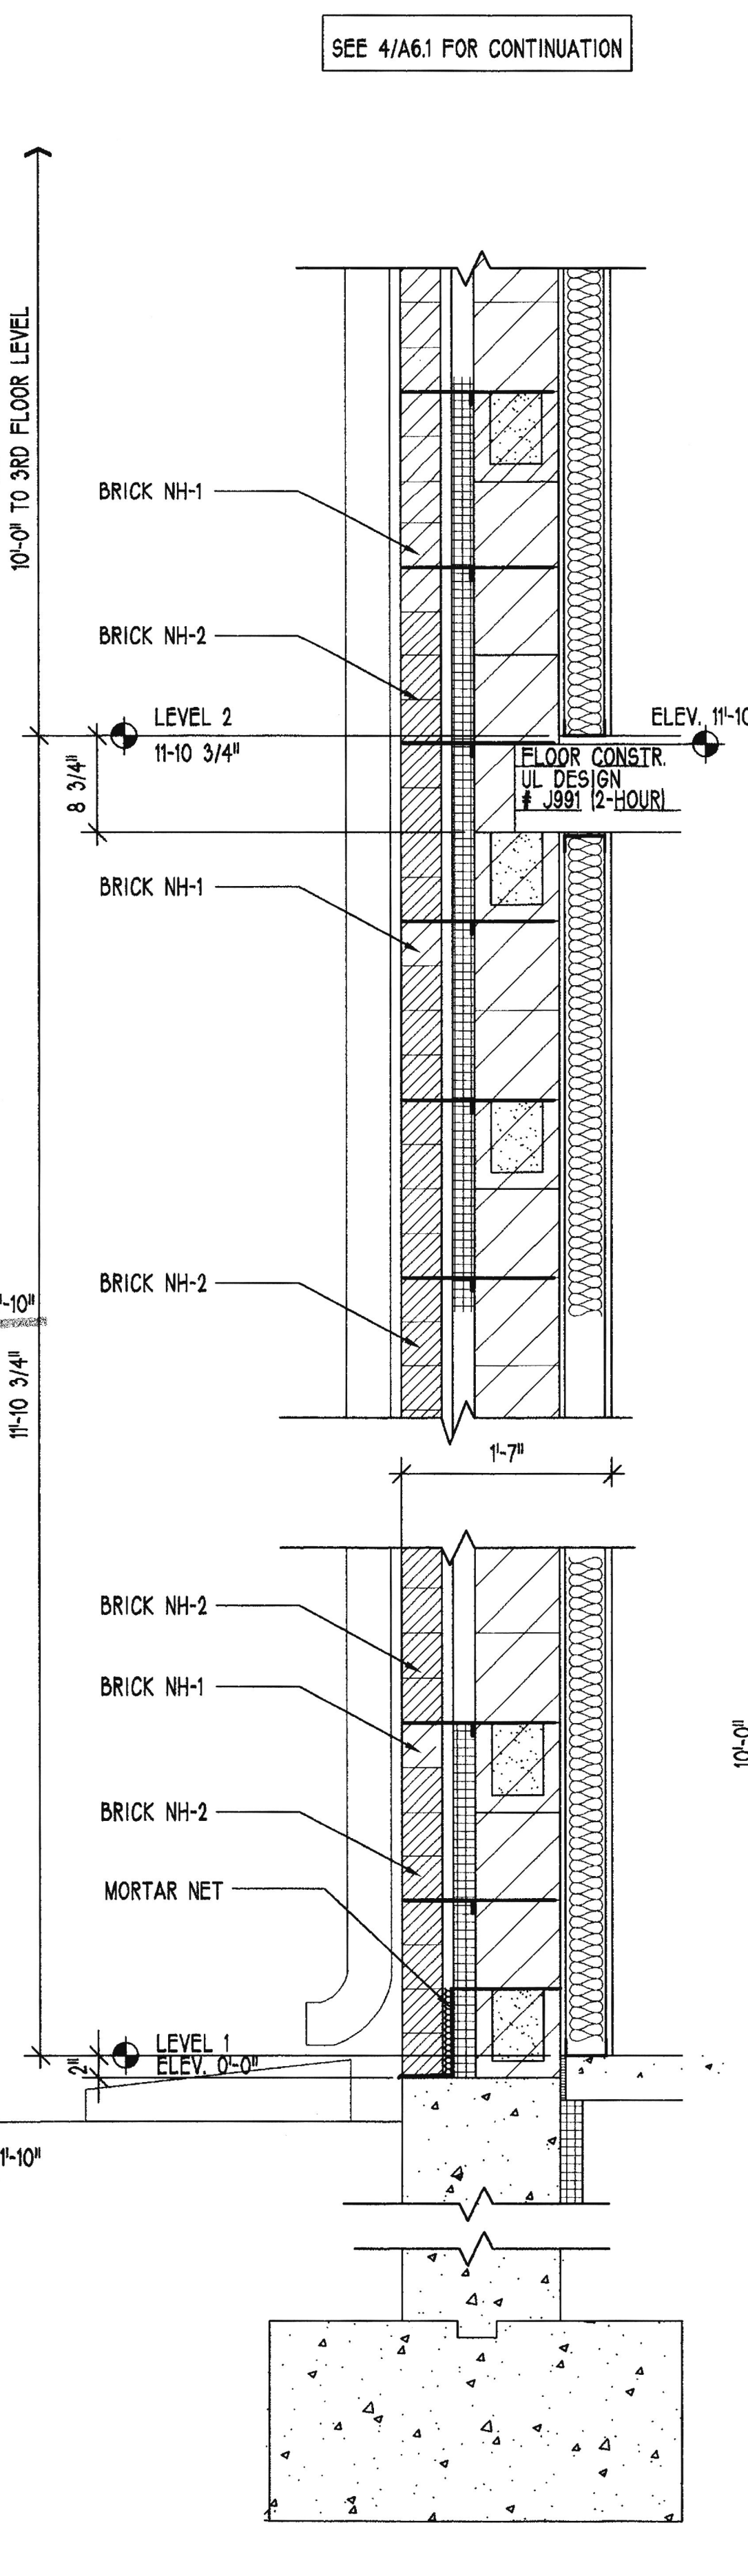

3
A6.1
TYPICAL WALL SECTION
1" = 1'

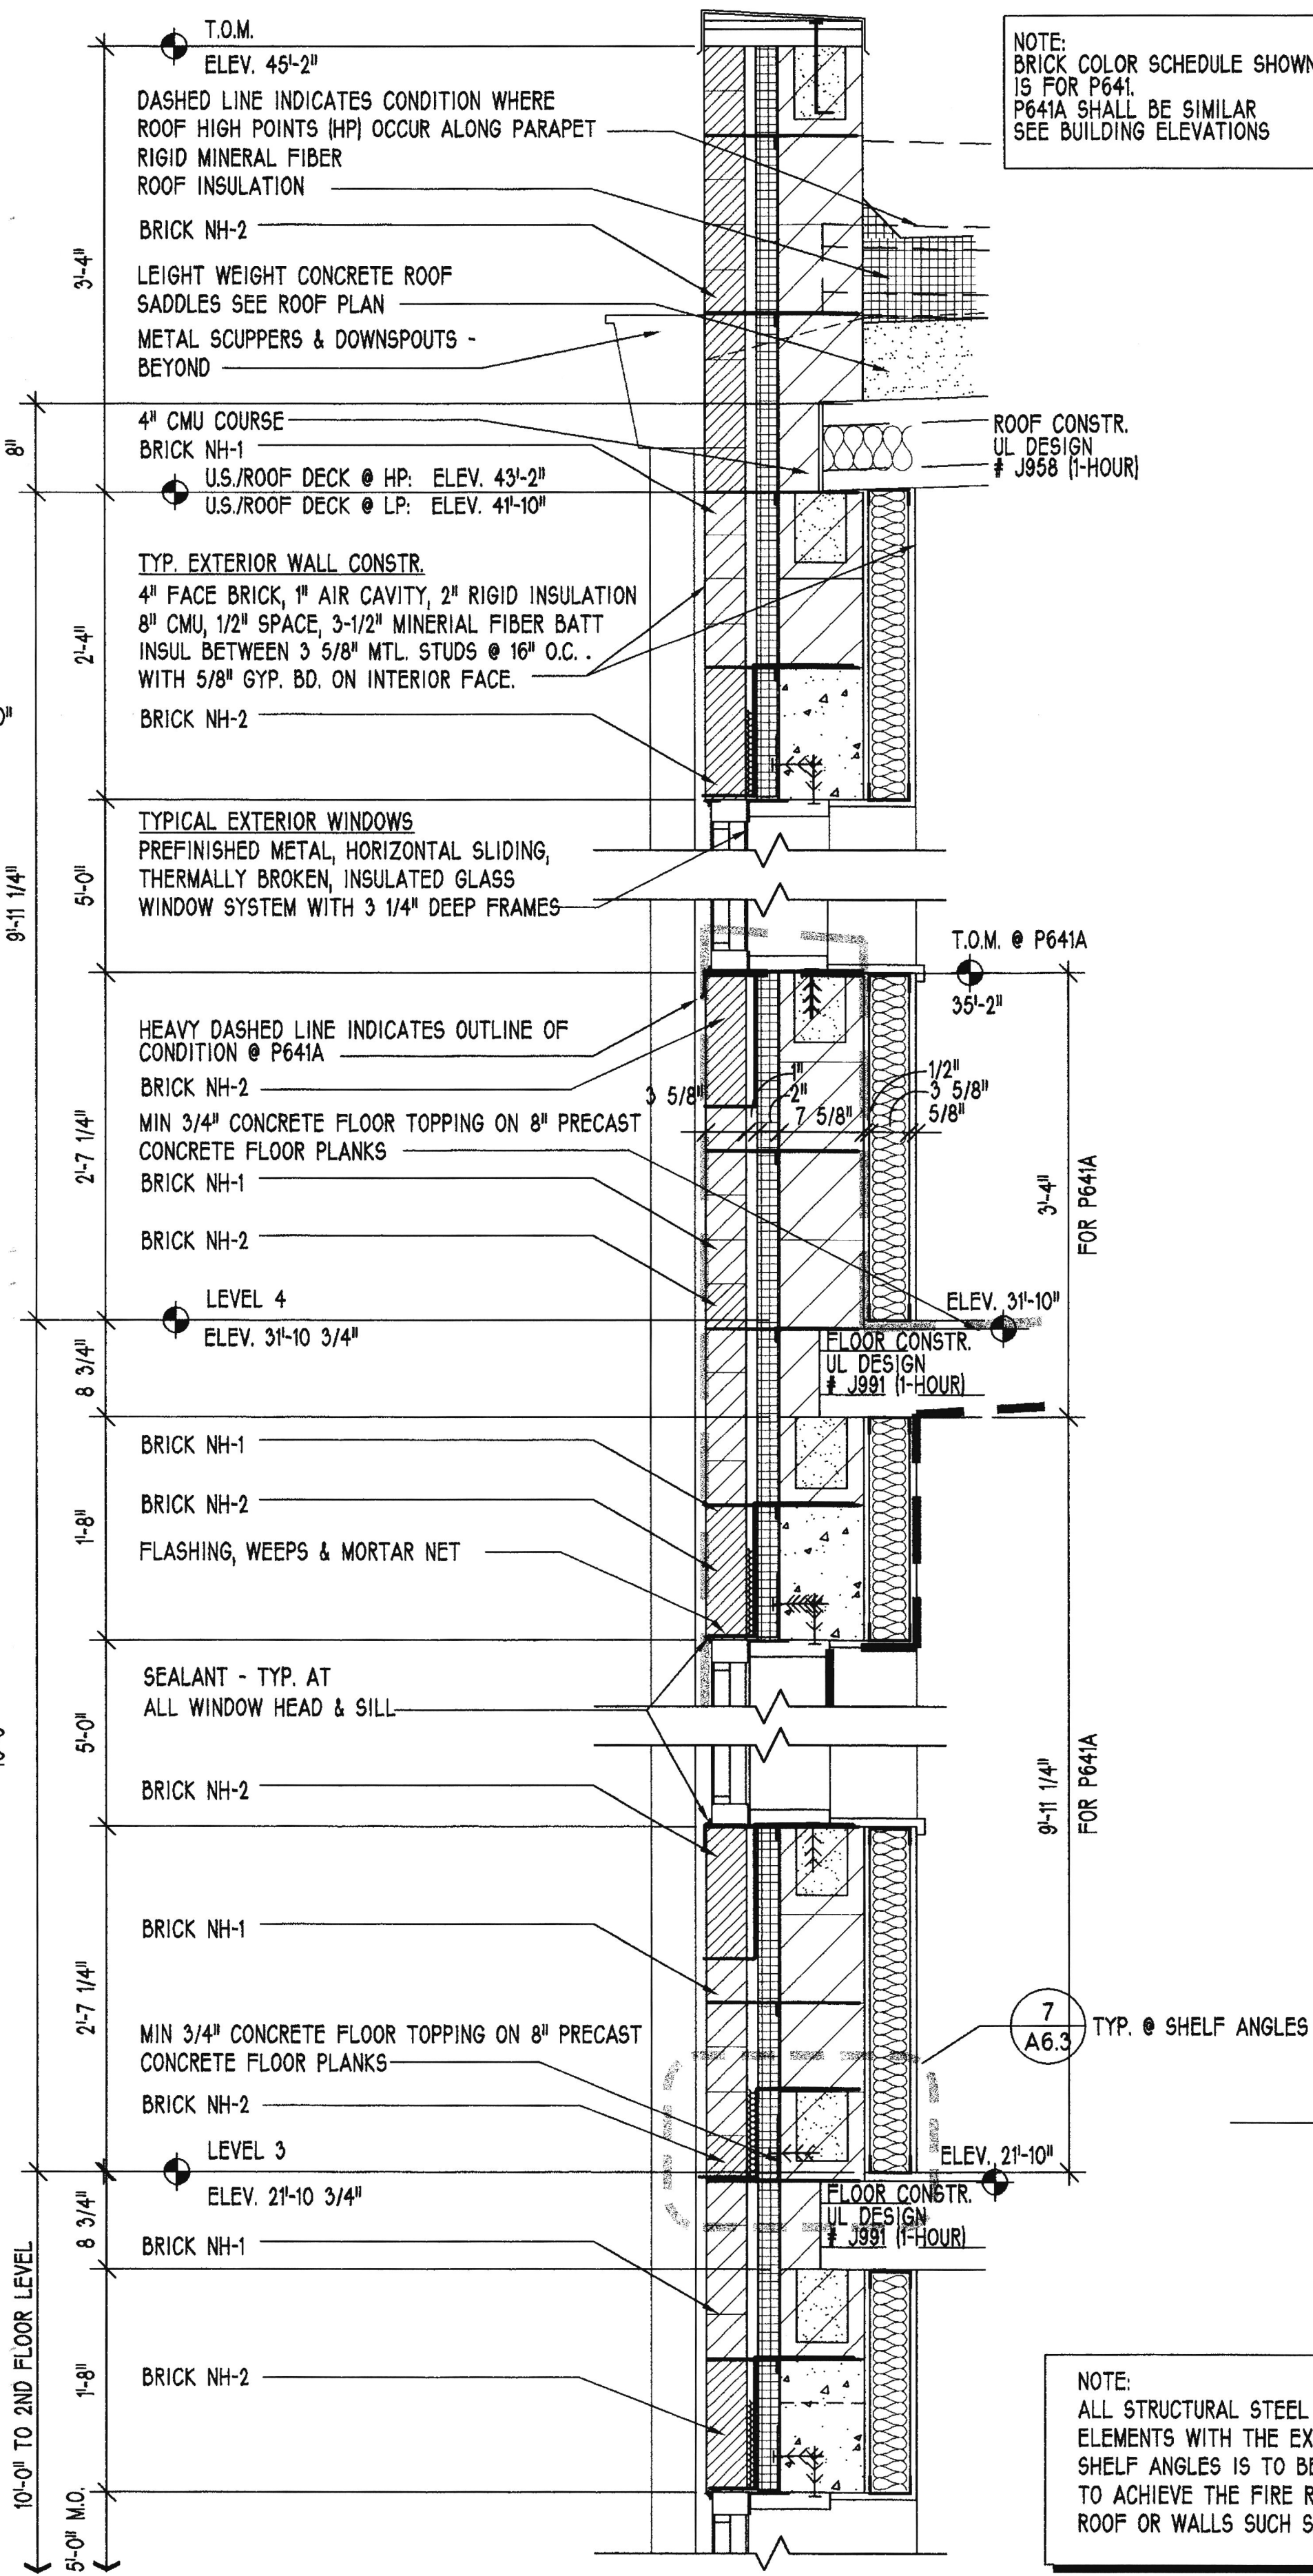

2
A6.1
P641 & P641A WALL SECTION - CONT.
1" = 1'

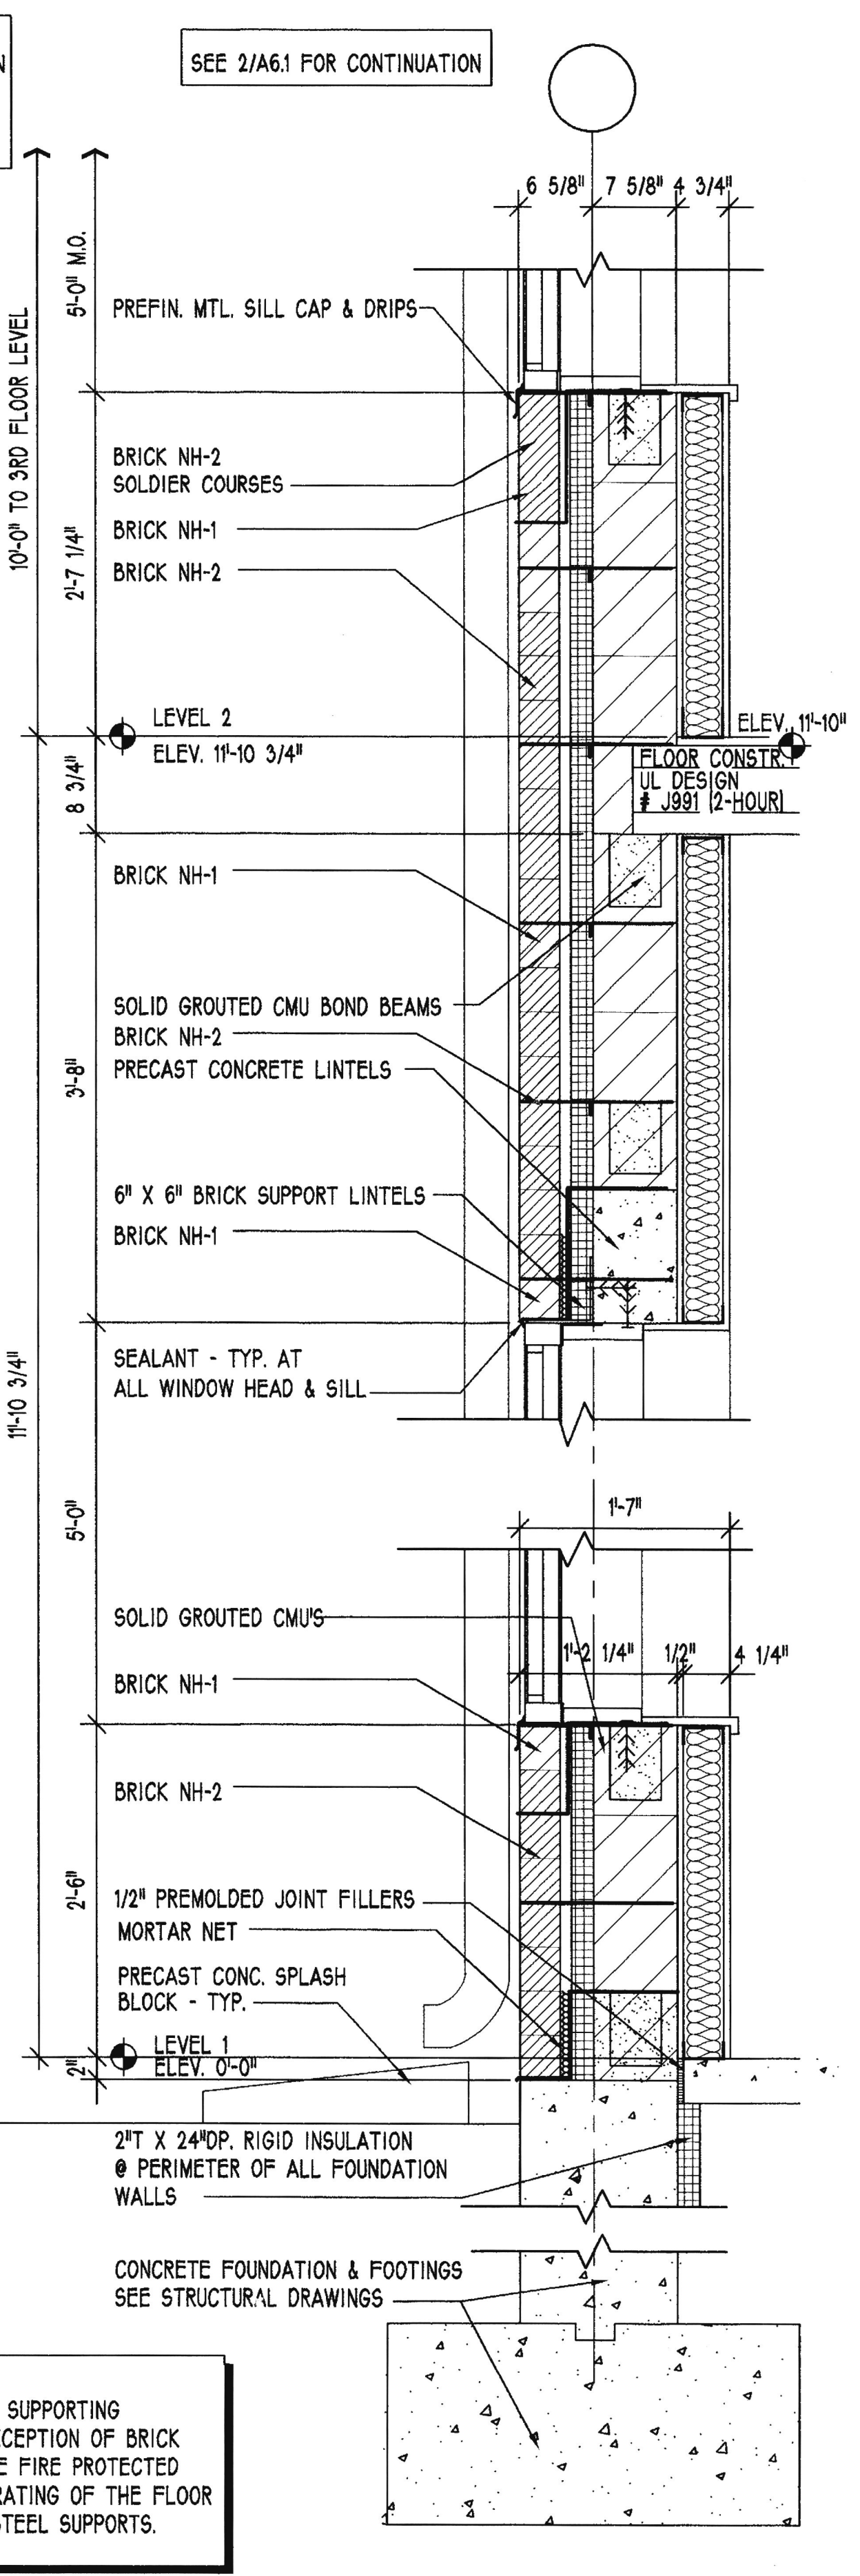

1
A6.1
P641 & P641A WALL SECTION
1" = 1'

DESIGNED BY:	DRAWN BY:	CHECKED BY:	BRANCH HEAD:	F.P.E.:	PROJ. ENG.:	DIV. DIR.:

REV.	DESCRIPTION	DATE	APPROVED	ISSUED FOR CONSTRUCTION		
		23 JULY 98				

NAVAL FACILITIES ENGINEERING COMMAND
GREAT LAKES, IL

NAVAL HOSPITAL
BACHELOR ENLISTED QUARTERS
P641 & P641A EXTERIOR WALL SECTIONS

ETD FOR COMMANDER, NAVFAC

RECORD DRAWING DATE:

CODE I.D. NO. 80091

DRAWING SIZE: D

SPEC. NO. 06-

CONSTR. CONTR. NO. N62467-96-C-0757

NAVFAC DRAWING NO.

SHEET OF

A6.1