

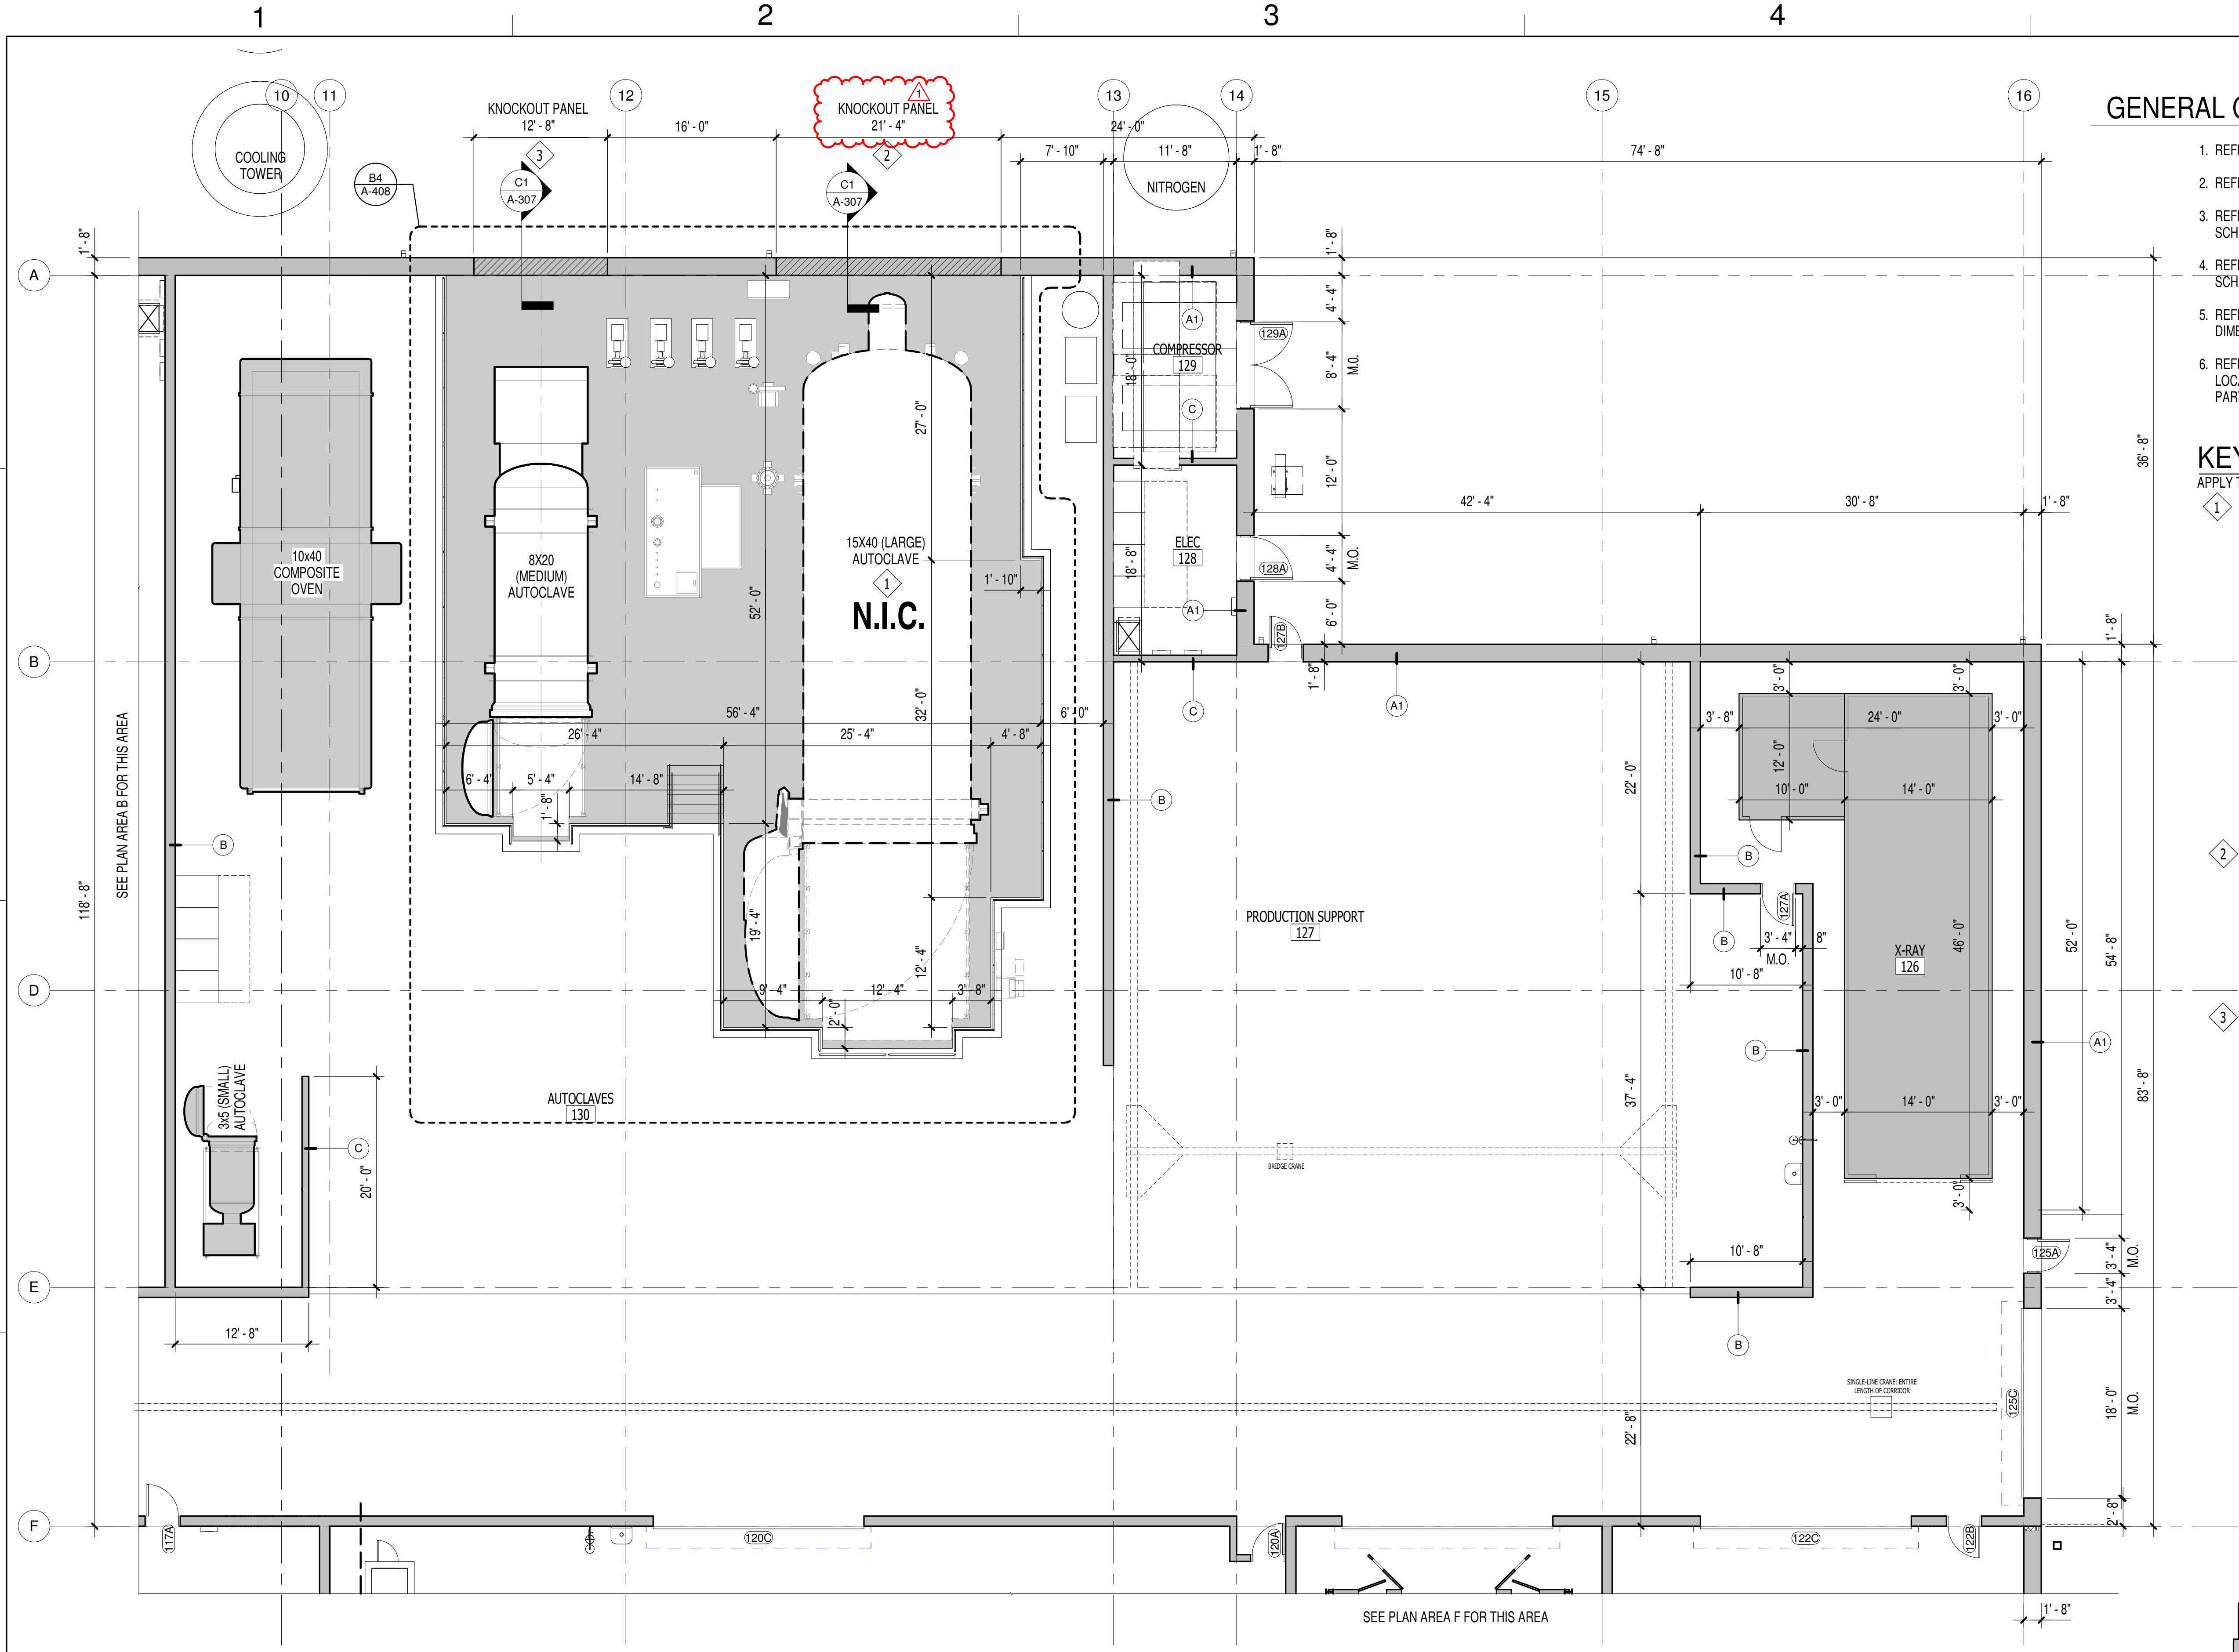
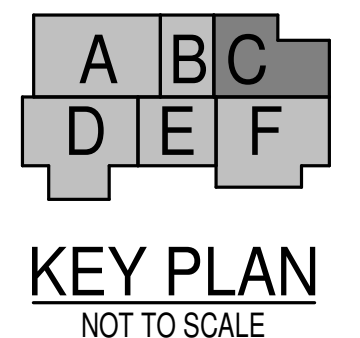


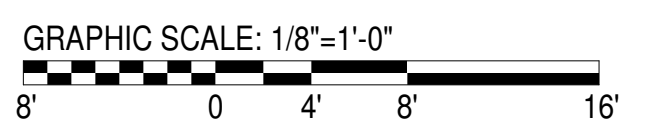

A1 FLOOR PLAN - AREA C
SCALE: 1/8" = 1'-0"

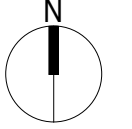

GENERAL CONSTRUCTION NOTES

- REFERENCE SHEET A-001 FOR SYMBOL LEGEND.
- REFERENCE SHEET(S) A-501 & A-502 FOR WALL TYPES.
- REFERENCE SHEET A-601 FOR DOOR AND FRAME SCHEDULE.
- REFERENCE INTERIOR DRAWING SET FOR FINISH SCHEDULE.
- REFERENCE INTERIOR DRAWING SET FOR CASEWORK DIMENSIONS AND DETAILS.
- REFERENCE THE LIFE SAFETY DRAWINGS FOR LOCATIONS OF RATED WALLS AND SMOKE PARTITIONS.

KEYED NOTES

APPLY TO THIS SHEET ONLY

- NOTE: LARGE AUTOCLAVE AS SHOWN IN PLAN IS NOT IN CONTRACT. BUILT PREPARATIONS TO ACCOMMODATE IT'S EVENTUAL PURCHASE AND INSTALLATION/DELIVERY (AT AN UNDETERMINED DATE, OUTSIDE OF THIS CONTRACT) IN THE BASE BID INCLUDE THE AUTOCLAVE PIT AS SHOWN AND KNOCKOUT EXTERIOR WALL PANEL RELATIVE TO IT'S EVENTUAL LOCATION.

SEE ELECTRICAL, PLUMBING AND MECHANICAL DRAWING SETS FOR INFORMATION RELATED TO BASIC ENGINEERING INFRASTRUCTURE INCLUDED IN THIS CONTRACT.

NOTE THAT THE ADJACENT MEDIUM AUTOCLAVE IS IN THE CONTRACT AND INCLUDES DESCRIBED INFRASTRUCTURE TO SUPPORT IT'S OPERATION, ALSO AS DESCRIBED IN THE SPECIFICATON.
- KNOCKOUT WALL PANEL "A" (LARGE AUTOCLAVE); SEE SHEET A-307 FOR FURTHER DETAIL AND DESCRIPTION INCLUDING STRUCTURAL DRAWINGS FOR LINTEL DESCRIPTION AT OPENING. NOTE THAT THE LARGE AUTOCLAVE IS NOT IN CONTRACT- THEREFORE SCOPE OF WORK IS TO BUILD THE KNOCKOUT PANEL AS DESCRIBED ON SHEET A-307 AS 'FINISHED WALL CONDITION'.
- KNOCKOUT WALL PANEL "B" (MEDIUM AUTOCLAVE); SEE SHEET A-307 FOR FURTHER DETAIL AND DESCRIPTION INCLUDING STRUCTURAL DRAWINGS FOR LINTEL DESCRIPTION AT OPENING. NOTE THAT THE MEDIUM AUTOCLAVE IS IN CONTRACT- THEREFORE SCOPE OF WORK IS TO BUILD THE KNOCKOUT PANEL AS DESCRIBED ON SHEET A-307 AS 'TEMPORARY INFILL WALL CONDITION' PRIOR TO AUTOCLAVE DELIVERY; UPON DELIVERY, DEMOLISH INFILL TO ACCOMMODATE DELIVERY/INSTALLATION; SUBSEQUENT TO DELIVERY/INSTALLATION, REBUILD PANEL AS DESCRIBED ON SHEET A-307 AS 'FINISHED WALL CONDITION'.

DATE		2026.04.07
DESCRIPTION		1 Amendment
SYM		1


307-C Pullock Street | New Bern, NC 28560
252-637-6373 | mbfarchitects.com
AE RFD

APPROVED	
FOR COMMANDER NAVFAC	
ACTIVITY	
Approved by Erik A. Lewis, Infrastructure Engineering Branch Head, FRCE Cherry Point via Electronic Signature	
SATISFACTORY TO 12/24/2025	
DES	DLG
DRW	DLG
CHK	DJE
PM/D	KTB/SOM
BRANCH MANAGER	CGM
CHIEF ENGINEER	JWJ
FIRE PROTECTION	HPN

DEPARTMENT OF THE NAVY
NAVAL FACILITIES ENGINEERING SYSTEMS COMMAND
DESIGN AND CONSTRUCTION (DDC) CORE
NAVAL STATION - NORFOLK, VA
MARINE CORPS AIR STATION
CHERRY POINT, NC
P-995 COMPOSITE REPAIR FACILITY
FLOOR PLAN - AREA C

SCALE:	AS INDICATED
PROJECT NO.:	1692230
STA. PROJ. NO.:	
NAVFAC DRAWING NO.:	12938262
SHEET	114 OF 456
A-104	

DRAWFORM REVISION: 25 AUGUST 2020

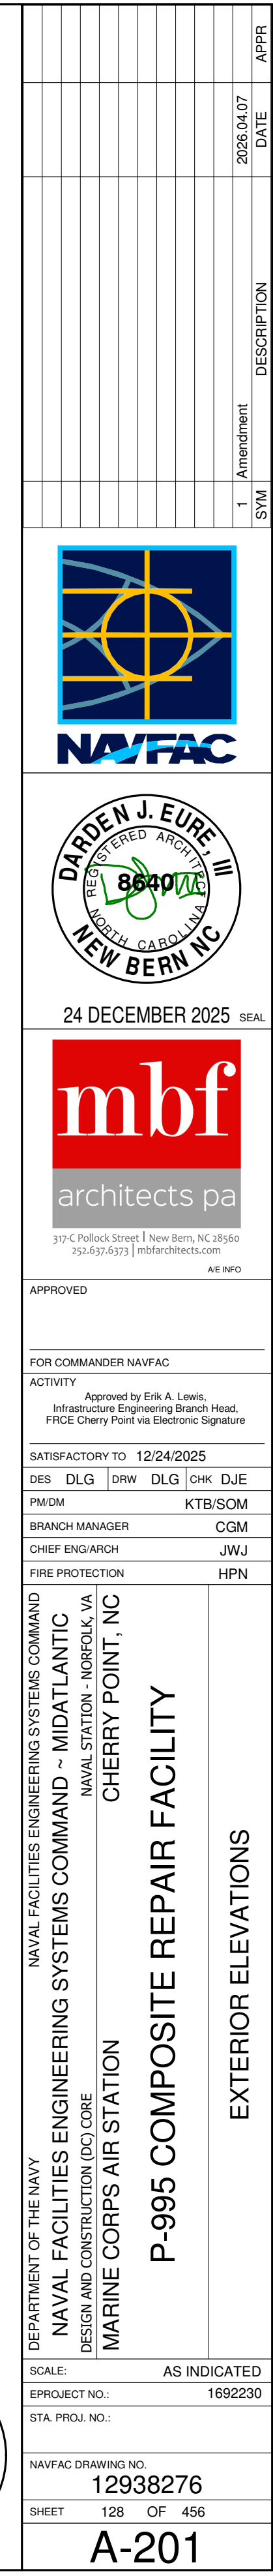


TOILET ACCESSORIES LEGEND

MARK	DESCRIPTION	MARK	DESCRIPTION	MARK	DESCRIPTION
(TTD)	TOILET TISSUE DISPENSER	(PTD)	PAPER TOWEL DISPENSER	(RSS)	RECESSED SOLID SURFACE SHOWER SHELF
(GB42)	GRAB BAR: 42"	(ITDW)	INTEGRAL TOWEL DISPENSER & WASTE RECEPTACLE	(SS)	SOLID SURFACE SHOWER SHELF
(GB36)	GRAB BAR: 36"	(CTD)	PAPER TOWEL DISPENSER: "C" FOLD TYPE	(DCS)	DIAPER CHANGING STATION
(GB18)	GRAB BAR: 18"	(RTD)	PAPER TOWEL DISPENSER: ROLL TYPE	(MHS)	SHELF / MOP AND BROOM HOLDER
(GBL)	GRAB BAR: L-SHAPED 24" x 18"	(EHD)	ELECTRIC HAND DRYER	(MH)	MOP HOOK
(SND)	SANITARY NAPKIN DISPOSAL	(SD)	SOAP DISPENSER - WALL MOUNTED	(TB)	TOWEL BAR: 18"
(SNV)	SANITARY NAPKIN VENDOR	(SDC)	SOAP DISPENSER - COUNTERTOP MOUNTED	(SCR)	SHOWER CURTAIN ROD
(TCD)	TOILET SEAT COVER DISPENSER	(WM)	WALL MIRROR: 18" x 36"	(RH)	ROBE HOOK
(FSS)	FOLDING SHOWER SEAT	(WM1)	WALL MIRROR (CUSTOM): SEE ELEVATION	(RHA)	ROBE HOOK - ACCESSIBLE MOUNTING HEIGHT

NOTES:


- CLEARANCES AND HEIGHTS OF FIXTURES AND ACCESSORIES MUST BE IN COMPLIANCE WITH ANSI A117.1 AND THE NCSBC ACCESSIBILITY STANDARDS
- ACCESSORIES SPECIFIED APPEAR ON DESIGNATED PLANS, HOWEVER NOT ALL ACCESSORIES SHOWN HERE MAY BE SPECIFIED. COORDINATE WITH PLAN DESIGNATIONS
- REFERENCE THE SPECIFICATIONS FOR DETAILED PRODUCT INFORMATION INCLUDING ACCEPTABLE MANUFACTURERS, FINISHES, ETC.
- MOUNT ACCESSORIES SUCH THAT DISPENSER OR OPERATING MECHANISM IS WITHIN ACCESSIBLE FORWARD REACH RANGES DEFINED BY THE ACCESSIBILITY STANDARDS IDENTIFIED ABOVE

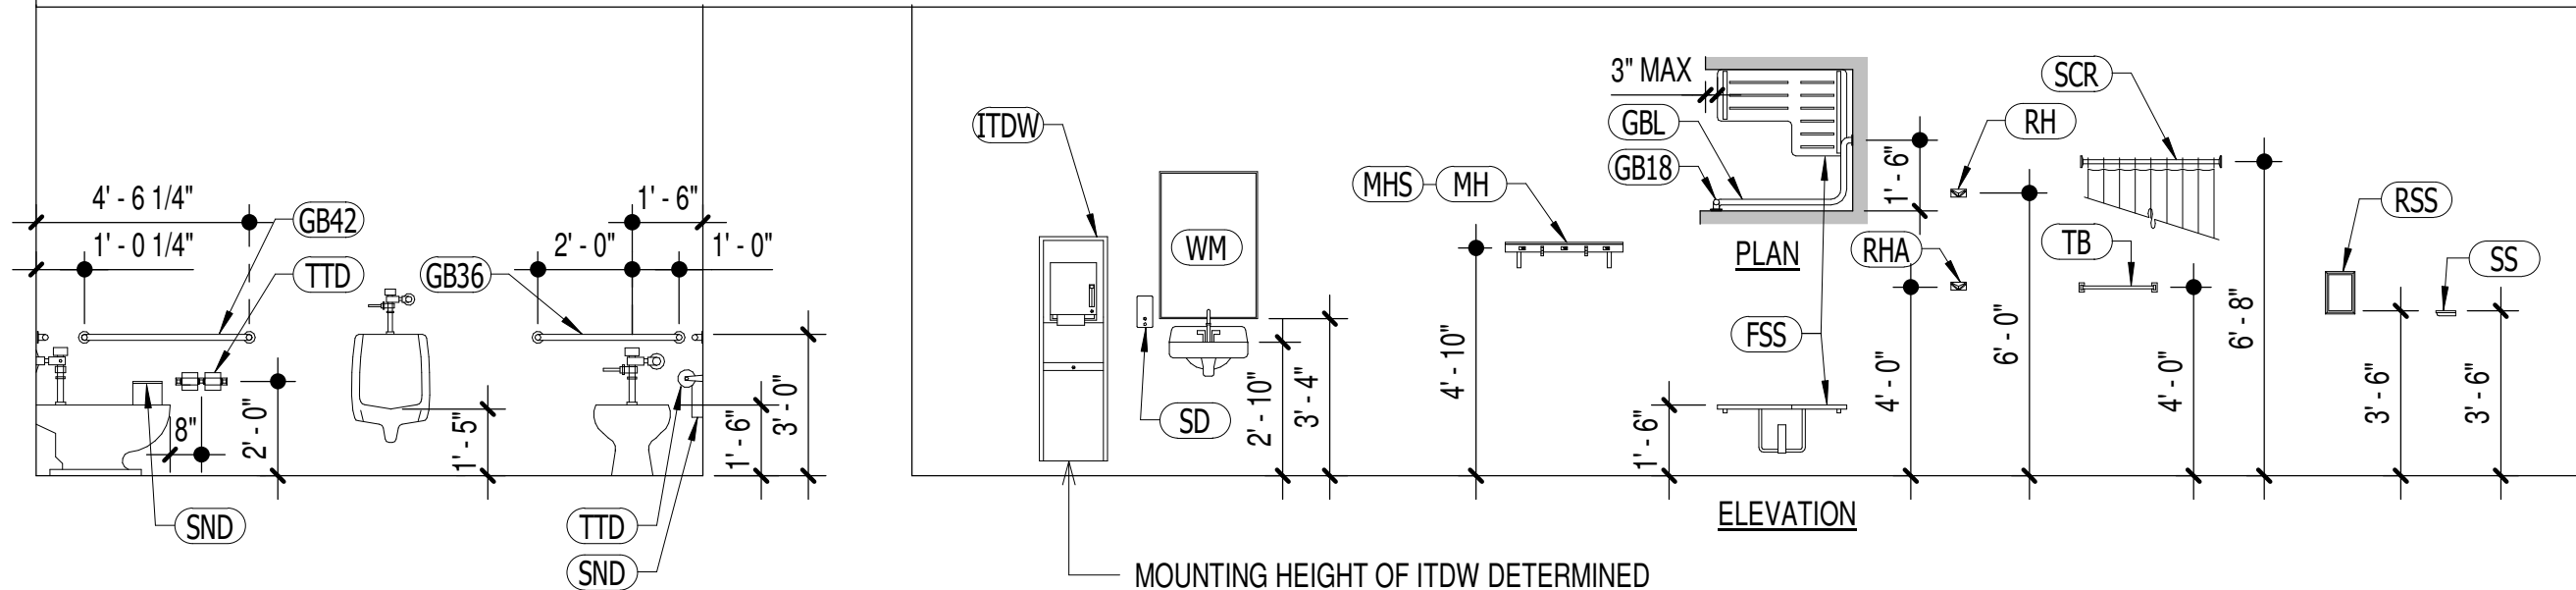

C1

TOILET ACCESSORY MOUNTING HEIGHTS

SCALE: 1/4" = 1'-0"

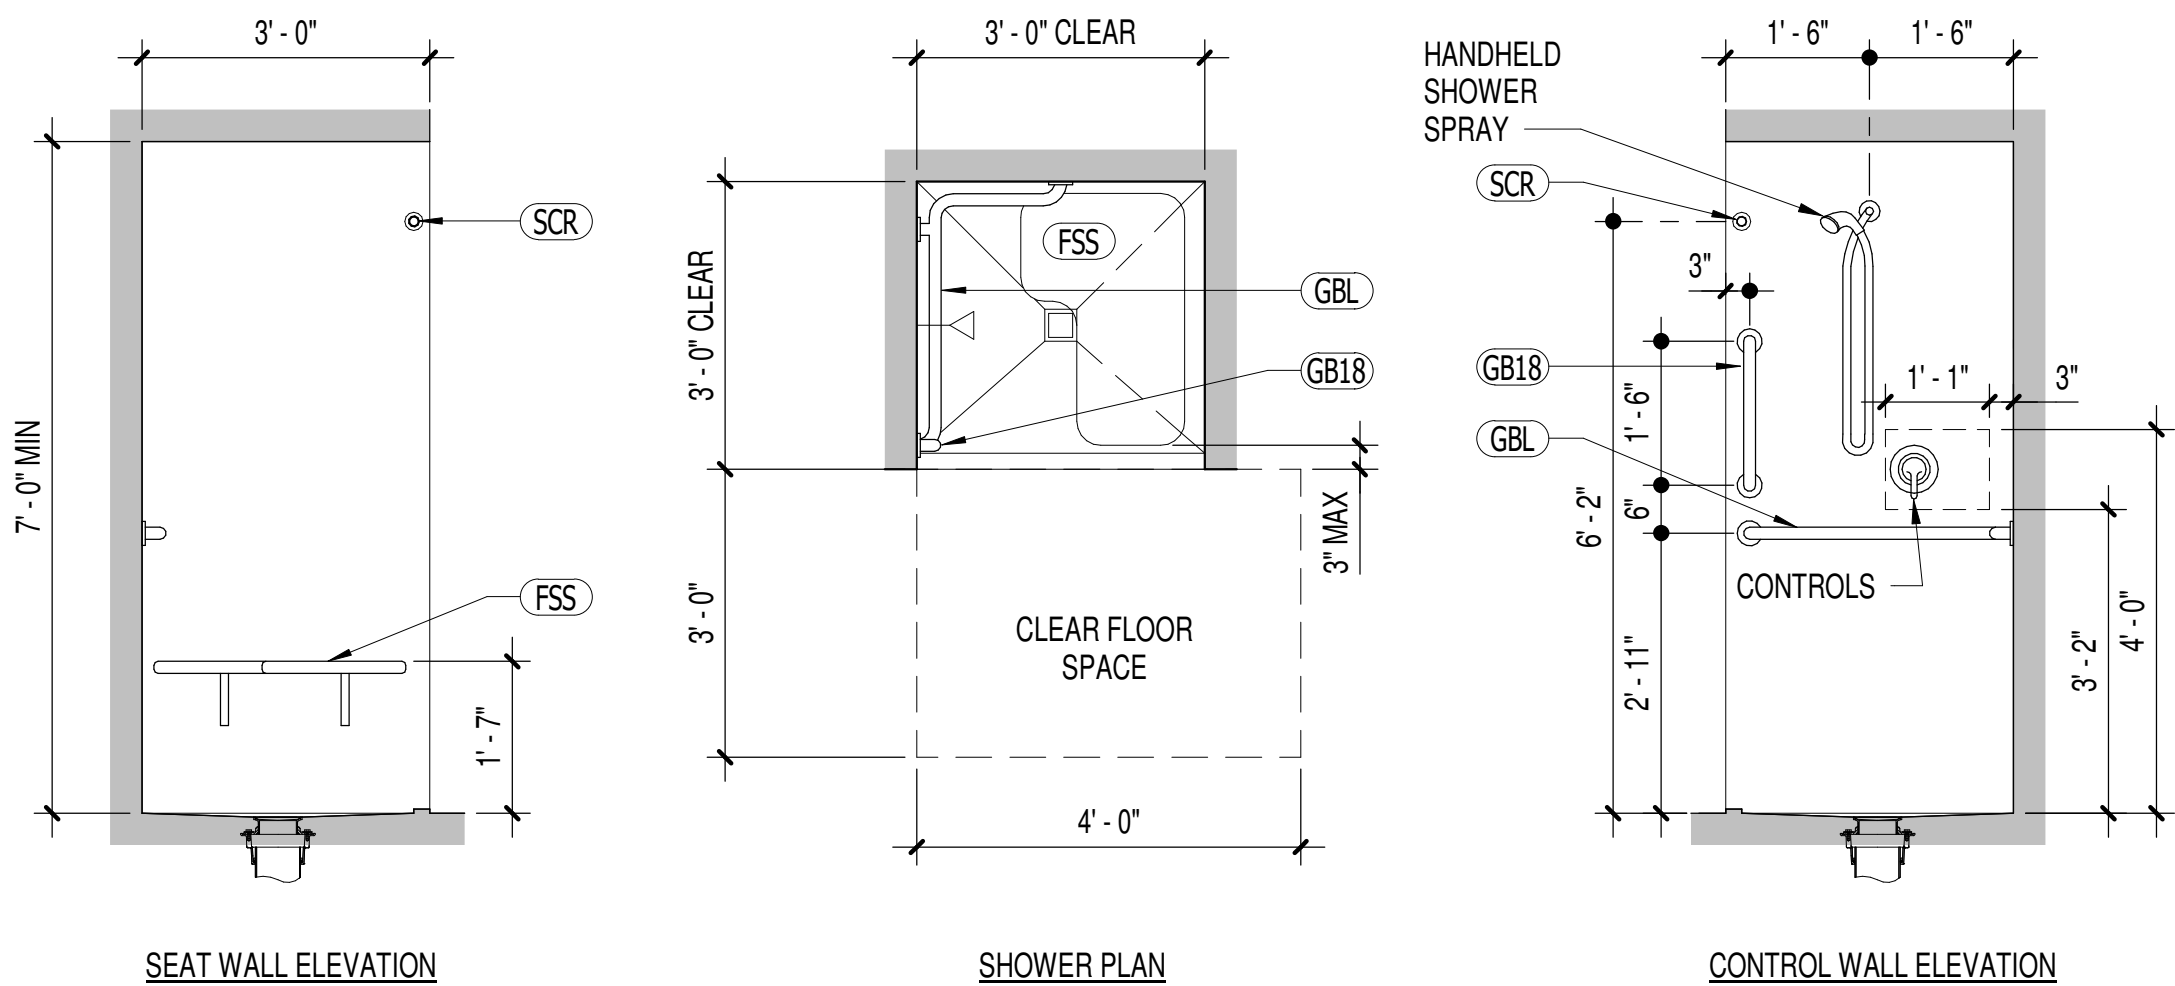


NOTES:

- SIZE AND CLEARANCES, SECTION 608.2.1, ABA
- GRAB BARS, SECTIONS 608.3 AND 608.3.1, ABA
- CONTROLS AND HAND SHOWER, SECTION 608.5, ABA
- THRESHOLD, SECTION 608.6, ABA
- SEAT, SECTIONS 610.1, 610.3.2 AND 610.4, ABA

A1

ACCESSIBLE SHOWER DETAILS

SCALE: 1/2" = 1'-0"

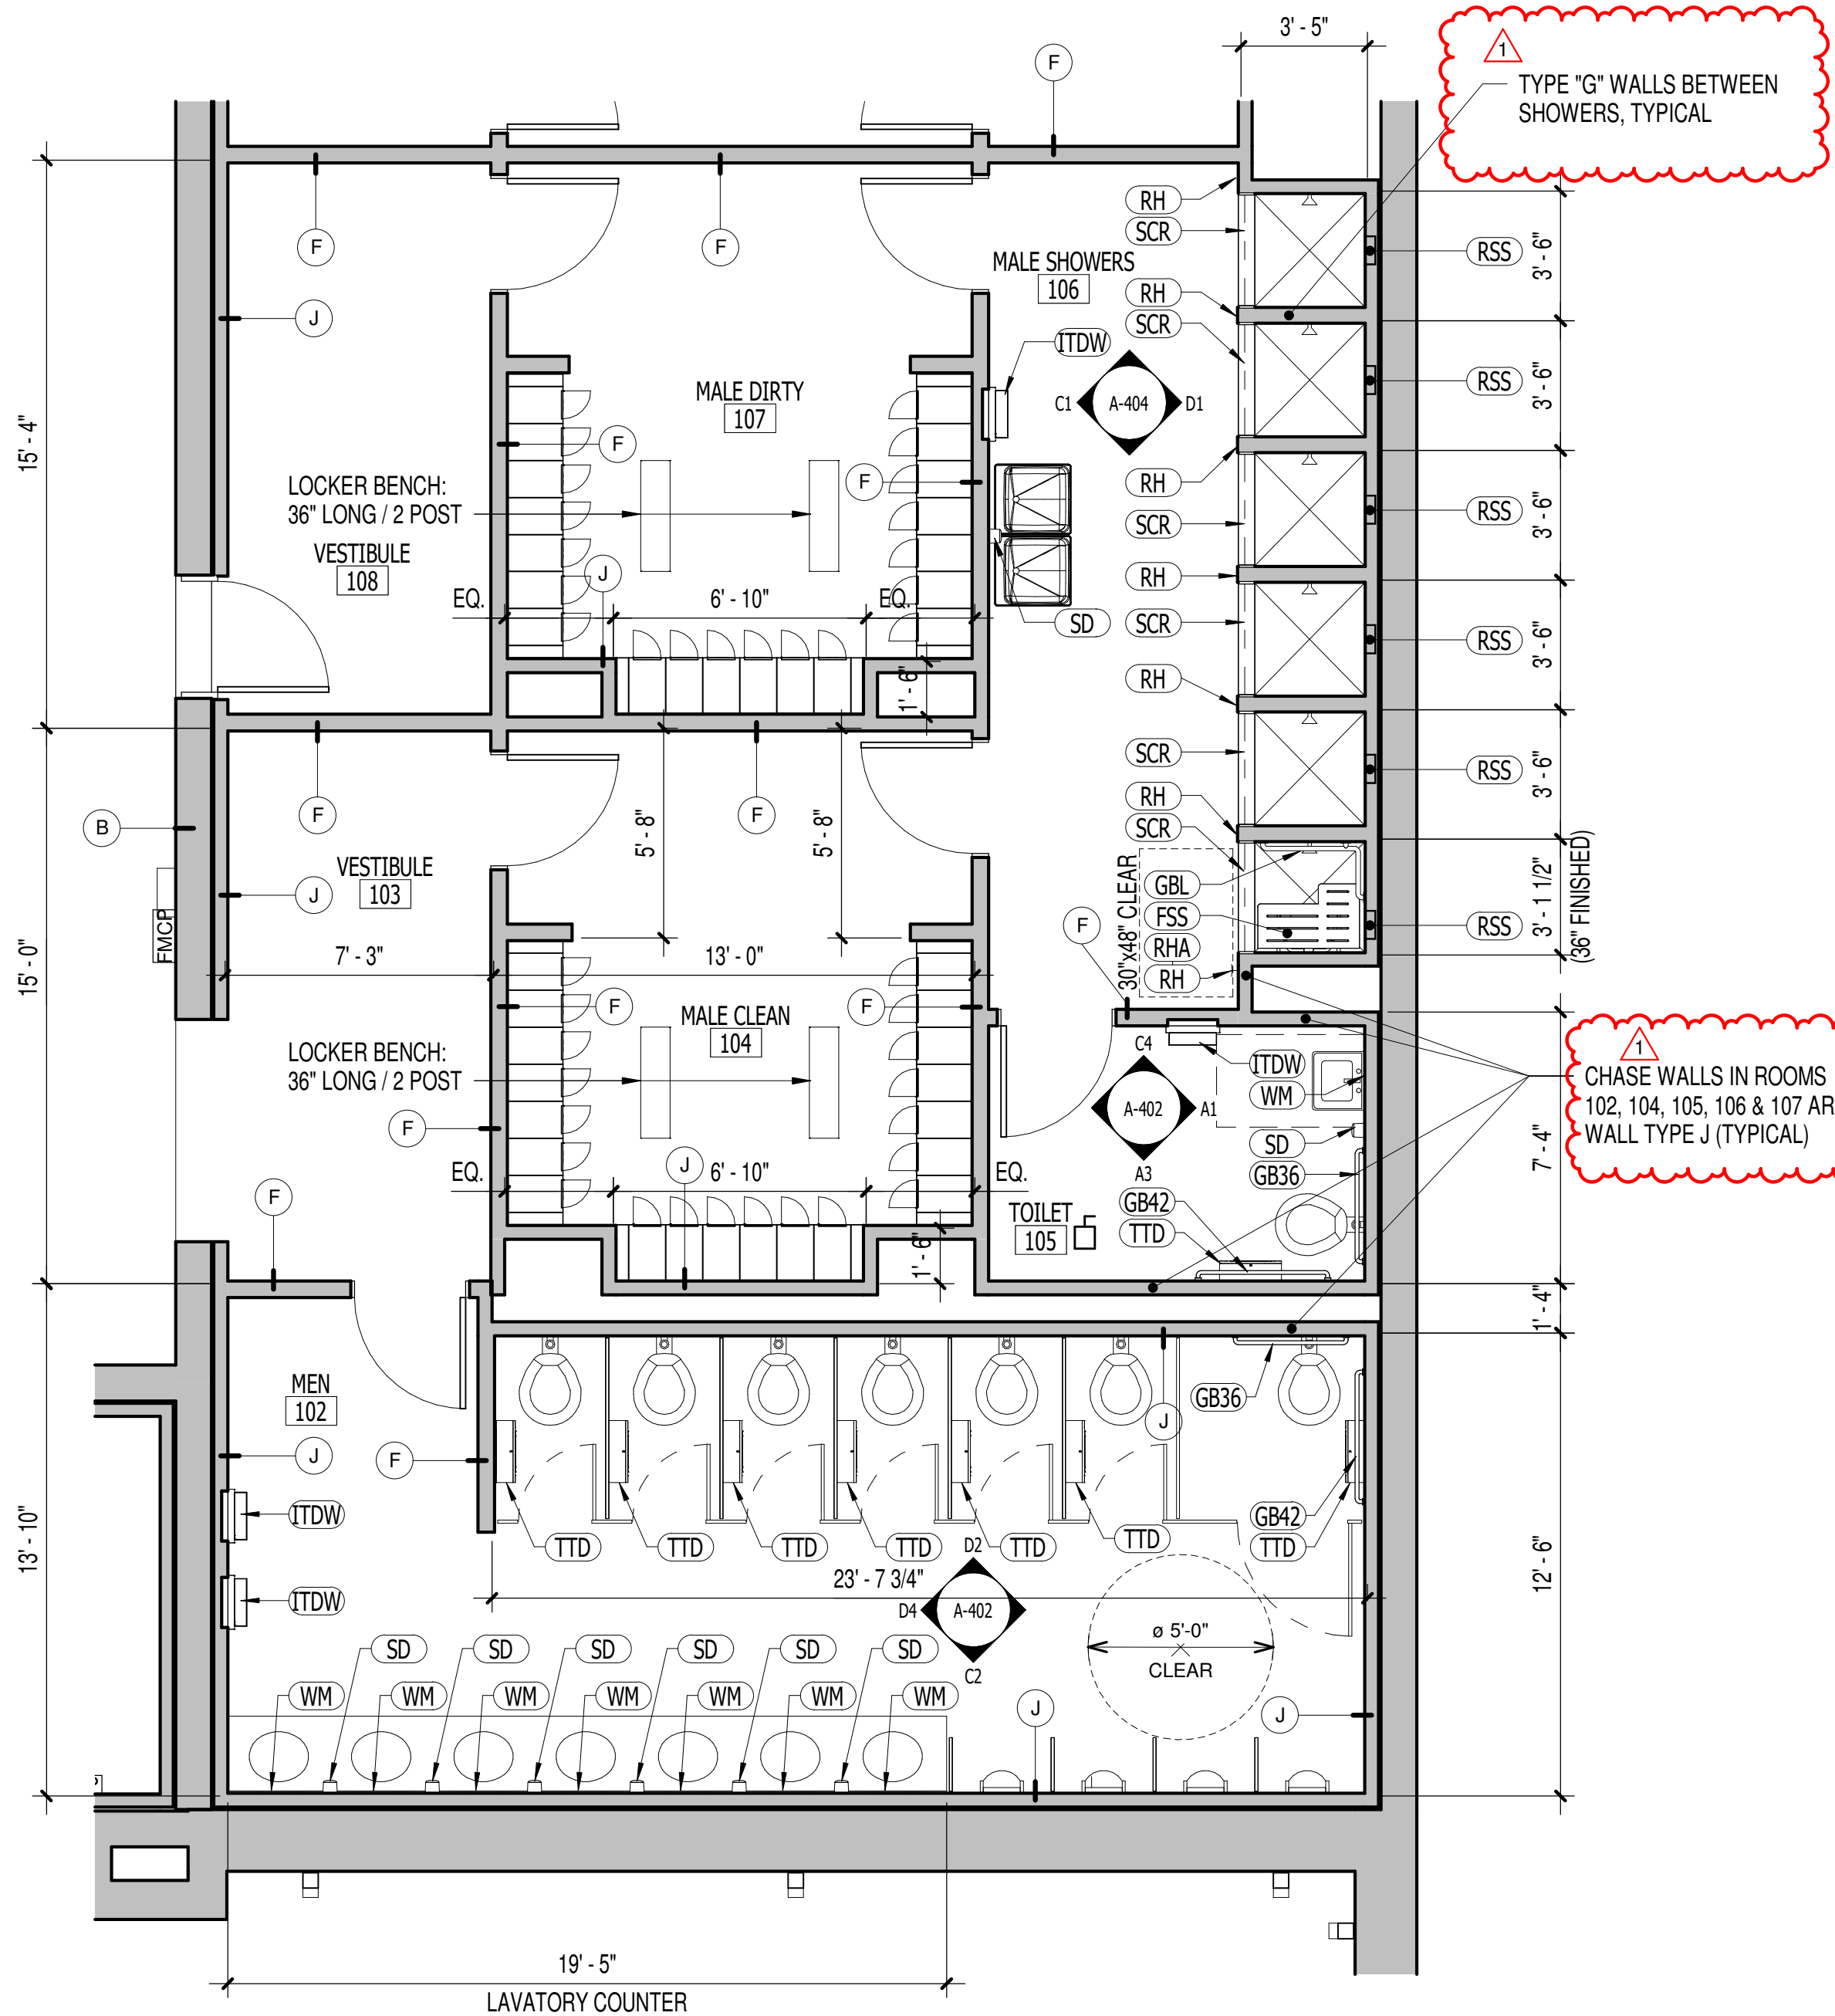


A4

ENLARGED MEN'S ROOM PLAN


SCALE: 1/4" = 1'-0"

NOTE: ALL DIMENSIONS ARE TO FACE OF STUD.
SEE INTERIORS DRAWINGS FOR LOCKERS.

GRAPHIC SCALE: 1/4"=1'-0"

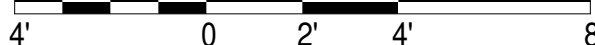

GRAPHIC SCALE: 1/2"=1'-0"

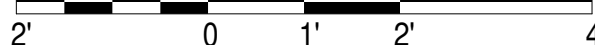

FOR COMMANDER NAVFAC
ACTIVITY Approved by Erik A. Lewis,
Infrastructure Engineering Branch Head,
FRCE Cherry Point via Electronic Signature

SATISFACTORY TO 12/24/2025

DES DLG DRW DLG CHK DJE

PM/DM KTB/SOM

BRANCH MANAGER CGM

CHIEF ENG/ARCH JWJ

FIRE PROTECTION HPN

NAVAL FACILITIES ENGINEERING SYSTEMS COMMAND
NAVAL FACILITIES ENGINEERING SYSTEMS COMMAND ~ MIDATLANTIC
DESIGN AND CONSTRUCTION (DD CORE)
MARINE CORPS AIR STATION
CHERRY POINT, NC

P-995 COMPOSITE REPAIR FACILITY

ENLARGED RESTROOM PLANS AND DETAILS

SCALE: AS INDICATED
PROJECT NO.: 1692230
STA. PROJ. NO.:
NAVFAC DRAWING NO.: 12938286
SHEET 138 OF 456
A-401

DRAWING REVISION: 25 AUGUST 2020

C:\Users\griffith\Documents\2136 ARCH_2023_griffith@mbfarchitects.com.rvt
4/14/2026 11:16:54 AM


File
Print

D

C

B


A

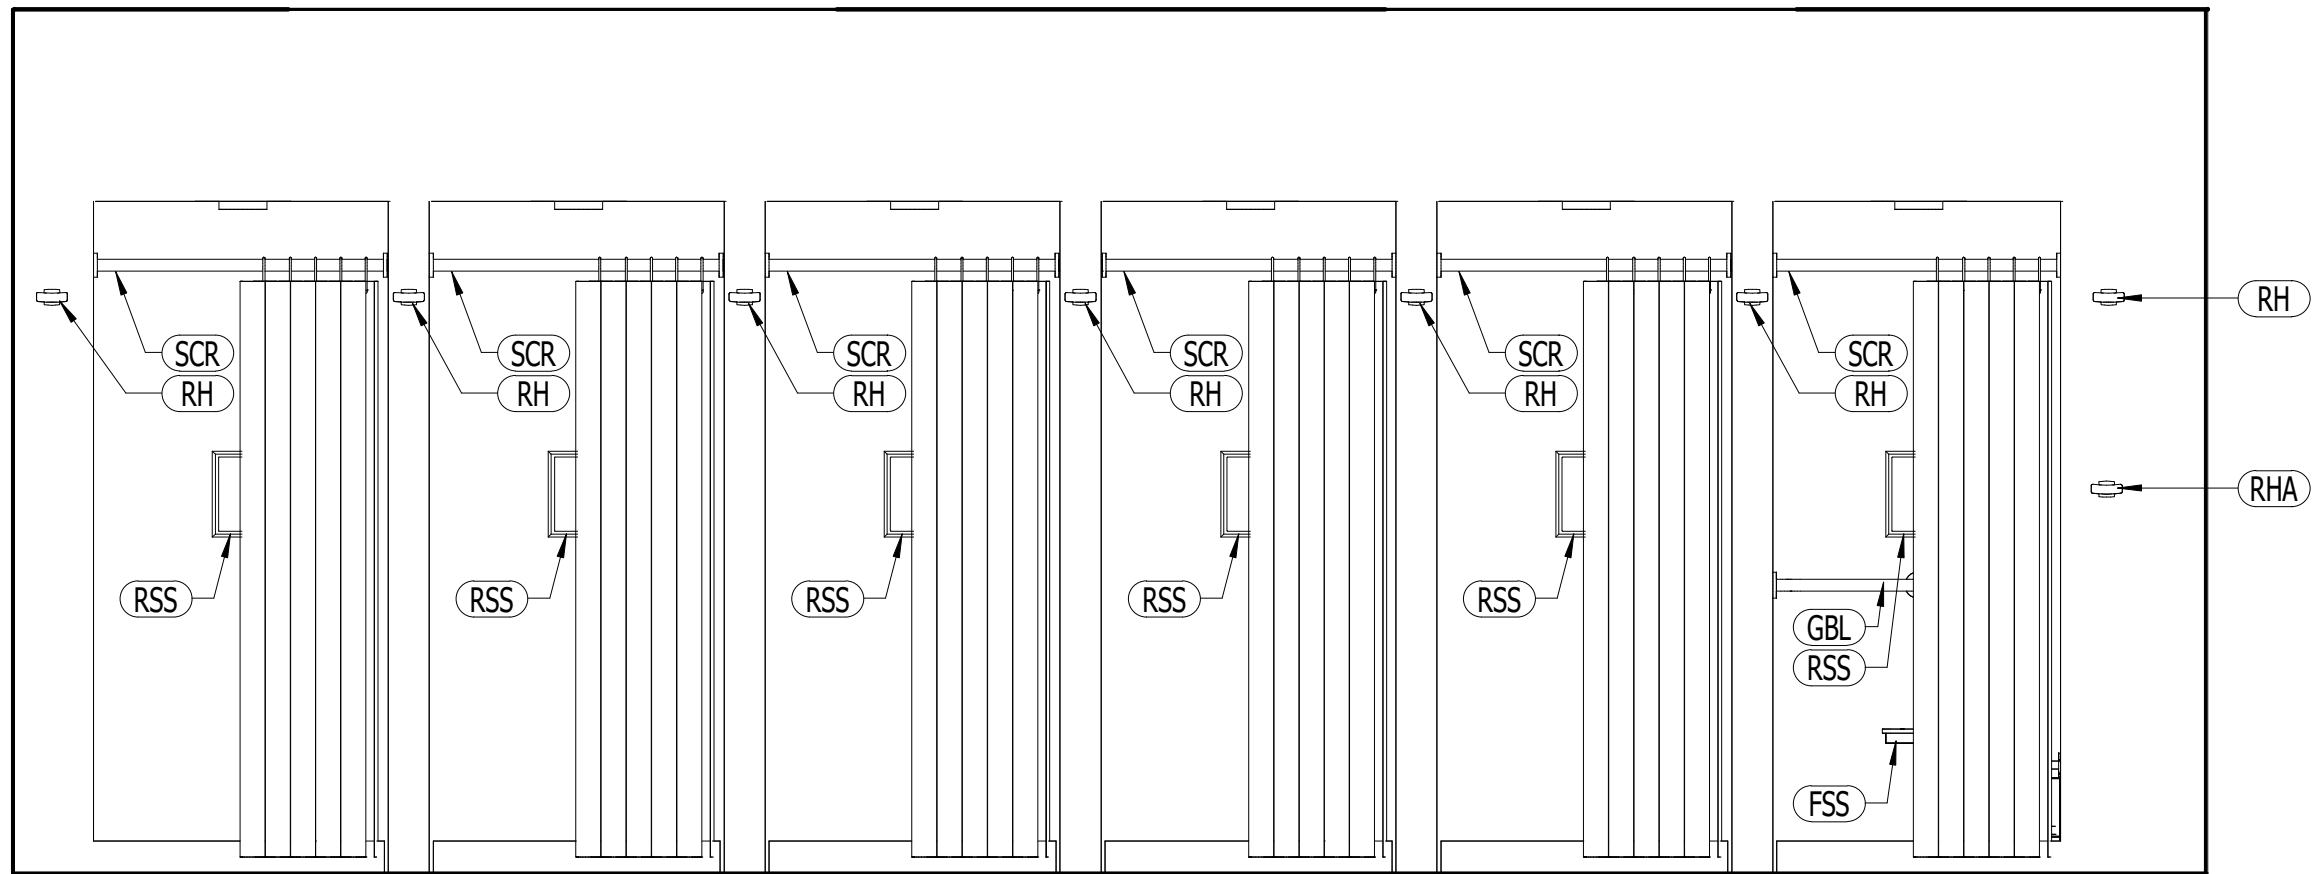


D1 ELEVATION AT MALE SHOWERS 106 - PLAN EAST
SCALE: 1/2" = 1'-0"



C1 ELEVATION AT MALE SHOWERS 106 - PLAN WEST
SCALE: 1/2" = 1'-0"

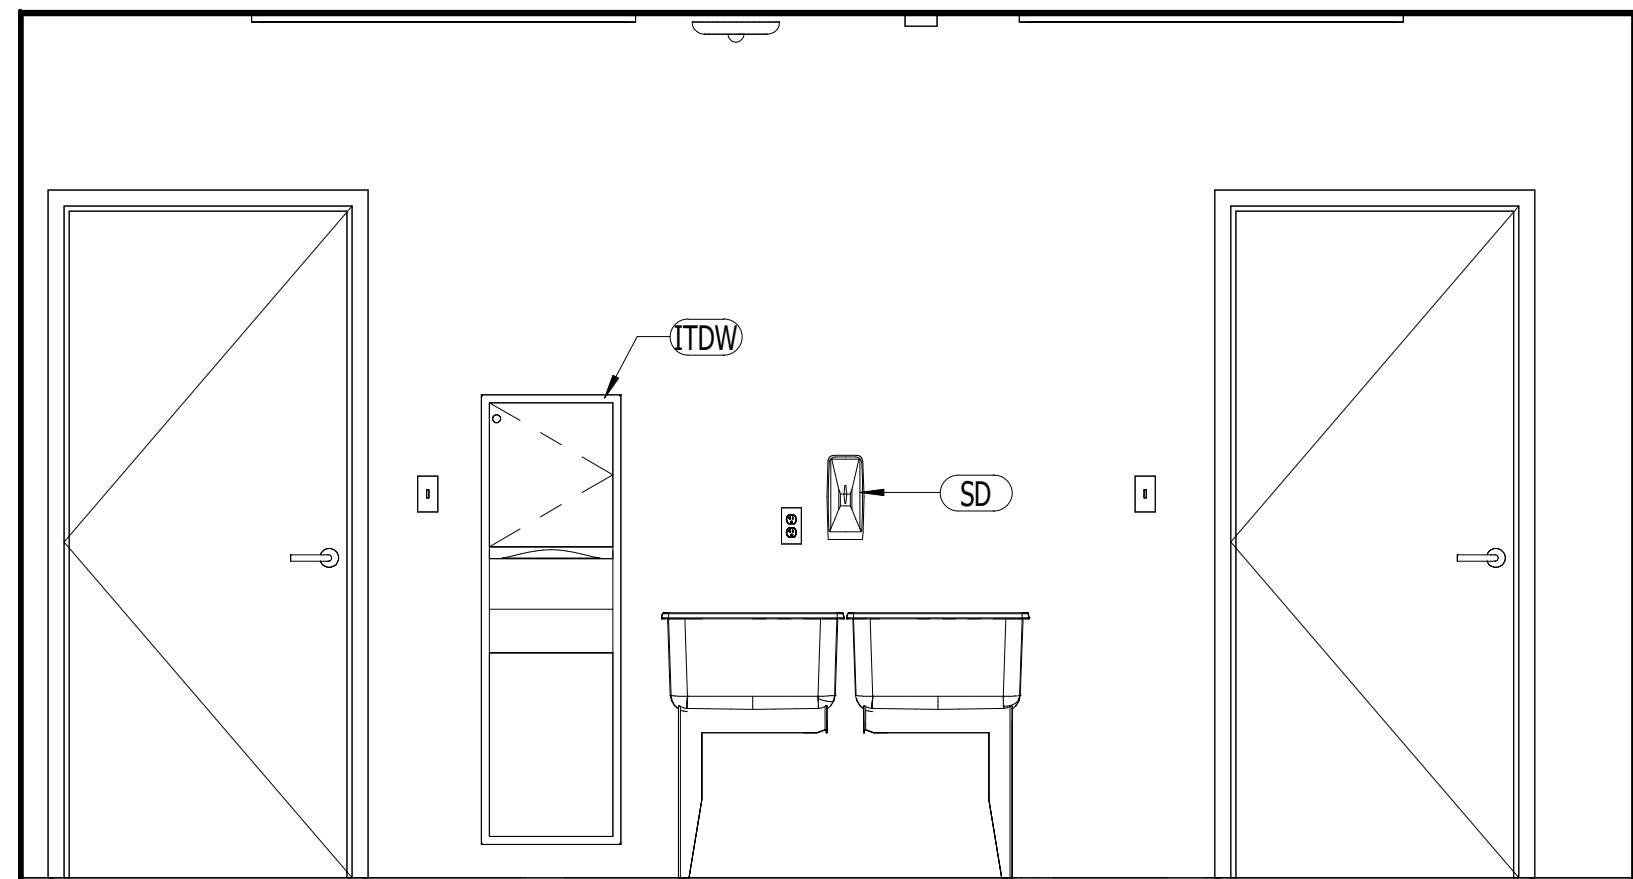


A1 ELEVATION AT FEMALE 111 - PLAN WEST
SCALE: 1/2" = 1'-0"

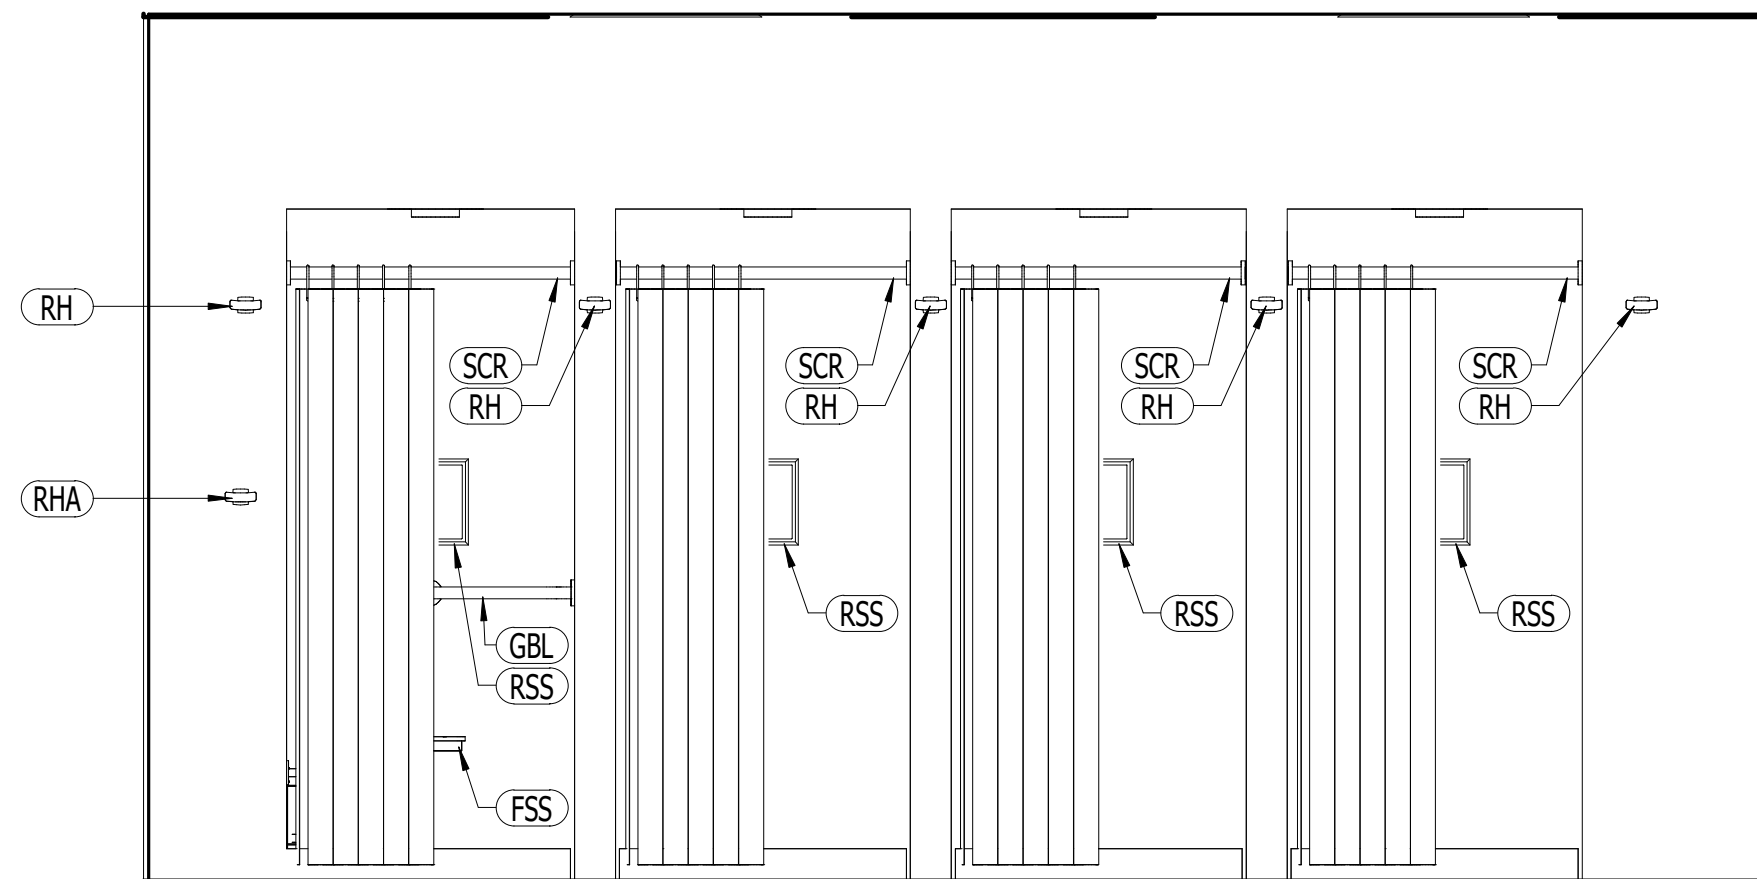


A3 ELEVATION AT FEMALE 111 - PLAN EAST
SCALE: 1/2" = 1'-0"

3

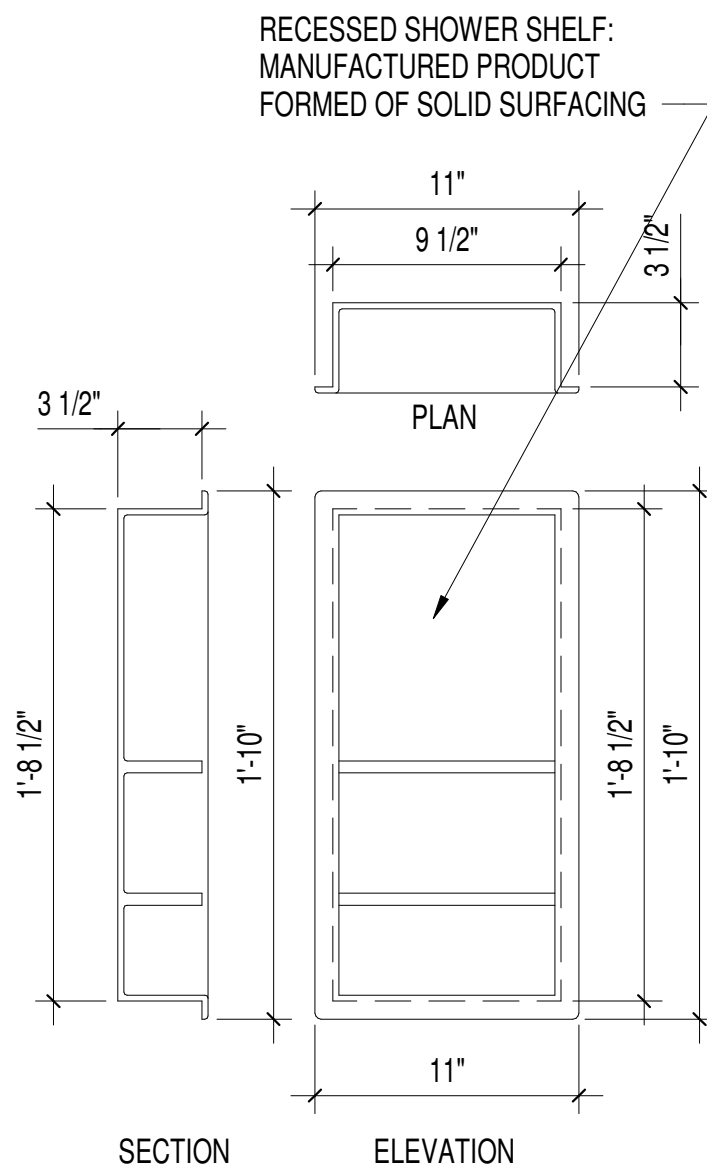

RECESSED SHOWER SHELF

4

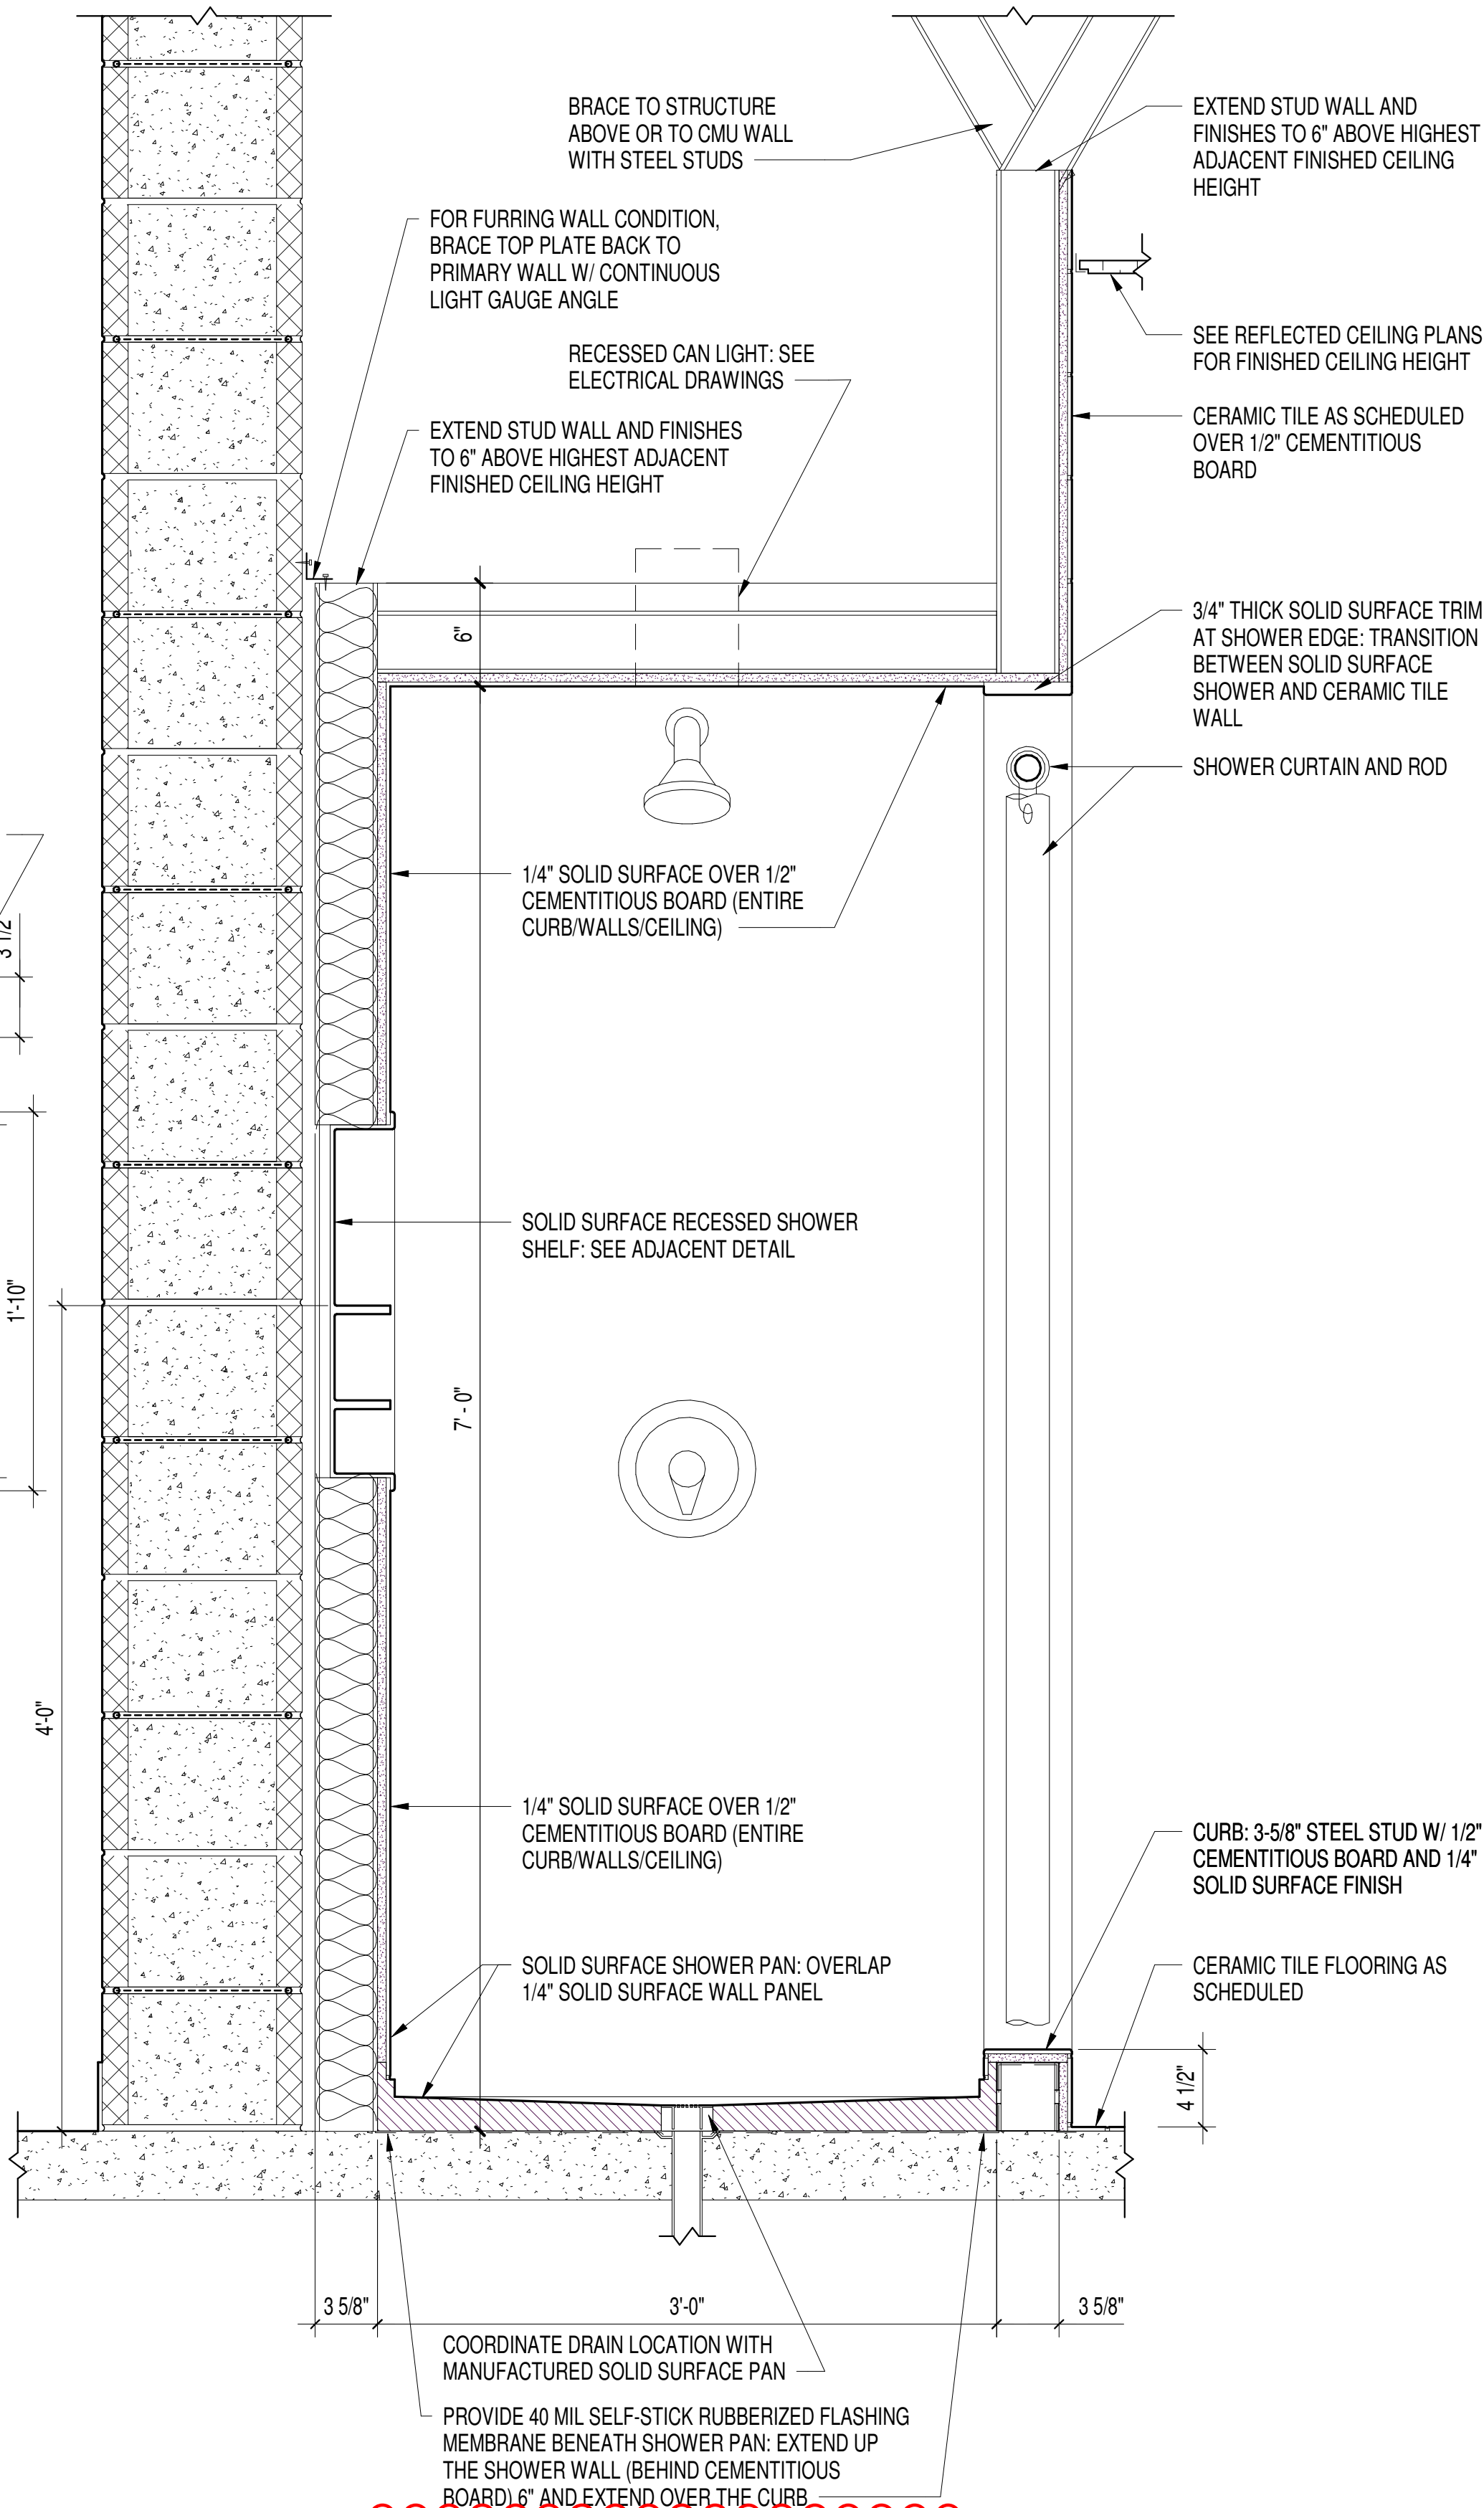

A5 SHOWER SECTION
SCALE: 1 1/2" = 1'-0"

GRAPHIC SCALE: 1/2"=1'-0"





GRAPHIC SCALE: 1 1/2"=1'-0"




--	--	

C:\Users\griffith\Documents\2136 ARCH_2023_griffith@mbfarchitects.com.rvt
4/16/2026 9:53:01 AM

File
Print

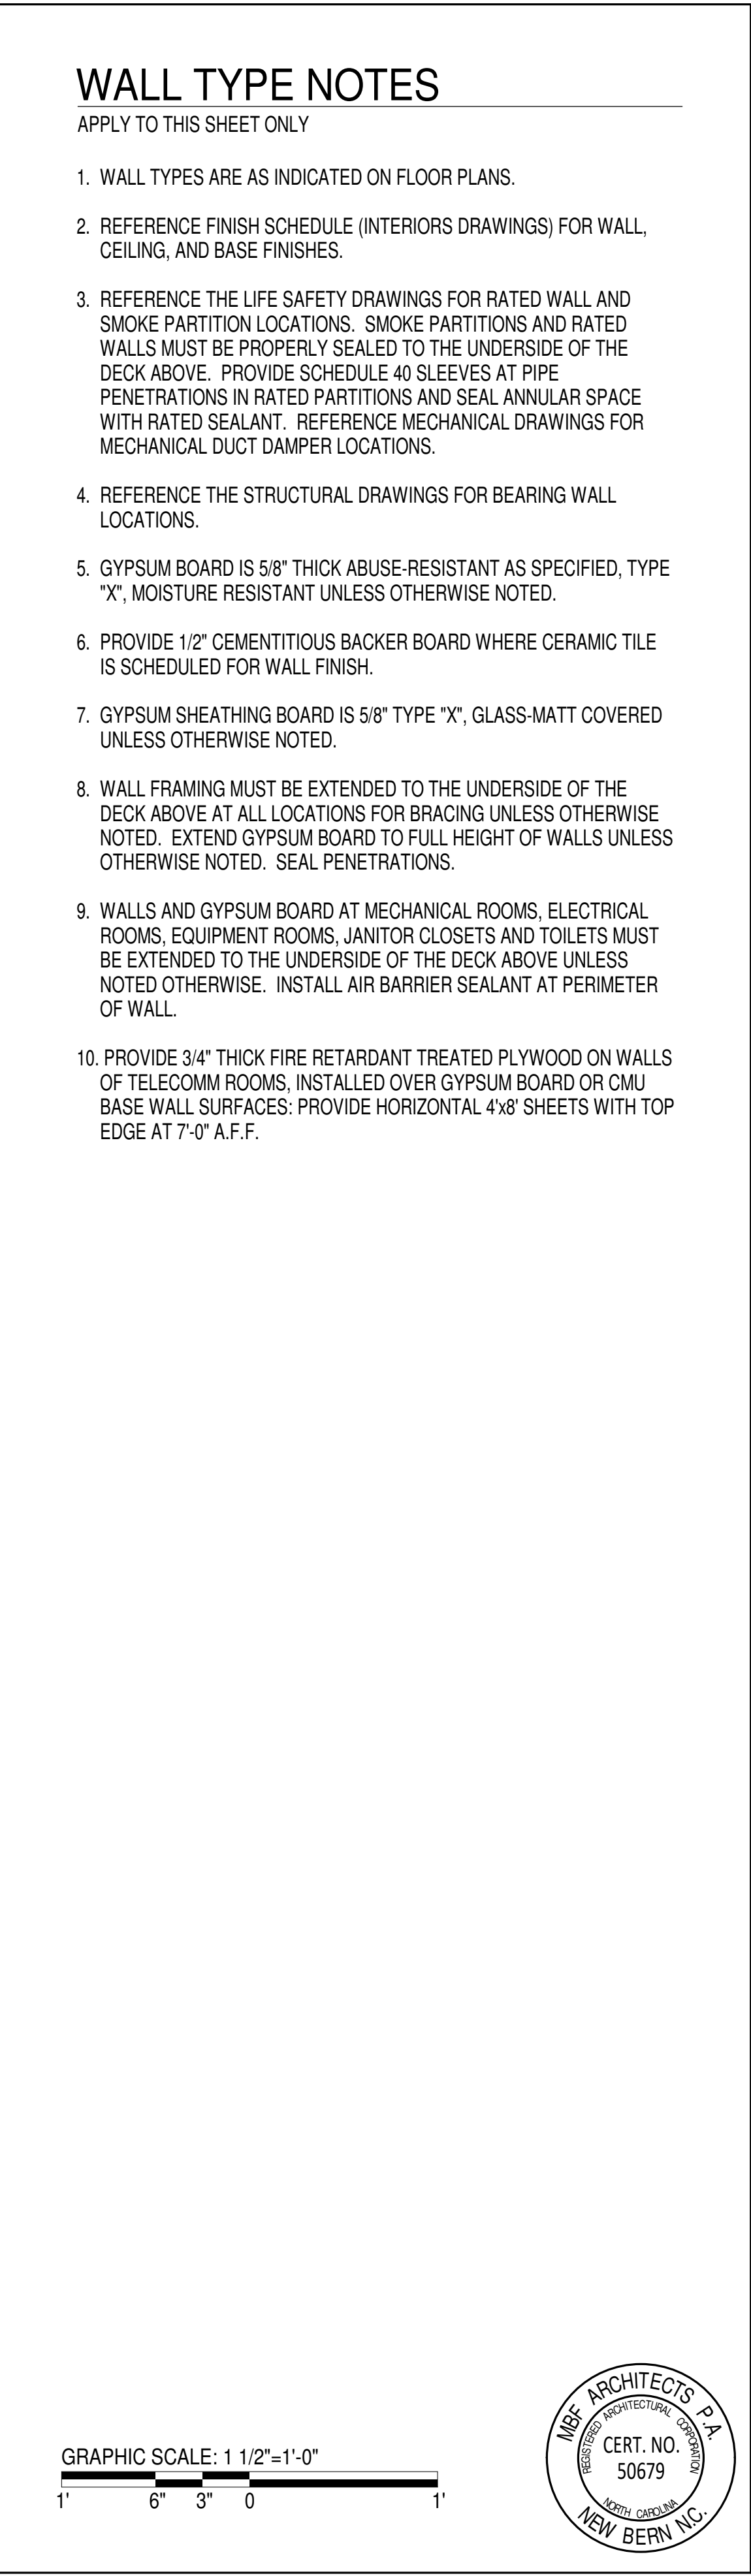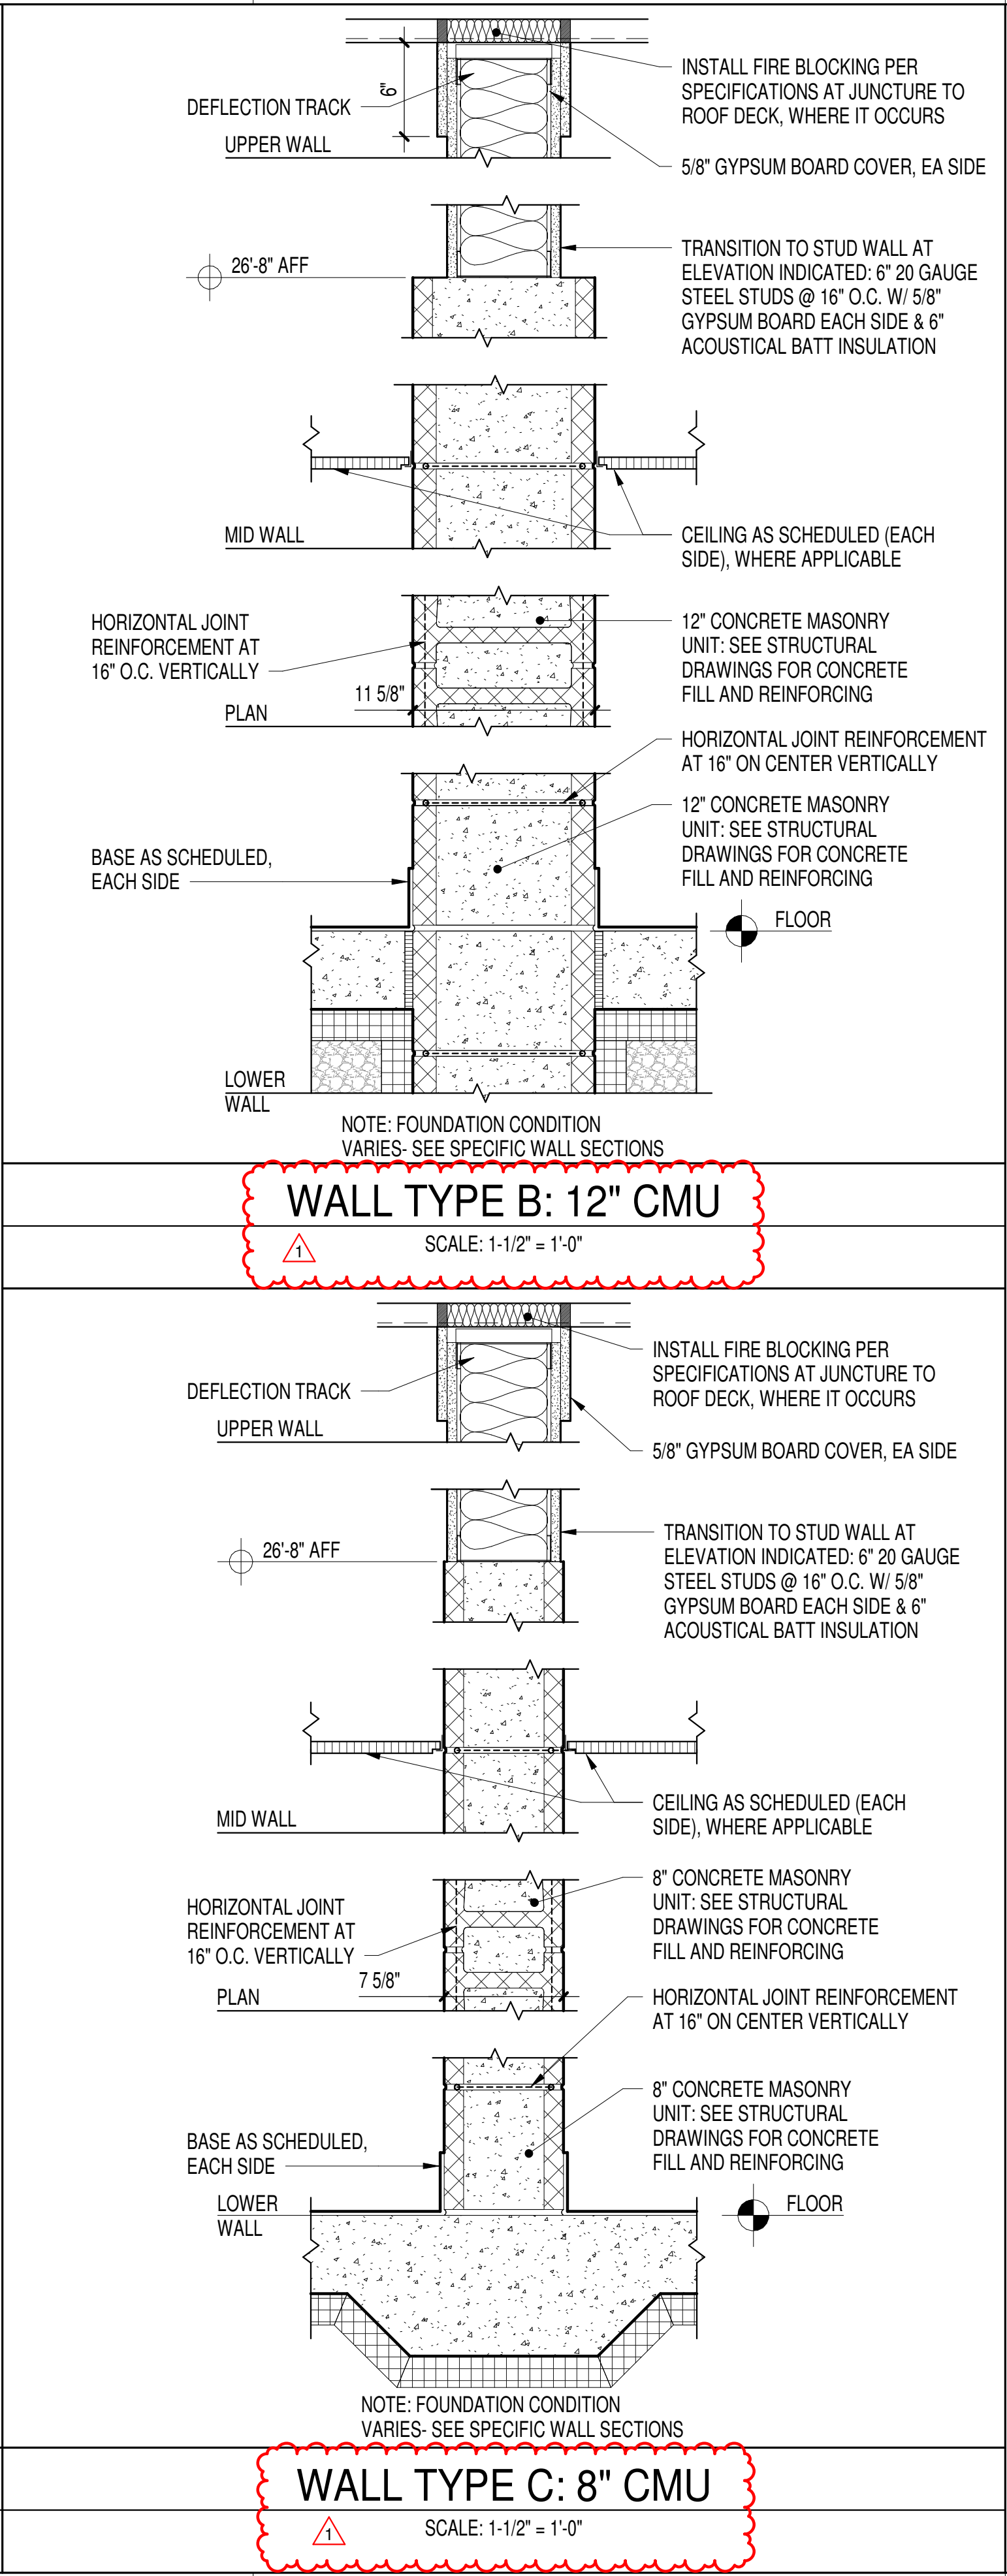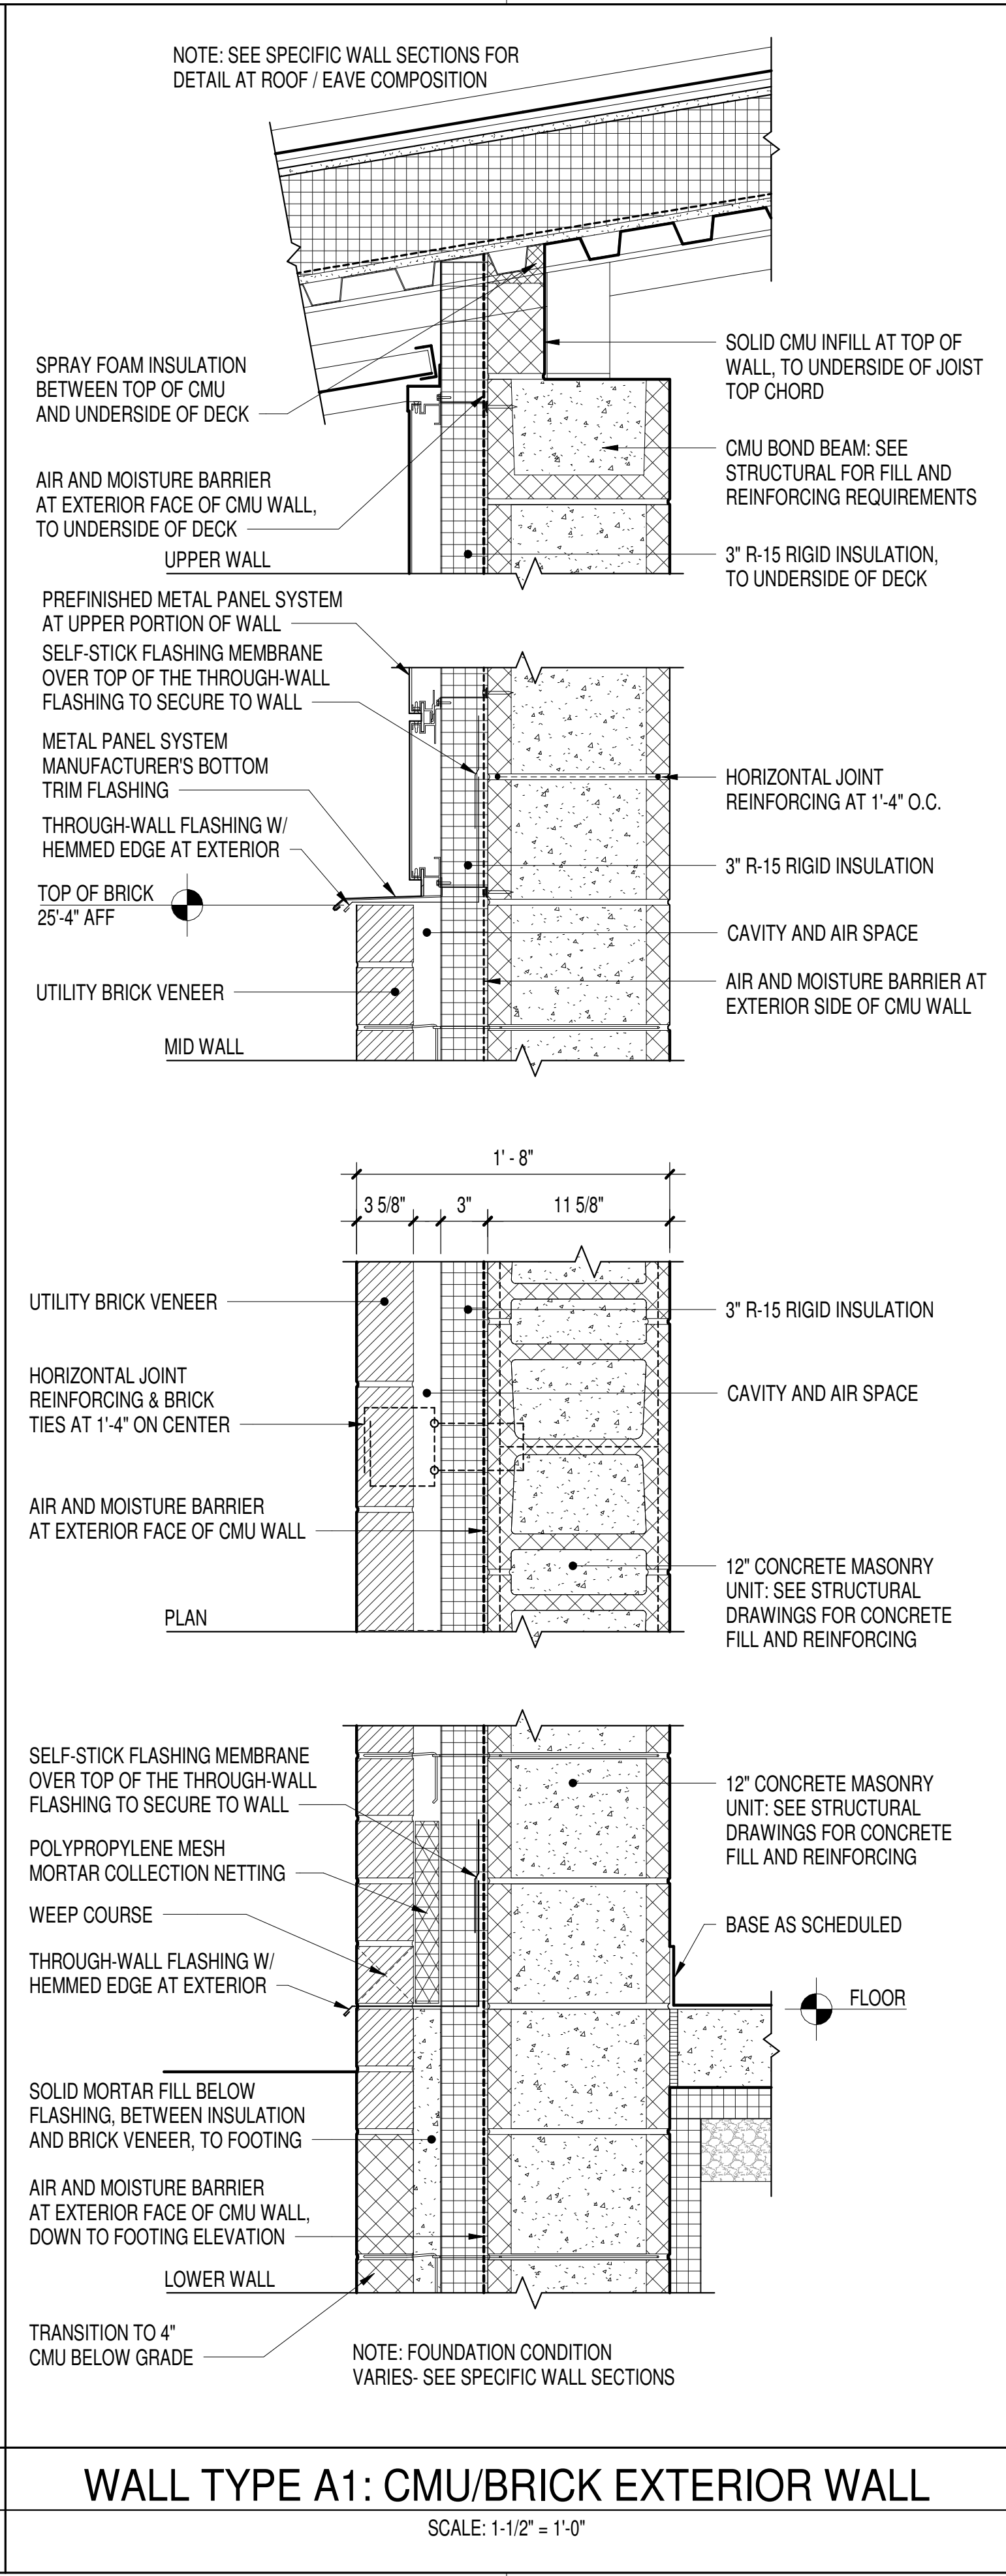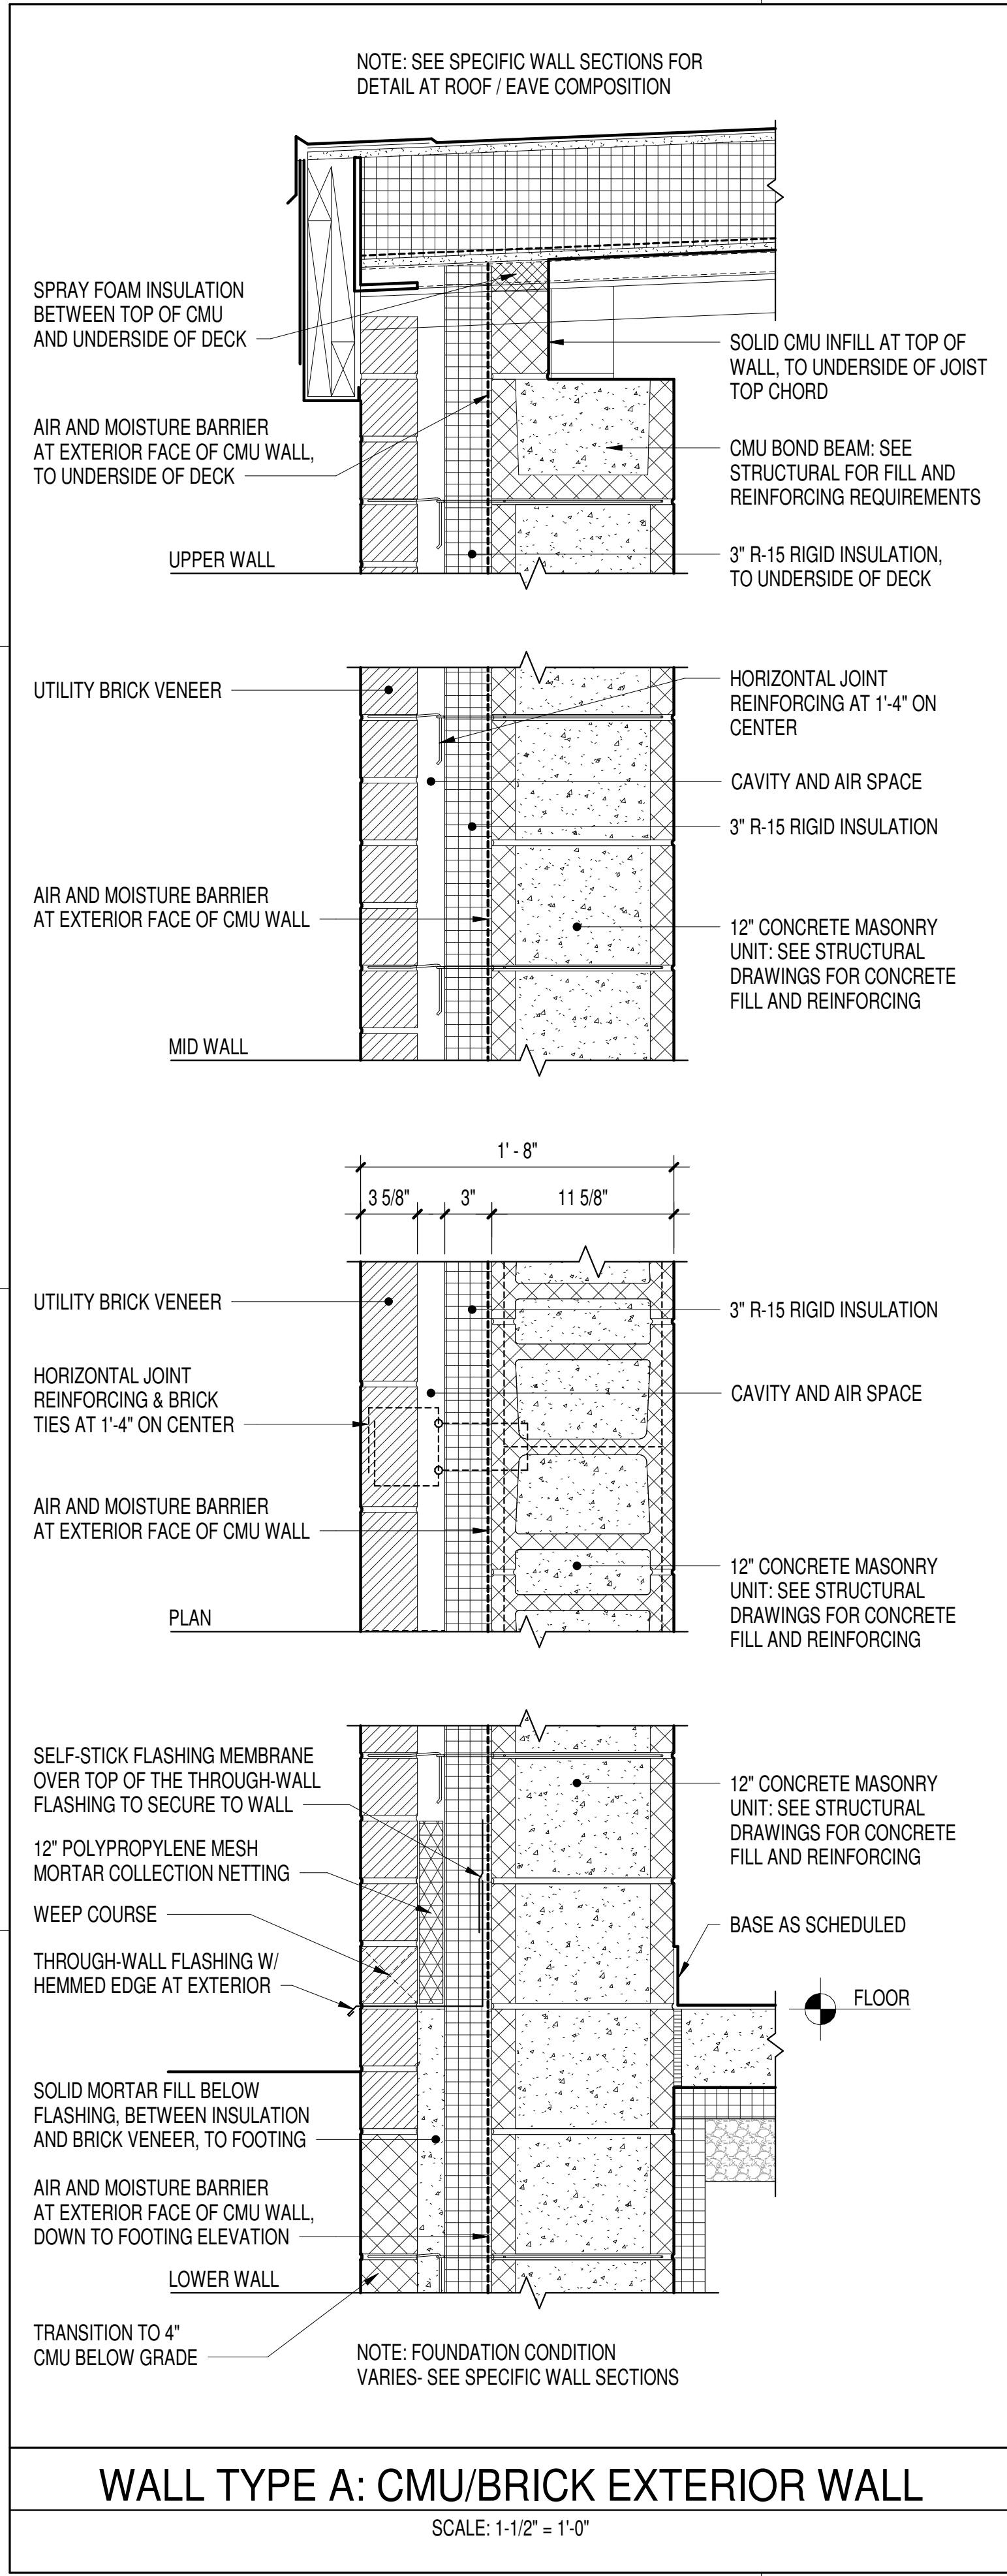

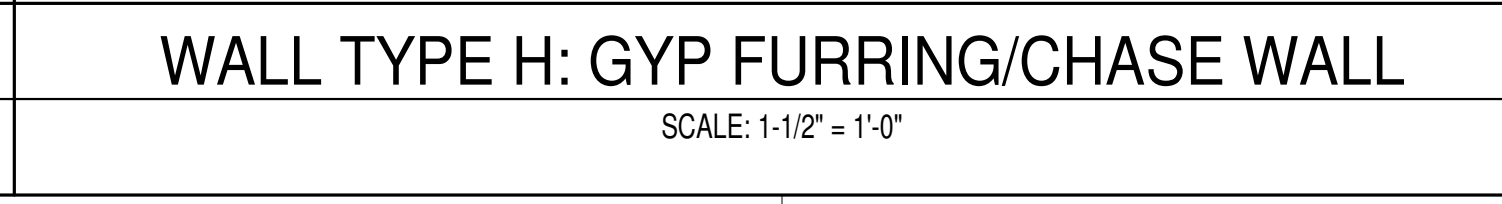

-

File Path: W:\2202 P995 Composite Repair Facility\Revit\2136_P995 WID_R23.rvt
Print Date: 4/16/2026 2:13:00 PM

D

C

B

A

FINISH LEGEND						
NO.	NAME	LOCATION	MANUFACTURER	MODEL	COLOR	SIZE
ACG-1	ACOUSTICAL CEILNG GRID	PAIRED W/ ACT-1	ARMSTRONG CEILINGS	INTERLUDE XL HRC	WHITE	9/16"
ACG-2	ACOUSTICAL CEILNG GRID	PAIRED W/ ACT-2	ARMSTRONG CEILINGS	CO-EXTRUDED CLEAN ROOM	WHITE	15/16"
ACT-1	ACOUSTICAL CEILING TILE	NON GWB OR EXPOSED CEILING LOCATIONS	ARMSTRONG CEILINGS	FINE FISSURED BEVELED TEGULAR	WHITE	24"X24"
ACT-2	ACOUSTICAL CEILING TILE	CLEAN ROOMS	ARMSTRONG CEILINGS	CLEAN ROOM FL	WHITE	24"X24"
CG-1	CORNER GUARD	OUTSIDE CORNERS IN ADMIN SPACES	INPRO	SOLID	GALA 0380	3" WING, INSTALL 8' HIGH
CG-2	STEEL CORNER GUARD	OUTSIDE CORNERS IN SHOP AREAS	INPRO	METALLIC	STAINLESS STEEL	3" WING, INSTALL 8' HIGH
CP-1	CABINET PULL	CASEWORK DOORS & DRAWERS	HAFELE	101.20.744	STAINLESS STEEL	3" CENTER TO CENTER
CPT-1	CARPET TILE	OPEN OFFICE	PATCRAFT	ON NEUTRAL GROUND 1	THREADED, BRAID	18"X36"
FRP-1	FIBERGLASS REINFORCED PANEL	JANITOR CLOSET	MARLITE	STANDARD PEBBLED	MED GREY P430N	48"H
FRP-2	FIBERGLASS REINFORCED PANEL	TRAINING ROOM	MARLITE	ARTIZAN MAX	KISMET, STONE	60"H
GR-1	GROUT	ALL TILE LOCATIONS	CUSTOM BUILDING PRODUCTS	EPOXY GROUT	DOVE GRAY 370	-
HDP-1	HIGH DENSITY POLYETHYLENE	TOILET PARTITIONS & LOCKERS	SCRANTON PRODUCTS	HINY HIDERS	GREY	-
LVT-1	LUXURY VINYL TILE	ADMIN COMMON AREAS	PATCRAFT	LINOCUT	BAREN	9"X36"
PLAM-1	PLASTIC LAMINATE	CASEWORK	FORMICA	8845	BLEACHED LEGNO	-
PNT-1	PAINT	PRIMARY WALLS	SHERWIN WILLIAMS	SW 7056	RESERVED WHITE	-
PNT-2	ACCENT PAINT	ACCENT WALLS	SHERWIN WILLIAMS	SW 7668	MARCH WIND	-
PNT-3	PAINT	DOOR FRAMES	SHERWIN WILLIAMS	SW 7674	PEPPERCORN	-
PNT-4	PAINT	GWB & EXPOSED CEILINGS	SHERWIN WILLIAMS	SW 7757	HIGH REFLECTIVE WHITE	-
PNT-5	PAINT (SEMI-GLOSS)	CLEAN ROOMS	SHERWIN WILLIAMS	SW 7056	RESERVED WHITE	-
RB-1	RUBBER BASE	PRIMARY BASE	ROPPE	MILLWORK PROFILE	123 CHARCOAL	4"H
RB-2	RUBBER BASE	JANITOR	MARLITE	M612	MED GREY P430N	-
RES-1	EPOXY RESIN (ESD)	SHOPS	SHERWIN WILLIAMS	RESUFLOL PERFORMANCE HPS	WHITE	-
RES-2	EPOXY RESIN (ESD)	MAIN CORRIDOR 125 & BACK CORRIDOR 150	SHERWIN WILLIAMS	RESUFLOL PERFORMANCE HPS	ROTUNDA RED	-
S-1	SIGNAGE FINISH	FONT	290 SIGNS	ESSENTIALS COLLECTION	708 SOFT WHITE	-
S-2	SIGNAGE FINISH	BACKGROUND	290 SIGNS	ESSENTIALS COLLECTION	704 BLACK	-
S-3	SIGNAGE FINISH	COPY	290 SIGNS	ESSENTIALS COLLECTION	101 SATIN	-
SC-1	SEALED CONCRETE	UTILITY SPACES	SCOFIELD	SELECT SEAL PLUS	CLEAR	-
SS-1	SOLID SURFACE	COUNTERTOPS	MEGANITE	C259A	PALLADIUM	1/2" THICK
SS-2	SOLID SURFACE	SHOWER SURROUNDS	CORIAN	-	GLACIER WHITE	1/4" THICK
T-1	FLOOR TILE	BATHROOMS & JANITOR	MOSAIC TILE	LAB	COAL	12X24
T-2	WALL TILE	BATHROOMS & JANITOR	ARCHITESSA	ESSENCE REFINED	MONTAUK GREY	12X24
T-3	ACCENT TILE	BATHROOM WALLS	ARCHITESSA	GRANT	NAVY MATTE	4X16
T-4	SMALL FLOOR TILE	SHOWER AREAS	MOSAIC TILE	LAB	COAL	1X6 MOSAIC
TS-1	TRANSITION STRIP	LVT TO EPOXY	SCHLUTER SYSTEMS	VINPRO-U	SATIN ANODIZED	-
TS-2	TRANSITION STRIP	CARPET TO EPOXY	SCHLUTER SYSTEMS	RENO-RAMP/K	SATIN ANODIZED	-
TS-3	TRANSITION STRIP	EPOXY TO CONCRETE	SCHLUTER SYSTEMS	SCHIENE	SATIN ANODIZED	-
TS-4	TRANSITION STRIP	FLOOR TILE TO EPOXY	SCHLUTER SYSTEMS	RENO-V	SATIN ANODIZED	-
TS-5	TRANSITION STRIP	TILE INSIDE CORNER	SCHLUTER SYSTEMS	DILEX-AHK	SATIN ANODIZED	-
TS-6	TRANSITION STRIP	TILE OUTSIDE CORNER	SCHLUTER SYSTEMS	QUADEC	SATIN ANODIZED	-
TS-7	TRANSITION STRIP	FRP TO GWB	MARLITE	EDGE M370	WHITE PVC TRIM	-
WD-1	WOOD FINISH	WOOD ENTRY DOORS	MASONITE ARCHITECTURAL	WHITE OAK	COCOA BEAN	-
WS-1	WINDOW SHADE	EXTERIOR WINDOWS	MERMET	GREENSCREEN EVOLVE 3%	RAIN	-
WS-2	WINDOW SHADE (BLACKOUT)	CONFERENCE	MERMET	ZORA TWILIGHT BLACKOUT	PEWTER/WHITE	-

FURNITURE SCHEDULE

NO.	ITEM	QTY	NO.	ITEM	QTY
A1	WALL CLOCK	11	S4	TOOL CABINET CONFIGURATION NO. 4	2
A2	COAT HOOK	2	S6	TOOL CABINET CONFIGURATION NO. 6	20
A3	TRASH/RECYCLE RECEPTACLE	6	S7	TOOL CABINET CONFIGURATION NO. 7	3
A4	MOP BUCKET	1	S9	TOOL CABINET CONFIGURATION NO. 9	2
A5	DESK WASTEBASKET	108	S10	TOOL CABINET CONFIGURATION NO. 10	8
A6	RUBBER DRAINAGE MAT	8	S11	4-HIGH LATERAL FILE CABINET	8
A7	DRY ICE BIN	3	S12	4-HIGH VERTICAL FILE CABINET	5
A8	3-SLOT PAPER RACK	7	S13	PRINT SUPPLY STORAGE CABINET	2
A9	WALK-OFF MAT	12	S14	LAPTOP STORAGE CABINET	4
A10	FIRE EXTINGUISHER	18	S15	FLAMMABLE STORAGE CABINET	4
A11	OILY WASTE CAN	1	S17	HONEYCOMB STORAGE RACK	6
C1	HEIGHT ADJUSTABLE SHOP STOOL	86	S18	INDUSTRIAL STORAGE CABINET	1
C2	OFFICE TASK CHAIR	30	S19	72" FREEZER SHELVING	8
C3	CONFERENCE CHAIR	10	S21	CORROSIVE SAFETY CABINET	1
C4	GUEST CHAIR	8	T1	CONFERENCE TABLE	1
C5	LOUNGE CHAIR W/ TABLET ARM	1	T2	ROUND MEETING TABLE	2
C6	BREAK ROOM CHAIR	60	T3	CAFETERIA TABLE	5
D1	U-SHAPED DESK	2	T4	180" X 96" PATCH TABLE	1
D2	RECTANGULAR STEEL DESK	5	T5	120" X 36" STAINLESS STEEL GANGING TABLE	8
D3	L-SHAPED DESK	1	T6	192" X 72" PATCH TABLE	1
E1	REFRIGERATOR	5	T7	PRINTER TABLE	1
E2	MICROWAVE	6	WB1	72" X 30" ESD WORKBENCH	15
E4	UNDER COUNTER REFRIGERATOR	1	WB2	72" X 30" STAINLESS STEEL WORKBENCH	21
S1	60"W STEEL STORAGE SHELF	23	WB3	120" X 48" STAINLESS STEEL WORKBENCH	55
S2	72"W STEEL STORAGE SHELF	9	WB4	120" X 36" BUTCHERBLOCK WORKBENCH	4
S3	48"W STEEL STORAGE SHELF	2	WS1	OPEN OFFICE WORKSTATION	22

EQUIPMENT SCHEDULE

NO.	ITEM	QTY
X1	TABLETOP DIGITAL SCALE	1
X2	SUBZERO UPRIGHT FREEZER	2
X3	DVD TABLE	2
X4	DEBULK TABLE	2
X5	FLOOR SCALE	1
X6	6X6 COMPOSITE OVEN	2
X7	10X10 COMPOSITE OVEN	2
X8	FERRIS WHEEL STORAGE RACK	9
X9	BLAST CABINET	2
X10	SLURRY WET BLASTER	1
X11	MOTORIZED PALLET LIFT	1
X12	SAMPLE CUTTING MACHINE	1
X13	TENSILE TESTER	1
X14	MICROSCOPE	1
X16	GRINDER	1
X17	BAND SAW	2
X18	DRILL MILL	1
X19	BELT SANDER	2
X20	12X20 COMPOSITE OVEN	2
X21	PAINT SHAKER W/ PEDESTAL	1
X22	HONEYCOMB MACHINE	1
X23	SUBZERO CHEST FREEZER	2

SHEET NOTES

- A. FINISHES INDICATED ARE THE APPROVED BASIS OF DESIGN TO CONVEY COLOR, PATTERN, TEXTURE AND SALIENT CHARACTERISTICS ONLY. THE LISTING OF MANUFACTURER INFORMATION IS NOT INTENDED TO LIMIT THE SELECTION OF PRODUCTS PROVIDED BY OTHER MANUFACTURERS. PRODUCTS MEETING THESE CRITERIA WILL BE CONSIDERED AND MUST BE REVIEWED BY THE INTERIOR DESIGNER OF RECORD (IDOR) AND THE NAVFAC INTERIOR DESIGNER AND APPROVED BY THE CONTRACTING OFFICER.
- B. FINISH ITEMS ARE NOT TO BE SUBSTITUTED DUE TO ORDERING LEAD TIMES. IT IS THE CONTRACTOR'S RESPONSIBILITY TO ORDER ALL MATERIALS IN TIME TO AVOID DELAYS.
- C. COORDINATE THERMOSTAT LOCATIONS WITH MECHANICAL DRAWINGS AND CONSTRUCTION MANAGER. INSTALL THERMOSTATS NEAR A CORNER OF THE ROOM OR BY LIGHT SWITCHES. DO NOT INSTALL THERMOSTATS IN THE CENTER OF A WALL.
- D. SPRAY PAINT ELECTRICAL PANELS, ACCESS PANELS, AND EXPANSION JOINTS TO MATCH THE ADJACENT WALL COLOR. PANELS PAINTED BY BRUSH ARE NOT ACCEPTABLE
- E. ALL FLOORING TRANSITIONS MUST MEET ABA GUIDELINES. FLOORING TRANSITIONS OCCURRING UNDER DOORS MUST BE CENTERED UNDER DOOR.
- F. ALL WALL AND CEILING FINISHES IN VERTICAL EXIT WAYS, EXIT LOBBIES, AND EXIT CORRIDORS MUST MEET MINIMUM CLASS A RATING.
- G. ROOMS IDENTIFIED TO RECEIVE TILE ON WALLS MUST INCLUDE METAL TRANSITIONS ON ALL OUTSIDE AND INSIDE CORNERS AS WELL AS THE INTERSECTION BETWEEN FLOOR AND WALL TILE WHERE APPLICABLE FOR A COMPLETE INSTALLATION.
- H. INSTALL CORNER GUARD ON ALL OUTSIDE CORNERS. INSTALL END CAPS ON ALL OPEN ENDED WALLS. CORNER GUARDS AND END CAPS MUST BE FULL HEIGHT AND SHOULD NOT BE USED ON CMU WALLS, TILED WALLS, OR MANUFACTURED STONE WALLS. ADMIN OFFICES TO RECEIVE CORNER GUARD CG-1. SHOP AREAS TO RECEIVE CORNER GUARD CG-2
- I. ALL AREAS TO RECEIVE RESILIENT BASE (RB-1) WITH THE EXCEPTION OF AREAS RECEIVING FLOOR TILE OR EPOXY RESINOUS FLOORING.
- J. ALL WALLS TO BE PAINTED (PNT-1) UNLESS OTHERWISE INDICATED. ALL HOLLOW METAL DOORS AND DOOR FRAMES TO BE PAINTED (PNT-3). ALL GWB AND EXPOSED CEILINGS TO BE PAINTED (PNT-4).
- K. ALL SHOWER PANS AND SHOWERS WALLS TO BE SOLID SURFACE (SS-2).
- L. ALL TOILET PARTITIONS, LOCKERS & LOCKER ROOM BENCHES TO BE HDPE FINISH (HDP-1)
- M. ALL INTERIOR WOOD DOORS TO BE FINISHED (WD-1).
- N. ALL TILE TO RECEIVE GROUT FINISH (GR-1).
- O. ALL MATERIALS/PRODUCTS ARE TO BE INSTALLED PER MANUFACTURER'S INSTALLATION REQUIREMENTS.
- P. SEE I-601 FOR ROOM FINISH SCHEDULE. SEE I-602 FOR FINISH LEGEND.

ACRONYM LEGEND

CFCI	CONTRACTOR FURNISHED CONTRACTOR INSTALLED
FF&E	FURNITURE FIXTURES & EQUIPMENT
EQ	EQUAL ON BOTH SIDES
GFGI	GOVERNMENT FURNISHED GOVERNMENT INSTALLED
HPL	HIGH PRESSURE LAMINATE
SID	STRUCTURAL INTERIOR DESIGN
TYP.	TYPICAL DIMENSION
U.O.N.	UNLESS OTHERWISE NOTED
V.I.F.	VERIFY IN FIELD

DATE	04/16/2026
DESCRIPTION	
SYN	1 PPT Revision
SEAL	
APPROVED	
FOR COMMANDER NAVFAC	
ACTIVITY	Approved by Erik A. Lewis, Infrastructure Engineering Branch Head, FRCE Cherry Point via Electronic Signature
SATISFACTORY TO	12/24/2025
DES	WID
DRW	APG
CHK	JKD
PMIDM	KTB/SOM
BRANCH MANAGER	CGM
CHIEF ENGINEER	JWJ
FIRE PROTECTION	HPN
NAVAL FACILITIES ENGINEERING SYSTEMS COMMAND	NAVAL FACILITIES ENGINEERING SYSTEMS COMMAND ~ MIDATLANTIC
DESIGN AND CONSTRUCTION (DC) CODE	NAVAL STATION - NORFOLK, VA
MARINE CORPS AIR STATION	CHERRY POINT, NC
P-995 COMPOSITE REPAIR FACILITY	
SCHEDULES & LEGENDS	
SCALE:	1/8" = 1'-0"
EPROJECT NO.:	1692230
STA. PROJ. NO.	
NAVFAC DRAWING NO.	12938345
SHEET	197 OF 456
I-602	
DRAWING REVISION: 25 AUGUST 2020	

D

C

B

A