

C:\Users\griffith\Documents\2136 ARCH_2023_griffith@mbfarchitects.com.rvt
4/8/2026 10:17:45 PM

File
Print

D

C

B

A


1

2

3

4


5

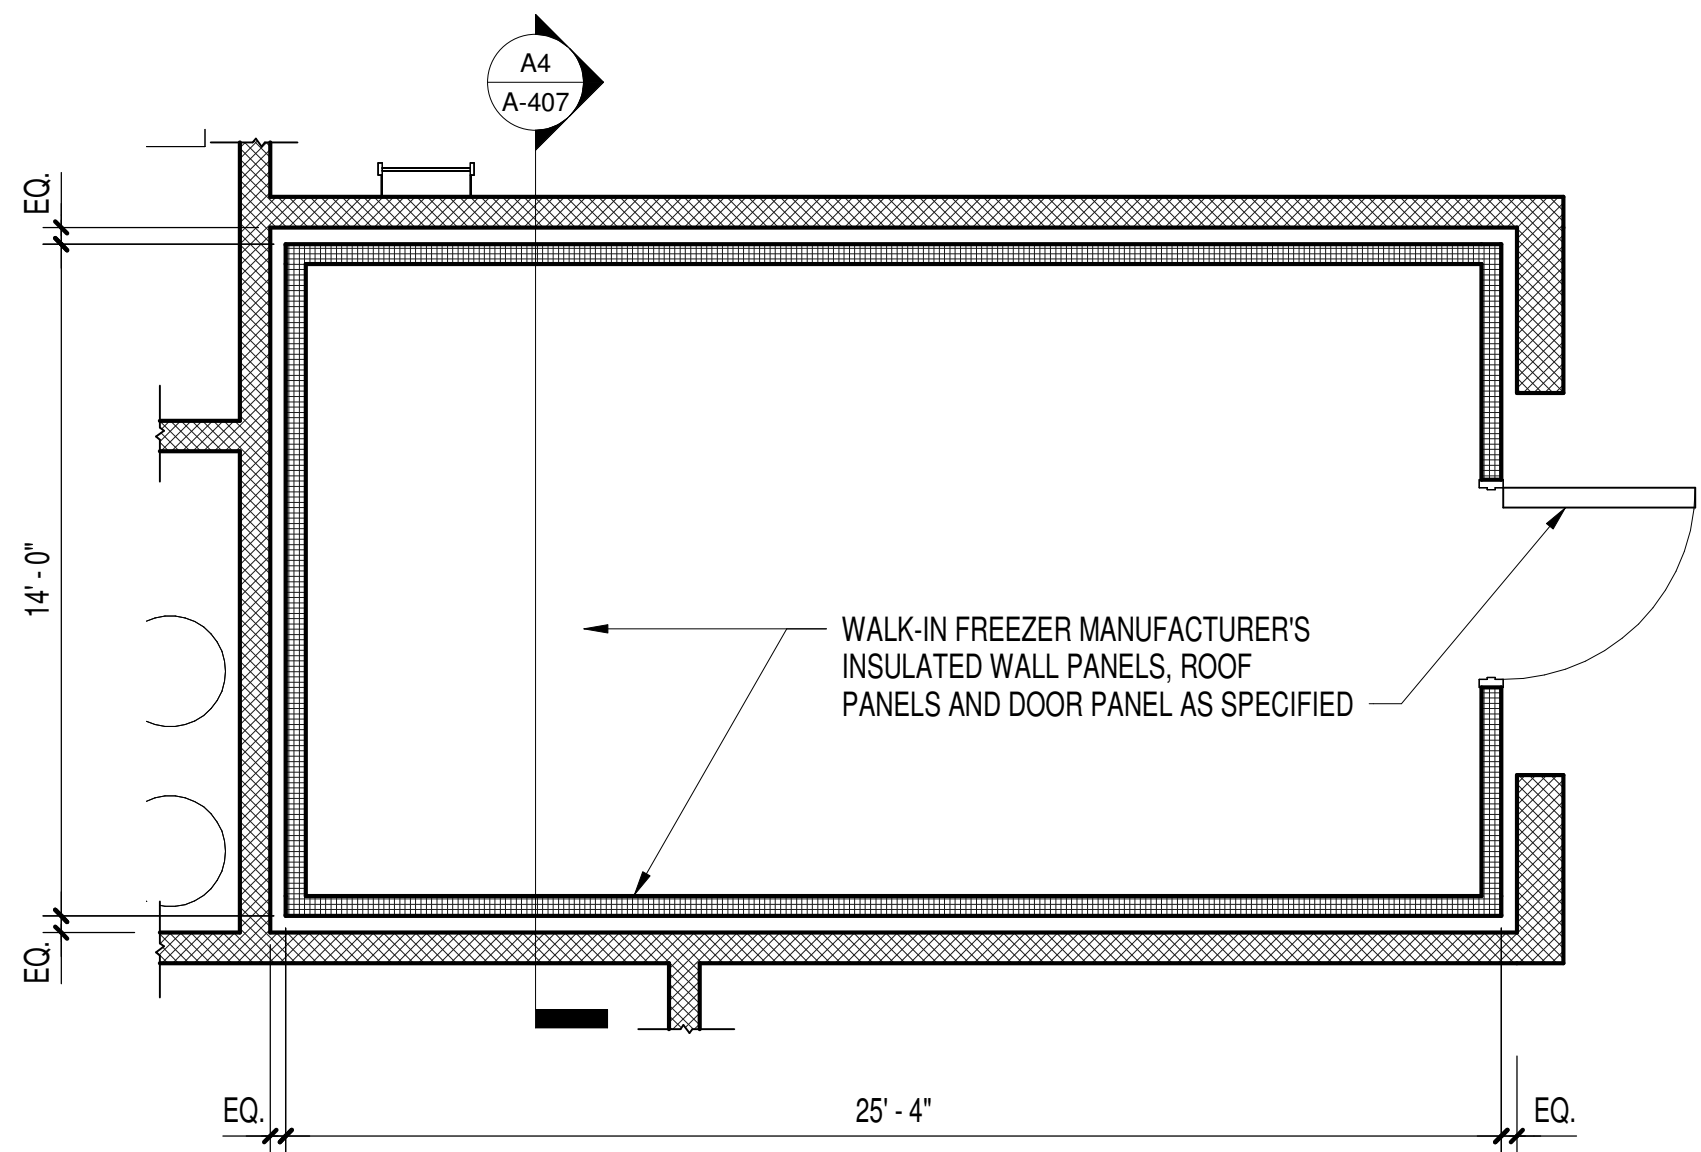

C4

ENLARGED PLAN AT WALK-IN FREEZER


SCALE: 1/4" = 1'-0"

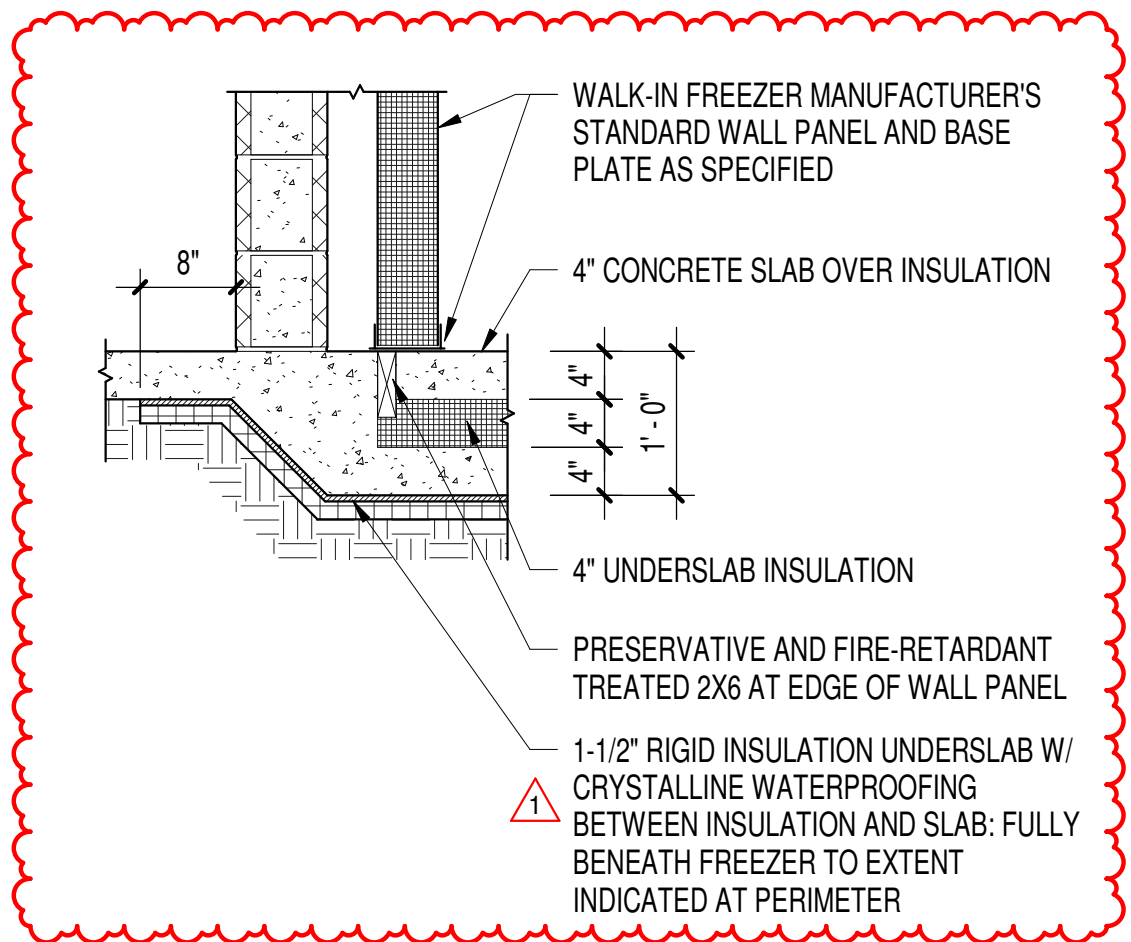

A3

FREEZER DETAIL

SCALE: 3/4" = 1'-0"

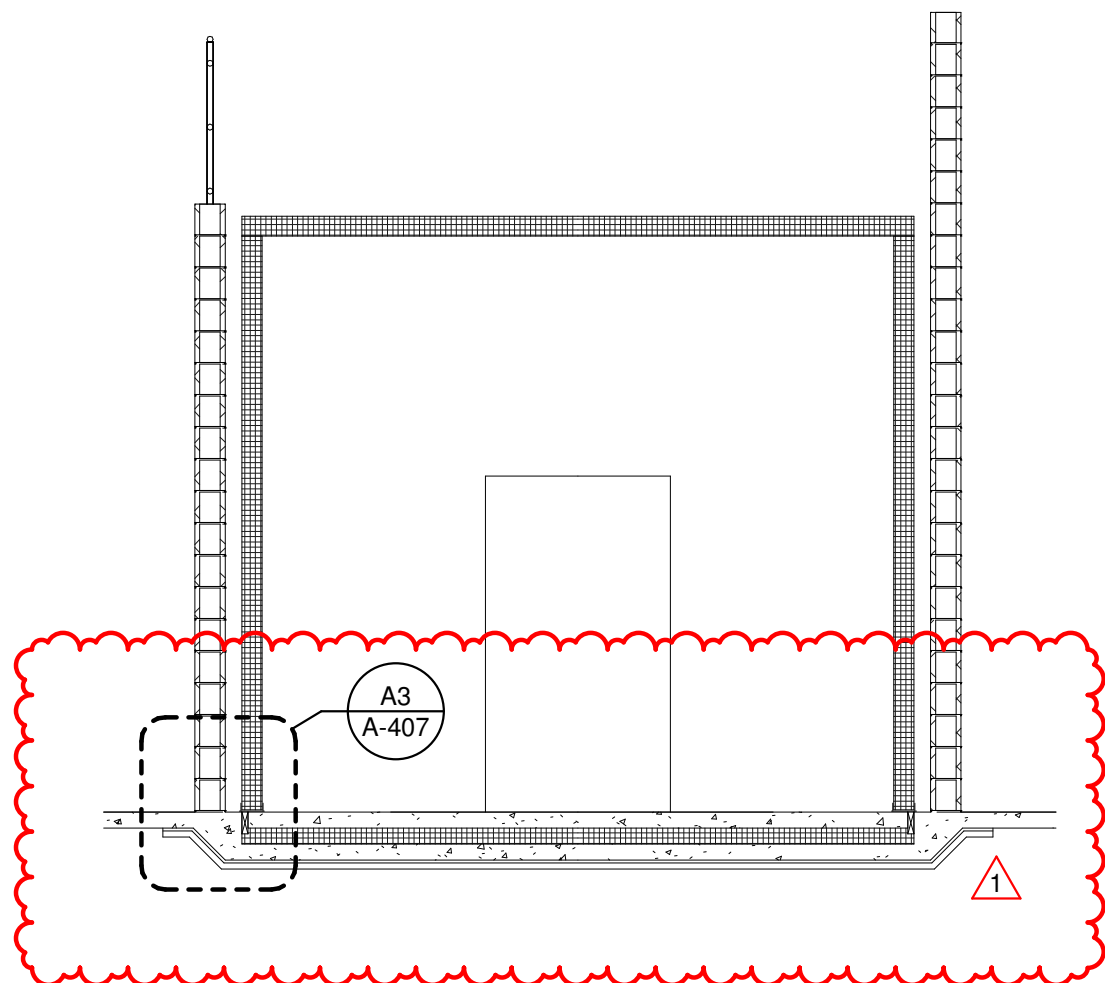


A4

SECTION AT WALK-IN FREEZER

SCALE: 1/4" = 1'-0"



SYN	DESCRIPTION	DATE	APPR
1	Amendment	2026.04.07	

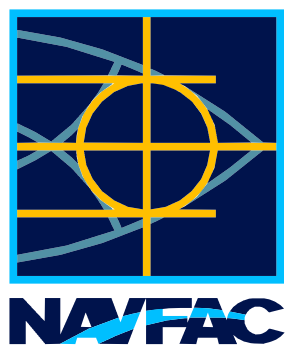

24 DECEMBER 2025 SEAL



APPROVED
FOR COMMANDER NAVFAC

ACTIVITY
Approved by Erik A. Lewis,
Infrastructure Engineering Branch Head,
FRCE Cherry Point via Electronic Signature

SATISFACTORY TO 12/24/2025

DES DLG DRW DLG CHK DJE

PM/DM KTB/SOM

BRANCH MANAGER CGM

CHIEF ENG/ARCH JWJ

FIRE PROTECTION HPN

DEPARTMENT OF THE NAVY
NAVAL FACILITIES ENGINEERING SYSTEMS COMMAND
NAVAL FACILITIES ENGINEERING SYSTEMS COMMAND - MIDATLANTIC
DESIGN AND CONSTRUCTION (DD CORE)
NAVAL STATION - NORFOLK, VA
MARINE CORPS AIR STATION
CHERRY POINT, NC
P-995 COMPOSITE REPAIR FACILITY
ENLARGED PLAN & SECTIONS - WALK-IN FREEZER

SCALE: AS INDICATED
EPROJCT NO.: 1692230
STA. PROJ. NO.:
NAVFAC DRAWING NO. 12938292
SHEET 144 OF 456
A-407

DRAWFORM REVISION: 25 AUGUST 2020

1

2

3

4

5